


Do not scale. All dimensions in mm. Check all dimensions on site.

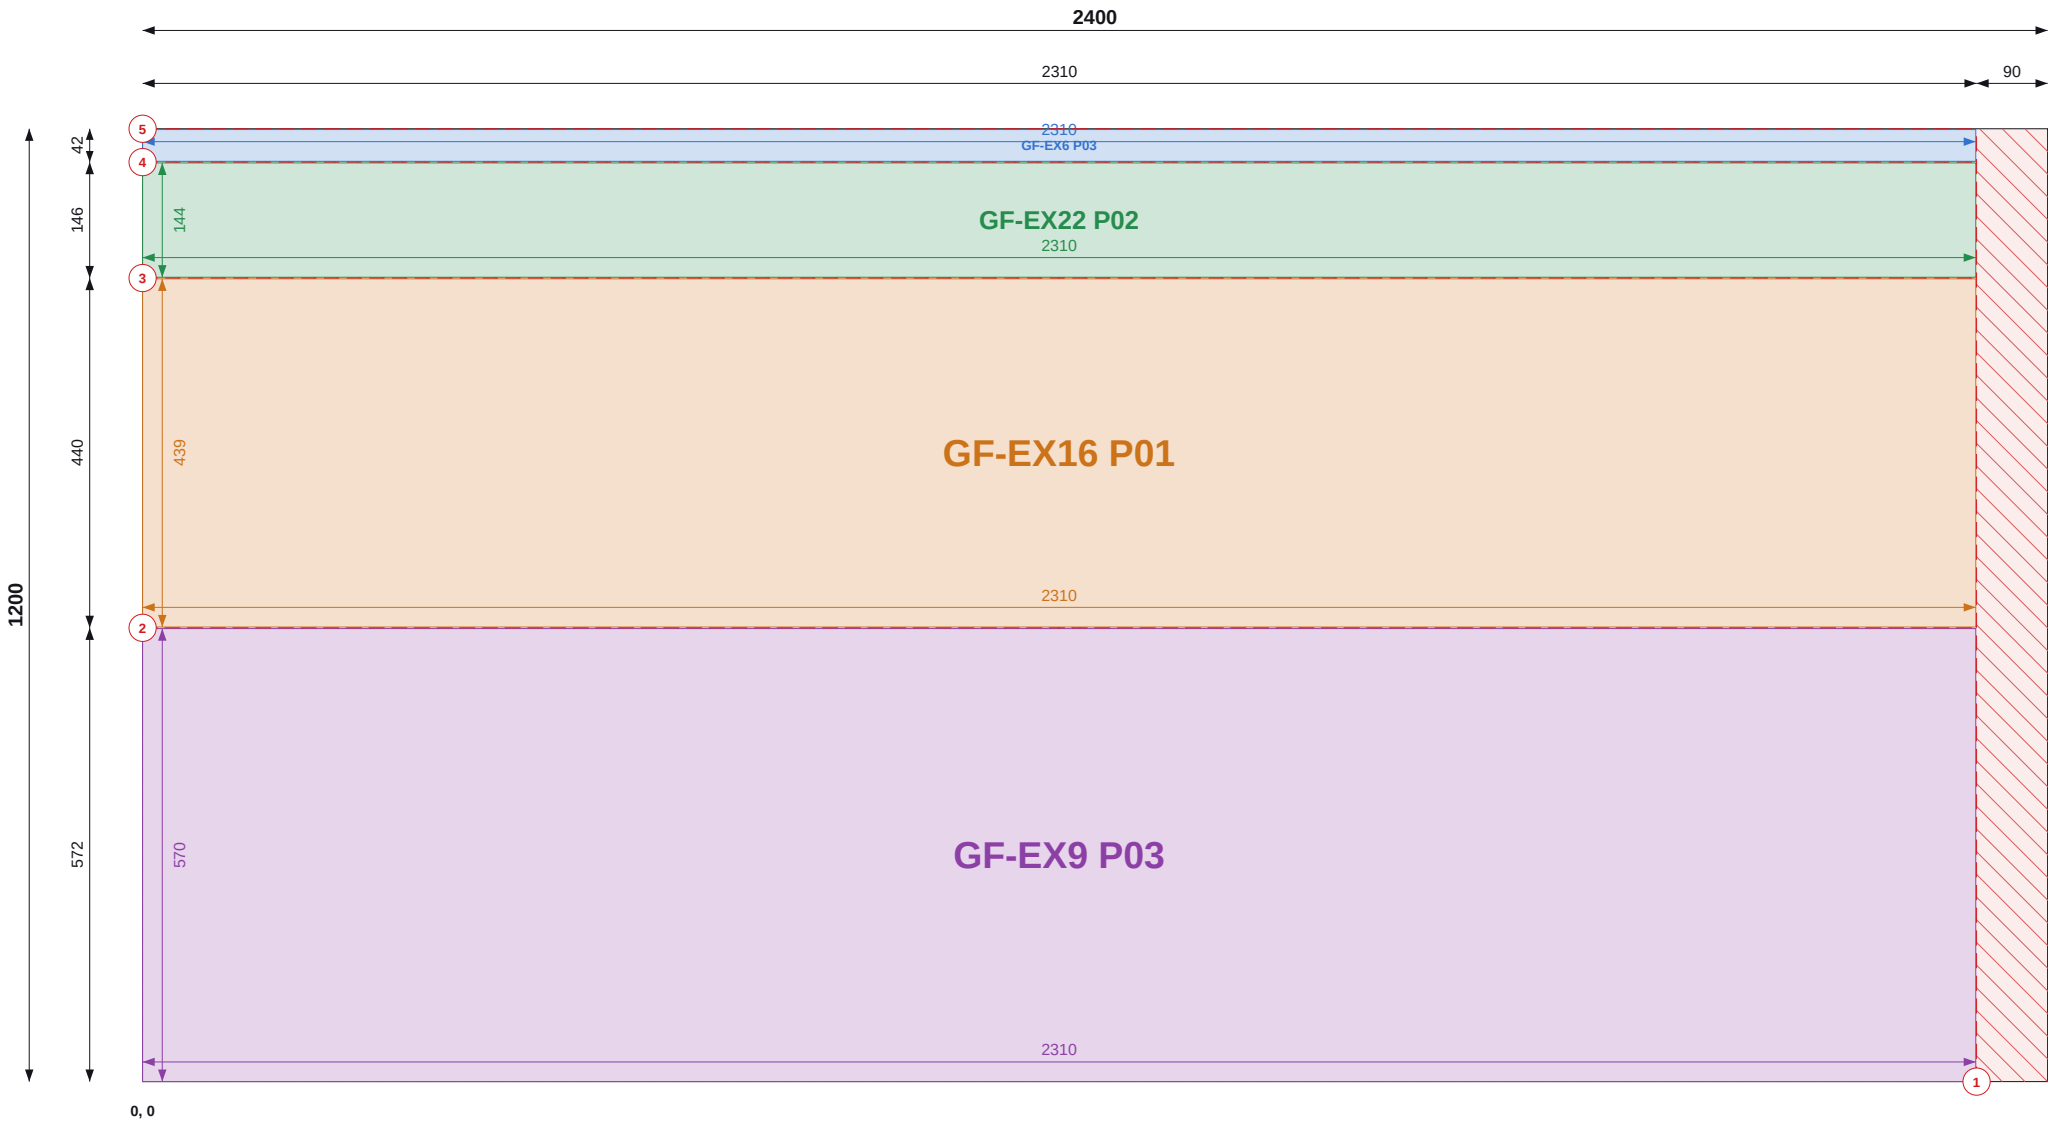

Top / left chains = saw cut positions (to cut centres). Coloured = part size and position.

SHEET 1 OF 21

THIS SHEET

Item	Value
Parts	4
Used / waste	95.7% / 0.12 m2
Reusable offcuts	0
Saw cuts / shared	5 / 3

PIECES (POSITION = BOTTOM-LEFT CORNER)

Label	Size	X, Y
GF-EX6 P03	40 x 2310	0, 1159
GF-EX22 P02	144 x 2310	0, 1013
GF-EX16 P01	439 x 2310	0, 572
GF-EX9 P03	570 x 2310	0, 0

GROUND FLOOR TOTALS

Item	Value
Sheets / pieces	21 / 154
Yield / waste	90.8% / 5.55 m2
Saw cuts / shared / on stock edge	187 / 133 / 111

NOTES

- Cut from PIR 120mm 1200x2400, 2mm saw kerf. Viewed on the face; dimensions from the sheet's bottom-left corner (0,0). Red numbered lines = saw cuts in order, each edge to edge.
- Coloured dimensions belong to the part of that colour: its width and height, and its position from the sheet edges. Raked parts: corner coordinates at each corner.
- Red hatch = waste. Labels = panel + piece mark on the manufacture drawing.

REVISIONS

REV	DATE	DESCRIPTION
C01	13.09.26	Construction issue



TLS TIMBER FRAME

Design & Manufacture

Scan: 3D model + drawings




CLIENT	PROJECT
MP Adams	MP Adams Plot 3, Eckington

DRAWING TITLE			
PIR CUTTING - GROUND FLOOR - SHEET 1 OF 21			
PIR 120mm 1200x2400 Ground Floor			

SCALE	SIZE	DATE	DRAWN
NTS	A3	13.09.26	TS

STATUS	DRAWING No.	REV
CONSTRUCTION	P3-CP-PIR-01 / 01	C01

Do not scale. All dimensions in mm. Check all dimensions on site.

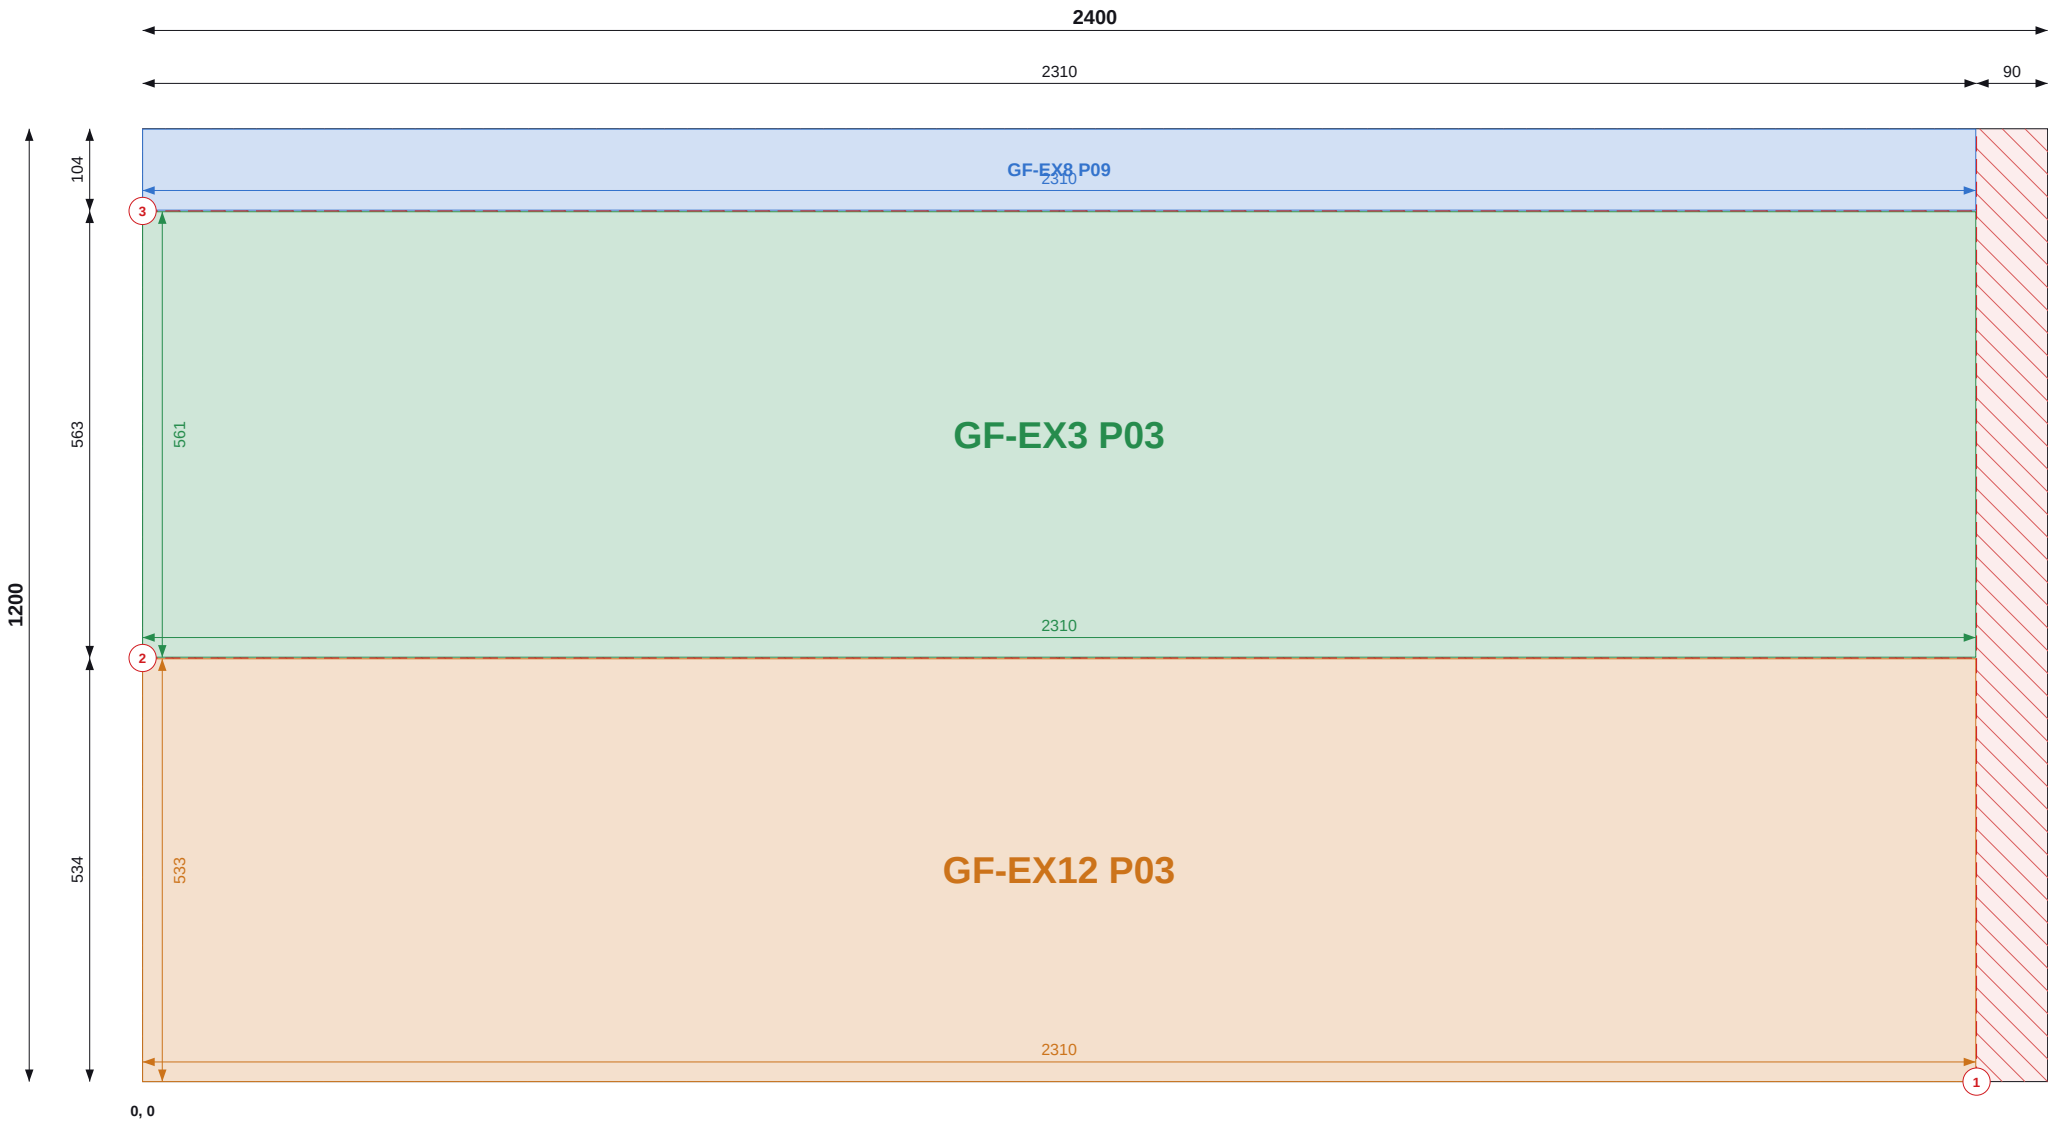

Top / left chains = saw cut positions (to cut centres). Coloured = part size and position.

SHEET 2 OF 21

THIS SHEET

Item	Value
Parts	3
Used / waste	95.9% / 0.12 m2
Reusable offcuts	0
Saw cuts / shared	3 / 2

PIECES (POSITION = BOTTOM-LEFT CORNER)

Label	Size	X, Y
GF-EX8 P09	102 x 2310	0, 1098
GF-EX3 P03	561 x 2310	0, 535
GF-EX12 P03	533 x 2310	0, 0

NOTES

- Cut from PIR 120mm 1200x2400, 2mm saw kerf. Viewed on the face; dimensions from the sheet's bottom-left corner (0,0). Red numbered lines = saw cuts in order, each edge to edge.
- Coloured dimensions belong to the part of that colour: its width and height, and its position from the sheet edges. Raked parts: corner coordinates at each corner.
- Red hatch = waste. Labels = panel + piece mark on the manufacture drawing.

REVISIONS

REV	DATE	DESCRIPTION
C01	13.09.26	Construction issue



TLS TIMBER FRAME

Design & Manufacture

Scan: 3D model + drawings



CLIENT	PROJECT
MP Adams	MP Adams Plot 3, Eckington


DRAWING TITLE
PIR CUTTING - GROUND FLOOR - SHEET 2 OF 21

PIR 120mm 1200x2400 | Ground Floor

SCALE	SIZE	DATE	DRAWN
NTS	A3	13.09.26	TS

STATUS	DRAWING No.	REV
CONSTRUCTION	P3-CP-PIR-01 / 02	C01

Do not scale. All dimensions in mm. Check all dimensions on site.

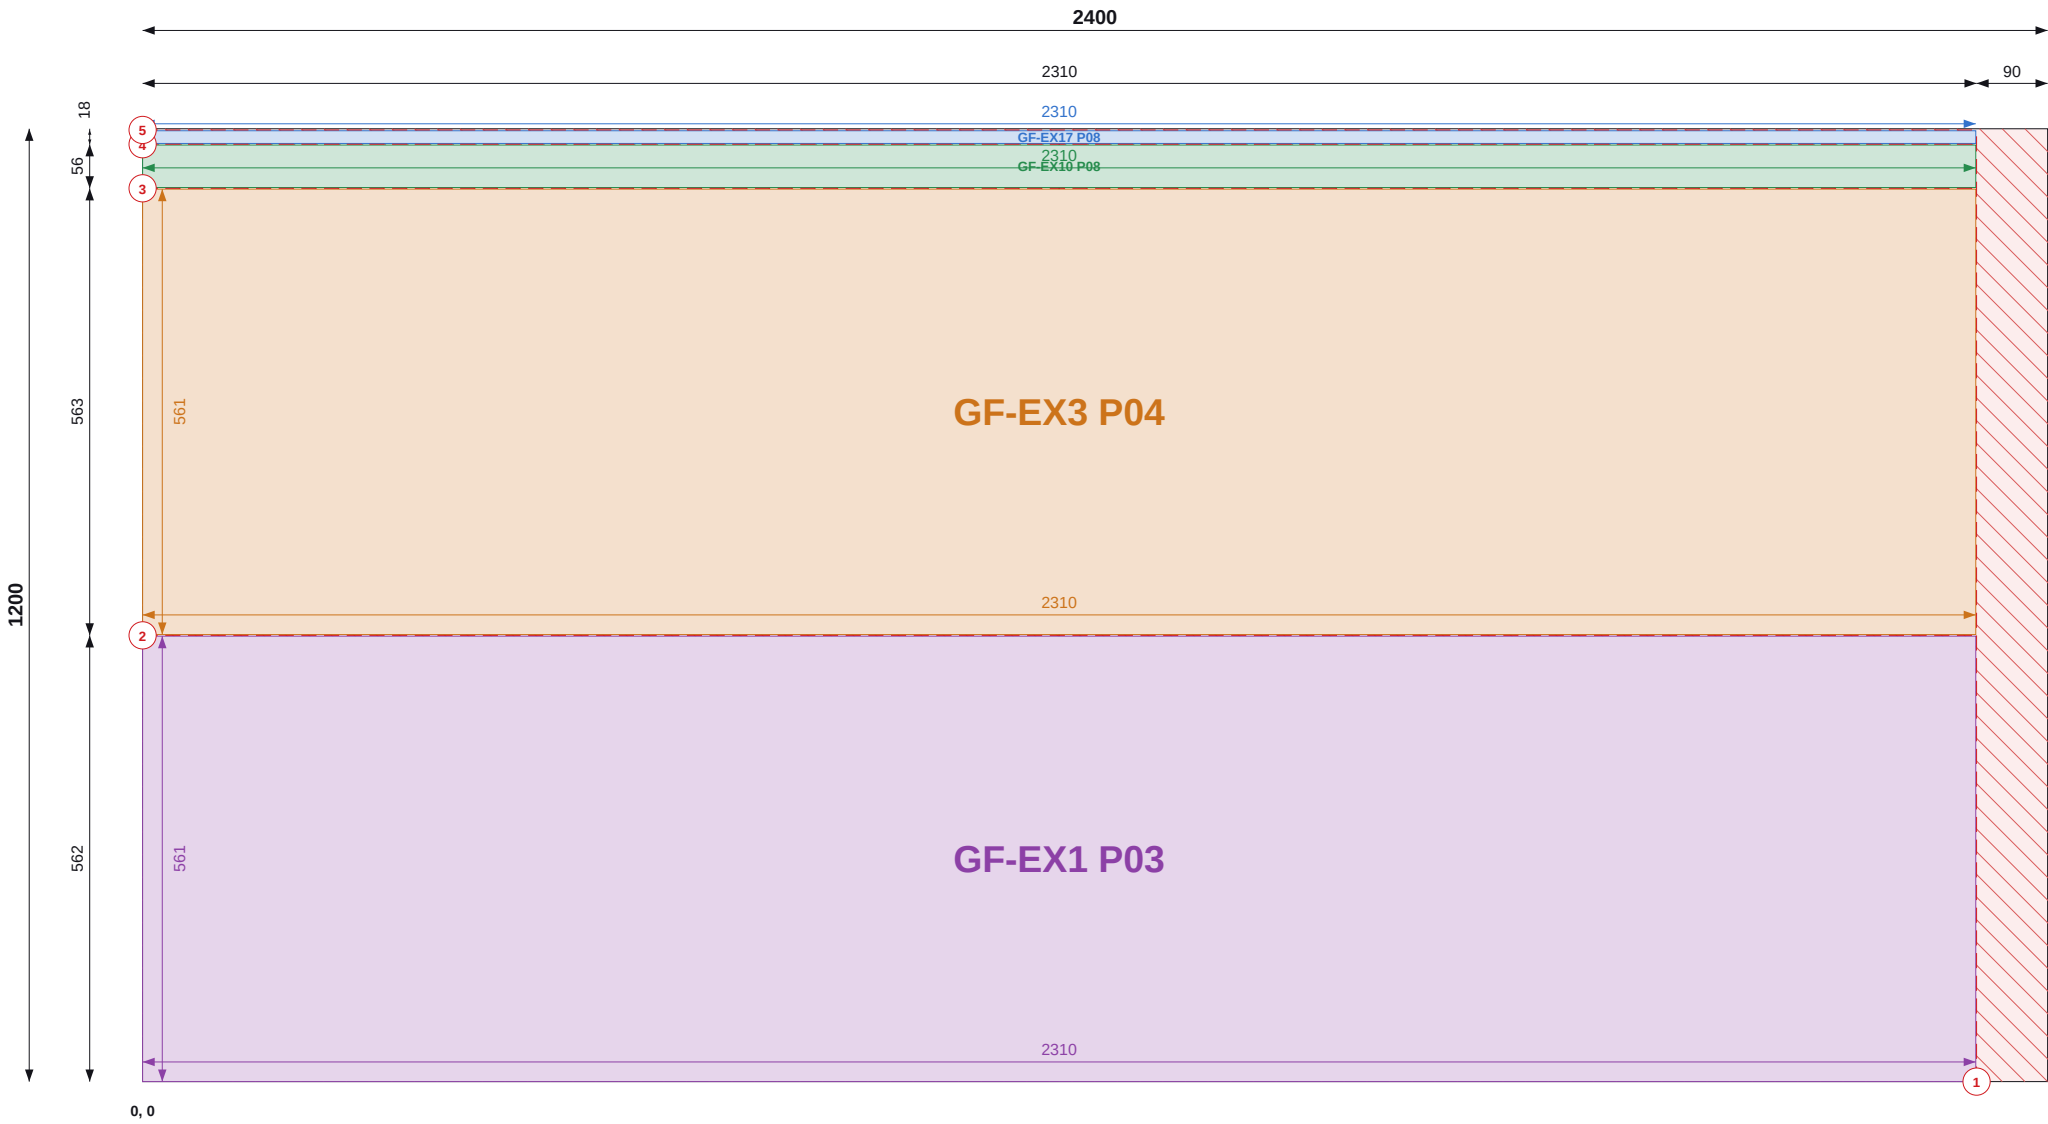

Top / left chains = saw cut positions (to cut centres). Coloured = part size and position.

SHEET 3 OF 21

THIS SHEET

Item	Value
Parts	4
Used / waste	95.5% / 0.13 m2
Reusable offcuts	0
Saw cuts / shared	5 / 3

PIECES (POSITION = BOTTOM-LEFT CORNER)

Label	Size	X, Y
GF-EX17 P08	16 x 2310	0, 1181
GF-EX10 P08	53 x 2310	0, 1126
GF-EX3 P04	561 x 2310	0, 563
GF-EX1 P03	561 x 2310	0, 0

NOTES

- Cut from PIR 120mm 1200x2400, 2mm saw kerf. Viewed on the face; dimensions from the sheet's bottom-left corner (0,0). Red numbered lines = saw cuts in order, each edge to edge.
- Coloured dimensions belong to the part of that colour: its width and height, and its position from the sheet edges. Raked parts: corner coordinates at each corner.
- Red hatch = waste. Labels = panel + piece mark on the manufacture drawing.

REVISIONS

REV	DATE	DESCRIPTION
C01	13.09.26	Construction issue



TLS TIMBER FRAME

Design & Manufacture

Scan: 3D model + drawings



CLIENT	PROJECT
MP Adams	MP Adams Plot 3, Eckington


DRAWING TITLE
PIR CUTTING - GROUND FLOOR - SHEET 3 OF 21

PIR 120mm 1200x2400 | Ground Floor

SCALE	SIZE	DATE	DRAWN
NTS	A3	13.09.26	TS

STATUS	DRAWING No.	REV
CONSTRUCTION	P3-CP-PIR-01 / 03	C01

Do not scale. All dimensions in mm. Check all dimensions on site.

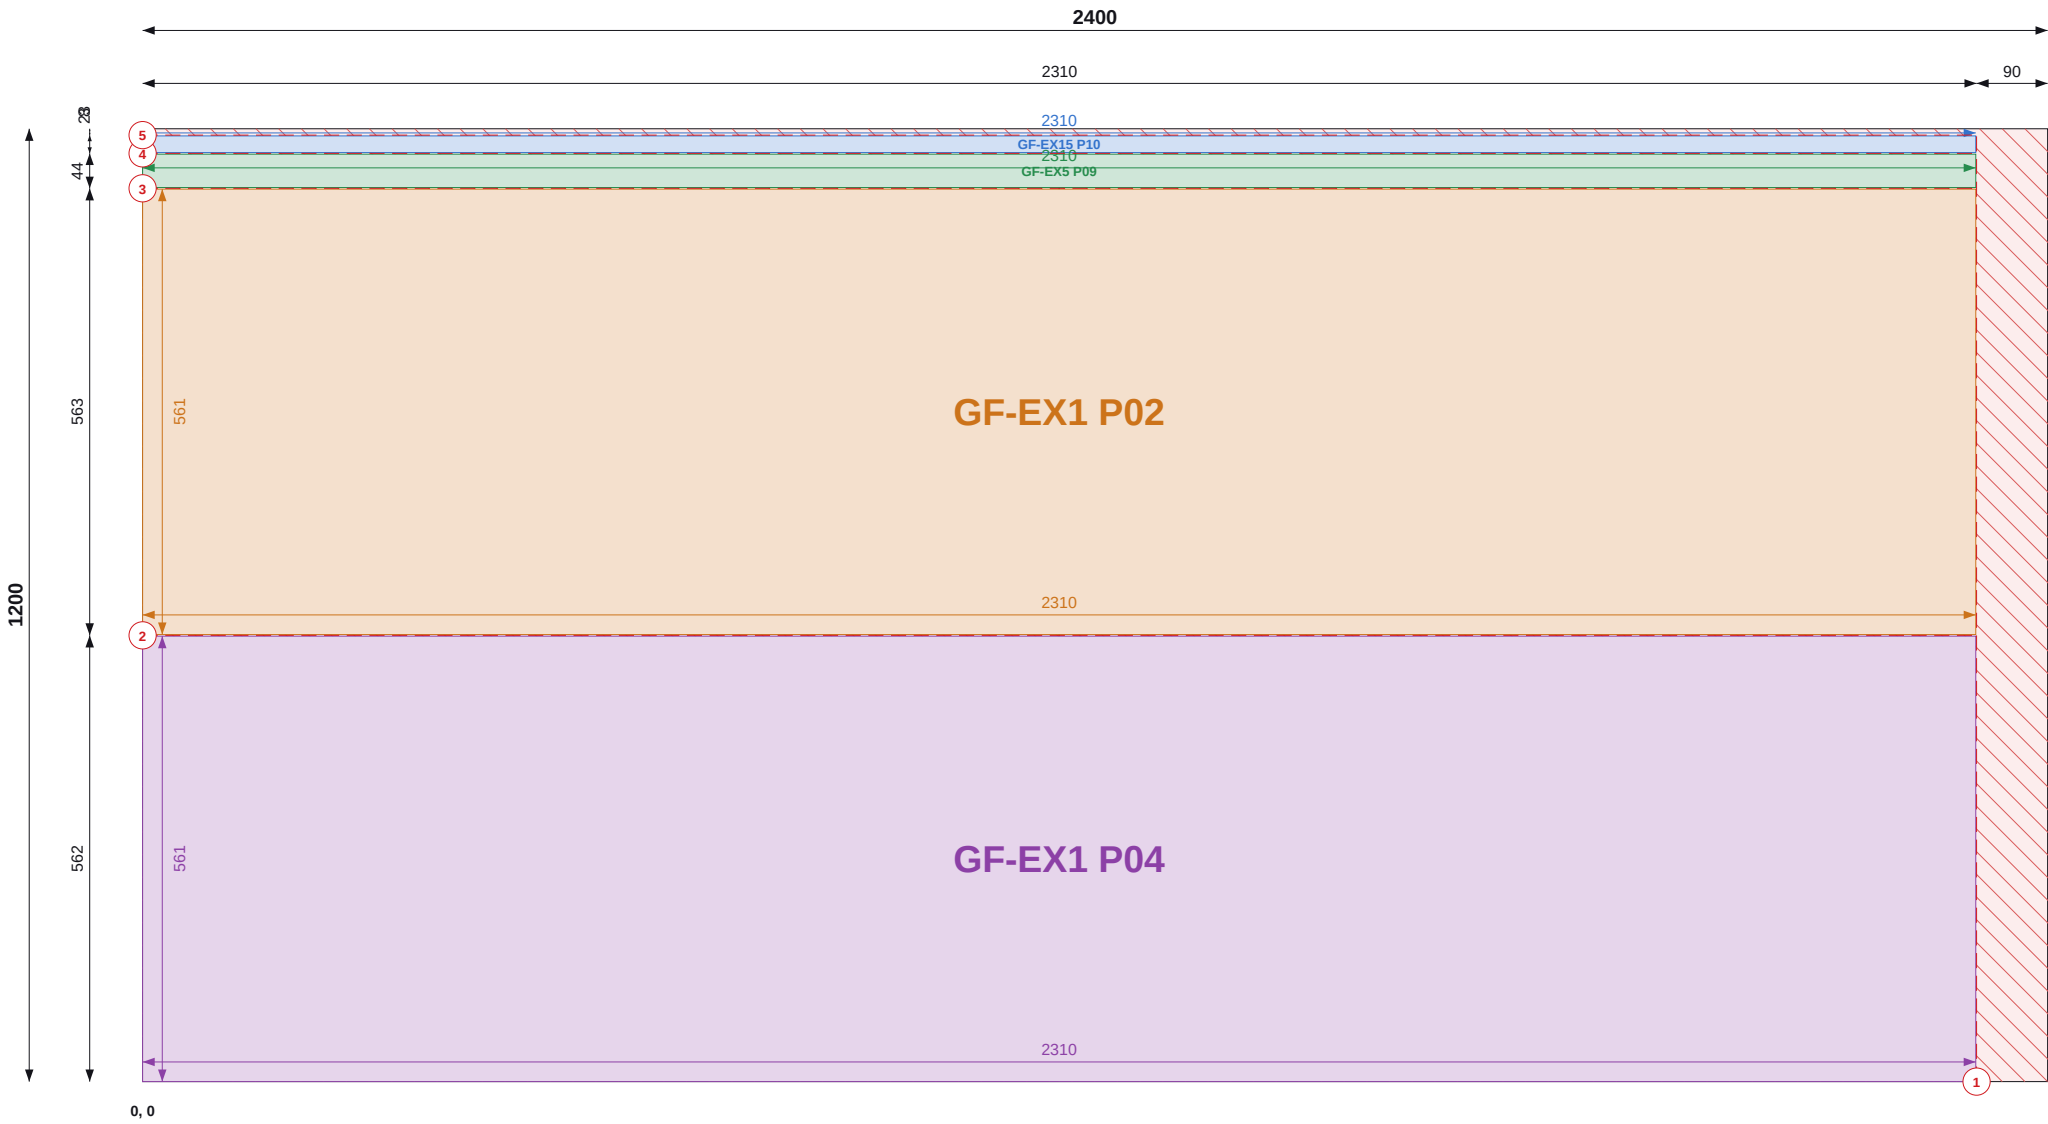

Top / left chains = saw cut positions (to cut centres). Coloured = part size and position.

SHEET 4 OF 21

THIS SHEET

Item	Value
Parts	4
Used / waste	95.0% / 0.14 m2
Reusable offcuts	0
Saw cuts / shared	5 / 3

PIECES (POSITION = BOTTOM-LEFT CORNER)

Label	Size	X, Y
GF-EX15 P10	21 x 2310	0, 1170
GF-EX5 P09	42 x 2310	0, 1126
GF-EX1 P02	561 x 2310	0, 563
GF-EX1 P04	561 x 2310	0, 0

NOTES

- Cut from PIR 120mm 1200x2400, 2mm saw kerf. Viewed on the face; dimensions from the sheet's bottom-left corner (0,0). Red numbered lines = saw cuts in order, each edge to edge.
- Coloured dimensions belong to the part of that colour: its width and height, and its position from the sheet edges. Raked parts: corner coordinates at each corner.
- Red hatch = waste. Labels = panel + piece mark on the manufacture drawing.

REVISIONS

REV	DATE	DESCRIPTION
C01	13.09.26	Construction issue



TLS TIMBER FRAME

Design & Manufacture

Scan: 3D model + drawings




CLIENT	PROJECT
MP Adams	MP Adams Plot 3, Eckington

DRAWING TITLE			
PIR CUTTING - GROUND FLOOR - SHEET 4 OF 21			
PIR 120mm 1200x2400 Ground Floor			

SCALE	SIZE	DATE	DRAWN
NTS	A3	13.09.26	TS

STATUS	DRAWING No.	REV
CONSTRUCTION	P3-CP-PIR-01 / 04	C01

Do not scale. All dimensions in mm. Check all dimensions on site.

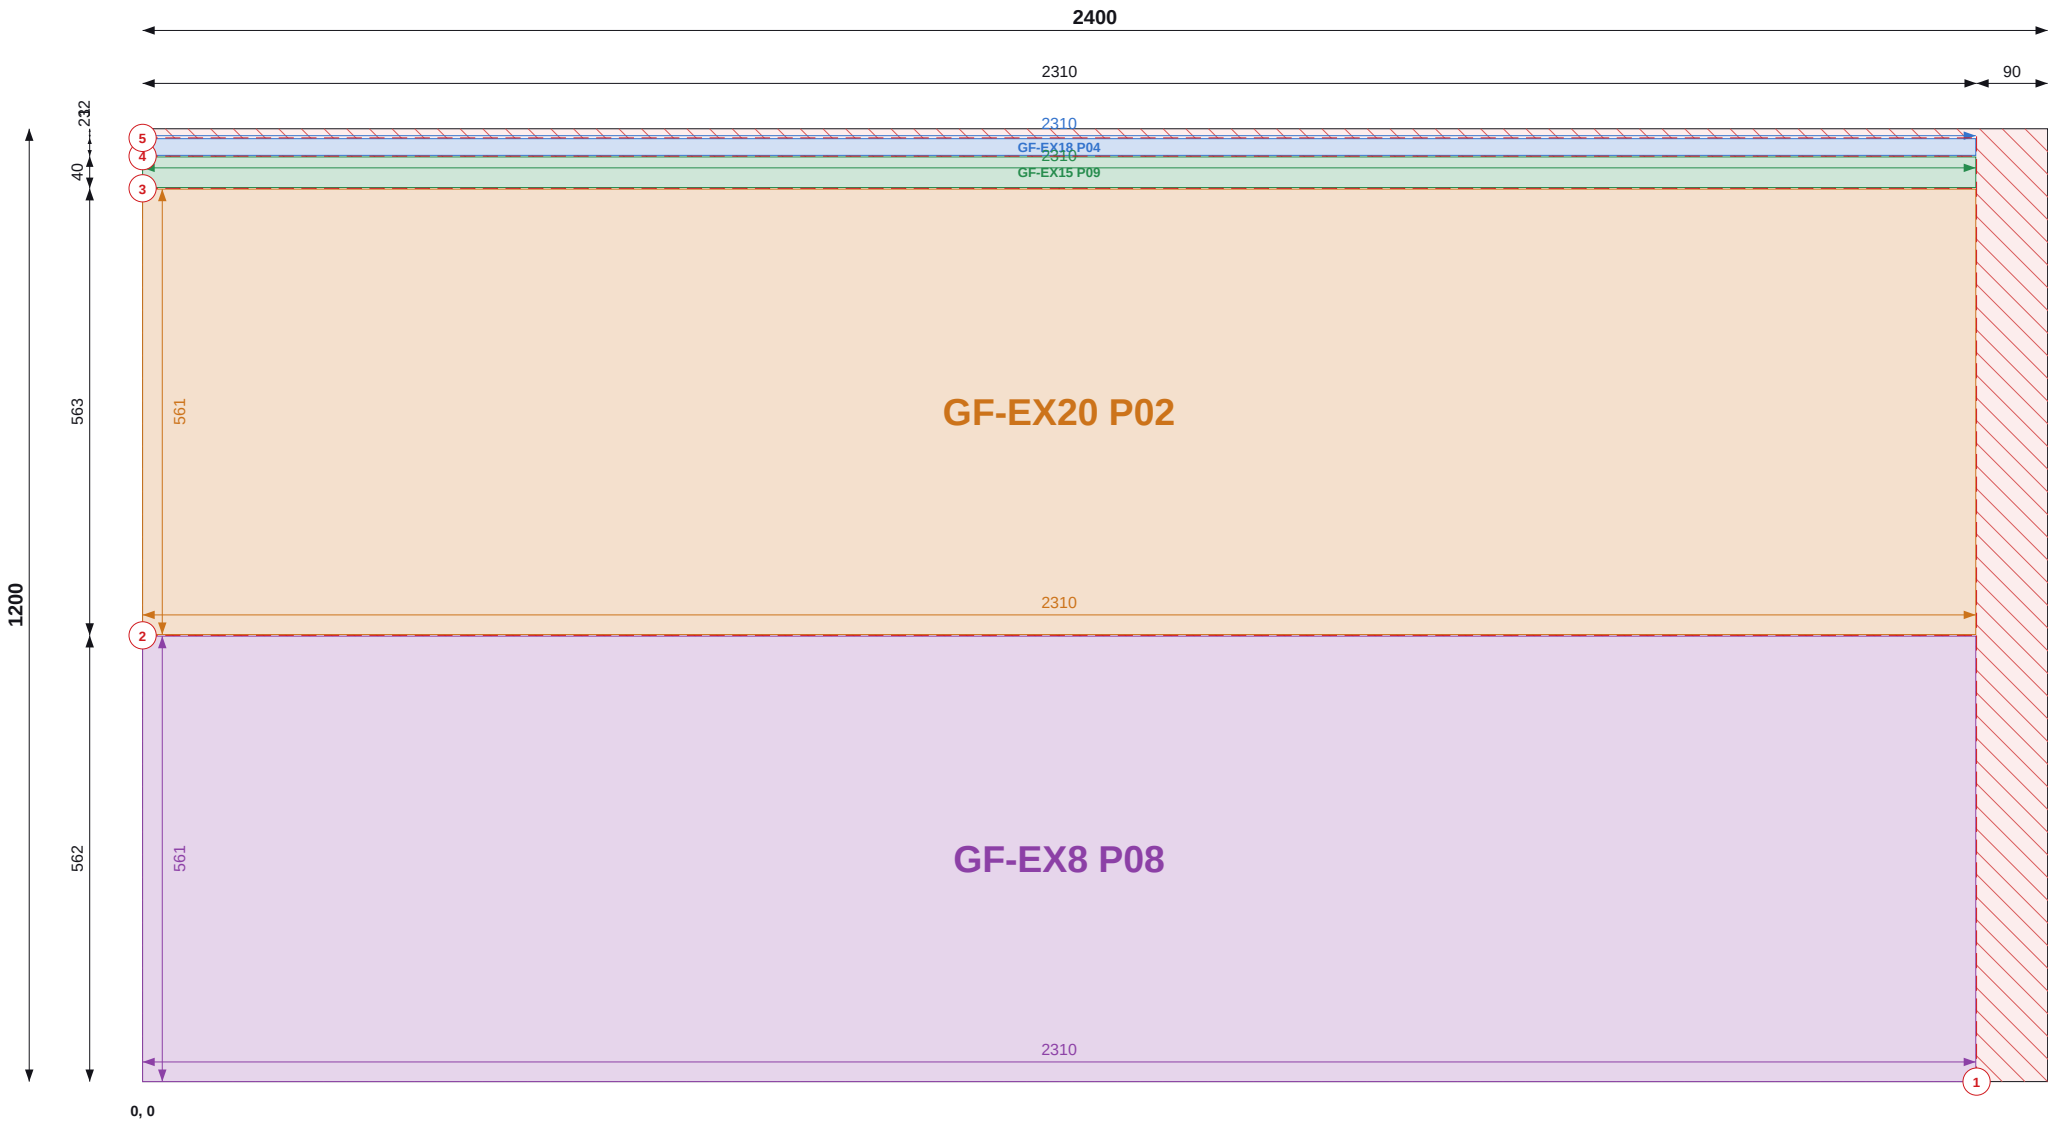

Top / left chains = saw cut positions (to cut centres). Coloured = part size and position.

SHEET 5 OF 21

THIS SHEET

Item	Value
Parts	4
Used / waste	94.7% / 0.15 m2
Reusable offcuts	0
Saw cuts / shared	5 / 3

PIECES (POSITION = BOTTOM-LEFT CORNER)

Label	Size	X, Y
GF-EX18 P04	21 x 2310	0, 1166
GF-EX15 P09	38 x 2310	0, 1126
GF-EX20 P02	561 x 2310	0, 563
GF-EX8 P08	561 x 2310	0, 0

NOTES

- Cut from PIR 120mm 1200x2400, 2mm saw kerf. Viewed on the face; dimensions from the sheet's bottom-left corner (0,0). Red numbered lines = saw cuts in order, each edge to edge.
- Coloured dimensions belong to the part of that colour: its width and height, and its position from the sheet edges. Raked parts: corner coordinates at each corner.
- Red hatch = waste. Labels = panel + piece mark on the manufacture drawing.

REVISIONS

REV	DATE	DESCRIPTION
C01	13.09.26	Construction issue



TLS TIMBER FRAME

Design & Manufacture

Scan: 3D model + drawings



CLIENT	PROJECT
MP Adams	MP Adams Plot 3, Eckington


DRAWING TITLE
PIR CUTTING - GROUND FLOOR - SHEET 5 OF 21

PIR 120mm 1200x2400 | Ground Floor

SCALE	SIZE	DATE	DRAWN
NTS	A3	13.09.26	TS

STATUS	DRAWING No.	REV
CONSTRUCTION	P3-CP-PIR-01 / 05	C01

Do not scale. All dimensions in mm. Check all dimensions on site.

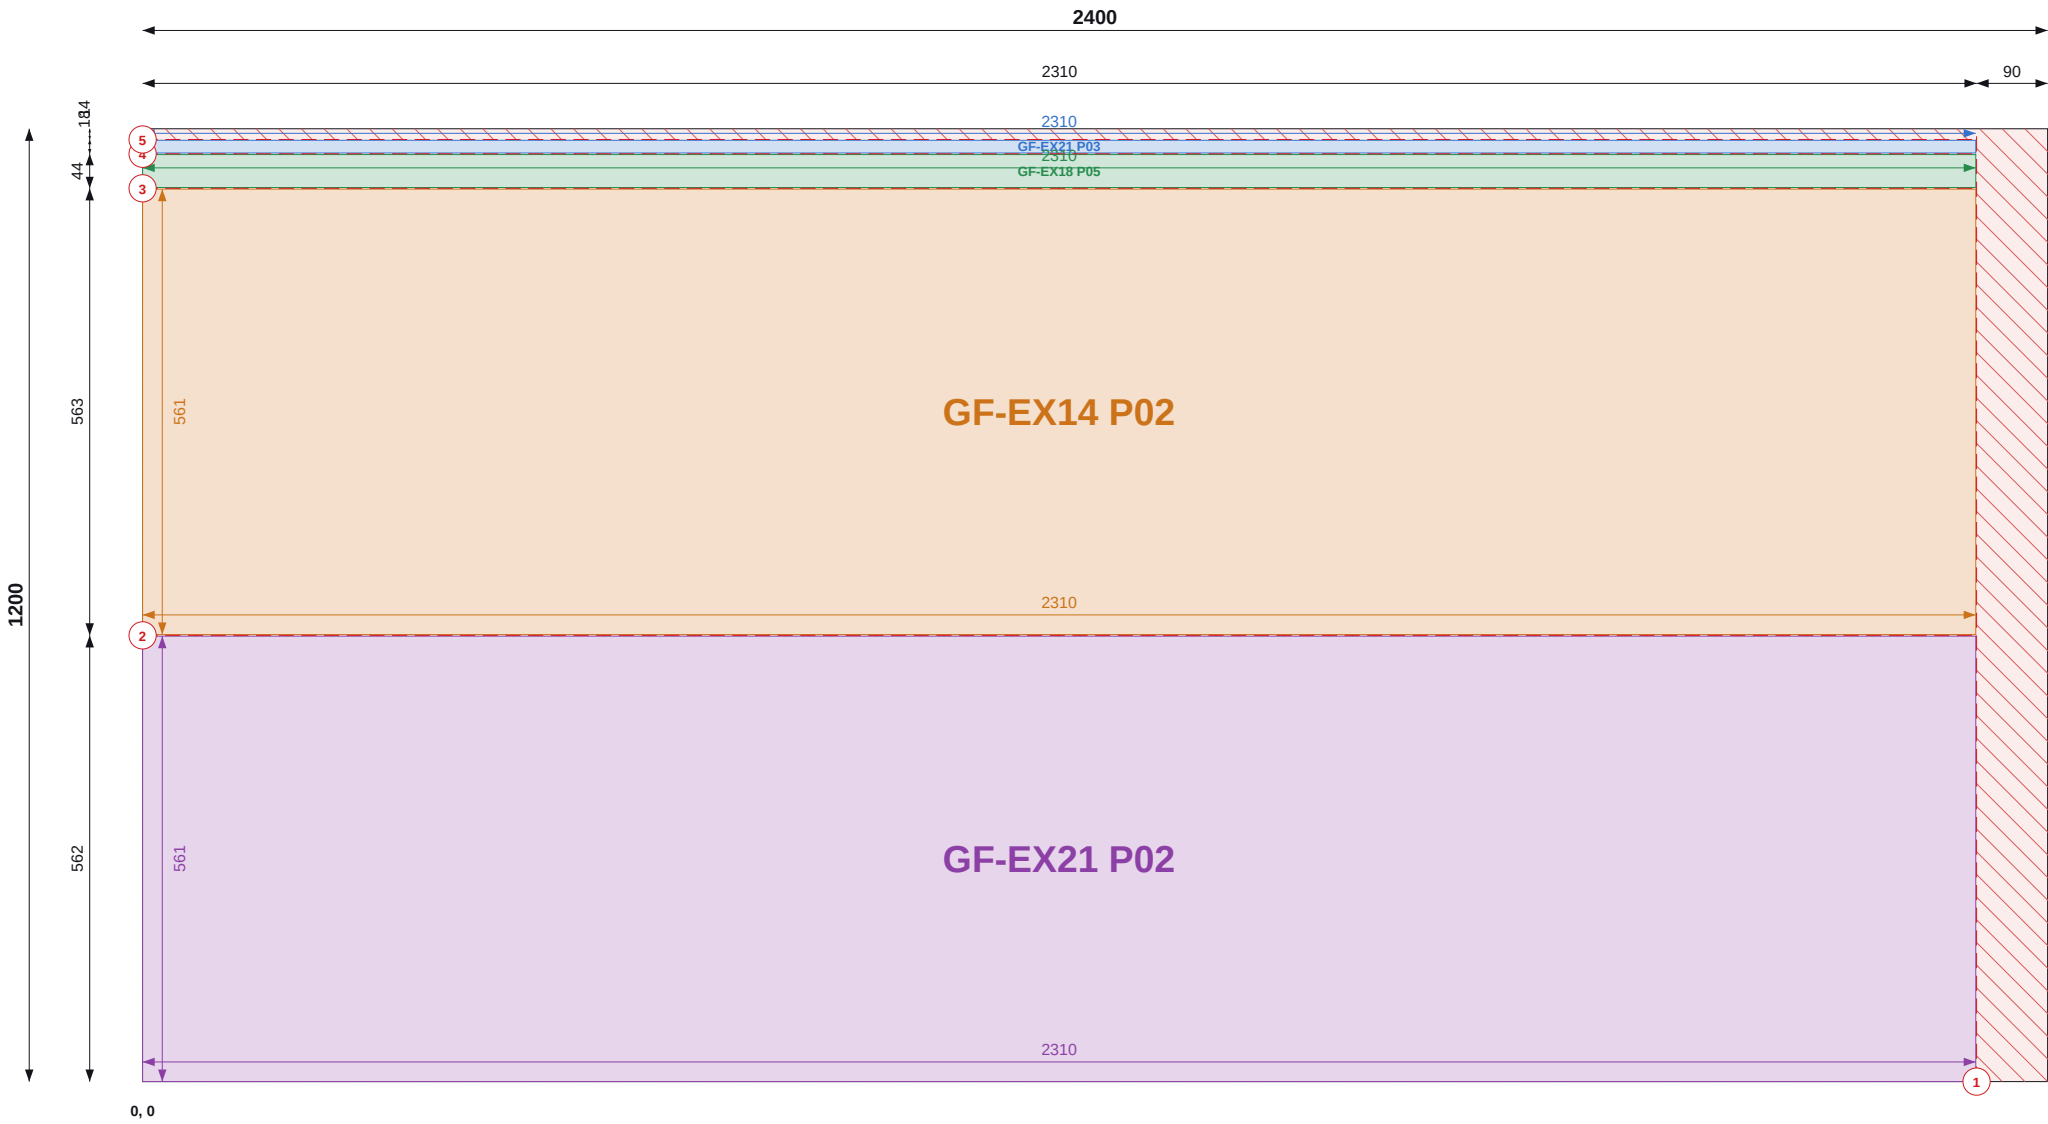

Top / left chains = saw cut positions (to cut centres). Coloured = part size and position.

SHEET 6 OF 21

THIS SHEET

Item	Value
Parts	4
Used / waste	94.6% / 0.16 m2
Reusable offcuts	0
Saw cuts / shared	5 / 3

PIECES (POSITION = BOTTOM-LEFT CORNER)

Label	Size	X, Y
GF-EX21 P03	16 x 2310	0, 1169
GF-EX18 P05	41 x 2310	0, 1126
GF-EX14 P02	561 x 2310	0, 563
GF-EX21 P02	561 x 2310	0, 0

NOTES

- Cut from PIR 120mm 1200x2400, 2mm saw kerf. Viewed on the face; dimensions from the sheet's bottom-left corner (0,0). Red numbered lines = saw cuts in order, each edge to edge.
- Coloured dimensions belong to the part of that colour: its width and height, and its position from the sheet edges. Raked parts: corner coordinates at each corner.
- Red hatch = waste. Labels = panel + piece mark on the manufacture drawing.

REVISIONS

REV	DATE	DESCRIPTION
C01	13.09.26	Construction issue



TLS TIMBER FRAME

Design & Manufacture

Scan: 3D model + drawings




CLIENT	PROJECT
MP Adams	MP Adams Plot 3, Eckington

DRAWING TITLE			
PIR CUTTING - GROUND FLOOR - SHEET 6 OF 21			
PIR 120mm 1200x2400 Ground Floor			

SCALE	SIZE	DATE	DRAWN
NTS	A3	13.09.26	TS

STATUS	DRAWING No.	REV
CONSTRUCTION	P3-CP-PIR-01 / 06	C01

Do not scale. All dimensions in mm. Check all dimensions on site.

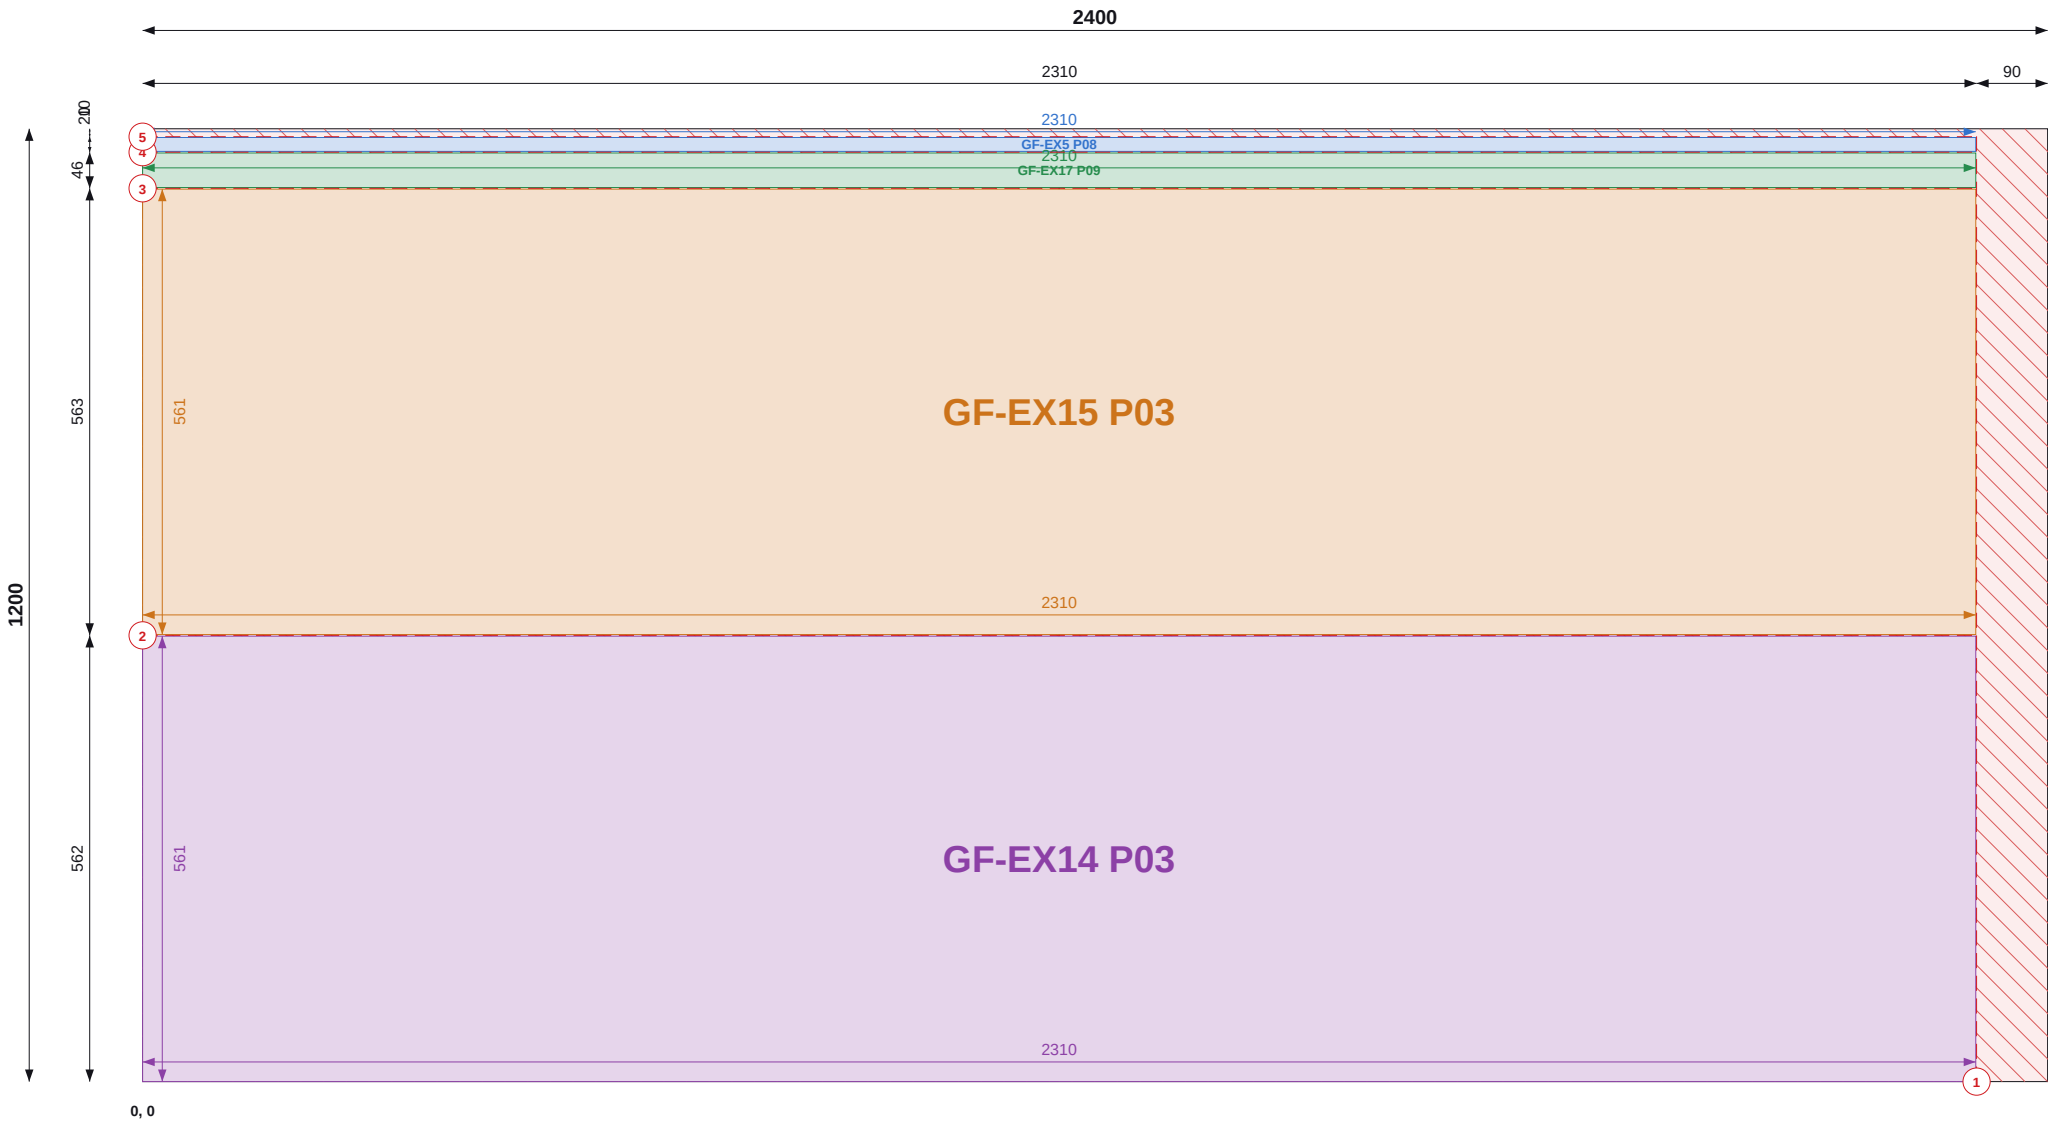

Top / left chains = saw cut positions (to cut centres). Coloured = part size and position.

SHEET 7 OF 21

THIS SHEET

Item	Value
Parts	4
Used / waste	94.9% / 0.15 m2
Reusable offcuts	0
Saw cuts / shared	5 / 3

PIECES (POSITION = BOTTOM-LEFT CORNER)

Label	Size	X, Y
GF-EX5 P08	17 x 2310	0, 1171
GF-EX17 P09	43 x 2310	0, 1126
GF-EX15 P03	561 x 2310	0, 563
GF-EX14 P03	561 x 2310	0, 0

NOTES

- Cut from PIR 120mm 1200x2400, 2mm saw kerf. Viewed on the face; dimensions from the sheet's bottom-left corner (0,0). Red numbered lines = saw cuts in order, each edge to edge.
- Coloured dimensions belong to the part of that colour: its width and height, and its position from the sheet edges. Raked parts: corner coordinates at each corner.
- Red hatch = waste. Labels = panel + piece mark on the manufacture drawing.

REVISIONS

REV	DATE	DESCRIPTION
C01	13.09.26	Construction issue



TLS TIMBER FRAME

Design & Manufacture

Scan: 3D model + drawings




CLIENT	PROJECT
MP Adams	MP Adams Plot 3, Eckington

DRAWING TITLE			
PIR CUTTING - GROUND FLOOR - SHEET 7 OF 21			
PIR 120mm 1200x2400 Ground Floor			

SCALE	SIZE	DATE	DRAWN
NTS	A3	13.09.26	TS

STATUS	DRAWING No.	REV
CONSTRUCTION	P3-CP-PIR-01 / 07	C01

Do not scale. All dimensions in mm. Check all dimensions on site.

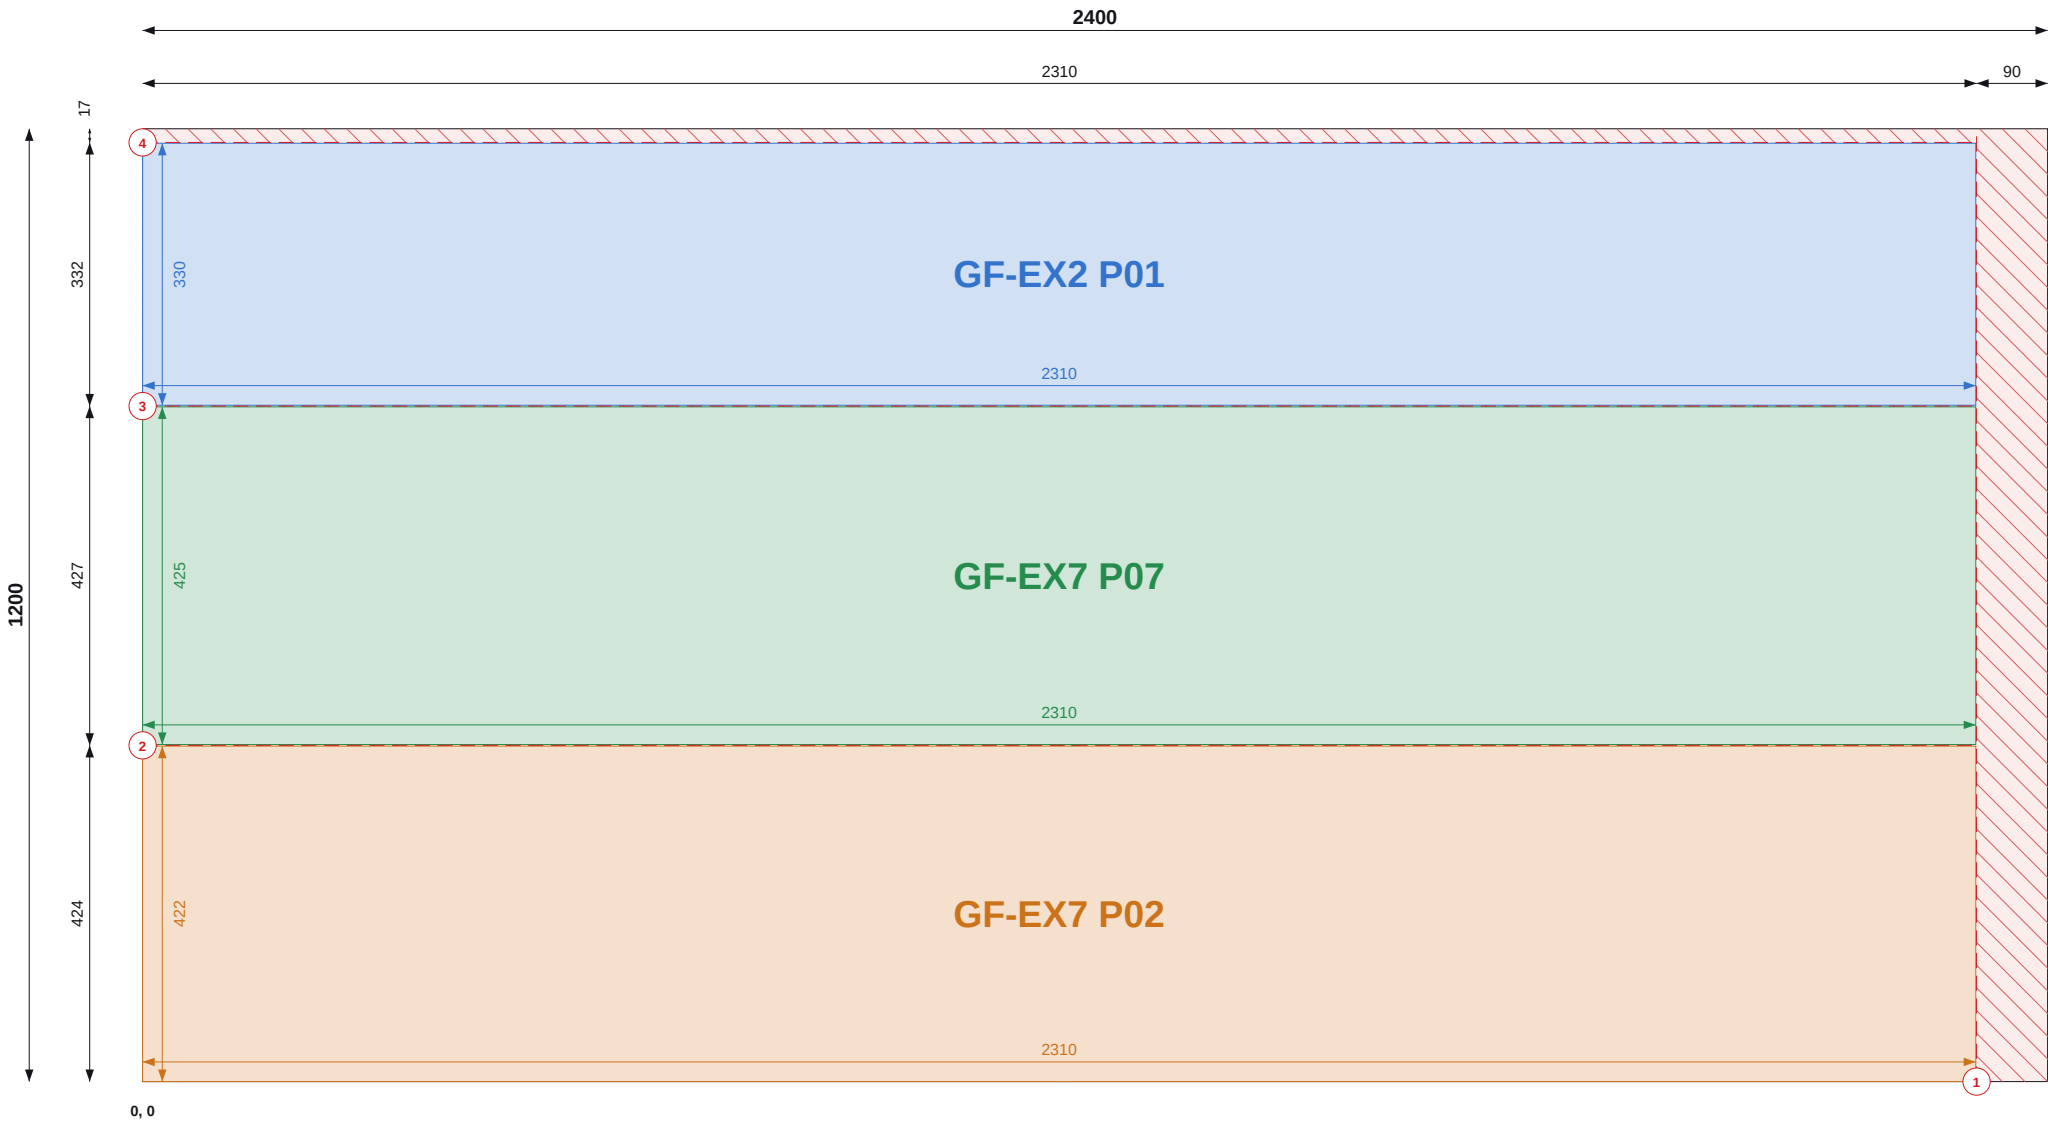

Top / left chains = saw cut positions (to cut centres). Coloured = part size and position.

SHEET 8 OF 21

THIS SHEET

Item	Value
Parts	3
Used / waste	94.4% / 0.16 m2
Reusable offcuts	0
Saw cuts / shared	4 / 2

PIECES (POSITION = BOTTOM-LEFT CORNER)

Label	Size	X, Y
GF-EX2 P01	330 x 2310	0, 852
GF-EX7 P07	425 x 2310	0, 424
GF-EX7 P02	422 x 2310	0, 0

NOTES

- Cut from PIR 120mm 1200x2400, 2mm saw kerf. Viewed on the face; dimensions from the sheet's bottom-left corner (0,0). Red numbered lines = saw cuts in order, each edge to edge.
- Coloured dimensions belong to the part of that colour: its width and height, and its position from the sheet edges. Raked parts: corner coordinates at each corner.
- Red hatch = waste. Labels = panel + piece mark on the manufacture drawing.

REVISIONS

REV	DATE	DESCRIPTION
C01	13.09.26	Construction issue



TLS TIMBER FRAME

Design & Manufacture

Scan: 3D model + drawings



CLIENT	PROJECT
MP Adams	MP Adams Plot 3, Eckington


DRAWING TITLE
PIR CUTTING - GROUND FLOOR - SHEET 8 OF 21

PIR 120mm 1200x2400 | Ground Floor

SCALE	SIZE	DATE	DRAWN
NTS	A3	13.09.26	TS

STATUS	DRAWING No.	REV
CONSTRUCTION	P3-CP-PIR-01 / 08	C01

Do not scale. All dimensions in mm. Check all dimensions on site.

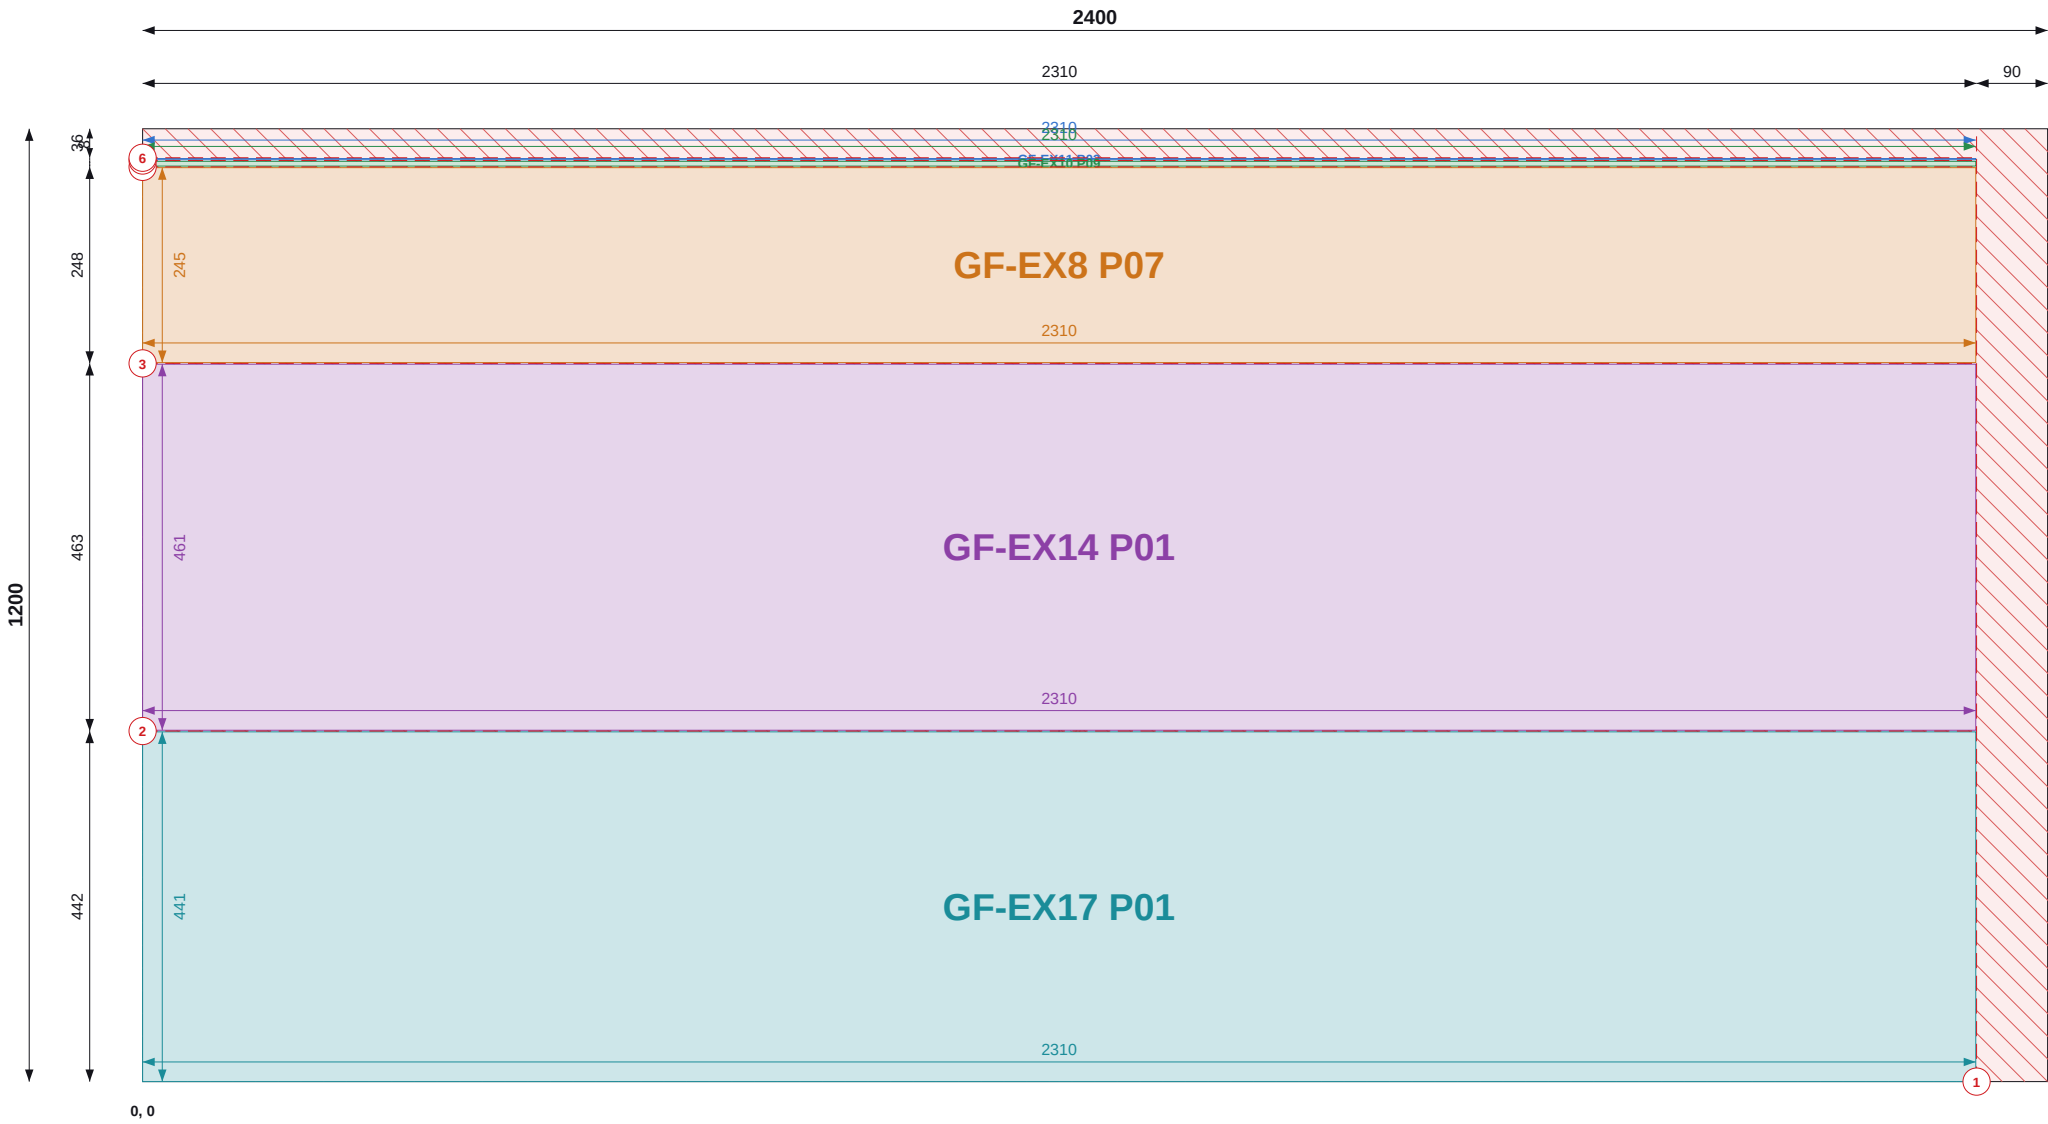

Top / left chains = saw cut positions (to cut centres). Coloured = part size and position.

SHEET 9 OF 21

THIS SHEET

Item	Value
Parts	5
Used / waste	92.6% / 0.21 m2
Reusable offcuts	0
Saw cuts / shared	6 / 4

PIECES (POSITION = BOTTOM-LEFT CORNER)

Label	Size	X, Y
GF-EX11 P03	1 x 2310	0, 1161
GF-EX10 P09	6 x 2310	0, 1153
GF-EX8 P07	245 x 2310	0, 905
GF-EX14 P01	461 x 2310	0, 443
GF-EX17 P01	441 x 2310	0, 0

NOTES

- Cut from PIR 120mm 1200x2400, 2mm saw kerf. Viewed on the face; dimensions from the sheet's bottom-left corner (0,0). Red numbered lines = saw cuts in order, each edge to edge.
- Coloured dimensions belong to the part of that colour: its width and height, and its position from the sheet edges. Raked parts: corner coordinates at each corner.
- Red hatch = waste. Labels = panel + piece mark on the manufacture drawing.

REVISIONS

REV	DATE	DESCRIPTION
C01	13.09.26	Construction issue



TLS TIMBER FRAME

Design & Manufacture

Scan: 3D model + drawings



CLIENT	PROJECT
MP Adams	MP Adams Plot 3, Eckington


DRAWING TITLE
PIR CUTTING - GROUND FLOOR - SHEET 9 OF 21

PIR 120mm 1200x2400 | Ground Floor

SCALE	SIZE	DATE	DRAWN
NTS	A3	13.09.26	TS

STATUS	DRAWING No.	REV
CONSTRUCTION	P3-CP-PIR-01 / 09	C01

Do not scale. All dimensions in mm. Check all dimensions on site.

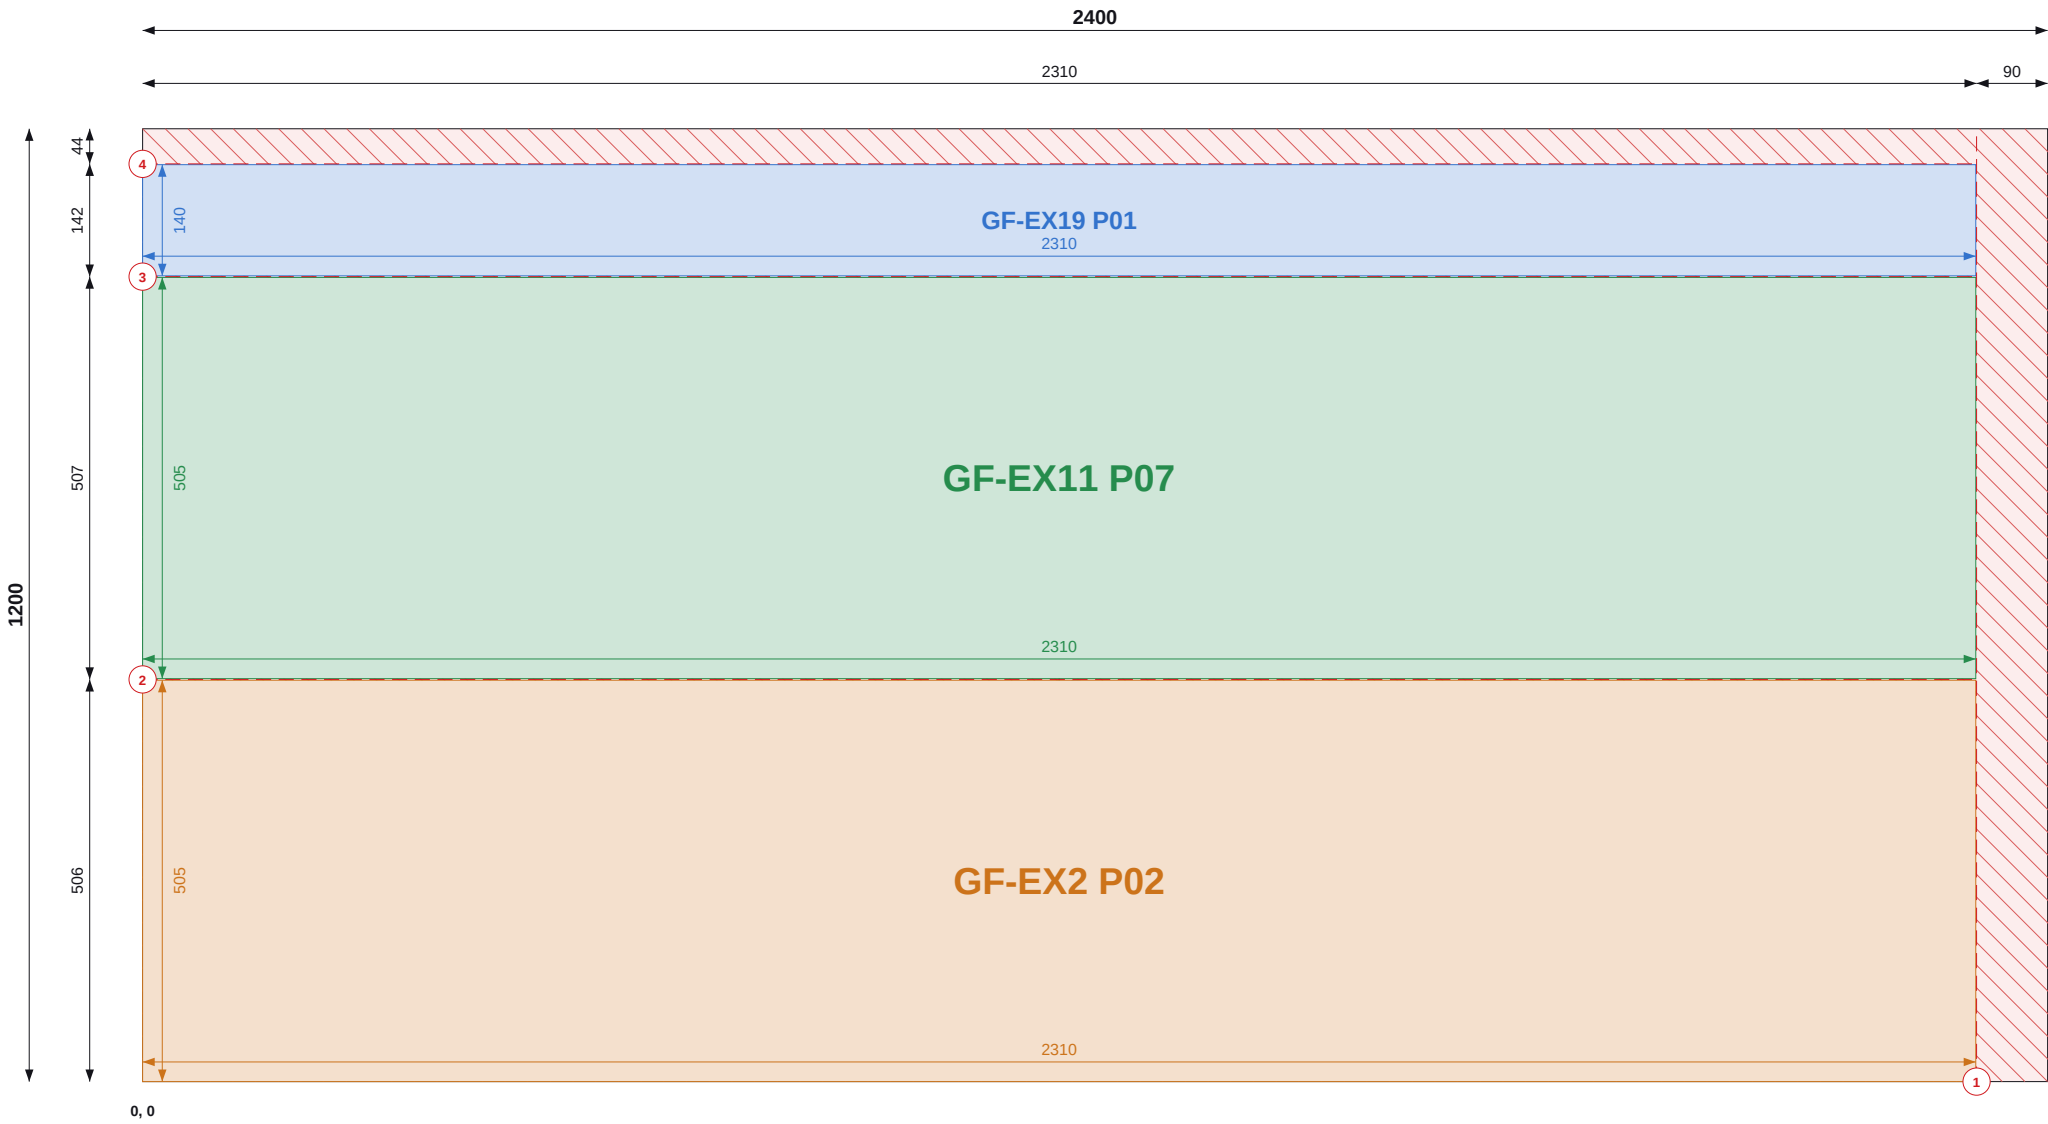

Top / left chains = saw cut positions (to cut centres). Coloured = part size and position.

SHEET 10 OF 21

THIS SHEET

Item	Value
Parts	3
Used / waste	92.3% / 0.22 m2
Reusable offcuts	0
Saw cuts / shared	4 / 2

PIECES (POSITION = BOTTOM-LEFT CORNER)

Label	Size	X, Y
GF-EX19 P01	140 x 2310	0, 1015
GF-EX11 P07	505 x 2310	0, 507
GF-EX2 P02	505 x 2310	0, 0

NOTES

1. Cut from PIR 120mm 1200x2400, 2mm saw kerf. Viewed on the face; dimensions from the sheet's bottom-left corner (0,0). Red numbered lines = saw cuts in order, each edge to edge.
2. Coloured dimensions belong to the part of that colour: its width and height, and its position from the sheet edges. Raked parts: corner coordinates at each corner.
3. Red hatch = waste. Labels = panel + piece mark on the manufacture drawing.

REVISIONS

REV	DATE	DESCRIPTION
C01	13.09.26	Construction issue



TLS TIMBER FRAME
Design & Manufacture
Scan: 3D model + drawings



CLIENT MP Adams	PROJECT MP Adams Plot 3, Eckington
--------------------	---------------------------------------


DRAWING TITLE
PIR CUTTING - GROUND FLOOR - SHEET 10 OF 21

PIR 120mm 1200x2400 | Ground Floor

SCALE NTS	SIZE A3	DATE 13.09.26	DRAWN TS
--------------	------------	------------------	-------------

STATUS CONSTRUCTION	DRAWING No. P3-CP-PIR-01 / 10	REV C01
-------------------------------	---	-------------------

Do not scale. All dimensions in mm. Check all dimensions on site.

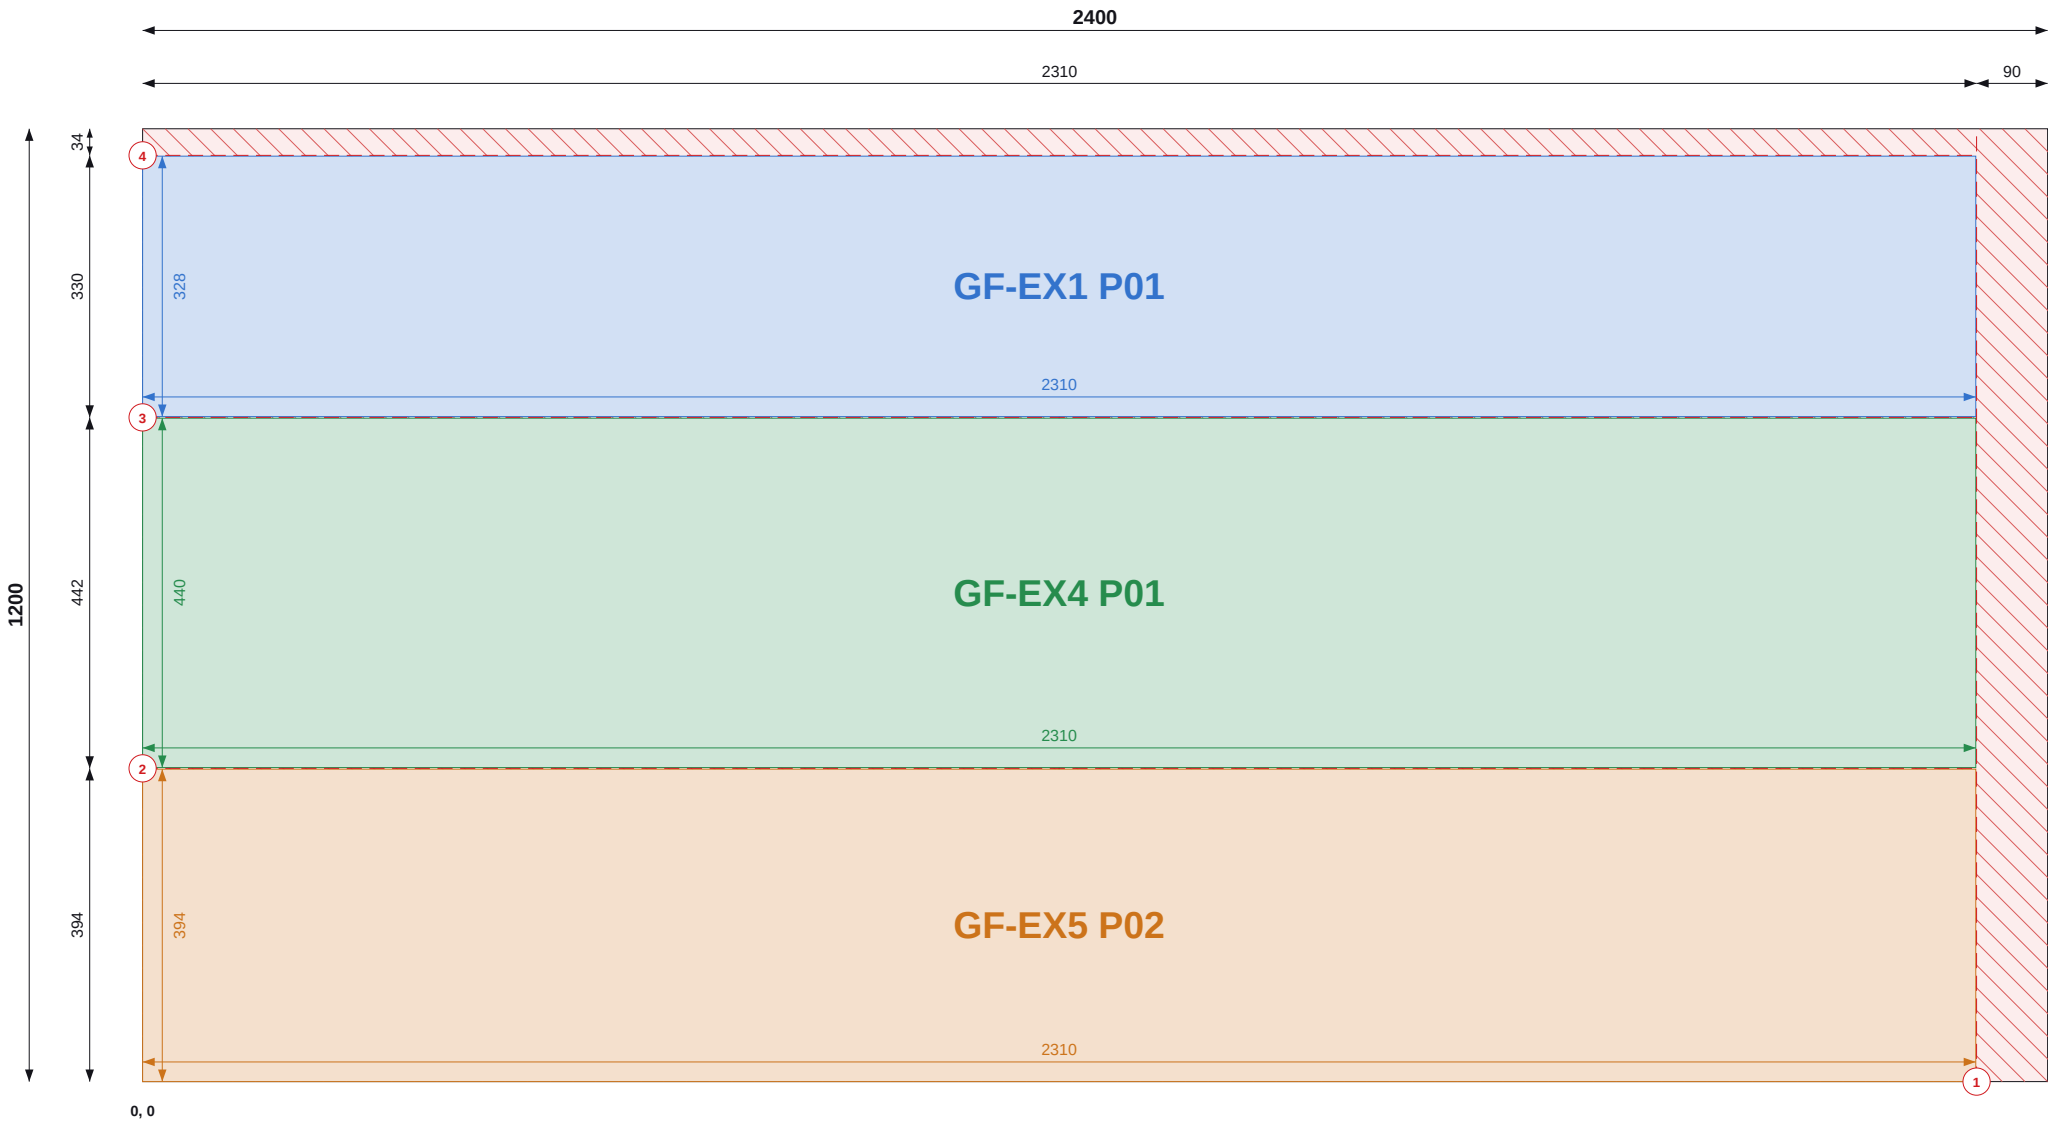

Top / left chains = saw cut positions (to cut centres). Coloured = part size and position.

SHEET 11 OF 21

THIS SHEET

Item	Value
Parts	3
Used / waste	93.1% / 0.20 m2
Reusable offcuts	0
Saw cuts / shared	4 / 2

PIECES (POSITION = BOTTOM-LEFT CORNER)

Label	Size	X, Y
GF-EX1 P01	328 x 2310	0, 837
GF-EX4 P01	440 x 2310	0, 396
GF-EX5 P02	394 x 2310	0, 0

NOTES

- Cut from PIR 120mm 1200x2400, 2mm saw kerf. Viewed on the face; dimensions from the sheet's bottom-left corner (0,0). Red numbered lines = saw cuts in order, each edge to edge.
- Coloured dimensions belong to the part of that colour: its width and height, and its position from the sheet edges. Raked parts: corner coordinates at each corner.
- Red hatch = waste. Labels = panel + piece mark on the manufacture drawing.

REVISIONS

REV	DATE	DESCRIPTION
C01	13.09.26	Construction issue



TLS TIMBER FRAME

Design & Manufacture

Scan: 3D model + drawings



CLIENT	PROJECT
MP Adams	MP Adams Plot 3, Eckington


DRAWING TITLE
PIR CUTTING - GROUND FLOOR - SHEET 11 OF 21

PIR 120mm 1200x2400 | Ground Floor

SCALE	SIZE	DATE	DRAWN
NTS	A3	13.09.26	TS

STATUS	DRAWING No.	REV
CONSTRUCTION	P3-CP-PIR-01 / 11	C01

Do not scale. All dimensions in mm. Check all dimensions on site.

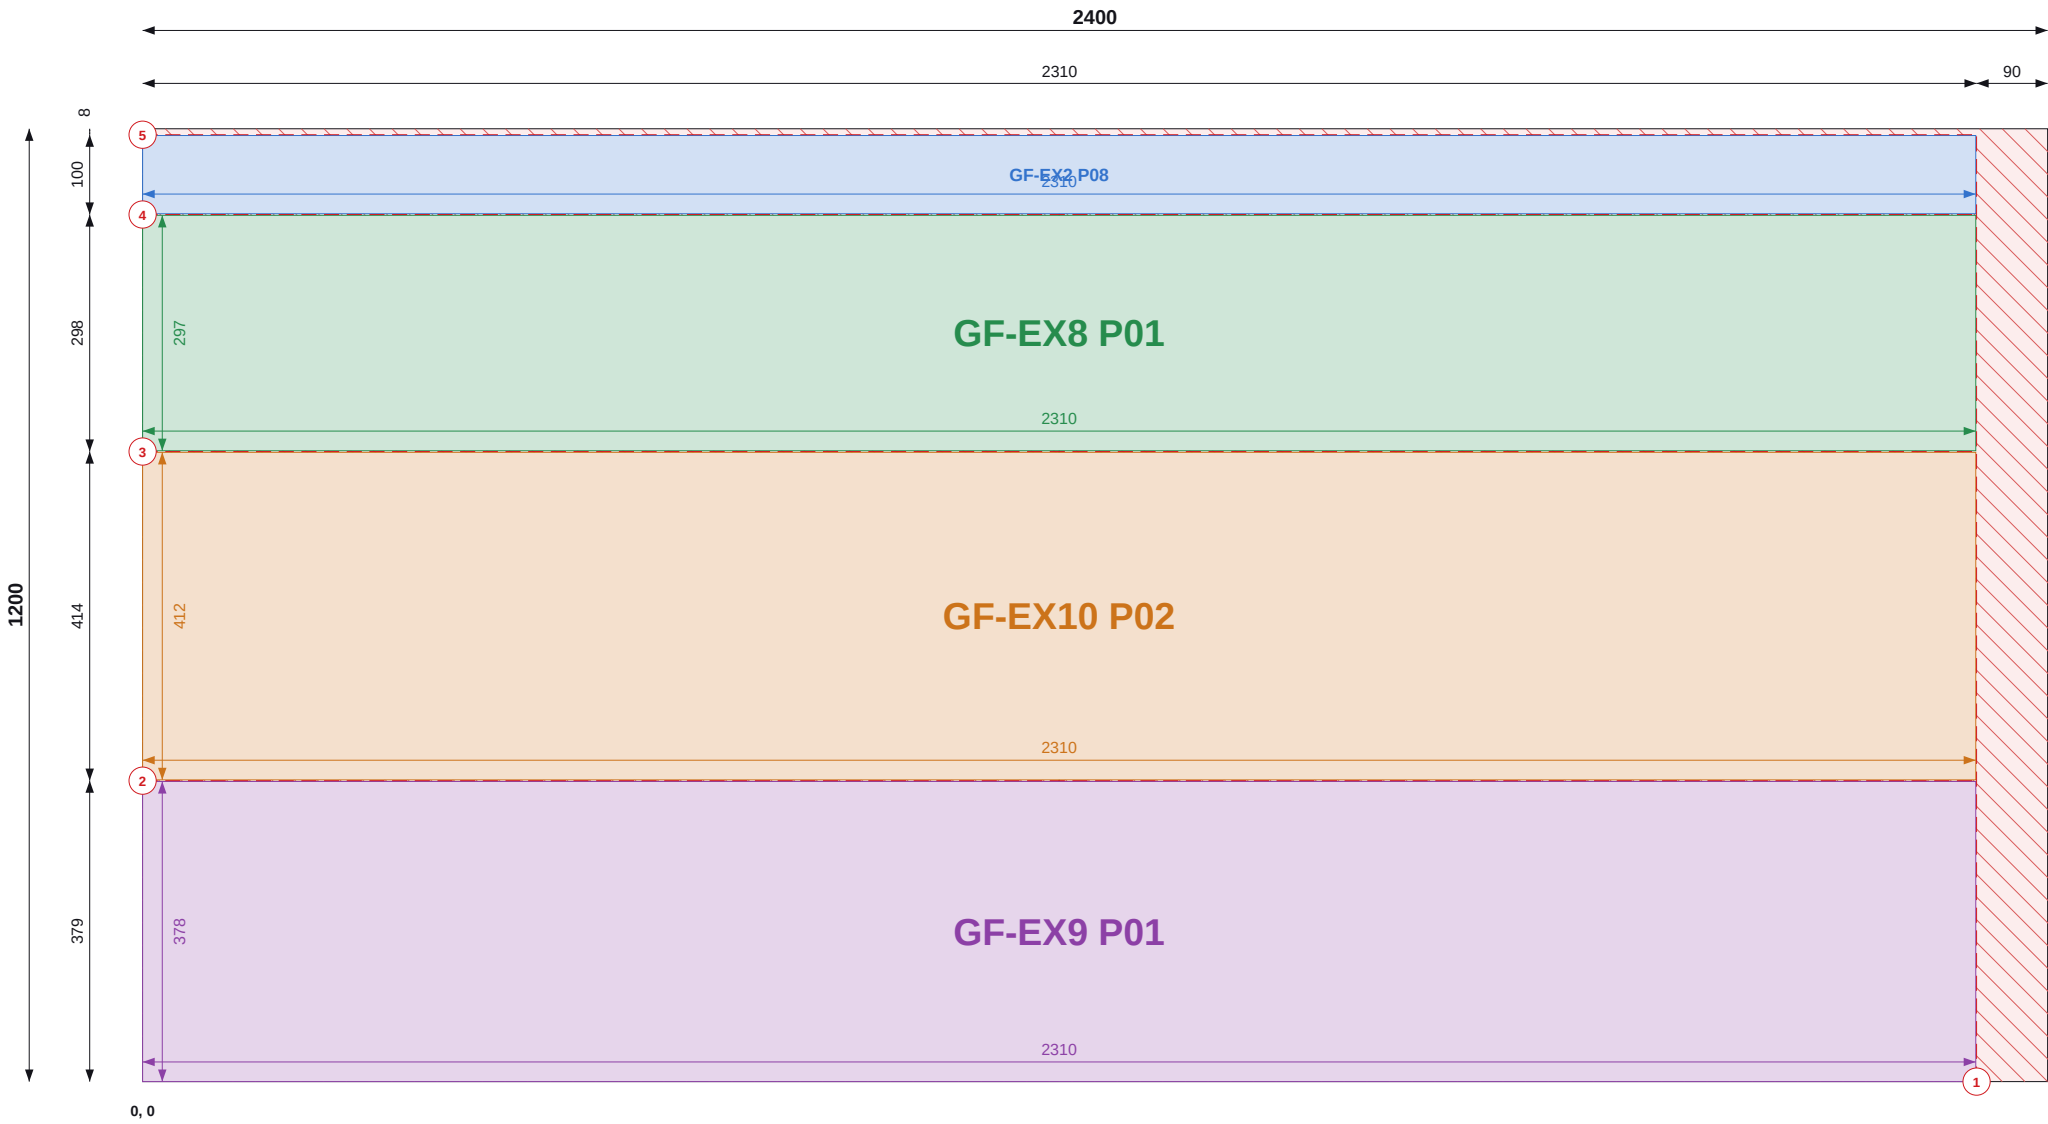

Top / left chains = saw cut positions (to cut centres). Coloured = part size and position.

SHEET 12 OF 21

THIS SHEET

Item	Value
Parts	4
Used / waste	95.1% / 0.14 m2
Reusable offcuts	0
Saw cuts / shared	5 / 3

PIECES (POSITION = BOTTOM-LEFT CORNER)

Label	Size	X, Y
GF-EX2 P08	99 x 2310	0, 1093
GF-EX8 P01	297 x 2310	0, 794
GF-EX10 P02	412 x 2310	0, 380
GF-EX9 P01	378 x 2310	0, 0

NOTES

- Cut from PIR 120mm 1200x2400, 2mm saw kerf. Viewed on the face; dimensions from the sheet's bottom-left corner (0,0). Red numbered lines = saw cuts in order, each edge to edge.
- Coloured dimensions belong to the part of that colour: its width and height, and its position from the sheet edges. Raked parts: corner coordinates at each corner.
- Red hatch = waste. Labels = panel + piece mark on the manufacture drawing.

REVISIONS

REV	DATE	DESCRIPTION
C01	13.09.26	Construction issue



TLS TIMBER FRAME

Design & Manufacture

Scan: 3D model + drawings




CLIENT	PROJECT
MP Adams	MP Adams Plot 3, Eckington

DRAWING TITLE			
PIR CUTTING - GROUND FLOOR - SHEET 12 OF 21			
PIR 120mm 1200x2400 Ground Floor			

SCALE	SIZE	DATE	DRAWN
NTS	A3	13.09.26	TS

STATUS	DRAWING No.	REV
CONSTRUCTION	P3-CP-PIR-01 / 12	C01

Do not scale. All dimensions in mm. Check all dimensions on site.

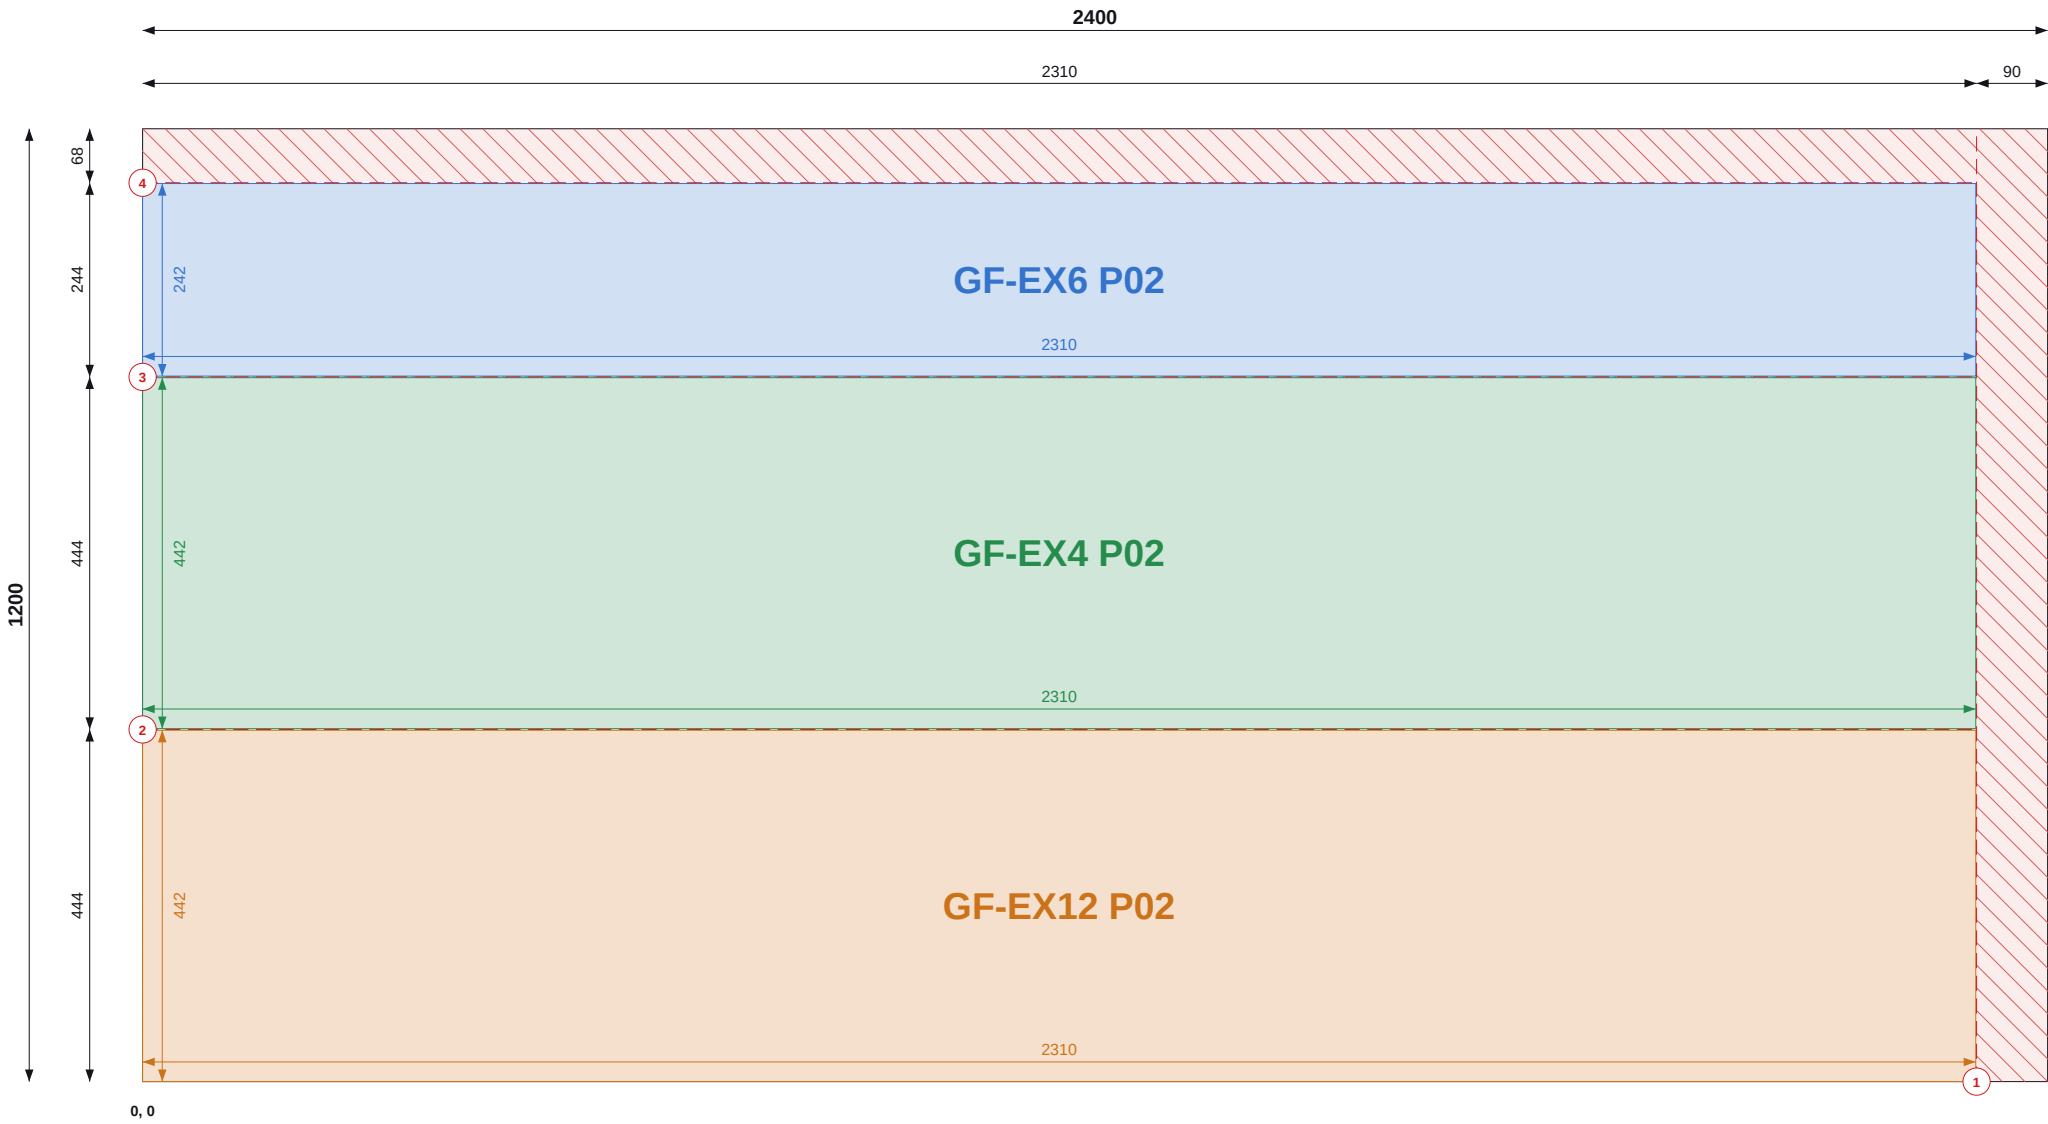

Top / left chains = saw cut positions (to cut centres). Coloured = part size and position.

SHEET 13 OF 21

THIS SHEET

Item	Value
Parts	3
Used / waste	90.4% / 0.28 m2
Reusable offcuts	0
Saw cuts / shared	4 / 2

PIECES (POSITION = BOTTOM-LEFT CORNER)

Label	Size	X, Y
GF-EX6 P02	242 x 2310	0, 889
GF-EX4 P02	442 x 2310	0, 444
GF-EX12 P02	442 x 2310	0, 0

NOTES

1. Cut from PIR 120mm 1200x2400, 2mm saw kerf. Viewed on the face; dimensions from the sheet's bottom-left corner (0,0). Red numbered lines = saw cuts in order, each edge to edge.
2. Coloured dimensions belong to the part of that colour: its width and height, and its position from the sheet edges. Raked parts: corner coordinates at each corner.
3. Red hatch = waste. Labels = panel + piece mark on the manufacture drawing.

REVISIONS

REV	DATE	DESCRIPTION
C01	13.09.26	Construction issue



TLS TIMBER FRAME

Design & Manufacture

Scan: 3D model + drawings




CLIENT	PROJECT
MP Adams	MP Adams Plot 3, Eckington

DRAWING TITLE			
PIR CUTTING - GROUND FLOOR - SHEET 13 OF 21			
PIR 120mm 1200x2400 Ground Floor			

SCALE	SIZE	DATE	DRAWN
NTS	A3	13.09.26	TS

STATUS	DRAWING No.	REV
CONSTRUCTION	P3-CP-PIR-01 / 13	C01

Do not scale. All dimensions in mm. Check all dimensions on site.

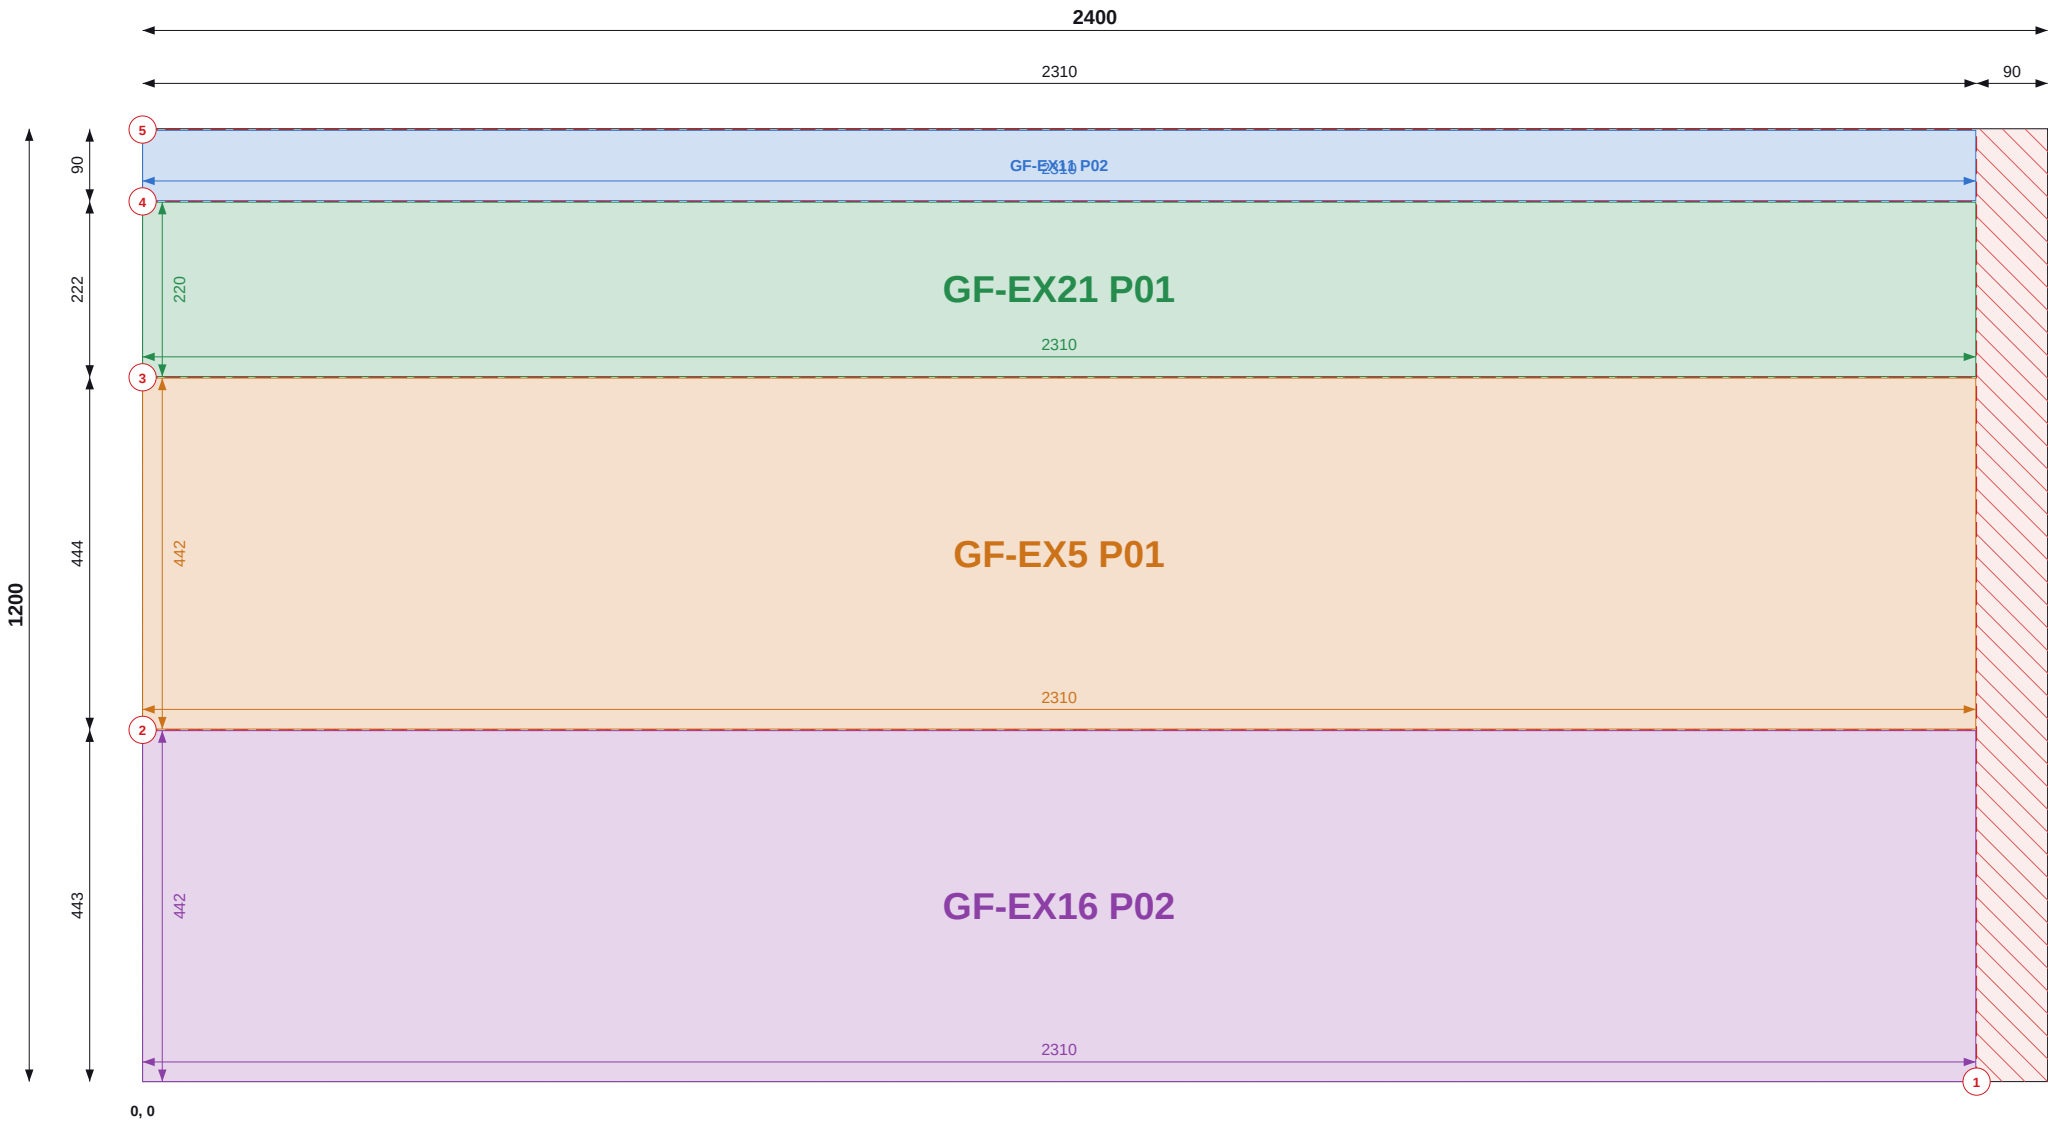

Top / left chains = saw cut positions (to cut centres). Coloured = part size and position.

SHEET 14 OF 21

THIS SHEET

Item	Value
Parts	4
Used / waste	95.6% / 0.13 m2
Reusable offcuts	0
Saw cuts / shared	5 / 3

PIECES (POSITION = BOTTOM-LEFT CORNER)

Label	Size	X, Y
GF-EX11 P02	89 x 2310	0, 1109
GF-EX21 P01	220 x 2310	0, 888
GF-EX5 P01	442 x 2310	0, 444
GF-EX16 P02	442 x 2310	0, 0

NOTES

- Cut from PIR 120mm 1200x2400, 2mm saw kerf. Viewed on the face; dimensions from the sheet's bottom-left corner (0,0). Red numbered lines = saw cuts in order, each edge to edge.
- Coloured dimensions belong to the part of that colour: its width and height, and its position from the sheet edges. Raked parts: corner coordinates at each corner.
- Red hatch = waste. Labels = panel + piece mark on the manufacture drawing.

REVISIONS

REV	DATE	DESCRIPTION
C01	13.09.26	Construction issue



TLS TIMBER FRAME

Design & Manufacture

Scan: 3D model + drawings



CLIENT	PROJECT
MP Adams	MP Adams Plot 3, Eckington


DRAWING TITLE
PIR CUTTING - GROUND FLOOR - SHEET 14 OF 21

PIR 120mm 1200x2400 | Ground Floor

SCALE	SIZE	DATE	DRAWN
NTS	A3	13.09.26	TS

STATUS	DRAWING No.	REV
CONSTRUCTION	P3-CP-PIR-01 / 14	C01

Do not scale. All dimensions in mm. Check all dimensions on site.

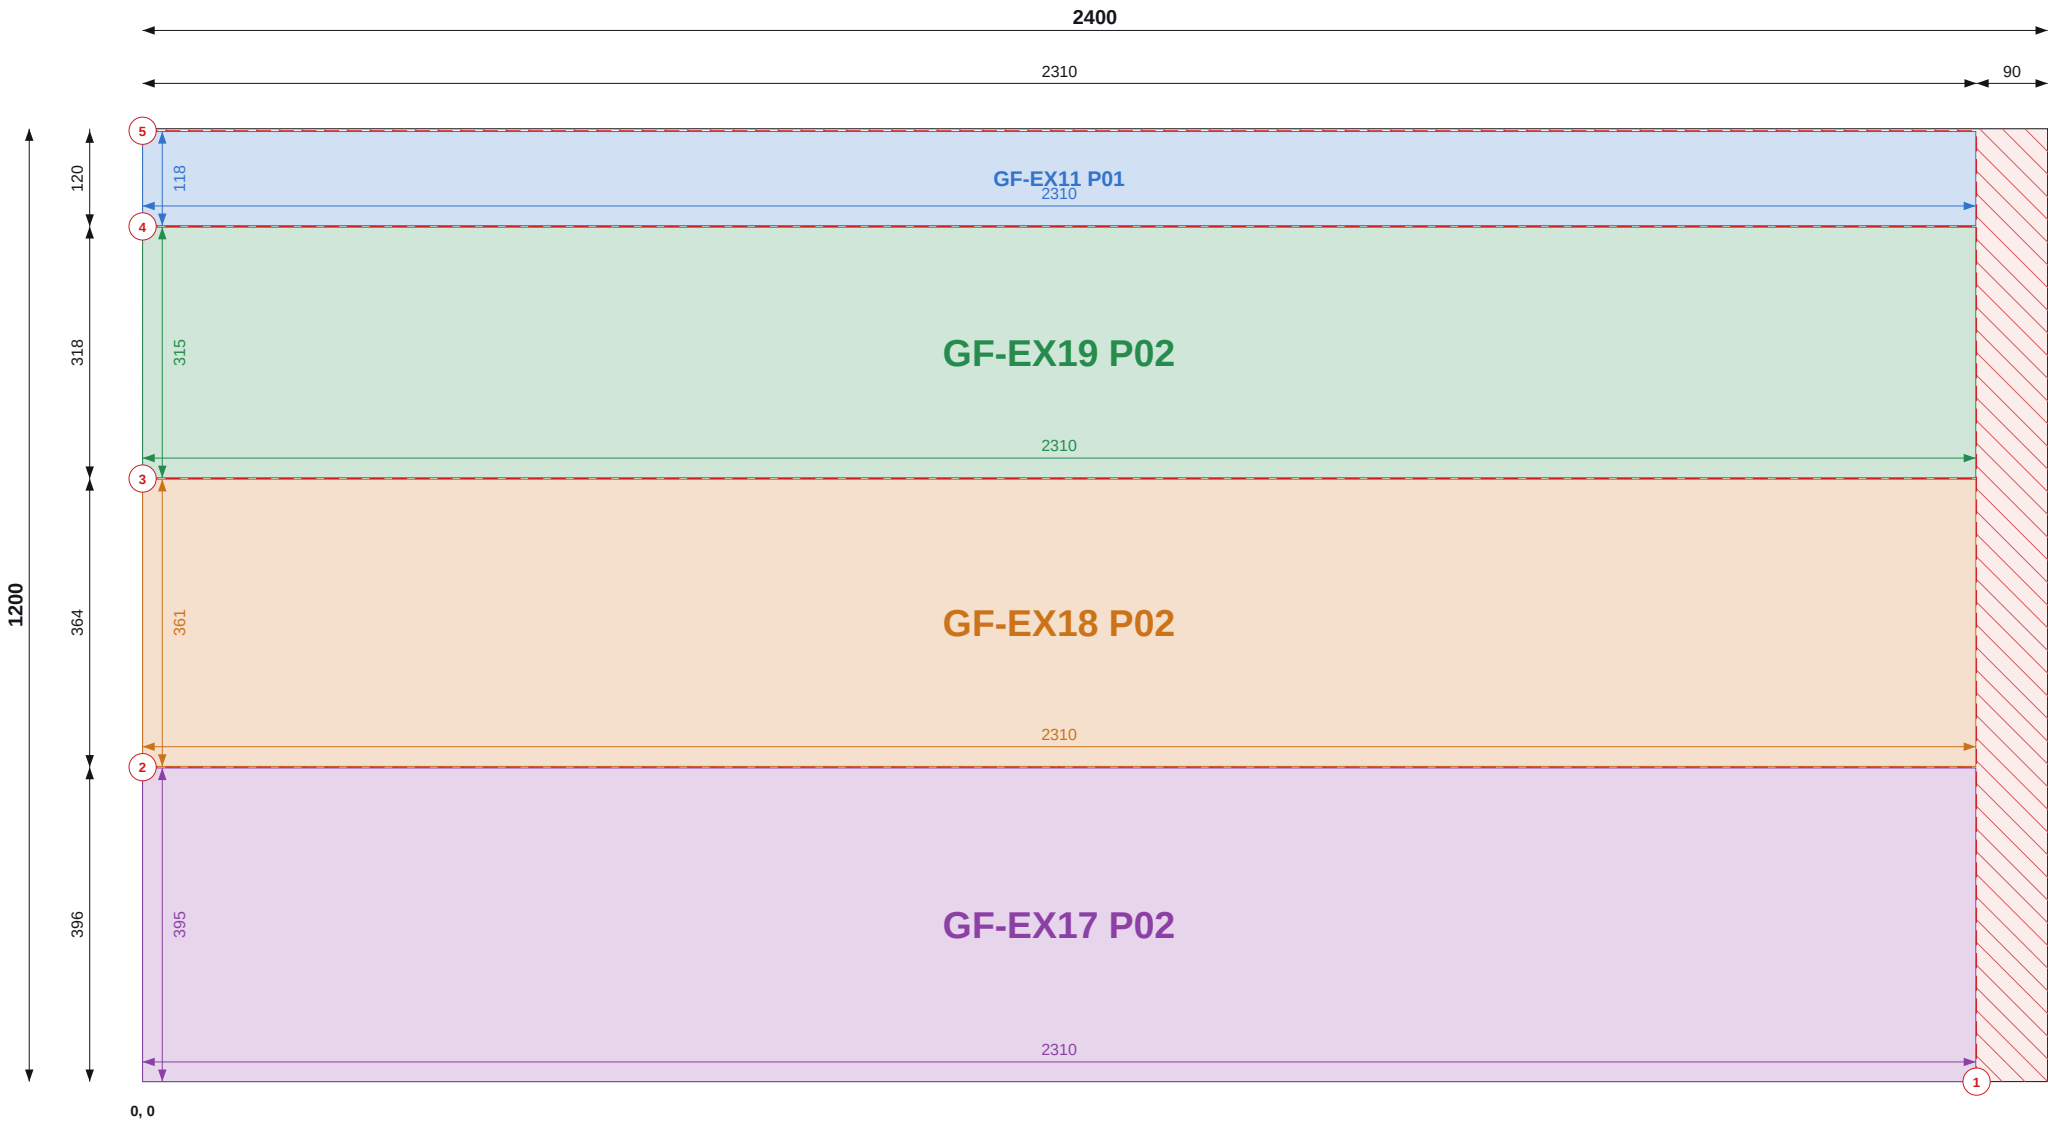

Top / left chains = saw cut positions (to cut centres). Coloured = part size and position.

SHEET 15 OF 21

THIS SHEET

Item	Value
Parts	4
Used / waste	95.5% / 0.13 m2
Reusable offcuts	0
Saw cuts / shared	5 / 3

PIECES (POSITION = BOTTOM-LEFT CORNER)

Label	Size	X, Y
GF-EX11 P01	118 x 2310	0, 1078
GF-EX19 P02	315 x 2310	0, 760
GF-EX18 P02	361 x 2310	0, 397
GF-EX17 P02	395 x 2310	0, 0

NOTES

- Cut from PIR 120mm 1200x2400, 2mm saw kerf. Viewed on the face; dimensions from the sheet's bottom-left corner (0,0). Red numbered lines = saw cuts in order, each edge to edge.
- Coloured dimensions belong to the part of that colour: its width and height, and its position from the sheet edges. Raked parts: corner coordinates at each corner.
- Red hatch = waste. Labels = panel + piece mark on the manufacture drawing.

REVISIONS

REV	DATE	DESCRIPTION
C01	13.09.26	Construction issue



TLS TIMBER FRAME
Design & Manufacture
Scan: 3D model + drawings



CLIENT MP Adams	PROJECT MP Adams Plot 3, Eckington
--------------------	---------------------------------------


DRAWING TITLE
PIR CUTTING - GROUND FLOOR - SHEET 15 OF 21

PIR 120mm 1200x2400 | Ground Floor

SCALE NTS	SIZE A3	DATE 13.09.26	DRAWN TS
--------------	------------	------------------	-------------

STATUS CONSTRUCTION	DRAWING No. P3-CP-PIR-01 / 15	REV C01
-------------------------------	---	-------------------

Do not scale. All dimensions in mm. Check all dimensions on site.

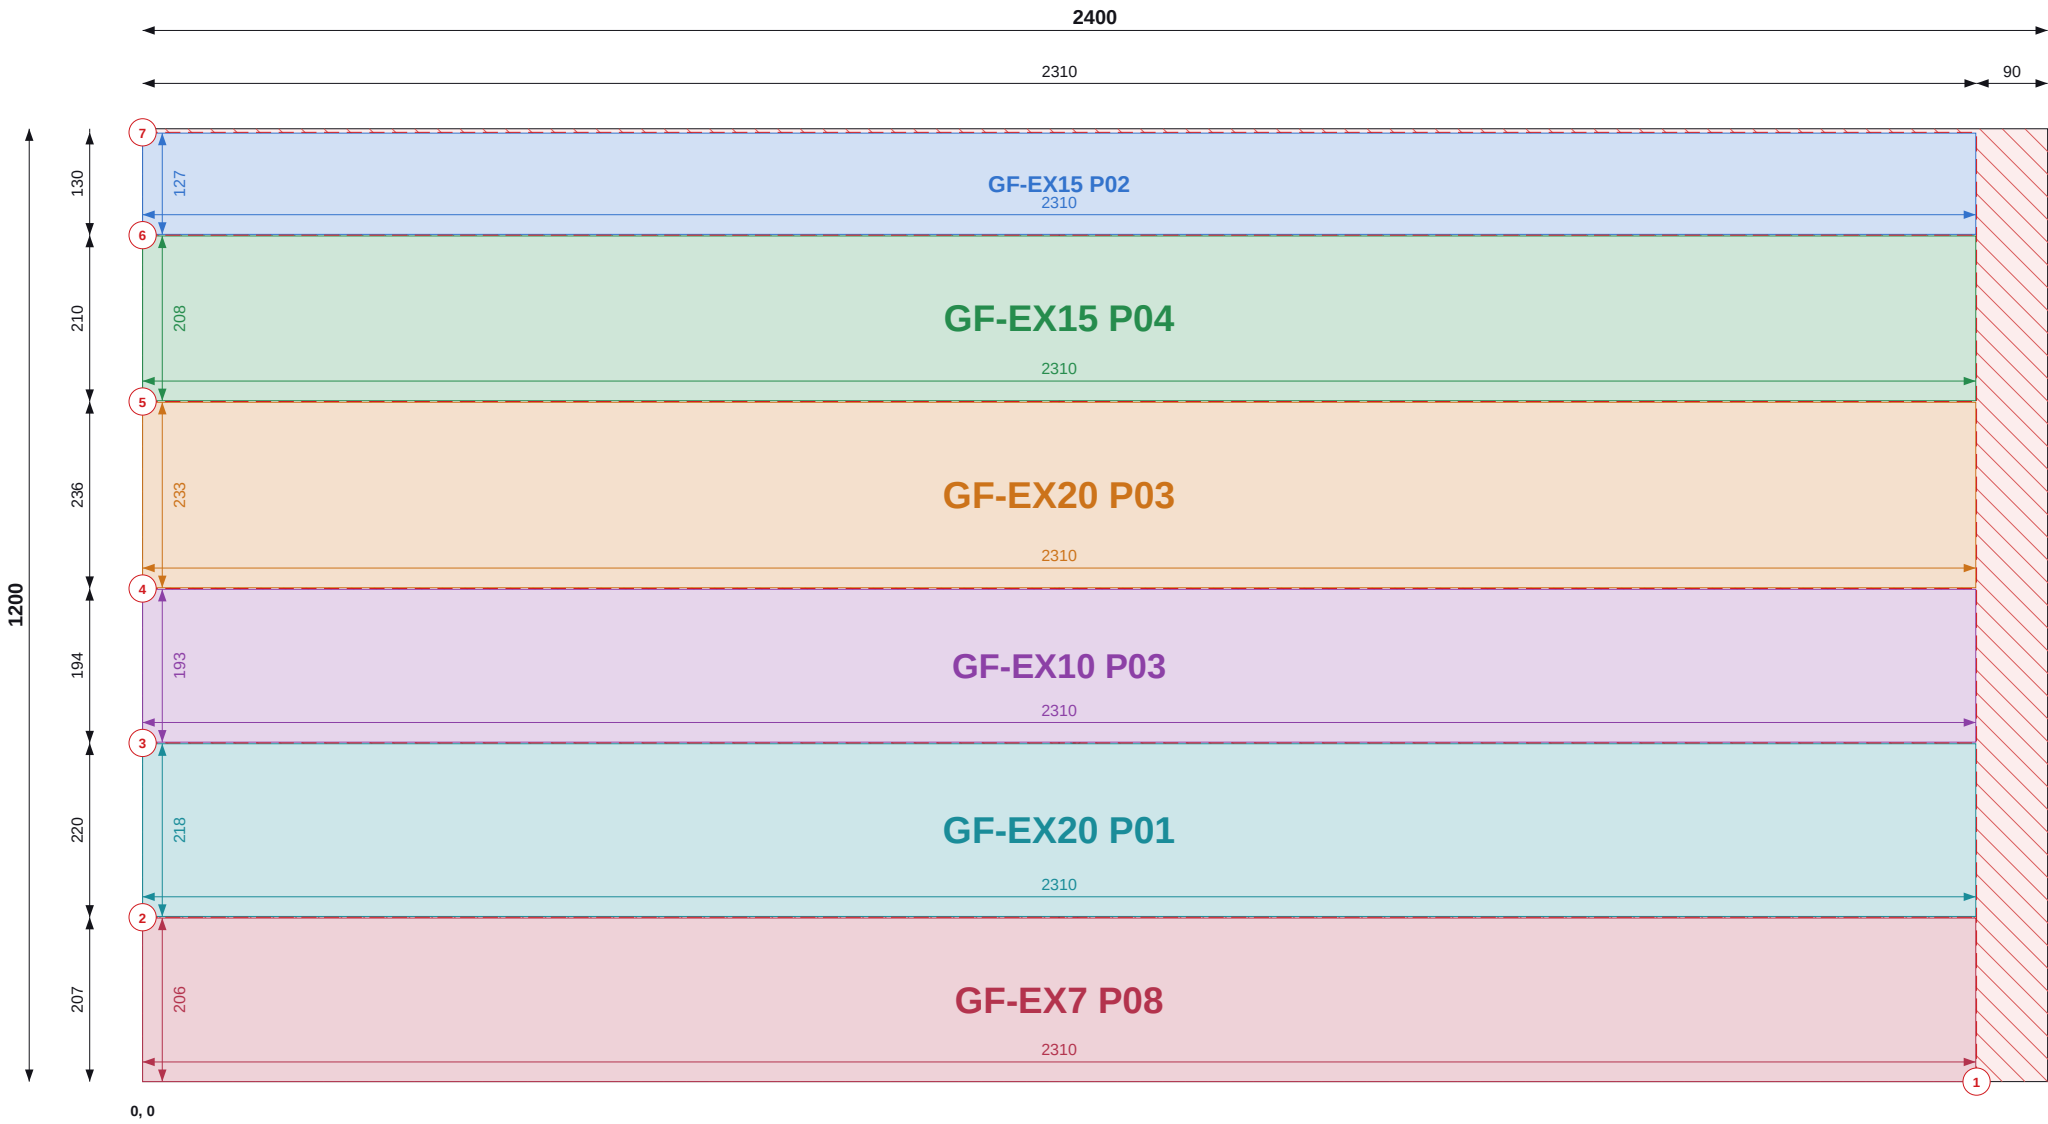

Top / left chains = saw cut positions (to cut centres). Coloured = part size and position.

SHEET 16 OF 21

THIS SHEET

Item	Value
Parts	6
Used / waste	95.0% / 0.14 m2
Reusable offcuts	0
Saw cuts / shared	7 / 5

PIECES (POSITION = BOTTOM-LEFT CORNER)

Label	Size	X, Y
GF-EX15 P02	127 x 2310	0, 1067
GF-EX15 P04	208 x 2310	0, 857
GF-EX20 P03	233 x 2310	0, 622
GF-EX10 P03	193 x 2310	0, 427
GF-EX20 P01	218 x 2310	0, 208
GF-EX7 P08	206 x 2310	0, 0

NOTES

- Cut from PIR 120mm 1200x2400, 2mm saw kerf. Viewed on the face; dimensions from the sheet's bottom-left corner (0,0). Red numbered lines = saw cuts in order, each edge to edge.
- Coloured dimensions belong to the part of that colour: its width and height, and its position from the sheet edges. Raked parts: corner coordinates at each corner.
- Red hatch = waste. Labels = panel + piece mark on the manufacture drawing.

REVISIONS

REV	DATE	DESCRIPTION
C01	13.09.26	Construction issue



TLS TIMBER FRAME

Design & Manufacture

Scan: 3D model + drawings



CLIENT	PROJECT
MP Adams	MP Adams Plot 3, Eckington


DRAWING TITLE
PIR CUTTING - GROUND FLOOR - SHEET 16 OF 21

PIR 120mm 1200x2400 | Ground Floor

SCALE	SIZE	DATE	DRAWN
NTS	A3	13.09.26	TS

STATUS	DRAWING No.	REV
CONSTRUCTION	P3-CP-PIR-01 / 16	C01

Do not scale. All dimensions in mm. Check all dimensions on site.

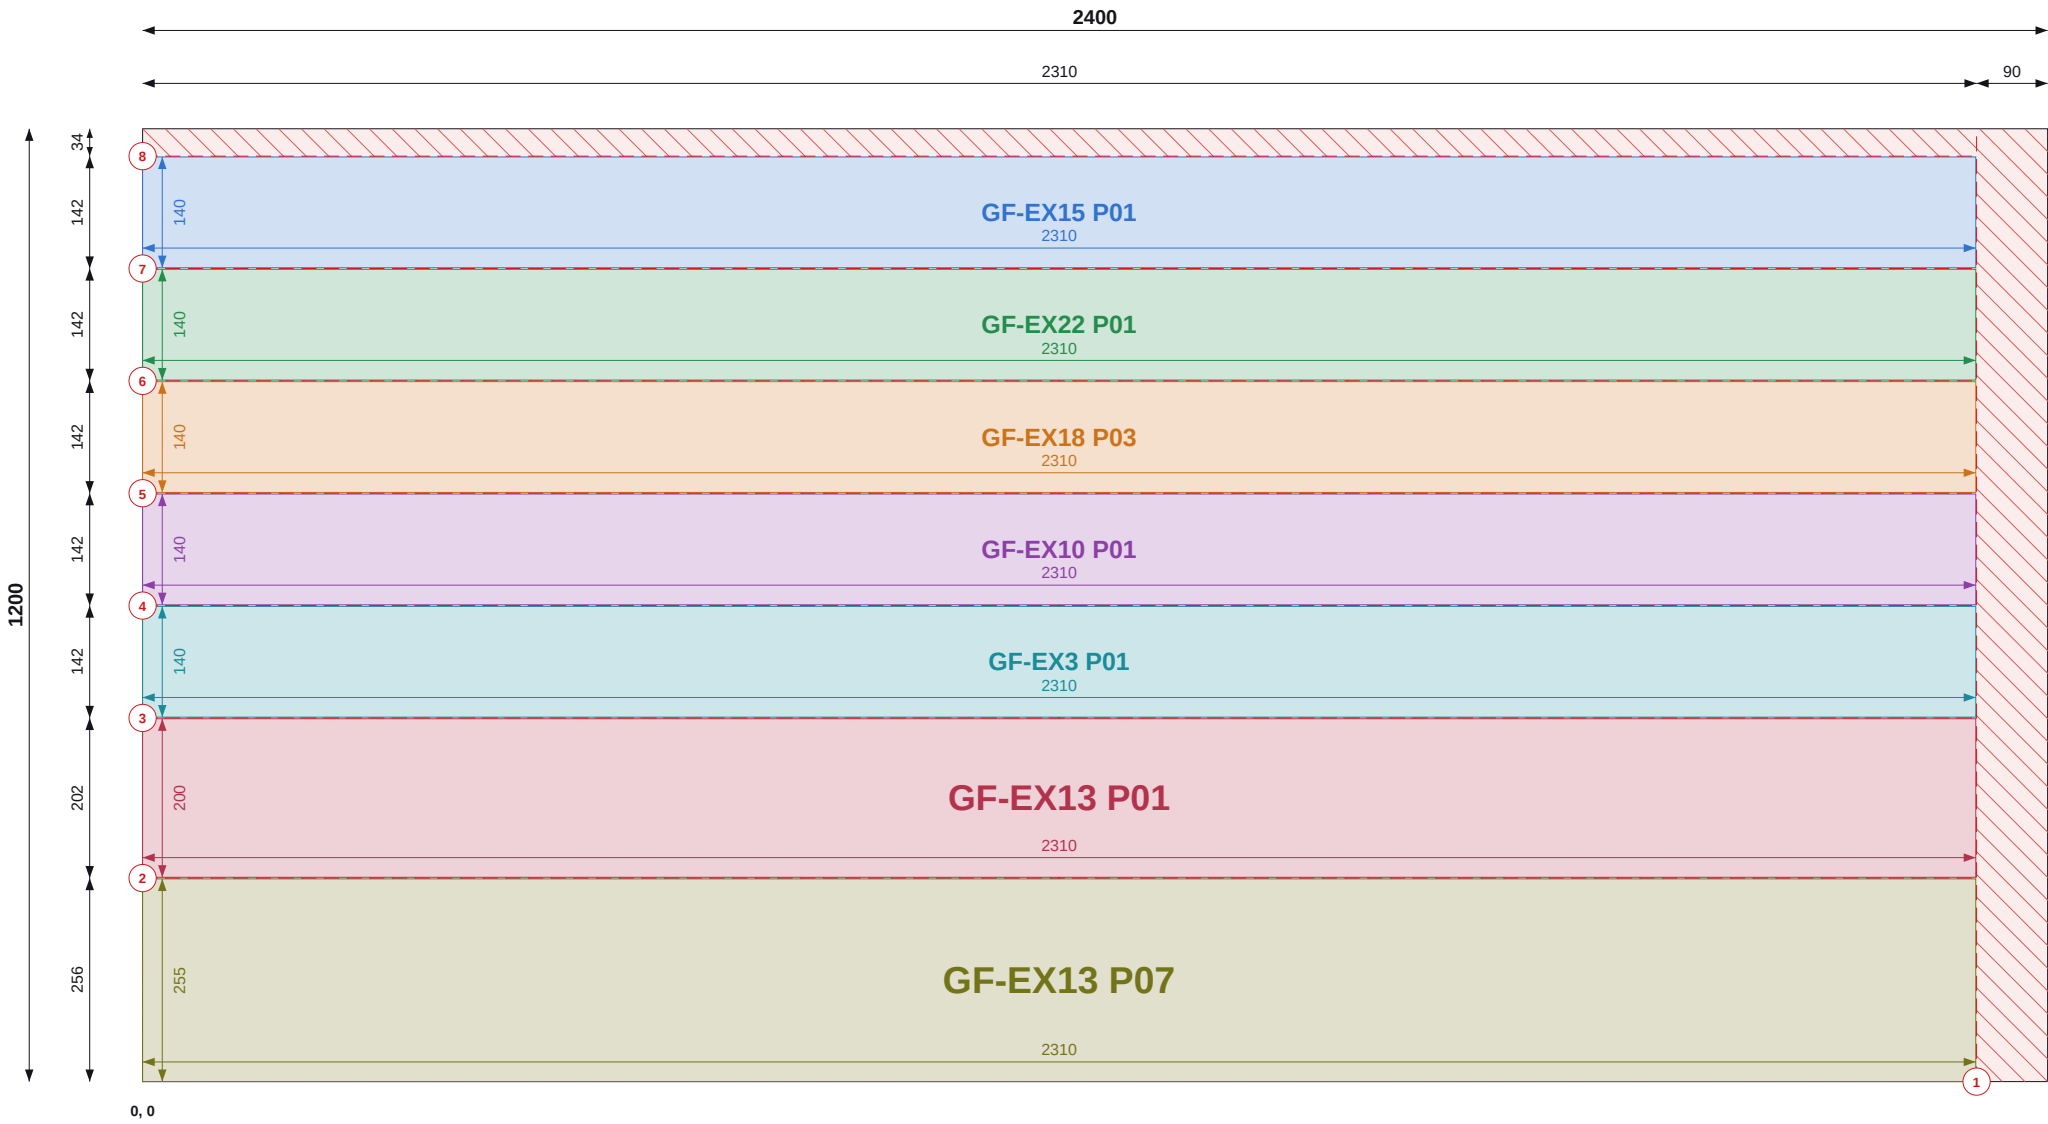

SHEET 17 OF 21

THIS SHEET

Item	Value
Parts	7
Used / waste	92.4% / 0.22 m2
Reusable offcuts	0
Saw cuts / shared	8 / 6

PIECES (POSITION = BOTTOM-LEFT CORNER)

Label	Size	X, Y
GF-EX15 P01	140 x 2310	0, 1025
GF-EX22 P01	140 x 2310	0, 883
GF-EX18 P03	140 x 2310	0, 742
GF-EX10 P01	140 x 2310	0, 600
GF-EX3 P01	140 x 2310	0, 459
GF-EX13 P01	200 x 2310	0, 257
GF-EX13 P07	255 x 2310	0, 0

NOTES

- Cut from PIR 120mm 1200x2400, 2mm saw kerf. Viewed on the face; dimensions from the sheet's bottom-left corner (0,0). Red numbered lines = saw cuts in order, each edge to edge.
- Coloured dimensions belong to the part of that colour: its width and height, and its position from the sheet edges. Raked parts: corner coordinates at each corner.
- Red hatch = waste. Labels = panel + piece mark on the manufacture drawing.

REVISIONS

REV	DATE	DESCRIPTION
C01	13.09.26	Construction issue



TLS TIMBER FRAME

Design & Manufacture

Scan: 3D model + drawings




CLIENT	PROJECT
MP Adams	MP Adams Plot 3, Eckington

DRAWING TITLE			
PIR CUTTING - GROUND FLOOR - SHEET 17 OF 21			
PIR 120mm 1200x2400 Ground Floor			

SCALE	SIZE	DATE	DRAWN
NTS	A3	13.09.26	TS

STATUS	DRAWING No.	REV
CONSTRUCTION	P3-CP-PIR-01 / 17	C01

Do not scale. All dimensions in mm. Check all dimensions on site.

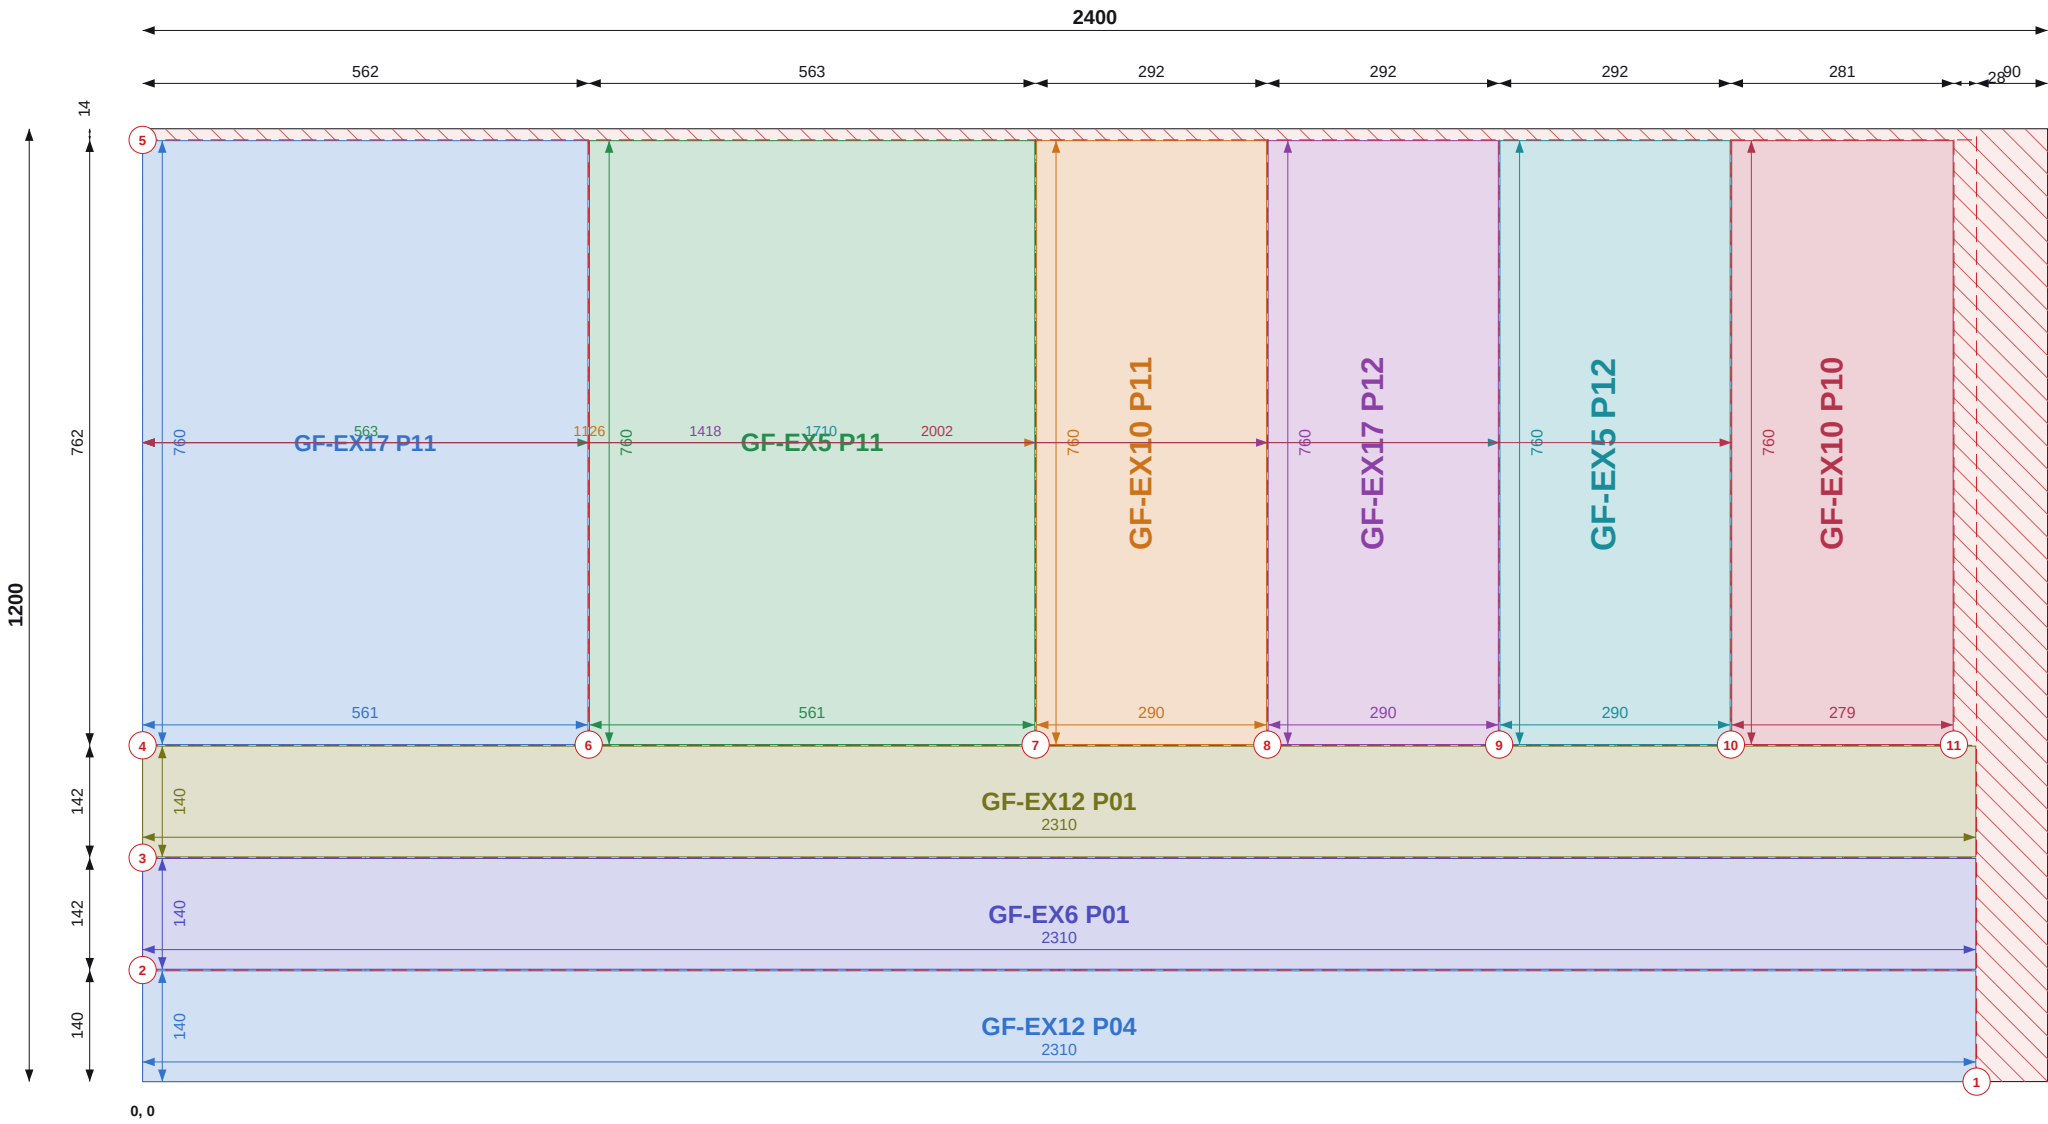

Top / left chains = saw cut positions (to cut centres). Coloured = part size and position.

SHEET 18 OF 21

THIS SHEET

Item	Value
Parts	9
Used / waste	93.5% / 0.19 m2
Reusable offcuts	0
Saw cuts / shared	11 / 8

PIECES (POSITION = BOTTOM-LEFT CORNER)

Label	Size	X, Y
GF-EX17 P11	561 x 760	0, 425
GF-EX5 P11	561 x 760	563, 425
GF-EX10 P11	290 x 760	1126, 425
GF-EX17 P12	290 x 760	1418, 425
GF-EX5 P12	290 x 760	1710, 425
GF-EX10 P10	279 x 760	2002, 425
GF-EX12 P01	140 x 2310	0, 283
GF-EX6 P01	140 x 2310	0, 142
GF-EX12 P04	140 x 2310	0, 0

NOTES

- Cut from PIR 120mm 1200x2400, 2mm saw kerf. Viewed on the face; dimensions from the sheet's bottom-left corner (0,0). Red numbered lines = saw cuts in order, each edge to edge.
- Coloured dimensions belong to the part of that colour: its width and height, and its position from the sheet edges. Raked parts: corner coordinates at each corner.
- Red hatch = waste. Labels = panel + piece mark on the manufacture drawing.

REVISIONS

REV	DATE	DESCRIPTION
C01	13.09.26	Construction issue



TLS TIMBER FRAME

Design & Manufacture

Scan: 3D model + drawings



CLIENT	PROJECT
MP Adams	MP Adams Plot 3, Eckington

DRAWING TITLE
PIR CUTTING - GROUND FLOOR - SHEET 18 OF 21

PIR 120mm 1200x2400 | Ground Floor

SCALE	SIZE	DATE	DRAWN
NTS	A3	13.09.26	TS

STATUS	DRAWING No.	REV
CONSTRUCTION	P3-CP-PIR-01 / 18	C01

Item	Value
Parts	17
Used / waste	92.1% / 0.23 m2
Reusable offcuts	0
Saw cuts / shared	23 / 16

PIECES (POSITION = BOTTOM-LEFT CORNER)

Label	Size	X, Y
GF-EX9 P02	89 x 2310	0, 1102
GF-EX2 P05	561 x 93	1388, 1001
GF-EX10 P05	298 x 93	1951, 1001
GF-EX8 P05	21 x 93	2251, 1001
GF-EX7 P06	18 x 93	2274, 1001
GF-EX2 P10	561 x 460	0, 539
GF-EX8 P11	561 x 460	462, 539
GF-EX21 P11	561 x 460	925, 539
GF-EX2 P11	290 x 460	1388, 539
GF-EX21 P12	290 x 460	1680, 539
GF-EX11 P04	425 x 93	1972, 539
GF-EX19 P06	309 x 93	2066, 539
GF-EX21 P07	309 x 93	2161, 539
GF-EX3 P05	152 x 2310	0, 385
GF-EX14 P04	125 x 2310	0, 258
GF-EX1 P05	127 x 2310	0, 129
GF-EX13 P08	127 x 2310	0, 0

NOTES

1. Cut from PIR 120mm 1200x2400, 2mm saw kerf. Viewed on the face; dimensions from the sheet's bottom-left corner (0,0). Red numbered lines = saw cuts in order, each edge to edge.
2. Coloured dimensions belong to the part of that colour: its width and height, and its position from the sheet edges. Raked parts: corner coordinates at each corner.
3. Red hatch = waste. Labels = panel + piece mark on the manufacture drawing.

REVISIONS

REV	DATE	DESCRIPTION
C01	13.09.26	Construction issue



TLS TIMBER FRAME

Design & Manufacture

Scan: 3D model + drawings



CLIENT

MP Adams

PROJECT

MP Adams Plot 3, Eckington

DRAWING TITLE

PIR CUTTING - GROUND FLOOR - SHEET 19 OF 21

PIR 120mm 1200x2400 | Ground Floor

SCALE	SIZE	DATE	DRAWN
NTS	A3	13.09.26	TS

STATUS

CONSTRUCTION

DRAWING No.


P3-CP-PIR-01 / 19

EV

C01

Do not scale. All dimensions in mm. Check all dimensions on site.

Do not scale. All dimensions in mm. Check all dimensions on site.

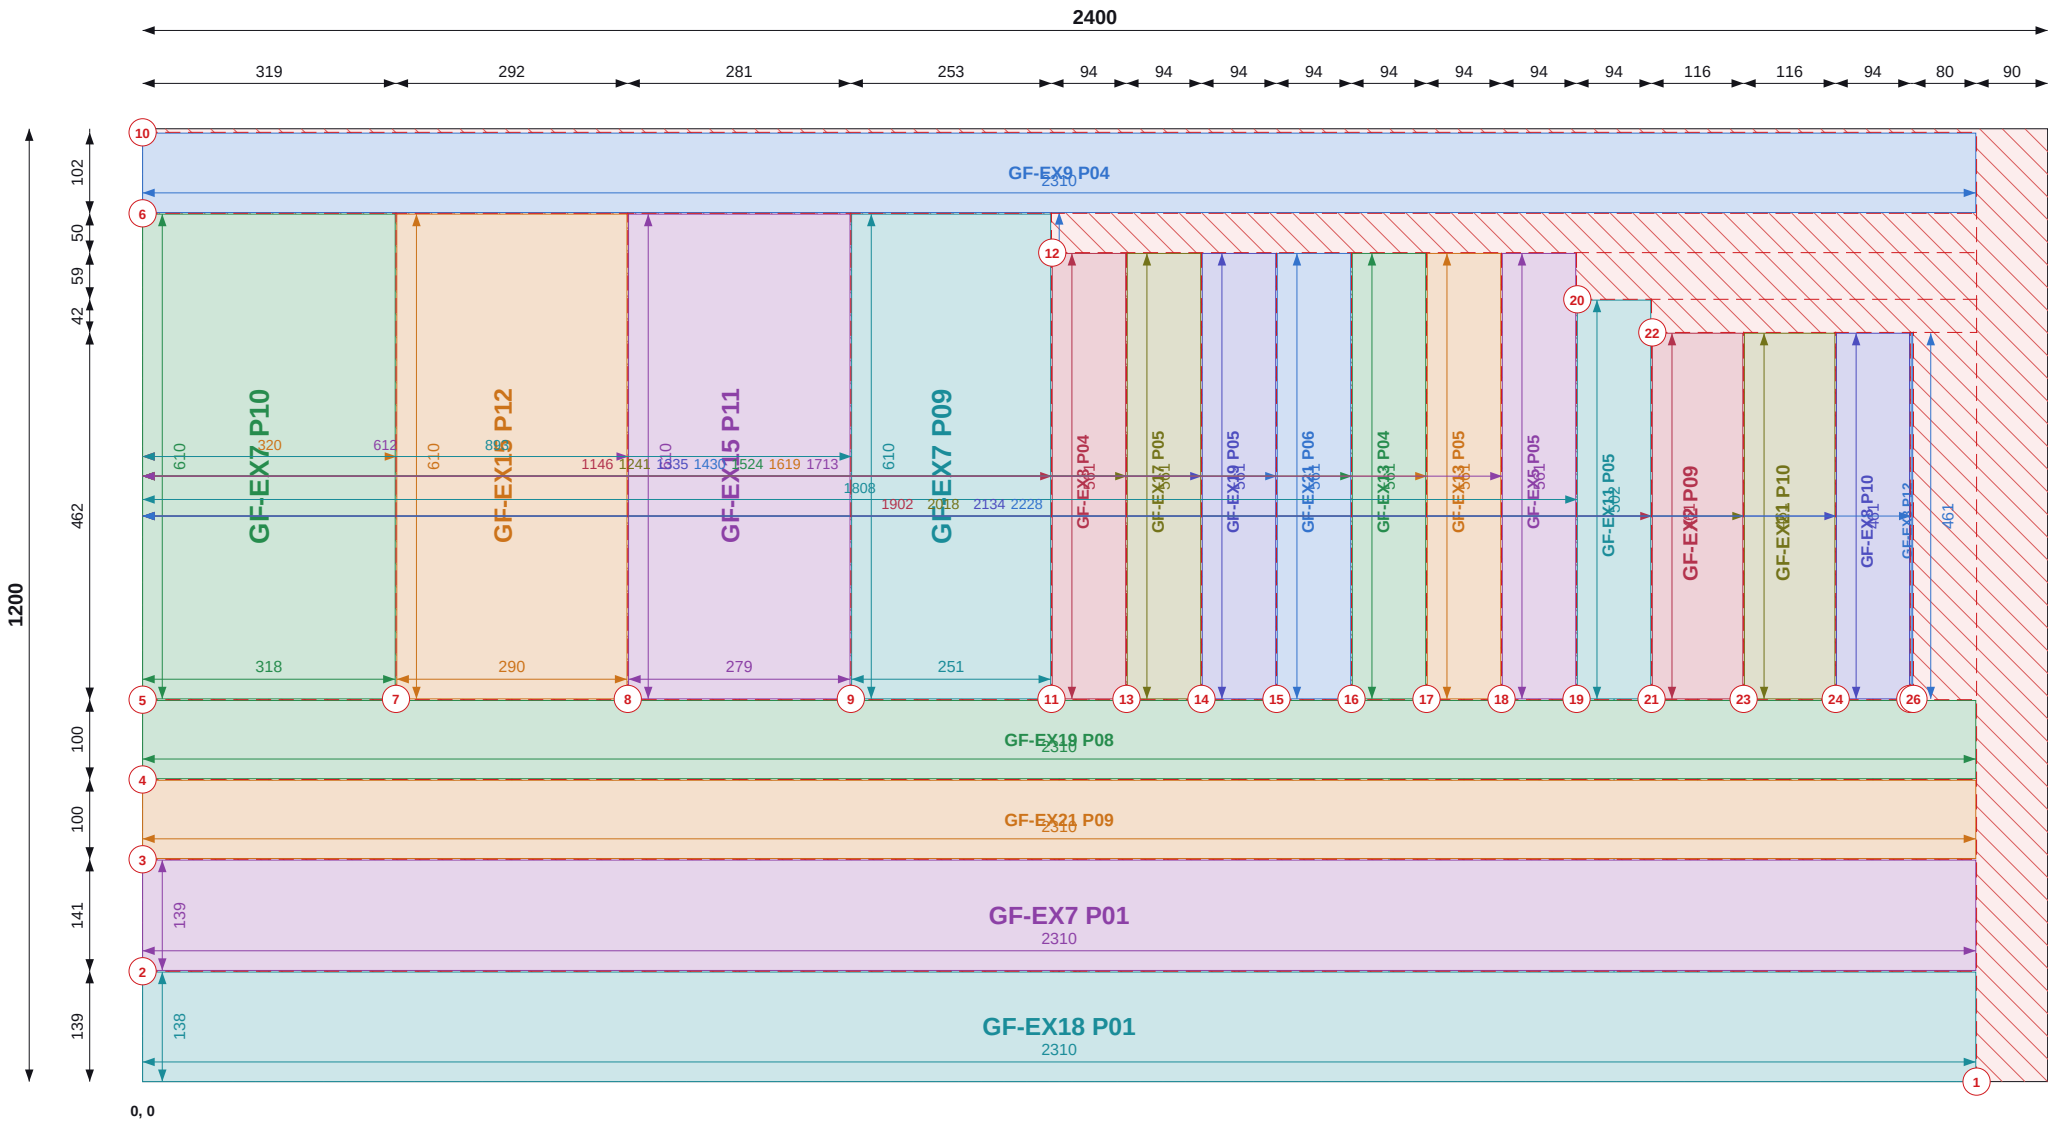

Top / left chains = saw cut positions (to cut centres). Coloured = part size and position.

SHEET 20 OF 21

THIS SHEET

Item	Value
Parts	21
Used / waste	89.5% / 0.30 m2
Reusable offcuts	0
Saw cuts / shared	26 / 20

PIECES (POSITION = BOTTOM-LEFT CORNER)

Label	Size	X, Y
GF-EX9 P04	100 x 2310	0, 1095
GF-EX7 P10	318 x 610	0, 482
GF-EX15 P12	290 x 610	320, 482
GF-EX15 P11	279 x 610	612, 482
GF-EX7 P09	251 x 610	893, 482
GF-EX8 P04	561 x 93	1146, 482
GF-EX17 P05	561 x 93	1241, 482
GF-EX19 P05	561 x 93	1335, 482
GF-EX21 P06	561 x 93	1430, 482
GF-EX13 P04	561 x 93	1524, 482
GF-EX13 P05	561 x 93	1619, 482
GF-EX5 P05	561 x 93	1713, 482
GF-EX11 P05	502 x 93	1808, 482
GF-EX2 P09	114 x 460	1902, 482
GF-EX21 P10	114 x 460	2018, 482
GF-EX8 P10	92 x 460	2134, 482
GF-EX8 P12	2 x 460	2228, 482
GF-EX19 P08	99 x 2310	0, 382
GF-EX21 P09	99 x 2310	0, 281
GF-EX7 P01	139 x 2310	0, 140
GF-EX18 P01	138 x 2310	0, 0

NOTES

- Cut from PIR 120mm 1200x2400, 2mm saw kerf. Viewed on the face; dimensions from the sheet's bottom-left corner (0,0). Red numbered lines = saw cuts in order, each edge to edge.
- Coloured dimensions belong to the part of that colour: its width and height, and its position from the sheet edges. Raked parts: corner coordinates at each corner.
- Red hatch = waste. Labels = panel + piece mark on the manufacture drawing.

REVISIONS

REV	DATE	DESCRIPTION
C01	13.09.26	Construction issue



TLS TIMBER FRAME

Design & Manufacture

Scan: 3D model + drawings



CLIENT	PROJECT
MP Adams	MP Adams Plot 3, Eckington

DRAWING TITLE
PIR CUTTING - GROUND FLOOR - SHEET 20 OF 21

PIR 120mm 1200x2400 | Ground Floor

SCALE	SIZE	DATE	DRAWN
NTS	A3	13.09.26	TS

STATUS	DRAWING No.	REV
CONSTRUCTION	P3-CP-PIR-01 / 20	C01

Item	Value
Parts	38
Used / waste	29.7% / 2.03 m2
Reusable offcuts	1
Saw cuts / shared	42 / 37

PIECES (POSITION = BOTTOM-LEFT CORNER)

Label	Size	X, Y
GF-EX15 P07	309 x 93	0, 987
GF-EX5 P06	309 x 93	311, 987
GF-EX7 P04	270 x 93	622, 987
GF-EX2 P04	133 x 93	894, 987
GF-EX21 P05	133 x 93	1029, 987
GF-EX17 P04	133 x 93	1164, 987
GF-EX5 P04	133 x 93	1299, 987
GF-EX8 P03	111 x 93	1434, 987
GF-EX7 P03	18 x 93	1547, 987
GF-EX2 P07	18 x 93	1567, 987
GF-EX2 P03	18 x 93	1587, 987
GF-EX11 P06	18 x 93	1607, 987
GF-EX8 P02	18 x 93	1627, 987
GF-EX10 P04	18 x 93	1647, 987
GF-EX10 P07	18 x 93	1667, 987
GF-EX8 P06	18 x 93	1687, 987
GF-EX17 P07	18 x 93	1707, 987
GF-EX17 P03	18 x 93	1727, 987
GF-EX21 P04	18 x 93	1747, 987
GF-EX19 P07	18 x 93	1767, 987
GF-EX21 P08	18 x 93	1787, 987
GF-EX19 P03	18 x 93	1807, 987
GF-EX13 P02	18 x 93	1827, 987
GF-EX13 P06	18 x 93	1847, 987
GF-EX15 P05	18 x 93	1867, 987
GF-EX15 P08	18 x 93	1887, 987
GF-EX5 P07	18 x 93	1907, 987
GF-EX5 P03	18 x 93	1927, 987
GF-EX19 P04	513 x 93	0, 892
GF-EX15 P06	298 x 93	515, 892
GF-EX7 P05	337 x 93	815, 892
GF-EX2 P06	309 x 93	1154, 892
GF-EX10 P06	309 x 93	1465, 892
GF-EX17 P06	309 x 93	1776, 892
GF-EX13 P03	208 x 93	2087, 892
GF-EX17 P10	114 x 760	0, 130
GF-EX5 P10	114 x 760	116, 130
GF-EX3 P02	128 x 2310	0, 0

NOTES

1. Cut from PIR 120mm 1200x2400, 2mm saw kerf. Viewed on the face; dimensions from the sheet's bottom-left corner (0,0). Red numbered lines = saw cuts in order, each edge to edge.
2. Coloured dimensions belong to the part of that colour: its width and height, and its position from the sheet edges. Raked parts: corner coordinates at each corner.
3. Red hatch = waste. Labels = panel + piece mark on the manufacture drawing.

REVISIONS

REV	DATE	DESCRIPTION
C01	13.09.26	Construction issue



TLS TIMBER FRAME

Design & Manufacture

Scan: 3D model + drawings



CLIENT	PROJECT
MP Adams	MP Adams Plot 3, Eckington


DRAWING TITLE

PIR CUTTING - GROUND FLOOR - SHEET 21 OF 21

PIR 120mm 1200x2400 | Ground Floor


SCALE	SIZE	DATE	DRAWN
NTS	A3	13.09.26	TS

STATUS	DRAWING No.	REV
CONSTRUCTION	P3-CP-PIR-01 / 21	C01

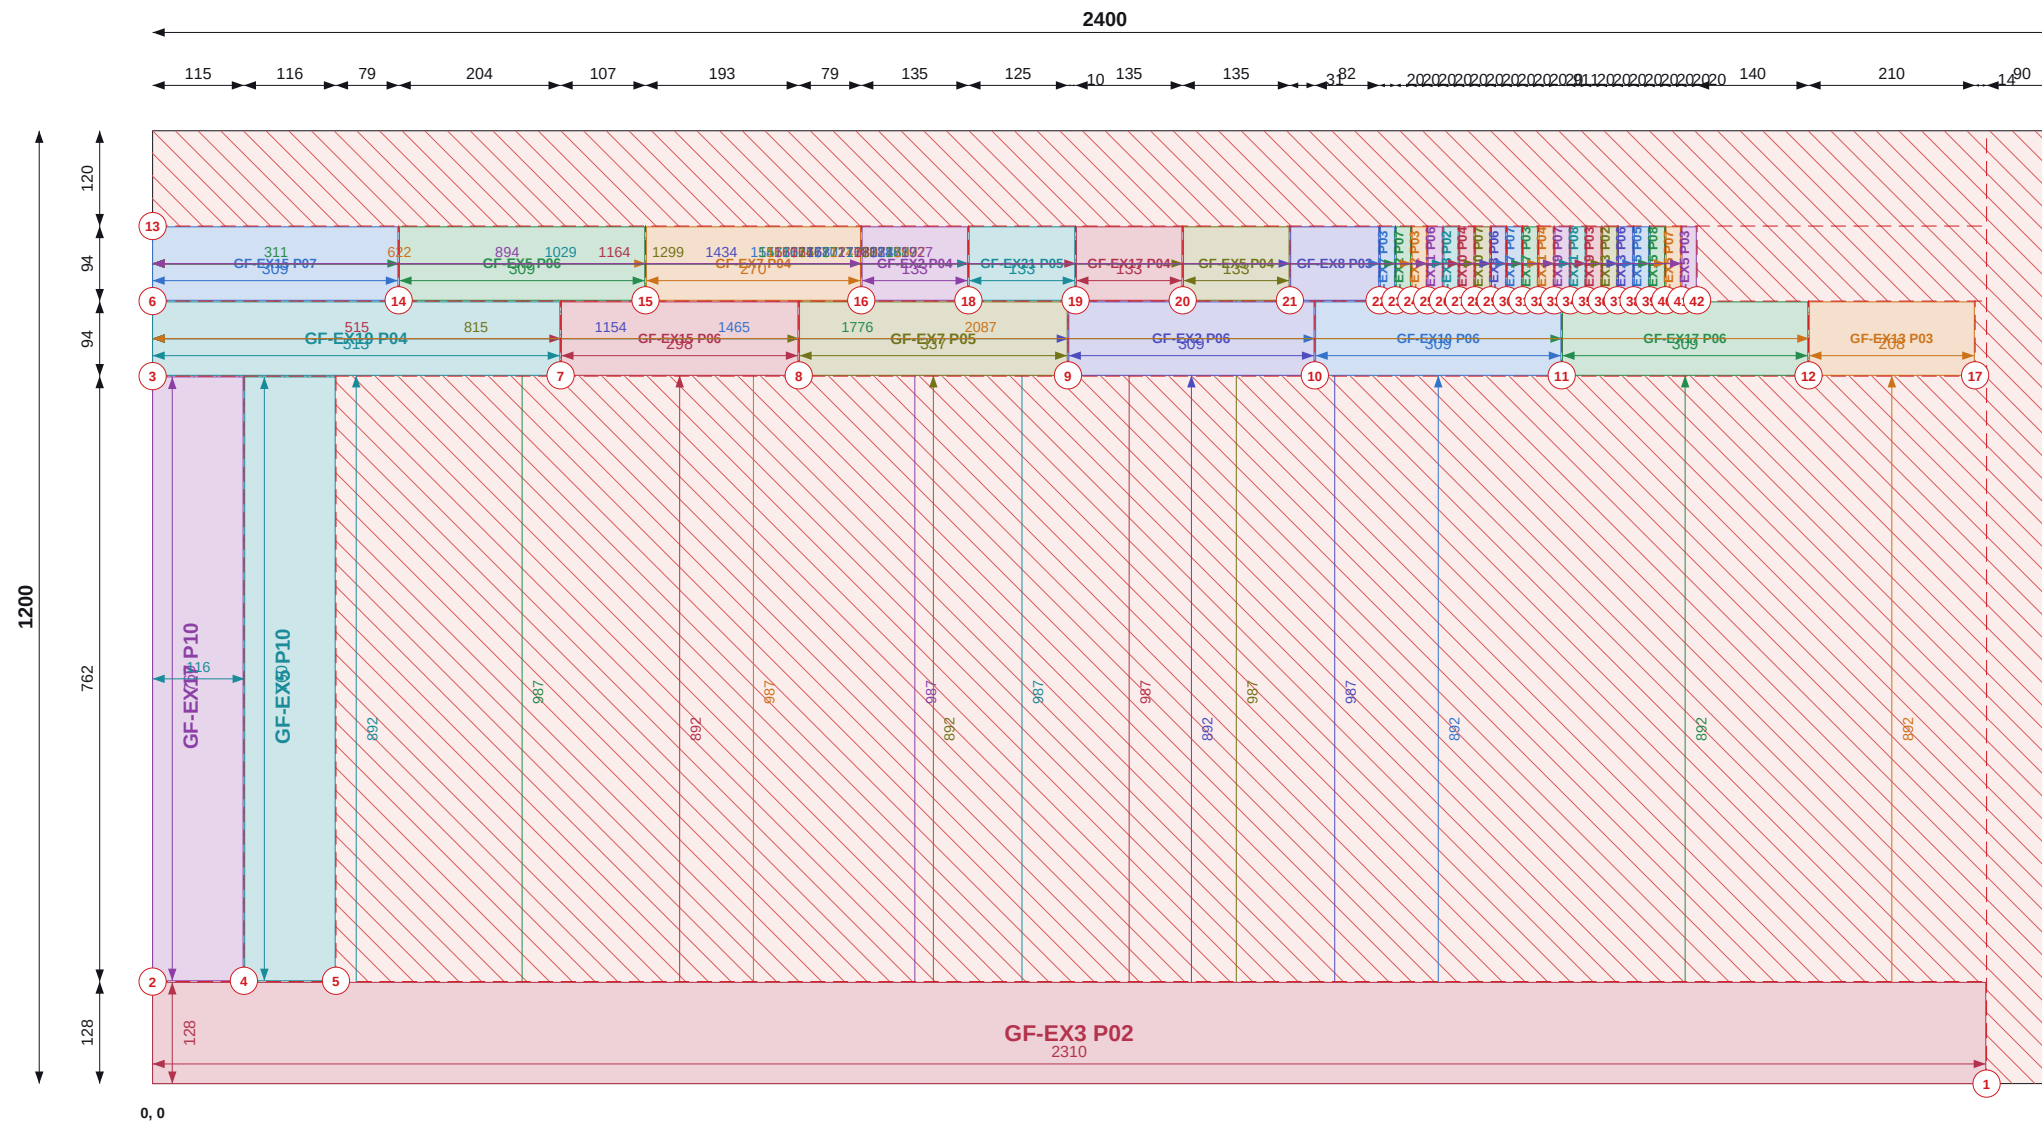

Top / left chains = saw cut positions (to cut centres). Coloured = part size and position.

Do not scale. All dimensions in mm. Check all dimensions on site.

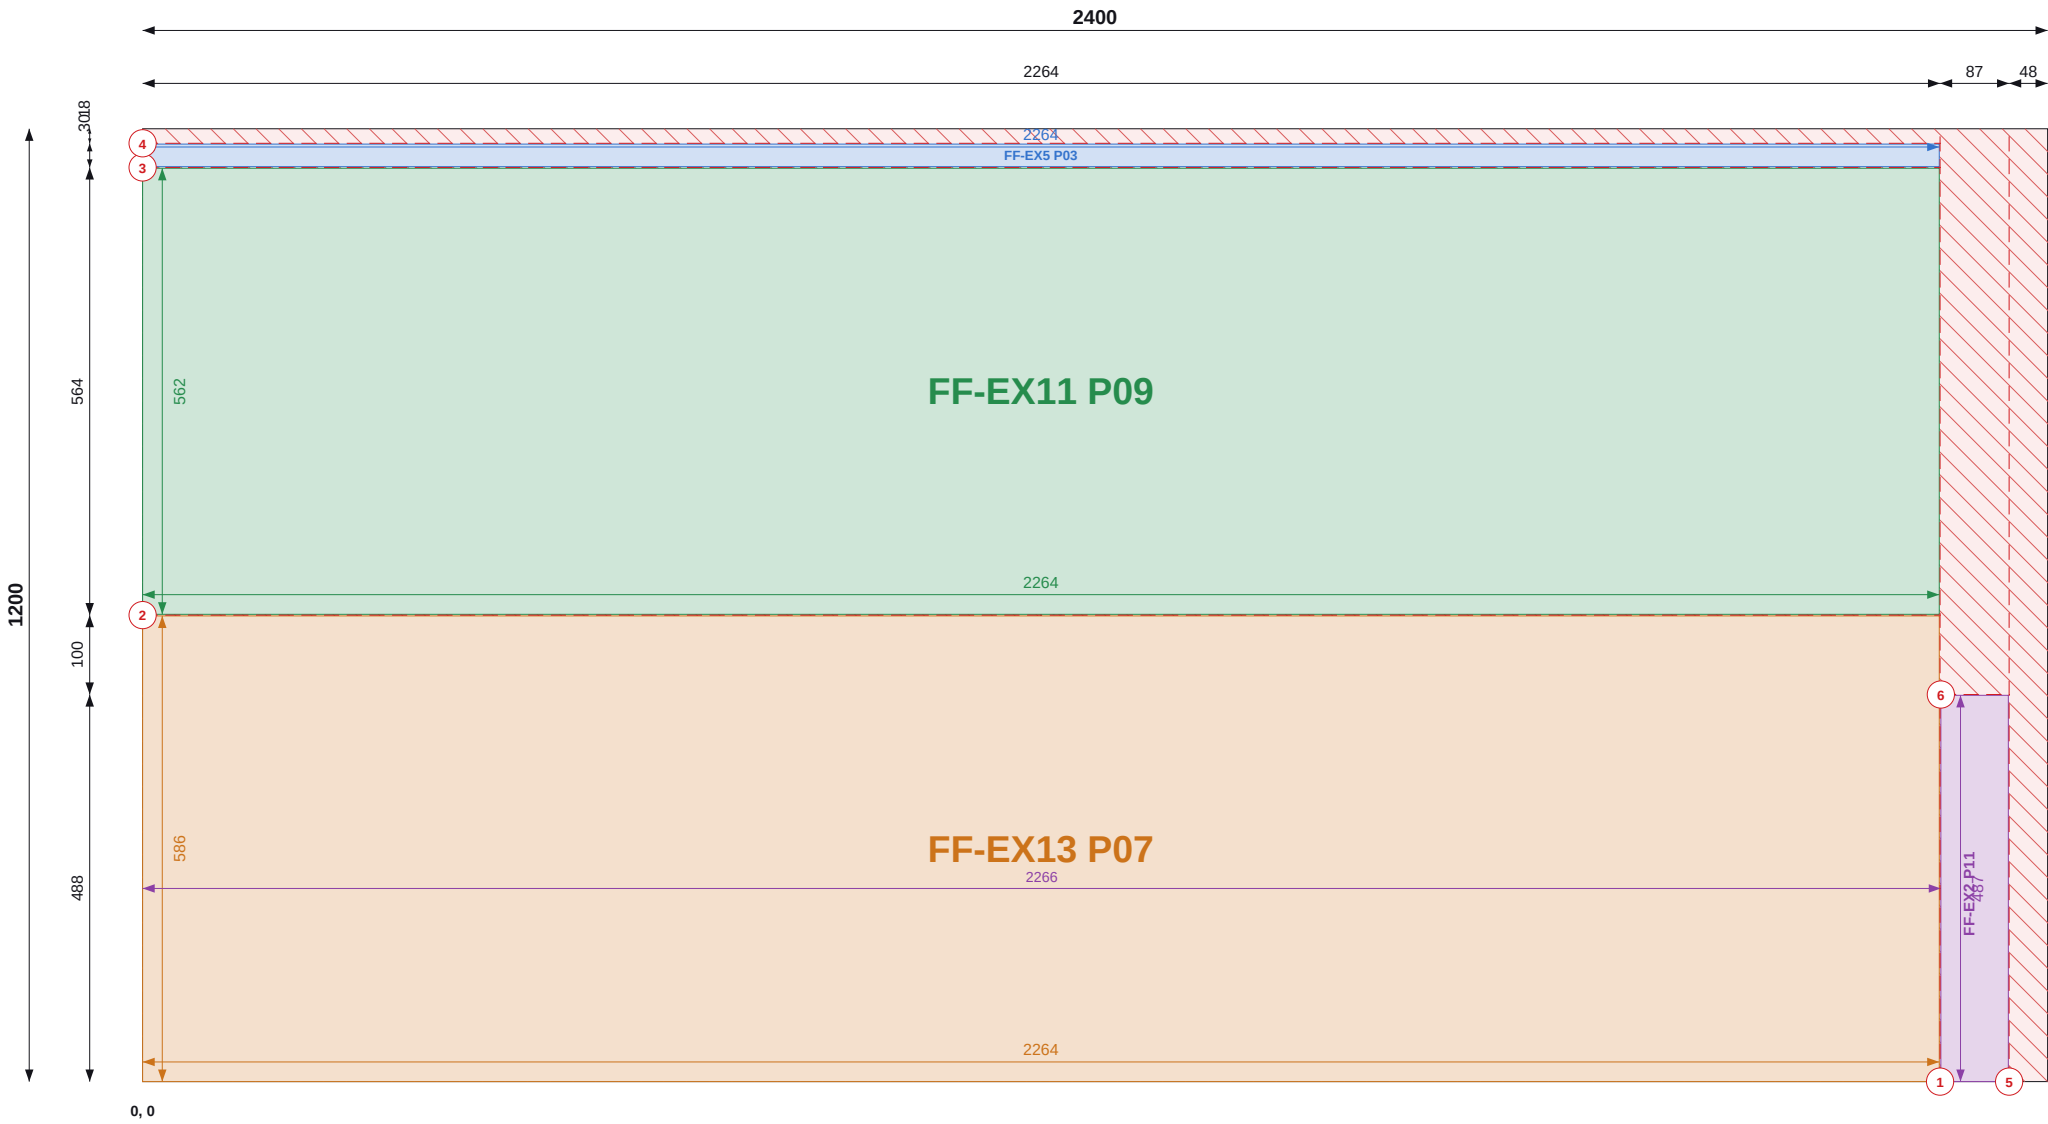

Top / left chains = saw cut positions (to cut centres). Coloured = part size and position.

SHEET 1 OF 23

THIS SHEET

Item	Value
Parts	4
Used / waste	93.9% / 0.18 m2
Reusable offcuts	0
Saw cuts / shared	6 / 3

PIECES (POSITION = BOTTOM-LEFT CORNER)

Label	Size	X, Y
FF-EX5 P03	28 x 2264	0, 1152
FF-EX11 P09	562 x 2264	0, 588
FF-EX13 P07	586 x 2264	0, 0
FF-EX2 P11	85 x 487	2266, 0

FIRST FLOOR TOTALS

Item	Value
Sheets / pieces	23 / 164
Yield / waste	90.6% / 6.21 m2
Saw cuts / shared / on stock edge	195 / 141 / 141

NOTES

- Cut from PIR 120mm 1200x2400, 2mm saw kerf. Viewed on the face; dimensions from the sheet's bottom-left corner (0,0). Red numbered lines = saw cuts in order, each edge to edge.
- Coloured dimensions belong to the part of that colour: its width and height, and its position from the sheet edges. Raked parts: corner coordinates at each corner.
- Red hatch = waste. Labels = panel + piece mark on the manufacture drawing.

REVISIONS

REV	DATE	DESCRIPTION
C01	13.09.26	Construction issue



TLS TIMBER FRAME

Design & Manufacture

Scan: 3D model + drawings



CLIENT	PROJECT
MP Adams	MP Adams Plot 3, Eckington


DRAWING TITLE
PIR CUTTING - FIRST FLOOR - SHEET 1 OF 23

PIR 120mm 1200x2400 | First Floor

SCALE	SIZE	DATE	DRAWN
NTS	A3	13.09.26	TS

STATUS	DRAWING No.	REV
CONSTRUCTION	P3-CP-PIR-02 / 01	C01

Do not scale. All dimensions in mm. Check all dimensions on site.

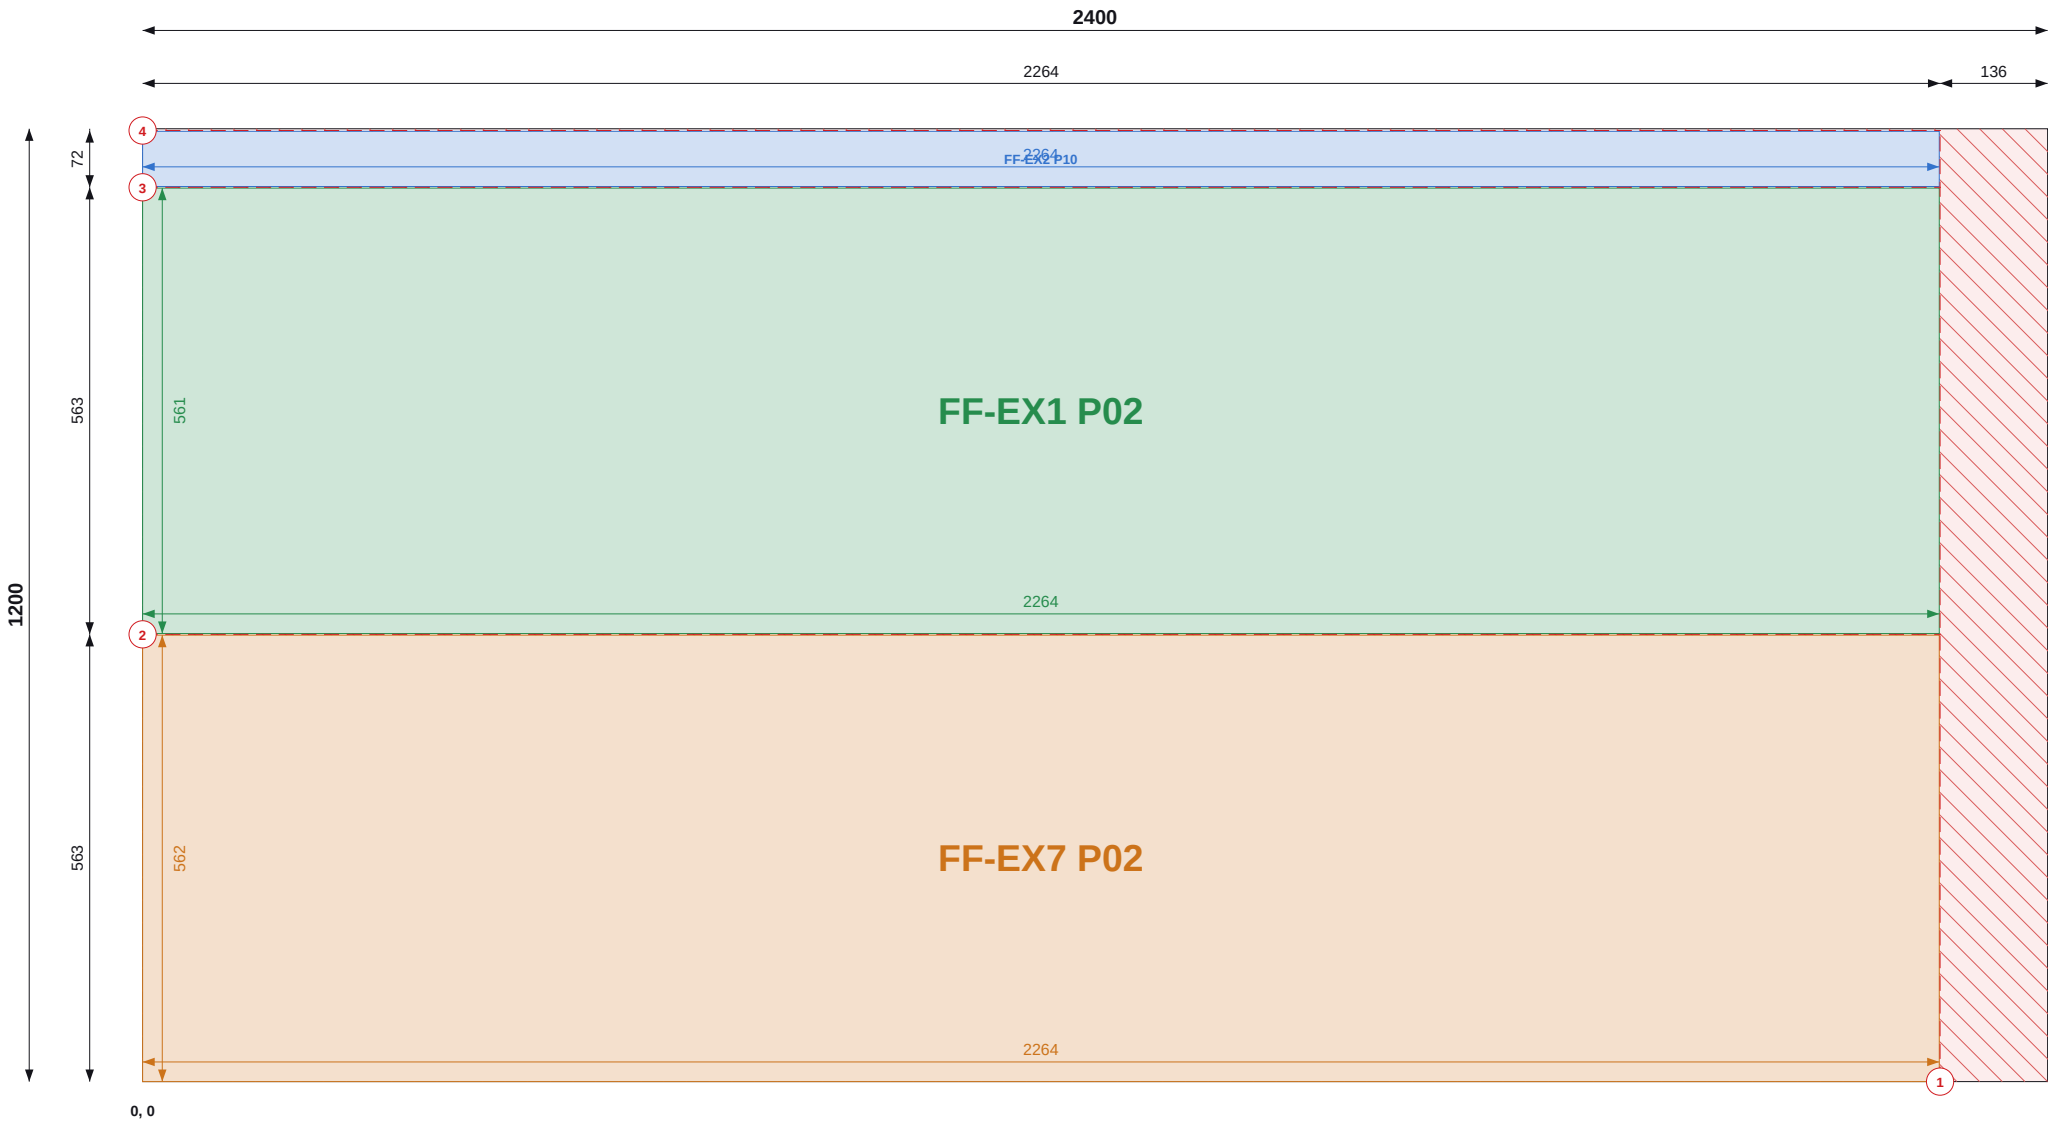

Top / left chains = saw cut positions (to cut centres). Coloured = part size and position.

SHEET 2 OF 23

THIS SHEET

Item	Value
Parts	3
Used / waste	93.7% / 0.18 m2
Reusable offcuts	0
Saw cuts / shared	4 / 2

PIECES (POSITION = BOTTOM-LEFT CORNER)

Label	Size	X, Y
FF-EX2 P10	70 x 2264	0, 1127
FF-EX1 P02	561 x 2264	0, 564
FF-EX7 P02	562 x 2264	0, 0

NOTES

- Cut from PIR 120mm 1200x2400, 2mm saw kerf. Viewed on the face; dimensions from the sheet's bottom-left corner (0,0). Red numbered lines = saw cuts in order, each edge to edge.
- Coloured dimensions belong to the part of that colour: its width and height, and its position from the sheet edges. Raked parts: corner coordinates at each corner.
- Red hatch = waste. Labels = panel + piece mark on the manufacture drawing.

REVISIONS

REV	DATE	DESCRIPTION
C01	13.09.26	Construction issue



TLS TIMBER FRAME

Design & Manufacture

Scan: 3D model + drawings



CLIENT	PROJECT
MP Adams	MP Adams Plot 3, Eckington


DRAWING TITLE
PIR CUTTING - FIRST FLOOR - SHEET 2 OF 23

PIR 120mm 1200x2400 | First Floor

SCALE	SIZE	DATE	DRAWN
NTS	A3	13.09.26	TS

STATUS	DRAWING No.	REV
CONSTRUCTION	P3-CP-PIR-02 / 02	C01

Do not scale. All dimensions in mm. Check all dimensions on site.

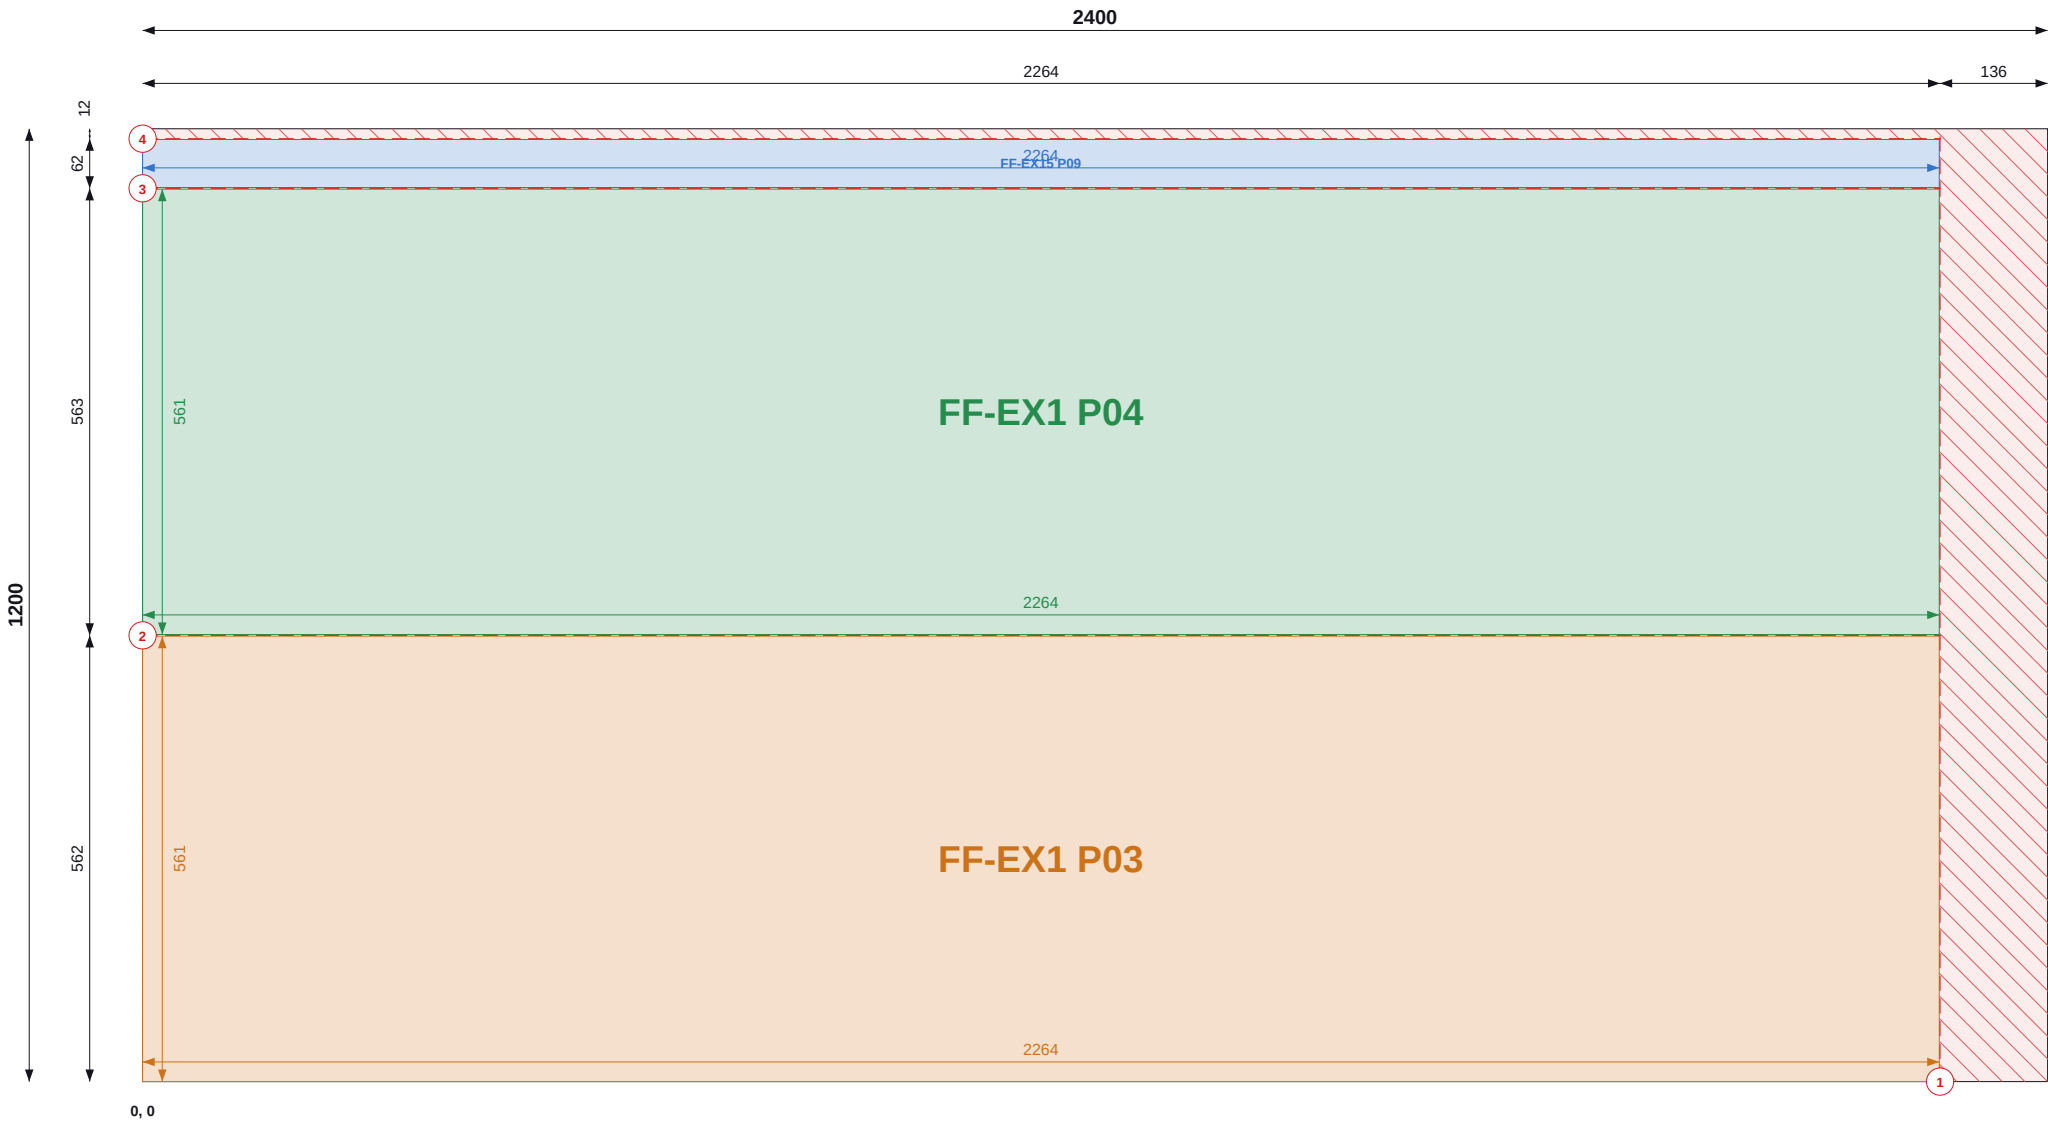

Top / left chains = saw cut positions (to cut centres). Coloured = part size and position.

SHEET 3 OF 23

THIS SHEET

Item	Value
Parts	3
Used / waste	92.9% / 0.20 m2
Reusable offcuts	0
Saw cuts / shared	4 / 2

PIECES (POSITION = BOTTOM-LEFT CORNER)

Label	Size	X, Y
FF-EX15 P09	61 x 2264	0, 1126
FF-EX1 P04	561 x 2264	0, 563
FF-EX1 P03	561 x 2264	0, 0

NOTES

- Cut from PIR 120mm 1200x2400, 2mm saw kerf. Viewed on the face; dimensions from the sheet's bottom-left corner (0,0). Red numbered lines = saw cuts in order, each edge to edge.
- Coloured dimensions belong to the part of that colour: its width and height, and its position from the sheet edges. Raked parts: corner coordinates at each corner.
- Red hatch = waste. Labels = panel + piece mark on the manufacture drawing.

REVISIONS

REV	DATE	DESCRIPTION
C01	13.09.26	Construction issue



TLS TIMBER FRAME

Design & Manufacture

Scan: 3D model + drawings




CLIENT	PROJECT
MP Adams	MP Adams Plot 3, Eckington

DRAWING TITLE			
PIR CUTTING - FIRST FLOOR - SHEET 3 OF 23			
PIR 120mm 1200x2400 First Floor			

SCALE	SIZE	DATE	DRAWN
NTS	A3	13.09.26	TS

STATUS	DRAWING No.	REV
CONSTRUCTION	P3-CP-PIR-02 / 03	C01

Do not scale. All dimensions in mm. Check all dimensions on site.

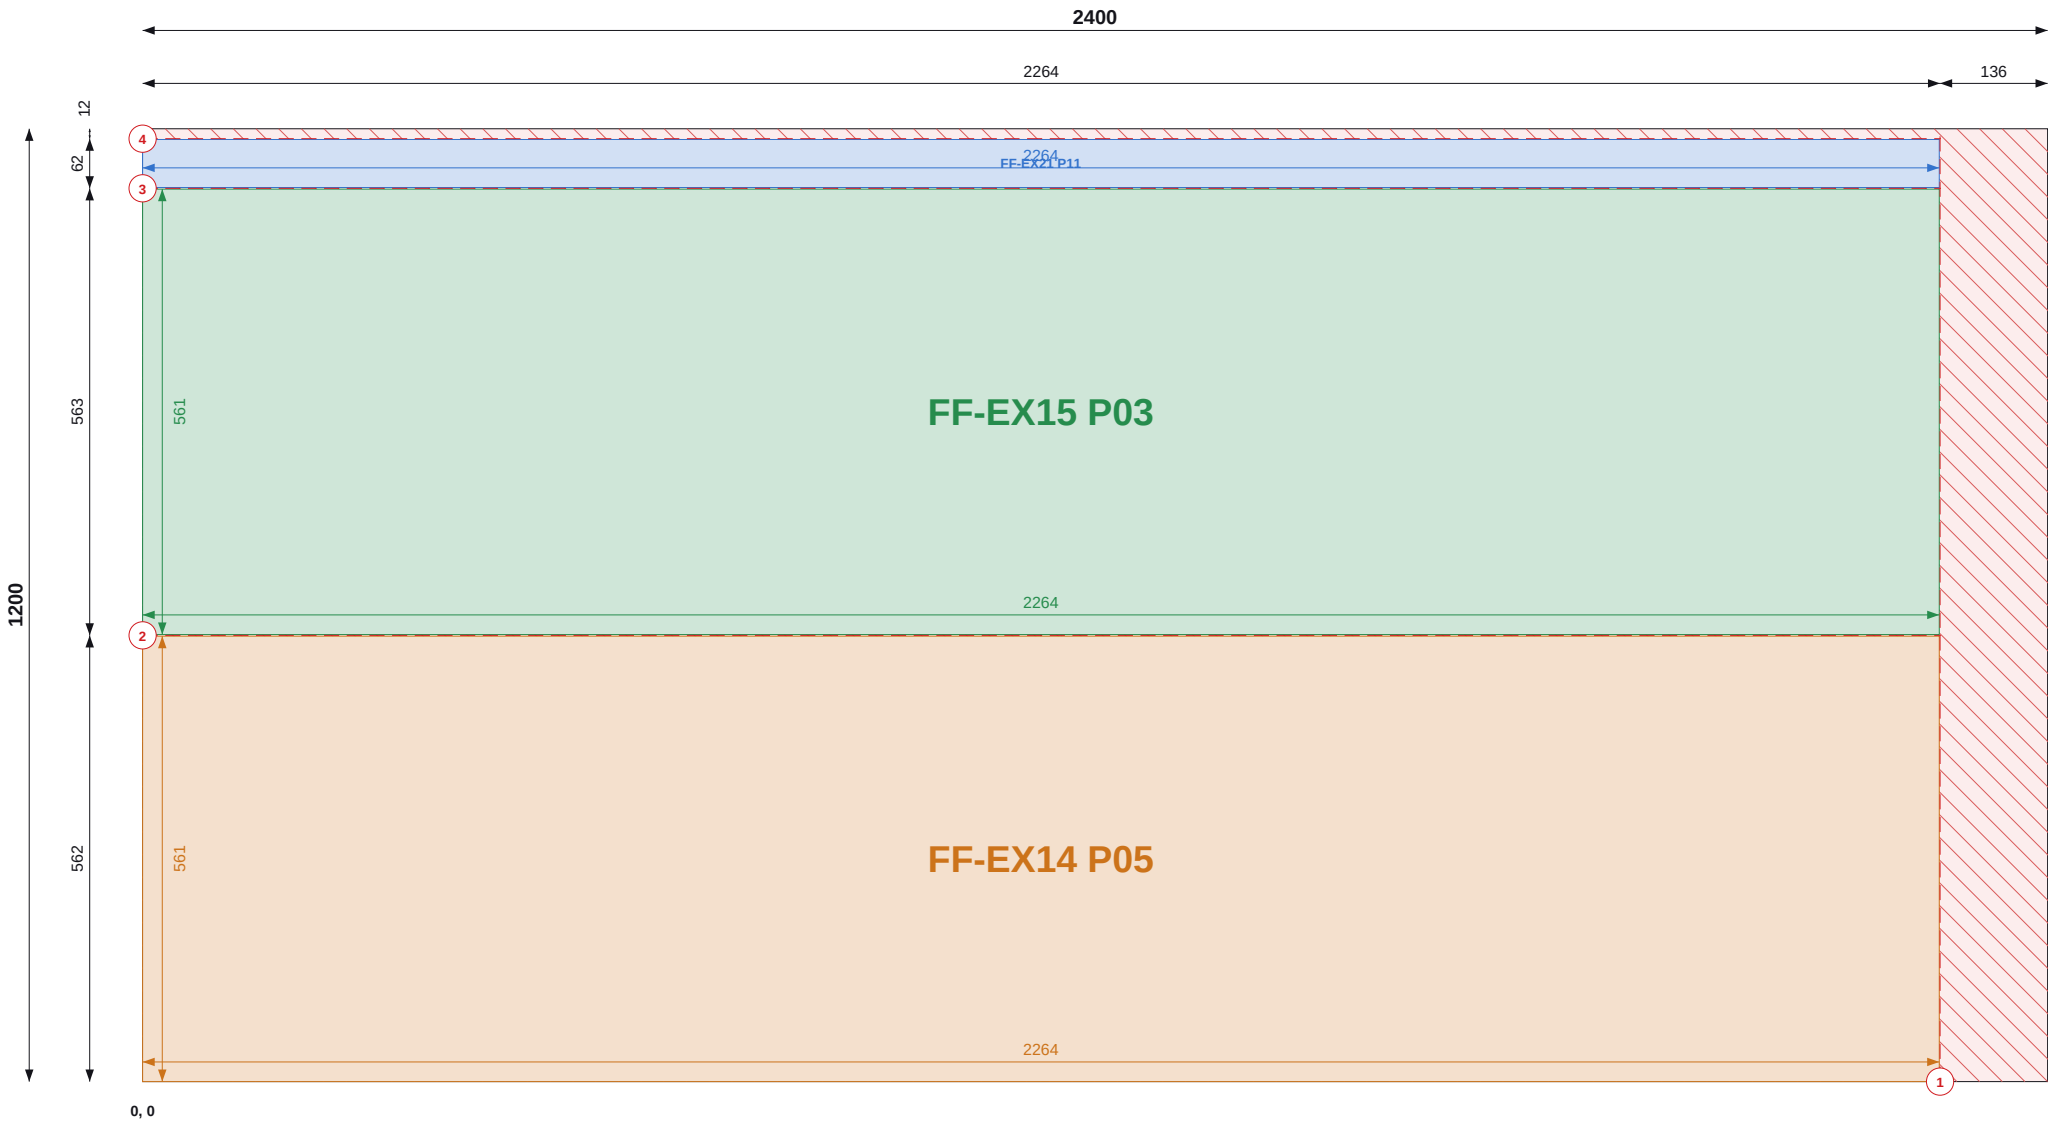

SHEET 4 OF 23

THIS SHEET

Item	Value
Parts	3
Used / waste	92.9% / 0.20 m2
Reusable offcuts	0
Saw cuts / shared	4 / 2

PIECES (POSITION = BOTTOM-LEFT CORNER)

Label	Size	X, Y
FF-EX21 P11	61 x 2264	0, 1126
FF-EX15 P03	561 x 2264	0, 563
FF-EX14 P05	561 x 2264	0, 0

NOTES

- Cut from PIR 120mm 1200x2400, 2mm saw kerf. Viewed on the face; dimensions from the sheet's bottom-left corner (0,0). Red numbered lines = saw cuts in order, each edge to edge.
- Coloured dimensions belong to the part of that colour: its width and height, and its position from the sheet edges. Raked parts: corner coordinates at each corner.
- Red hatch = waste. Labels = panel + piece mark on the manufacture drawing.

REVISIONS

REV	DATE	DESCRIPTION
C01	13.09.26	Construction issue



TLS TIMBER FRAME

Design & Manufacture

Scan: 3D model + drawings



CLIENT	PROJECT
MP Adams	MP Adams Plot 3, Eckington


DRAWING TITLE
PIR CUTTING - FIRST FLOOR - SHEET 4 OF 23

PIR 120mm 1200x2400 | First Floor

SCALE	SIZE	DATE	DRAWN
NTS	A3	13.09.26	TS

STATUS	DRAWING No.	REV
CONSTRUCTION	P3-CP-PIR-02 / 04	C01

Do not scale. All dimensions in mm. Check all dimensions on site.

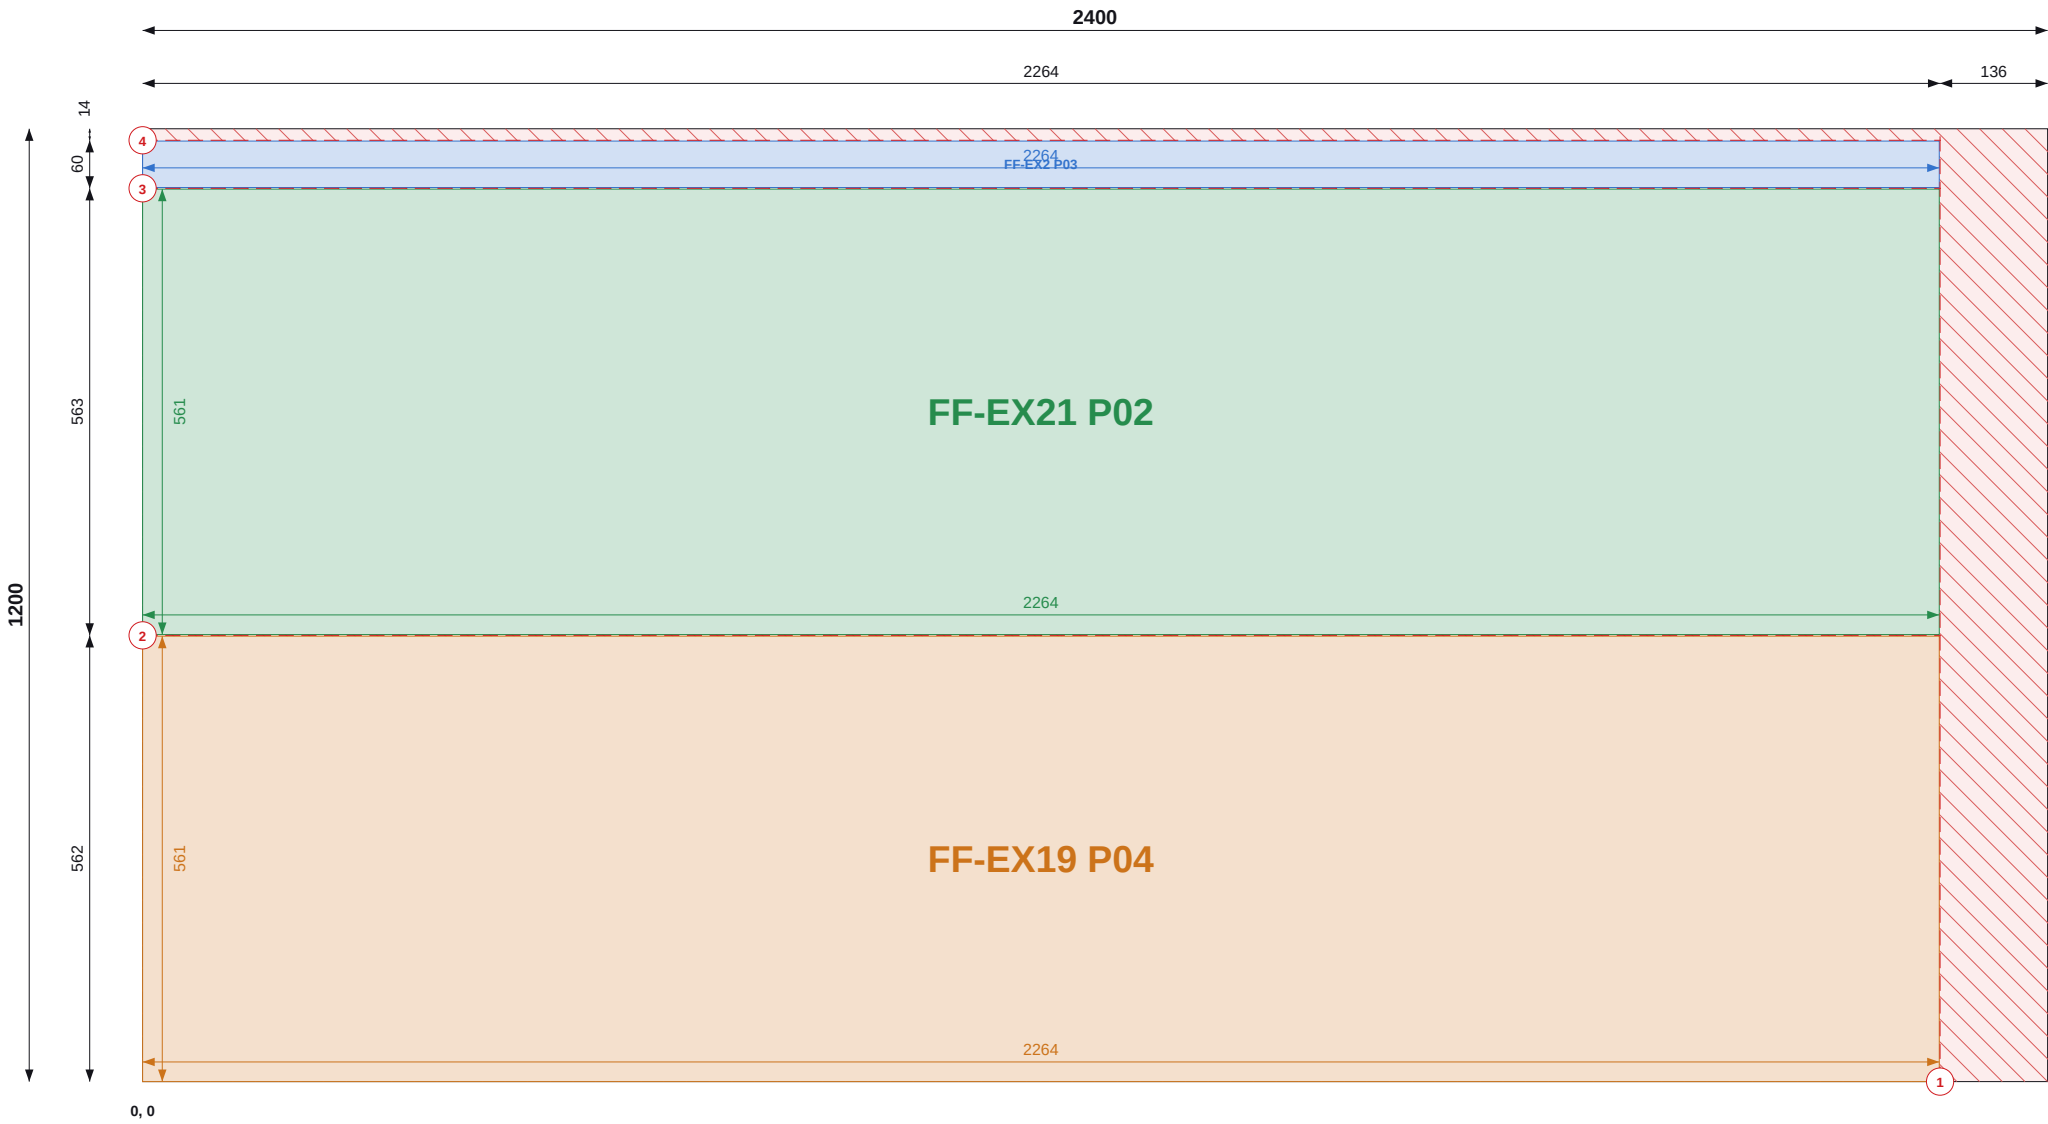

Top / left chains = saw cut positions (to cut centres). Coloured = part size and position.

SHEET 5 OF 23

THIS SHEET

Item	Value
Parts	3
Used / waste	92.8% / 0.21 m2
Reusable offcuts	0
Saw cuts / shared	4 / 2

PIECES (POSITION = BOTTOM-LEFT CORNER)

Label	Size	X, Y
FF-EX2 P03	59 x 2264	0, 1126
FF-EX21 P02	561 x 2264	0, 563
FF-EX19 P04	561 x 2264	0, 0

NOTES

1. Cut from PIR 120mm 1200x2400, 2mm saw kerf. Viewed on the face; dimensions from the sheet's bottom-left corner (0,0). Red numbered lines = saw cuts in order, each edge to edge.
2. Coloured dimensions belong to the part of that colour: its width and height, and its position from the sheet edges. Raked parts: corner coordinates at each corner.
3. Red hatch = waste. Labels = panel + piece mark on the manufacture drawing.

REVISIONS

REV	DATE	DESCRIPTION
C01	13.09.26	Construction issue



TLS TIMBER FRAME

Design & Manufacture

Scan: 3D model + drawings



CLIENT	PROJECT
MP Adams	MP Adams Plot 3, Eckington


DRAWING TITLE
PIR CUTTING - FIRST FLOOR - SHEET 5 OF 23

PIR 120mm 1200x2400 | First Floor

SCALE	SIZE	DATE	DRAWN
NTS	A3	13.09.26	TS

STATUS	DRAWING No.	REV
CONSTRUCTION	P3-CP-PIR-02 / 05	C01

Do not scale. All dimensions in mm. Check all dimensions on site.

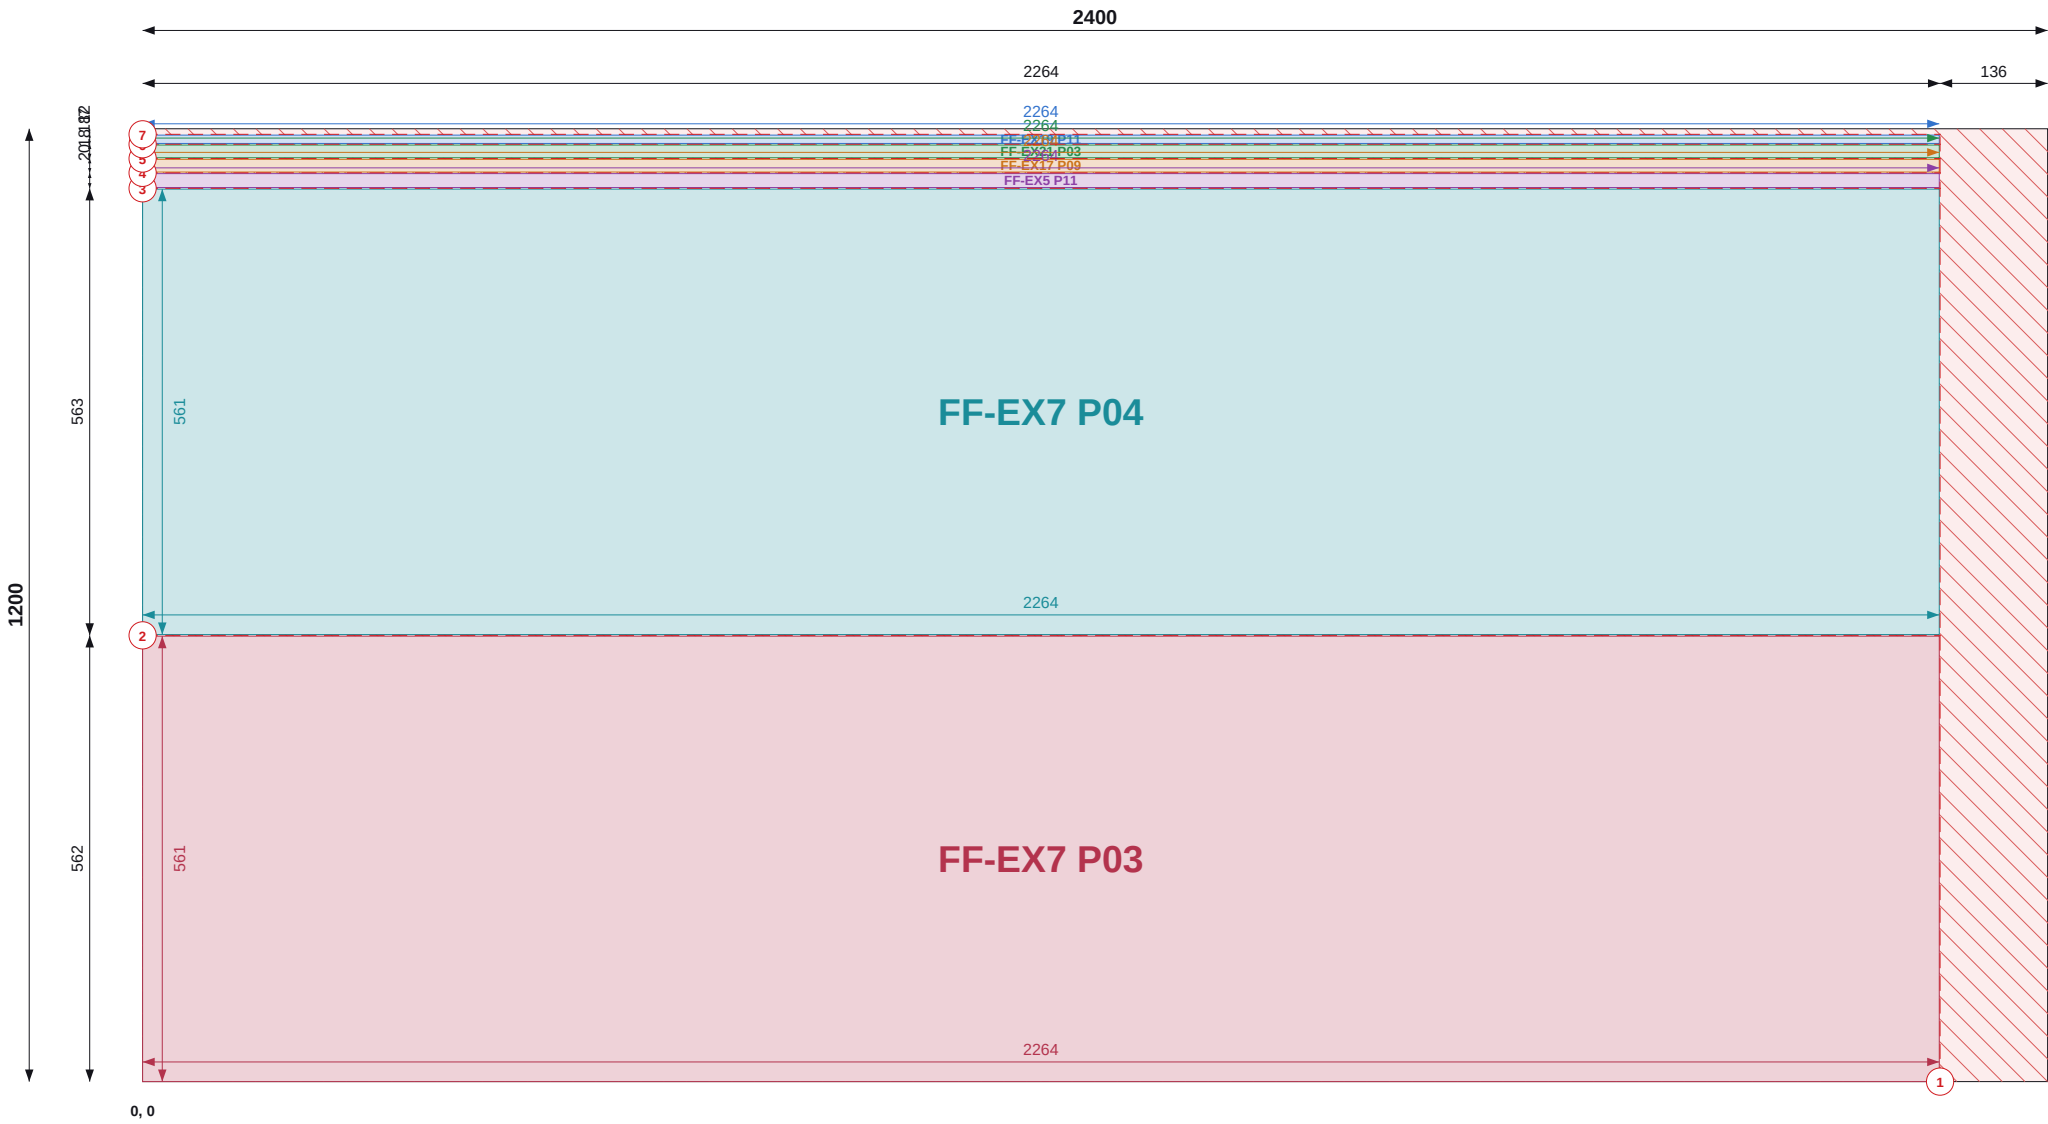

Top / left chains = saw cut positions (to cut centres). Coloured = part size and position.

SHEET 6 OF 23

THIS SHEET

Item	Value
Parts	6
Used / waste	92.9% / 0.20 m2
Reusable offcuts	0
Saw cuts / shared	7 / 5

PIECES (POSITION = BOTTOM-LEFT CORNER)

Label	Size	X, Y
FF-EX19 P11	11 x 2264	0, 1181
FF-EX21 P03	16 x 2264	0, 1163
FF-EX17 P09	16 x 2264	0, 1145
FF-EX5 P11	17 x 2264	0, 1126
FF-EX7 P04	561 x 2264	0, 563
FF-EX7 P03	561 x 2264	0, 0

NOTES

- Cut from PIR 120mm 1200x2400, 2mm saw kerf. Viewed on the face; dimensions from the sheet's bottom-left corner (0,0). Red numbered lines = saw cuts in order, each edge to edge.
- Coloured dimensions belong to the part of that colour: its width and height, and its position from the sheet edges. Raked parts: corner coordinates at each corner.
- Red hatch = waste. Labels = panel + piece mark on the manufacture drawing.

REVISIONS

REV	DATE	DESCRIPTION
C01	13.09.26	Construction issue



TLS TIMBER FRAME

Design & Manufacture

Scan: 3D model + drawings




CLIENT	PROJECT
MP Adams	MP Adams Plot 3, Eckington

DRAWING TITLE
PIR CUTTING - FIRST FLOOR - SHEET 6 OF 23
PIR 120mm 1200x2400 First Floor

SCALE	SIZE	DATE	DRAWN
NTS	A3	13.09.26	TS

STATUS	DRAWING No.	REV
CONSTRUCTION	P3-CP-PIR-02 / 06	C01

Do not scale. All dimensions in mm. Check all dimensions on site.

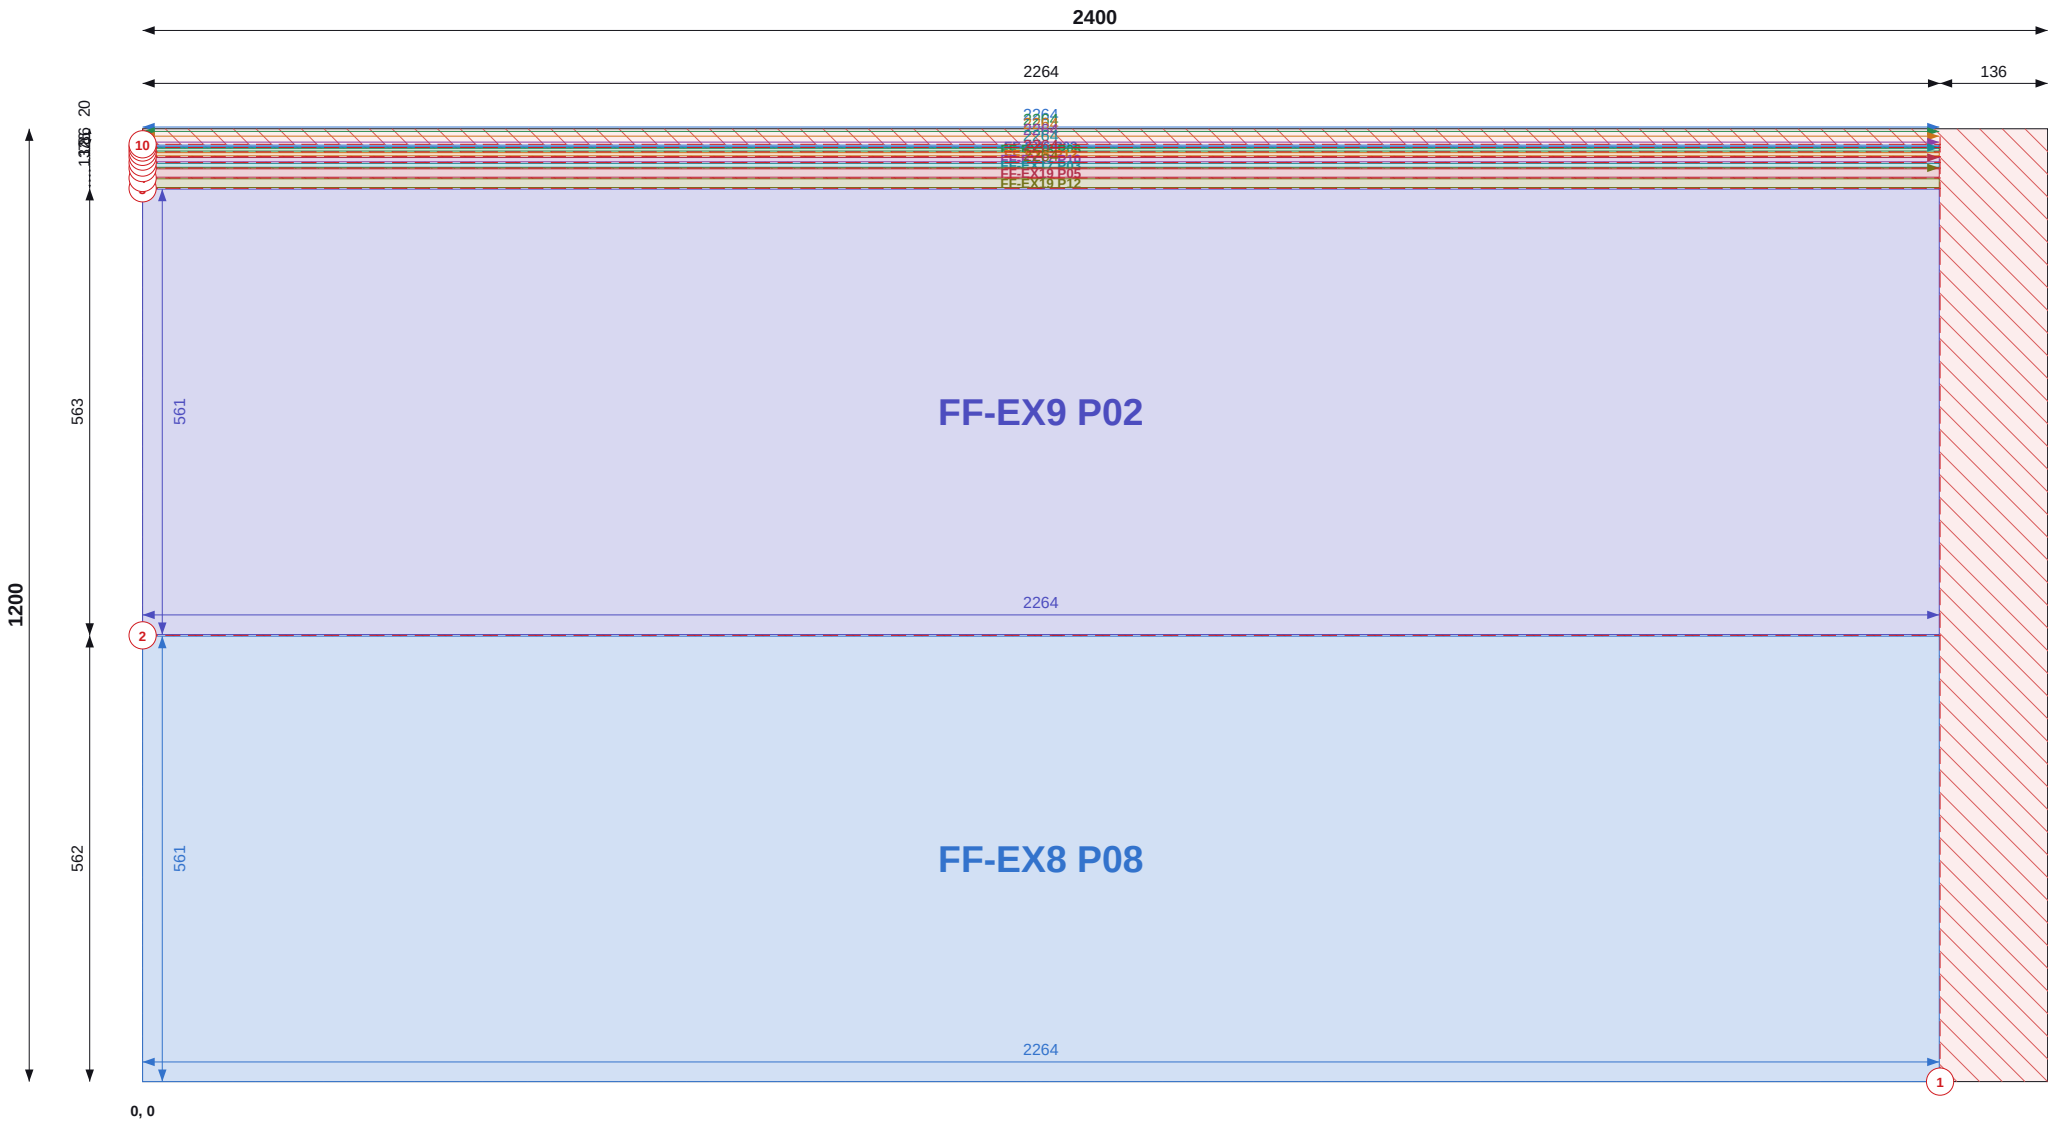

Top / left chains = saw cut positions (to cut centres). Coloured = part size and position.

SHEET 7 OF 23

THIS SHEET

Item	Value
Parts	9
Used / waste	91.4% / 0.25 m2
Reusable offcuts	0
Saw cuts / shared	10 / 8

PIECES (POSITION = BOTTOM-LEFT CORNER)

Label	Size	X, Y
FF-EX6 P03	2 x 2264	0, 1177
FF-EX18 P06	3 x 2264	0, 1172
FF-EX5 P12	4 x 2264	0, 1166
FF-EX17 P10	5 x 2264	0, 1158
FF-EX17 P03	5 x 2264	0, 1151
FF-EX19 P05	10 x 2264	0, 1139
FF-EX19 P12	11 x 2264	0, 1126
FF-EX9 P02	561 x 2264	0, 563
FF-EX8 P08	561 x 2264	0, 0

NOTES

- Cut from PIR 120mm 1200x2400, 2mm saw kerf. Viewed on the face; dimensions from the sheet's bottom-left corner (0,0). Red numbered lines = saw cuts in order, each edge to edge.
- Coloured dimensions belong to the part of that colour: its width and height, and its position from the sheet edges. Raked parts: corner coordinates at each corner.
- Red hatch = waste. Labels = panel + piece mark on the manufacture drawing.

REVISIONS

REV	DATE	DESCRIPTION
C01	13.09.26	Construction issue



TLS TIMBER FRAME

Design & Manufacture

Scan: 3D model + drawings



CLIENT	PROJECT
MP Adams	MP Adams Plot 3, Eckington


DRAWING TITLE
PIR CUTTING - FIRST FLOOR - SHEET 7 OF 23

PIR 120mm 1200x2400 | First Floor

SCALE	SIZE	DATE	DRAWN
NTS	A3	13.09.26	TS

STATUS	DRAWING No.	REV
CONSTRUCTION	P3-CP-PIR-02 / 07	C01

Do not scale. All dimensions in mm. Check all dimensions on site.

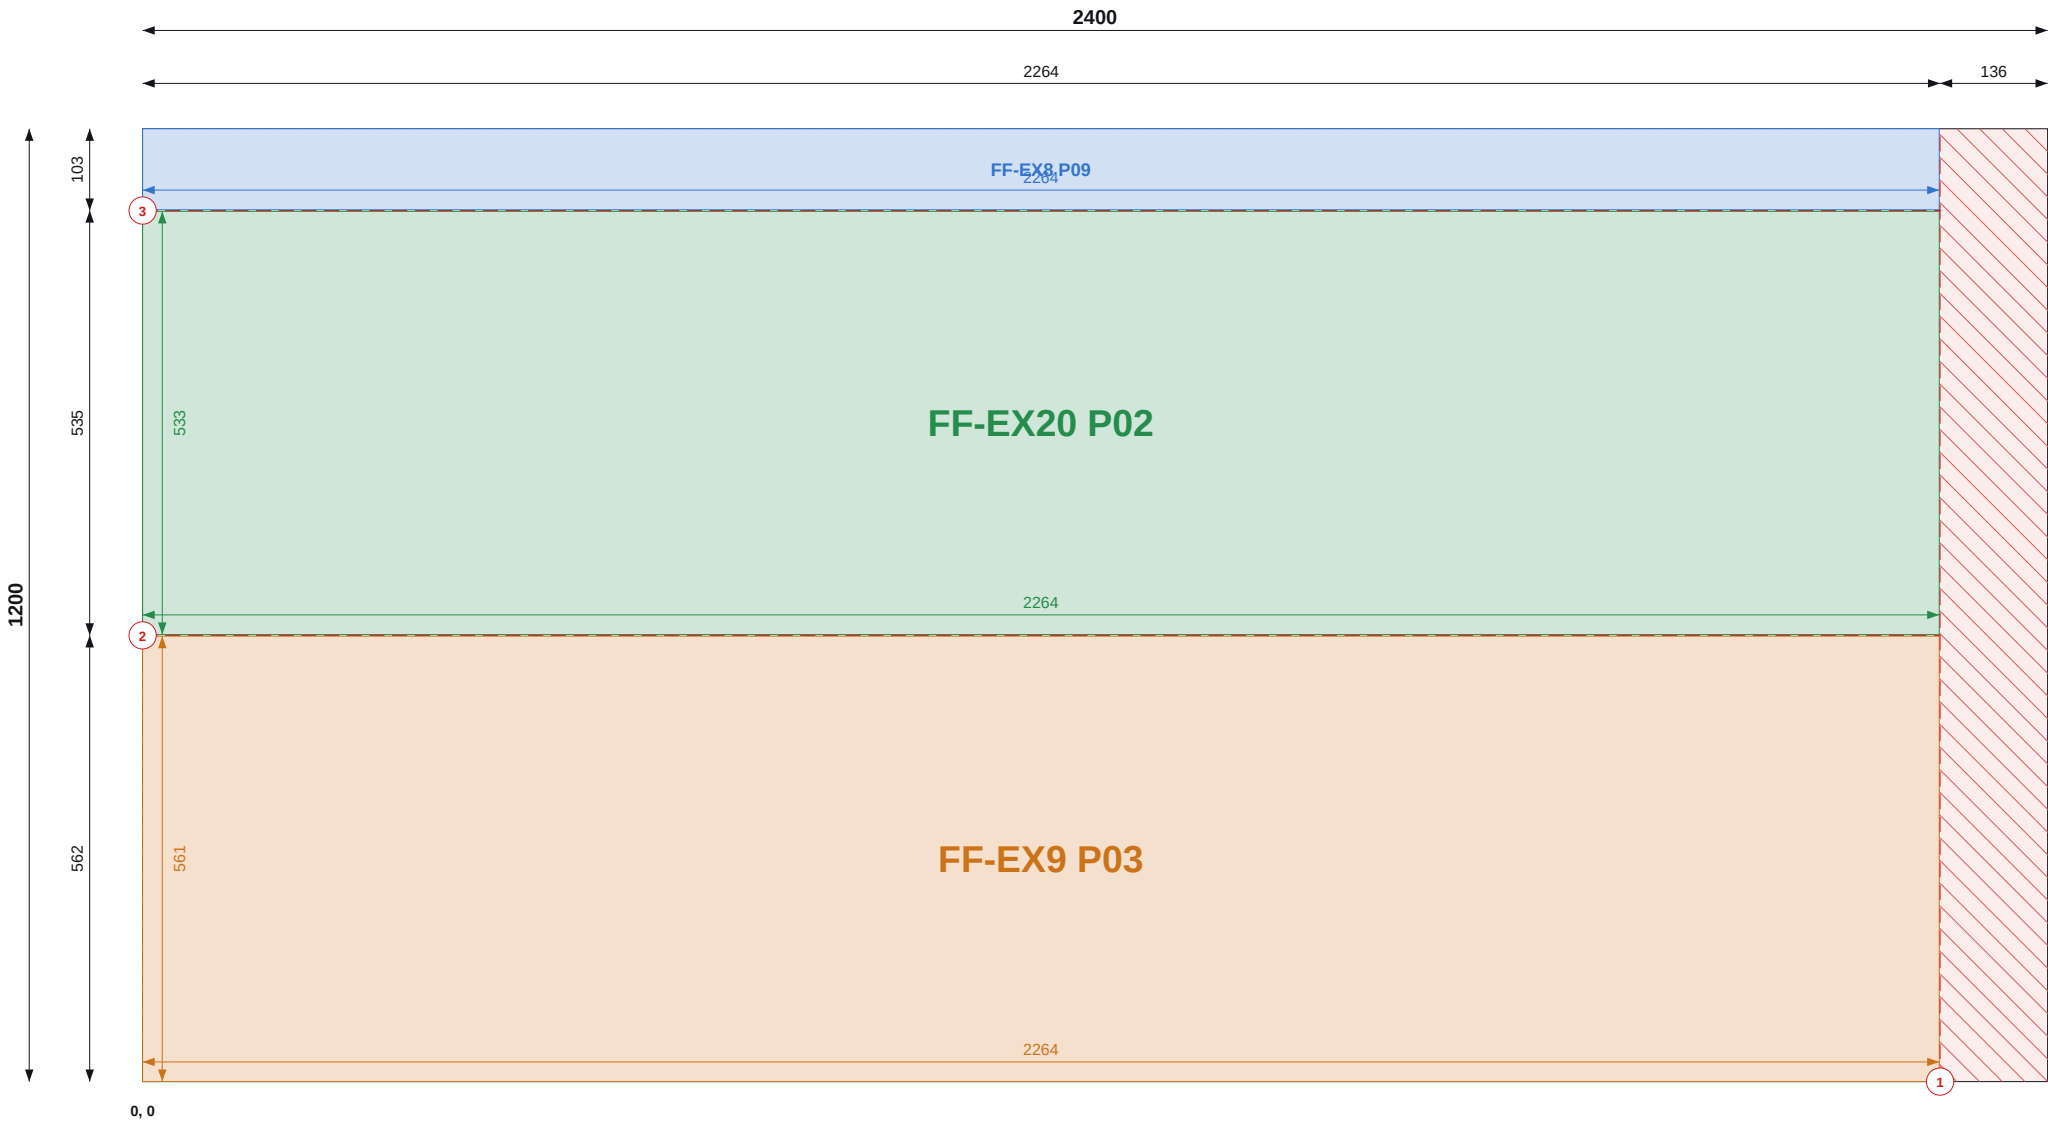

Top / left chains = saw cut positions (to cut centres). Coloured = part size and position.

SHEET 8 OF 23

THIS SHEET

Item	Value
Parts	3
Used / waste	94.0% / 0.17 m2
Reusable offcuts	0
Saw cuts / shared	3 / 2

PIECES (POSITION = BOTTOM-LEFT CORNER)

Label	Size	X, Y
FF-EX8 P09	102 x 2264	0, 1098
FF-EX20 P02	533 x 2264	0, 563
FF-EX9 P03	561 x 2264	0, 0

NOTES

- Cut from PIR 120mm 1200x2400, 2mm saw kerf. Viewed on the face; dimensions from the sheet's bottom-left corner (0,0). Red numbered lines = saw cuts in order, each edge to edge.
- Coloured dimensions belong to the part of that colour: its width and height, and its position from the sheet edges. Raked parts: corner coordinates at each corner.
- Red hatch = waste. Labels = panel + piece mark on the manufacture drawing.

REVISIONS

REV	DATE	DESCRIPTION
C01	13.09.26	Construction issue



TLS TIMBER FRAME

Design & Manufacture

Scan: 3D model + drawings



CLIENT	PROJECT
MP Adams	MP Adams Plot 3, Eckington


DRAWING TITLE
PIR CUTTING - FIRST FLOOR - SHEET 8 OF 23

PIR 120mm 1200x2400 | First Floor

SCALE	SIZE	DATE	DRAWN
NTS	A3	13.09.26	TS

STATUS	DRAWING No.	REV
CONSTRUCTION	P3-CP-PIR-02 / 08	C01

Do not scale. All dimensions in mm. Check all dimensions on site.

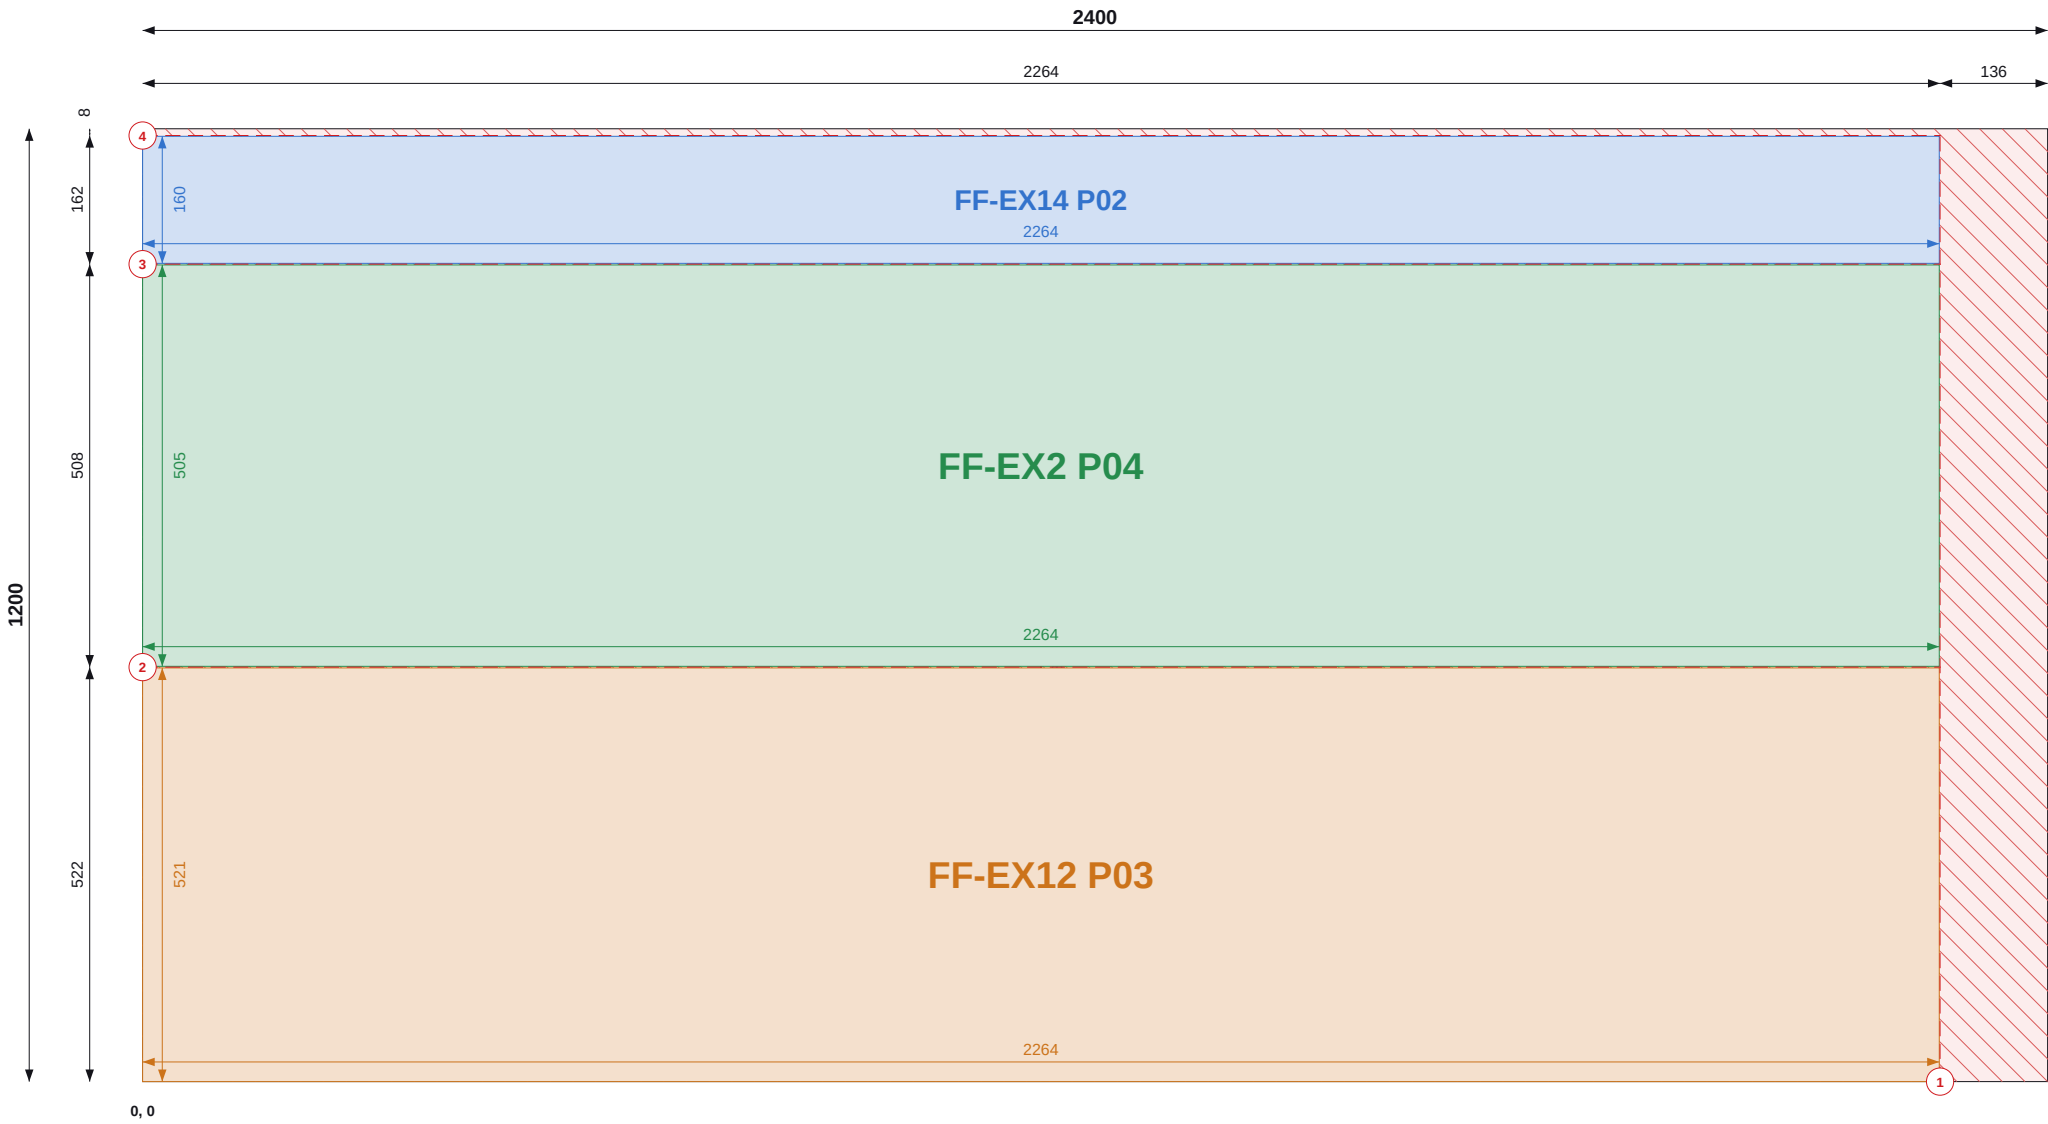

Top / left chains = saw cut positions (to cut centres). Coloured = part size and position.

SHEET 9 OF 23

THIS SHEET

Item	Value
Parts	3
Used / waste	93.3% / 0.19 m2
Reusable offcuts	0
Saw cuts / shared	4 / 2

PIECES (POSITION = BOTTOM-LEFT CORNER)

Label	Size	X, Y
FF-EX14 P02	160 x 2264	0, 1030
FF-EX2 P04	505 x 2264	0, 523
FF-EX12 P03	521 x 2264	0, 0

NOTES

- Cut from PIR 120mm 1200x2400, 2mm saw kerf. Viewed on the face; dimensions from the sheet's bottom-left corner (0,0). Red numbered lines = saw cuts in order, each edge to edge.
- Coloured dimensions belong to the part of that colour: its width and height, and its position from the sheet edges. Raked parts: corner coordinates at each corner.
- Red hatch = waste. Labels = panel + piece mark on the manufacture drawing.

REVISIONS

REV	DATE	DESCRIPTION
C01	13.09.26	Construction issue



TLS TIMBER FRAME

Design & Manufacture

Scan: 3D model + drawings



CLIENT	PROJECT
MP Adams	MP Adams Plot 3, Eckington


DRAWING TITLE
PIR CUTTING - FIRST FLOOR - SHEET 9 OF 23

PIR 120mm 1200x2400 | First Floor

SCALE	SIZE	DATE	DRAWN
NTS	A3	13.09.26	TS

STATUS	DRAWING No.	REV
CONSTRUCTION	P3-CP-PIR-02 / 09	C01

Do not scale. All dimensions in mm. Check all dimensions on site.

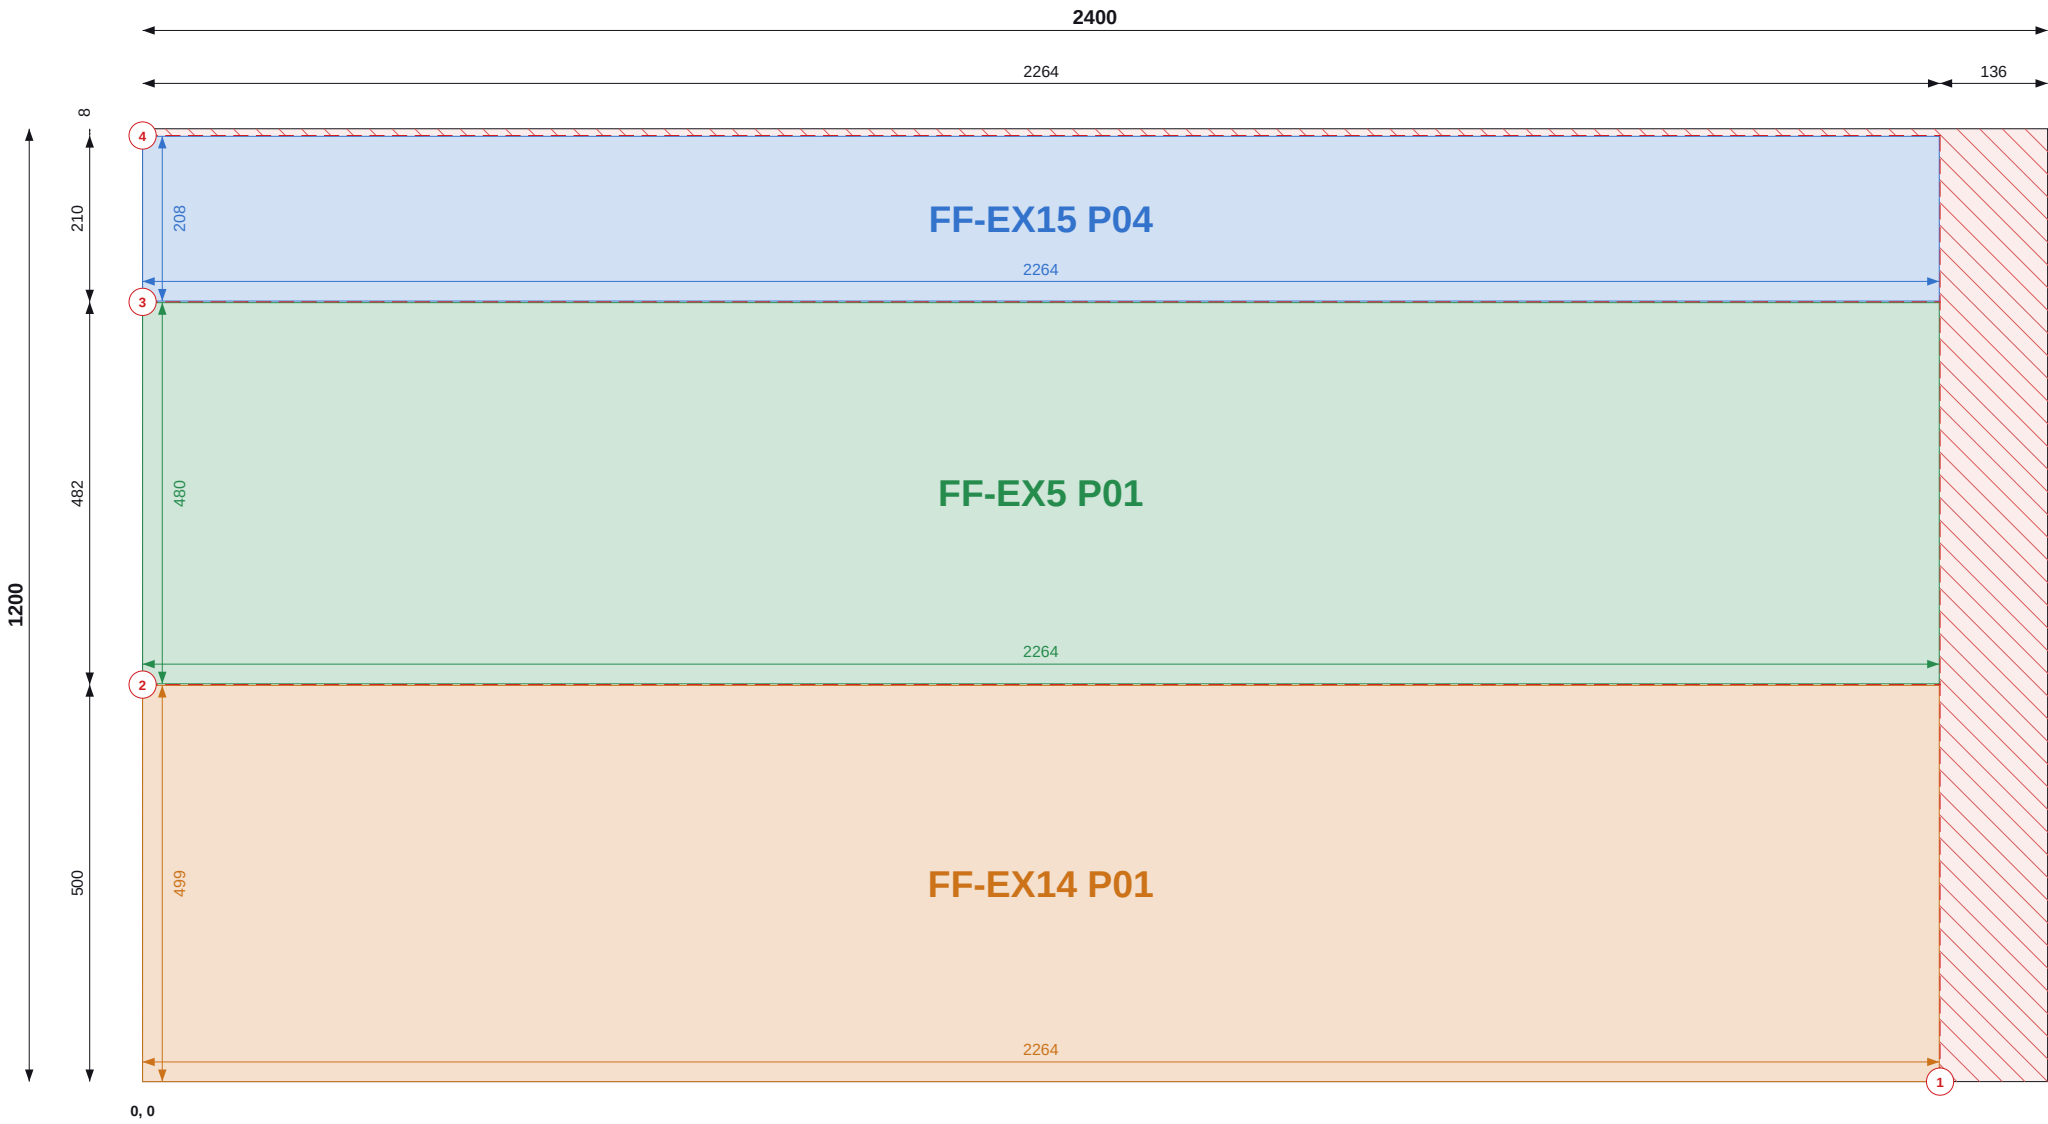

Top / left chains = saw cut positions (to cut centres). Coloured = part size and position.

SHEET 10 OF 23

THIS SHEET

Item	Value
Parts	3
Used / waste	93.3% / 0.19 m2
Reusable offcuts	0
Saw cuts / shared	4 / 2

PIECES (POSITION = BOTTOM-LEFT CORNER)

Label	Size	X, Y
FF-EX15 P04	208 x 2264	0, 983
FF-EX5 P01	480 x 2264	0, 501
FF-EX14 P01	499 x 2264	0, 0

NOTES

- Cut from PIR 120mm 1200x2400, 2mm saw kerf. Viewed on the face; dimensions from the sheet's bottom-left corner (0,0). Red numbered lines = saw cuts in order, each edge to edge.
- Coloured dimensions belong to the part of that colour: its width and height, and its position from the sheet edges. Raked parts: corner coordinates at each corner.
- Red hatch = waste. Labels = panel + piece mark on the manufacture drawing.

REVISIONS

REV	DATE	DESCRIPTION
C01	13.09.26	Construction issue



TLS TIMBER FRAME

Design & Manufacture

Scan: 3D model + drawings




CLIENT	PROJECT
MP Adams	MP Adams Plot 3, Eckington

DRAWING TITLE			
PIR CUTTING - FIRST FLOOR - SHEET 10 OF 23			
PIR 120mm 1200x2400 First Floor			

SCALE	SIZE	DATE	DRAWN
NTS	A3	13.09.26	TS

STATUS	DRAWING No.	REV
CONSTRUCTION	P3-CP-PIR-02 / 10	C01

Do not scale. All dimensions in mm. Check all dimensions on site.

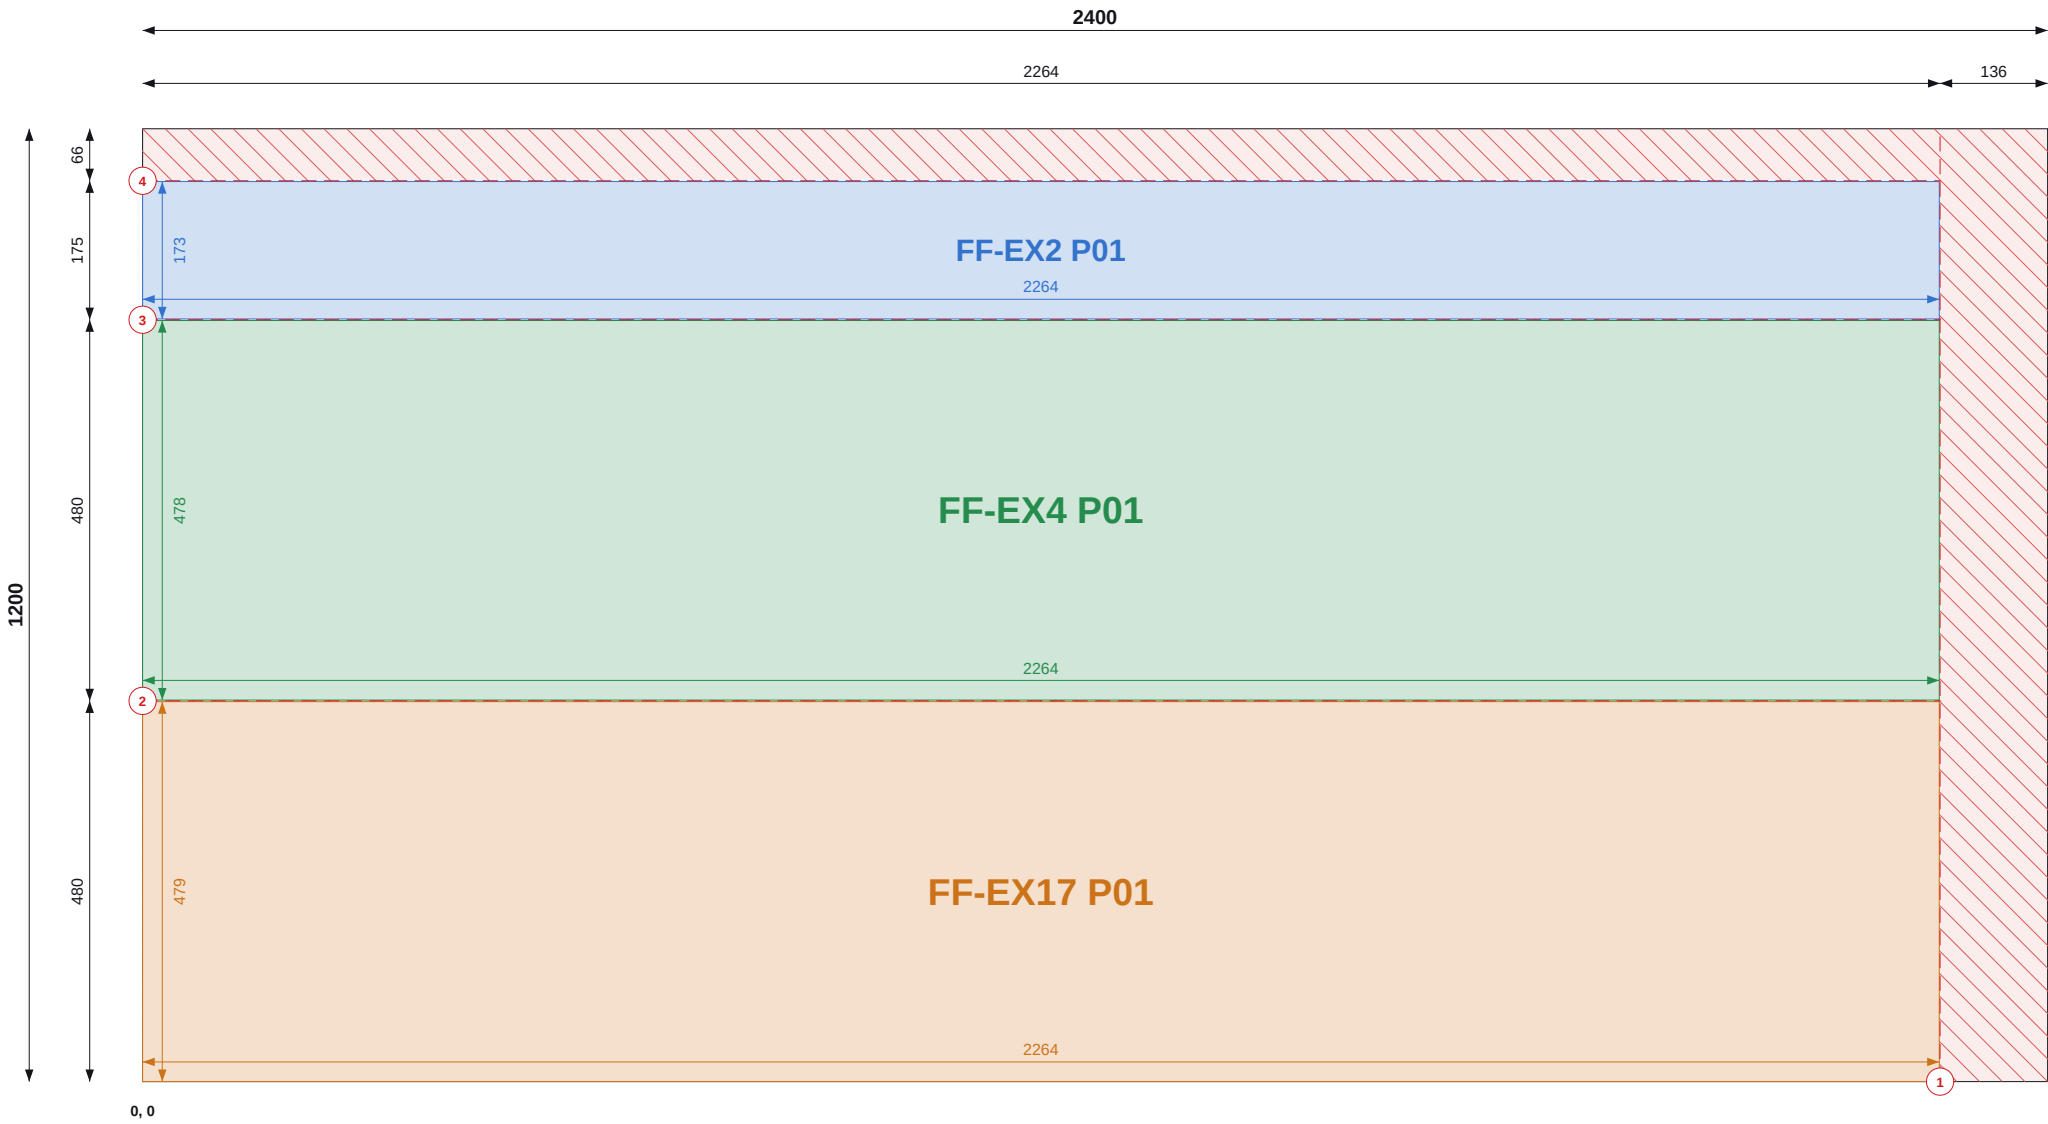

SHEET 11 OF 23

THIS SHEET

Item	Value
Parts	3
Used / waste	88.8% / 0.32 m2
Reusable offcuts	0
Saw cuts / shared	4 / 2

PIECES (POSITION = BOTTOM-LEFT CORNER)

Label	Size	X, Y
FF-EX2 P01	173 x 2264	0, 960
FF-EX4 P01	478 x 2264	0, 481
FF-EX17 P01	479 x 2264	0, 0

NOTES

- Cut from PIR 120mm 1200x2400, 2mm saw kerf. Viewed on the face; dimensions from the sheet's bottom-left corner (0,0). Red numbered lines = saw cuts in order, each edge to edge.
- Coloured dimensions belong to the part of that colour: its width and height, and its position from the sheet edges. Raked parts: corner coordinates at each corner.
- Red hatch = waste. Labels = panel + piece mark on the manufacture drawing.

REVISIONS

REV	DATE	DESCRIPTION
C01	13.09.26	Construction issue



TLS TIMBER FRAME

Design & Manufacture

Scan: 3D model + drawings




CLIENT	PROJECT
MP Adams	MP Adams Plot 3, Eckington

DRAWING TITLE			
PIR CUTTING - FIRST FLOOR - SHEET 11 OF 23			
PIR 120mm 1200x2400 First Floor			

SCALE	SIZE	DATE	DRAWN
NTS	A3	13.09.26	TS

STATUS	DRAWING No.	REV
CONSTRUCTION	P3-CP-PIR-02 / 11	C01

Do not scale. All dimensions in mm. Check all dimensions on site.

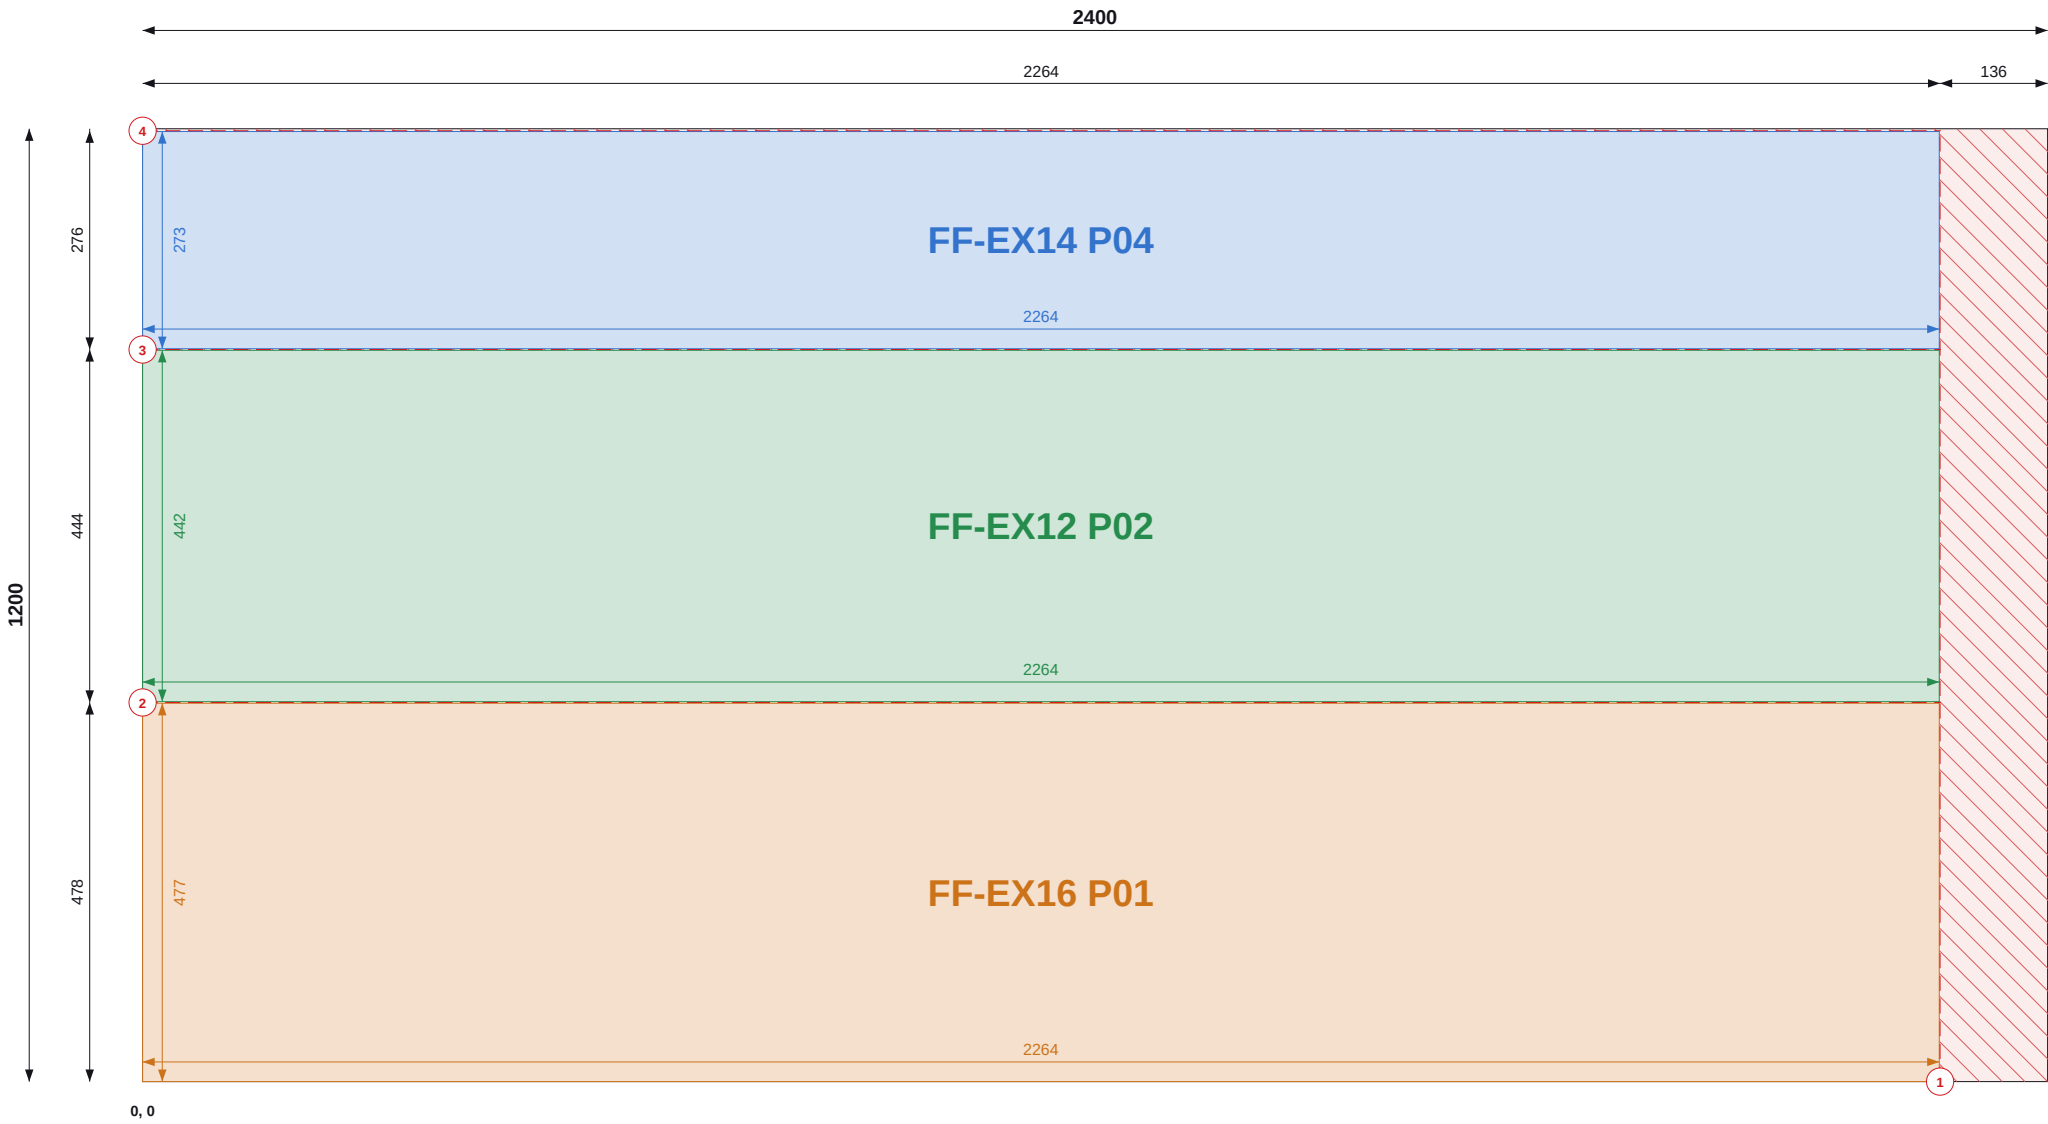

Top / left chains = saw cut positions (to cut centres). Coloured = part size and position.

SHEET 12 OF 23

THIS SHEET

Item	Value
Parts	3
Used / waste	93.7% / 0.18 m2
Reusable offcuts	0
Saw cuts / shared	4 / 2

PIECES (POSITION = BOTTOM-LEFT CORNER)

Label	Size	X, Y
FF-EX14 P04	273 x 2264	0, 923
FF-EX12 P02	442 x 2264	0, 479
FF-EX16 P01	477 x 2264	0, 0

NOTES

- Cut from PIR 120mm 1200x2400, 2mm saw kerf. Viewed on the face; dimensions from the sheet's bottom-left corner (0,0). Red numbered lines = saw cuts in order, each edge to edge.
- Coloured dimensions belong to the part of that colour: its width and height, and its position from the sheet edges. Raked parts: corner coordinates at each corner.
- Red hatch = waste. Labels = panel + piece mark on the manufacture drawing.

REVISIONS

REV	DATE	DESCRIPTION
C01	13.09.26	Construction issue



TLS TIMBER FRAME

Design & Manufacture

Scan: 3D model + drawings



CLIENT	PROJECT
MP Adams	MP Adams Plot 3, Eckington


DRAWING TITLE
PIR CUTTING - FIRST FLOOR - SHEET 12 OF 23

PIR 120mm 1200x2400 | First Floor

SCALE	SIZE	DATE	DRAWN
NTS	A3	13.09.26	TS

STATUS	DRAWING No.	REV
CONSTRUCTION	P3-CP-PIR-02 / 12	C01

Do not scale. All dimensions in mm. Check all dimensions on site.

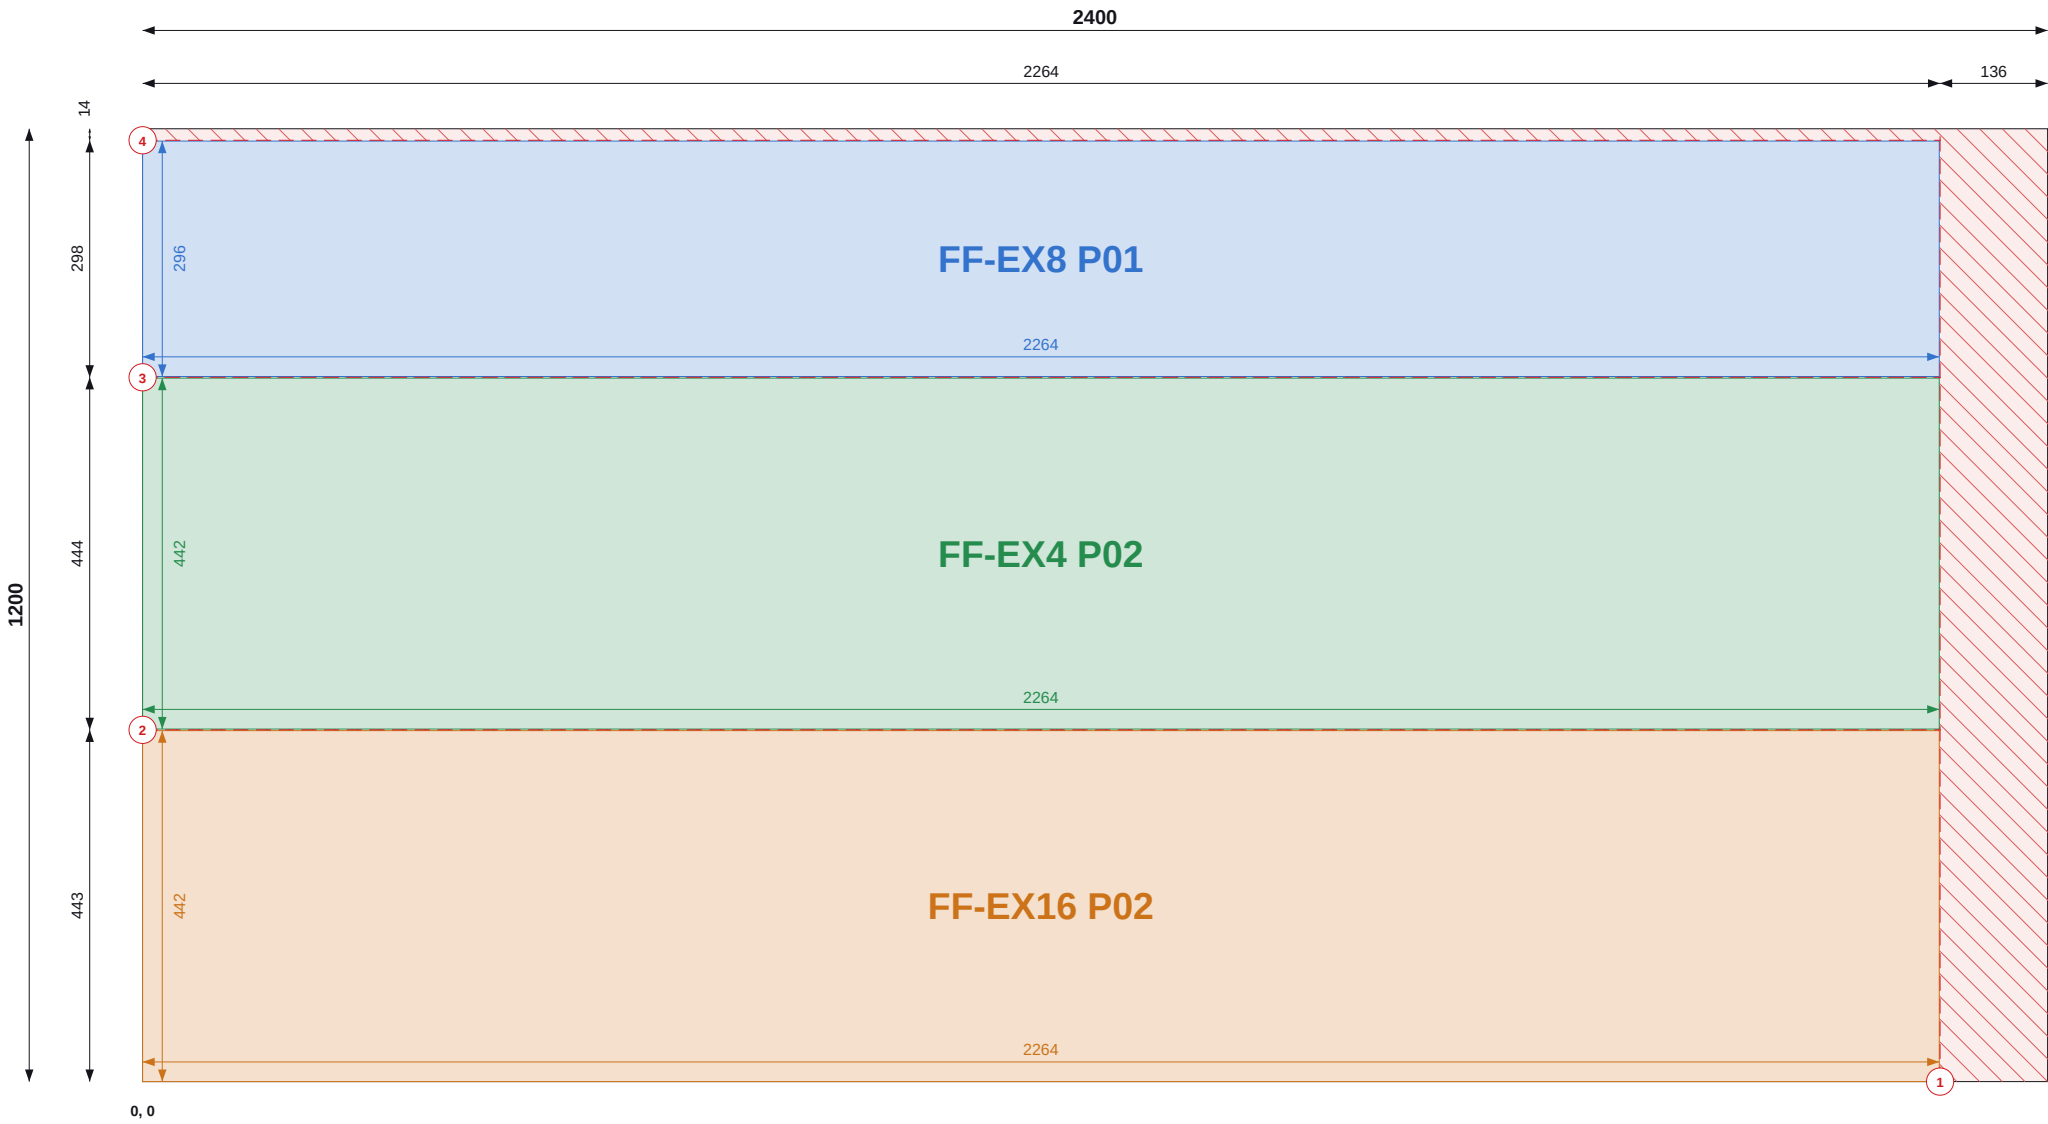

Top / left chains = saw cut positions (to cut centres). Coloured = part size and position.

SHEET 13 OF 23

THIS SHEET

Item	Value
Parts	3
Used / waste	92.8% / 0.21 m2
Reusable offcuts	0
Saw cuts / shared	4 / 2

PIECES (POSITION = BOTTOM-LEFT CORNER)

Label	Size	X, Y
FF-EX8 P01	296 x 2264	0, 888
FF-EX4 P02	442 x 2264	0, 444
FF-EX16 P02	442 x 2264	0, 0

NOTES

- Cut from PIR 120mm 1200x2400, 2mm saw kerf. Viewed on the face; dimensions from the sheet's bottom-left corner (0,0). Red numbered lines = saw cuts in order, each edge to edge.
- Coloured dimensions belong to the part of that colour: its width and height, and its position from the sheet edges. Raked parts: corner coordinates at each corner.
- Red hatch = waste. Labels = panel + piece mark on the manufacture drawing.

REVISIONS

REV	DATE	DESCRIPTION
C01	13.09.26	Construction issue



TLS TIMBER FRAME

Design & Manufacture

Scan: 3D model + drawings




CLIENT	PROJECT
MP Adams	MP Adams Plot 3, Eckington

DRAWING TITLE			
PIR CUTTING - FIRST FLOOR - SHEET 13 OF 23			
PIR 120mm 1200x2400 First Floor			

SCALE	SIZE	DATE	DRAWN
NTS	A3	13.09.26	TS

STATUS	DRAWING No.	REV
CONSTRUCTION	P3-CP-PIR-02 / 13	C01

Do not scale. All dimensions in mm. Check all dimensions on site.

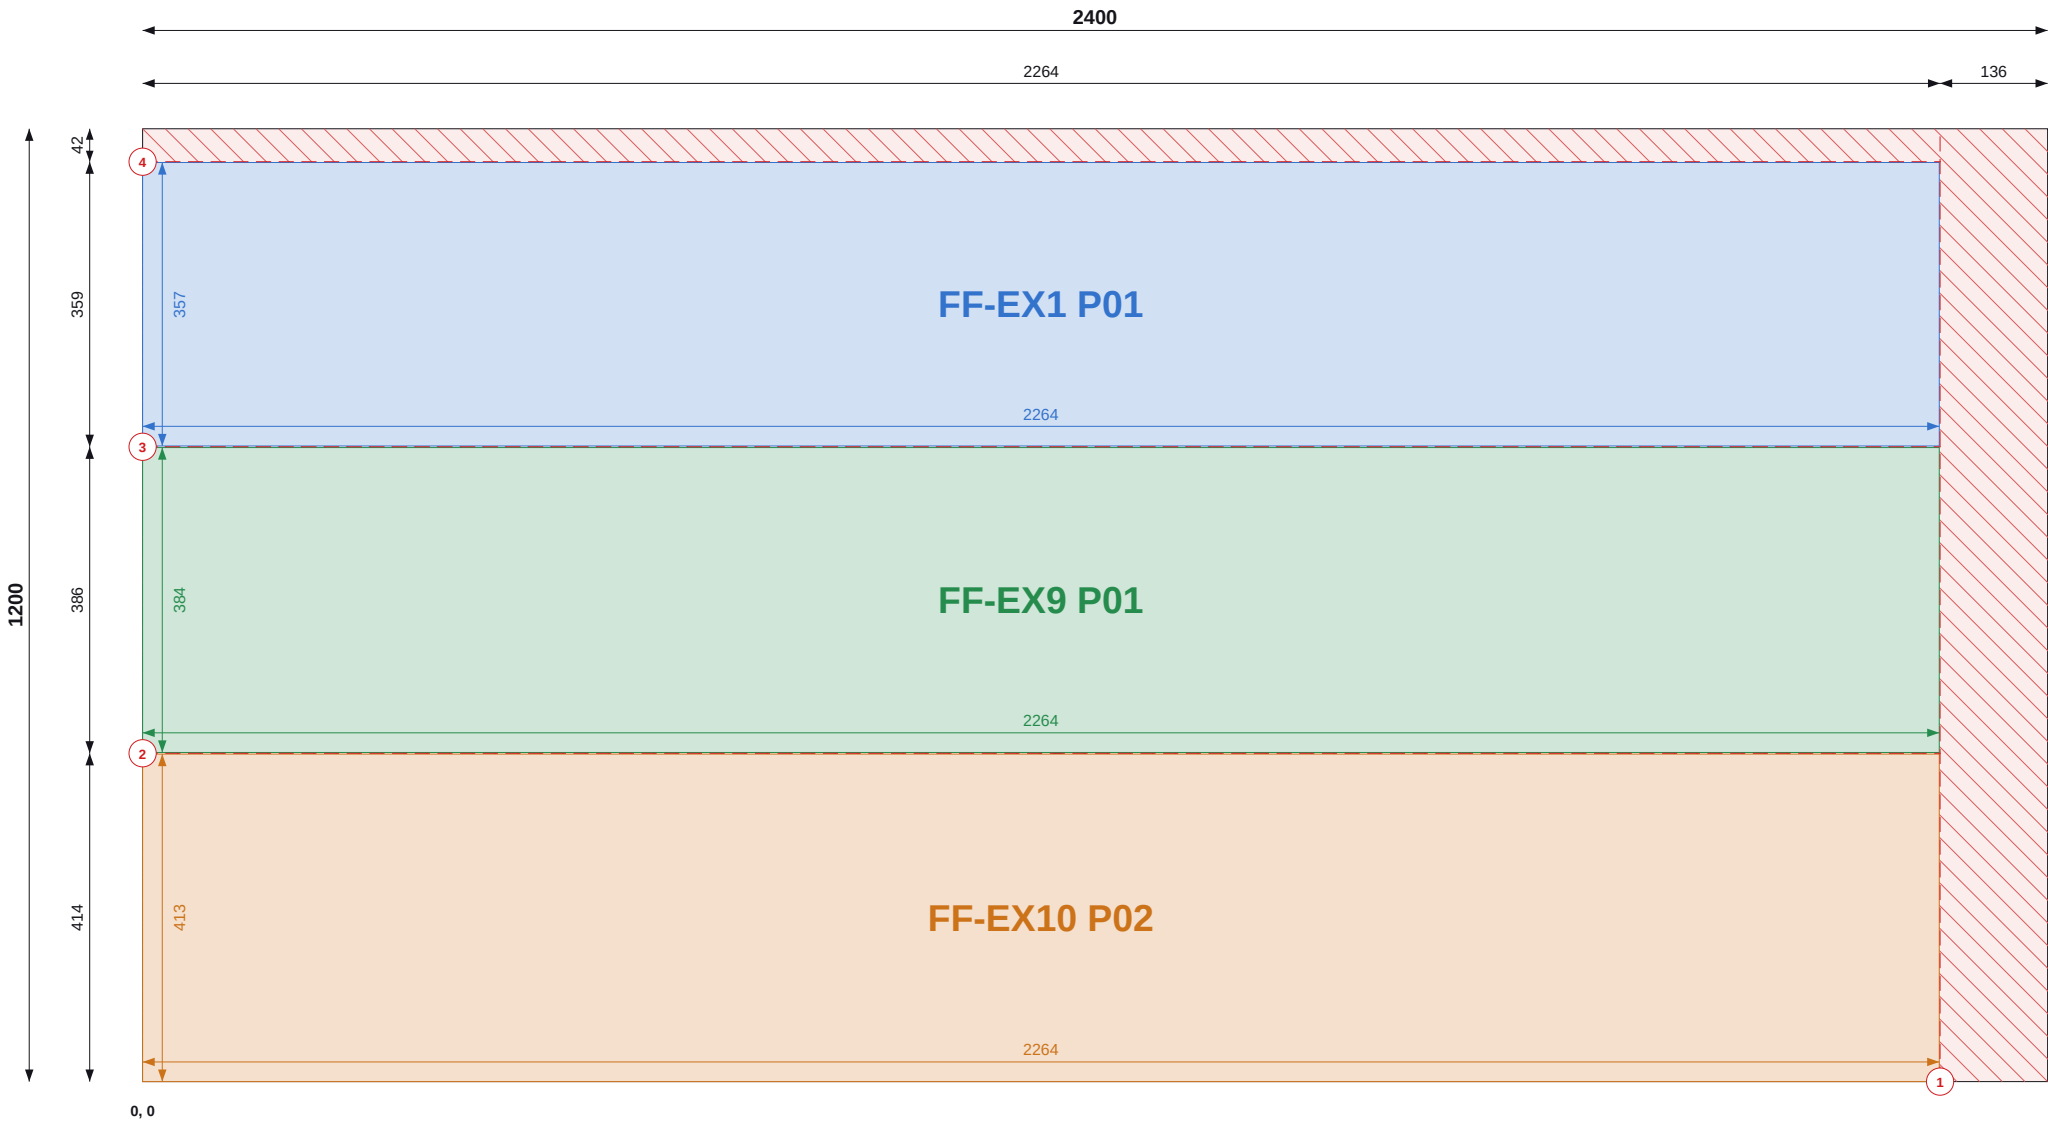

Top / left chains = saw cut positions (to cut centres). Coloured = part size and position.

SHEET 14 OF 23

THIS SHEET

Item	Value
Parts	3
Used / waste	90.7% / 0.27 m2
Reusable offcuts	0
Saw cuts / shared	4 / 2

PIECES (POSITION = BOTTOM-LEFT CORNER)

Label	Size	X, Y
FF-EX1 P01	357 x 2264	0, 800
FF-EX9 P01	384 x 2264	0, 415
FF-EX10 P02	413 x 2264	0, 0

NOTES

- Cut from PIR 120mm 1200x2400, 2mm saw kerf. Viewed on the face; dimensions from the sheet's bottom-left corner (0,0). Red numbered lines = saw cuts in order, each edge to edge.
- Coloured dimensions belong to the part of that colour: its width and height, and its position from the sheet edges. Raked parts: corner coordinates at each corner.
- Red hatch = waste. Labels = panel + piece mark on the manufacture drawing.

REVISIONS

REV	DATE	DESCRIPTION
C01	13.09.26	Construction issue



TLS TIMBER FRAME

Design & Manufacture

Scan: 3D model + drawings



CLIENT	PROJECT
MP Adams	MP Adams Plot 3, Eckington

DRAWING TITLE
PIR CUTTING - FIRST FLOOR - SHEET 14 OF 23

PIR 120mm 1200x2400 | First Floor

SCALE	SIZE	DATE	DRAWN
NTS	A3	13.09.26	TS

STATUS	DRAWING No.	REV
CONSTRUCTION	P3-CP-PIR-02 / 14	C01



SHEET 15 OF 23

THIS SHEET

Item	Value
Parts	37
Used / waste	92.3% / 0.22 m2
Reusable offcuts	0
Saw cuts / shared	39 / 36

PIECES (POSITION = BOTTOM-LEFT CORNER)

Label	Size	X, Y
FF-EX11 P06	284 x 69	0, 1121
FF-EX15 P06	260 x 69	286, 1121
FF-EX13 P05	255 x 69	548, 1121
FF-EX19 P08	130 x 69	805, 1121
FF-EX8 P03	111 x 69	937, 1121
FF-EX2 P06	104 x 69	1050, 1121
FF-EX17 P05	95 x 69	1156, 1121
FF-EX21 P05	95 x 69	1253, 1121
FF-EX5 P05	95 x 69	1350, 1121
FF-EX19 P09	65 x 69	1447, 1121
FF-EX21 P08	57 x 69	1513, 1121
FF-EX5 P08	55 x 69	1572, 1121
FF-EX21 P07	42 x 69	1629, 1121
FF-EX5 P07	42 x 69	1673, 1121
FF-EX8 P05	21 x 69	1716, 1121
FF-EX11 P04	18 x 69	1739, 1121
FF-EX11 P07	18 x 69	1759, 1121
FF-EX13 P03	18 x 69	1779, 1121
FF-EX13 P06	18 x 69	1799, 1121
FF-EX15 P05	18 x 69	1819, 1121
FF-EX15 P08	18 x 69	1839, 1121
FF-EX17 P04	18 x 69	1859, 1121
FF-EX17 P08	18 x 69	1879, 1121
FF-EX19 P06	18 x 69	1899, 1121
FF-EX19 P10	18 x 69	1919, 1121
FF-EX2 P05	18 x 69	1939, 1121
FF-EX2 P09	18 x 69	1959, 1121
FF-EX21 P04	18 x 69	1979, 1121
FF-EX21 P10	18 x 69	1999, 1121
FF-EX5 P04	18 x 69	2019, 1121
FF-EX5 P10	18 x 69	2039, 1121
FF-EX8 P02	18 x 69	2059, 1121
FF-EX8 P06	18 x 69	2079, 1121
FF-EX19 P01	155 x 2264	0, 964
FF-EX5 P02	288 x 2264	0, 674
FF-EX17 P02	313 x 2264	0, 359
FF-EX13 P01	357 x 2264	0, 0

NOTES

1. Cut from PIR 120mm 1200x2400, 2mm saw kerf. Viewed on the face; dimensions from the sheet's bottom-left corner (0,0). Red numbered lines = saw cuts in order, each edge to edge.
2. Coloured dimensions belong to the part of that colour: its width and height, and its position from the sheet edges. Raked parts: corner coordinates at each corner.
3. Red hatch = waste. Labels = panel + piece mark on the manufacture drawing.

REVISIONS

REV	DATE	DESCRIPTION
C01	13.09.26	Construction issue



TLS TIMBER FRAME

Design & Manufacture

Scan: 3D model + drawings



CLIENT	PROJECT
MP Adams	MP Adams Plot 3, Eckington

DRAWING TITLE


PIR CUTTING - FIRST FLOOR - SHEET 15 OF 23

PIR 120mm 1200x2400 | First Floor

SCALE	SIZE	DATE	DRAWN
NTS	A3	13.09.26	TS

STATUS	DRAWING No.	REV
CONSTRUCTION	P3-CP-PIR-02 / 15	C01

Do not scale. All dimensions in mm. Check all dimensions on site.

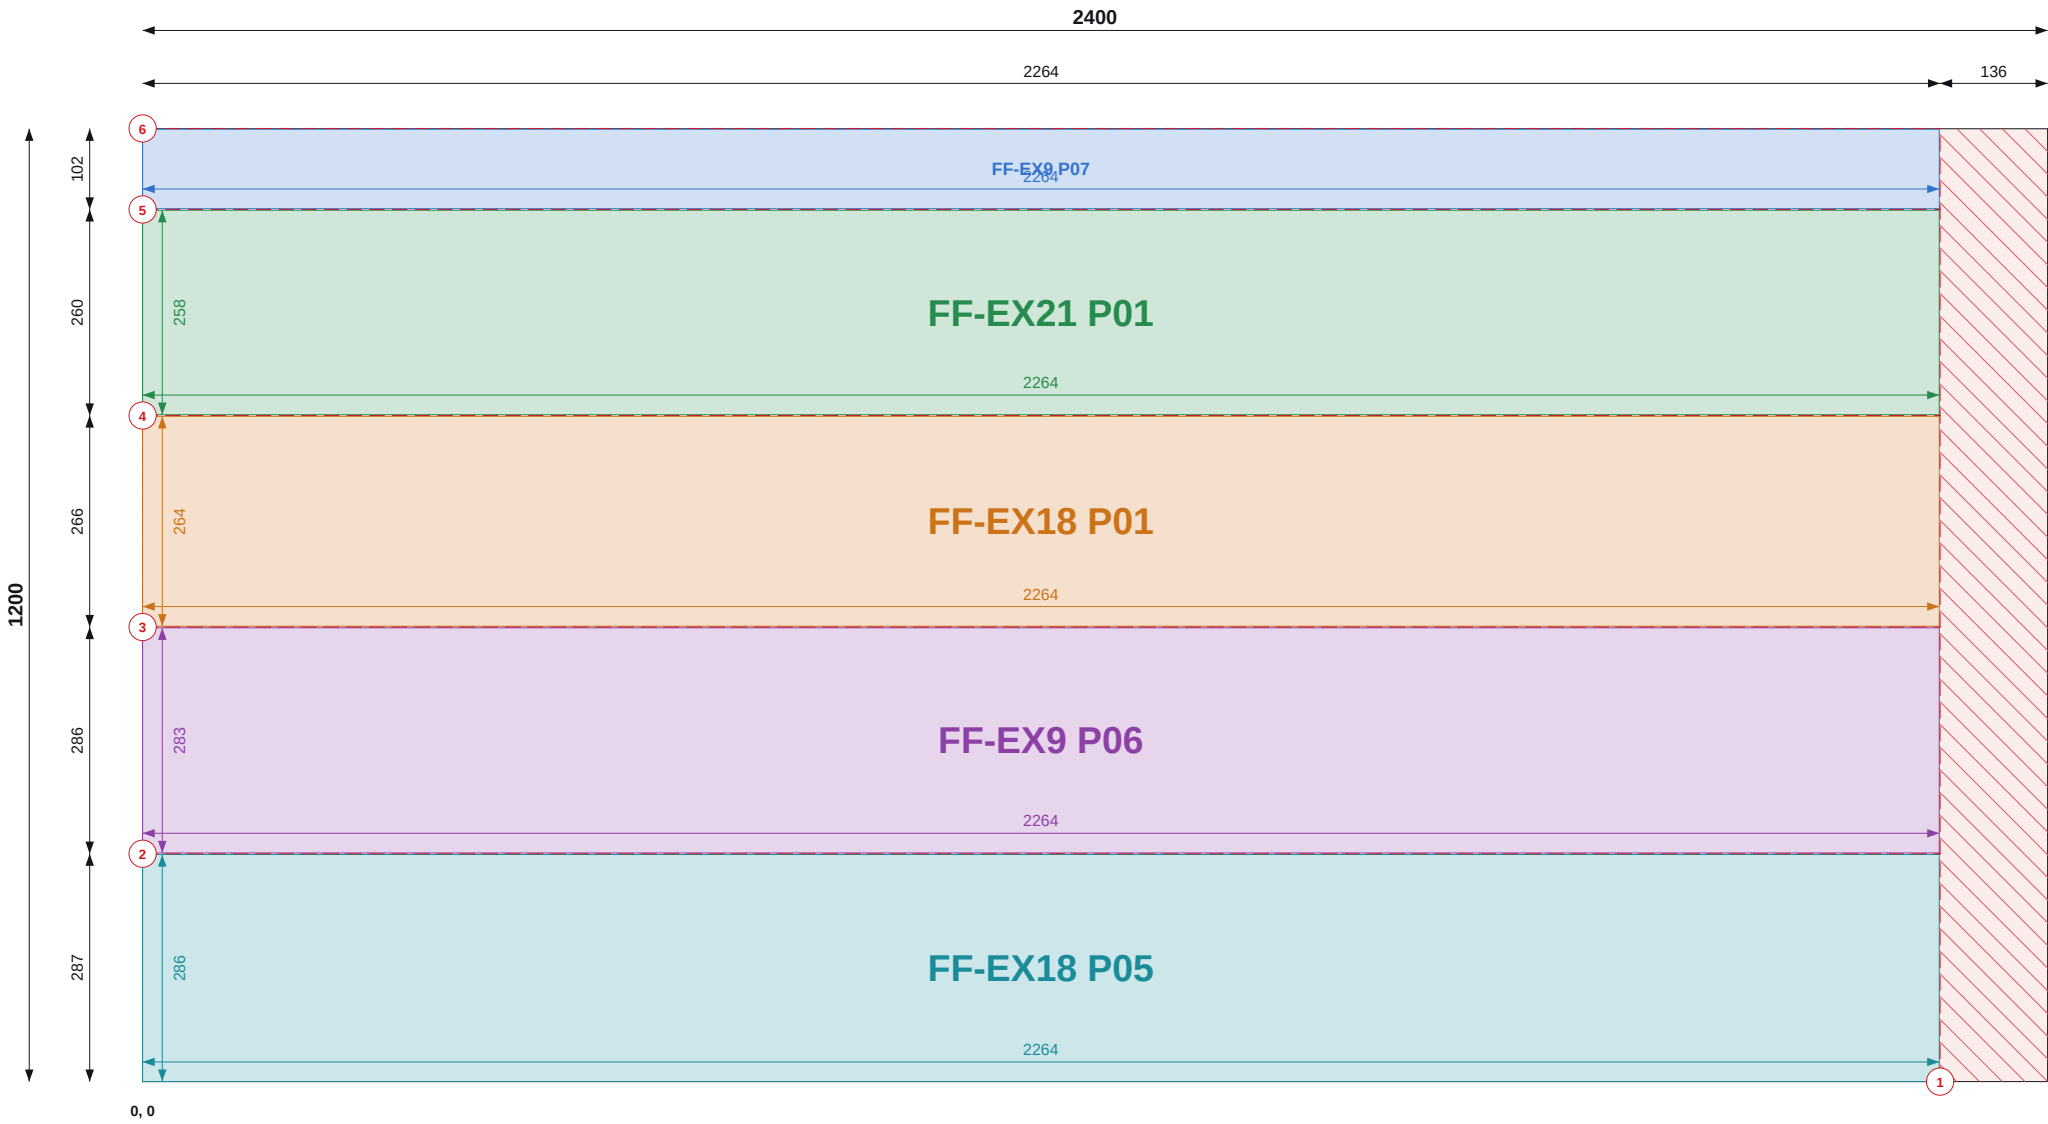

Top / left chains = saw cut positions (to cut centres). Coloured = part size and position.

SHEET 16 OF 23

THIS SHEET

Item	Value
Parts	5
Used / waste	93.6% / 0.18 m2
Reusable offcuts	0
Saw cuts / shared	6 / 4

PIECES (POSITION = BOTTOM-LEFT CORNER)

Label	Size	X, Y
FF-EX9 P07	100 x 2264	0, 1099
FF-EX21 P01	258 x 2264	0, 840
FF-EX18 P01	264 x 2264	0, 574
FF-EX9 P06	283 x 2264	0, 288
FF-EX18 P05	286 x 2264	0, 0

NOTES

- Cut from PIR 120mm 1200x2400, 2mm saw kerf. Viewed on the face; dimensions from the sheet's bottom-left corner (0,0). Red numbered lines = saw cuts in order, each edge to edge.
- Coloured dimensions belong to the part of that colour: its width and height, and its position from the sheet edges. Raked parts: corner coordinates at each corner.
- Red hatch = waste. Labels = panel + piece mark on the manufacture drawing.

REVISIONS

REV	DATE	DESCRIPTION
C01	13.09.26	Construction issue



TLS TIMBER FRAME

Design & Manufacture

Scan: 3D model + drawings



CLIENT	PROJECT
MP Adams	MP Adams Plot 3, Eckington


DRAWING TITLE
PIR CUTTING - FIRST FLOOR - SHEET 16 OF 23

PIR 120mm 1200x2400 | First Floor

SCALE	SIZE	DATE	DRAWN
NTS	A3	13.09.26	TS

STATUS	DRAWING No.	REV
CONSTRUCTION	P3-CP-PIR-02 / 16	C01

Do not scale. All dimensions in mm. Check all dimensions on site.

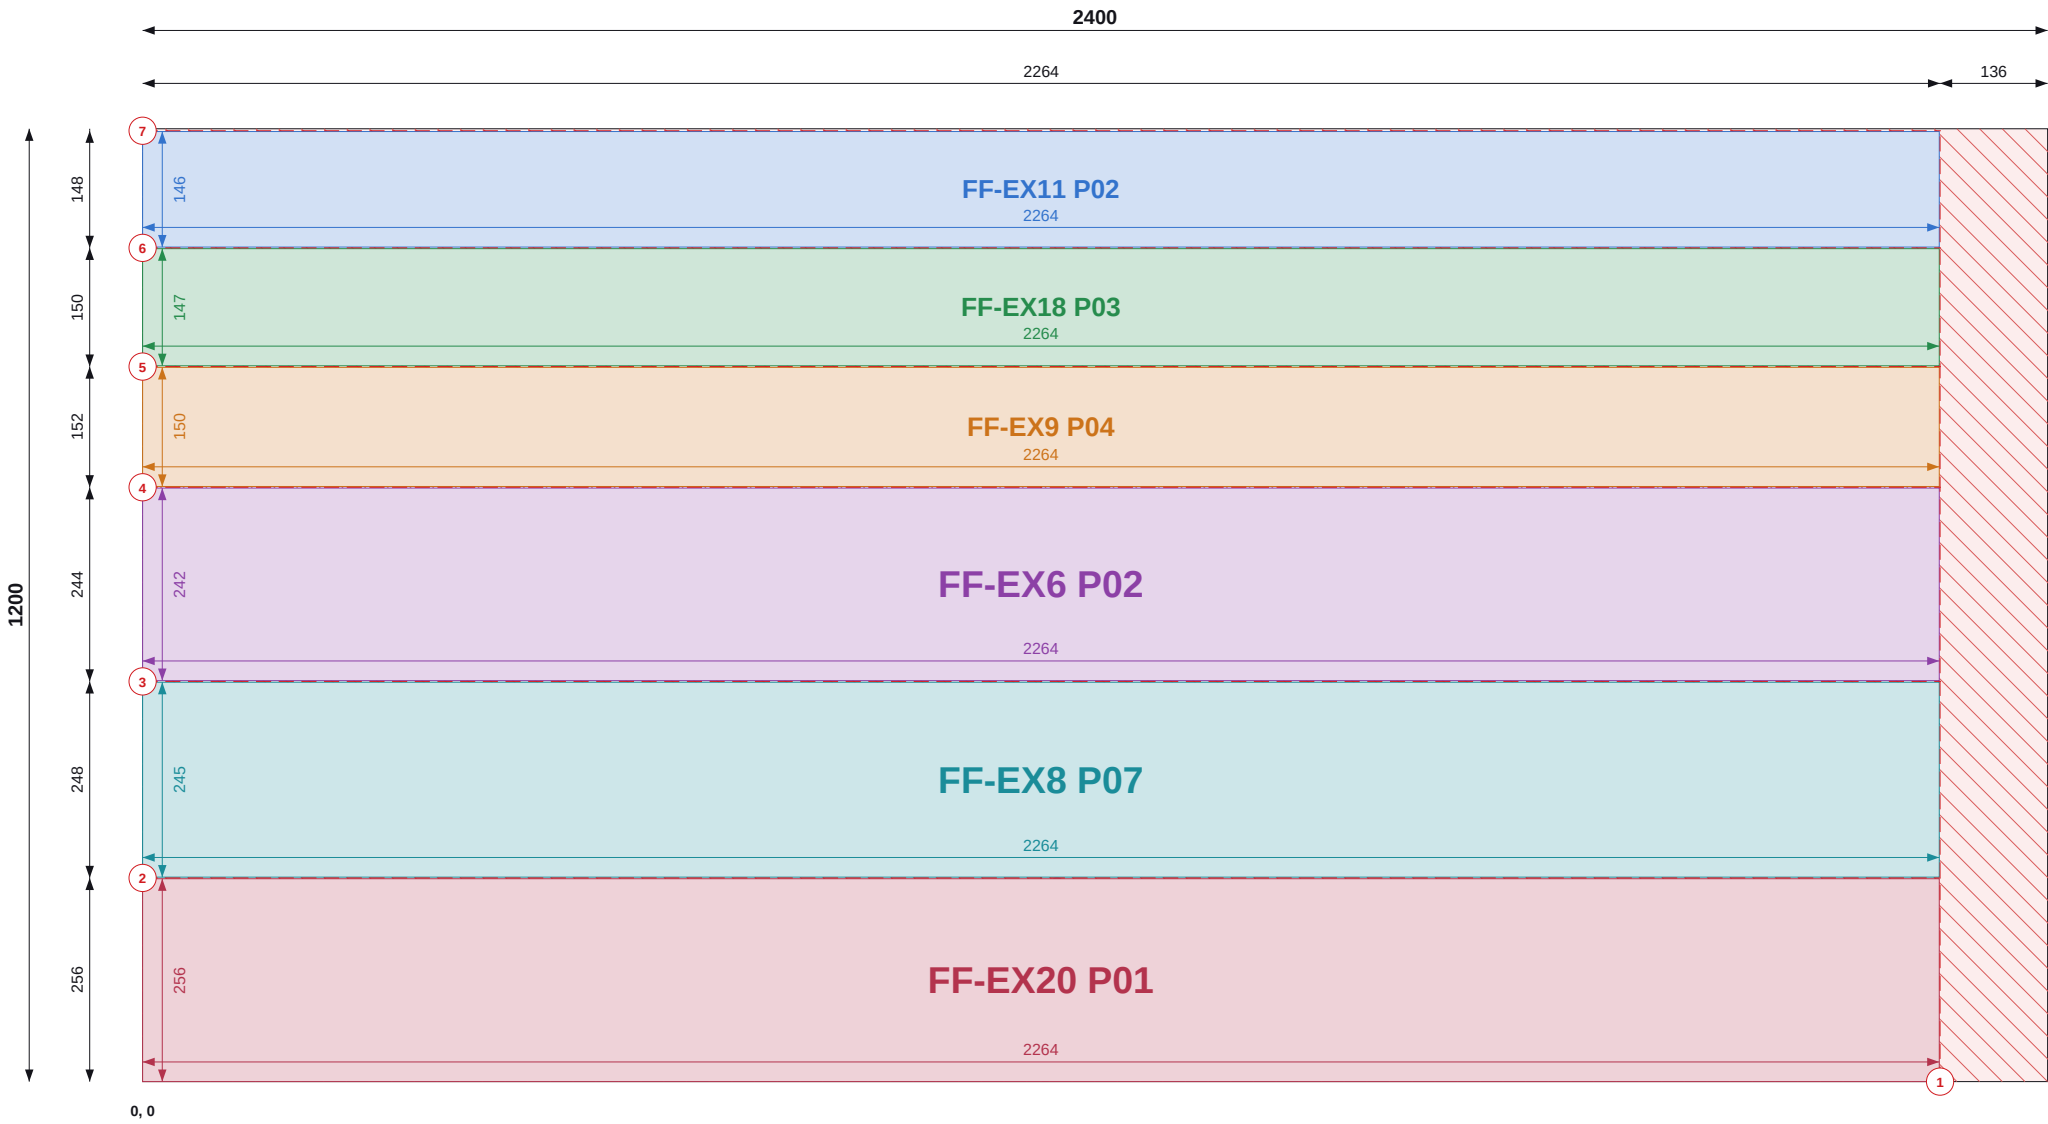

Top / left chains = saw cut positions (to cut centres). Coloured = part size and position.

SHEET 17 OF 23

THIS SHEET

Item	Value
Parts	6
Used / waste	93.3% / 0.19 m2
Reusable offcuts	0
Saw cuts / shared	7 / 5

PIECES (POSITION = BOTTOM-LEFT CORNER)

Label	Size	X, Y
FF-EX11 P02	146 x 2264	0, 1051
FF-EX18 P03	147 x 2264	0, 901
FF-EX9 P04	150 x 2264	0, 749
FF-EX6 P02	242 x 2264	0, 505
FF-EX8 P07	245 x 2264	0, 258
FF-EX20 P01	256 x 2264	0, 0

NOTES

- Cut from PIR 120mm 1200x2400, 2mm saw kerf. Viewed on the face; dimensions from the sheet's bottom-left corner (0,0). Red numbered lines = saw cuts in order, each edge to edge.
- Coloured dimensions belong to the part of that colour: its width and height, and its position from the sheet edges. Raked parts: corner coordinates at each corner.
- Red hatch = waste. Labels = panel + piece mark on the manufacture drawing.

REVISIONS

REV	DATE	DESCRIPTION
C01	13.09.26	Construction issue



TLS TIMBER FRAME
Design & Manufacture
Scan: 3D model + drawings



CLIENT MP Adams	PROJECT MP Adams Plot 3, Eckington
--------------------	---------------------------------------


DRAWING TITLE
PIR CUTTING - FIRST FLOOR - SHEET 17 OF 23

PIR 120mm 1200x2400 | First Floor

SCALE NTS	SIZE A3	DATE 13.09.26	DRAWN TS
--------------	------------	------------------	-------------

STATUS CONSTRUCTION	DRAWING No. P3-CP-PIR-02 / 17	REV C01
-------------------------------	---	-------------------

Do not scale. All dimensions in mm. Check all dimensions on site.

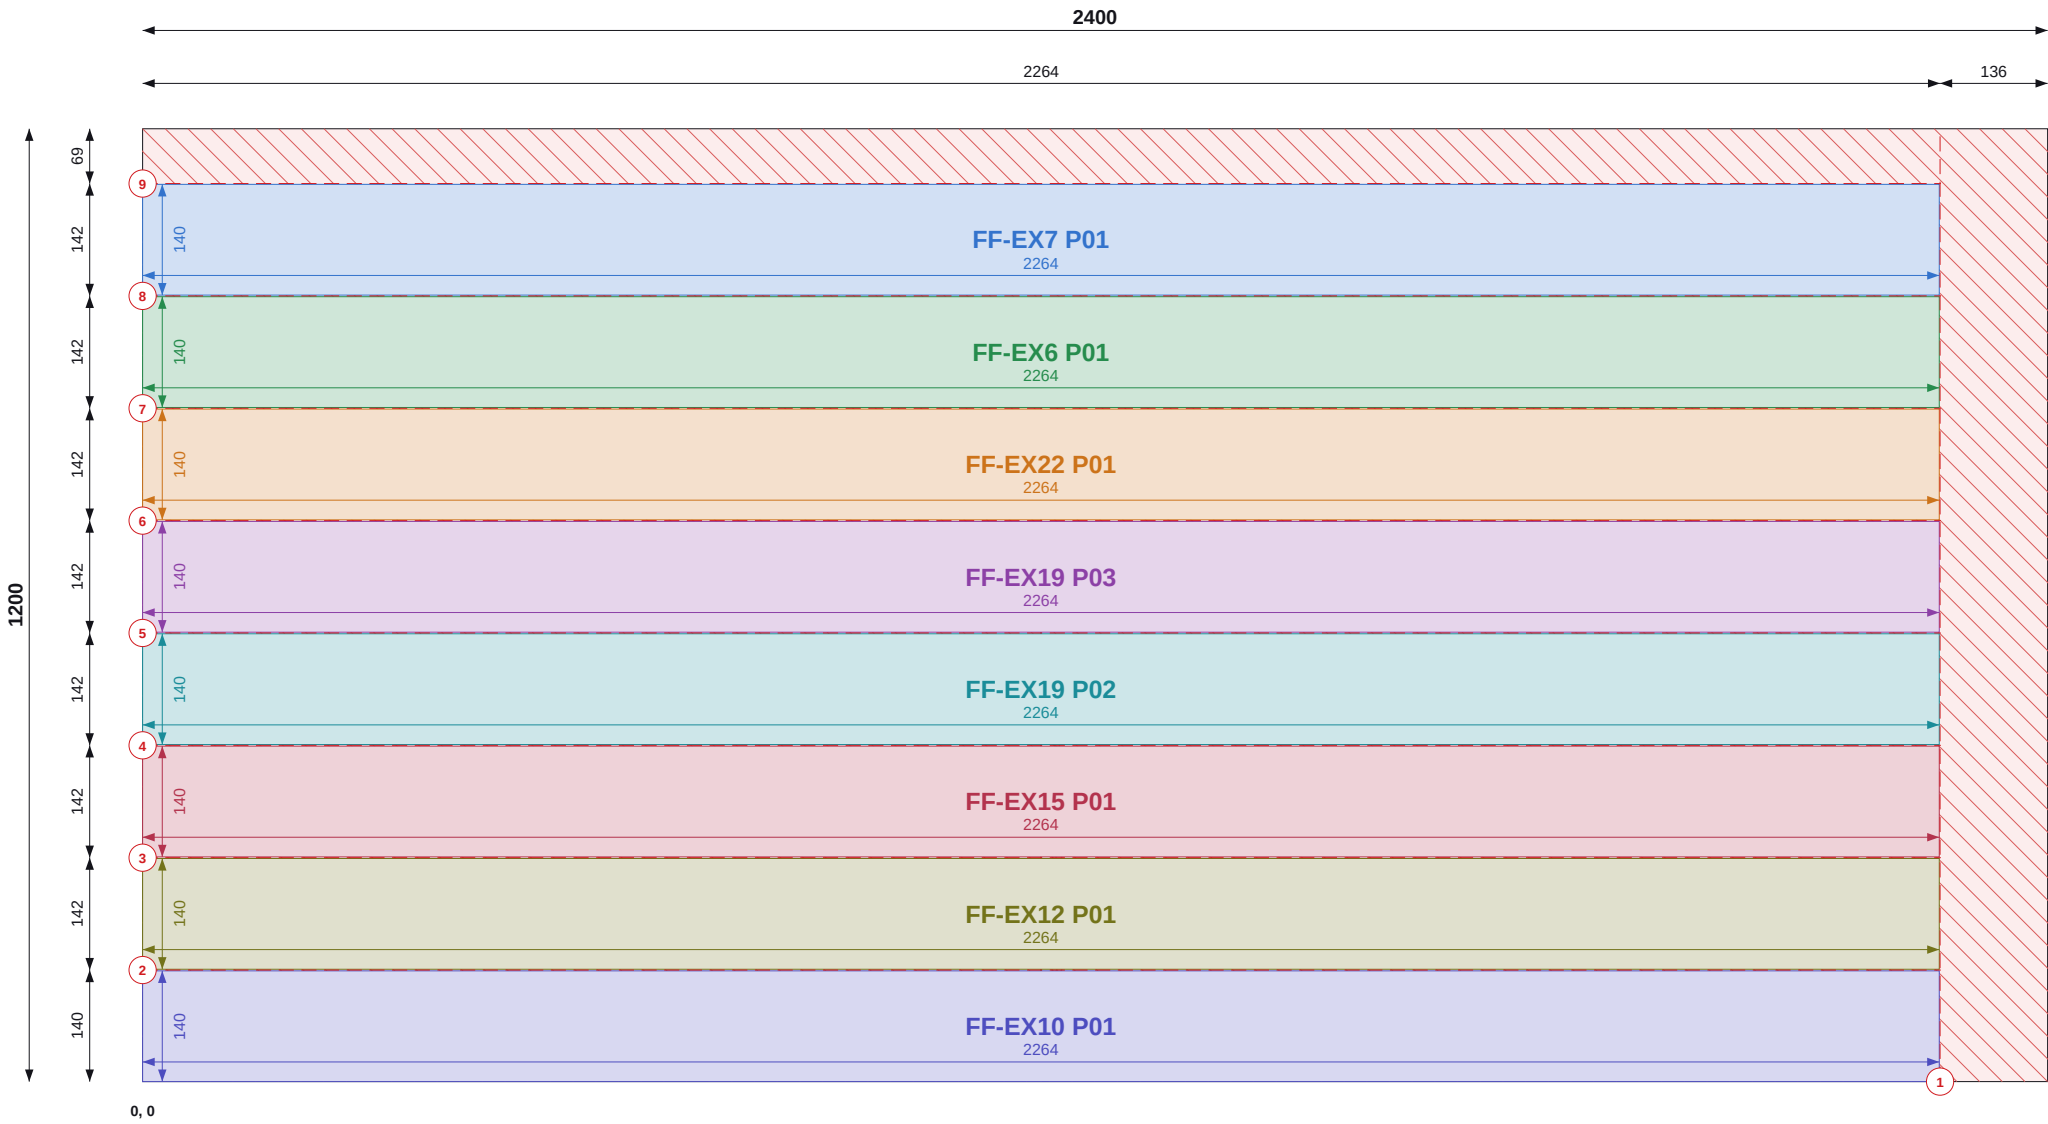

Top / left chains = saw cut positions (to cut centres). Coloured = part size and position.

SHEET 18 OF 23

THIS SHEET

Item	Value
Parts	8
Used / waste	87.7% / 0.35 m2
Reusable offcuts	0
Saw cuts / shared	9 / 7

PIECES (POSITION = BOTTOM-LEFT CORNER)

Label	Size	X, Y
FF-EX7 P01	140 x 2264	0, 991
FF-EX6 P01	140 x 2264	0, 849
FF-EX22 P01	140 x 2264	0, 708
FF-EX19 P03	140 x 2264	0, 566
FF-EX19 P02	140 x 2264	0, 425
FF-EX15 P01	140 x 2264	0, 283
FF-EX12 P01	140 x 2264	0, 142
FF-EX10 P01	140 x 2264	0, 0

NOTES

- Cut from PIR 120mm 1200x2400, 2mm saw kerf. Viewed on the face; dimensions from the sheet's bottom-left corner (0,0). Red numbered lines = saw cuts in order, each edge to edge.
- Coloured dimensions belong to the part of that colour: its width and height, and its position from the sheet edges. Raked parts: corner coordinates at each corner.
- Red hatch = waste. Labels = panel + piece mark on the manufacture drawing.

REVISIONS

REV	DATE	DESCRIPTION
C01	13.09.26	Construction issue



TLS TIMBER FRAME

Design & Manufacture

Scan: 3D model + drawings



CLIENT	PROJECT
MP Adams	MP Adams Plot 3, Eckington


DRAWING TITLE
PIR CUTTING - FIRST FLOOR - SHEET 18 OF 23

PIR 120mm 1200x2400 | First Floor

SCALE	SIZE	DATE	DRAWN
NTS	A3	13.09.26	TS

STATUS	DRAWING No.	REV
CONSTRUCTION	P3-CP-PIR-02 / 18	C01

Do not scale. All dimensions in mm. Check all dimensions on site.

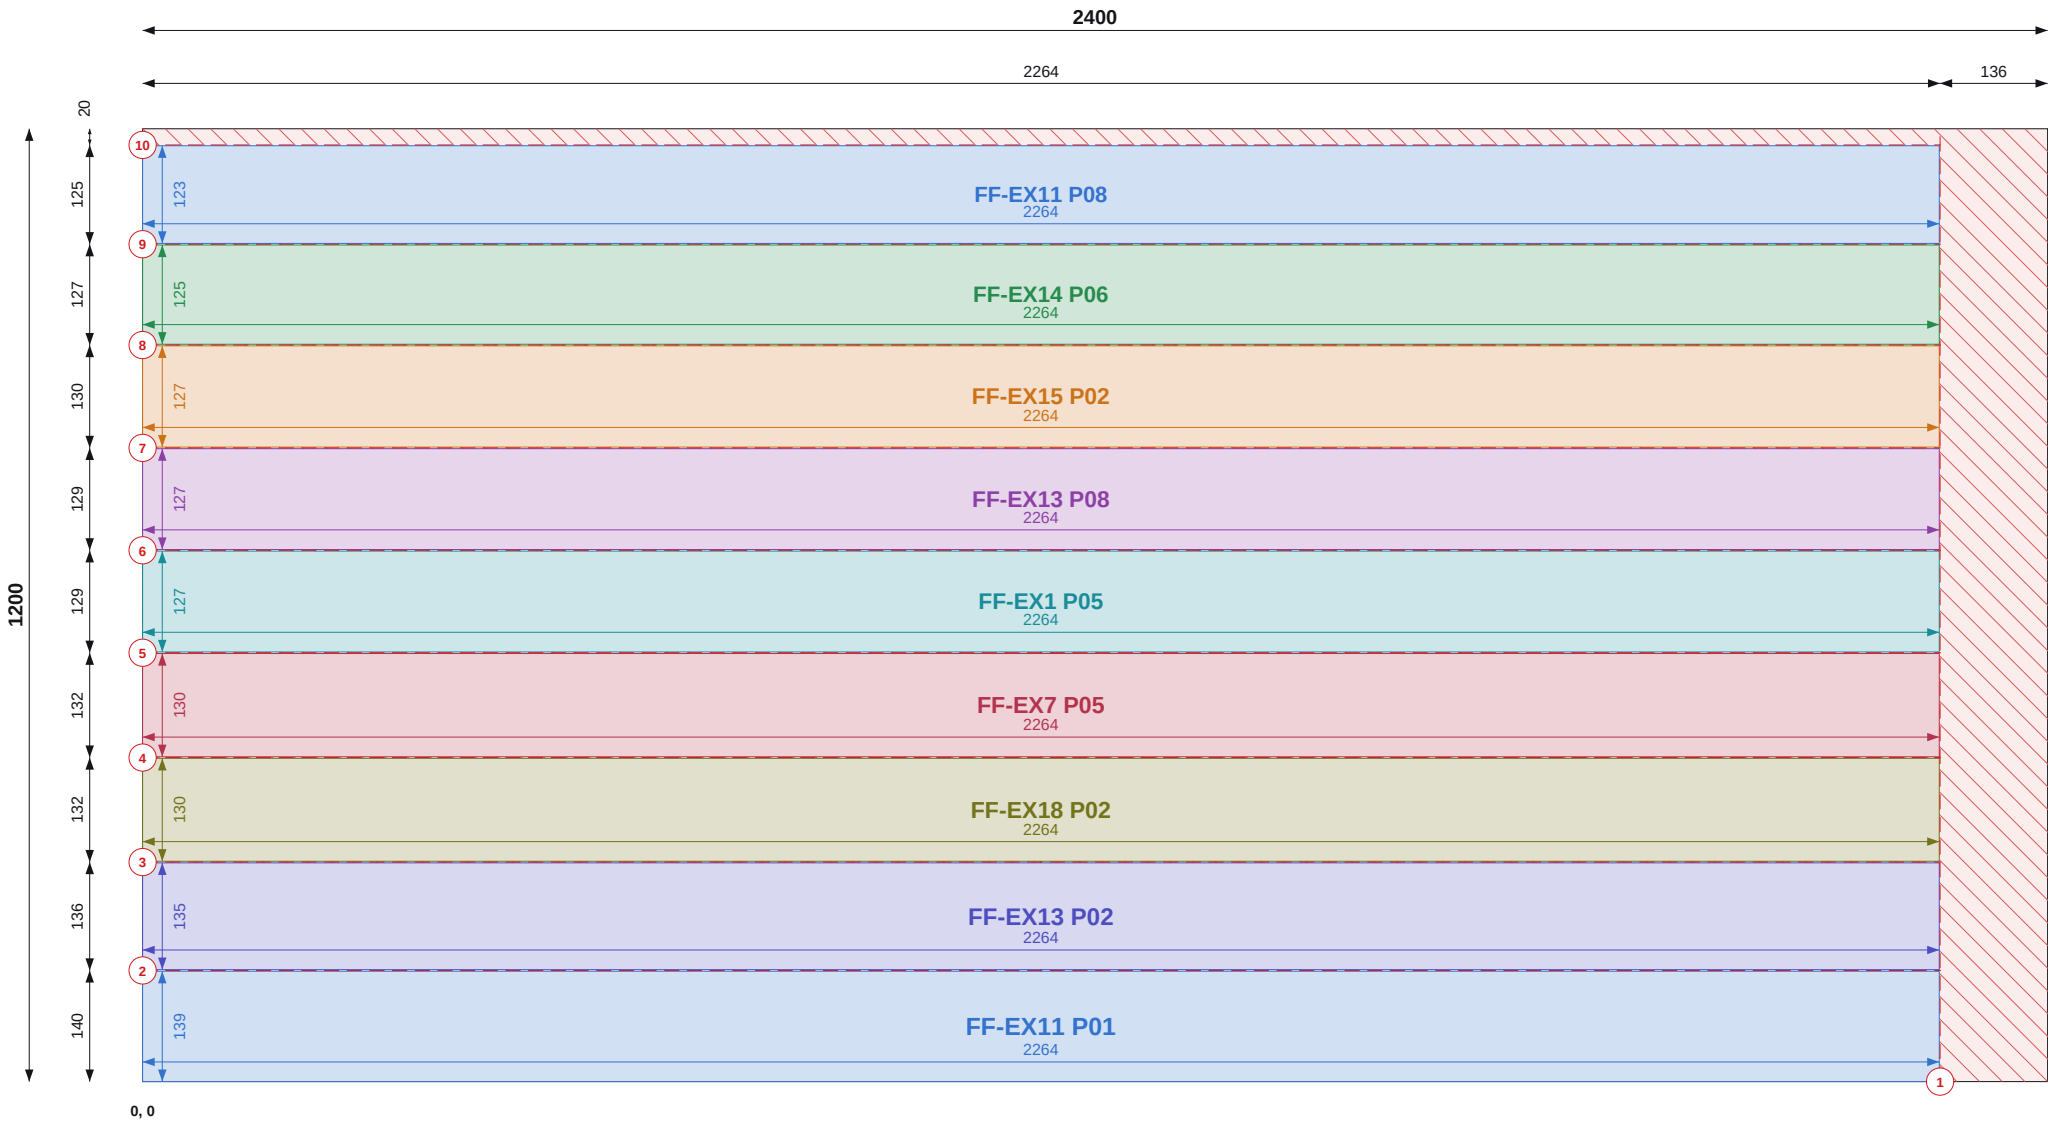

Top / left chains = saw cut positions (to cut centres). Coloured = part size and position.

SHEET 19 OF 23

THIS SHEET

Item	Value
Parts	9
Used / waste	91.4% / 0.25 m2
Reusable offcuts	0
Saw cuts / shared	10 / 8

PIECES (POSITION = BOTTOM-LEFT CORNER)

Label	Size	X, Y
FF-EX11 P08	123 x 2264	0, 1056
FF-EX14 P06	125 x 2264	0, 929
FF-EX15 P02	127 x 2264	0, 799
FF-EX13 P08	127 x 2264	0, 670
FF-EX1 P05	127 x 2264	0, 541
FF-EX7 P05	130 x 2264	0, 409
FF-EX18 P02	130 x 2264	0, 278
FF-EX13 P02	135 x 2264	0, 141
FF-EX11 P01	139 x 2264	0, 0

NOTES

- Cut from PIR 120mm 1200x2400, 2mm saw kerf. Viewed on the face; dimensions from the sheet's bottom-left corner (0,0). Red numbered lines = saw cuts in order, each edge to edge.
- Coloured dimensions belong to the part of that colour: its width and height, and its position from the sheet edges. Raked parts: corner coordinates at each corner.
- Red hatch = waste. Labels = panel + piece mark on the manufacture drawing.

REVISIONS

REV	DATE	DESCRIPTION
C01	13.09.26	Construction issue



TLS TIMBER FRAME

Design & Manufacture

Scan: 3D model + drawings




CLIENT	PROJECT
MP Adams	MP Adams Plot 3, Eckington

DRAWING TITLE
PIR CUTTING - FIRST FLOOR - SHEET 19 OF 23
PIR 120mm 1200x2400 First Floor

SCALE	SIZE	DATE	DRAWN
NTS	A3	13.09.26	TS

STATUS	DRAWING No.	REV
CONSTRUCTION	P3-CP-PIR-02 / 19	C01

Do not scale. All dimensions in mm. Check all dimensions on site.

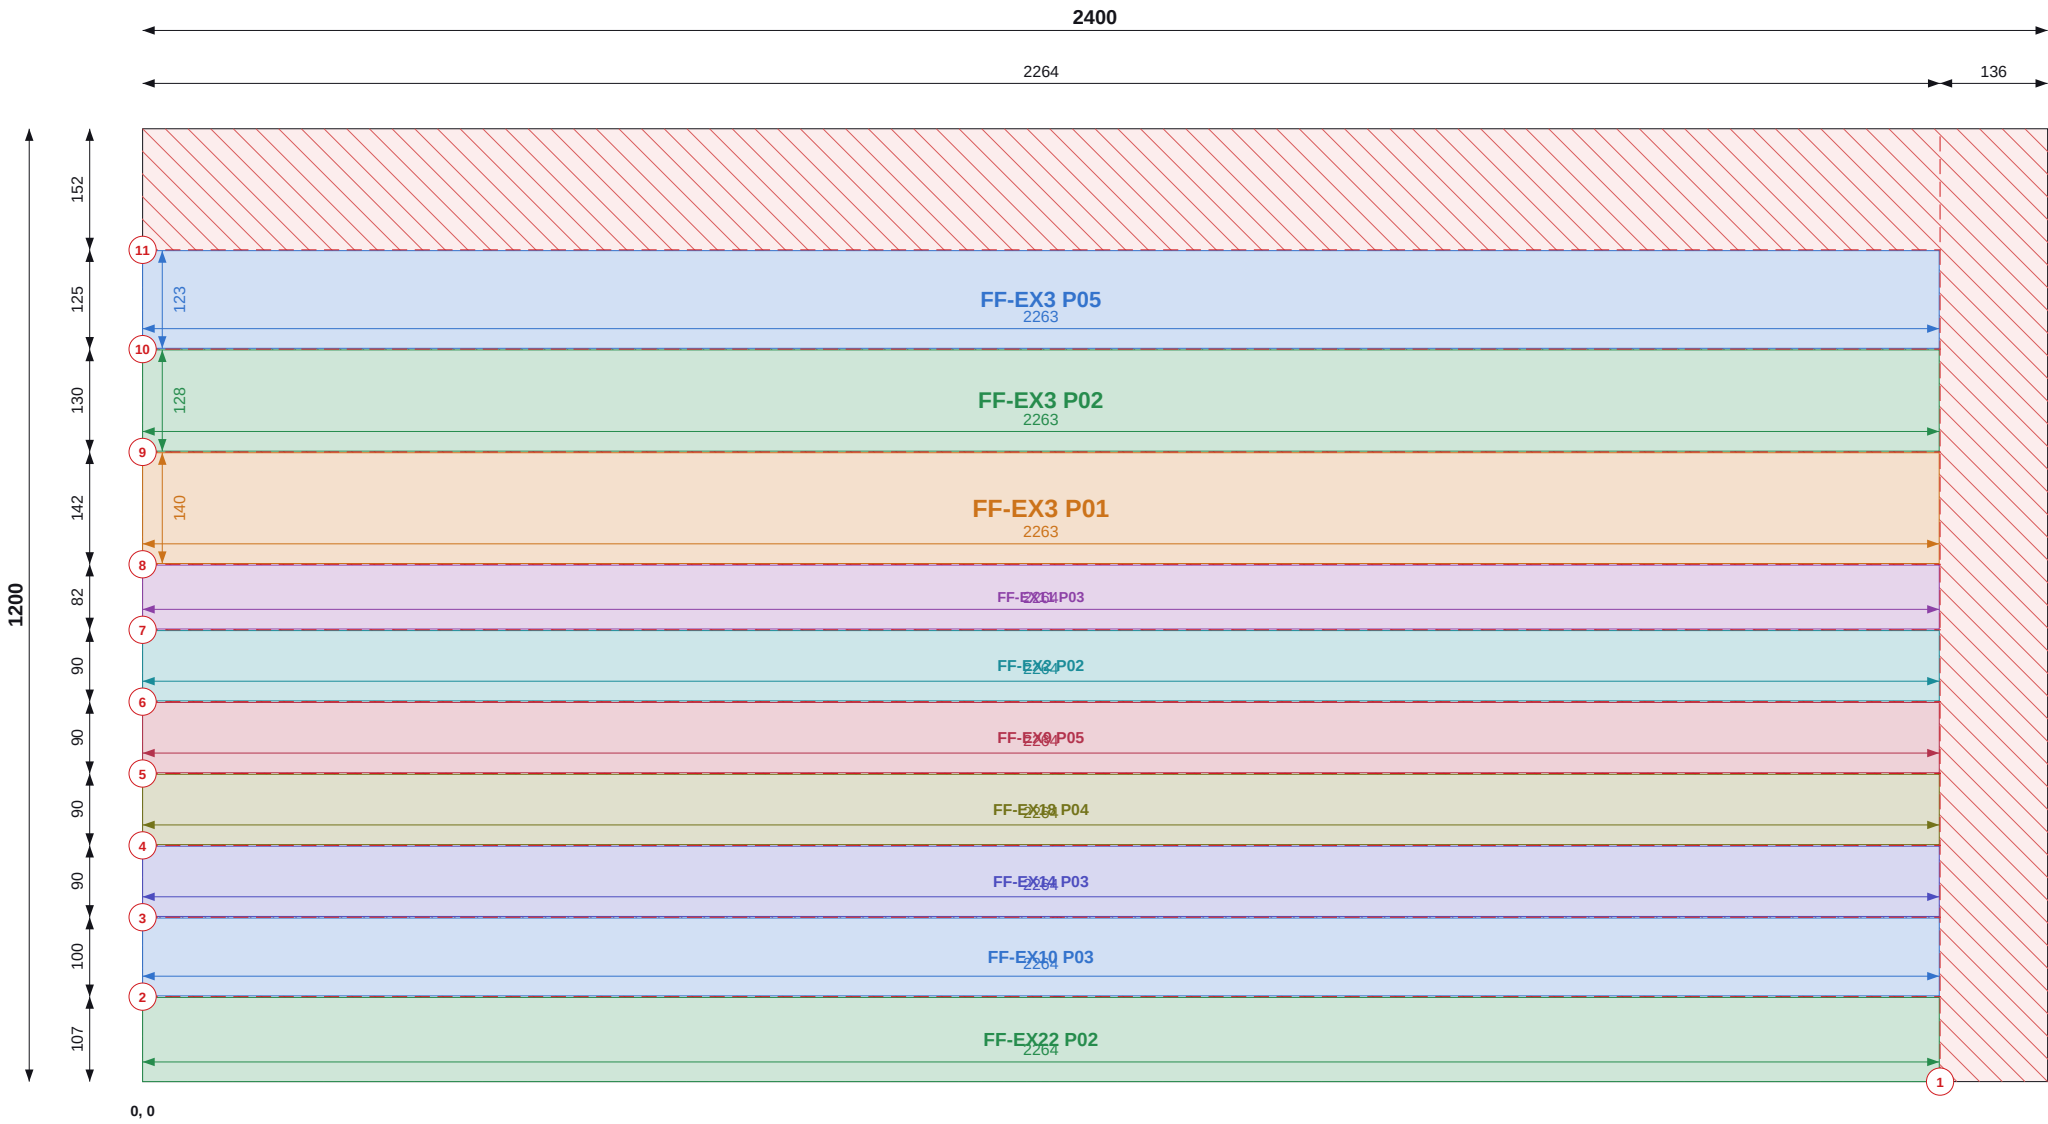

SHEET 20 OF 23

THIS SHEET

Item	Value
Parts	10
Used / waste	80.8% / 0.55 m2
Reusable offcuts	0
Saw cuts / shared	11 / 9

PIECES (POSITION = BOTTOM-LEFT CORNER)

Label	Size	X, Y
FF-EX3 P05	123 x 2263	0, 923
FF-EX3 P02	128 x 2263	0, 794
FF-EX3 P01	140 x 2263	0, 652
FF-EX11 P03	80 x 2264	0, 570
FF-EX2 P02	88 x 2264	0, 480
FF-EX9 P05	89 x 2264	0, 389
FF-EX18 P04	89 x 2264	0, 299
FF-EX14 P03	89 x 2264	0, 208
FF-EX10 P03	98 x 2264	0, 108
FF-EX22 P02	106 x 2264	0, 0

NOTES

- Cut from PIR 120mm 1200x2400, 2mm saw kerf. Viewed on the face; dimensions from the sheet's bottom-left corner (0,0). Red numbered lines = saw cuts in order, each edge to edge.
- Coloured dimensions belong to the part of that colour: its width and height, and its position from the sheet edges. Raked parts: corner coordinates at each corner.
- Red hatch = waste. Labels = panel + piece mark on the manufacture drawing.

REVISIONS

REV	DATE	DESCRIPTION
C01	13.09.26	Construction issue



TLS TIMBER FRAME

Design & Manufacture

Scan: 3D model + drawings



CLIENT	PROJECT
MP Adams	MP Adams Plot 3, Eckington


DRAWING TITLE
PIR CUTTING - FIRST FLOOR - SHEET 20 OF 23

PIR 120mm 1200x2400 | First Floor

SCALE	SIZE	DATE	DRAWN
NTS	A3	13.09.26	TS

STATUS	DRAWING No.	REV
CONSTRUCTION	P3-CP-PIR-02 / 20	C01

Do not scale. All dimensions in mm. Check all dimensions on site.

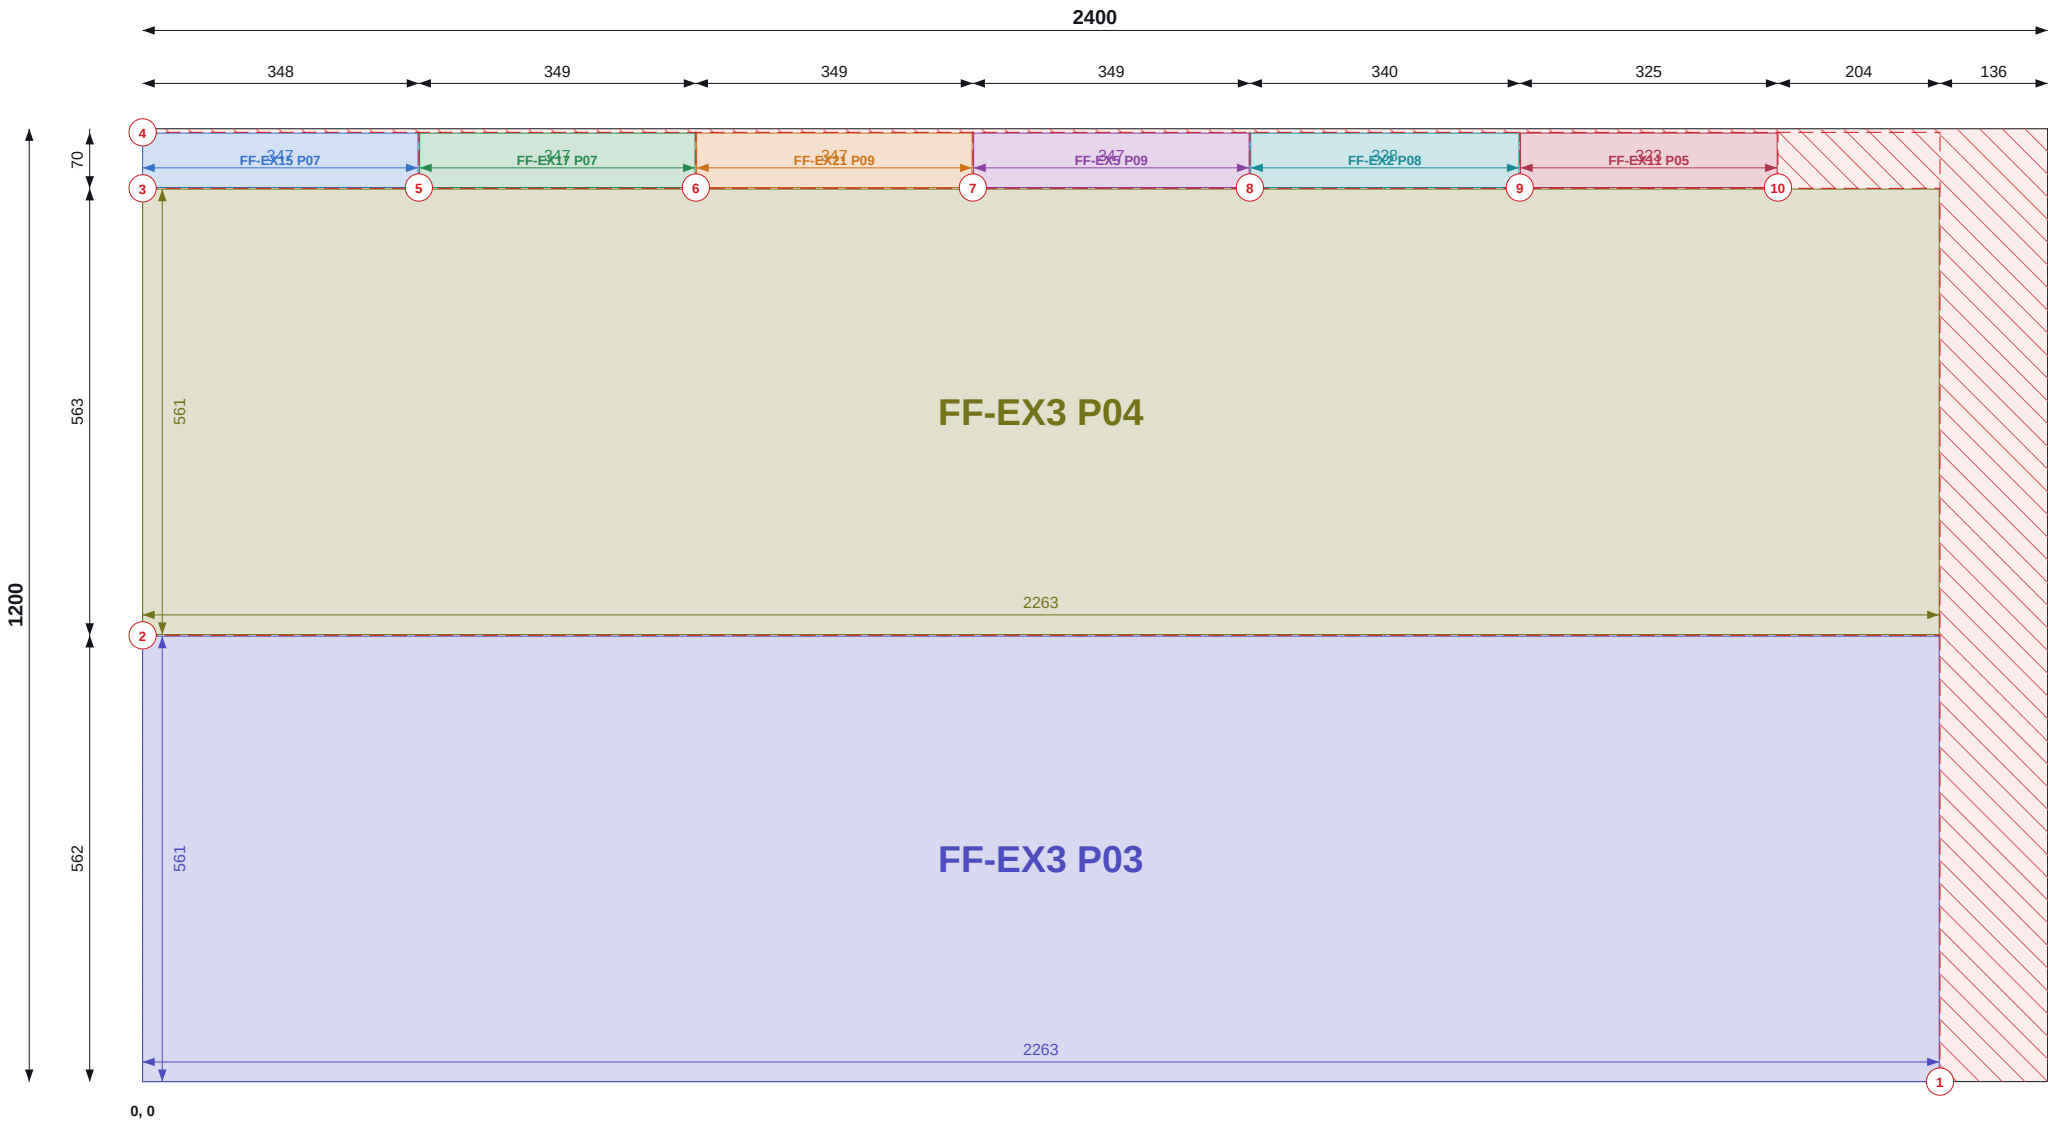

Top / left chains = saw cut positions (to cut centres). Coloured = part size and position.

SHEET 21 OF 23

THIS SHEET

Item	Value
Parts	8
Used / waste	93.1% / 0.20 m2
Reusable offcuts	0
Saw cuts / shared	10 / 7

PIECES (POSITION = BOTTOM-LEFT CORNER)

Label	Size	X, Y
FF-EX15 P07	347 x 69	0, 1126
FF-EX17 P07	347 x 69	349, 1126
FF-EX21 P09	347 x 69	698, 1126
FF-EX5 P09	347 x 69	1047, 1126
FF-EX2 P08	338 x 69	1396, 1126
FF-EX11 P05	323 x 69	1736, 1126
FF-EX3 P04	561 x 2263	0, 563
FF-EX3 P03	561 x 2263	0, 0

NOTES

- Cut from PIR 120mm 1200x2400, 2mm saw kerf. Viewed on the face; dimensions from the sheet's bottom-left corner (0,0). Red numbered lines = saw cuts in order, each edge to edge.
- Coloured dimensions belong to the part of that colour: its width and height, and its position from the sheet edges. Raked parts: corner coordinates at each corner.
- Red hatch = waste. Labels = panel + piece mark on the manufacture drawing.

REVISIONS

REV	DATE	DESCRIPTION
C01	13.09.26	Construction issue



TLS TIMBER FRAME

Design & Manufacture

Scan: 3D model + drawings




CLIENT	PROJECT
MP Adams	MP Adams Plot 3, Eckington

DRAWING TITLE			
PIR CUTTING - FIRST FLOOR - SHEET 21 OF 23			
PIR 120mm 1200x2400 First Floor			

SCALE	SIZE	DATE	DRAWN
NTS	A3	13.09.26	TS

STATUS	DRAWING No.	REV
CONSTRUCTION	P3-CP-PIR-02 / 21	C01

Do not scale. All dimensions in mm. Check all dimensions on site.

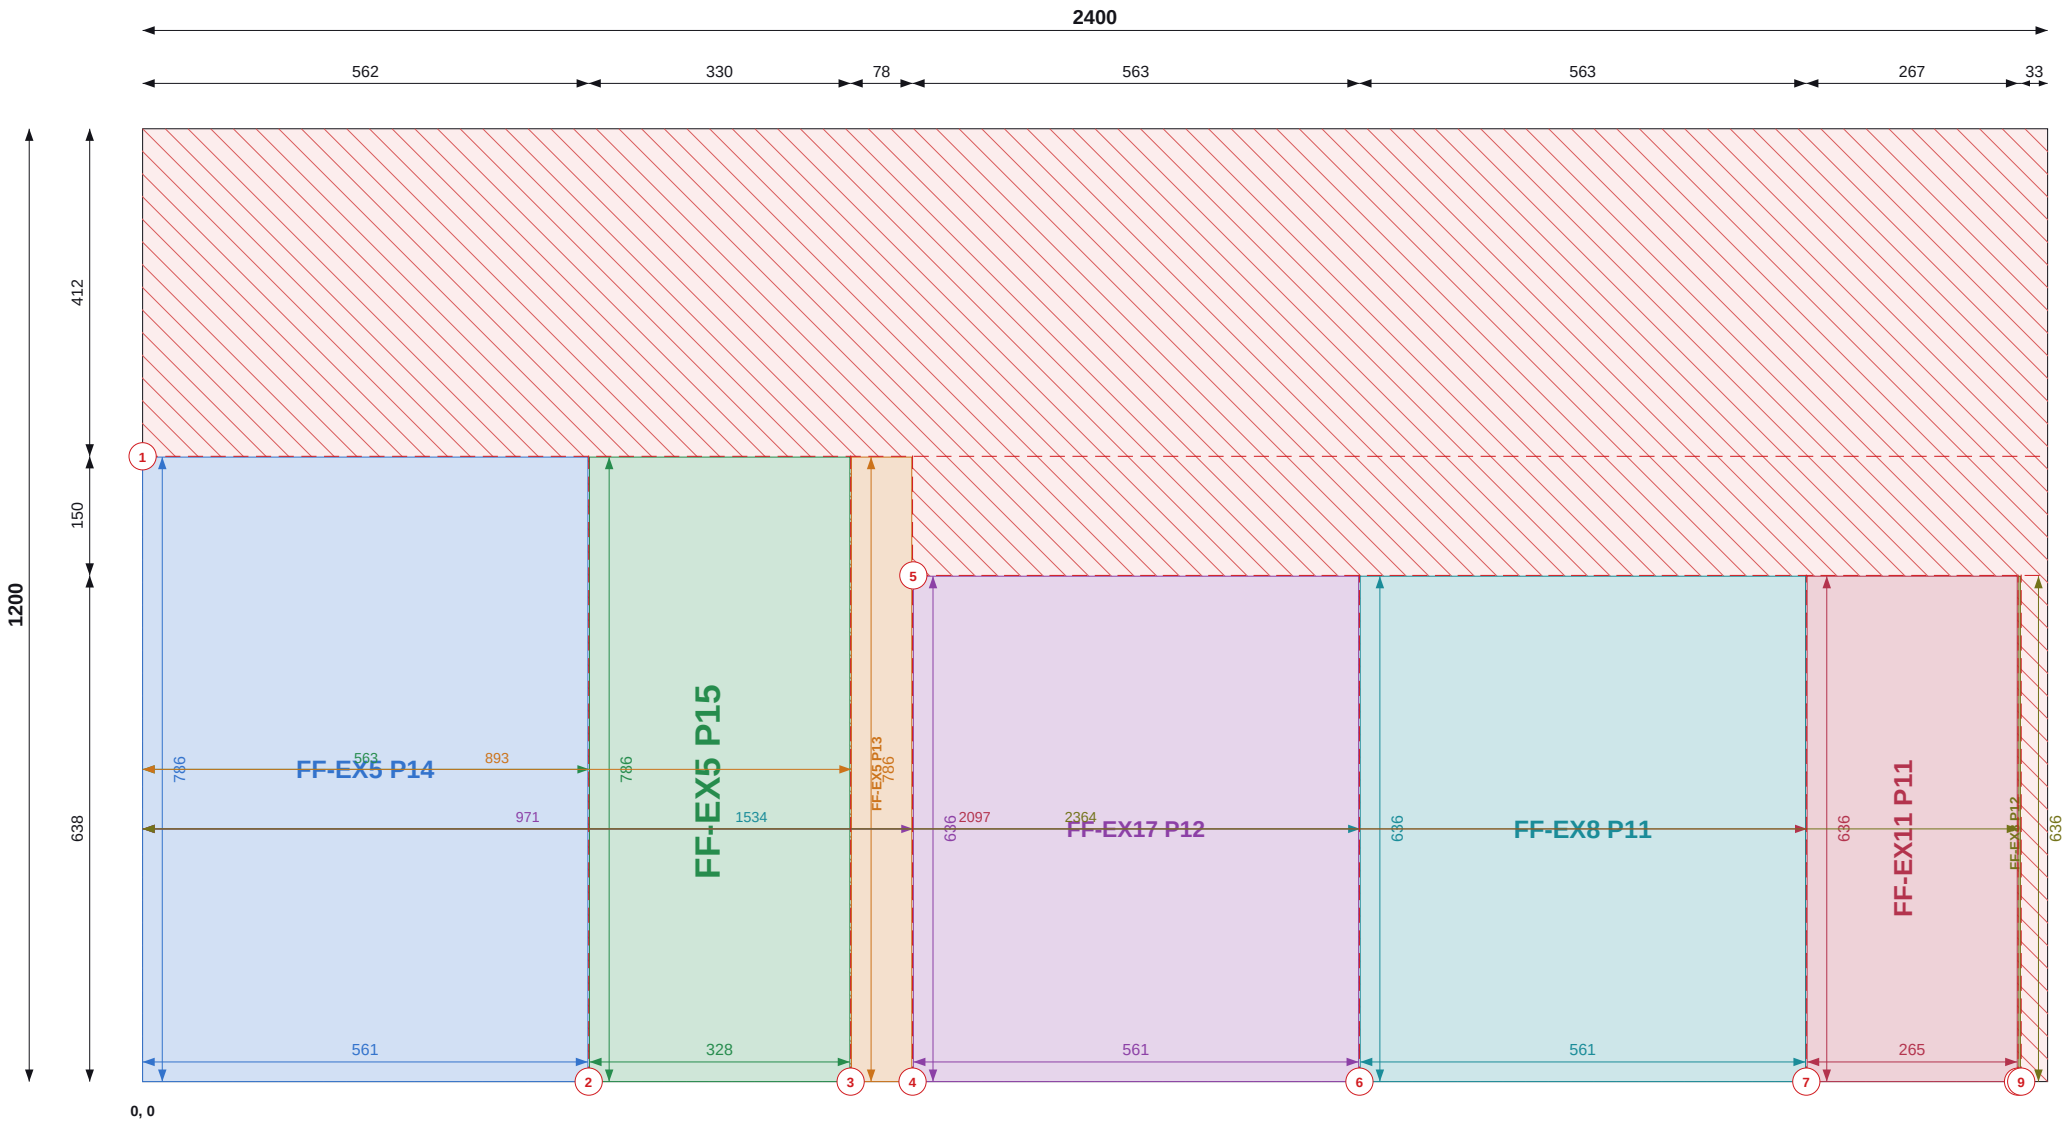

Top / left chains = saw cut positions (to cut centres). Coloured = part size and position.

SHEET 22 OF 23

THIS SHEET

Item	Value
Parts	7
Used / waste	57.0% / 1.24 m2
Reusable offcuts	1
Saw cuts / shared	9 / 6

PIECES (POSITION = BOTTOM-LEFT CORNER)

Label	Size	X, Y
FF-EX5 P14	561 x 786	0, 0
FF-EX5 P15	328 x 786	563, 0
FF-EX5 P13	76 x 786	893, 0
FF-EX17 P12	561 x 636	971, 0
FF-EX8 P11	561 x 636	1534, 0
FF-EX11 P11	265 x 636	2097, 0
FF-EX8 P12	2 x 636	2364, 0

NOTES

- Cut from PIR 120mm 1200x2400, 2mm saw kerf. Viewed on the face; dimensions from the sheet's bottom-left corner (0,0). Red numbered lines = saw cuts in order, each edge to edge.
- Coloured dimensions belong to the part of that colour: its width and height, and its position from the sheet edges. Raked parts: corner coordinates at each corner.
- Red hatch = waste. Labels = panel + piece mark on the manufacture drawing.

REVISIONS

REV	DATE	DESCRIPTION
C01	13.09.26	Construction issue



TLS TIMBER FRAME

Design & Manufacture

Scan: 3D model + drawings




CLIENT	PROJECT
MP Adams	MP Adams Plot 3, Eckington

DRAWING TITLE
PIR CUTTING - FIRST FLOOR - SHEET 22 OF 23

PIR 120mm 1200x2400 | First Floor

SCALE	SIZE	DATE	DRAWN
NTS	A3	13.09.26	TS

STATUS	DRAWING No.	REV
CONSTRUCTION	P3-CP-PIR-02 / 22	C01

 

SHEET 23 OF 23

THIS SHEET

Item	Value
Parts	22
Used / waste	97.9% / 0.06 m2
Reusable offcuts	0
Saw cuts / shared	28 / 21

PIECES (POSITION = BOTTOM-LEFT CORNER)

Label	Size	X, Y
FF-EX19 P07	485 x 69	1189, 1127
FF-EX13 P04	477 x 69	1676, 1127
FF-EX2 P12	561 x 487	0, 638
FF-EX21 P13	561 x 487	489, 638
FF-EX17 P06	561 x 69	977, 638
FF-EX2 P07	561 x 69	1048, 638
FF-EX8 P04	561 x 69	1118, 638
FF-EX19 P13	466 x 487	1189, 638
FF-EX19 P14	328 x 487	1657, 638
FF-EX21 P14	328 x 487	1987, 638
FF-EX21 P12	76 x 487	2317, 638
FF-EX21 P06	309 x 69	2079, 559
FF-EX5 P06	310 x 69	2079, 489
FF-EX13 P09	458 x 636	0, 0
FF-EX15 P11	328 x 636	460, 0
FF-EX17 P13	328 x 636	790, 0
FF-EX11 P10	304 x 636	1120, 0
FF-EX15 P10	241 x 636	1426, 0
FF-EX13 P10	236 x 636	1669, 0
FF-EX8 P10	92 x 636	1907, 0
FF-EX17 P11	76 x 636	2001, 0
FF-EX2 P13	319 x 487	2079, 0

NOTES

1. Cut from PIR 120mm 1200x2400, 2mm saw kerf. Viewed on the face; dimensions from the sheet's bottom-left corner (0,0). Red numbered lines = saw cuts in order, each edge to edge.
2. Coloured dimensions belong to the part of that colour: its width and height, and its position from the sheet edges. Raked parts: corner coordinates at each corner.
3. Red hatch = waste. Labels = panel + piece mark on the manufacture drawing.

REVISIONS

REV	DATE	DESCRIPTION
C01	13.09.26	Construction issue



TLS TIMBER FRAME

Design & Manufacture

Scan: 3D model + drawing:



CLIENT	PROJECT
MP Adams	MP Adams Plot 3, Eckington

DRAWING TITLE


PIR CUTTING - FIRST FLOOR - SHEET 23 OF 23

MR 120mm 1200x2400 | First Floor

SCALE	SIZE	DATE	DRAWN
1:1	A3	13.09.26	TS

STATUS	DRAWING No.	REV
CONSTRUCTION	P3-CP-PIR-02 / 23	C01

Do not scale. All dimensions in mm. Check all dimensions on site.

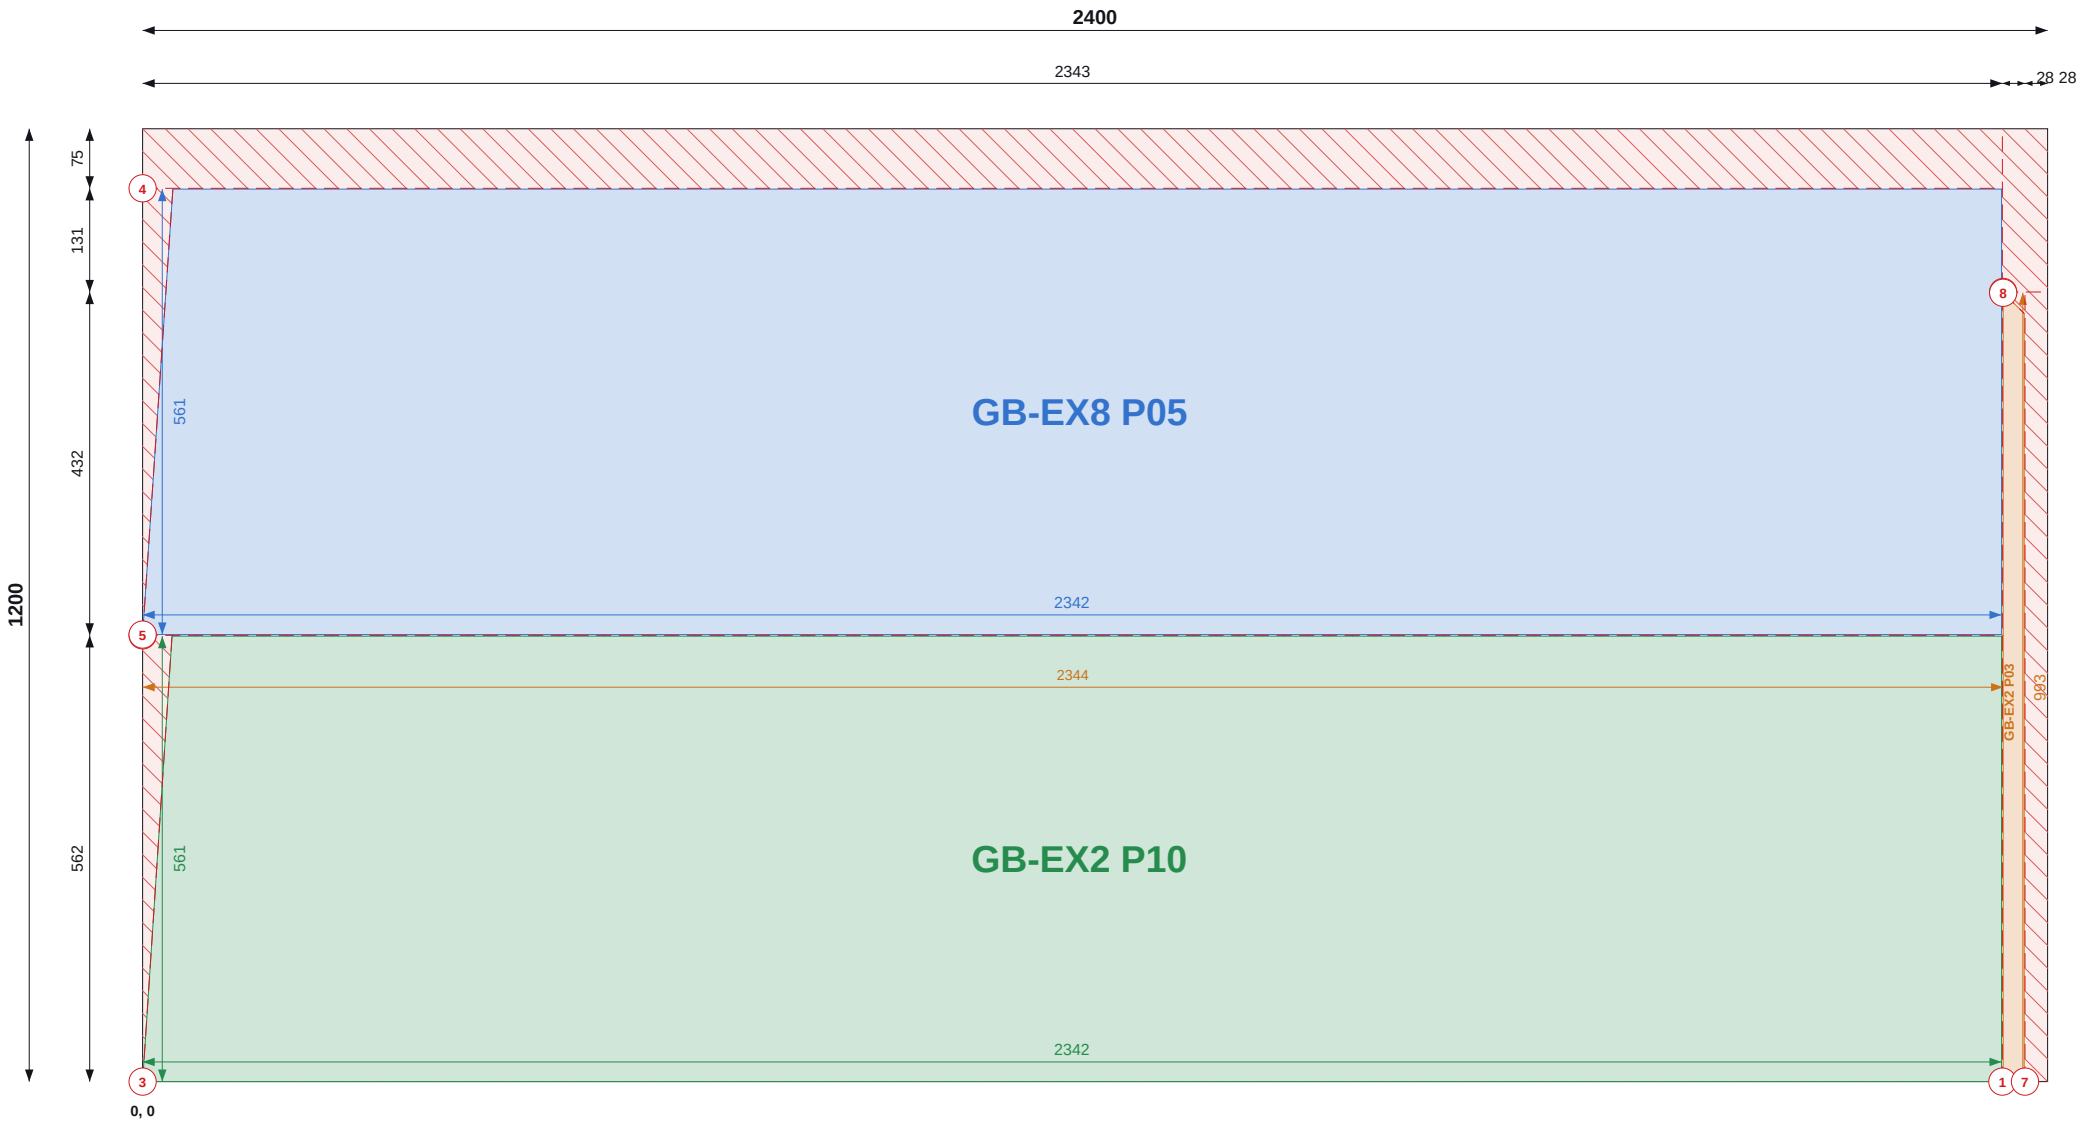

Top / left chains = saw cut positions (to cut centres). Coloured = part size and position.

SHEET 1 OF 11

THIS SHEET

Item	Value
Parts	3
Used / waste	91.4% / 0.25 m2
Reusable offcuts	0
Saw cuts / shared	8 / 5

PIECES (POSITION = BOTTOM-LEFT CORNER)

Label	Size	X, Y
GB-EX8 P05	561 x 2342	0, 563
GB-EX2 P10	561 x 2342	0, 0
GB-EX2 P03	27 x 993	2344, 0

GABLES TOTALS

Item	Value
Sheets / pieces	11 / 63
Yield / waste	87.6% / 3.92 m2
Saw cuts / shared / on stock edge	104 / 62 / 49

NOTES

- Cut from PIR 120mm 1200x2400, 2mm saw kerf. Viewed on the face; dimensions from the sheet's bottom-left corner (0,0). Red numbered lines = saw cuts in order, each edge to edge.
- Coloured dimensions belong to the part of that colour: its width and height, and its position from the sheet edges. Raked parts: corner coordinates at each corner.
- Red hatch = waste. Labels = panel + piece mark on the manufacture drawing.

REVISIONS

REV	DATE	DESCRIPTION
C01	13.09.26	Construction issue



TLS TIMBER FRAME

Design & Manufacture

Scan: 3D model + drawings



CLIENT	PROJECT
MP Adams	MP Adams Plot 3, Eckington


DRAWING TITLE
PIR CUTTING - GABLES - SHEET 1 OF 11

PIR 120mm 1200x2400 | Gables

SCALE	SIZE	DATE	DRAWN
NTS	A3	13.09.26	TS

STATUS	DRAWING No.	REV
CONSTRUCTION	P3-CP-PIR-03 / 01	C01

Do not scale. All dimensions in mm. Check all dimensions on site.

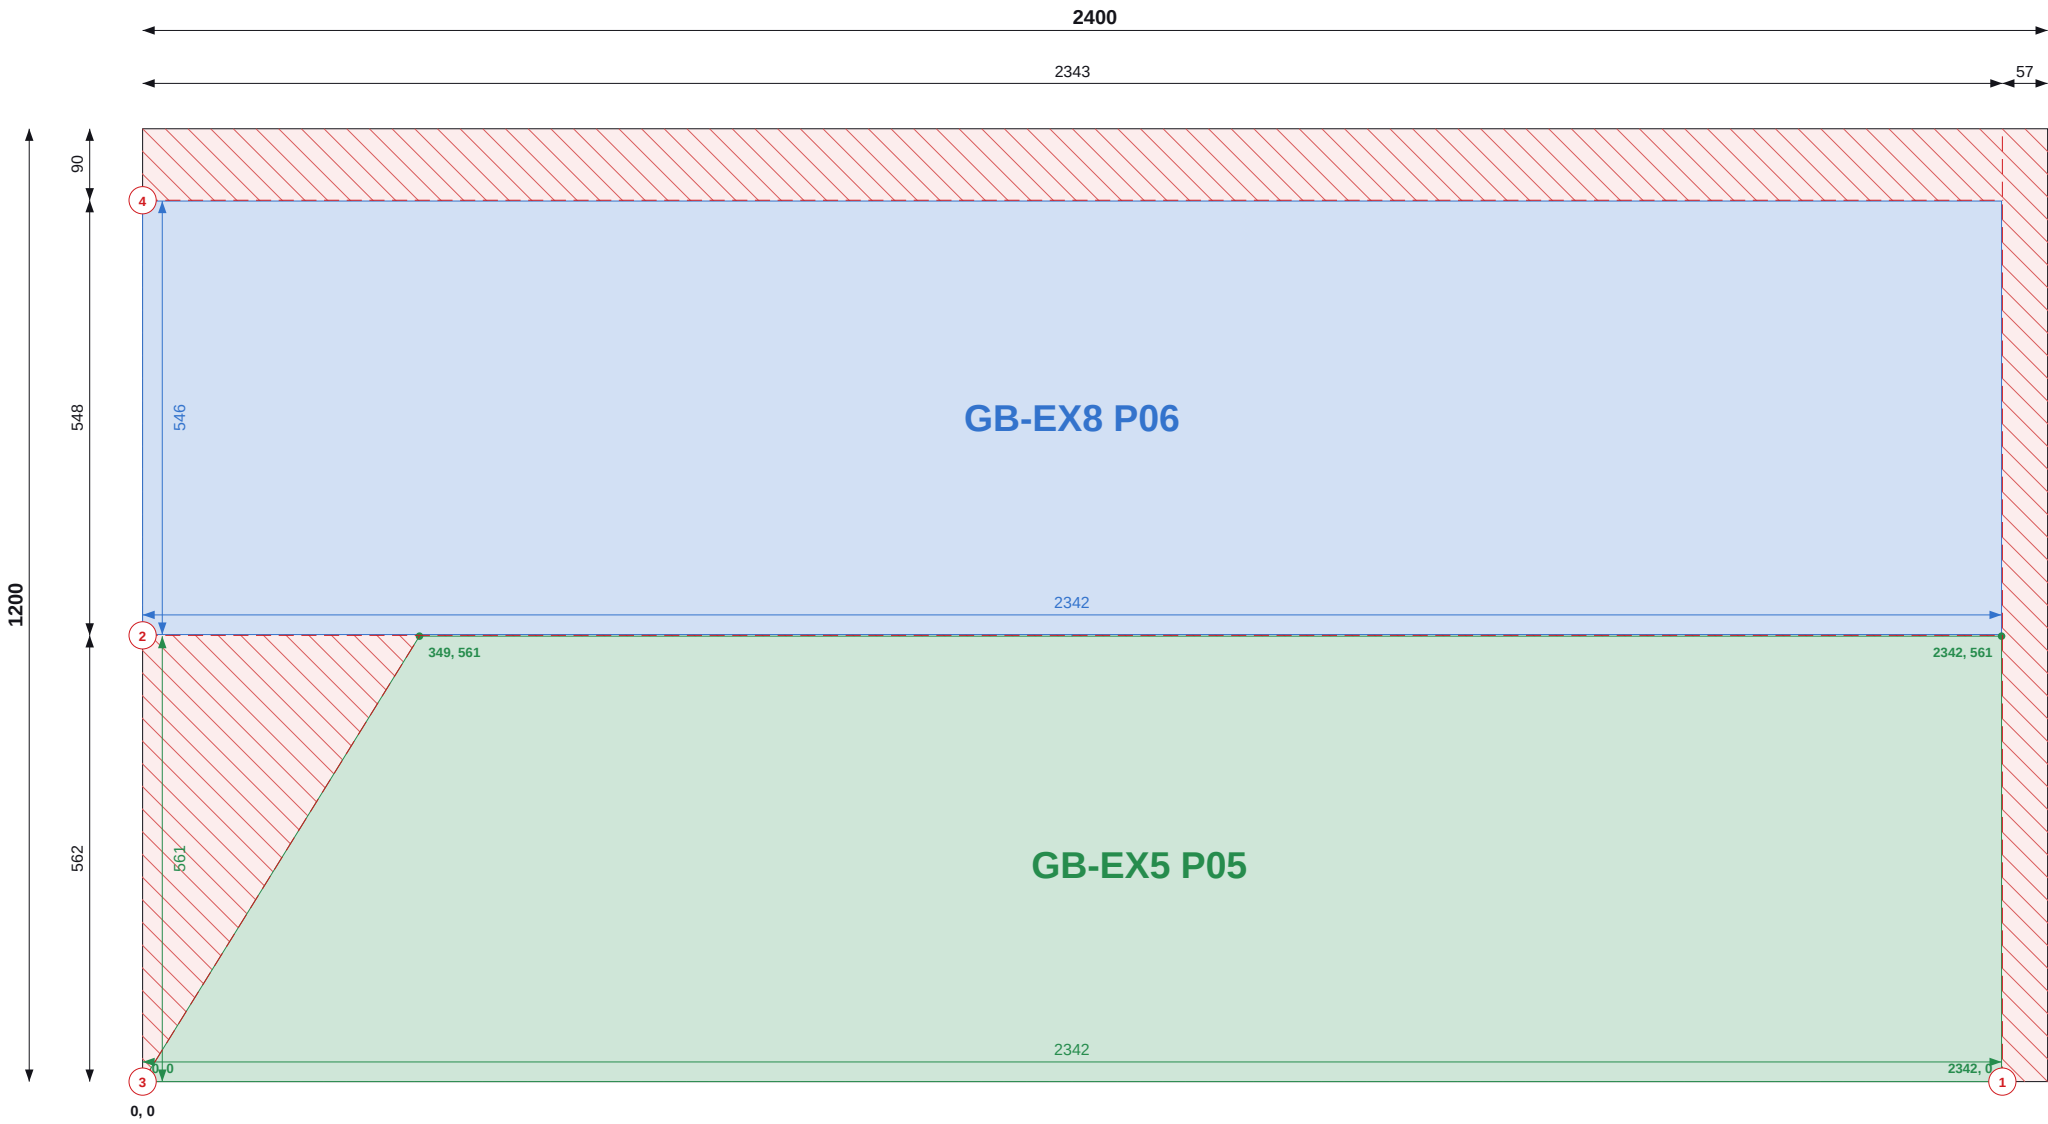

Top / left chains = saw cut positions (to cut centres). Coloured = part size and position.

SHEET 2 OF 11

THIS SHEET

Item	Value
Parts	2
Used / waste	86.6% / 0.39 m2
Reusable offcuts	0
Saw cuts / shared	4 / 2

PIECES (POSITION = BOTTOM-LEFT CORNER)

Label	Size	X, Y
GB-EX8 P06	546 x 2342	0, 563
GB-EX5 P05	561 x 2342 rake to 1994	0, 0

NOTES

- Cut from PIR 120mm 1200x2400, 2mm saw kerf. Viewed on the face; dimensions from the sheet's bottom-left corner (0,0). Red numbered lines = saw cuts in order, each edge to edge.
- Coloured dimensions belong to the part of that colour: its width and height, and its position from the sheet edges. Raked parts: corner coordinates at each corner.
- Red hatch = waste. Labels = panel + piece mark on the manufacture drawing.

REVISIONS

REV	DATE	DESCRIPTION
C01	13.09.26	Construction issue



TLS TIMBER FRAME

Design & Manufacture

Scan: 3D model + drawings



CLIENT	PROJECT
MP Adams	MP Adams Plot 3, Eckington


DRAWING TITLE
PIR CUTTING - GABLES - SHEET 2 OF 11

PIR 120mm 1200x2400 | Gables

SCALE	SIZE	DATE	DRAWN
NTS	A3	13.09.26	TS

STATUS	DRAWING No.	REV
CONSTRUCTION	P3-CP-PIR-03 / 02	C01

Do not scale. All dimensions in mm. Check all dimensions on site.

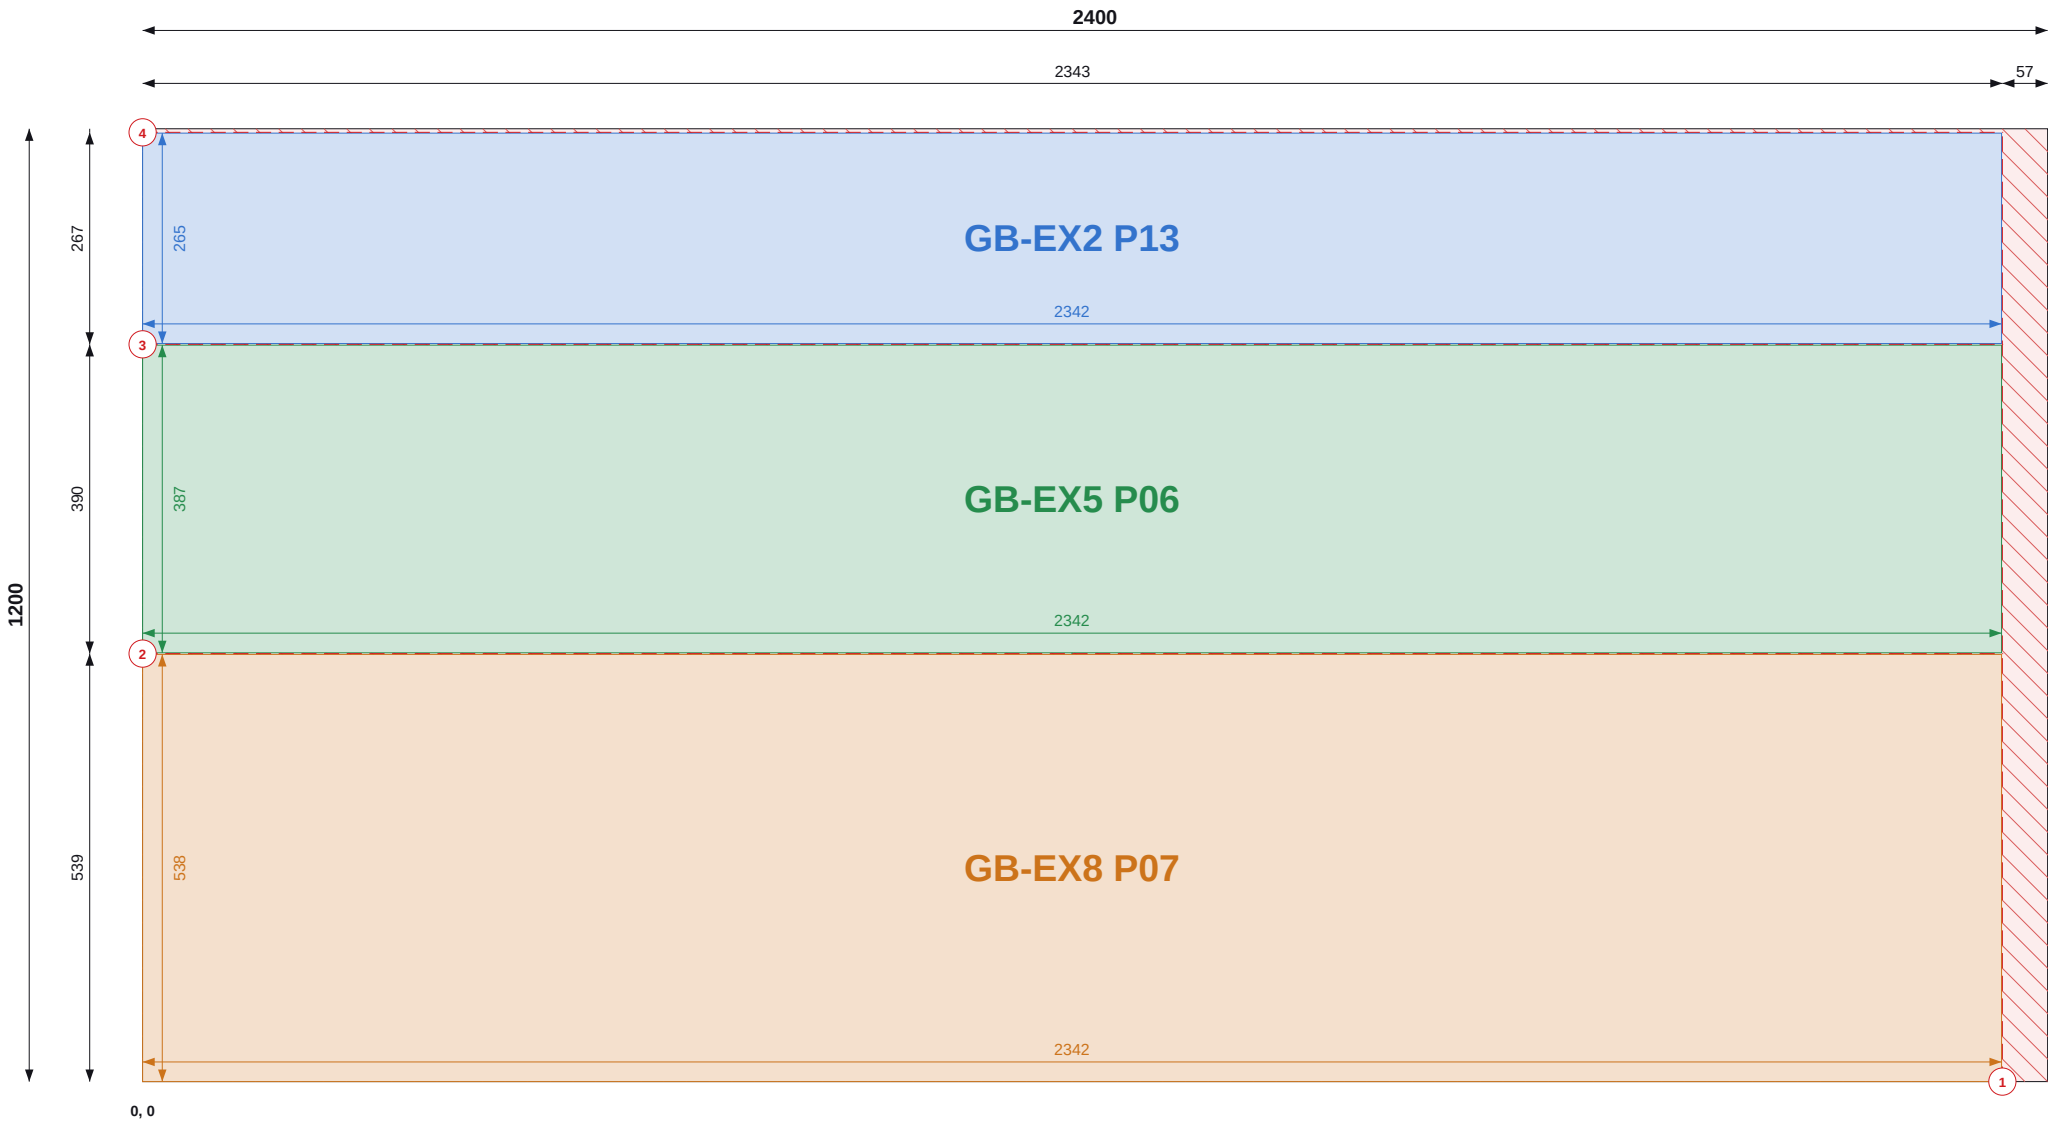

Top / left chains = saw cut positions (to cut centres). Coloured = part size and position.

SHEET 3 OF 11

THIS SHEET

Item	Value
Parts	3
Used / waste	96.8% / 0.09 m2
Reusable offcuts	0
Saw cuts / shared	4 / 2

PIECES (POSITION = BOTTOM-LEFT CORNER)

Label	Size	X, Y
GB-EX2 P13	265 x 2342	0, 930
GB-EX5 P06	387 x 2342	0, 540
GB-EX8 P07	538 x 2342	0, 0

NOTES

- Cut from PIR 120mm 1200x2400, 2mm saw kerf. Viewed on the face; dimensions from the sheet's bottom-left corner (0,0). Red numbered lines = saw cuts in order, each edge to edge.
- Coloured dimensions belong to the part of that colour: its width and height, and its position from the sheet edges. Raked parts: corner coordinates at each corner.
- Red hatch = waste. Labels = panel + piece mark on the manufacture drawing.

REVISIONS

REV	DATE	DESCRIPTION
C01	13.09.26	Construction issue



TLS TIMBER FRAME

Design & Manufacture

Scan: 3D model + drawings



CLIENT	PROJECT
MP Adams	MP Adams Plot 3, Eckington


DRAWING TITLE
PIR CUTTING - GABLES - SHEET 3 OF 11

PIR 120mm 1200x2400 | Gables

SCALE	SIZE	DATE	DRAWN
NTS	A3	13.09.26	TS

STATUS	DRAWING No.	REV
CONSTRUCTION	P3-CP-PIR-03 / 03	C01

Do not scale. All dimensions in mm. Check all dimensions on site.

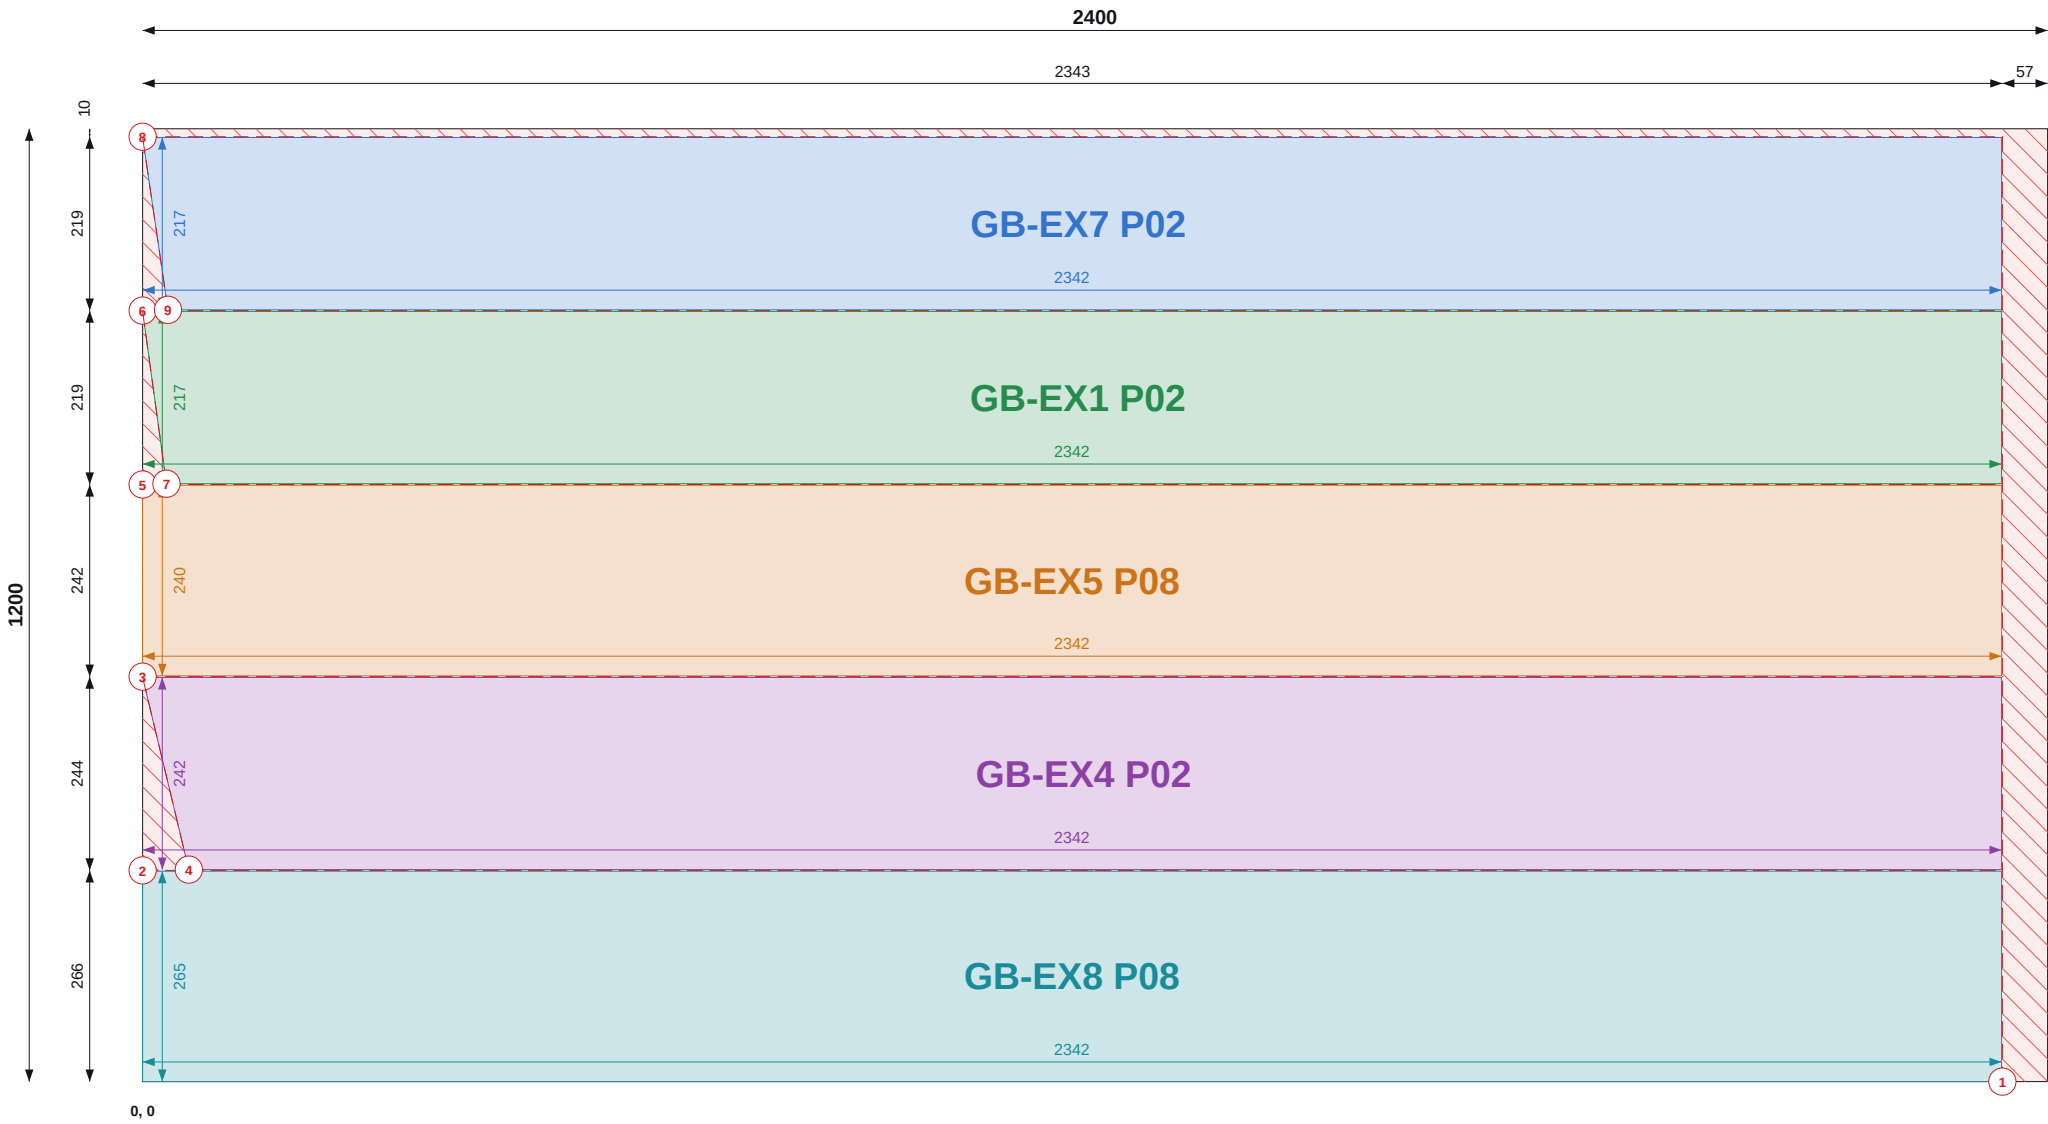

Top / left chains = saw cut positions (to cut centres). Coloured = part size and position.

SHEET 4 OF 11

THIS SHEET

Item	Value
Parts	5
Used / waste	95.6% / 0.13 m2
Reusable offcuts	0
Saw cuts / shared	9 / 7

PIECES (POSITION = BOTTOM-LEFT CORNER)

Label	Size	X, Y
GB-EX7 P02	217 x 2342	0, 972
GB-EX1 P02	217 x 2342	0, 753
GB-EX5 P08	240 x 2342	0, 511
GB-EX4 P02	242 x 2342	0, 267
GB-EX8 P08	265 x 2342	0, 0

NOTES

- Cut from PIR 120mm 1200x2400, 2mm saw kerf. Viewed on the face; dimensions from the sheet's bottom-left corner (0,0). Red numbered lines = saw cuts in order, each edge to edge.
- Coloured dimensions belong to the part of that colour: its width and height, and its position from the sheet edges. Raked parts: corner coordinates at each corner.
- Red hatch = waste. Labels = panel + piece mark on the manufacture drawing.

REVISIONS

REV	DATE	DESCRIPTION
C01	13.09.26	Construction issue



TLS TIMBER FRAME

Design & Manufacture

Scan: 3D model + drawings



CLIENT	PROJECT
MP Adams	MP Adams Plot 3, Eckington


DRAWING TITLE
PIR CUTTING - GABLES - SHEET 4 OF 11

PIR 120mm 1200x2400 | Gables

SCALE	SIZE	DATE	DRAWN
NTS	A3	13.09.26	TS

STATUS	DRAWING No.	REV
CONSTRUCTION	P3-CP-PIR-03 / 04	C01

Do not scale. All dimensions in mm. Check all dimensions on site.

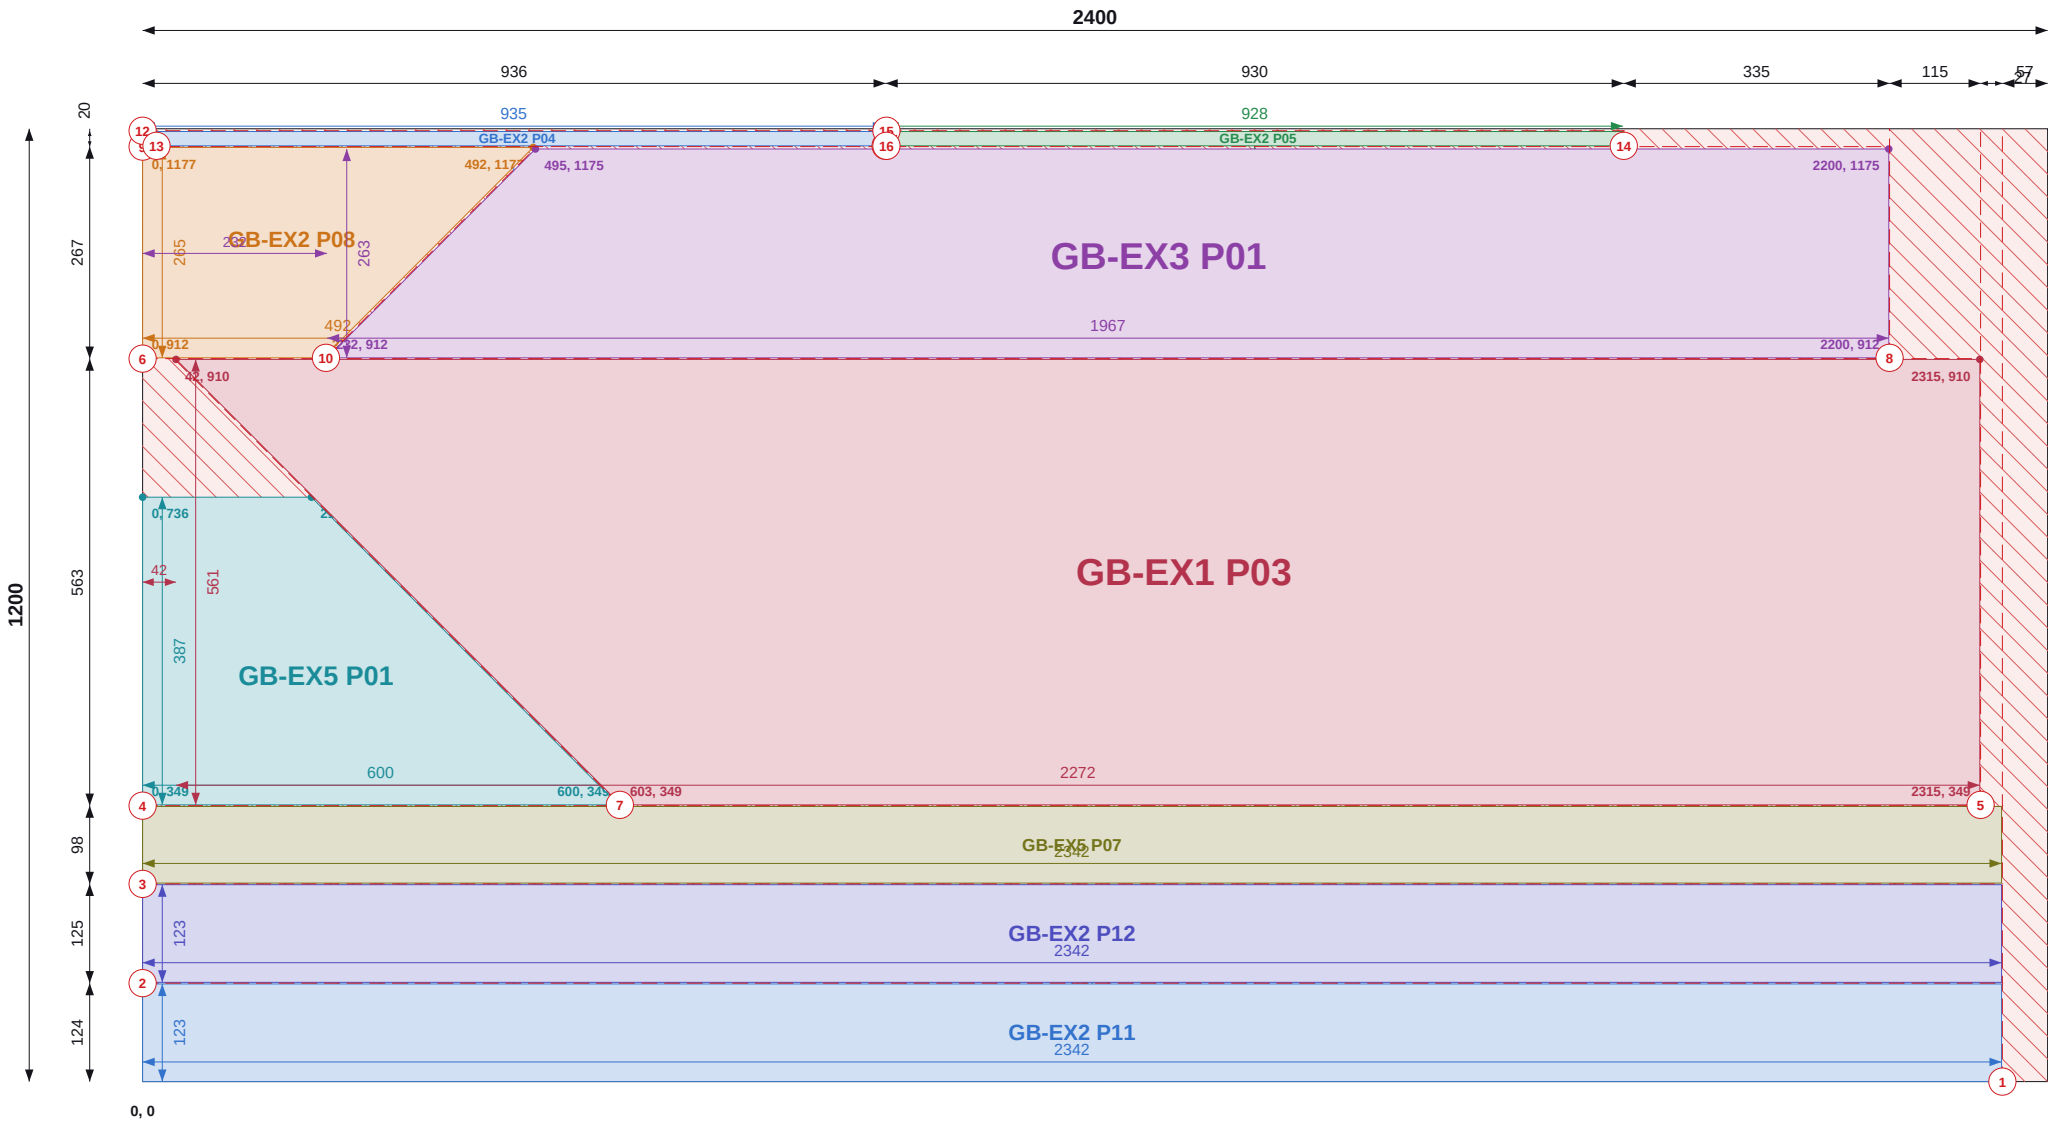

Top / left chains = saw cut positions (to cut centres). Coloured = part size and position.

SHEET 5 OF 11

THIS SHEET

Item	Value
Parts	9
Used / waste	93.4% / 0.19 m2
Reusable offcuts	0
Saw cuts / shared	16 / 10

PIECES (POSITION = BOTTOM-LEFT CORNER)

Label	Size	X, Y
GB-EX2 P04	18 x 935	0, 1179
GB-EX2 P05	18 x 928	937, 1179
GB-EX2 P08	265 x 492 rake to 229	0, 912
GB-EX3 P01	263 x 1967 rake to 1706	232, 912
GB-EX5 P01	387 x 599 rake to 214	0, 349
GB-EX1 P03	561 x 2272 rake to 1713	42, 349
GB-EX5 P07	97 x 2342	0, 250
GB-EX2 P12	123 x 2342	0, 125
GB-EX2 P11	123 x 2342	0, 0

NOTES

- Cut from PIR 120mm 1200x2400, 2mm saw kerf. Viewed on the face; dimensions from the sheet's bottom-left corner (0,0). Red numbered lines = saw cuts in order, each edge to edge.
- Coloured dimensions belong to the part of that colour: its width and height, and its position from the sheet edges. Raked parts: corner coordinates at each corner.
- Red hatch = waste. Labels = panel + piece mark on the manufacture drawing.

REVISIONS

REV	DATE	DESCRIPTION
C01	13.09.26	Construction issue



TLS TIMBER FRAME

Design & Manufacture

Scan: 3D model + drawings



CLIENT	PROJECT
MP Adams	MP Adams Plot 3, Eckington


DRAWING TITLE
PIR CUTTING - GABLES - SHEET 5 OF 11

PIR 120mm 1200x2400 | Gables

SCALE	SIZE	DATE	DRAWN
NTS	A3	13.09.26	TS

STATUS	DRAWING No.	REV
CONSTRUCTION	P3-CP-PIR-03 / 05	C01

Do not scale. All dimensions in mm. Check all dimensions on site.

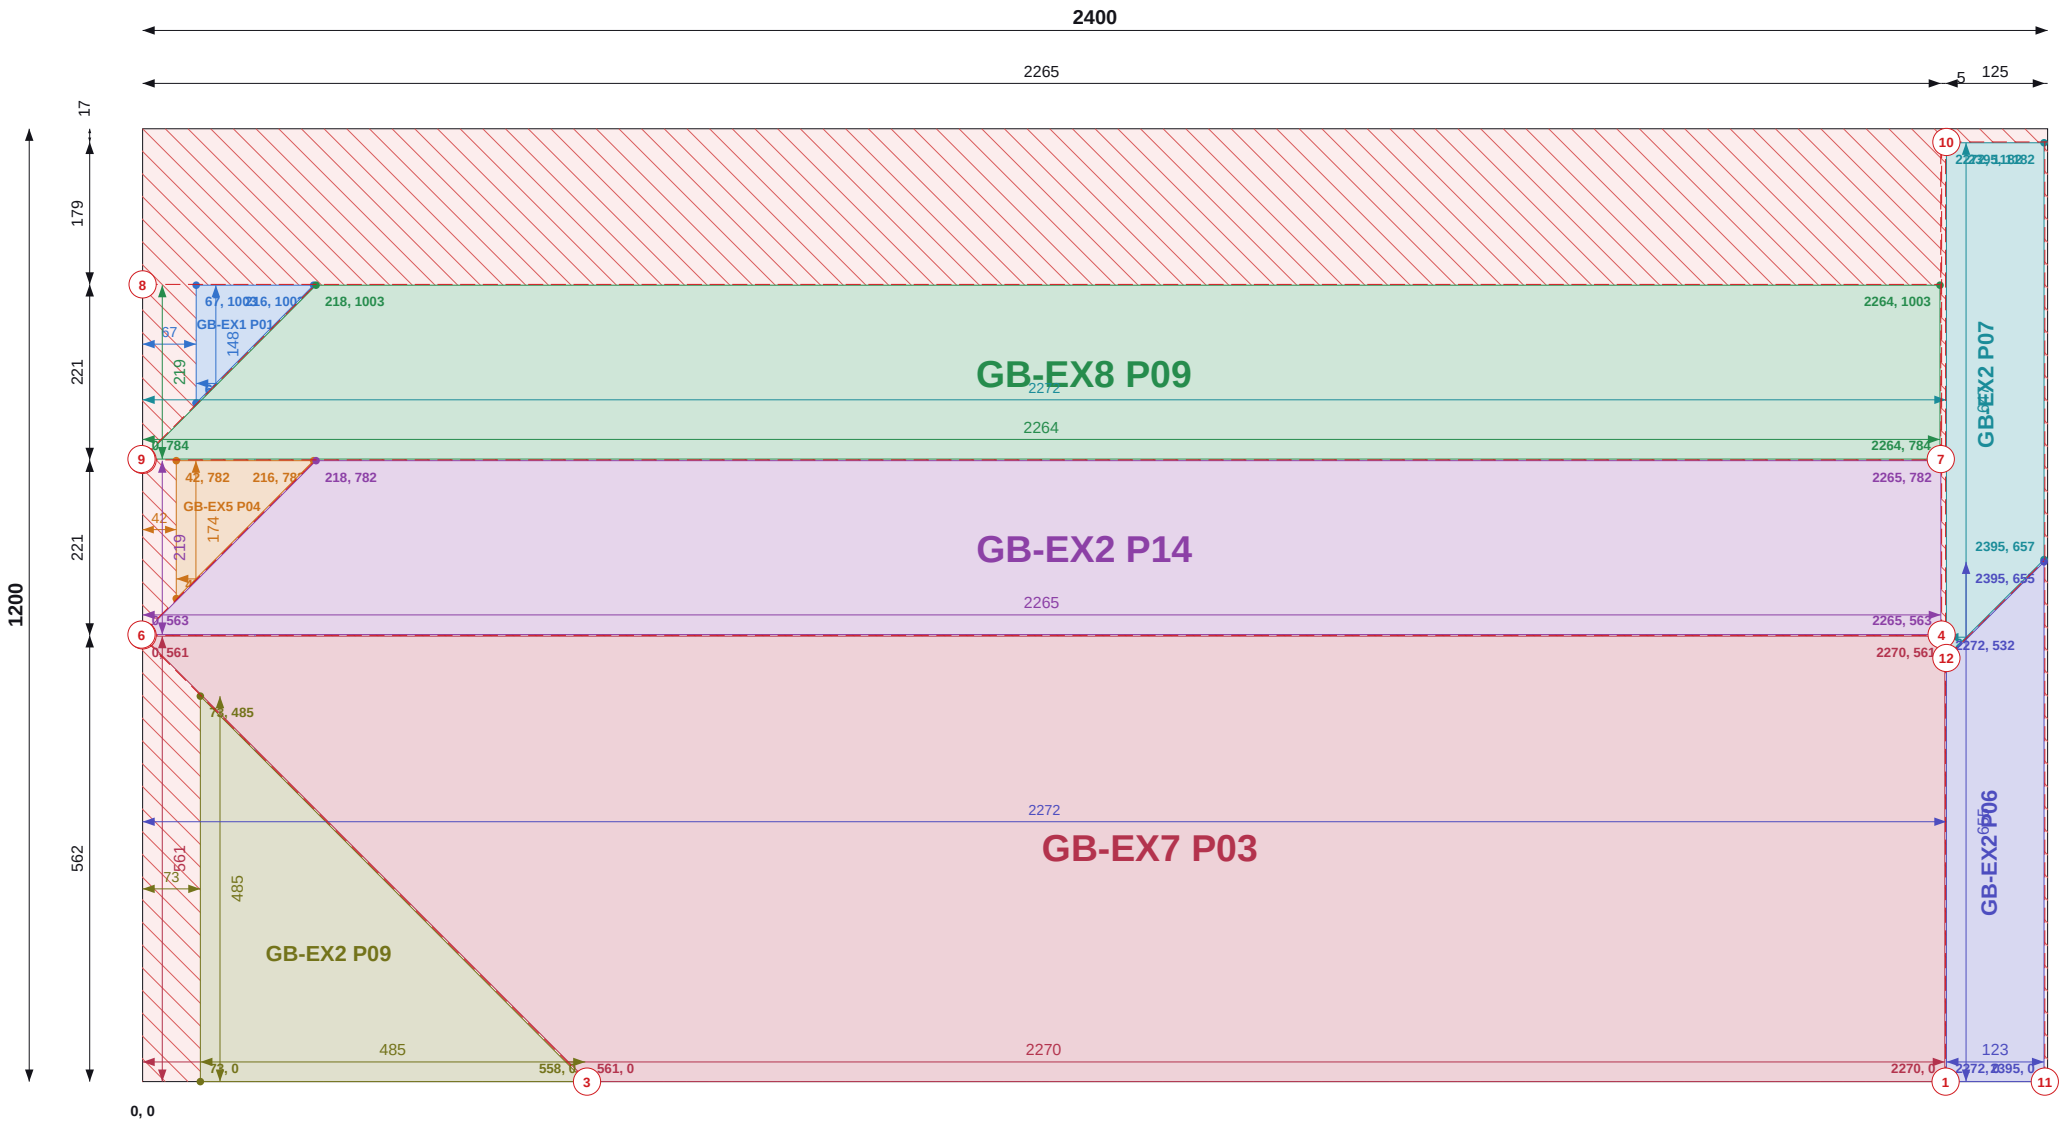

Top / left chains = saw cut positions (to cut centres). Coloured = part size and position.

SHEET 6 OF 11

THIS SHEET

Item	Value
Parts	8
Used / waste	81.6% / 0.53 m2
Reusable offcuts	0
Saw cuts / shared	12 / 7

PIECES (POSITION = BOTTOM-LEFT CORNER)

Label	Size	X, Y
GB-EX1 P01	148 x 148 rake to 1	67, 855
GB-EX8 P09	219 x 2264 rake to 2047	0, 784
GB-EX5 P04	174 x 173 rake to 1	42, 608
GB-EX2 P14	219 x 2265 rake to 2048	0, 563
GB-EX2 P07	123 x 647 rake to 526	2272, 535
GB-EX7 P03	561 x 2270 rake to 1710	0, 0
GB-EX2 P09	485 x 485 rake to 1	73, 0
GB-EX2 P06	123 x 654 rake to 533	2272, 0

NOTES

- Cut from PIR 120mm 1200x2400, 2mm saw kerf. Viewed on the face; dimensions from the sheet's bottom-left corner (0,0). Red numbered lines = saw cuts in order, each edge to edge.
- Coloured dimensions belong to the part of that colour: its width and height, and its position from the sheet edges. Raked parts: corner coordinates at each corner.
- Red hatch = waste. Labels = panel + piece mark on the manufacture drawing.

REVISIONS

REV	DATE	DESCRIPTION
C01	13.09.26	Construction issue



TLS TIMBER FRAME
Design & Manufacture
Scan: 3D model + drawings



CLIENT MP Adams	PROJECT MP Adams Plot 3, Eckington
--------------------	---------------------------------------


DRAWING TITLE
PIR CUTTING - GABLES - SHEET 6 OF 11

PIR 120mm 1200x2400 | Gables

SCALE NTS	SIZE A3	DATE 13.09.26	DRAWN TS
--------------	------------	------------------	-------------

STATUS CONSTRUCTION	DRAWING No. P3-CP-PIR-03 / 06	REV C01
-------------------------------	---	-------------------

Do not scale. All dimensions in mm. Check all dimensions on site.

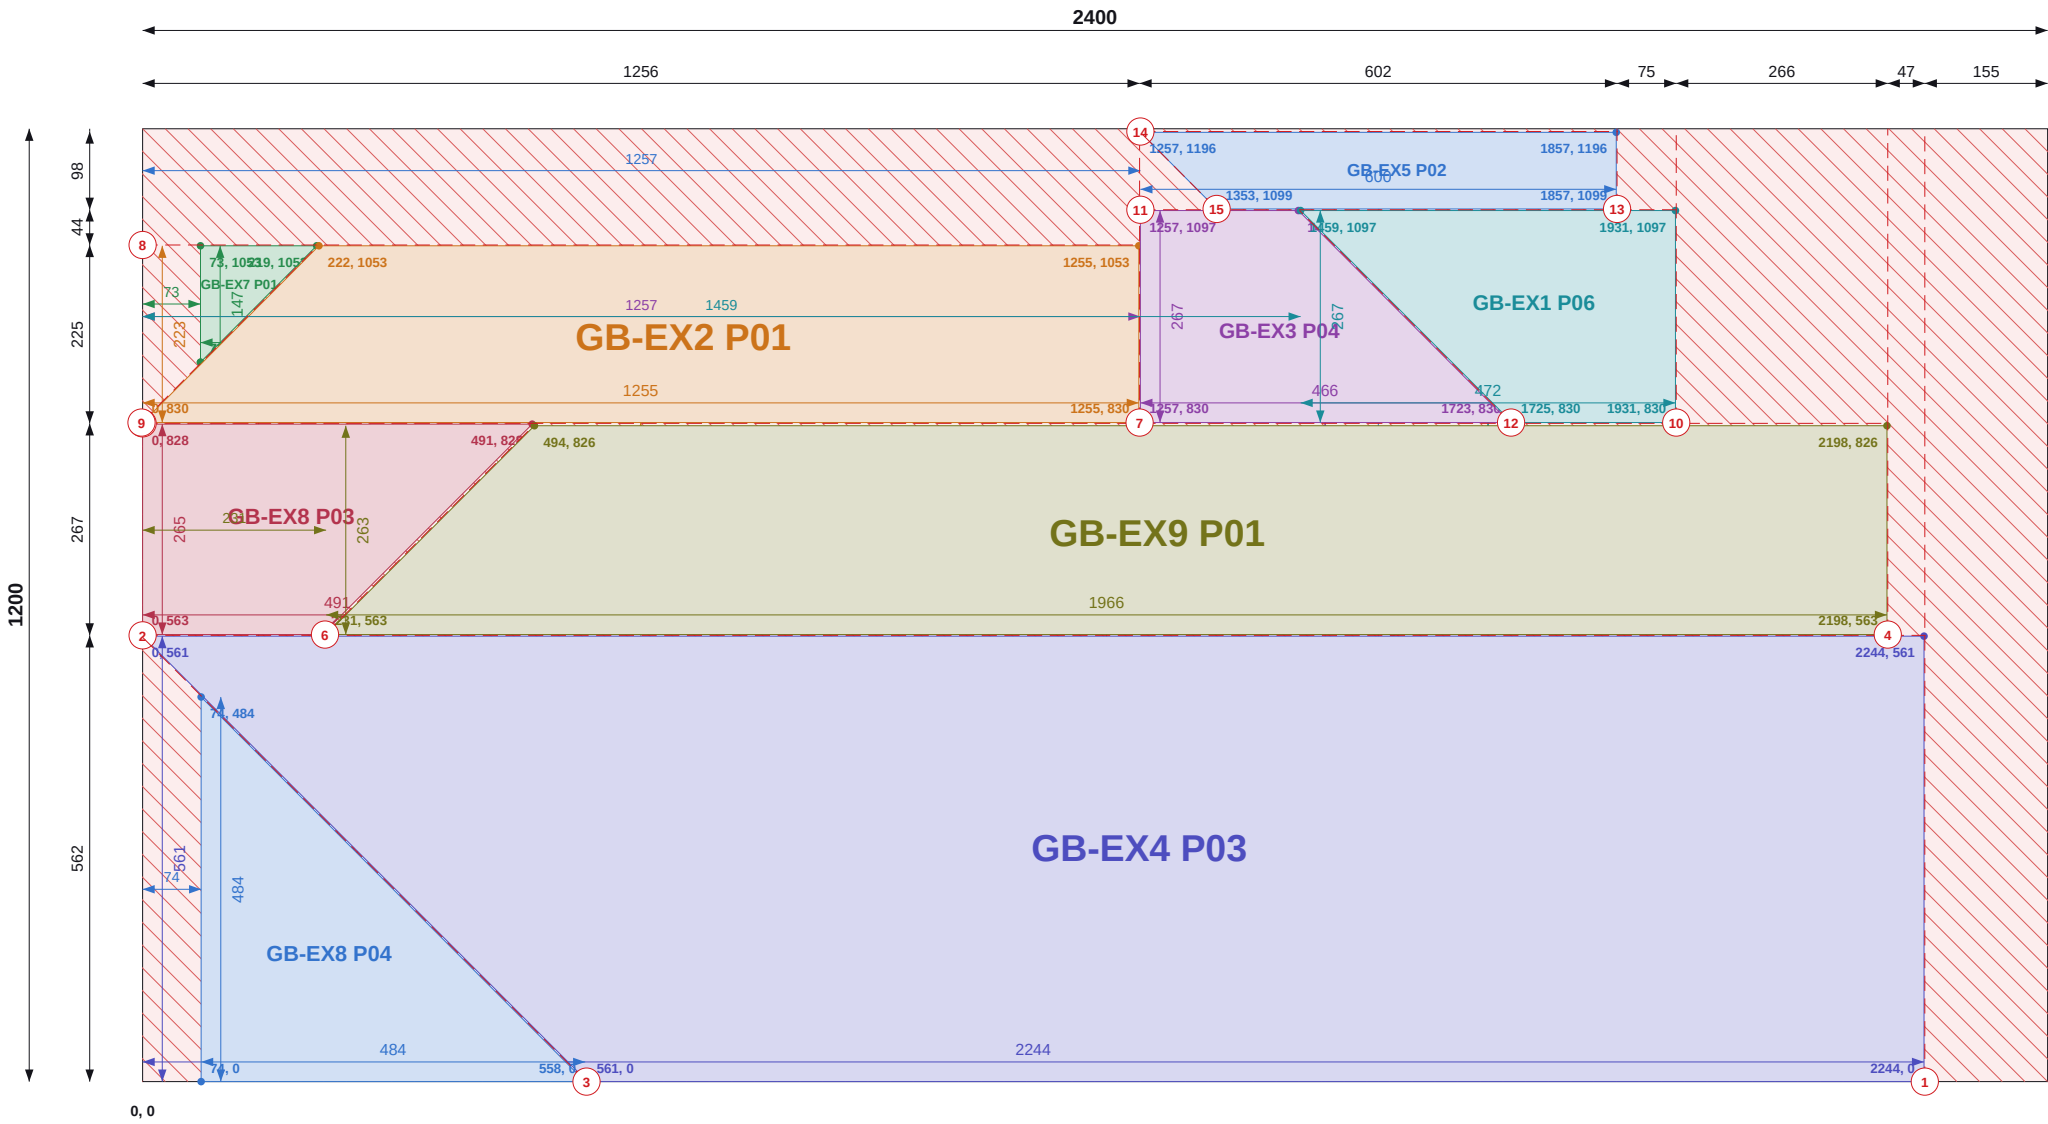

Top / left chains = saw cut positions (to cut centres). Coloured = part size and position.

SHEET 7 OF 11

THIS SHEET

Item	Value
Parts	9
Used / waste	79.7% / 0.59 m2
Reusable offcuts	0
Saw cuts / shared	15 / 9

PIECES (POSITION = BOTTOM-LEFT CORNER)

Label	Size	X, Y
GB-EX5 P02	97 x 599 rake to 505	1257, 1099
GB-EX7 P01	147 x 146 rake to 1	73, 906
GB-EX2 P01	223 x 1255 rake to 1034	0, 830
GB-EX3 P04	267 x 465 rake to 200	1257, 830
GB-EX1 P06	267 x 472 rake to 207	1459, 830
GB-EX8 P03	265 x 491 rake to 227	0, 563
GB-EX9 P01	263 x 1966 rake to 1705	231, 563
GB-EX4 P03	561 x 2244 rake to 1685	0, 0
GB-EX8 P04	484 x 484 rake to 1	74, 0

NOTES

- Cut from PIR 120mm 1200x2400, 2mm saw kerf. Viewed on the face; dimensions from the sheet's bottom-left corner (0,0). Red numbered lines = saw cuts in order, each edge to edge.
- Coloured dimensions belong to the part of that colour: its width and height, and its position from the sheet edges. Raked parts: corner coordinates at each corner.
- Red hatch = waste. Labels = panel + piece mark on the manufacture drawing.

REVISIONS

REV	DATE	DESCRIPTION
C01	13.09.26	Construction issue



TLS TIMBER FRAME

Design & Manufacture

Scan: 3D model + drawings



CLIENT	PROJECT
MP Adams	MP Adams Plot 3, Eckington


DRAWING TITLE
PIR CUTTING - GABLES - SHEET 7 OF 11

PIR 120mm 1200x2400 | Gables

SCALE	SIZE	DATE	DRAWN
NTS	A3	13.09.26	TS

STATUS	DRAWING No.	REV
CONSTRUCTION	P3-CP-PIR-03 / 07	C01

Do not scale. All dimensions in mm. Check all dimensions on site.

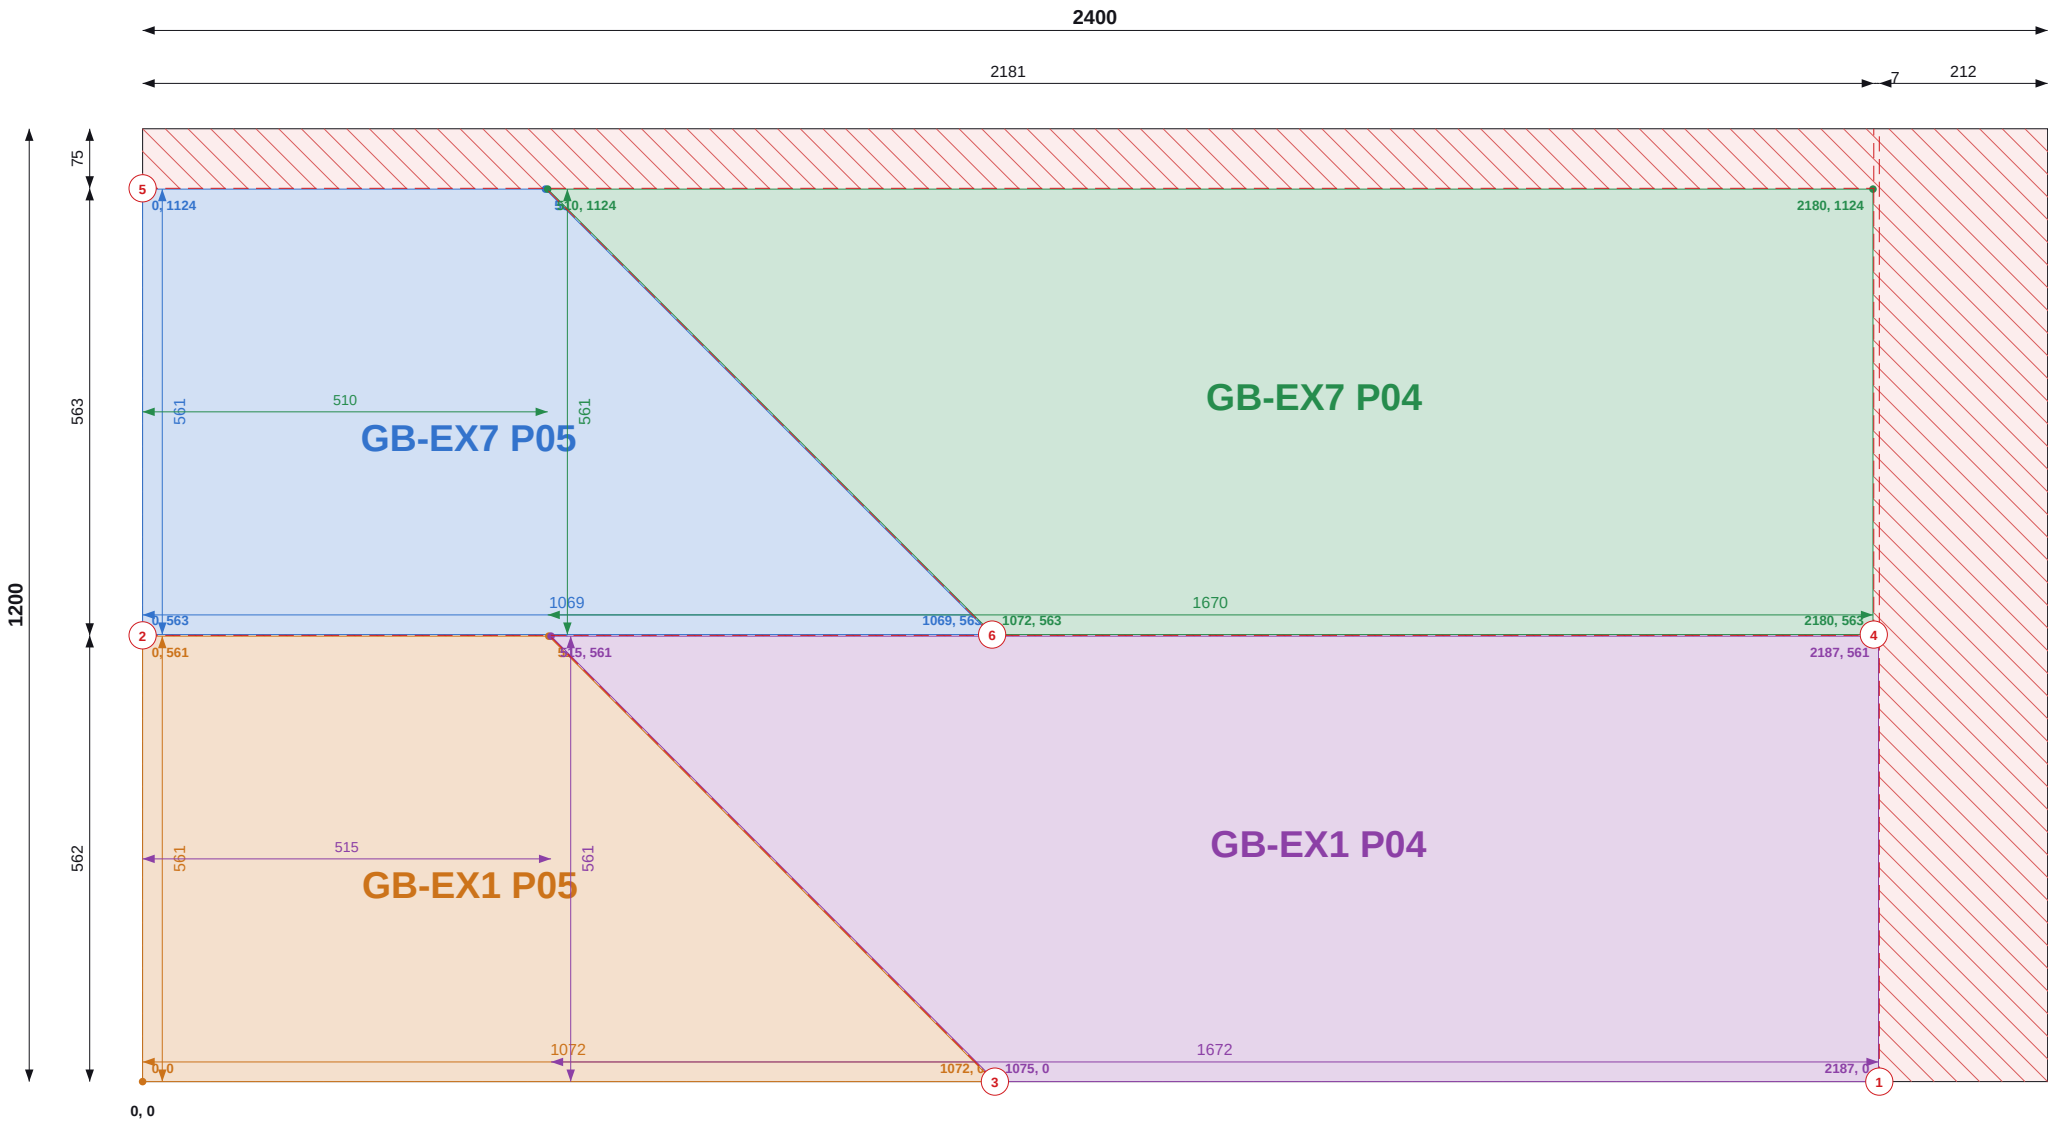

SHEET 8 OF 11

THIS SHEET

Item	Value
Parts	4
Used / waste	85.0% / 0.43 m2
Reusable offcuts	0
Saw cuts / shared	6 / 3

PIECES (POSITION = BOTTOM-LEFT CORNER)

Label	Size	X, Y
GB-EX7 P05	561 x 1069 rake to 509	0, 563
GB-EX7 P04	561 x 1670 rake to 1109	510, 563
GB-EX1 P05	561 x 1072 rake to 513	0, 0
GB-EX1 P04	561 x 1672 rake to 1113	515, 0

NOTES

- Cut from PIR 120mm 1200x2400, 2mm saw kerf. Viewed on the face; dimensions from the sheet's bottom-left corner (0,0). Red numbered lines = saw cuts in order, each edge to edge.
- Coloured dimensions belong to the part of that colour: its width and height, and its position from the sheet edges. Raked parts: corner coordinates at each corner.
- Red hatch = waste. Labels = panel + piece mark on the manufacture drawing.

REVISIONS

REV	DATE	DESCRIPTION
C01	13.09.26	Construction issue



TLS TIMBER FRAME
Design & Manufacture
Scan: 3D model + drawings



CLIENT MP Adams	PROJECT MP Adams Plot 3, Eckington
--------------------	---------------------------------------


DRAWING TITLE
PIR CUTTING - GABLES - SHEET 8 OF 11

PIR 120mm 1200x2400 | Gables

SCALE NTS	SIZE A3	DATE 13.09.26	DRAWN TS
--------------	------------	------------------	-------------

STATUS CONSTRUCTION	DRAWING No. P3-CP-PIR-03 / 08	REV C01
-------------------------------	---	-------------------

Do not scale. All dimensions in mm. Check all dimensions on site.

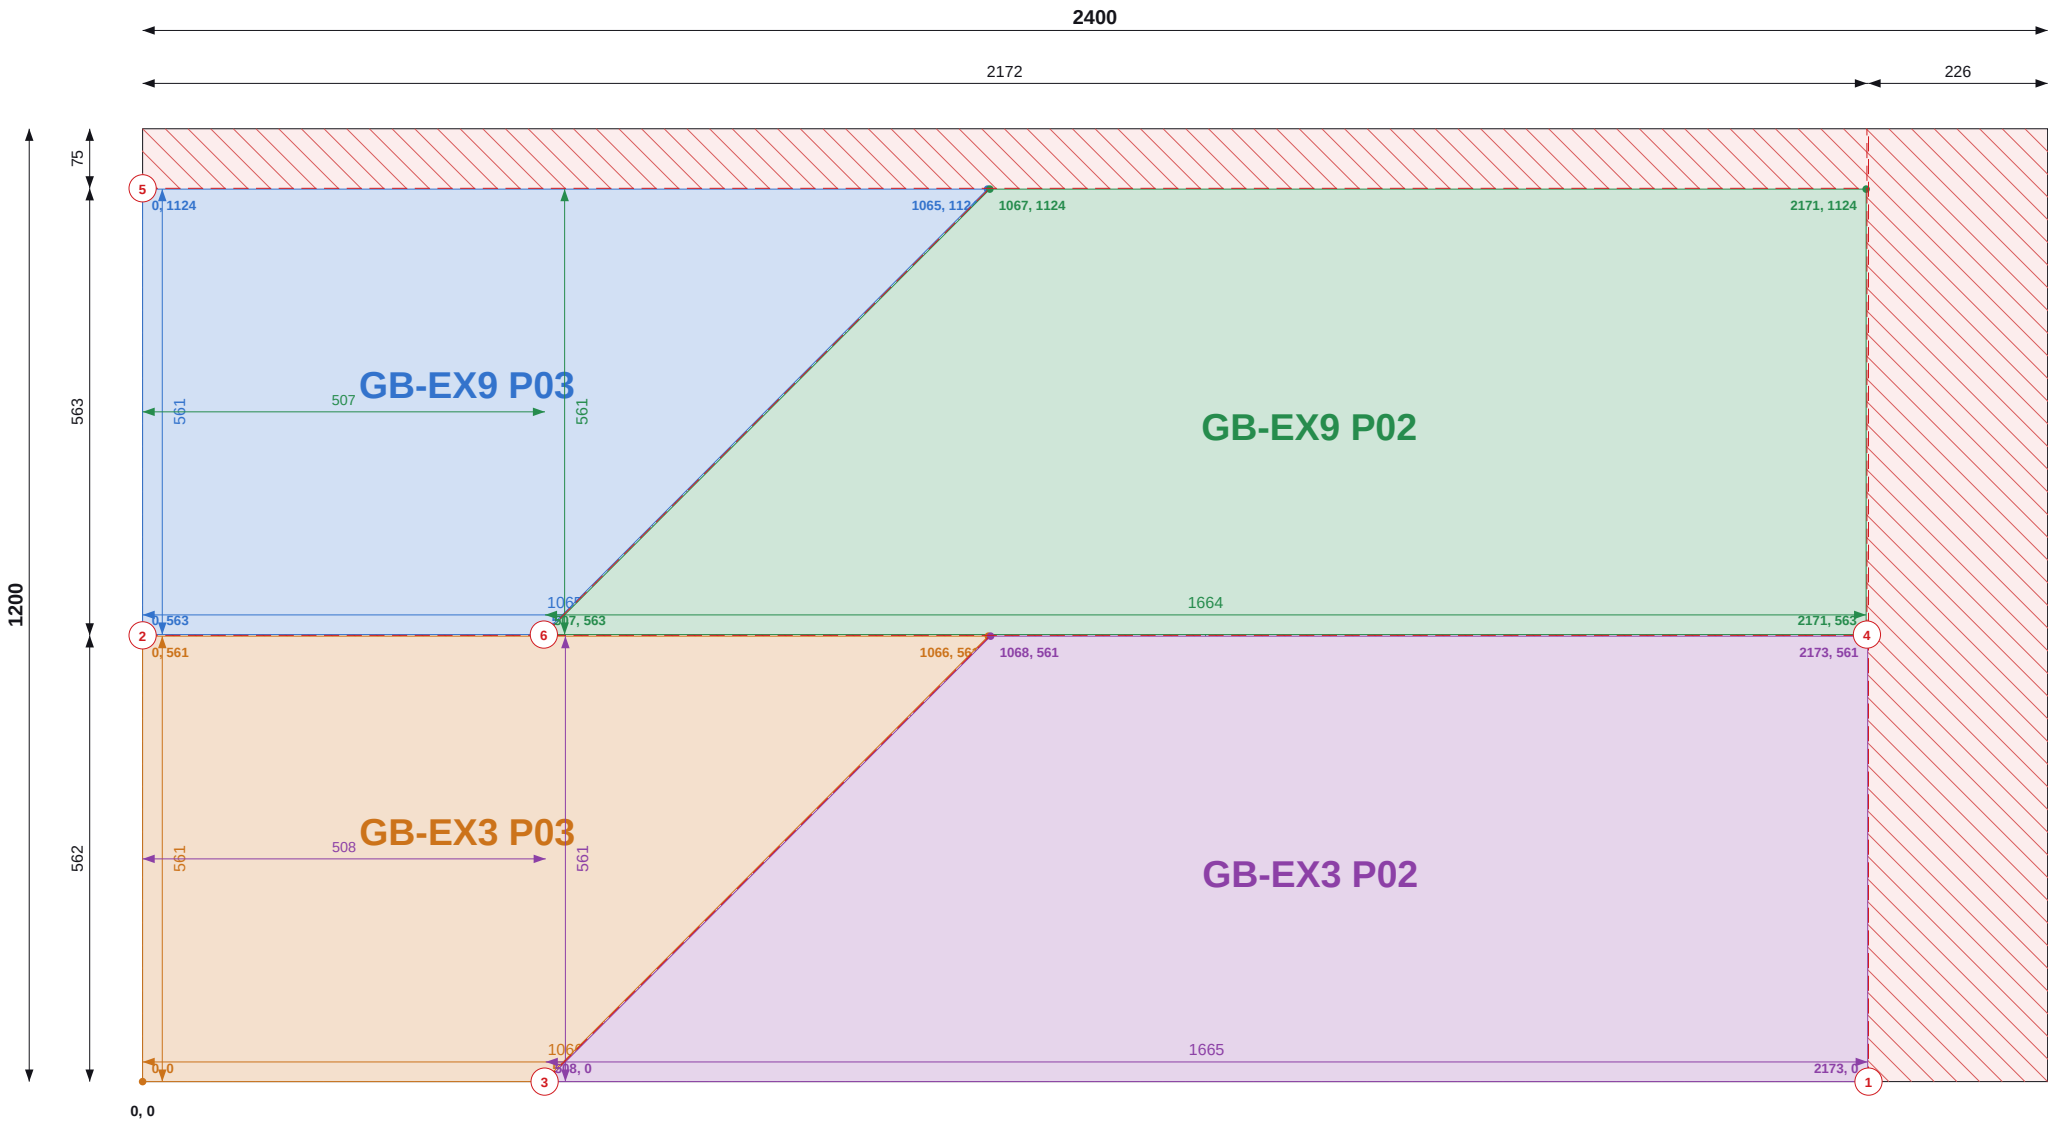

Top / left chains = saw cut positions (to cut centres). Coloured = part size and position.

SHEET 9 OF 11

THIS SHEET

Item	Value
Parts	4
Used / waste	84.5% / 0.45 m2
Reusable offcuts	0
Saw cuts / shared	6 / 3

PIECES (POSITION = BOTTOM-LEFT CORNER)

Label	Size	X, Y
GB-EX9 P03	561 x 1064 rake to 505	0, 563
GB-EX9 P02	561 x 1664 rake to 1105	507, 563
GB-EX3 P03	561 x 1065 rake to 506	0, 0
GB-EX3 P02	561 x 1665 rake to 1106	508, 0

NOTES

- Cut from PIR 120mm 1200x2400, 2mm saw kerf. Viewed on the face; dimensions from the sheet's bottom-left corner (0,0). Red numbered lines = saw cuts in order, each edge to edge.
- Coloured dimensions belong to the part of that colour: its width and height, and its position from the sheet edges. Raked parts: corner coordinates at each corner.
- Red hatch = waste. Labels = panel + piece mark on the manufacture drawing.

REVISIONS

REV	DATE	DESCRIPTION
C01	13.09.26	Construction issue



TLS TIMBER FRAME

Design & Manufacture

Scan: 3D model + drawings



CLIENT MP Adams	PROJECT MP Adams Plot 3, Eckington
--------------------	---------------------------------------


DRAWING TITLE PIR CUTTING - GABLES - SHEET 9 OF 11

PIR 120mm 1200x2400 | Gables

SCALE NTS	SIZE A3	DATE 13.09.26	DRAWN TS
--------------	------------	------------------	-------------

STATUS CONSTRUCTION	DRAWING No. P3-CP-PIR-03 / 09	REV C01
------------------------	----------------------------------	------------

Do not scale. All dimensions in mm. Check all dimensions on site.

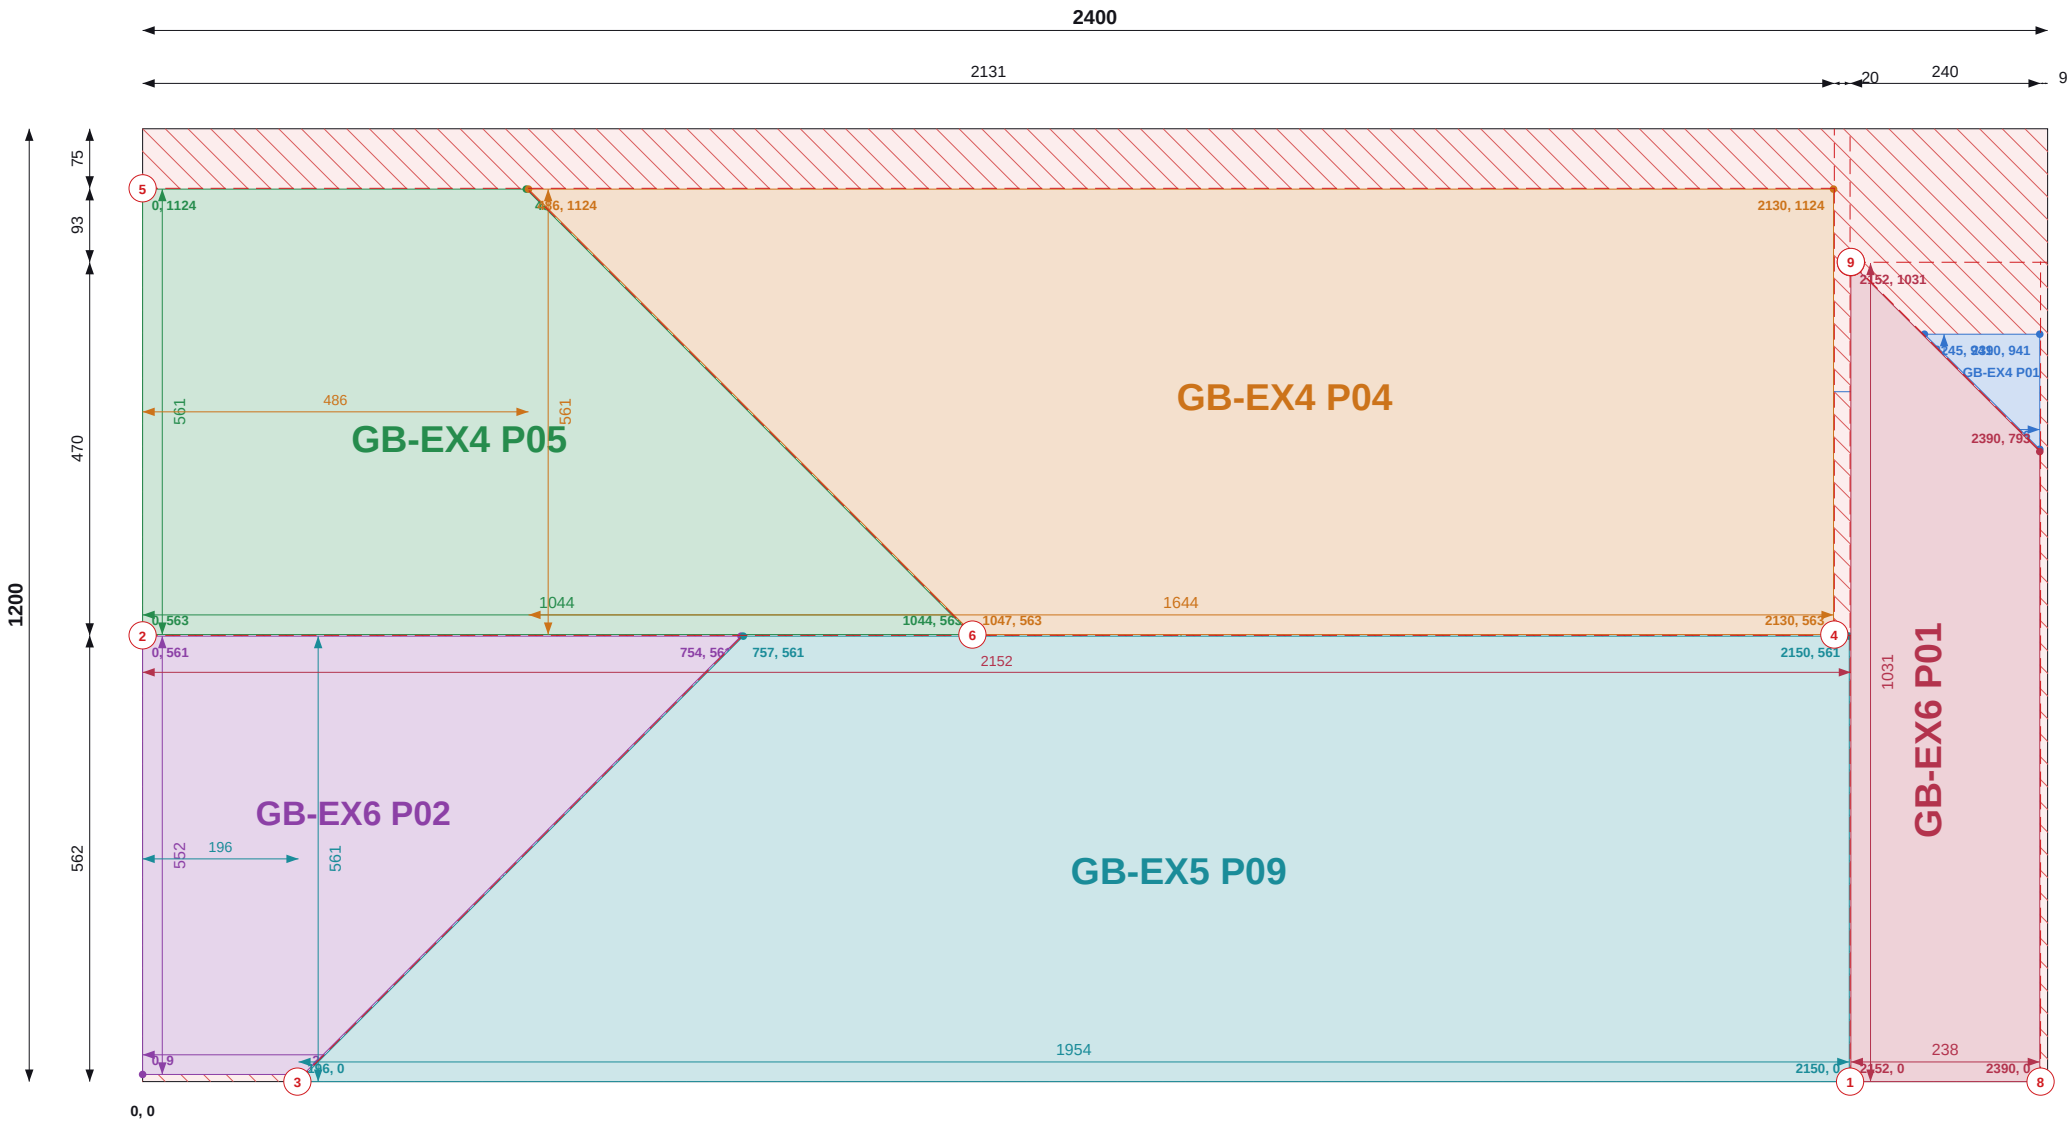

Top / left chains = saw cut positions (to cut centres). Coloured = part size and position.

SHEET 10 OF 11

THIS SHEET

Item	Value
Parts	6
Used / waste	91.1% / 0.26 m2
Reusable offcuts	0
Saw cuts / shared	9 / 5

PIECES (POSITION = BOTTOM-LEFT CORNER)

Label	Size	X, Y
GB-EX4 P01	145 x 145 rake to 1	2245, 796
GB-EX4 P05	561 x 1044 rake to 484	0, 563
GB-EX4 P04	561 x 1644 rake to 1085	486, 563
GB-EX6 P02	552 x 754 rake to 204	0, 9
GB-EX5 P09	561 x 1954 rake to 1394	196, 0
GB-EX6 P01	238 x 1031 rake to 795	2152, 0

NOTES

- Cut from PIR 120mm 1200x2400, 2mm saw kerf. Viewed on the face; dimensions from the sheet's bottom-left corner (0,0). Red numbered lines = saw cuts in order, each edge to edge.
- Coloured dimensions belong to the part of that colour: its width and height, and its position from the sheet edges. Raked parts: corner coordinates at each corner.
- Red hatch = waste. Labels = panel + piece mark on the manufacture drawing.

REVISIONS

REV	DATE	DESCRIPTION
C01	13.09.26	Construction issue



TLS TIMBER FRAME

Design & Manufacture

Scan: 3D model + drawings



CLIENT	PROJECT
MP Adams	MP Adams Plot 3, Eckington


DRAWING TITLE
PIR CUTTING - GABLES - SHEET 10 OF 11

PIR 120mm 1200x2400 | Gables

SCALE	SIZE	DATE	DRAWN
NTS	A3	13.09.26	TS

STATUS	DRAWING No.	REV
CONSTRUCTION	P3-CP-PIR-03 / 10	C01

Do not scale. All dimensions in mm. Check all dimensions on site.

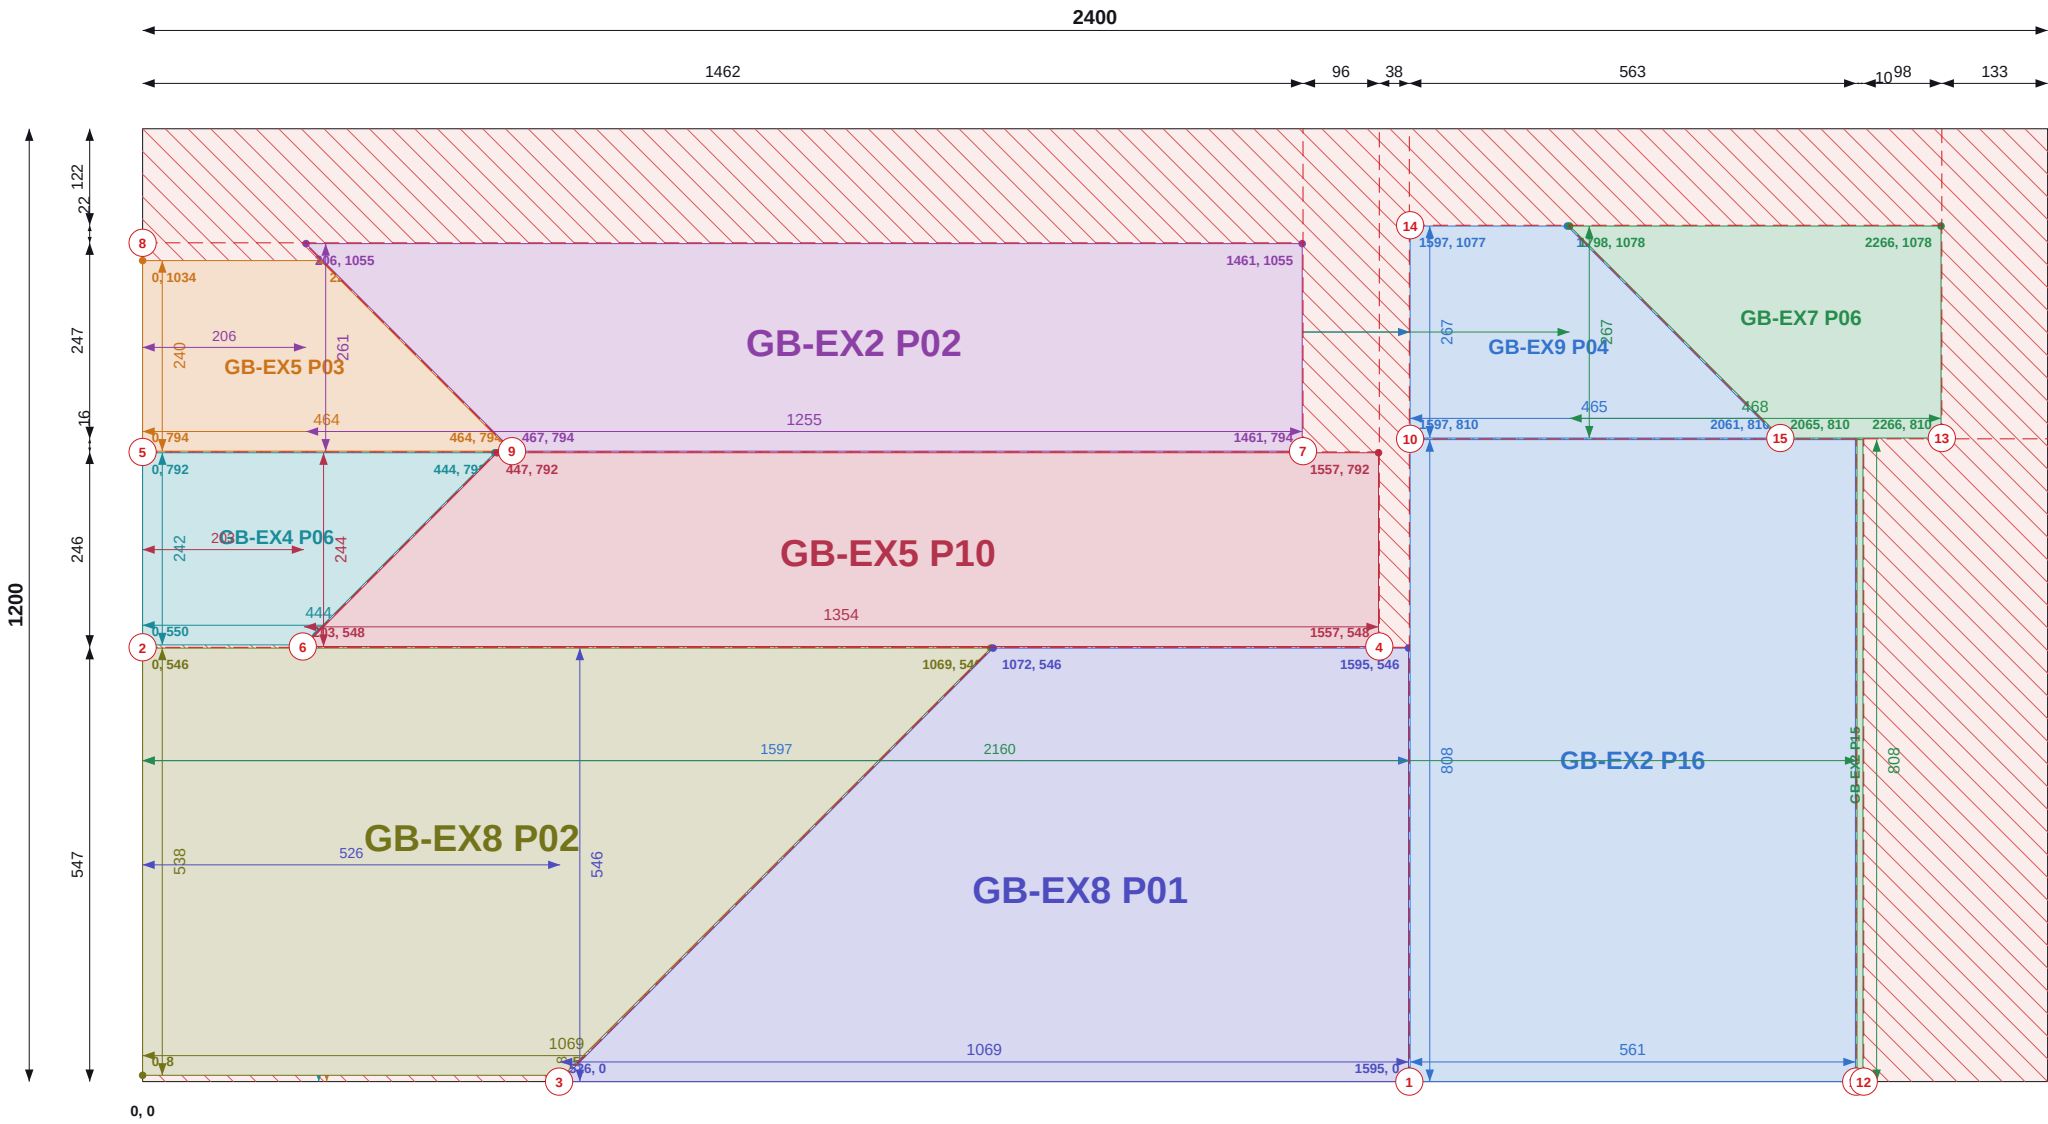

Top / left chains = saw cut positions (to cut centres). Coloured = part size and position.

SHEET 11 OF 11

THIS SHEET

Item	Value
Parts	10
Used / waste	78.4% / 0.62 m2
Reusable offcuts	0
Saw cuts / shared	15 / 9

PIECES (POSITION = BOTTOM-LEFT CORNER)

Label	Size	X, Y
GB-EX9 P04	267 x 464 rake to 199	1597, 810
GB-EX7 P06	267 x 468 rake to 202	1798, 810
GB-EX5 P03	240 x 464 rake to 225	0, 794
GB-EX2 P02	261 x 1255 rake to 995	206, 794
GB-EX4 P06	242 x 444 rake to 203	0, 550
GB-EX5 P10	244 x 1354 rake to 1111	203, 548
GB-EX8 P02	538 x 1069 rake to 531	0, 8
GB-EX8 P01	546 x 1069 rake to 524	526, 0
GB-EX2 P16	561 x 808	1597, 0
GB-EX2 P15	8 x 808	2160, 0

NOTES

- Cut from PIR 120mm 1200x2400, 2mm saw kerf. Viewed on the face; dimensions from the sheet's bottom-left corner (0,0). Red numbered lines = saw cuts in order, each edge to edge.
- Coloured dimensions belong to the part of that colour: its width and height, and its position from the sheet edges. Raked parts: corner coordinates at each corner.
- Red hatch = waste. Labels = panel + piece mark on the manufacture drawing.

REVISIONS

REV	DATE	DESCRIPTION
C01	13.09.26	Construction issue



TLS TIMBER FRAME

Design & Manufacture

Scan: 3D model + drawings



CLIENT	PROJECT
MP Adams	MP Adams Plot 3, Eckington

DRAWING TITLE
PIR CUTTING - GABLES - SHEET 11 OF 11

PIR 120mm 1200x2400 | Gables

SCALE	SIZE	DATE	DRAWN
NTS	A3	13.09.26	TS

STATUS	DRAWING No.	REV
CONSTRUCTION	P3-CP-PIR-03 / 11	C01