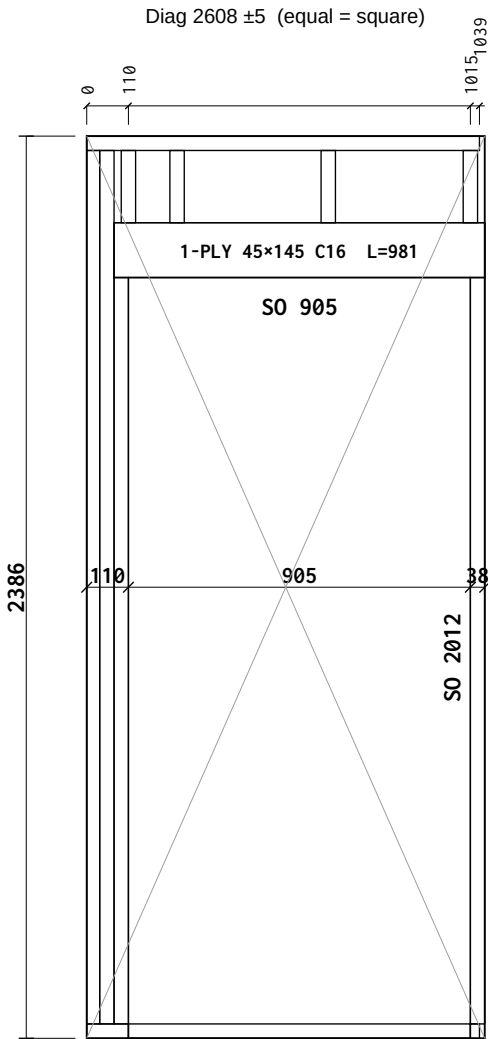


Cut List

Item	Section	Len	Bot°	Top°	Qty
BR1	Bottom Rail	38×89 C16	905	0	0 1
BR2	Bottom Rail	38×89 C16	110	0	0 1
BR3	Bottom Rail	38×89 C16	24	0	0 1
TR1	Top Rail	38×89 C16	1039	0	0 1
ES1	End Stud	38×89 C16	191	0	0 1
ES2	End Stud	38×89 C16	191	0	0 1
KS1	Vertical Stud	38×89 C16	2310	0	0 1
CS1	Cripple Stud	38×89 C16	1974	0	0 2
LP1	Lintel Ply	981×45 C16	981	0	0 1
PK1	Lintel Packer	981×41 C16	981	0	0 1
OS1	OSB Support	38×89 C16	191	0	0 2
JS1	Junction Stud	38×34 C16	2310	0	0 1

Total: 14 pcs / 13.37 m

Sheathing & Insulation

Material	W	HLabel
----------	---	--------

General Notes:

Frame Nailing:
140mm Frames Nail Using 3no, 3.1×90mm length field galvanised twisted strip nails
90mm Frames Nail Using 2no, 3.1×90mm length field galvanised twisted strip nails


Sheathing Nails:
Components ≤ 100mm should be +/- 1mm
Components > 100mm should be +/- 1.5mm
Stepped check should be +/- 1.5mm
Sloped Opening sizes are +/-2mm

Nailing:
30x90mm Nails, 75mm Ctrs Perimeter / 150mm Ctrs Internal.

Manufacturing Tolerances:
Length ±3 · Height ±2 · Diagonals ±5 · Openings 0/+5 (mm).
Do not scale — work to figured dimensions. All dims in mm.

Panel Changes:
When the panel design is changed, a clean-up of the workbench, jig, and offcut tray is required before the next panel is laid out. Verify cut-list against this drawing's revision before continuing.


KEY PLAN

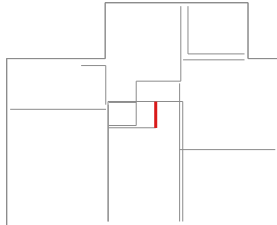

Revisions (Rev · Date · Note):

C01 - Construction issue

Date:	2026-09-13	Scale:	1:20	Drawn:	TS	Checked:	
Project Name:	MP Adams Plot 3, Eckington						
Site:	Eckington			Client:	MP Adams		
Title:	Panel Fabrication — 38 x 140 C16 CLS						
Project Number:	P3			Revision:	C01		
Panel No:	GF-IN1			Drawing No:	P3-MF-GF-IN1		
Panel L×H×T:	1053×2386×89			Weight:	19 kg		
Status:	CONSTRUCTION			Sheet:	1 / 1		

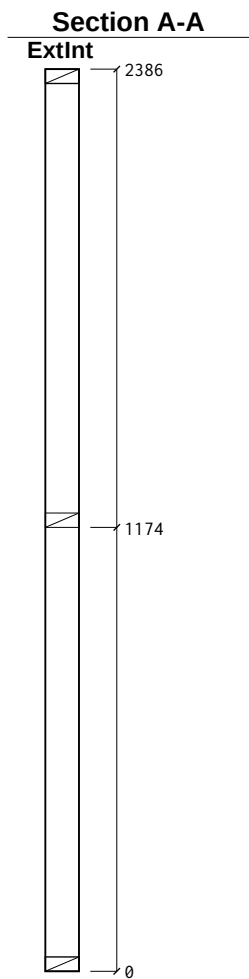

Item	Section	Len	Bot°	Top° Qty
BR1 Bottom Rail	38x89 C16	1807	0	0 1
TR1 Top Rail	38x89 C16	1807	0	0 1
ES1 End Stud	38x89 C16	2310	0	0 1
ES2 End Stud	38x89 C16	2310	0	0 1
VS1 Vertical Stud	38x89 C16	2310	0	0 4
NG1 Noggin	38x89 C16	372	0	0 1
NG2 Noggin	38x89 C16	360	0	0 3
NG3 Noggin	38x89 C16	118	0	0 1
Total: 13 pcs / 19.04 m				
Sheathing & Insulation				
Material			W	HLabel

General Notes:

Frame Nailing:

140mm Frames Nail Using 3no, 3.1×90mm length field galvanised twisted strip nails

90mm Frames Nail Using 2no, 3.1×90mm length field galvanised twisted strip nails

Sheathing Nails:

Components ≤ 100mm should be +/- 1mm

Components > 100mm should be +/- 1.5mm

Stepped check should be +/- 1.5mm

Sloped Opening sizes are +/-2mm

Nailing:

30x90mm Nails, 75mm Ctrs Perimeter / 150mm Ctrs Internal.

Manufacturing Tolerances:


Length ±3 · Height ±2 · Diagonals ±5 · Openings 0/+5 (mm).

Do not scale — work to figured dimensions. All dims in mm.

Panel Changes:

When the panel design is changed, a clean-up of the workbench, jig, and offcut tray is required before the next panel is laid out. Verify cut-list against this drawing's revision before continuing.

KEY PLAN

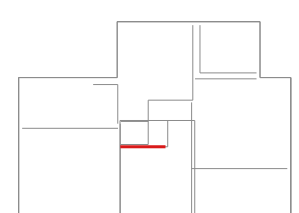

Revisions (Rev · Date · Note):

C01 - Construction issue

Date:2026-09-13

Scale:1:20

Drawn:TS

Checked:

Project Name:

MP Adams Plot 3, Eckington

Site:Eckington

Client:MP Adams

Title:

Panel Fabrication — 38 x 140 C16 CLS

Project Number:P3

Revision:C01

Panel No:GF-IN2




Drawing No:P3-MF-GF-IN2

Panel LxHxT:1807×2386×89

Weight:27 kg

Status:CONSTRUCTION

Sheet:1 / 1

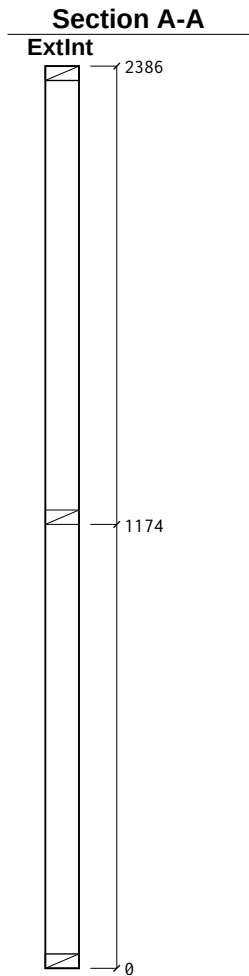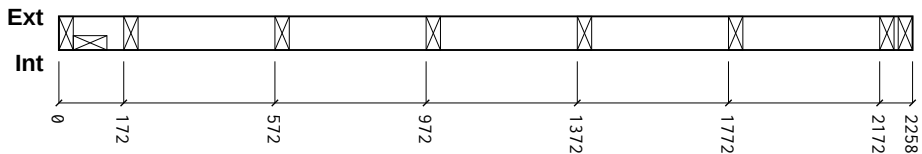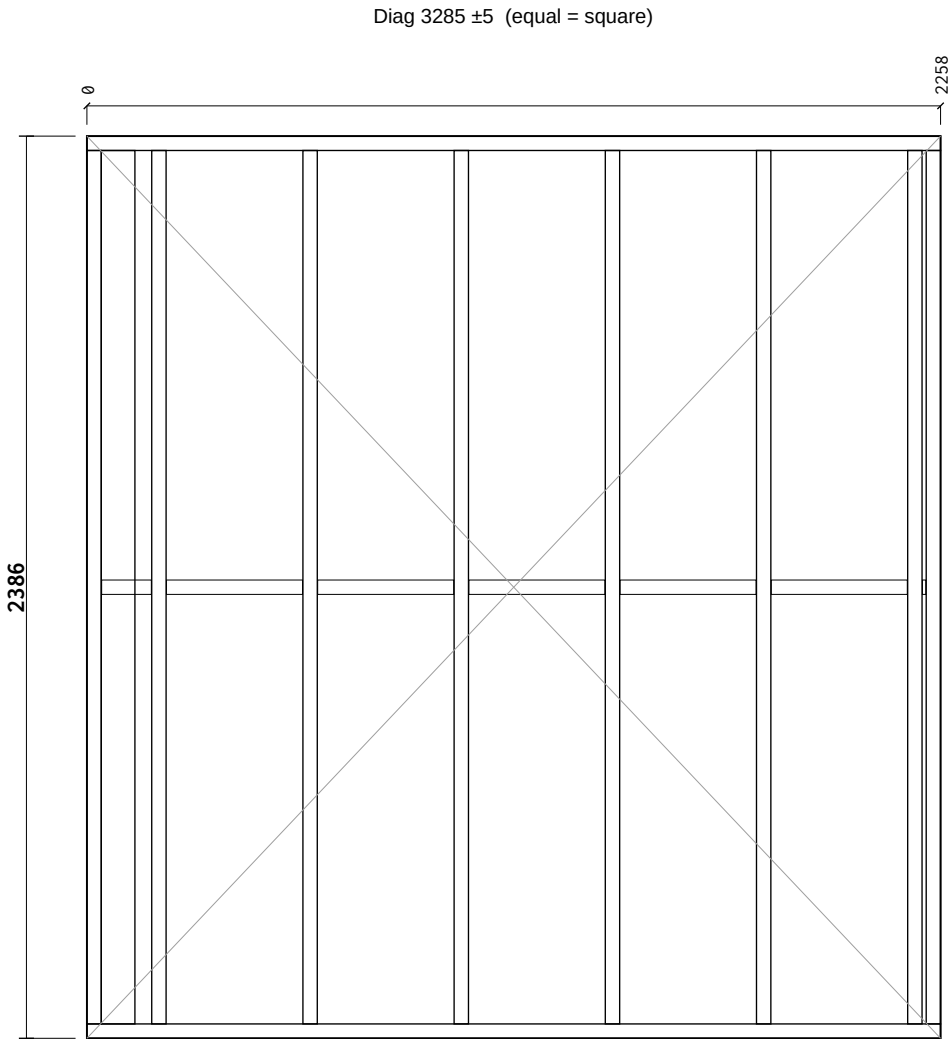

Cut List

Item	Section	Len	Bot°	Top°	Qty
BR1 Bottom Rail	38×89 C16	2258	0	0	1
TR1 Top Rail	38×89 C16	2258	0	0	1
ES1 End Stud	38×89 C16	2310	0	0	1
ES2 End Stud	38×89 C16	2310	0	0	1
VS1 Vertical Stud	38×89 C16	2310	0	0	6
JS1 Junction Stud	38×89 C16	2310	0	0	1
NG1 Noggin	38×89 C16	360	0	0	5
NG2 Noggin	38×89 C16	132	0	0	1
NG3 Noggin	38×89 C16	9	0	0	1
Total: 18 pcs / 27.25 m					

Sheathing & Insulation

Material	W	HLabel
----------	---	--------

General Notes:

Frame Nailing:
140mm Frames Nail Using 3no, 3.1×90mm length field galvanised twisted strip nails
90mm Frames Nail Using 2no, 3.1×90mm length field galvanised twisted strip nails


Sheathing Nails:
Components ≤ 100mm should be +/- 1mm
Components > 100mm should be +/- 1.5mm
Stepped check should be +/- 1.5mm
Sloped Opening sizes are +/-2mm

Nailing:
30x90mm Nails, 75mm Ctrs Perimeter / 150mm Ctrs Internal.

Manufacturing Tolerances:
Length ±3 · Height ±2 · Diagonals ±5 · Openings 0/+5 (mm).
Do not scale — work to figured dimensions. All dims in mm.

Panel Changes:
When the panel design is changed, a clean-up of the workbench, jig, and offcut tray is required before the next panel is laid out. Verify cut-list against this drawing's revision before continuing.




KEY PLAN

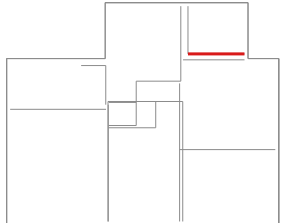

Revisions (Rev · Date · Note):

C01 - Construction issue

Date:	2026-09-13	Scale:	1:20	Drawn:	TS	Checked:	
Project Name:		MP Adams Plot 3, Eckington					
Site:	Eckington			Client:	MP Adams		
Title:		Panel Fabrication — 38 x 140 C16 CLS					
Project Number:		P3		Revision:	C01		
Panel No:		GF-IN3		Drawing No:	P3-MF-GF-IN3		
Panel L×H×T:		2258×2386×89		Weight:	39 kg		
Status:		CONSTRUCTION		Sheet:	1 / 1		

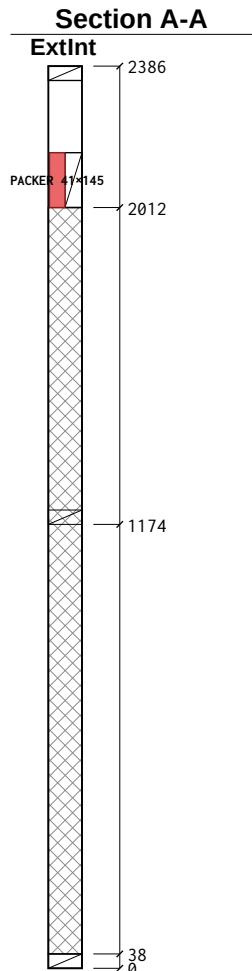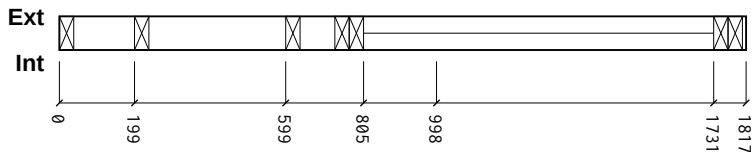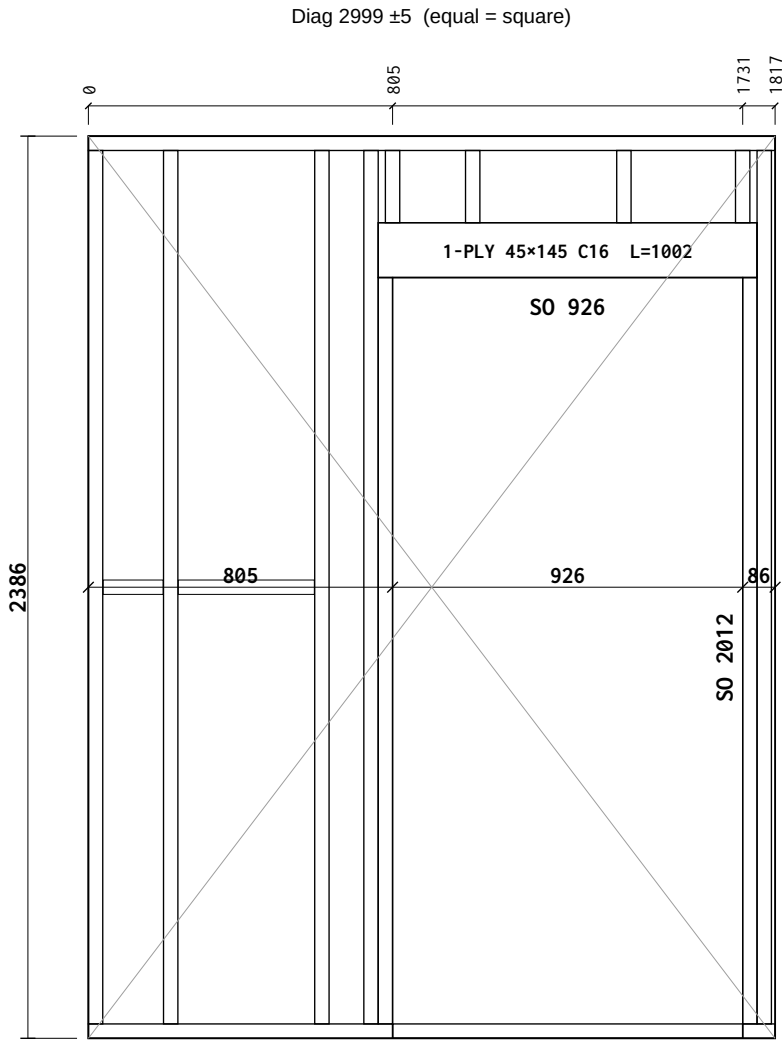

Cut List

Item	Section	Len	Bot°	Top°	Qty
BR1	Bottom Rail	38×89 C16	926	0	0 1
BR2	Bottom Rail	38×89 C16	805	0	0 1
BR3	Bottom Rail	38×89 C16	86	0	0 1
TR1	Top Rail	38×89 C16	1817	0	0 1
ES1	End Stud	38×89 C16	2310	0	0 1
ES2	End Stud	38×89 C16	191	0	0 1
KS1	Vertical Stud	38×89 C16	2310	0	0 2
CS1	Cripple Stud	38×89 C16	1974	0	0 2
LP1	Lintel Ply	1002×45 C16	1002	0	0 1
PK1	Lintel Packer	1002×41 C16	1002	0	0 1
OS1	OSB Support	38×89 C16	191	0	0 2
VS1	Vertical Stud	38×89 C16	2310	0	0 2
VS2	Vertical Stud	38×89 C16	191	0	0 1
NG1	Noggin	38×89 C16	360	0	0 1
NG2	Noggin	38×89 C16	159	0	0 1

Total: 19 pcs / 22.42 m

Sheathing & Insulation

Material	W	HLabelI
----------	---	---------

General Notes:

Frame Nailing:
140mm Frames Nail Using 3no, 3.1×90mm length field galvanised twisted strip nails
90mm Frames Nail Using 2no, 3.1×90mm length field galvanised twisted strip nails


Sheathing Nails:
Components ≤ 100mm should be +/- 1mm
Components > 100mm should be +/- 1.5mm
Stepped check should be +/- 1.5mm
Sloped Opening sizes are +/-2mm

Nailing:
30x90mm Nails, 75mm Ctrs Perimeter / 150mm Ctrs Internal.

Manufacturing Tolerances:
Length ±3 · Height ±2 · Diagonals ±5 · Openings 0/+5 (mm).
Do not scale — work to figured dimensions. All dims in mm.

Panel Changes:
When the panel design is changed, a clean-up of the workbench, jig, and offcut tray is required before the next panel is laid out. Verify cut-list against this drawing's revision before continuing.

KEY PLAN

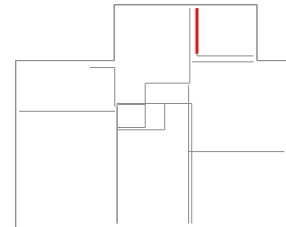

Revisions (Rev · Date · Note):

C01 - Construction issue

Date:	2026-09-13	Scale:	1:20	Drawn:	TS	Checked:	
Project Name:	MP Adams Plot 3, Eckington						
Site:	Eckington			Client:	MP Adams		
Title:	Panel Fabrication — 38 x 140 C16 CLS						
Project Number:	P3			Revision:	C01		
Panel No:	GF-IN4			Drawing No:	P3-MF-GF-IN4		
Panel L×H×T:	1817×2386×89			Weight:	34 kg		
Status:	CONSTRUCTION			Sheet:	1 / 1		