

Do not scale. All dimensions in mm. Check all dimensions on site.



Top / left chains = saw cut positions (to cut centres). Coloured = part size and position.

SHEET 1 OF 38

THIS SHEET

Item	Value
Parts	1
Used / waste	99.4% / 0.02 m2
Reusable offcuts	0
Saw cuts / shared	1 / 0

PIECES (POSITION = BOTTOM-LEFT CORNER)

Label	Size	X, Y
GF-EX1 S02	1197 x 2383	0, 0

GROUND FLOOR TOTALS

Item	Value
Sheets / pieces	38 / 79
Yield / waste	92.4% / 8.25 m2
Saw cuts / shared / on stock edge	119 / 41 / 118

NOTES

- Cut from OSB/3 9mm 1197x2397, 2mm saw kerf. Viewed on the face; dimensions from the sheet's bottom-left corner (0,0). Red numbered lines = saw cuts in order, each edge to edge.
- Coloured dimensions belong to the part of that colour: its width and height, and its position from the sheet edges. Raked parts: corner coordinates at each corner.
- Red hatch = waste. Labels = panel + piece mark on the manufacture drawing.

REVISIONS

REV	DATE	DESCRIPTION
C01	13.09.26	Construction issue



TLS TIMBER FRAME

Design & Manufacture

Scan: 3D model + drawings



CLIENT	PROJECT
MP Adams	MP Adams Plot 3, Eckington

DRAWING TITLE
OSB CUTTING - GROUND FLOOR - SHEET 1 OF 38

OSB/3 9mm 1197x2397 | Ground Floor

SCALE	SIZE	DATE	DRAWN
NTS	A3	13.09.26	TS

STATUS	DRAWING No.	REV
CONSTRUCTION	P3-CP-OSB-01 / 01	C01

Do not scale. All dimensions in mm. Check all dimensions on site.



Top / left chains = saw cut positions (to cut centres). Coloured = part size and position.

SHEET 2 OF 38

THIS SHEET

Item	Value
Parts	1
Used / waste	99.4% / 0.02 m2
Reusable offcuts	0
Saw cuts / shared	1 / 0

PIECES (POSITION = BOTTOM-LEFT CORNER)

Label	Size	X, Y
GF-IL6 S02	1197 x 2383	0, 0

NOTES

1. Cut from OSB/3 9mm 1197x2397, 2mm saw kerf. Viewed on the face; dimensions from the sheet's bottom-left corner (0,0). Red numbered lines = saw cuts in order, each edge to edge.
2. Coloured dimensions belong to the part of that colour: its width and height, and its position from the sheet edges. Raked parts: corner coordinates at each corner.
3. Red hatch = waste. Labels = panel + piece mark on the manufacture drawing.

REVISIONS

REV	DATE	DESCRIPTION
C01	13.09.26	Construction issue



TLS TIMBER FRAME

Design & Manufacture

Scan: 3D model + drawings



CLIENT	PROJECT
MP Adams	MP Adams Plot 3, Eckington

DRAWING TITLE			
OSB CUTTING - GROUND FLOOR - SHEET 2 OF 38			
OSB/3 9mm 1197x2397 Ground Floor			

SCALE	SIZE	DATE	DRAWN
NTS	A3	13.09.26	TS

STATUS	DRAWING No.	REV
CONSTRUCTION	P3-CP-OSB-01 / 02	C01

Do not scale. All dimensions in mm. Check all dimensions on site.



Top / left chains = saw cut positions (to cut centres). Coloured = part size and position.

SHEET 3 OF 38

THIS SHEET

Item	Value
Parts	1
Used / waste	99.4% / 0.02 m2
Reusable offcuts	0
Saw cuts / shared	1 / 0

PIECES (POSITION = BOTTOM-LEFT CORNER)

Label	Size	X, Y
GF-IL1 S02	1197 x 2383	0, 0

NOTES

- Cut from OSB/3 9mm 1197x2397, 2mm saw kerf. Viewed on the face; dimensions from the sheet's bottom-left corner (0,0). Red numbered lines = saw cuts in order, each edge to edge.
- Coloured dimensions belong to the part of that colour: its width and height, and its position from the sheet edges. Raked parts: corner coordinates at each corner.
- Red hatch = waste. Labels = panel + piece mark on the manufacture drawing.

REVISIONS

REV	DATE	DESCRIPTION
C01	13.09.26	Construction issue



TLS TIMBER FRAME

Design & Manufacture

Scan: 3D model + drawings



CLIENT	PROJECT
MP Adams	MP Adams Plot 3, Eckington


DRAWING TITLE
OSB CUTTING - GROUND FLOOR - SHEET 3 OF 38

OSB/3 9mm 1197x2397 | Ground Floor

SCALE	SIZE	DATE	DRAWN
NTS	A3	13.09.26	TS

STATUS	DRAWING No.	REV
CONSTRUCTION	P3-CP-OSB-01 / 03	C01

Do not scale. All dimensions in mm. Check all dimensions on site.

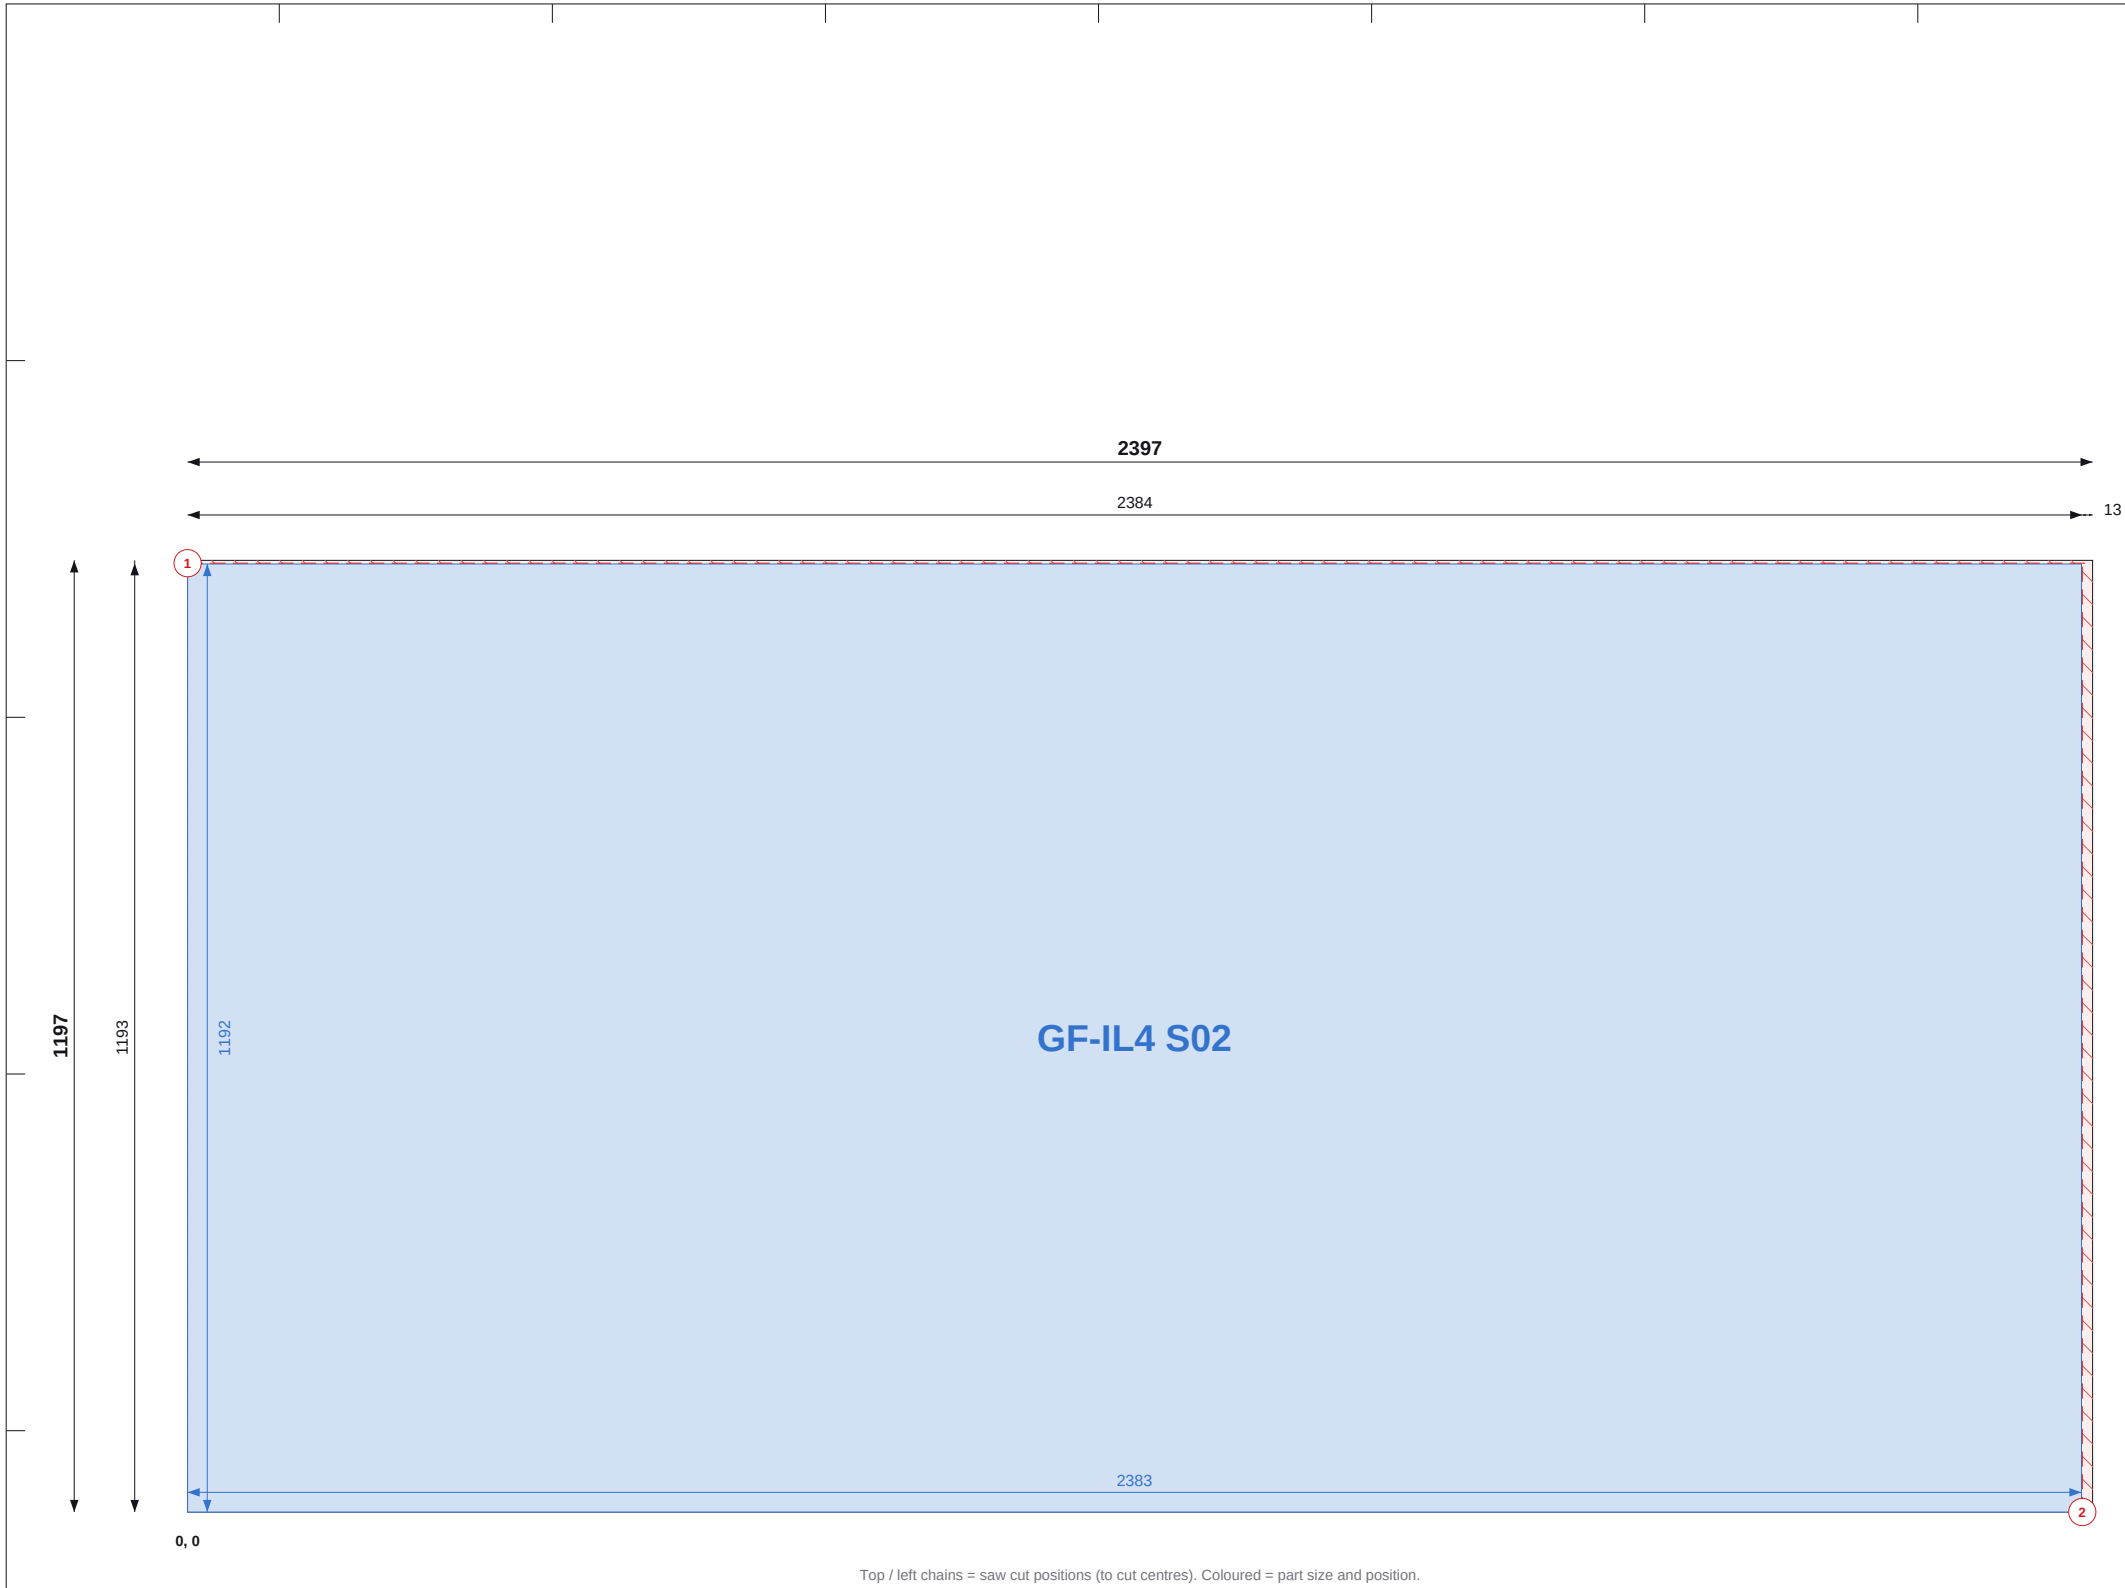

Top / left chains = saw cut positions (to cut centres). Coloured = part size and position.

SHEET 4 OF 38

THIS SHEET

Item	Value
Parts	1
Used / waste	99.0% / 0.03 m2
Reusable offcuts	0
Saw cuts / shared	2 / 0

PIECES (POSITION = BOTTOM-LEFT CORNER)

Label	Size	X, Y
GF-IL4 S02	1192 x 2383	0, 0

NOTES

- Cut from OSB/3 9mm 1197x2397, 2mm saw kerf. Viewed on the face; dimensions from the sheet's bottom-left corner (0,0). Red numbered lines = saw cuts in order, each edge to edge.
- Coloured dimensions belong to the part of that colour: its width and height, and its position from the sheet edges. Raked parts: corner coordinates at each corner.
- Red hatch = waste. Labels = panel + piece mark on the manufacture drawing.

REVISIONS

REV	DATE	DESCRIPTION
C01	13.09.26	Construction issue



TLS TIMBER FRAME

Design & Manufacture

Scan: 3D model + drawings




CLIENT	PROJECT
MP Adams	MP Adams Plot 3, Eckington

DRAWING TITLE			
OSB CUTTING - GROUND FLOOR - SHEET 4 OF 38			
OSB/3 9mm 1197x2397 Ground Floor			

SCALE	SIZE	DATE	DRAWN
NTS	A3	13.09.26	TS

STATUS	DRAWING No.	REV
CONSTRUCTION	P3-CP-OSB-01 / 04	C01

Do not scale. All dimensions in mm. Check all dimensions on site.

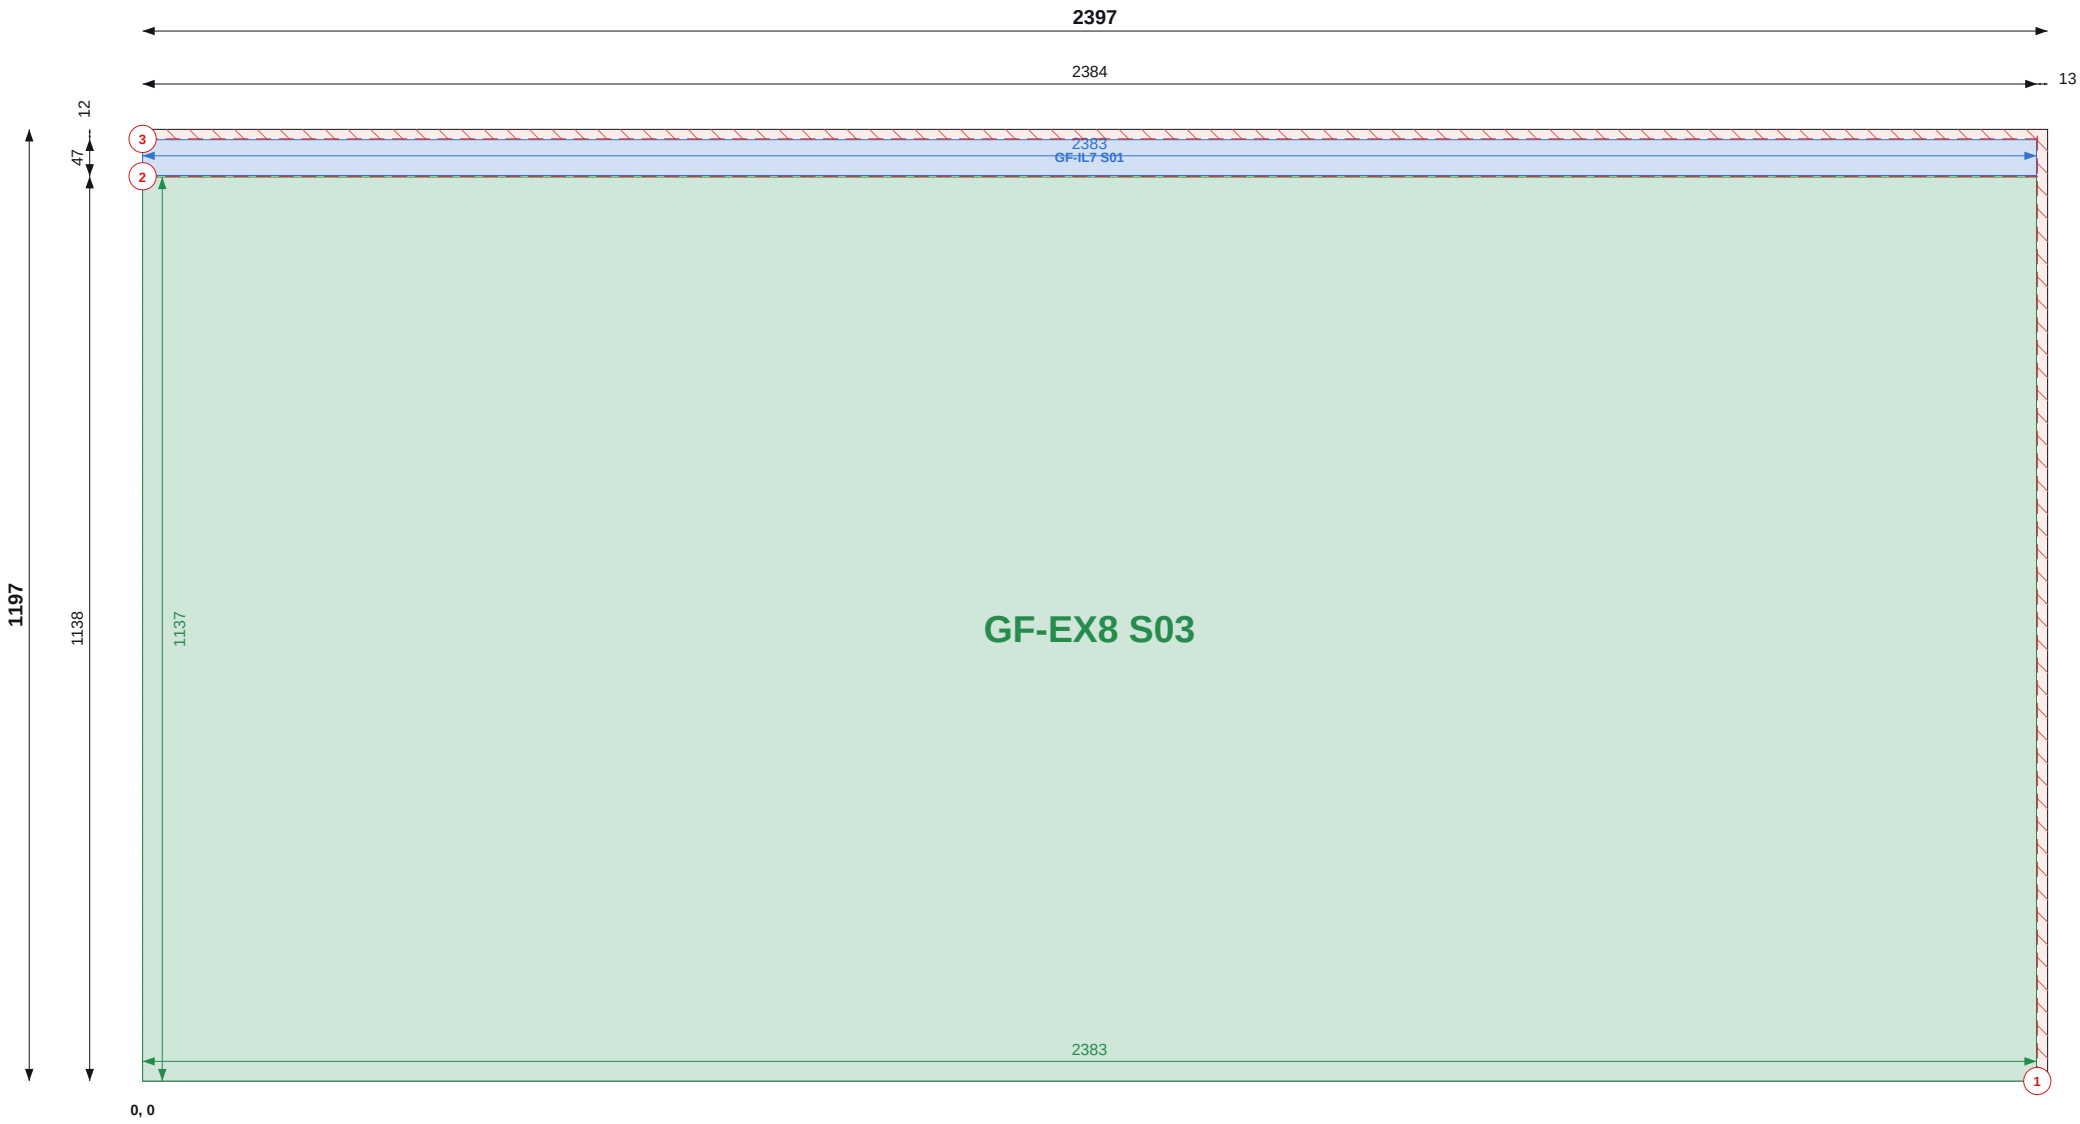

Top / left chains = saw cut positions (to cut centres). Coloured = part size and position.

SHEET 5 OF 38

THIS SHEET

Item	Value
Parts	2
Used / waste	98.2% / 0.05 m2
Reusable offcuts	0
Saw cuts / shared	3 / 1

PIECES (POSITION = BOTTOM-LEFT CORNER)

Label	Size	X, Y
GF-IL7 S01	45 x 2383	0, 1139
GF-EX8 S03	1137 x 2383	0, 0

NOTES

- Cut from OSB/3 9mm 1197x2397, 2mm saw kerf. Viewed on the face; dimensions from the sheet's bottom-left corner (0,0). Red numbered lines = saw cuts in order, each edge to edge.
- Coloured dimensions belong to the part of that colour: its width and height, and its position from the sheet edges. Raked parts: corner coordinates at each corner.
- Red hatch = waste. Labels = panel + piece mark on the manufacture drawing.

REVISIONS

REV	DATE	DESCRIPTION
C01	13.09.26	Construction issue



TLS TIMBER FRAME

Design & Manufacture

Scan: 3D model + drawings




CLIENT	PROJECT
MP Adams	MP Adams Plot 3, Eckington

DRAWING TITLE			
OSB CUTTING - GROUND FLOOR - SHEET 5 OF 38			
OSB/3 9mm 1197x2397 Ground Floor			

SCALE	SIZE	DATE	DRAWN
NTS	A3	13.09.26	TS

STATUS	DRAWING No.	REV
CONSTRUCTION	P3-CP-OSB-01 / 05	C01

Do not scale. All dimensions in mm. Check all dimensions on site.

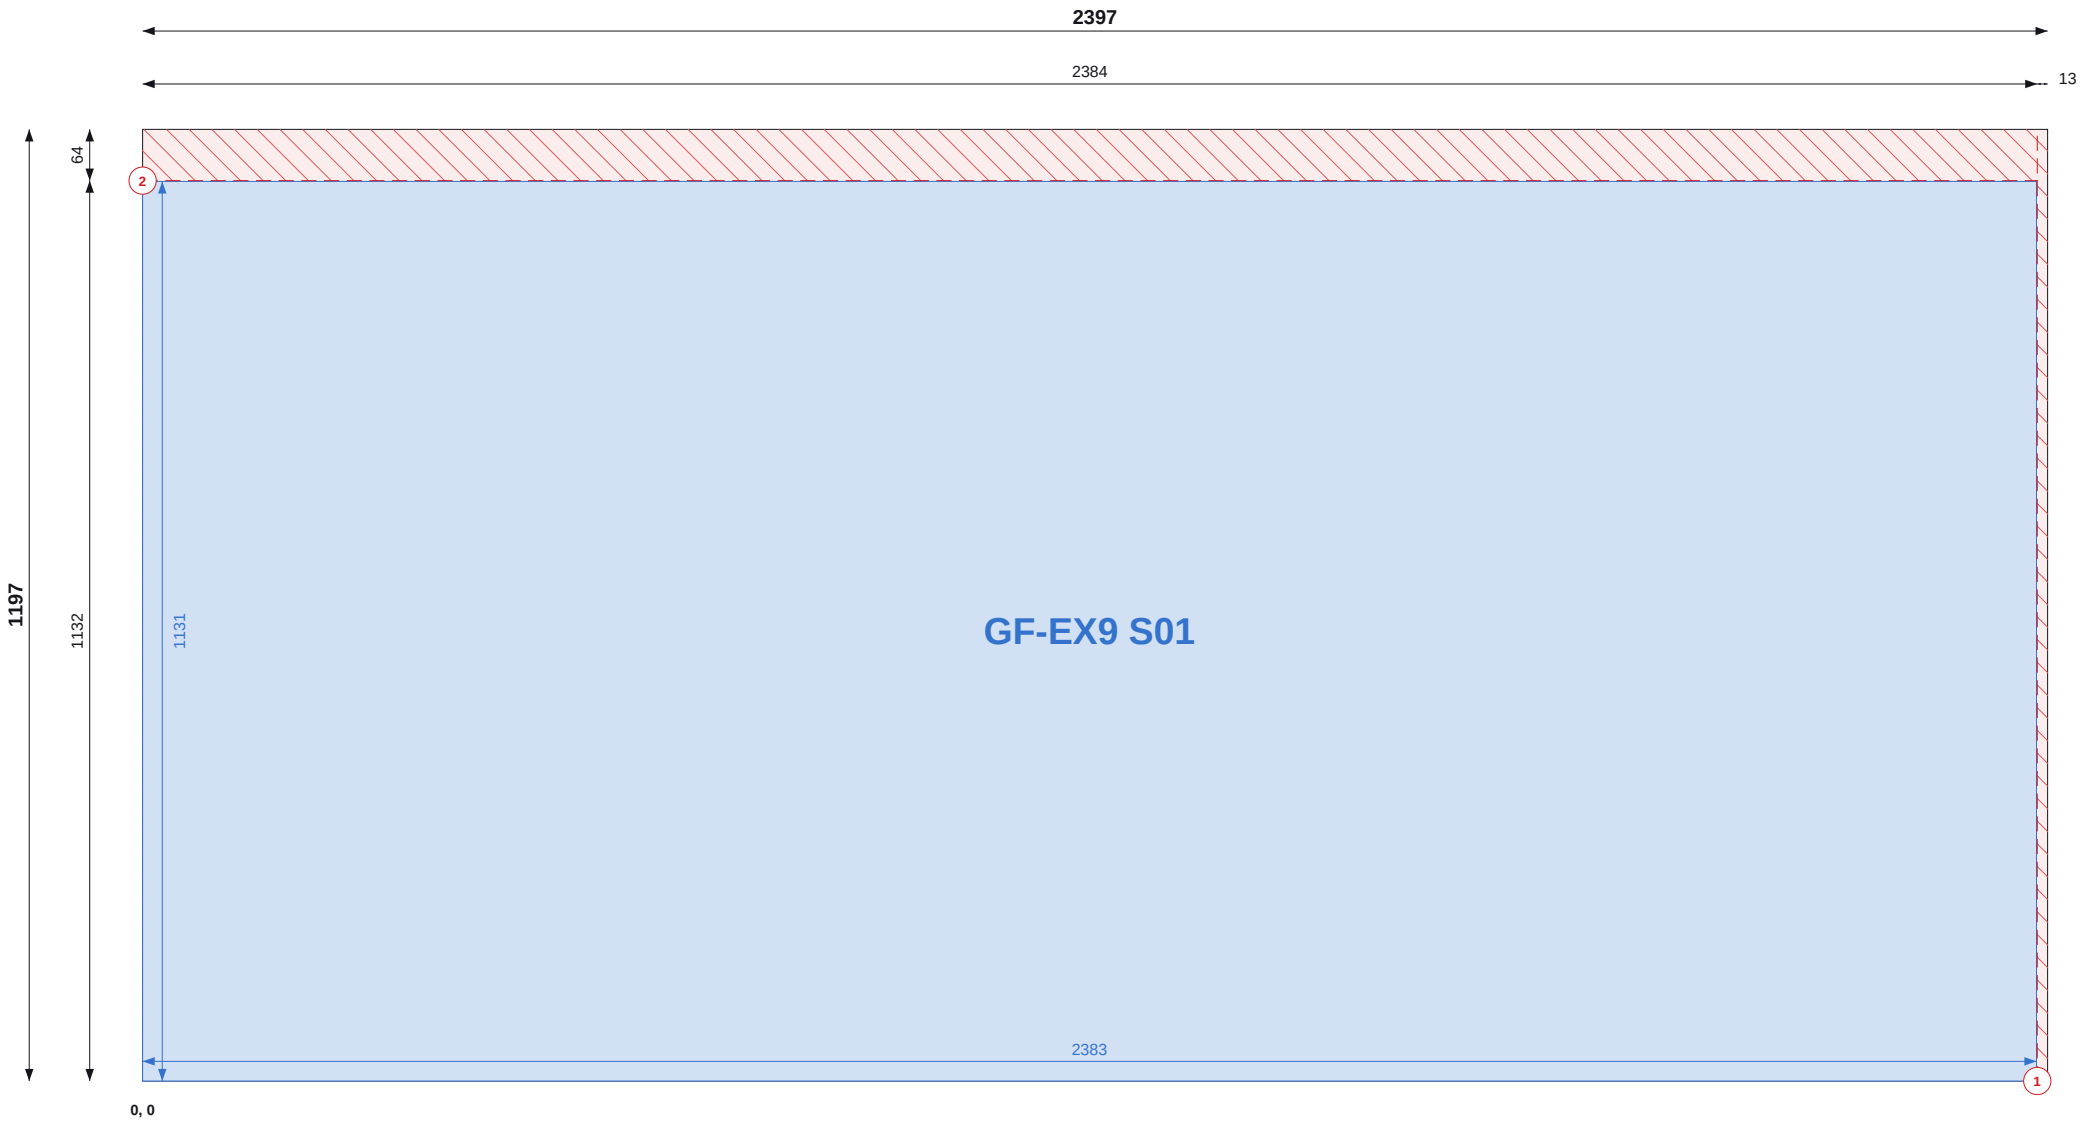

Top / left chains = saw cut positions (to cut centres). Coloured = part size and position.

SHEET 6 OF 38

THIS SHEET

Item	Value
Parts	1
Used / waste	94.0% / 0.17 m2
Reusable offcuts	0
Saw cuts / shared	2 / 0

PIECES (POSITION = BOTTOM-LEFT CORNER)

Label	Size	X, Y
GF-EX9 S01	1131 x 2383	0, 0

NOTES

1. Cut from OSB/3 9mm 1197x2397, 2mm saw kerf. Viewed on the face; dimensions from the sheet's bottom-left corner (0,0). Red numbered lines = saw cuts in order, each edge to edge.
2. Coloured dimensions belong to the part of that colour: its width and height, and its position from the sheet edges. Raked parts: corner coordinates at each corner.
3. Red hatch = waste. Labels = panel + piece mark on the manufacture drawing.

REVISIONS

REV	DATE	DESCRIPTION
C01	13.09.26	Construction issue



TLS TIMBER FRAME

Design & Manufacture

Scan: 3D model + drawings




CLIENT	PROJECT
MP Adams	MP Adams Plot 3, Eckington

DRAWING TITLE			
OSB CUTTING - GROUND FLOOR - SHEET 6 OF 38			
OSB/3 9mm 1197x2397 Ground Floor			

SCALE	SIZE	DATE	DRAWN
NTS	A3	13.09.26	TS

STATUS	DRAWING No.	REV
CONSTRUCTION	P3-CP-OSB-01 / 06	C01

Do not scale. All dimensions in mm. Check all dimensions on site.

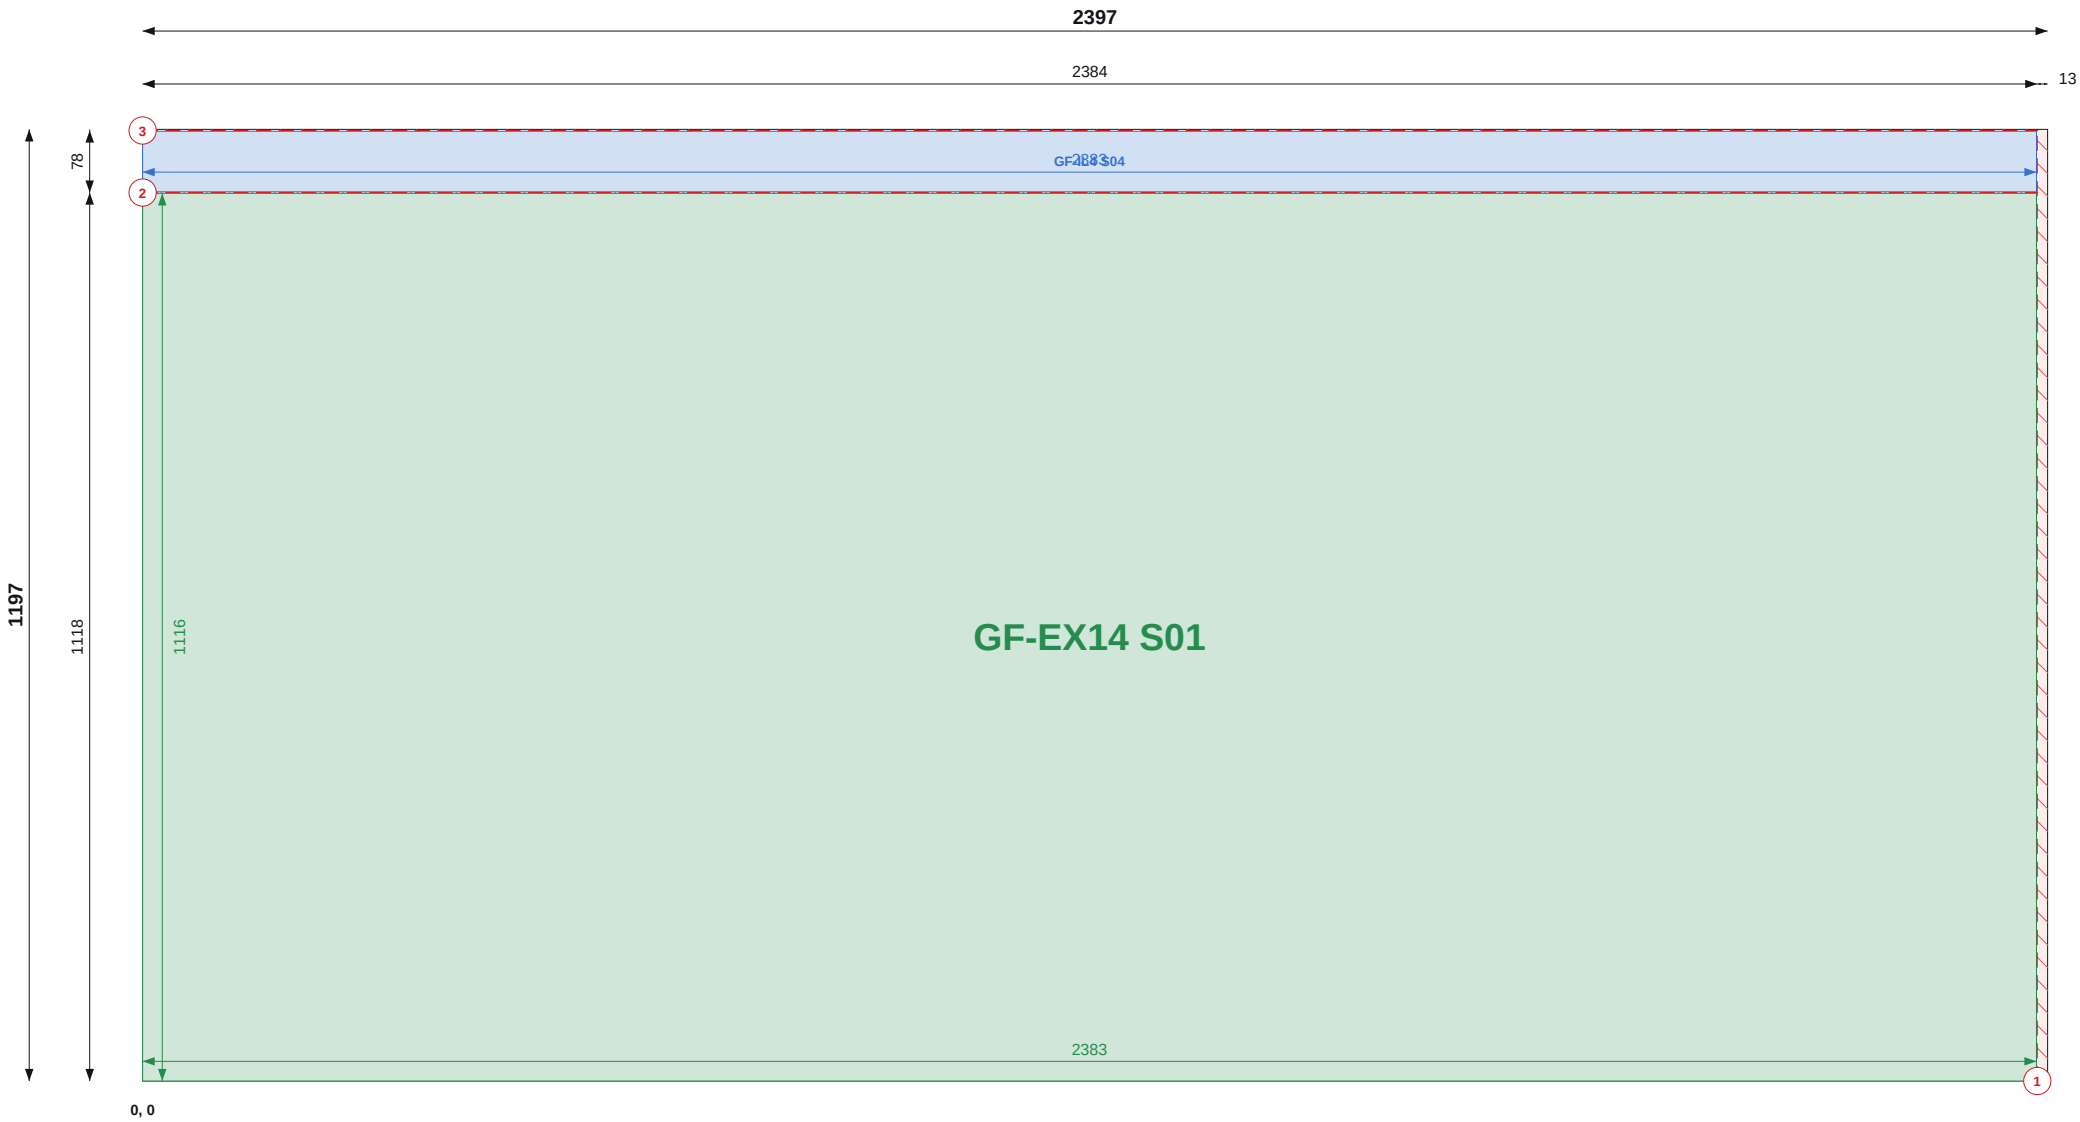

Top / left chains = saw cut positions (to cut centres). Coloured = part size and position.

SHEET 7 OF 38

THIS SHEET

Item	Value
Parts	2
Used / waste	99.0% / 0.03 m2
Reusable offcuts	0
Saw cuts / shared	3 / 1

PIECES (POSITION = BOTTOM-LEFT CORNER)

Label	Size	X, Y
GF-IL4 S04	76 x 2383	0, 1118
GF-EX14 S01	1116 x 2383	0, 0

NOTES

- Cut from OSB/3 9mm 1197x2397, 2mm saw kerf. Viewed on the face; dimensions from the sheet's bottom-left corner (0,0). Red numbered lines = saw cuts in order, each edge to edge.
- Coloured dimensions belong to the part of that colour: its width and height, and its position from the sheet edges. Raked parts: corner coordinates at each corner.
- Red hatch = waste. Labels = panel + piece mark on the manufacture drawing.

REVISIONS

REV	DATE	DESCRIPTION
C01	13.09.26	Construction issue



TLS TIMBER FRAME
Design & Manufacture
Scan: 3D model + drawings



CLIENT MP Adams	PROJECT MP Adams Plot 3, Eckington
--------------------	---------------------------------------


DRAWING TITLE
OSB CUTTING - GROUND FLOOR - SHEET 7 OF 38

OSB/3 9mm 1197x2397 | Ground Floor

SCALE NTS	SIZE A3	DATE 13.09.26	DRAWN TS
--------------	------------	------------------	-------------

STATUS CONSTRUCTION	DRAWING No. P3-CP-OSB-01 / 07	REV C01
-------------------------------	---	-------------------

Do not scale. All dimensions in mm. Check all dimensions on site.

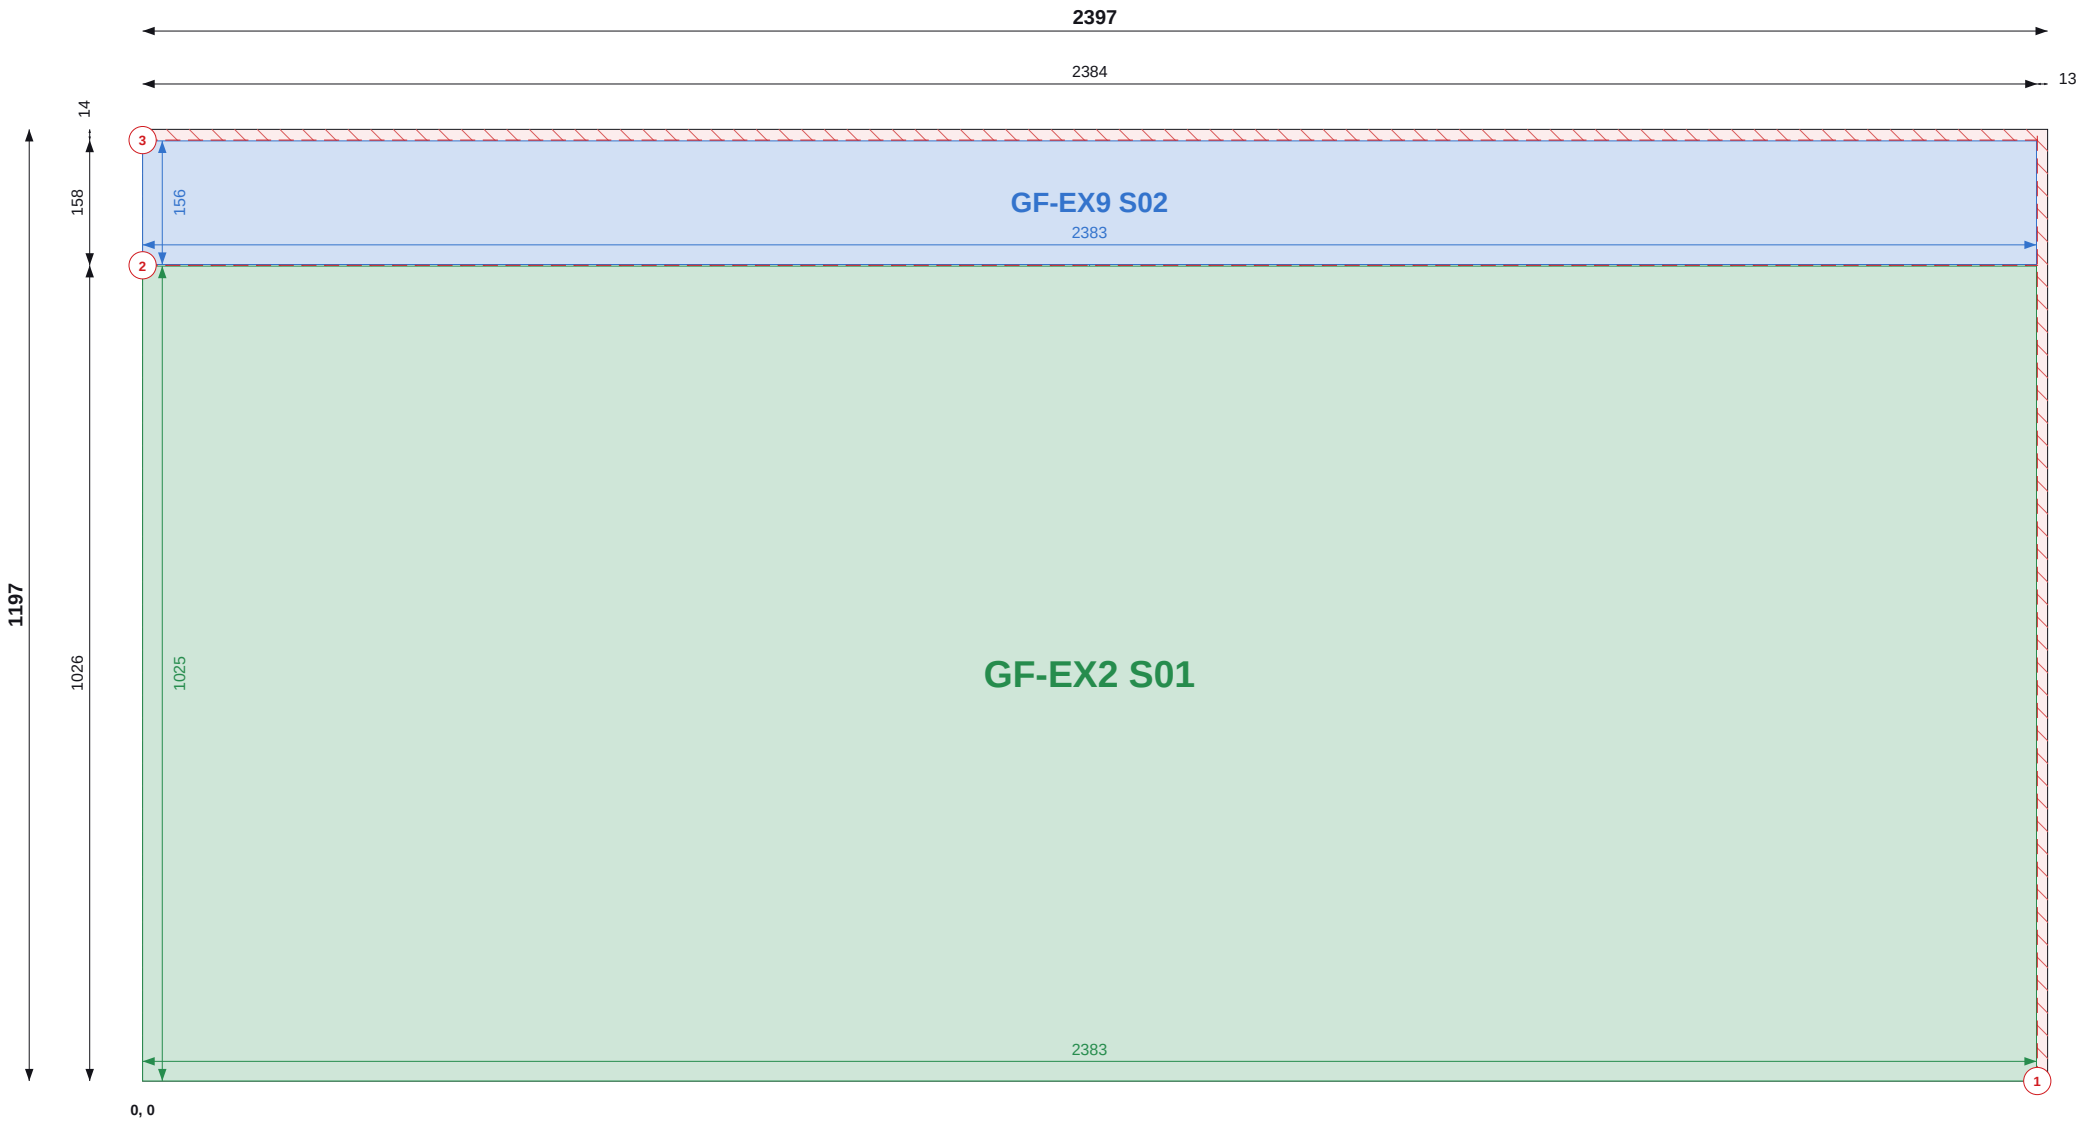

Top / left chains = saw cut positions (to cut centres). Coloured = part size and position.

SHEET 8 OF 38

THIS SHEET

Item	Value
Parts	2
Used / waste	98.0% / 0.06 m2
Reusable offcuts	0
Saw cuts / shared	3 / 1

PIECES (POSITION = BOTTOM-LEFT CORNER)

Label	Size	X, Y
GF-EX9 S02	156 x 2383	0, 1027
GF-EX2 S01	1025 x 2383	0, 0

NOTES

- Cut from OSB/3 9mm 1197x2397, 2mm saw kerf. Viewed on the face; dimensions from the sheet's bottom-left corner (0,0). Red numbered lines = saw cuts in order, each edge to edge.
- Coloured dimensions belong to the part of that colour: its width and height, and its position from the sheet edges. Raked parts: corner coordinates at each corner.
- Red hatch = waste. Labels = panel + piece mark on the manufacture drawing.

REVISIONS

REV	DATE	DESCRIPTION
C01	13.09.26	Construction issue



TLS TIMBER FRAME

Design & Manufacture

Scan: 3D model + drawings



CLIENT	PROJECT
MP Adams	MP Adams Plot 3, Eckington


DRAWING TITLE
OSB CUTTING - GROUND FLOOR - SHEET 8 OF 38

OSB/3 9mm 1197x2397 | Ground Floor

SCALE	SIZE	DATE	DRAWN
NTS	A3	13.09.26	TS

STATUS	DRAWING No.	REV
CONSTRUCTION	P3-CP-OSB-01 / 08	C01

Do not scale. All dimensions in mm. Check all dimensions on site.

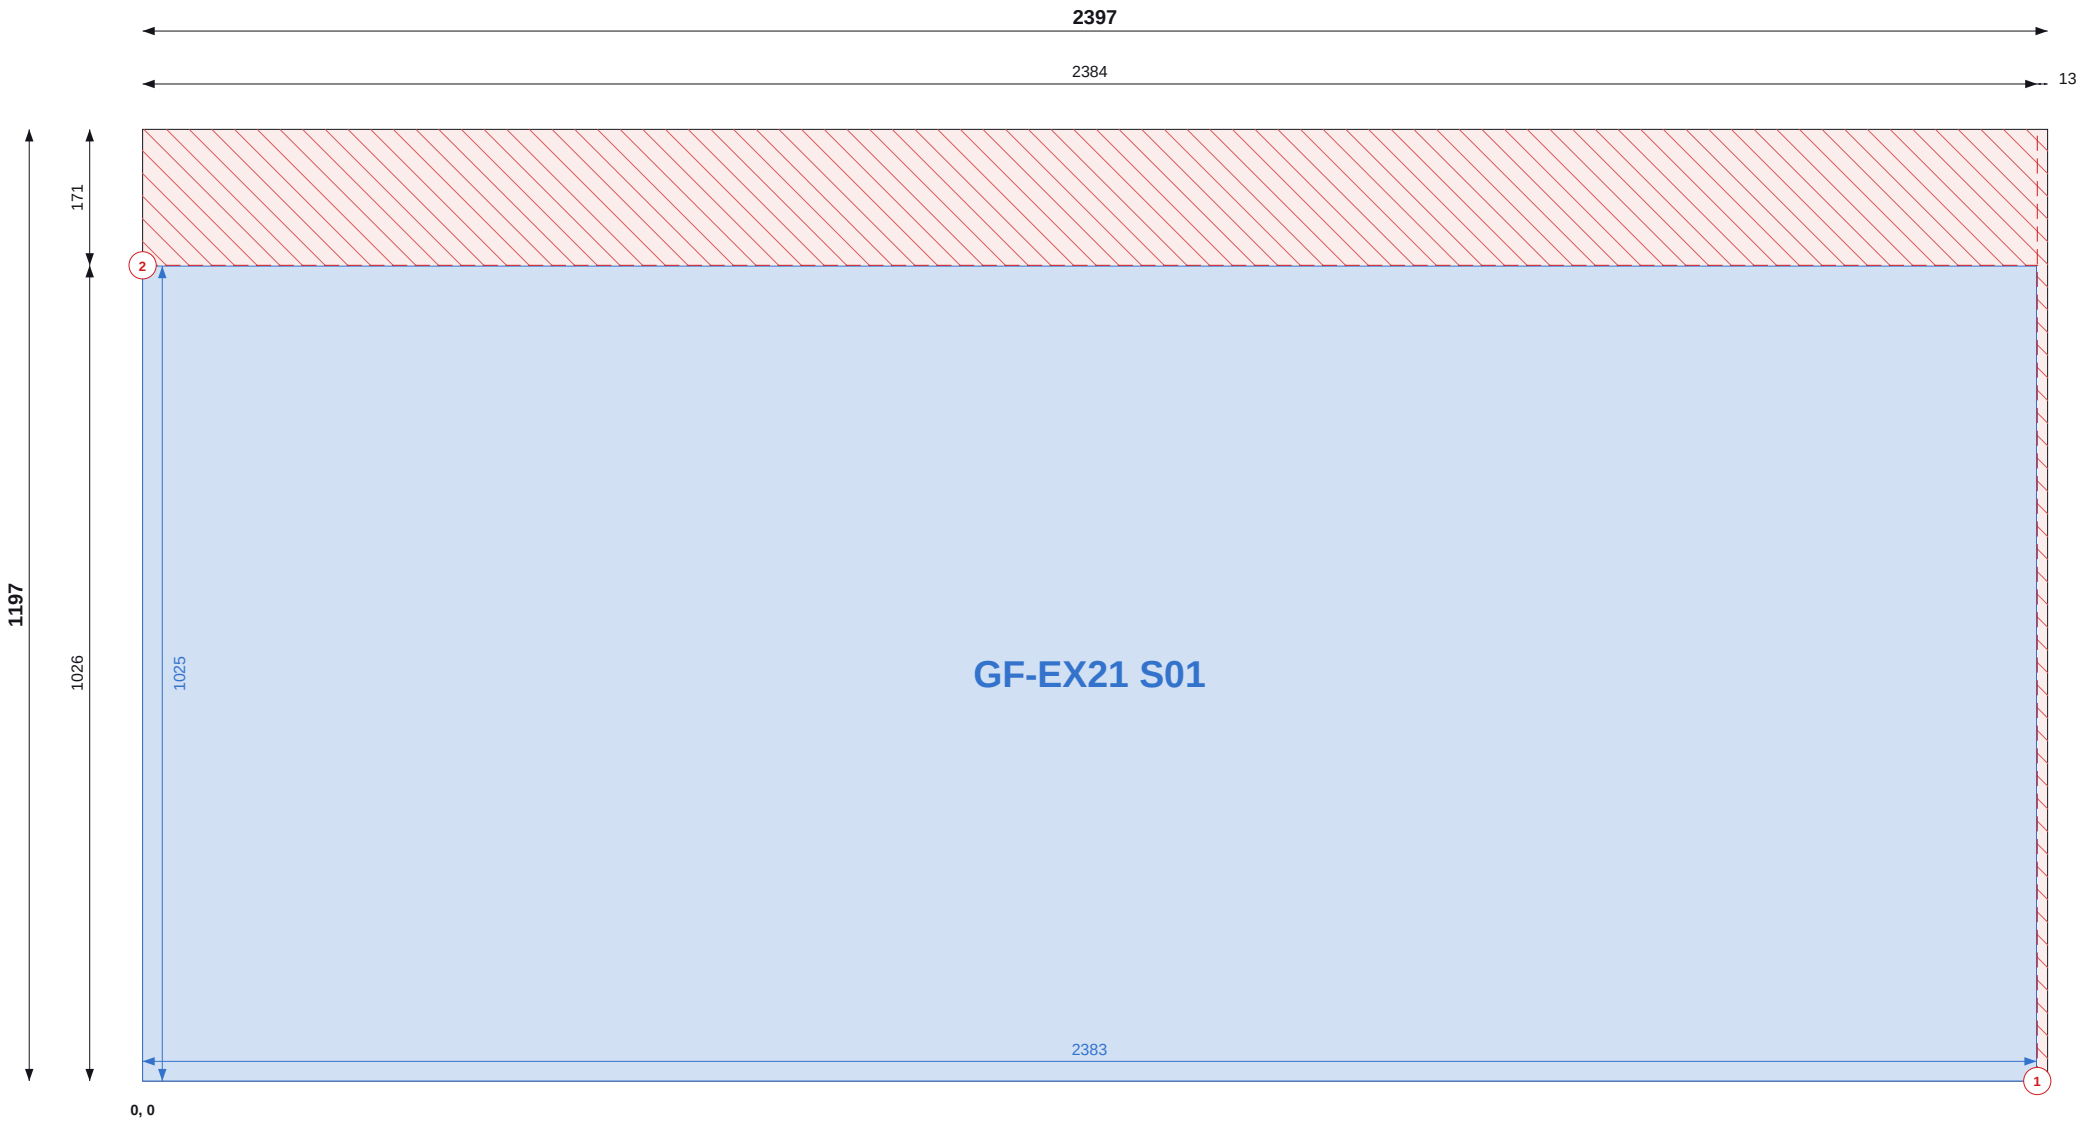

Top / left chains = saw cut positions (to cut centres). Coloured = part size and position.

SHEET 9 OF 38

THIS SHEET

Item	Value
Parts	1
Used / waste	85.1% / 0.43 m2
Reusable offcuts	0
Saw cuts / shared	2 / 0

PIECES (POSITION = BOTTOM-LEFT CORNER)

Label	Size	X, Y
GF-EX21 S01	1025 x 2383	0, 0

NOTES

- Cut from OSB/3 9mm 1197x2397, 2mm saw kerf. Viewed on the face; dimensions from the sheet's bottom-left corner (0,0). Red numbered lines = saw cuts in order, each edge to edge.
- Coloured dimensions belong to the part of that colour: its width and height, and its position from the sheet edges. Raked parts: corner coordinates at each corner.
- Red hatch = waste. Labels = panel + piece mark on the manufacture drawing.

REVISIONS

REV	DATE	DESCRIPTION
C01	13.09.26	Construction issue



TLS TIMBER FRAME

Design & Manufacture

Scan: 3D model + drawings



CLIENT	PROJECT
MP Adams	MP Adams Plot 3, Eckington


DRAWING TITLE
OSB CUTTING - GROUND FLOOR - SHEET 9 OF 38

OSB/3 9mm 1197x2397 | Ground Floor

SCALE	SIZE	DATE	DRAWN
NTS	A3	13.09.26	TS

STATUS	DRAWING No.	REV
CONSTRUCTION	P3-CP-OSB-01 / 09	C01

Do not scale. All dimensions in mm. Check all dimensions on site.

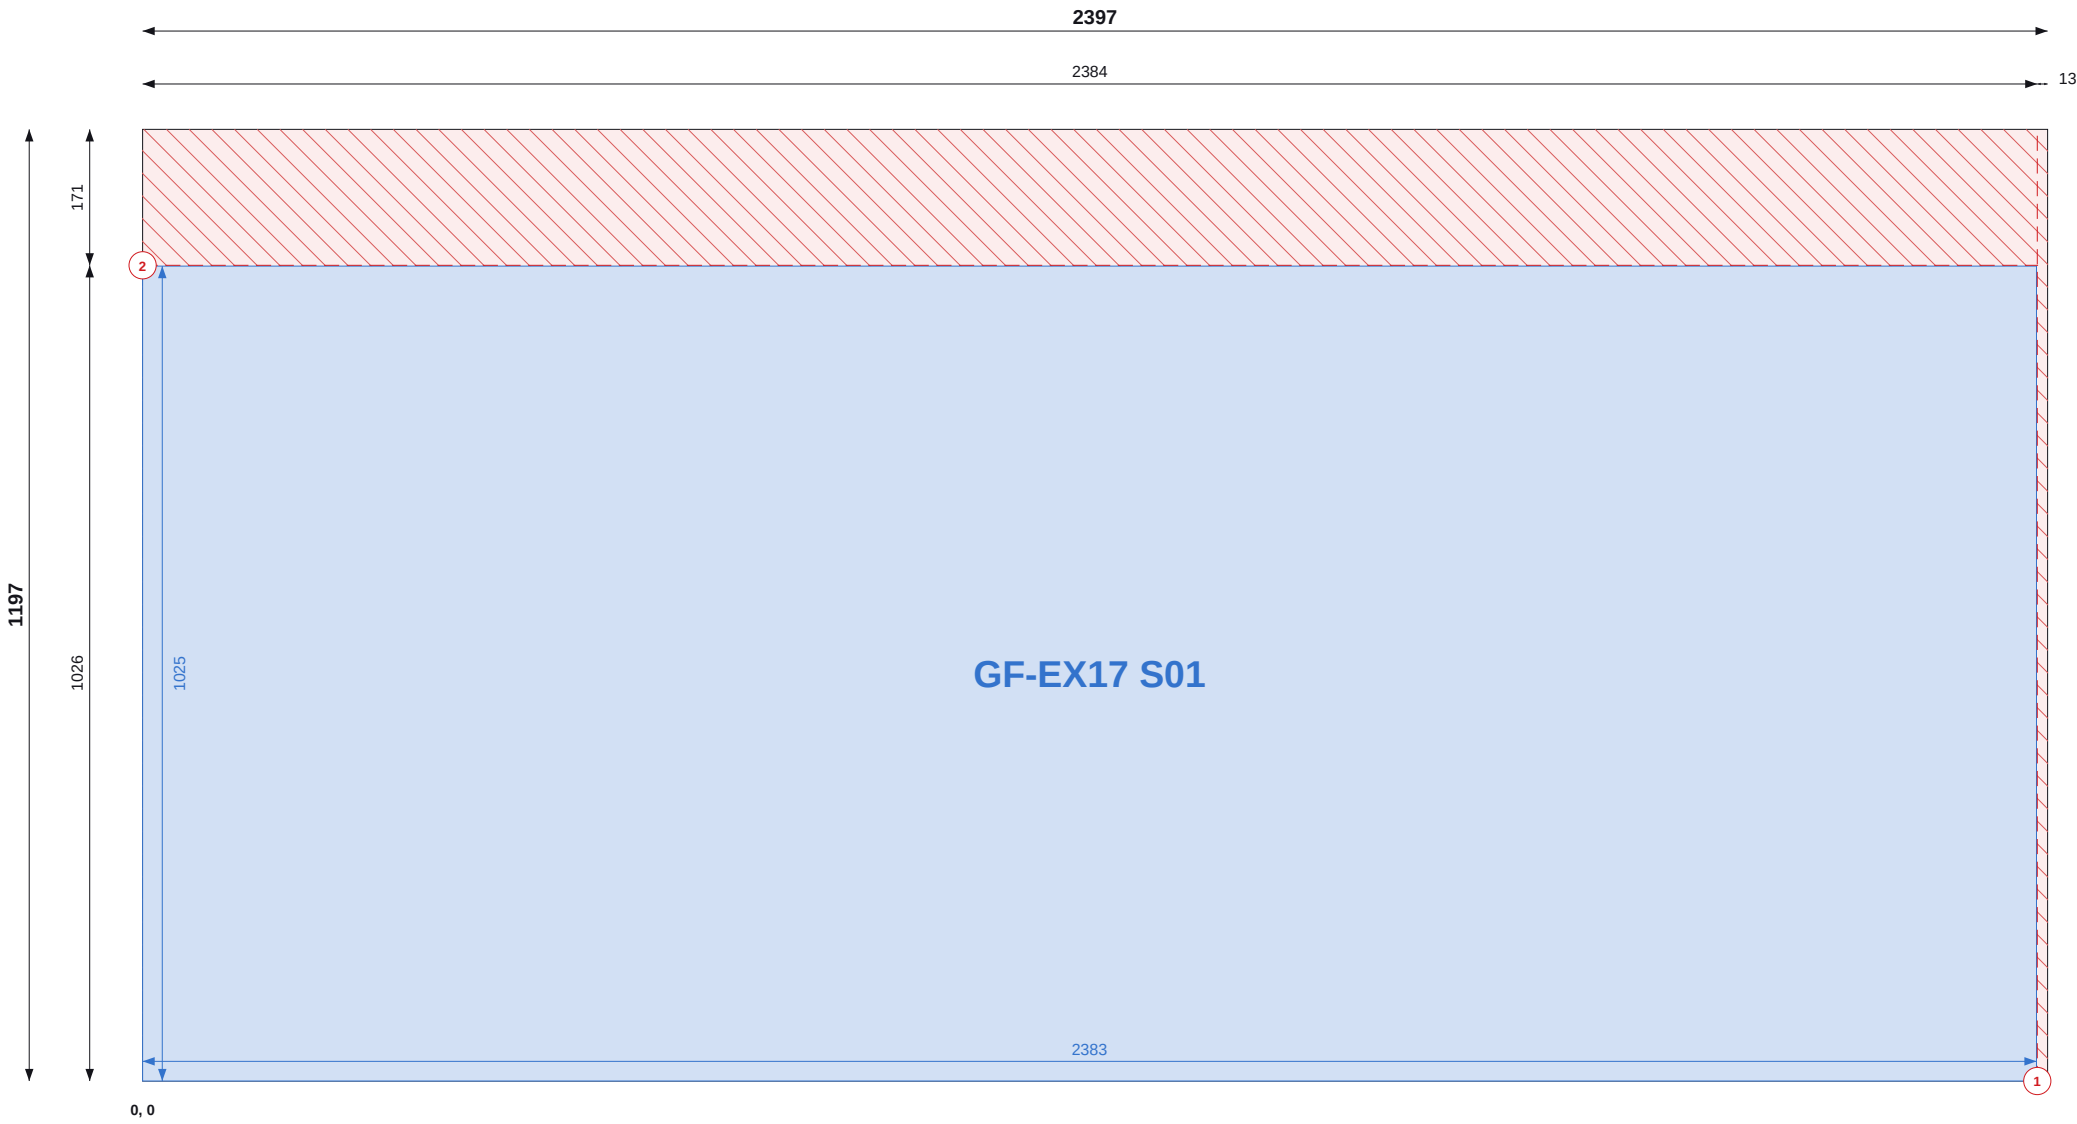

Top / left chains = saw cut positions (to cut centres). Coloured = part size and position.

SHEET 10 OF 38

THIS SHEET

Item	Value
Parts	1
Used / waste	85.1% / 0.43 m2
Reusable offcuts	0
Saw cuts / shared	2 / 0

PIECES (POSITION = BOTTOM-LEFT CORNER)

Label	Size	X, Y
GF-EX17 S01	1025 x 2383	0, 0

NOTES

- Cut from OSB/3 9mm 1197x2397, 2mm saw kerf. Viewed on the face; dimensions from the sheet's bottom-left corner (0,0). Red numbered lines = saw cuts in order, each edge to edge.
- Coloured dimensions belong to the part of that colour: its width and height, and its position from the sheet edges. Raked parts: corner coordinates at each corner.
- Red hatch = waste. Labels = panel + piece mark on the manufacture drawing.

REVISIONS

REV	DATE	DESCRIPTION
C01	13.09.26	Construction issue



TLS TIMBER FRAME
Design & Manufacture
Scan: 3D model + drawings



CLIENT MP Adams	PROJECT MP Adams Plot 3, Eckington
--------------------	---------------------------------------


DRAWING TITLE
OSB CUTTING - GROUND FLOOR - SHEET 10 OF 38

OSB/3 9mm 1197x2397 | Ground Floor

SCALE NTS	SIZE A3	DATE 13.09.26	DRAWN TS
--------------	------------	------------------	-------------

STATUS CONSTRUCTION	DRAWING No. P3-CP-OSB-01 / 10	REV C01
------------------------	----------------------------------	------------

Do not scale. All dimensions in mm. Check all dimensions on site.

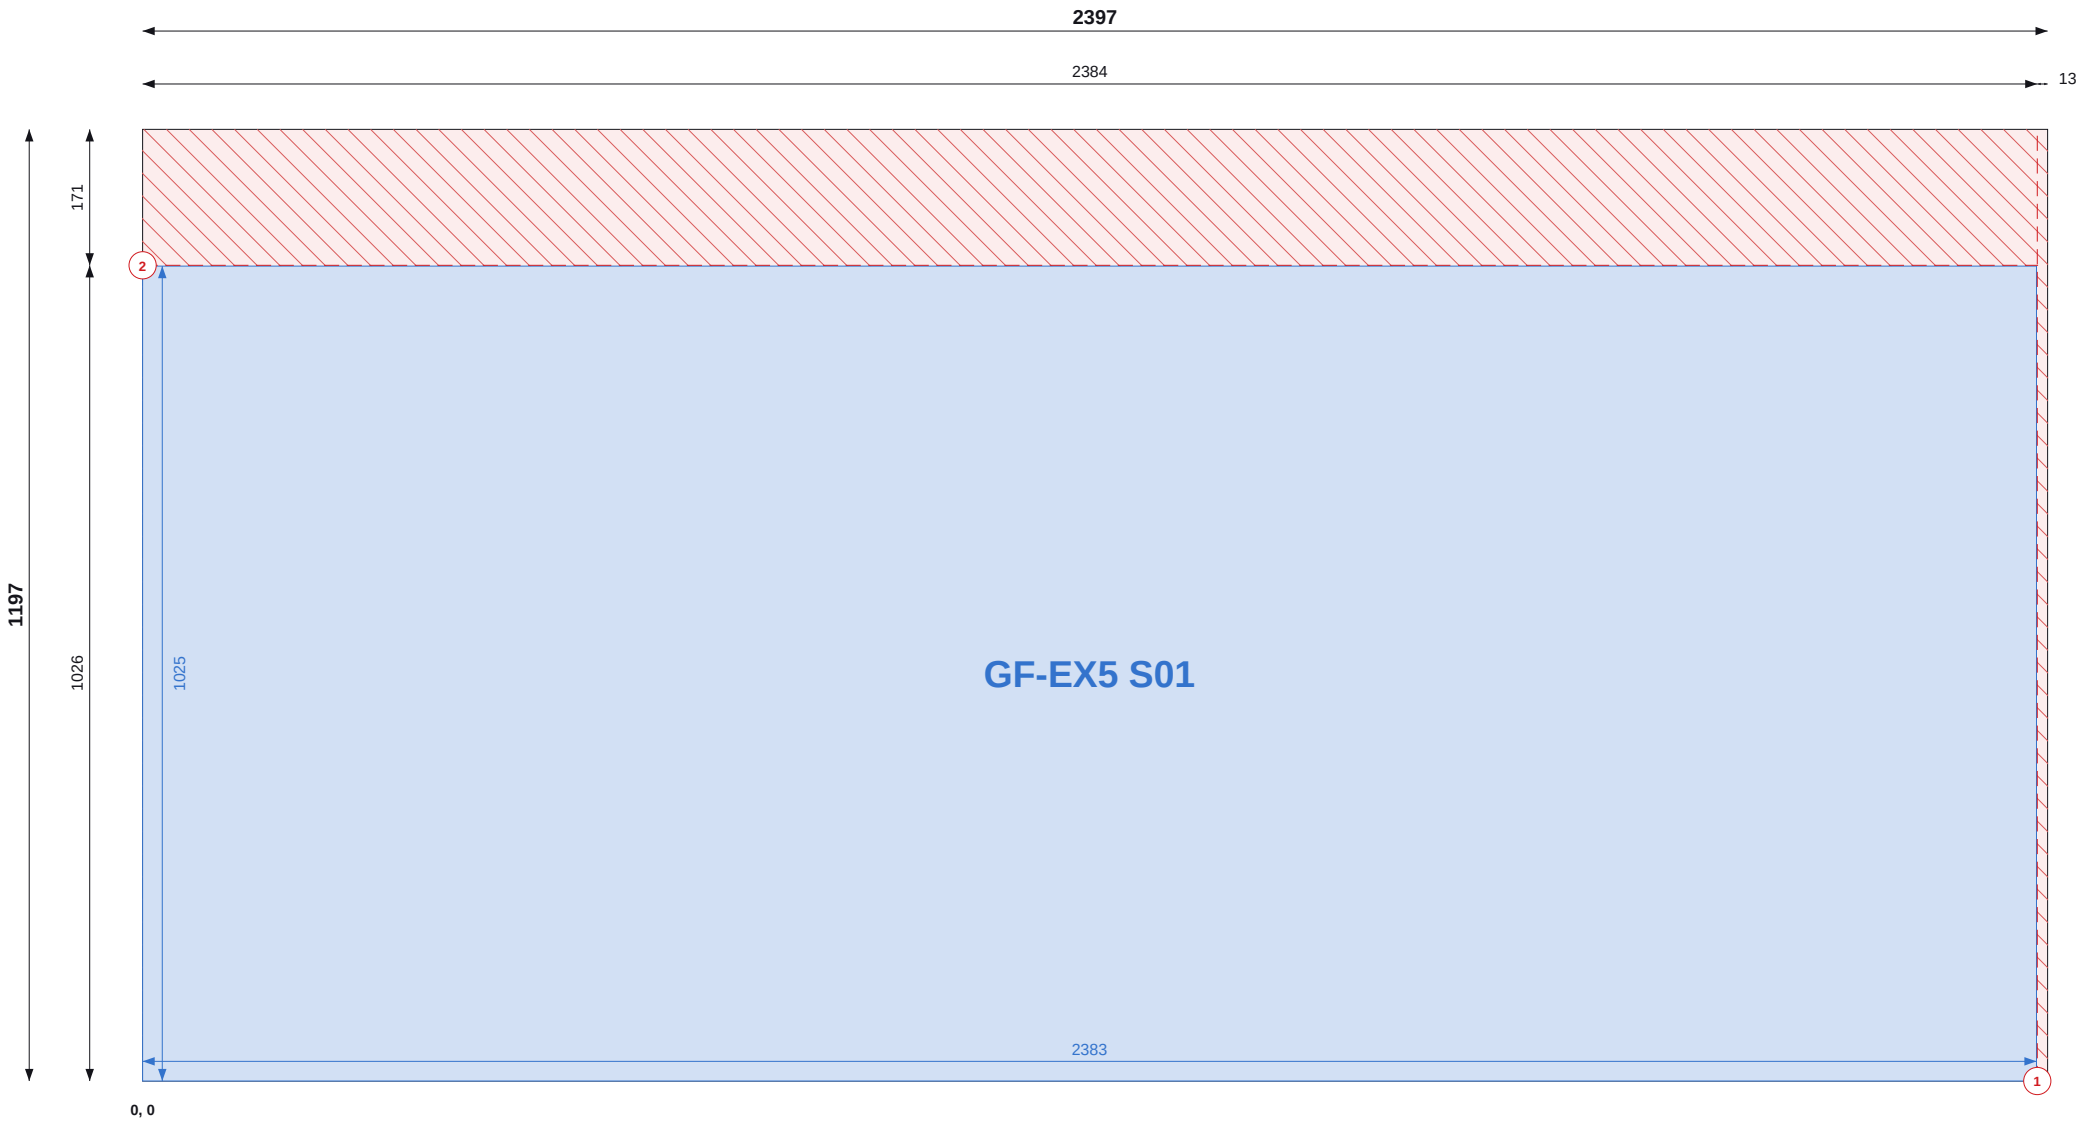

Top / left chains = saw cut positions (to cut centres). Coloured = part size and position.

SHEET 11 OF 38

THIS SHEET

Item	Value
Parts	1
Used / waste	85.1% / 0.43 m2
Reusable offcuts	0
Saw cuts / shared	2 / 0

PIECES (POSITION = BOTTOM-LEFT CORNER)

Label	Size	X, Y
GF-EX5 S01	1025 x 2383	0, 0

NOTES

- Cut from OSB/3 9mm 1197x2397, 2mm saw kerf. Viewed on the face; dimensions from the sheet's bottom-left corner (0,0). Red numbered lines = saw cuts in order, each edge to edge.
- Coloured dimensions belong to the part of that colour: its width and height, and its position from the sheet edges. Raked parts: corner coordinates at each corner.
- Red hatch = waste. Labels = panel + piece mark on the manufacture drawing.

REVISIONS

REV	DATE	DESCRIPTION
C01	13.09.26	Construction issue



TLS TIMBER FRAME

Design & Manufacture

Scan: 3D model + drawings




CLIENT	PROJECT
MP Adams	MP Adams Plot 3, Eckington

DRAWING TITLE			
OSB CUTTING - GROUND FLOOR - SHEET 11 OF 38			
OSB/3 9mm 1197x2397 Ground Floor			

SCALE	SIZE	DATE	DRAWN
NTS	A3	13.09.26	TS

STATUS	DRAWING No.	REV
CONSTRUCTION	P3-CP-OSB-01 / 11	C01

Do not scale. All dimensions in mm. Check all dimensions on site.

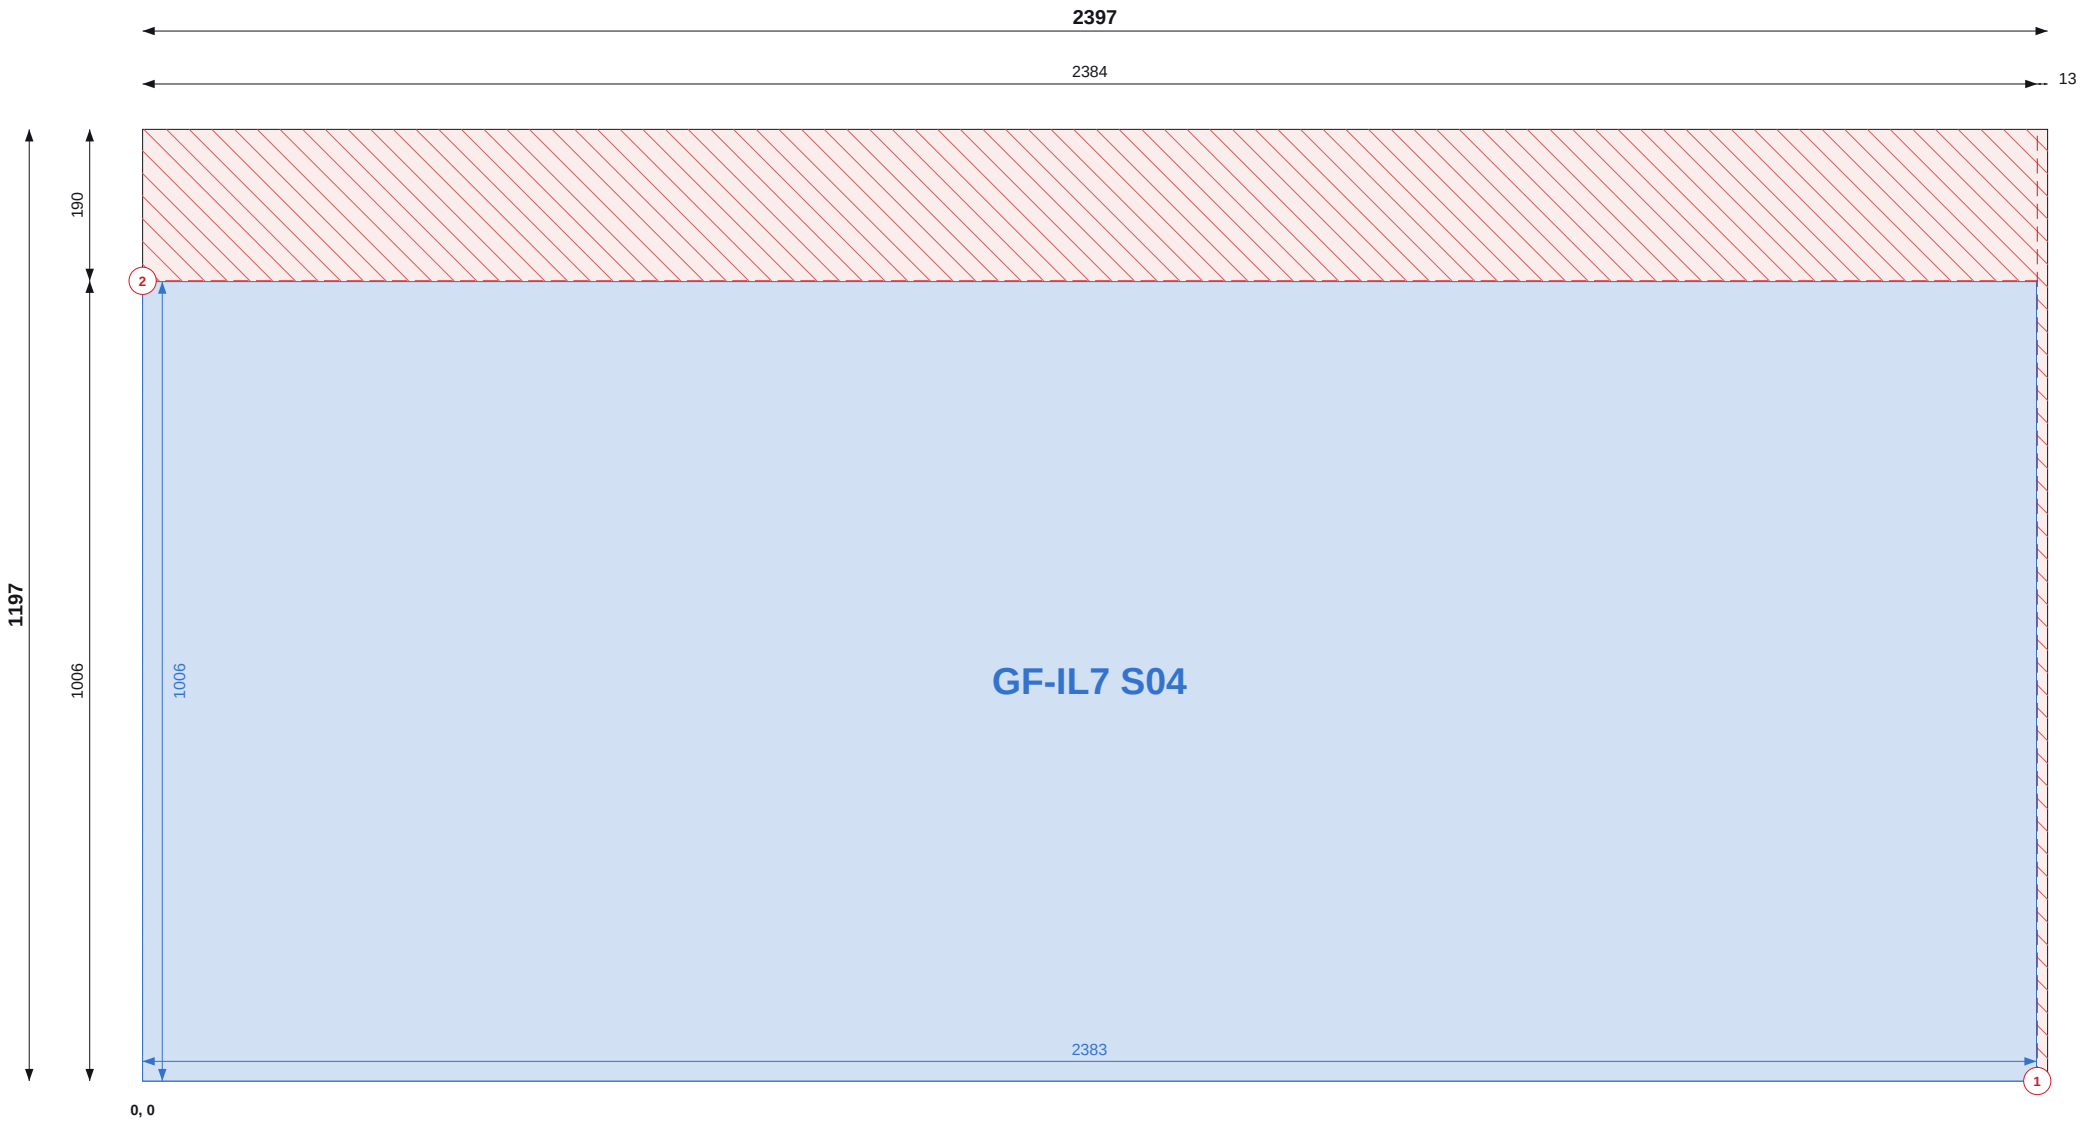

Top / left chains = saw cut positions (to cut centres). Coloured = part size and position.

SHEET 12 OF 38

THIS SHEET

Item	Value
Parts	1
Used / waste	83.5% / 0.47 m2
Reusable offcuts	0
Saw cuts / shared	2 / 0

PIECES (POSITION = BOTTOM-LEFT CORNER)

Label	Size	X, Y
GF-IL7 S04	1006 x 2383	0, 0

NOTES

- Cut from OSB/3 9mm 1197x2397, 2mm saw kerf. Viewed on the face; dimensions from the sheet's bottom-left corner (0,0). Red numbered lines = saw cuts in order, each edge to edge.
- Coloured dimensions belong to the part of that colour: its width and height, and its position from the sheet edges. Raked parts: corner coordinates at each corner.
- Red hatch = waste. Labels = panel + piece mark on the manufacture drawing.

REVISIONS

REV	DATE	DESCRIPTION
C01	13.09.26	Construction issue



TLS TIMBER FRAME

Design & Manufacture

Scan: 3D model + drawings



CLIENT	PROJECT
MP Adams	MP Adams Plot 3, Eckington


DRAWING TITLE
OSB CUTTING - GROUND FLOOR - SHEET 12 OF 38

OSB/3 9mm 1197x2397 | Ground Floor

SCALE	SIZE	DATE	DRAWN
NTS	A3	13.09.26	TS

STATUS	DRAWING No.	REV
CONSTRUCTION	P3-CP-OSB-01 / 12	C01

Do not scale. All dimensions in mm. Check all dimensions on site.

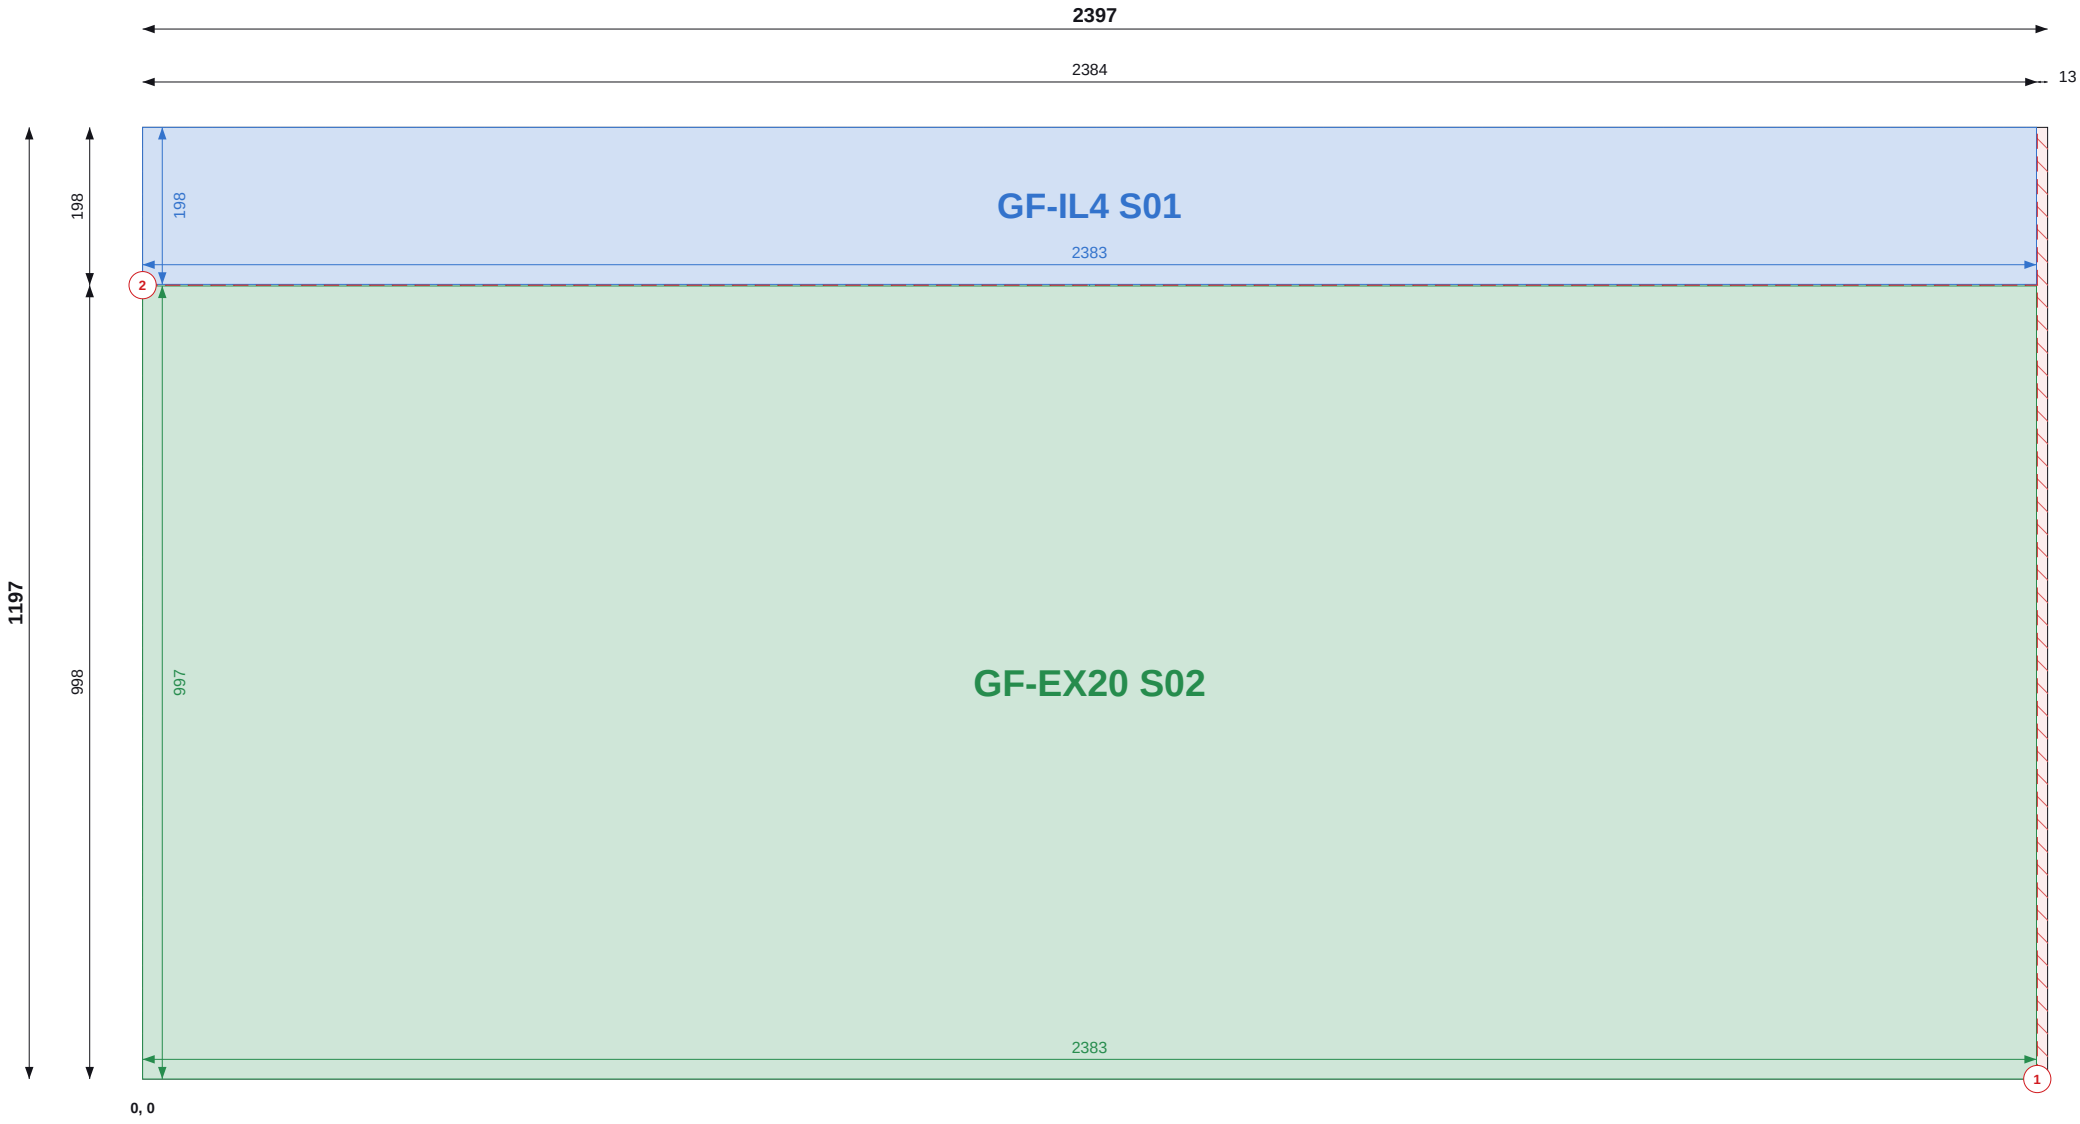

Top / left chains = saw cut positions (to cut centres). Coloured = part size and position.

SHEET 13 OF 38

THIS SHEET

Item	Value
Parts	2
Used / waste	99.2% / 0.02 m2
Reusable offcuts	0
Saw cuts / shared	2 / 1

PIECES (POSITION = BOTTOM-LEFT CORNER)

Label	Size	X, Y
GF-IL4 S01	198 x 2383	0, 999
GF-EX20 S02	997 x 2383	0, 0

NOTES

- Cut from OSB/3 9mm 1197x2397, 2mm saw kerf. Viewed on the face; dimensions from the sheet's bottom-left corner (0,0). Red numbered lines = saw cuts in order, each edge to edge.
- Coloured dimensions belong to the part of that colour: its width and height, and its position from the sheet edges. Raked parts: corner coordinates at each corner.
- Red hatch = waste. Labels = panel + piece mark on the manufacture drawing.

REVISIONS

REV	DATE	DESCRIPTION
C01	13.09.26	Construction issue



TLS TIMBER FRAME

Design & Manufacture

Scan: 3D model + drawings



CLIENT	PROJECT
MP Adams	MP Adams Plot 3, Eckington


DRAWING TITLE
OSB CUTTING - GROUND FLOOR - SHEET 13 OF 38

OSB/3 9mm 1197x2397 | Ground Floor

SCALE	SIZE	DATE	DRAWN
NTS	A3	13.09.26	TS

STATUS	DRAWING No.	REV
CONSTRUCTION	P3-CP-OSB-01 / 13	C01

Do not scale. All dimensions in mm. Check all dimensions on site.

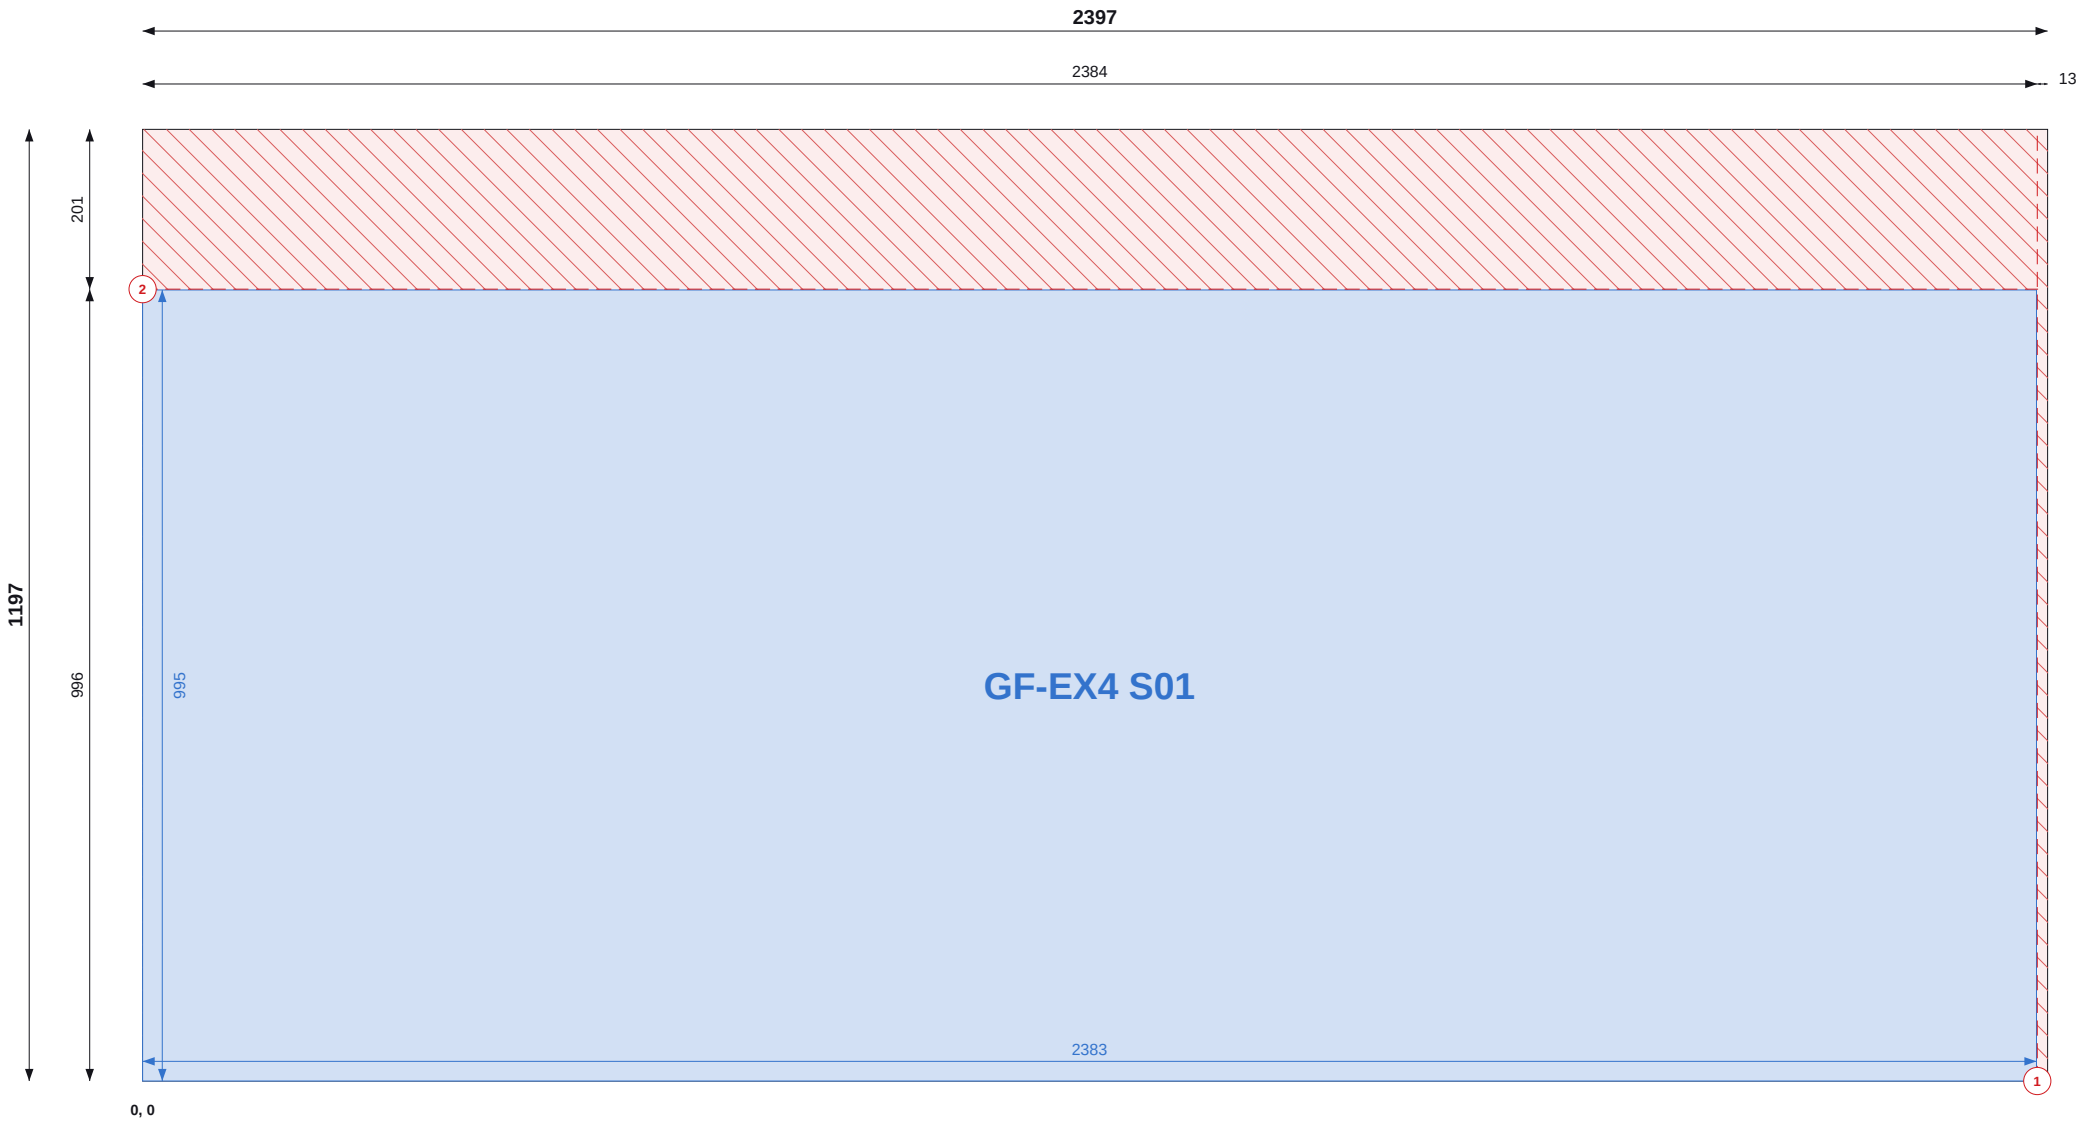

Top / left chains = saw cut positions (to cut centres). Coloured = part size and position.

SHEET 14 OF 38

THIS SHEET

Item	Value
Parts	1
Used / waste	82.6% / 0.50 m2
Reusable offcuts	0
Saw cuts / shared	2 / 0

PIECES (POSITION = BOTTOM-LEFT CORNER)

Label	Size	X, Y
GF-EX4 S01	995 x 2383	0, 0

NOTES

- Cut from OSB/3 9mm 1197x2397, 2mm saw kerf. Viewed on the face; dimensions from the sheet's bottom-left corner (0,0). Red numbered lines = saw cuts in order, each edge to edge.
- Coloured dimensions belong to the part of that colour: its width and height, and its position from the sheet edges. Raked parts: corner coordinates at each corner.
- Red hatch = waste. Labels = panel + piece mark on the manufacture drawing.

REVISIONS

REV	DATE	DESCRIPTION
C01	13.09.26	Construction issue



TLS TIMBER FRAME

Design & Manufacture

Scan: 3D model + drawings



CLIENT	PROJECT
MP Adams	MP Adams Plot 3, Eckington


DRAWING TITLE
OSB CUTTING - GROUND FLOOR - SHEET 14 OF 38

OSB/3 9mm 1197x2397 | Ground Floor

SCALE	SIZE	DATE	DRAWN
NTS	A3	13.09.26	TS

STATUS	DRAWING No.	REV
CONSTRUCTION	P3-CP-OSB-01 / 14	C01

Do not scale. All dimensions in mm. Check all dimensions on site.

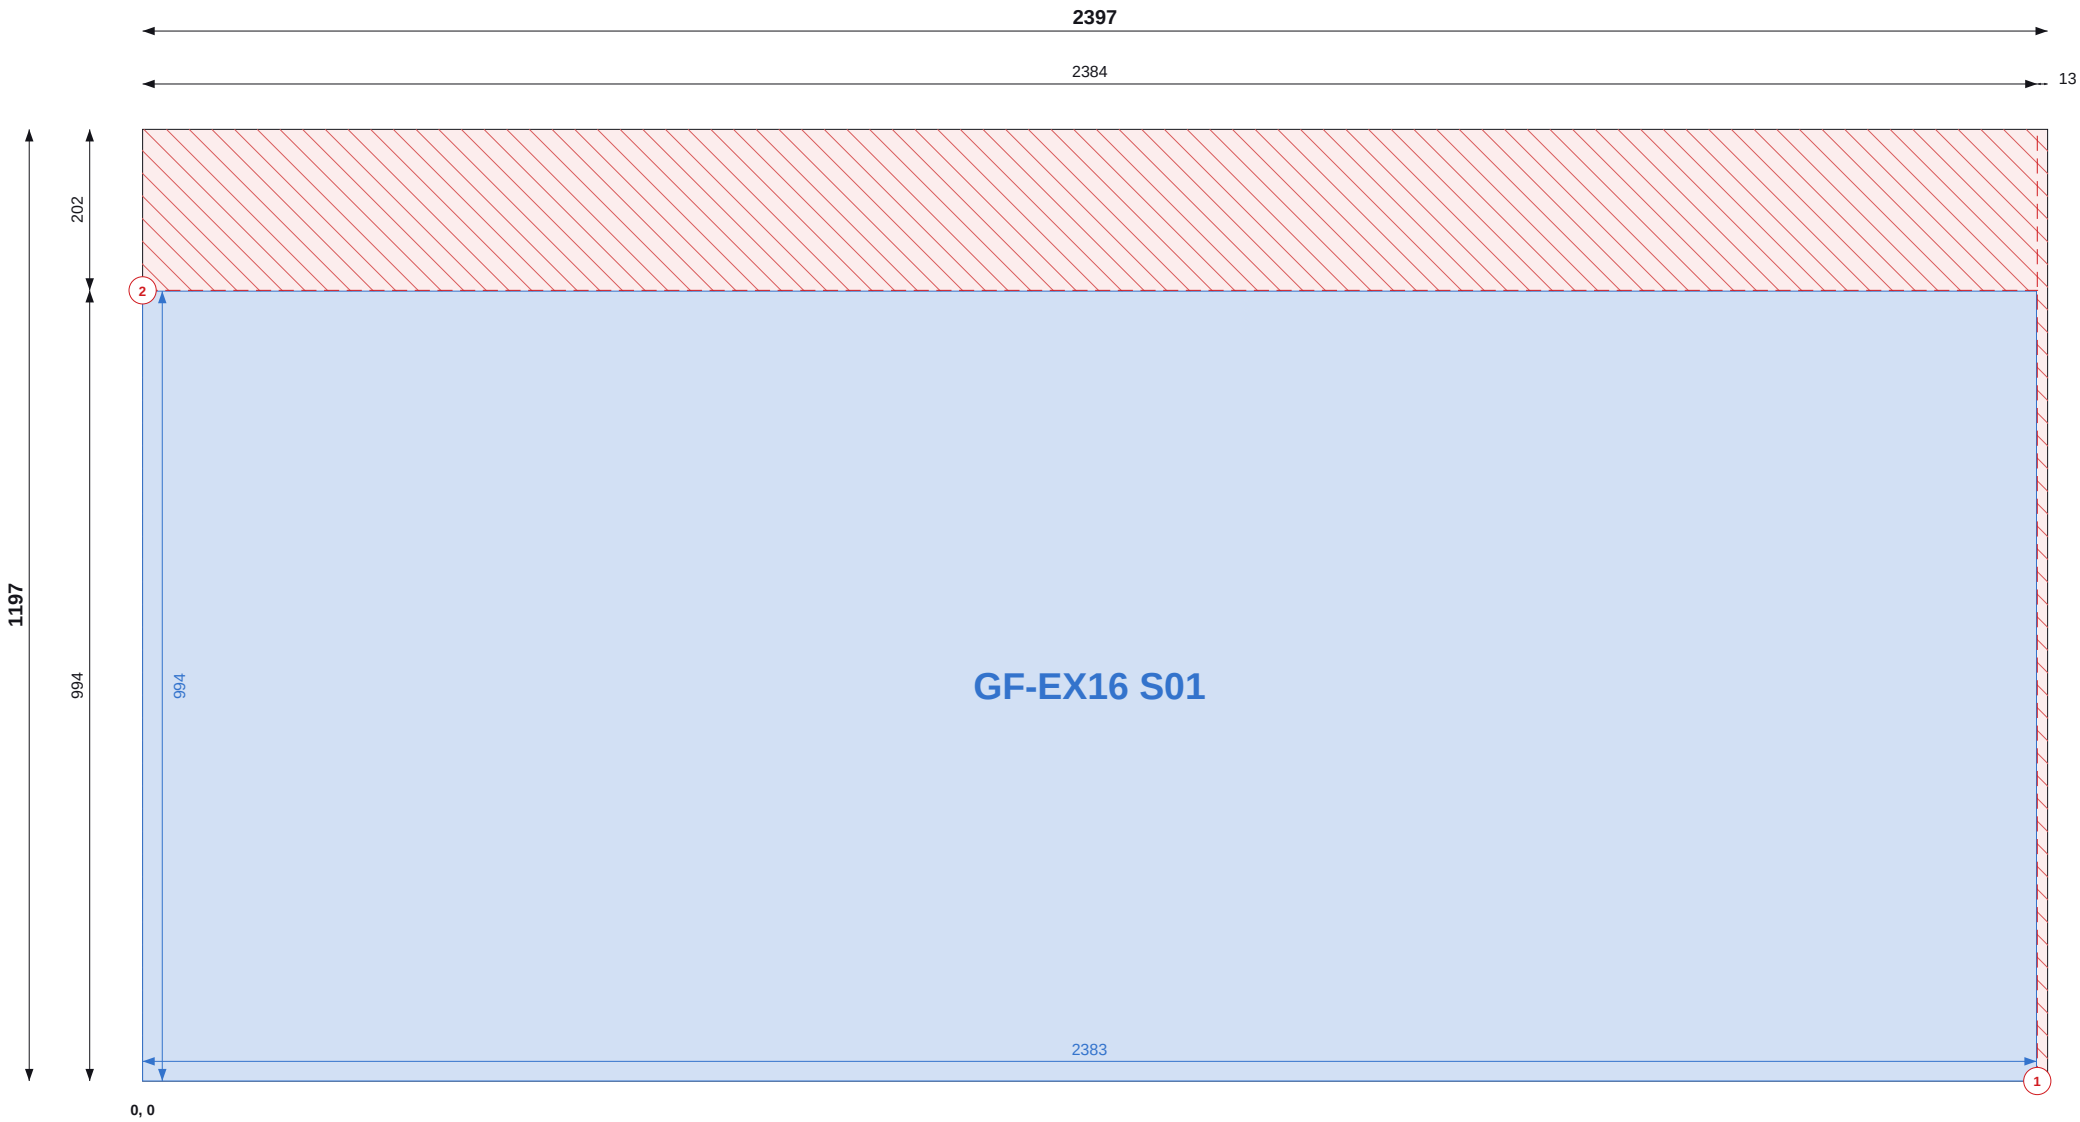

Top / left chains = saw cut positions (to cut centres). Coloured = part size and position.

SHEET 15 OF 38

THIS SHEET

Item	Value
Parts	1
Used / waste	82.5% / 0.50 m2
Reusable offcuts	0
Saw cuts / shared	2 / 0

PIECES (POSITION = BOTTOM-LEFT CORNER)

Label	Size	X, Y
GF-EX16 S01	994 x 2383	0, 0

NOTES

- Cut from OSB/3 9mm 1197x2397, 2mm saw kerf. Viewed on the face; dimensions from the sheet's bottom-left corner (0,0). Red numbered lines = saw cuts in order, each edge to edge.
- Coloured dimensions belong to the part of that colour: its width and height, and its position from the sheet edges. Raked parts: corner coordinates at each corner.
- Red hatch = waste. Labels = panel + piece mark on the manufacture drawing.

REVISIONS

REV	DATE	DESCRIPTION
C01	13.09.26	Construction issue



TLS TIMBER FRAME

Design & Manufacture

Scan: 3D model + drawings



CLIENT	PROJECT
MP Adams	MP Adams Plot 3, Eckington


DRAWING TITLE
OSB CUTTING - GROUND FLOOR - SHEET 15 OF 38

OSB/3 9mm 1197x2397 | Ground Floor

SCALE	SIZE	DATE	DRAWN
NTS	A3	13.09.26	TS

STATUS	DRAWING No.	REV
CONSTRUCTION	P3-CP-OSB-01 / 15	C01

Do not scale. All dimensions in mm. Check all dimensions on site.

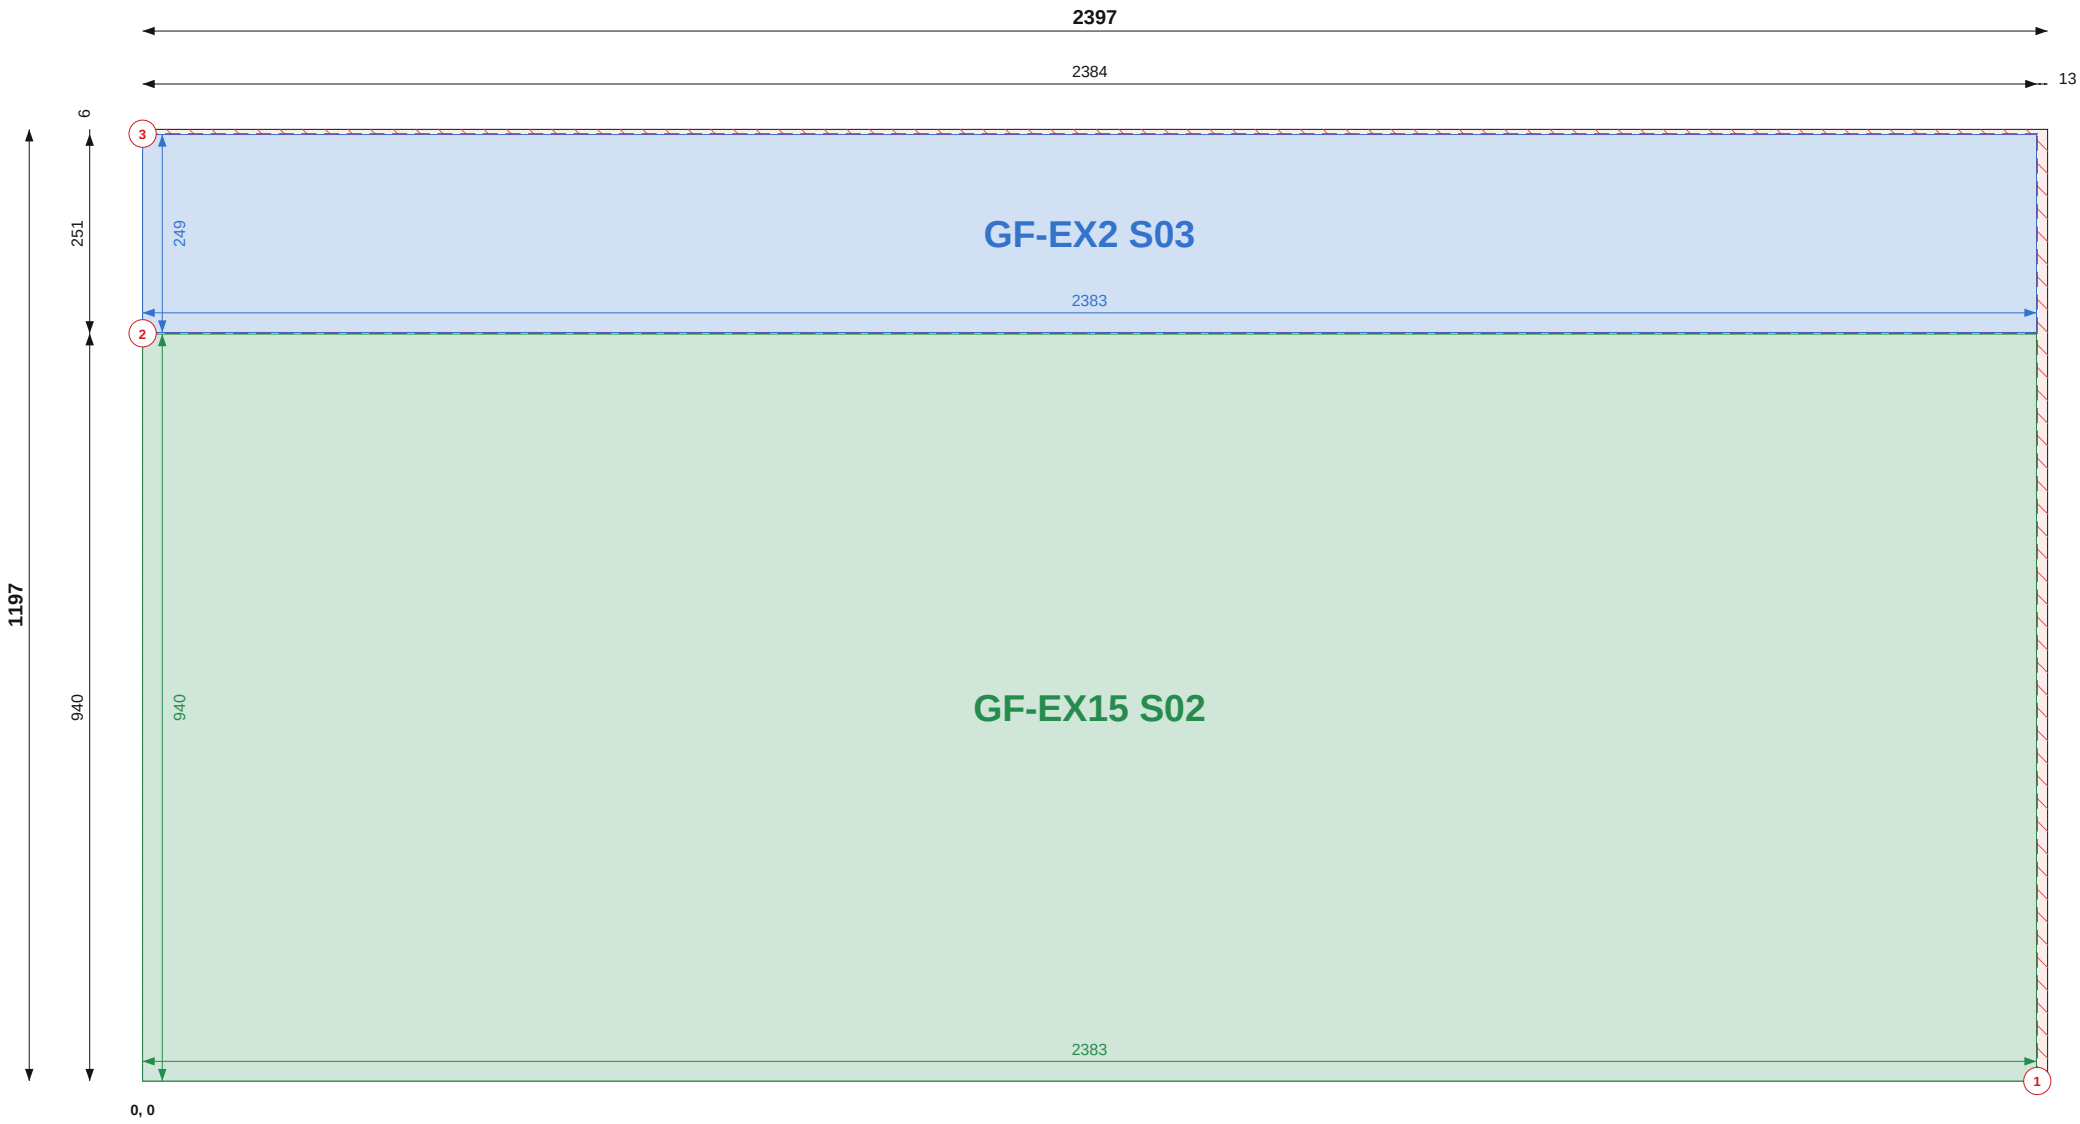

Top / left chains = saw cut positions (to cut centres). Coloured = part size and position.

SHEET 16 OF 38

THIS SHEET

Item	Value
Parts	2
Used / waste	98.7% / 0.04 m2
Reusable offcuts	0
Saw cuts / shared	3 / 1

PIECES (POSITION = BOTTOM-LEFT CORNER)

Label	Size	X, Y
GF-EX2 S03	249 x 2383	0, 942
GF-EX15 S02	940 x 2383	0, 0

NOTES

- Cut from OSB/3 9mm 1197x2397, 2mm saw kerf. Viewed on the face; dimensions from the sheet's bottom-left corner (0,0). Red numbered lines = saw cuts in order, each edge to edge.
- Coloured dimensions belong to the part of that colour: its width and height, and its position from the sheet edges. Raked parts: corner coordinates at each corner.
- Red hatch = waste. Labels = panel + piece mark on the manufacture drawing.

REVISIONS

REV	DATE	DESCRIPTION
C01	13.09.26	Construction issue



TLS TIMBER FRAME

Design & Manufacture

Scan: 3D model + drawings



CLIENT	PROJECT
MP Adams	MP Adams Plot 3, Eckington

DRAWING TITLE			
OSB CUTTING - GROUND FLOOR - SHEET 16 OF 38			
OSB/3 9mm 1197x2397 Ground Floor			

SCALE	SIZE	DATE	DRAWN
NTS	A3	13.09.26	TS

STATUS	DRAWING No.	REV
CONSTRUCTION	P3-CP-OSB-01 / 16	C01

Item	Value
Parts	2
Used / waste	98.3% / 0.05 m2
Reusable offcuts	0
Saw cuts / shared	3 / 1

PIECES (POSITION = BOTTOM-LEFT CORNER)

Label	Size	X, Y
GF-EX10 S03	249 x 2383	0, 936
GF-EX10 S01	934 x 2383	0, 0

NOTES

1. Cut from OSB/3 9mm 1197x2397, 2mm saw kerf. Viewed on the face; dimensions from the sheet's bottom-left corner (0,0). Red numbered lines = saw cuts in order, each edge to edge.
2. Coloured dimensions belong to the part of that colour: its width and height, and its position from the sheet edges. Raked parts: corner coordinates at each corner.
3. Red hatch = waste. Labels = panel + piece mark on the manufacture drawing.

REVISIONS

REV	DATE	DESCRIPTION
C01	13.09.26	Construction issue



TLS TIMBER FRAME

Design & Manufacture

Scan: 3D model + drawings



CLIENT	PROJECT
MP Adams	MP Adams Plot 3, Eckington

DRAWING TITLE

OSB CUTTING - GROUND FLOOR - SHEET 17 OF 38


OSB/3 9mm 1197x2397 | Ground Floor

SCALE	SIZE	DATE	DRAWN
NTS	A3	13.09.26	TS

STATUS CONSTRUCTION	DRAWING No. P3-CP-OSB-01 / 17	REV C01
-----------------------------------	---	-----------------------

Do not scale. All dimensions in mm. Check all dimensions on site.

Do not scale. All dimensions in mm. Check all dimensions on site.

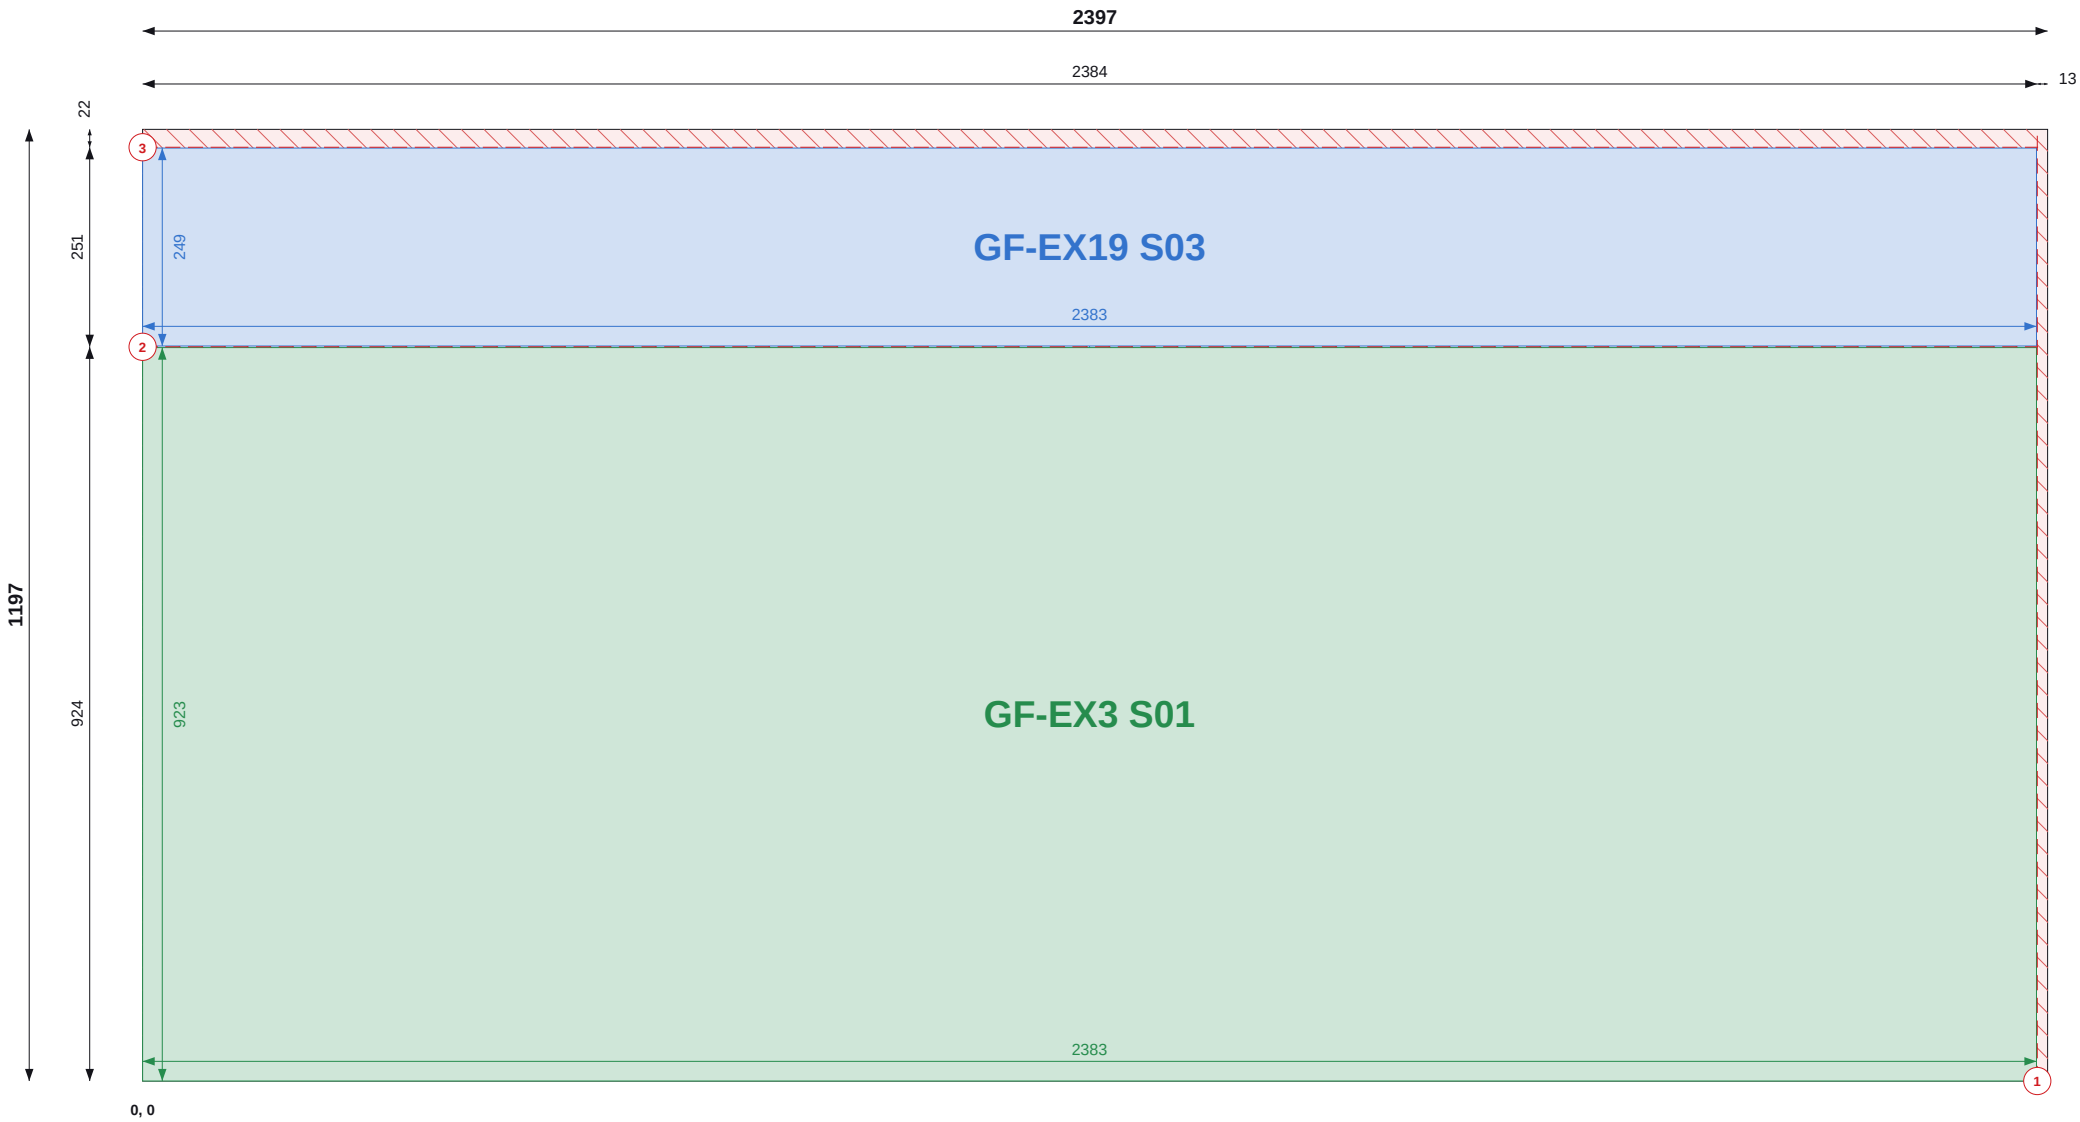

Top / left chains = saw cut positions (to cut centres). Coloured = part size and position.

SHEET 18 OF 38

THIS SHEET

Item	Value
Parts	2
Used / waste	97.3% / 0.08 m2
Reusable offcuts	0
Saw cuts / shared	3 / 1

PIECES (POSITION = BOTTOM-LEFT CORNER)

Label	Size	X, Y
GF-EX19 S03	249 x 2383	0, 925
GF-EX3 S01	923 x 2383	0, 0

NOTES

- Cut from OSB/3 9mm 1197x2397, 2mm saw kerf. Viewed on the face; dimensions from the sheet's bottom-left corner (0,0). Red numbered lines = saw cuts in order, each edge to edge.
- Coloured dimensions belong to the part of that colour: its width and height, and its position from the sheet edges. Raked parts: corner coordinates at each corner.
- Red hatch = waste. Labels = panel + piece mark on the manufacture drawing.

REVISIONS

REV	DATE	DESCRIPTION
C01	13.09.26	Construction issue



TLS TIMBER FRAME

Design & Manufacture

Scan: 3D model + drawings

CLIENT	PROJECT
MP Adams	MP Adams Plot 3, Eckington


DRAWING TITLE
OSB CUTTING - GROUND FLOOR - SHEET 18 OF 38

OSB/3 9mm 1197x2397 | Ground Floor

SCALE	SIZE	DATE	DRAWN
NTS	A3	13.09.26	TS

STATUS	DRAWING No.	REV
CONSTRUCTION	P3-CP-OSB-01 / 18	C01

Do not scale. All dimensions in mm. Check all dimensions on site.

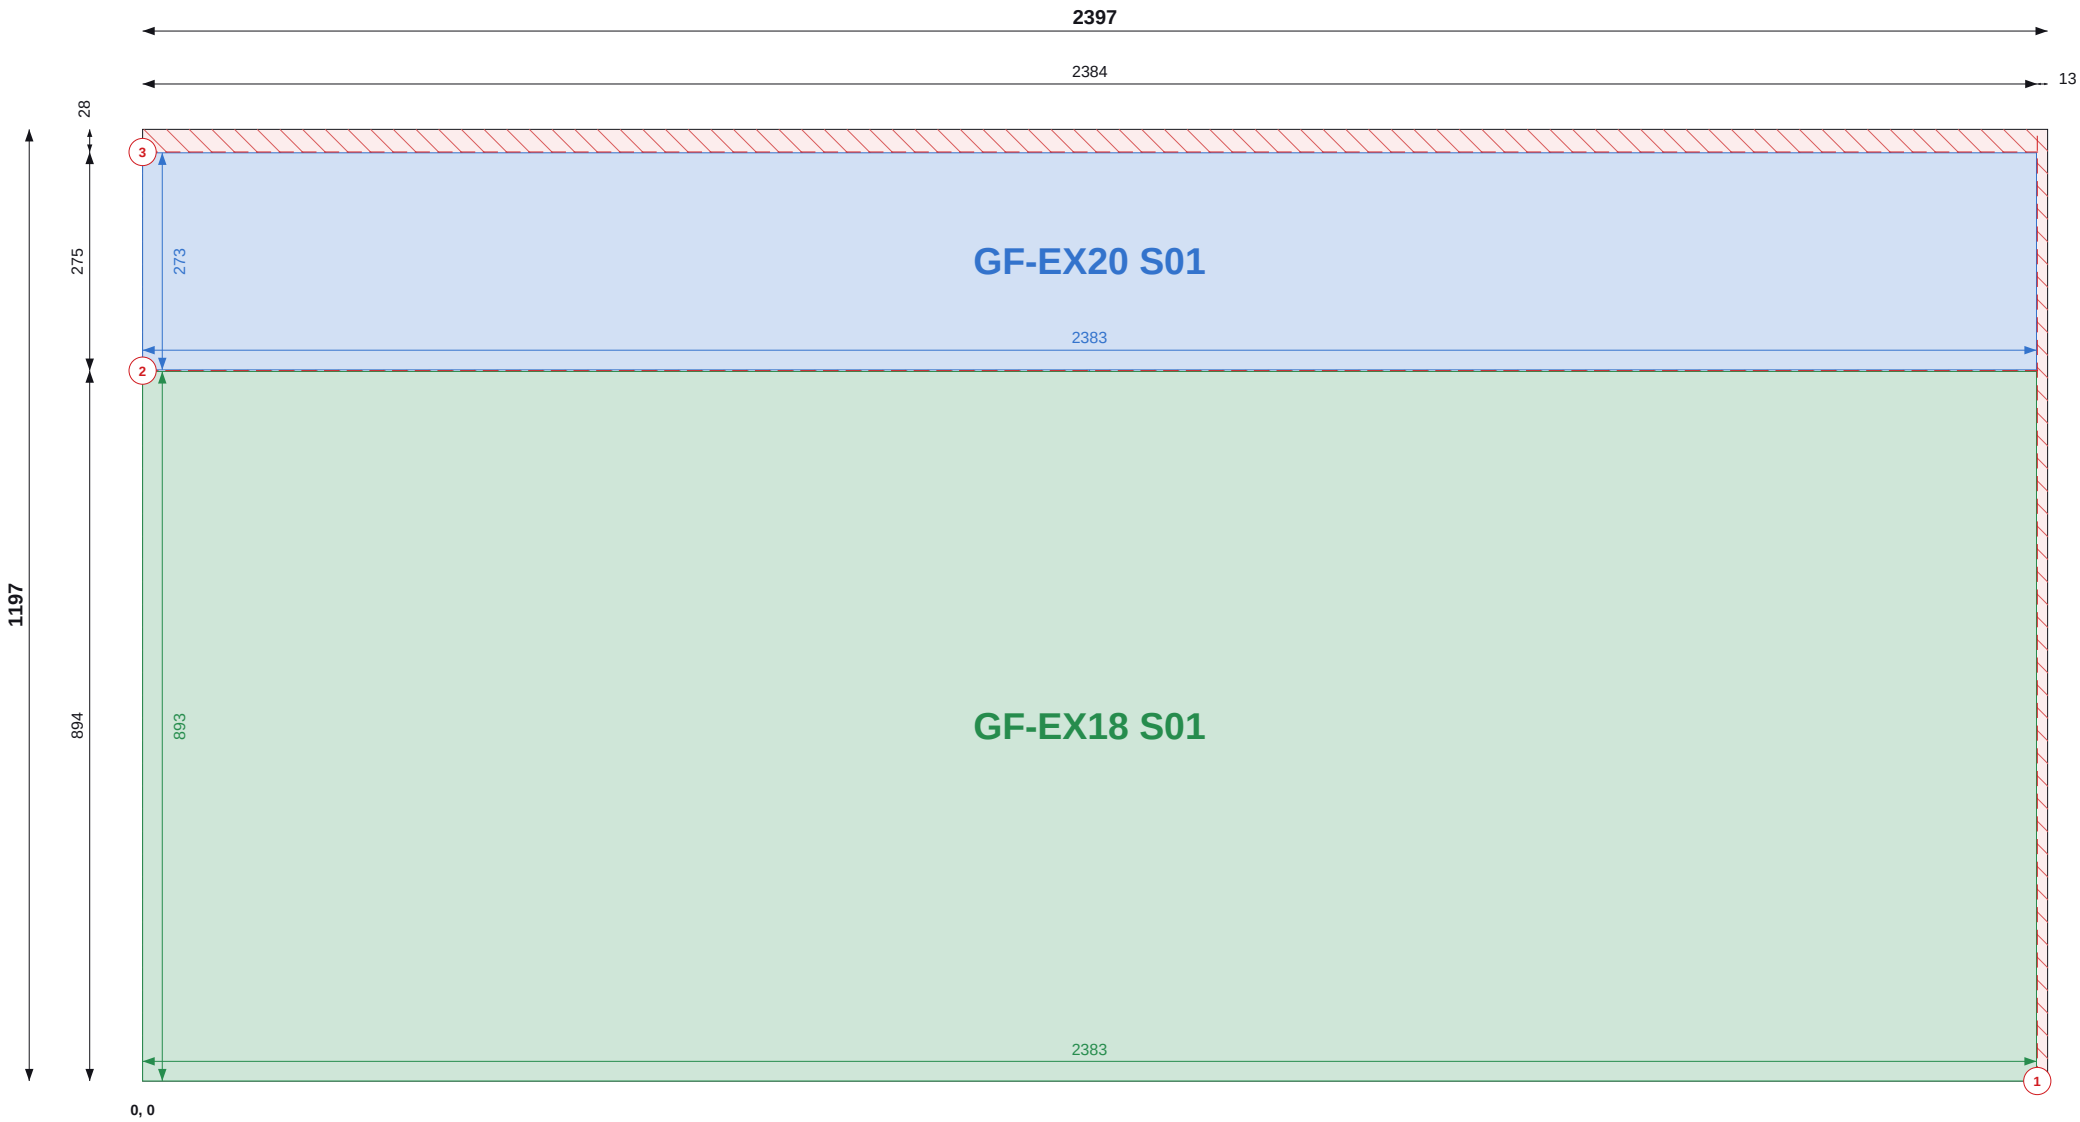

Top / left chains = saw cut positions (to cut centres). Coloured = part size and position.

SHEET 19 OF 38

THIS SHEET

Item	Value
Parts	2
Used / waste	96.8% / 0.09 m2
Reusable offcuts	0
Saw cuts / shared	3 / 1

PIECES (POSITION = BOTTOM-LEFT CORNER)

Label	Size	X, Y
GF-EX20 S01	273 x 2383	0, 895
GF-EX18 S01	893 x 2383	0, 0

NOTES

- Cut from OSB/3 9mm 1197x2397, 2mm saw kerf. Viewed on the face; dimensions from the sheet's bottom-left corner (0,0). Red numbered lines = saw cuts in order, each edge to edge.
- Coloured dimensions belong to the part of that colour: its width and height, and its position from the sheet edges. Raked parts: corner coordinates at each corner.
- Red hatch = waste. Labels = panel + piece mark on the manufacture drawing.

REVISIONS

REV	DATE	DESCRIPTION
C01	13.09.26	Construction issue



TLS TIMBER FRAME

Design & Manufacture

Scan: 3D model + drawings



CLIENT	PROJECT
MP Adams	MP Adams Plot 3, Eckington


DRAWING TITLE
OSB CUTTING - GROUND FLOOR - SHEET 19 OF 38

OSB/3 9mm 1197x2397 | Ground Floor

SCALE	SIZE	DATE	DRAWN
NTS	A3	13.09.26	TS

STATUS	DRAWING No.	REV
CONSTRUCTION	P3-CP-OSB-01 / 19	C01

Do not scale. All dimensions in mm. Check all dimensions on site.

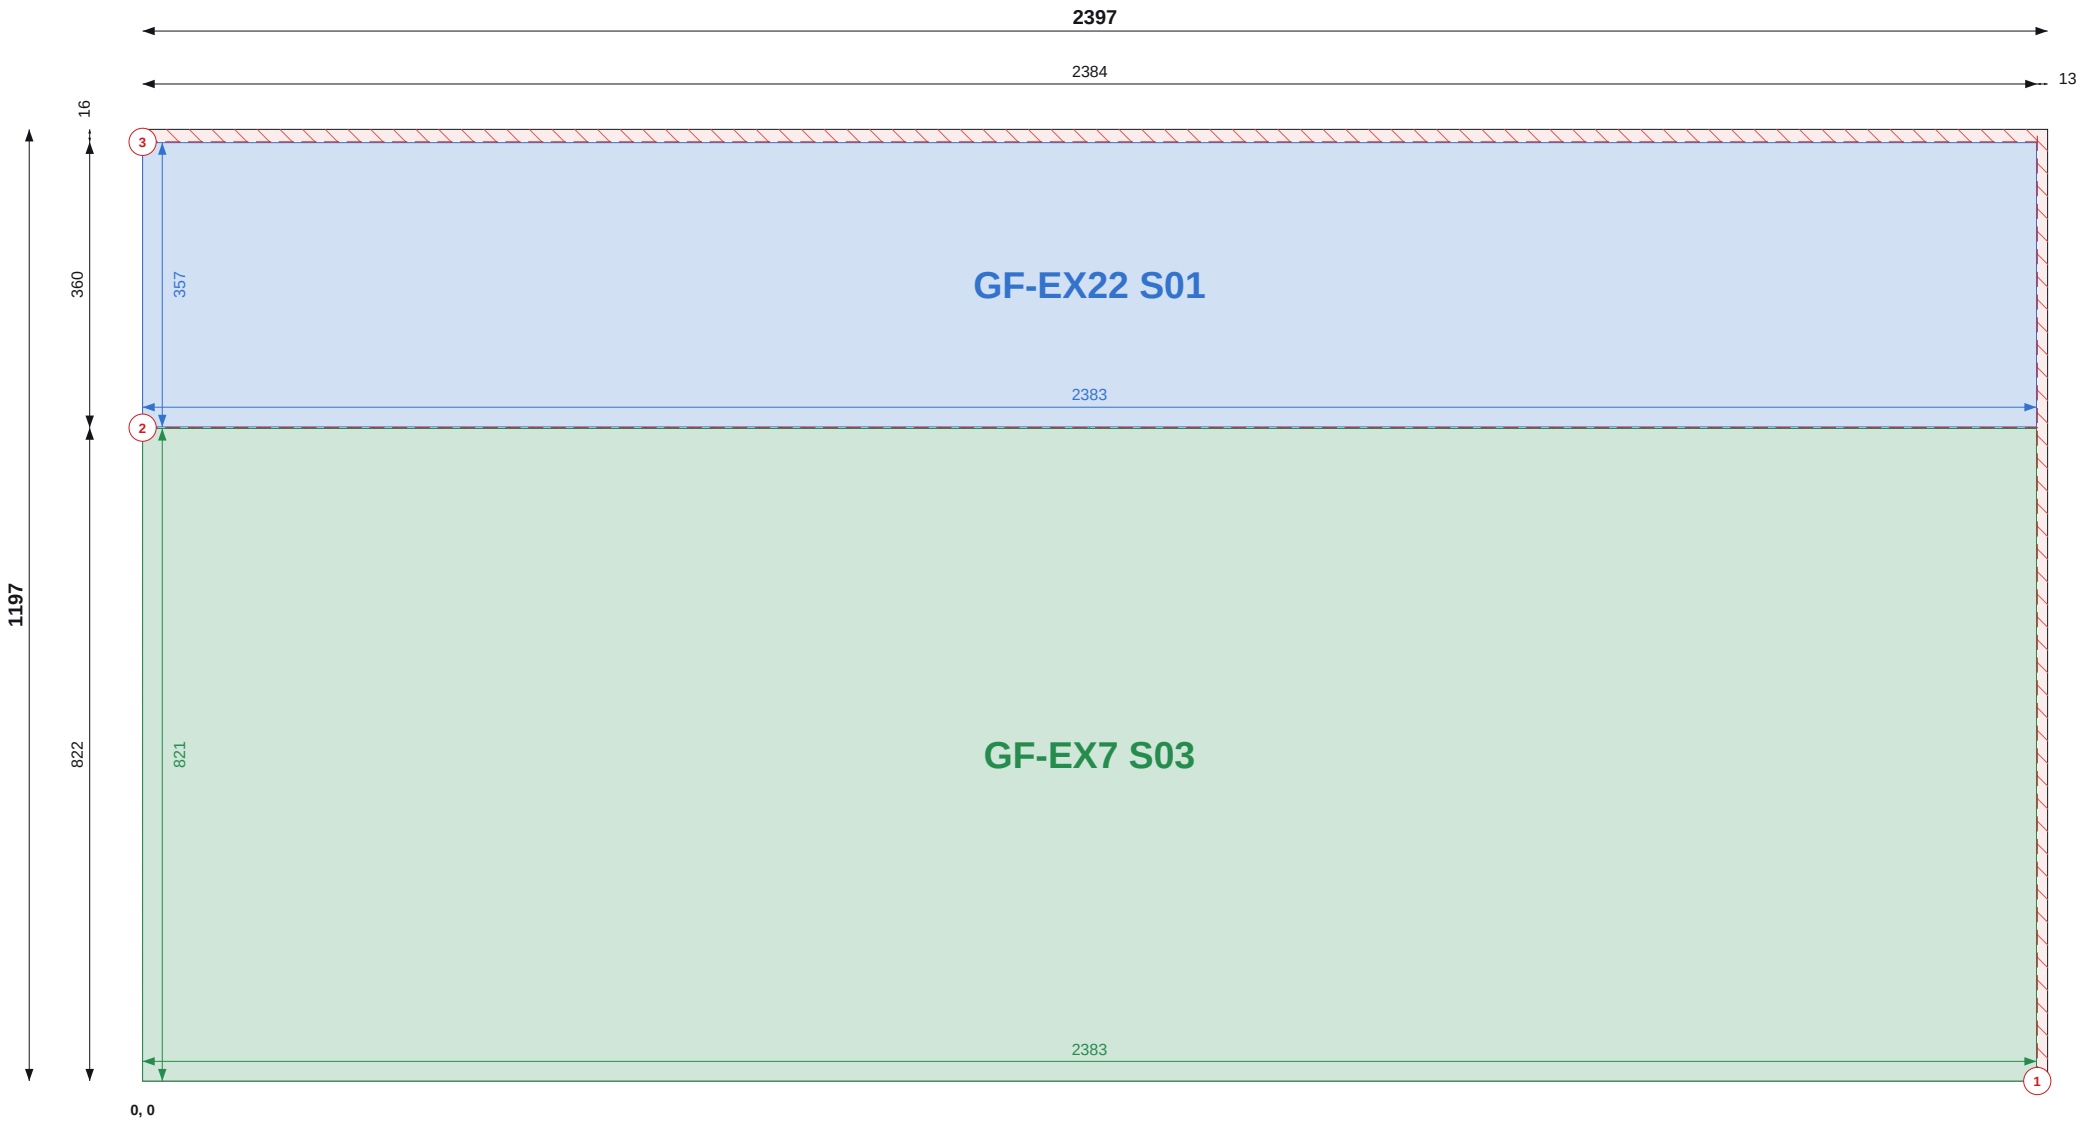

Top / left chains = saw cut positions (to cut centres). Coloured = part size and position.

SHEET 20 OF 38

THIS SHEET

Item	Value
Parts	2
Used / waste	97.9% / 0.06 m2
Reusable offcuts	0
Saw cuts / shared	3 / 1

PIECES (POSITION = BOTTOM-LEFT CORNER)

Label	Size	X, Y
GF-EX22 S01	357 x 2383	0, 823
GF-EX7 S03	821 x 2383	0, 0

NOTES

- Cut from OSB/3 9mm 1197x2397, 2mm saw kerf. Viewed on the face; dimensions from the sheet's bottom-left corner (0,0). Red numbered lines = saw cuts in order, each edge to edge.
- Coloured dimensions belong to the part of that colour: its width and height, and its position from the sheet edges. Raked parts: corner coordinates at each corner.
- Red hatch = waste. Labels = panel + piece mark on the manufacture drawing.

REVISIONS

REV	DATE	DESCRIPTION
C01	13.09.26	Construction issue



TLS TIMBER FRAME

Design & Manufacture

Scan: 3D model + drawings



CLIENT	PROJECT
MP Adams	MP Adams Plot 3, Eckington


DRAWING TITLE
OSB CUTTING - GROUND FLOOR - SHEET 20 OF 38

OSB/3 9mm 1197x2397 | Ground Floor

SCALE	SIZE	DATE	DRAWN
NTS	A3	13.09.26	TS

STATUS	DRAWING No.	REV
CONSTRUCTION	P3-CP-OSB-01 / 20	C01

Do not scale. All dimensions in mm. Check all dimensions on site.

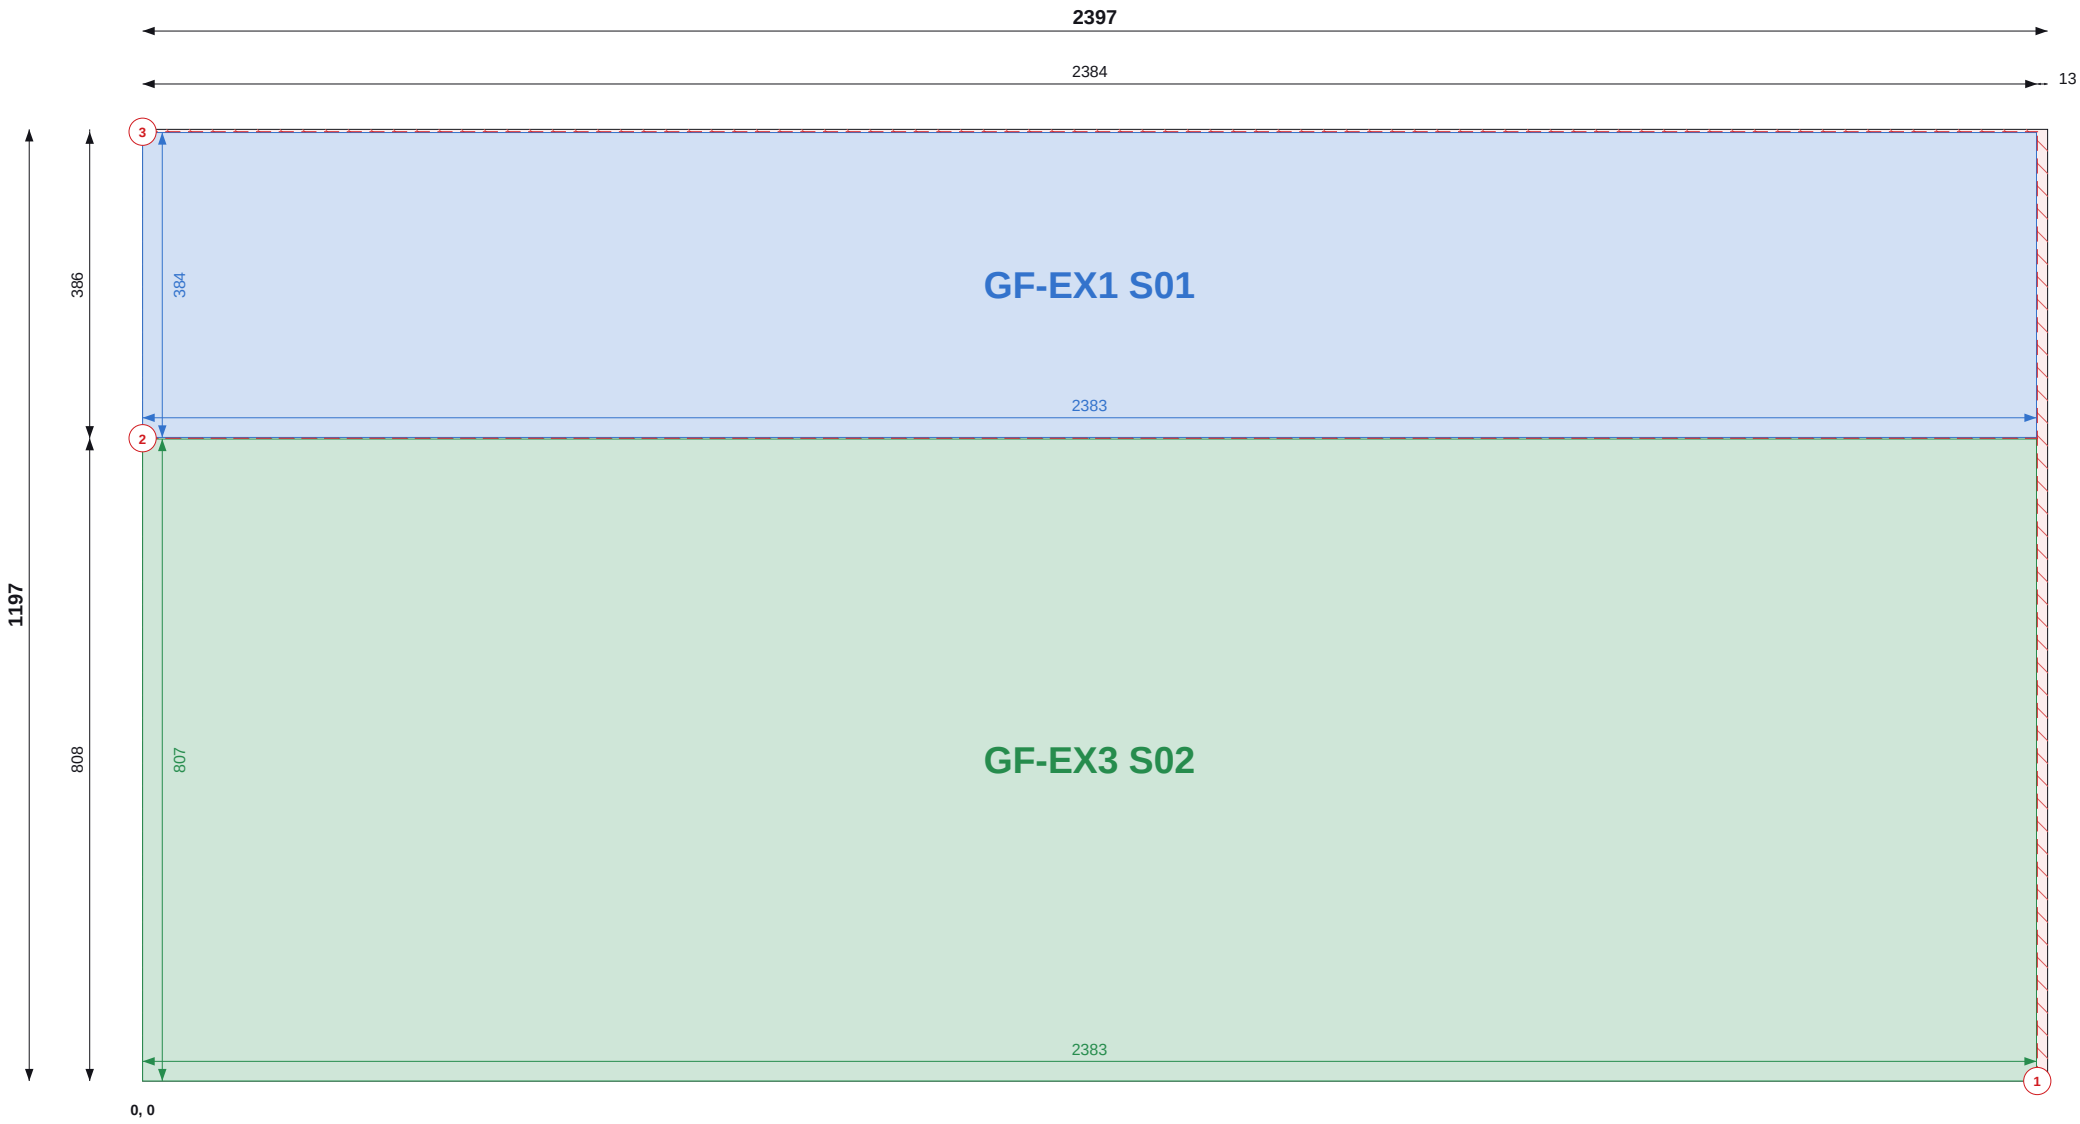

Top / left chains = saw cut positions (to cut centres). Coloured = part size and position.

SHEET 21 OF 38

THIS SHEET

Item	Value
Parts	2
Used / waste	98.9% / 0.03 m2
Reusable offcuts	0
Saw cuts / shared	3 / 1

PIECES (POSITION = BOTTOM-LEFT CORNER)

Label	Size	X, Y
GF-EX1 S01	384 x 2383	0, 809
GF-EX3 S02	807 x 2383	0, 0

NOTES

- Cut from OSB/3 9mm 1197x2397, 2mm saw kerf. Viewed on the face; dimensions from the sheet's bottom-left corner (0,0). Red numbered lines = saw cuts in order, each edge to edge.
- Coloured dimensions belong to the part of that colour: its width and height, and its position from the sheet edges. Raked parts: corner coordinates at each corner.
- Red hatch = waste. Labels = panel + piece mark on the manufacture drawing.

REVISIONS

REV	DATE	DESCRIPTION
C01	13.09.26	Construction issue



TLS TIMBER FRAME

Design & Manufacture

Scan: 3D model + drawings



CLIENT	PROJECT
MP Adams	MP Adams Plot 3, Eckington


DRAWING TITLE
OSB CUTTING - GROUND FLOOR - SHEET 21 OF 38

OSB/3 9mm 1197x2397 | Ground Floor

SCALE	SIZE	DATE	DRAWN
NTS	A3	13.09.26	TS

STATUS	DRAWING No.	REV
CONSTRUCTION	P3-CP-OSB-01 / 21	C01

Do not scale. All dimensions in mm. Check all dimensions on site.

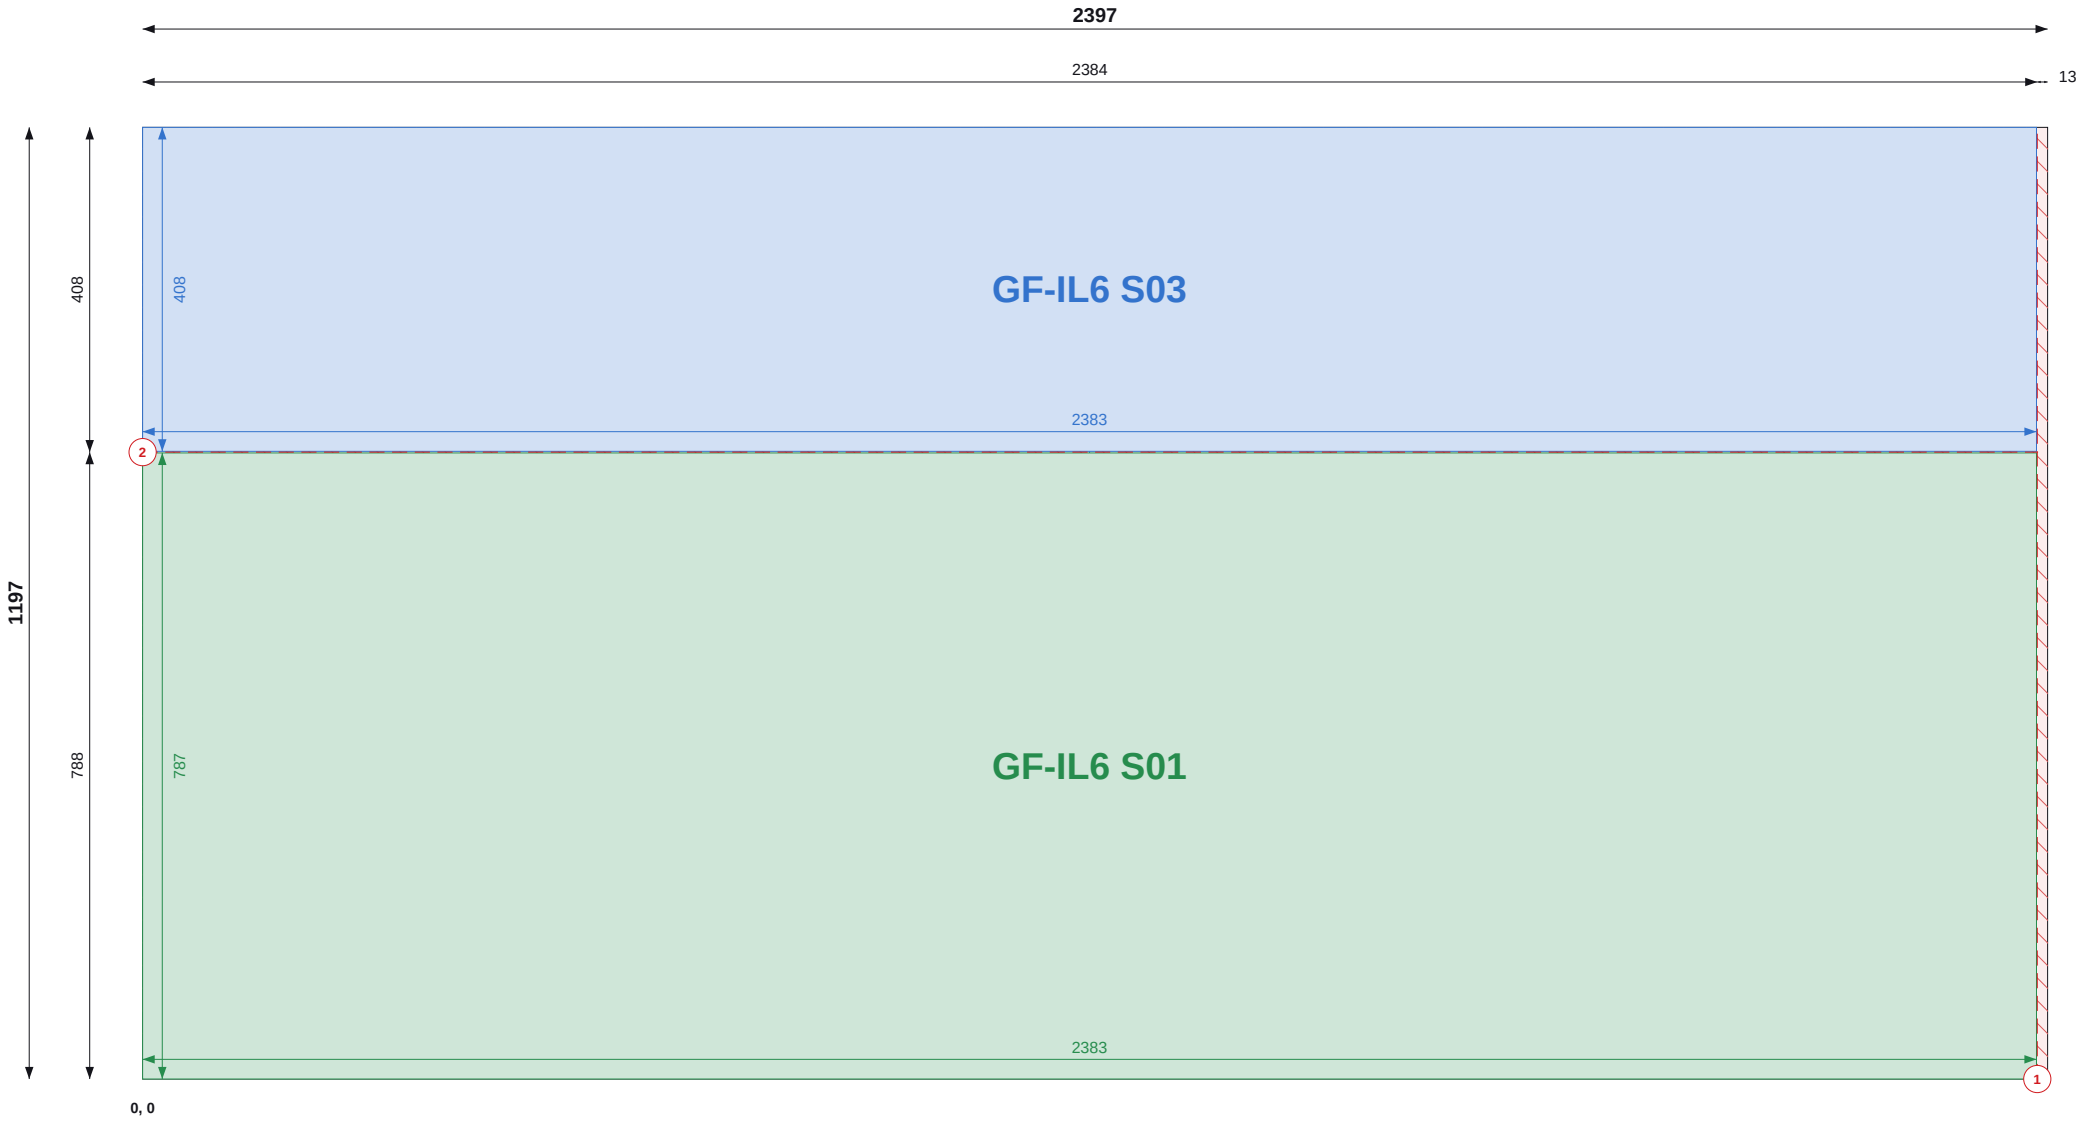

Top / left chains = saw cut positions (to cut centres). Coloured = part size and position.

SHEET 22 OF 38

THIS SHEET

Item	Value
Parts	2
Used / waste	99.2% / 0.02 m2
Reusable offcuts	0
Saw cuts / shared	2 / 1

PIECES (POSITION = BOTTOM-LEFT CORNER)

Label	Size	X, Y
GF-IL6 S03	408 x 2383	0, 789
GF-IL6 S01	787 x 2383	0, 0

NOTES

- Cut from OSB/3 9mm 1197x2397, 2mm saw kerf. Viewed on the face; dimensions from the sheet's bottom-left corner (0,0). Red numbered lines = saw cuts in order, each edge to edge.
- Coloured dimensions belong to the part of that colour: its width and height, and its position from the sheet edges. Raked parts: corner coordinates at each corner.
- Red hatch = waste. Labels = panel + piece mark on the manufacture drawing.

REVISIONS

REV	DATE	DESCRIPTION
C01	13.09.26	Construction issue



TLS TIMBER FRAME

Design & Manufacture

Scan: 3D model + drawings



CLIENT	PROJECT
MP Adams	MP Adams Plot 3, Eckington

DRAWING TITLE			
OSB CUTTING - GROUND FLOOR - SHEET 22 OF 38			
OSB/3 9mm 1197x2397 Ground Floor			

SCALE	SIZE	DATE	DRAWN
NTS	A3	13.09.26	TS

STATUS	DRAWING No.	REV
CONSTRUCTION	P3-CP-OSB-01 / 22	C01

Do not scale. All dimensions in mm. Check all dimensions on site.



Top / left chains = saw cut positions (to cut centres). Coloured = part size and position.

SHEET 23 OF 38

THIS SHEET

Item	Value
Parts	2
Used / waste	99.2% / 0.02 m2
Reusable offcuts	0
Saw cuts / shared	2 / 1

PIECES (POSITION = BOTTOM-LEFT CORNER)

Label	Size	X, Y
GF-IL1 S01	413 x 2383	0, 784
GF-EX1 S03	782 x 2383	0, 0

NOTES

- Cut from OSB/3 9mm 1197x2397, 2mm saw kerf. Viewed on the face; dimensions from the sheet's bottom-left corner (0,0). Red numbered lines = saw cuts in order, each edge to edge.
- Coloured dimensions belong to the part of that colour: its width and height, and its position from the sheet edges. Raked parts: corner coordinates at each corner.
- Red hatch = waste. Labels = panel + piece mark on the manufacture drawing.

REVISIONS

REV	DATE	DESCRIPTION
C01	13.09.26	Construction issue



TLS TIMBER FRAME

Design & Manufacture

Scan: 3D model + drawings



CLIENT MP Adams	PROJECT MP Adams Plot 3, Eckington
--------------------	---------------------------------------


DRAWING TITLE
OSB CUTTING - GROUND FLOOR - SHEET 23 OF 38

OSB/3 9mm 1197x2397 | Ground Floor

SCALE NTS	SIZE A3	DATE 13.09.26	DRAWN TS
--------------	------------	------------------	-------------

STATUS CONSTRUCTION	DRAWING No. P3-CP-OSB-01 / 23	REV C01
-------------------------------	---	-------------------

Do not scale. All dimensions in mm. Check all dimensions on site.

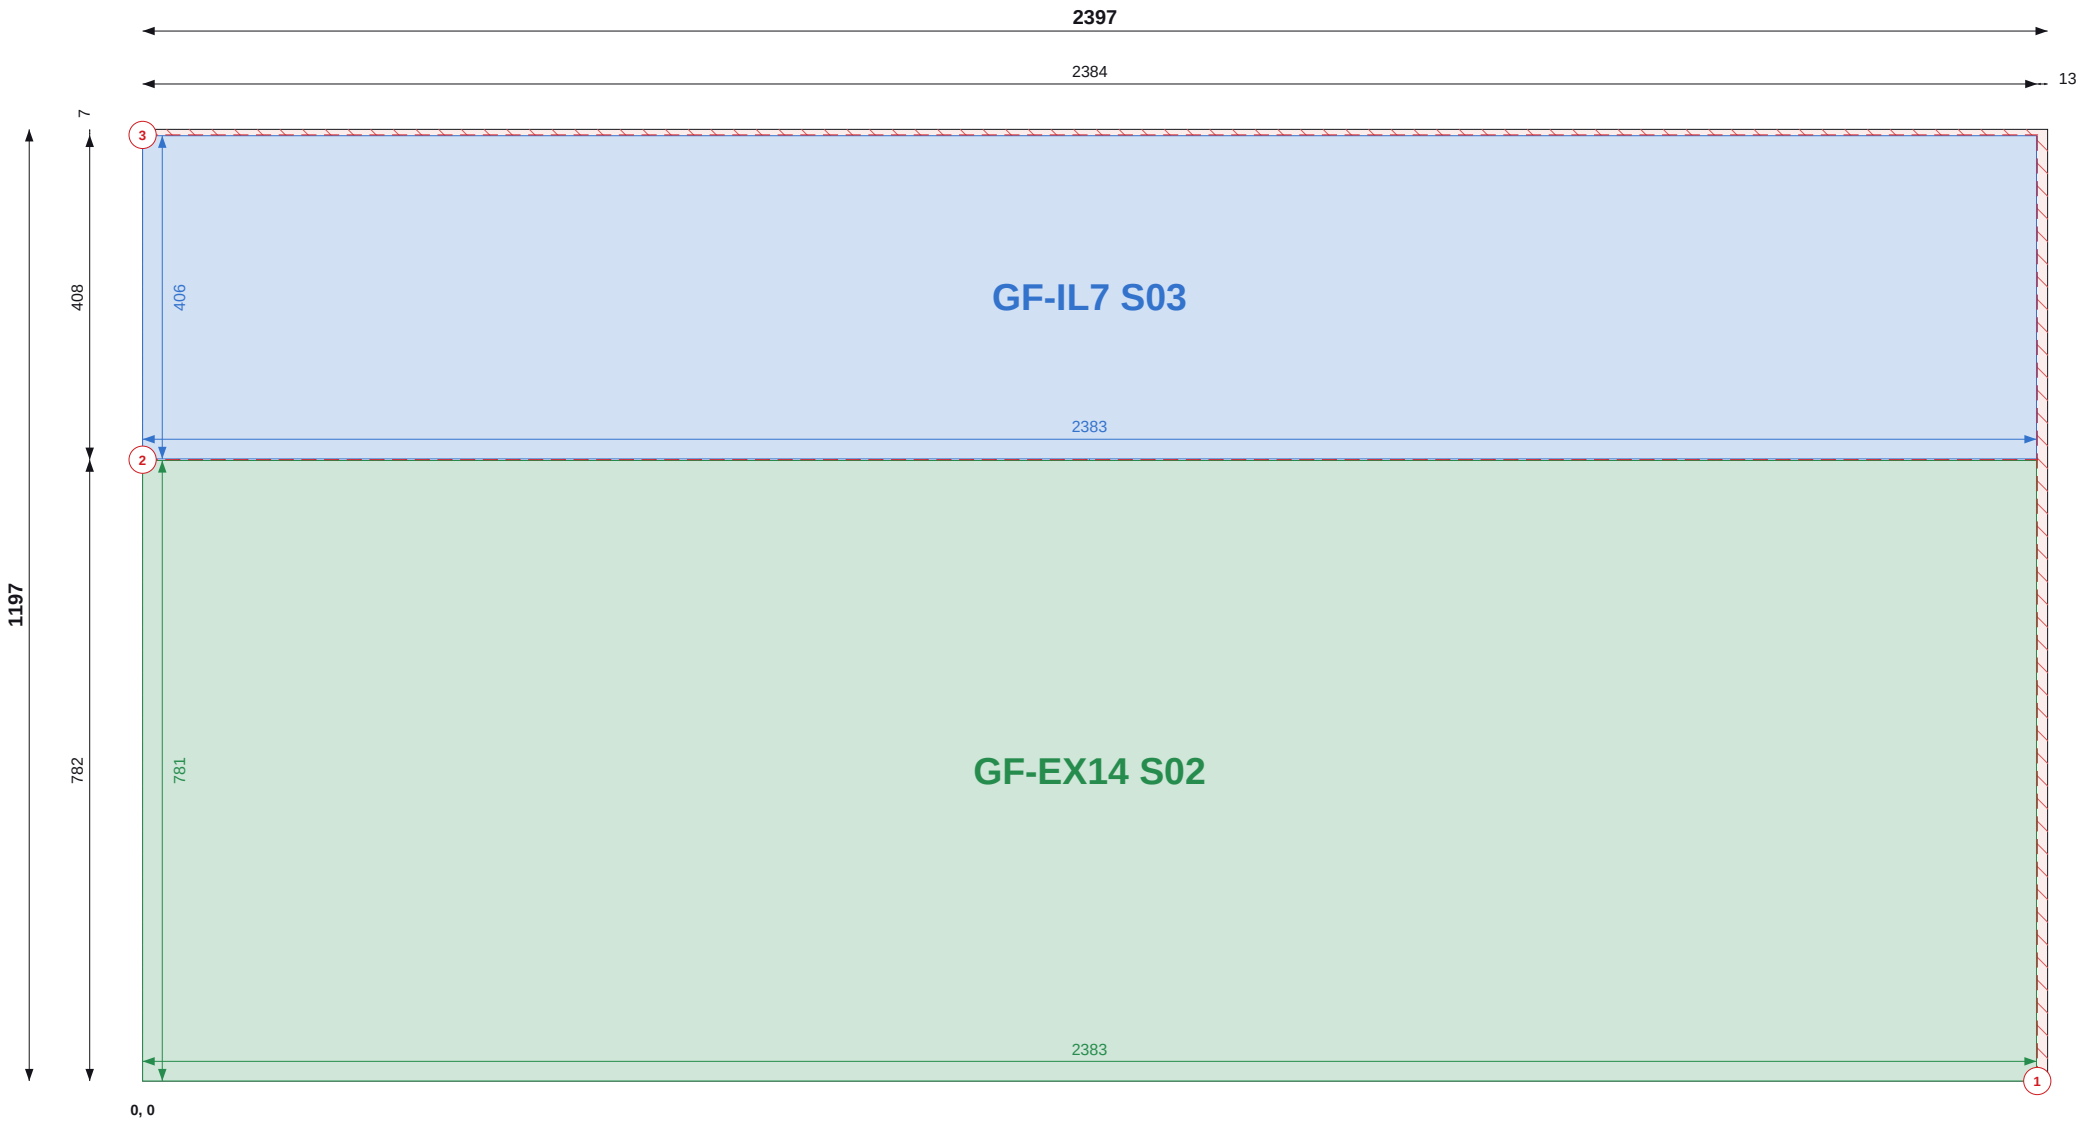

Top / left chains = saw cut positions (to cut centres). Coloured = part size and position.

SHEET 24 OF 38

THIS SHEET

Item	Value
Parts	2
Used / waste	98.6% / 0.04 m2
Reusable offcuts	0
Saw cuts / shared	3 / 1

PIECES (POSITION = BOTTOM-LEFT CORNER)

Label	Size	X, Y
GF-IL7 S03	406 x 2383	0, 783
GF-EX14 S02	781 x 2383	0, 0

NOTES

- Cut from OSB/3 9mm 1197x2397, 2mm saw kerf. Viewed on the face; dimensions from the sheet's bottom-left corner (0,0). Red numbered lines = saw cuts in order, each edge to edge.
- Coloured dimensions belong to the part of that colour: its width and height, and its position from the sheet edges. Raked parts: corner coordinates at each corner.
- Red hatch = waste. Labels = panel + piece mark on the manufacture drawing.

REVISIONS

REV	DATE	DESCRIPTION
C01	13.09.26	Construction issue



TLS TIMBER FRAME

Design & Manufacture

Scan: 3D model + drawings




CLIENT	PROJECT
MP Adams	MP Adams Plot 3, Eckington

DRAWING TITLE			
OSB CUTTING - GROUND FLOOR - SHEET 24 OF 38			
OSB/3 9mm 1197x2397 Ground Floor			

SCALE	SIZE	DATE	DRAWN
NTS	A3	13.09.26	TS

STATUS	DRAWING No.	REV
CONSTRUCTION	P3-CP-OSB-01 / 24	C01

Do not scale. All dimensions in mm. Check all dimensions on site.

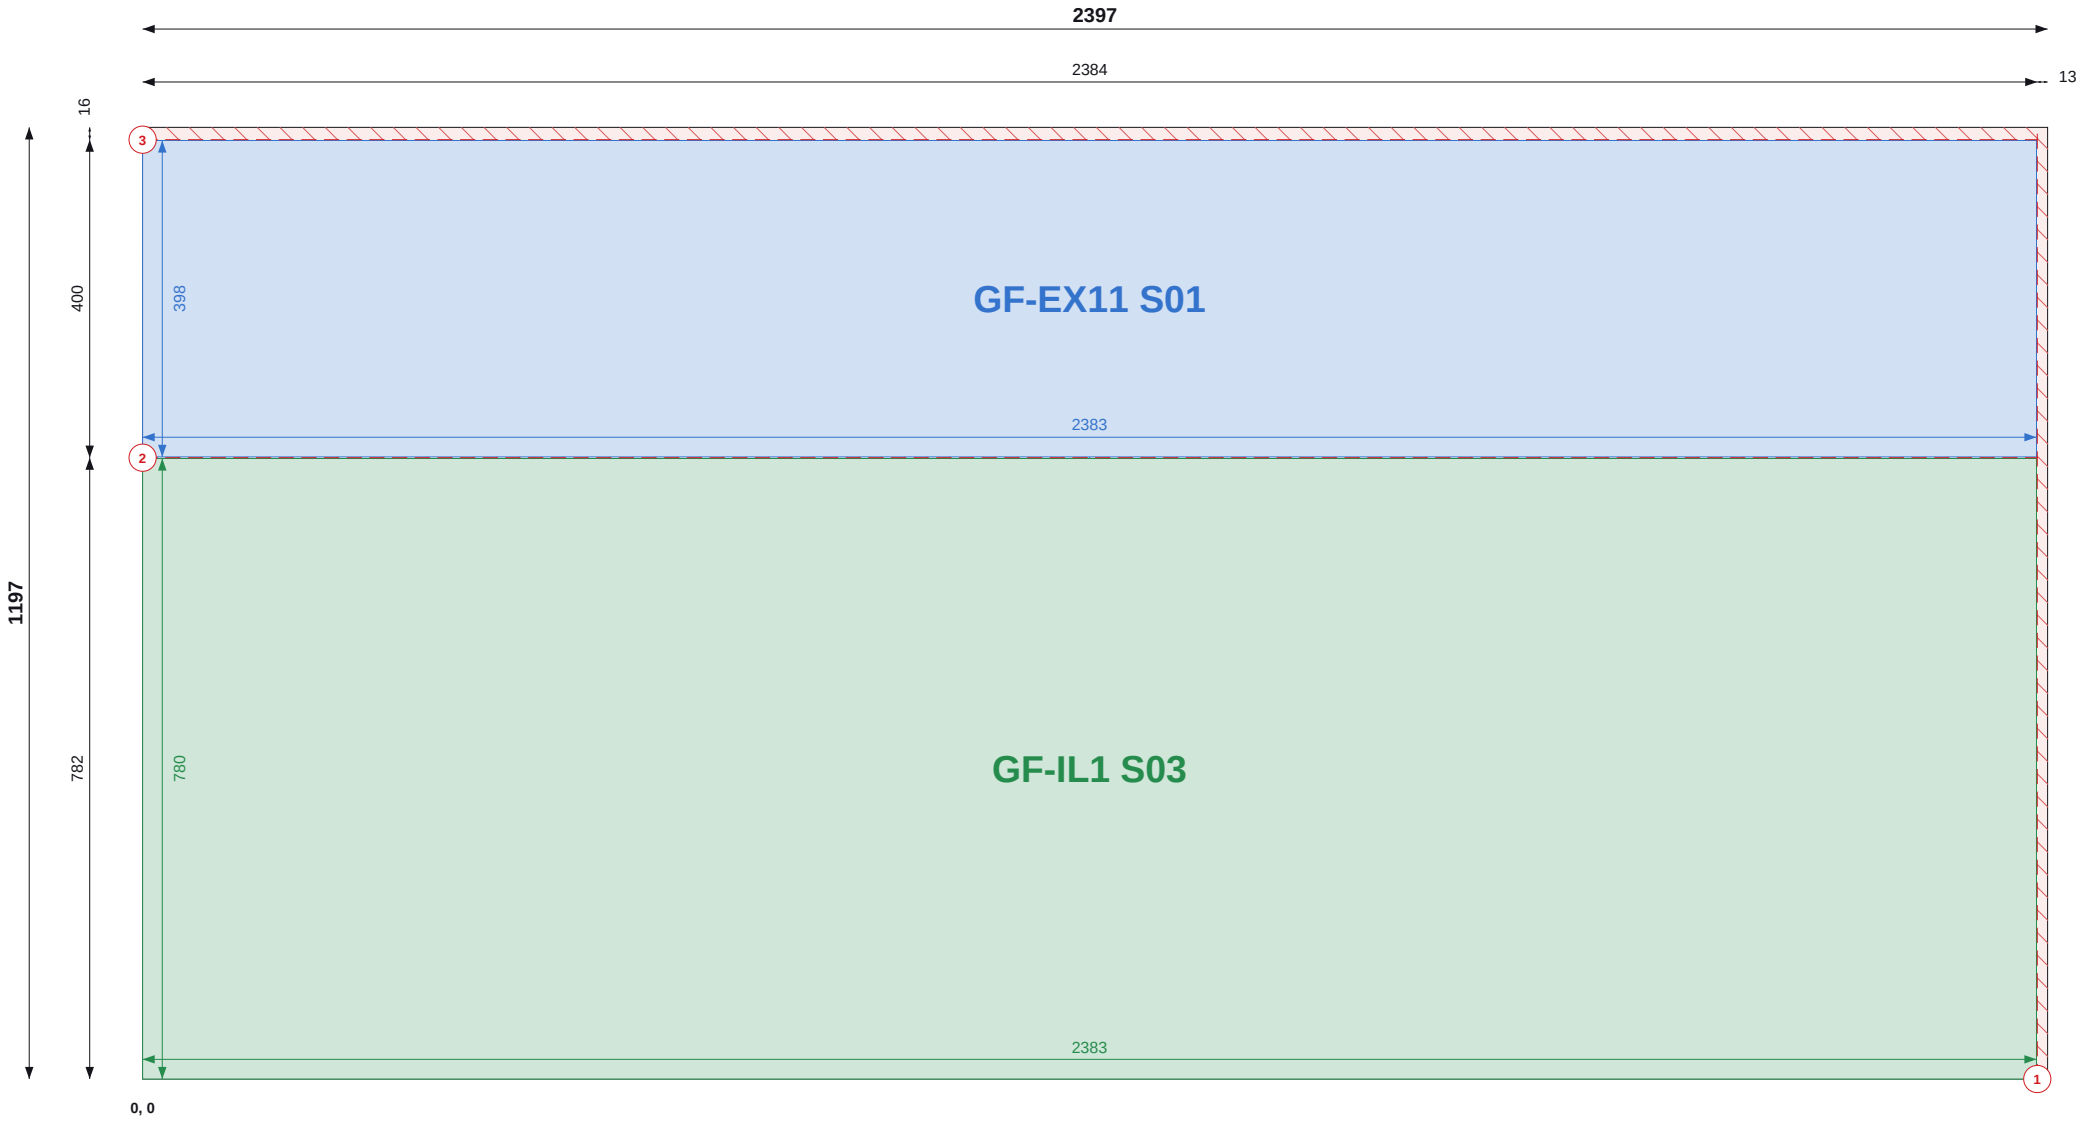

Top / left chains = saw cut positions (to cut centres). Coloured = part size and position.

SHEET 25 OF 38

THIS SHEET

Item	Value
Parts	2
Used / waste	97.9% / 0.06 m2
Reusable offcuts	0
Saw cuts / shared	3 / 1

PIECES (POSITION = BOTTOM-LEFT CORNER)

Label	Size	X, Y
GF-EX11 S01	398 x 2383	0, 782
GF-IL1 S03	780 x 2383	0, 0

NOTES

- Cut from OSB/3 9mm 1197x2397, 2mm saw kerf. Viewed on the face; dimensions from the sheet's bottom-left corner (0,0). Red numbered lines = saw cuts in order, each edge to edge.
- Coloured dimensions belong to the part of that colour: its width and height, and its position from the sheet edges. Raked parts: corner coordinates at each corner.
- Red hatch = waste. Labels = panel + piece mark on the manufacture drawing.

REVISIONS

REV	DATE	DESCRIPTION
C01	13.09.26	Construction issue



TLS TIMBER FRAME

Design & Manufacture

Scan: 3D model + drawings




CLIENT	PROJECT
MP Adams	MP Adams Plot 3, Eckington

DRAWING TITLE			
OSB CUTTING - GROUND FLOOR - SHEET 25 OF 38			
OSB/3 9mm 1197x2397 Ground Floor			

SCALE	SIZE	DATE	DRAWN
NTS	A3	13.09.26	TS

STATUS	DRAWING No.	REV
CONSTRUCTION	P3-CP-OSB-01 / 25	C01

Do not scale. All dimensions in mm. Check all dimensions on site.

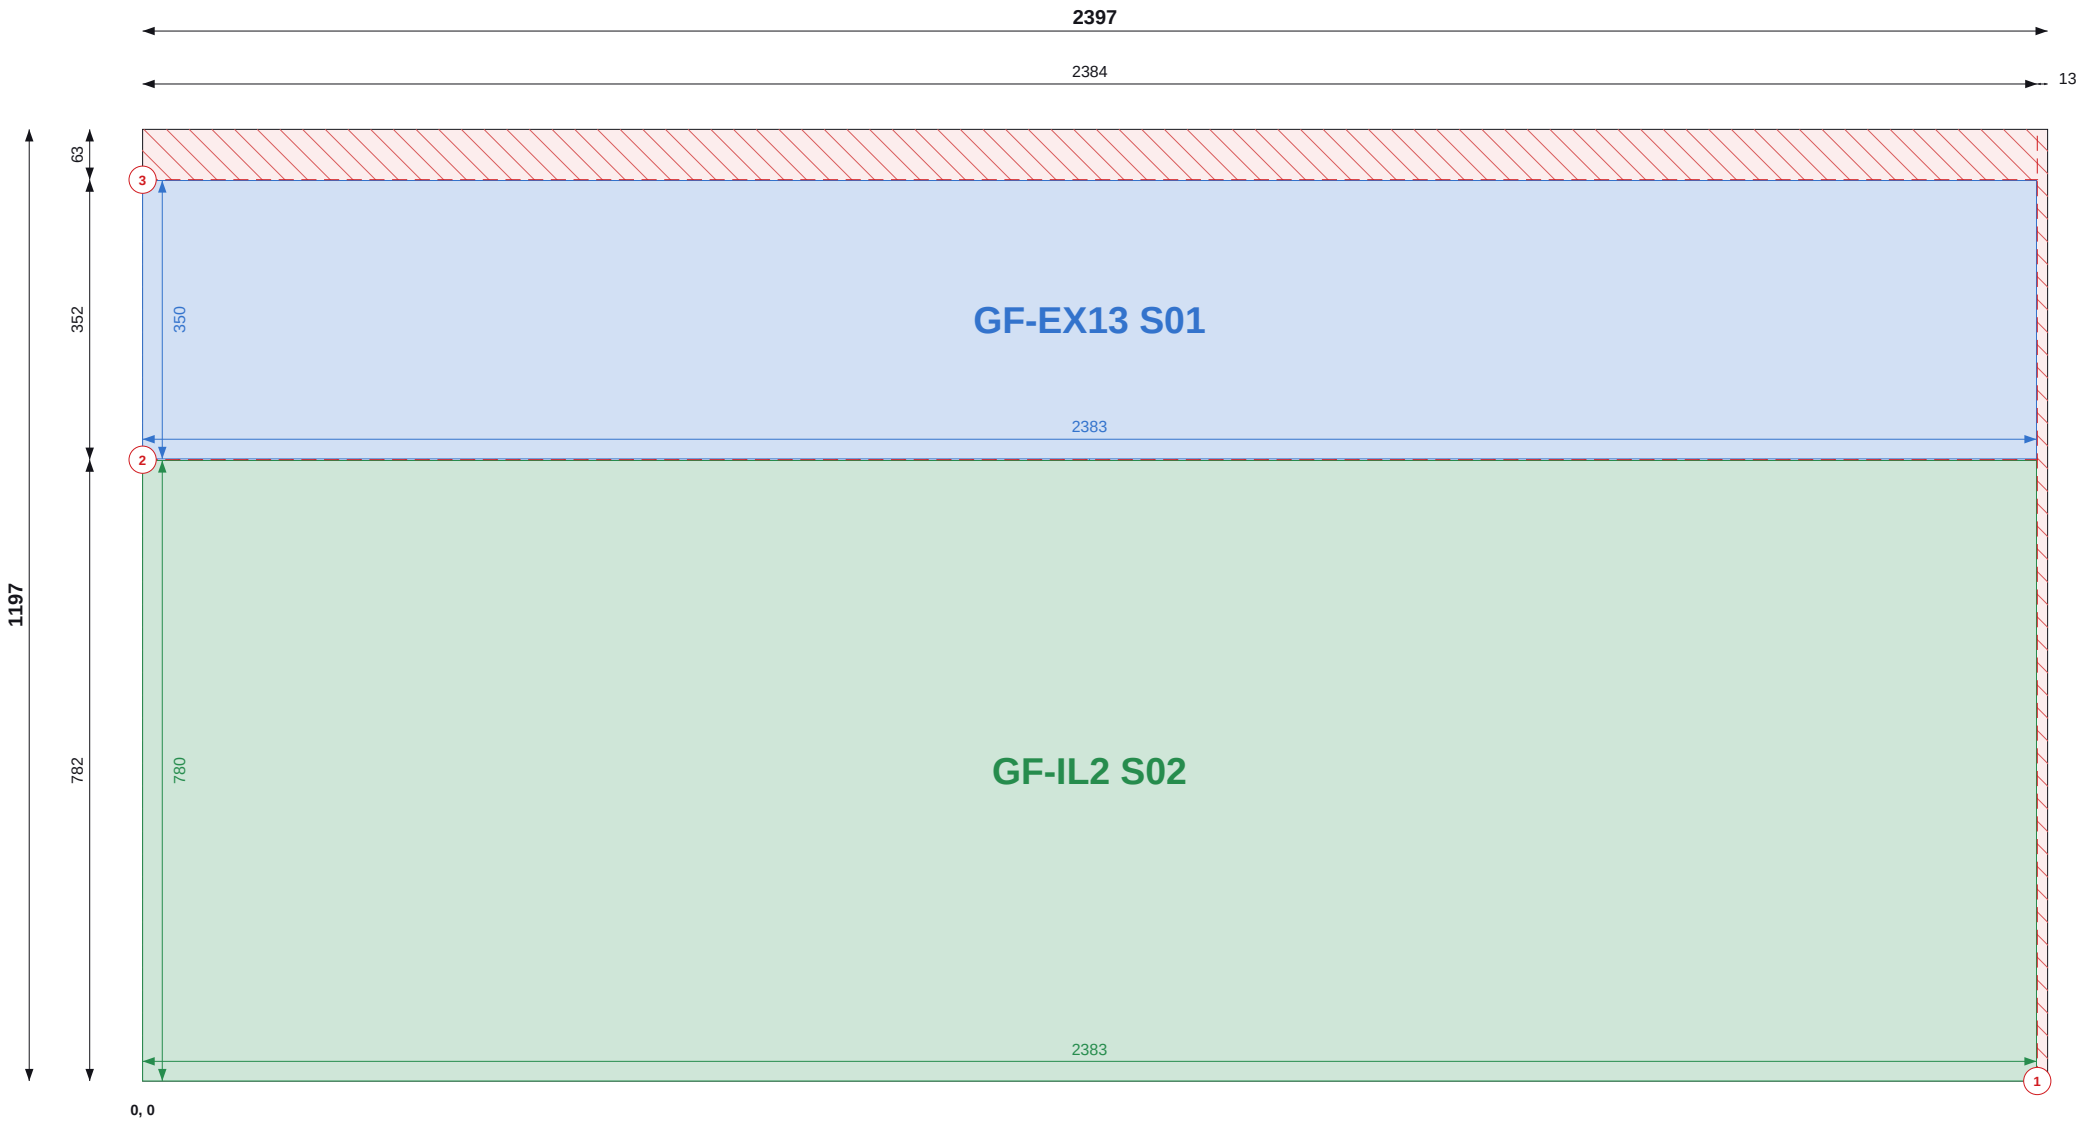

Top / left chains = saw cut positions (to cut centres). Coloured = part size and position.

SHEET 26 OF 38

THIS SHEET

Item	Value
Parts	2
Used / waste	93.9% / 0.17 m2
Reusable offcuts	0
Saw cuts / shared	3 / 1

PIECES (POSITION = BOTTOM-LEFT CORNER)

Label	Size	X, Y
GF-EX13 S01	350 x 2383	0, 782
GF-IL2 S02	780 x 2383	0, 0

NOTES

- Cut from OSB/3 9mm 1197x2397, 2mm saw kerf. Viewed on the face; dimensions from the sheet's bottom-left corner (0,0). Red numbered lines = saw cuts in order, each edge to edge.
- Coloured dimensions belong to the part of that colour: its width and height, and its position from the sheet edges. Raked parts: corner coordinates at each corner.
- Red hatch = waste. Labels = panel + piece mark on the manufacture drawing.

REVISIONS

REV	DATE	DESCRIPTION
C01	13.09.26	Construction issue



TLS TIMBER FRAME

Design & Manufacture

Scan: 3D model + drawings



CLIENT MP Adams	PROJECT MP Adams Plot 3, Eckington
--------------------	---------------------------------------


DRAWING TITLE OSB CUTTING - GROUND FLOOR - SHEET 26 OF 38

OSB/3 9mm 1197x2397 | Ground Floor

SCALE NTS	SIZE A3	DATE 13.09.26	DRAWN TS
--------------	------------	------------------	-------------

STATUS CONSTRUCTION	DRAWING No. P3-CP-OSB-01 / 26	REV C01
-------------------------------	---	-------------------

Do not scale. All dimensions in mm. Check all dimensions on site.

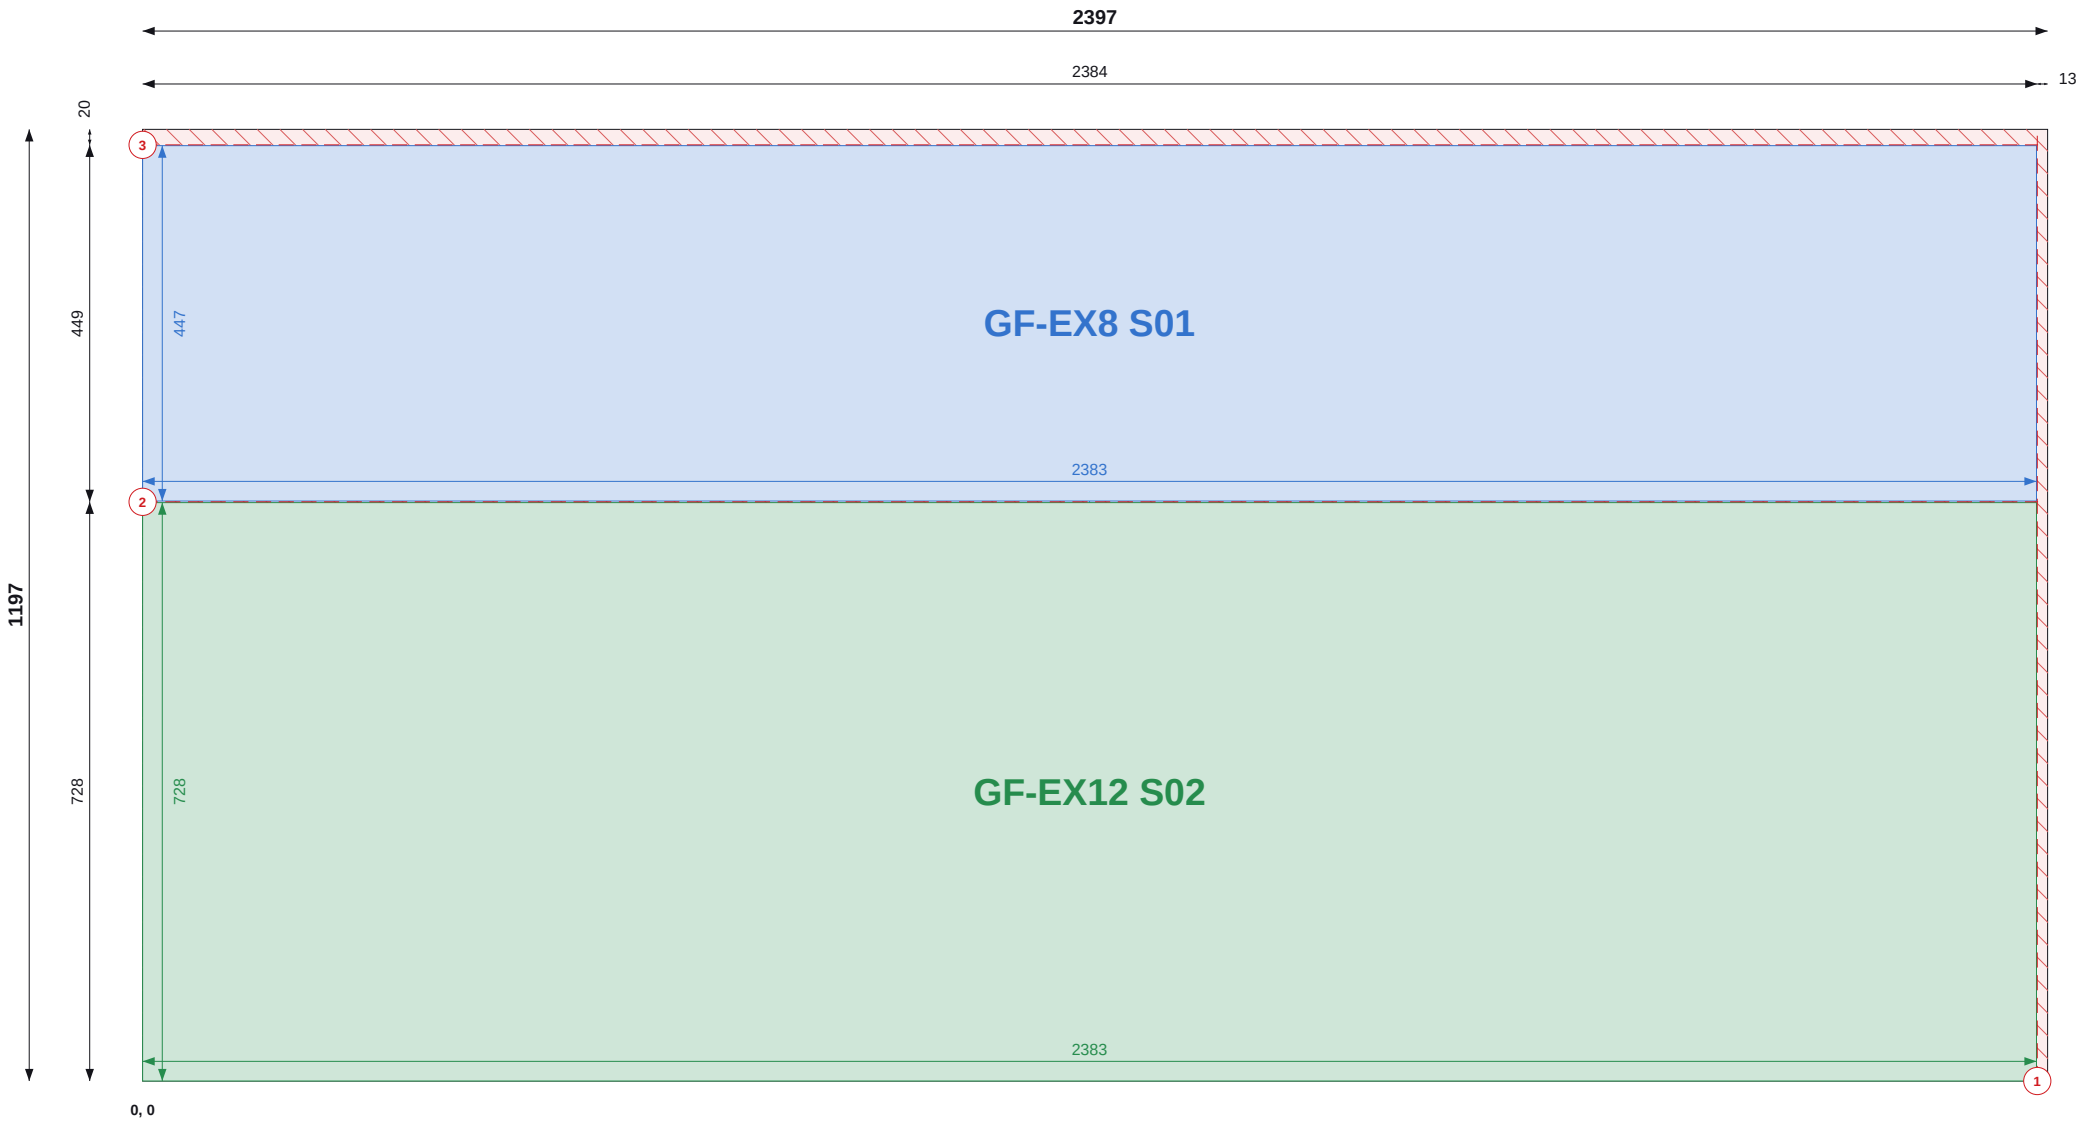

Top / left chains = saw cut positions (to cut centres). Coloured = part size and position.

SHEET 27 OF 38

THIS SHEET

Item	Value
Parts	2
Used / waste	97.5% / 0.07 m2
Reusable offcuts	0
Saw cuts / shared	3 / 1

PIECES (POSITION = BOTTOM-LEFT CORNER)

Label	Size	X, Y
GF-EX8 S01	447 x 2383	0, 730
GF-EX12 S02	728 x 2383	0, 0

NOTES

- Cut from OSB/3 9mm 1197x2397, 2mm saw kerf. Viewed on the face; dimensions from the sheet's bottom-left corner (0,0). Red numbered lines = saw cuts in order, each edge to edge.
- Coloured dimensions belong to the part of that colour: its width and height, and its position from the sheet edges. Raked parts: corner coordinates at each corner.
- Red hatch = waste. Labels = panel + piece mark on the manufacture drawing.

REVISIONS

REV	DATE	DESCRIPTION
C01	13.09.26	Construction issue



TLS TIMBER FRAME

Design & Manufacture

Scan: 3D model + drawings



CLIENT MP Adams	PROJECT MP Adams Plot 3, Eckington
--------------------	---------------------------------------


DRAWING TITLE
OSB CUTTING - GROUND FLOOR - SHEET 27 OF 38

OSB/3 9mm 1197x2397 | Ground Floor

SCALE NTS	SIZE A3	DATE 13.09.26	DRAWN TS
--------------	------------	------------------	-------------

STATUS CONSTRUCTION	DRAWING No. P3-CP-OSB-01 / 27	REV C01
-------------------------------	---	-------------------

Do not scale. All dimensions in mm. Check all dimensions on site.

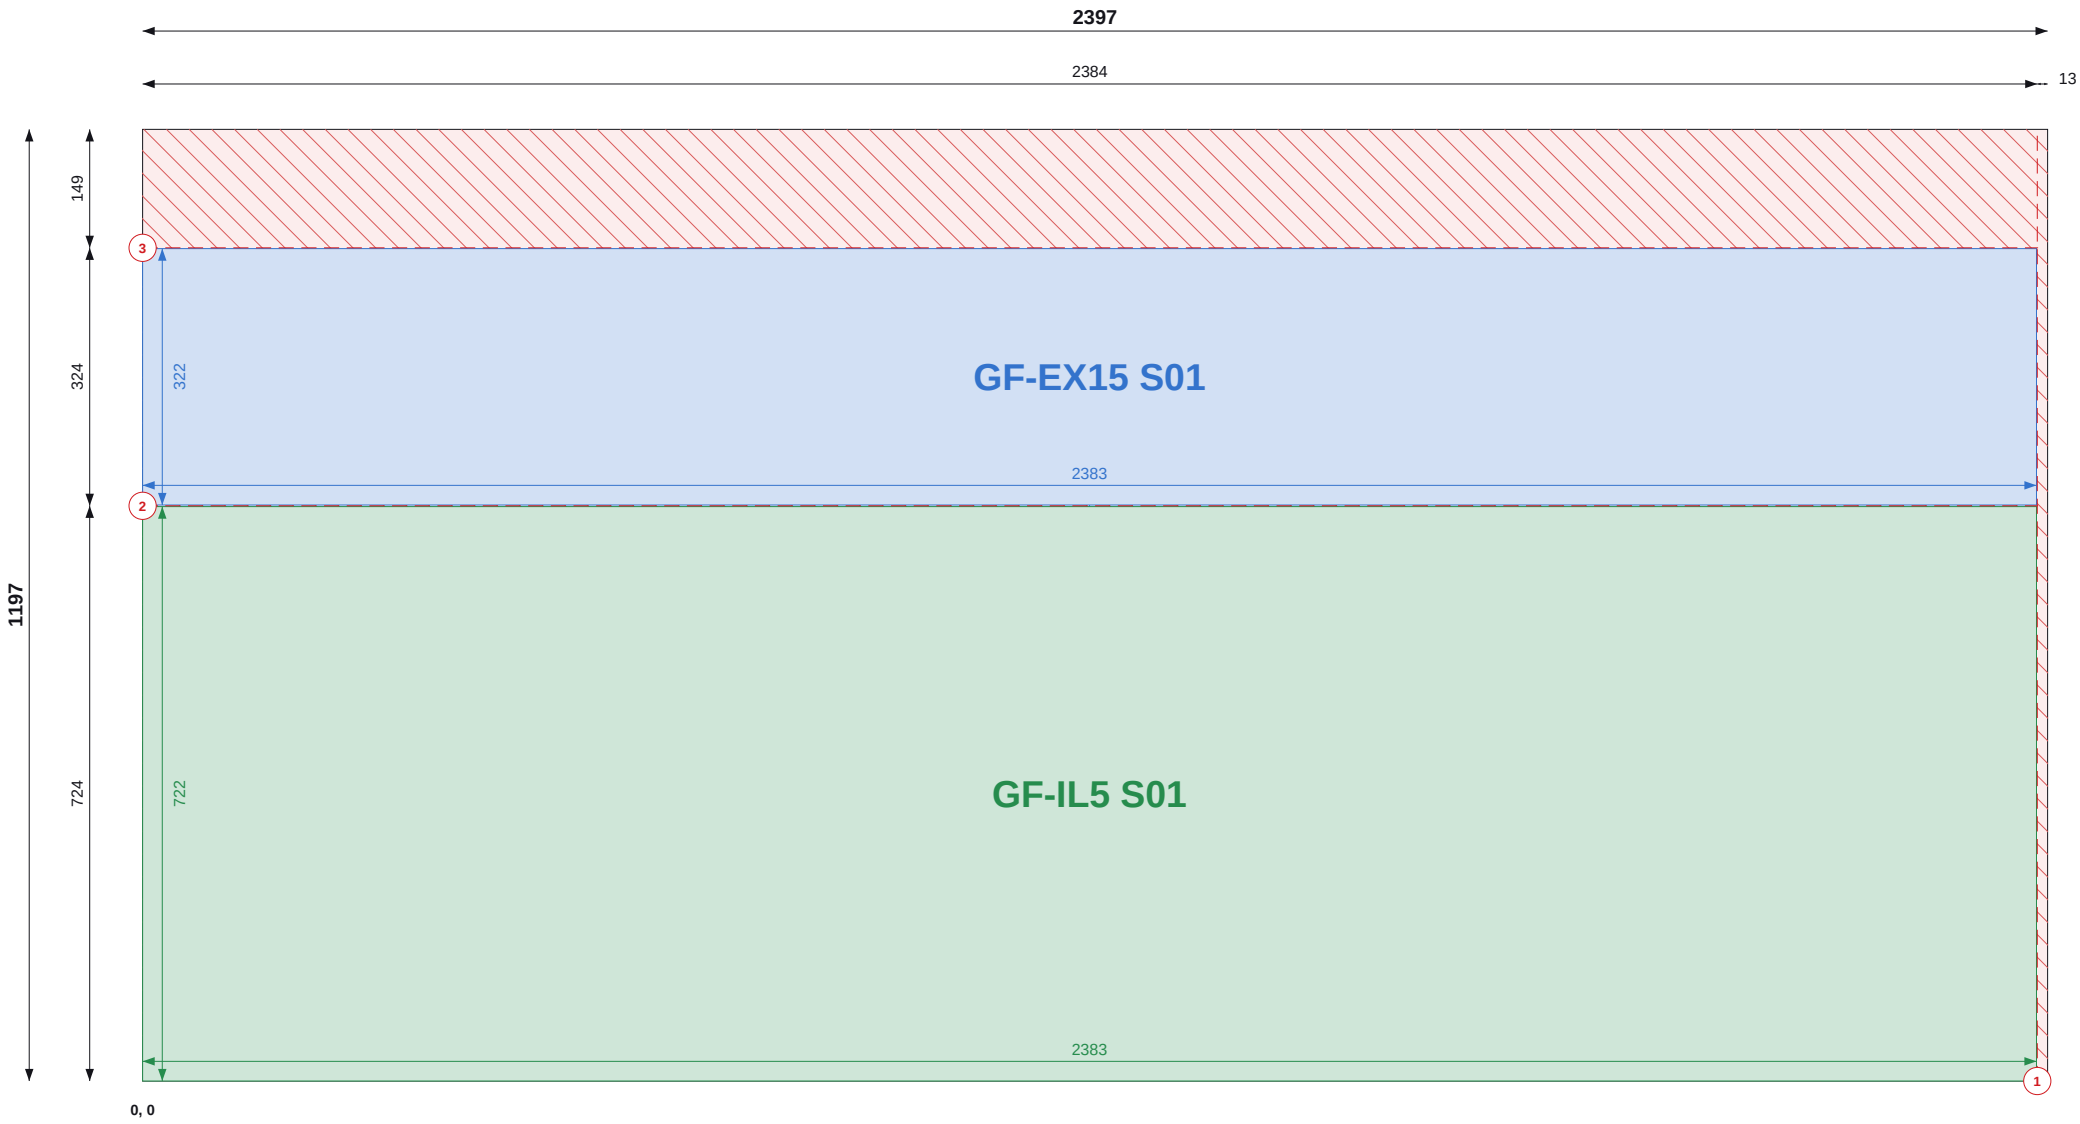

Top / left chains = saw cut positions (to cut centres). Coloured = part size and position.

SHEET 28 OF 38

THIS SHEET

Item	Value
Parts	2
Used / waste	86.8% / 0.38 m2
Reusable offcuts	0
Saw cuts / shared	3 / 1

PIECES (POSITION = BOTTOM-LEFT CORNER)

Label	Size	X, Y
GF-EX15 S01	322 x 2383	0, 724
GF-IL5 S01	722 x 2383	0, 0

NOTES

- Cut from OSB/3 9mm 1197x2397, 2mm saw kerf. Viewed on the face; dimensions from the sheet's bottom-left corner (0,0). Red numbered lines = saw cuts in order, each edge to edge.
- Coloured dimensions belong to the part of that colour: its width and height, and its position from the sheet edges. Raked parts: corner coordinates at each corner.
- Red hatch = waste. Labels = panel + piece mark on the manufacture drawing.

REVISIONS

REV	DATE	DESCRIPTION
C01	13.09.26	Construction issue



TLS TIMBER FRAME

Design & Manufacture

Scan: 3D model + drawings



CLIENT MP Adams	PROJECT MP Adams Plot 3, Eckington
--------------------	---------------------------------------


DRAWING TITLE OSB CUTTING - GROUND FLOOR - SHEET 28 OF 38

OSB/3 9mm 1197x2397 | Ground Floor

SCALE NTS	SIZE A3	DATE 13.09.26	DRAWN TS
--------------	------------	------------------	-------------

STATUS CONSTRUCTION	DRAWING No. P3-CP-OSB-01 / 28	REV C01
-------------------------------	---	-------------------

Do not scale. All dimensions in mm. Check all dimensions on site.

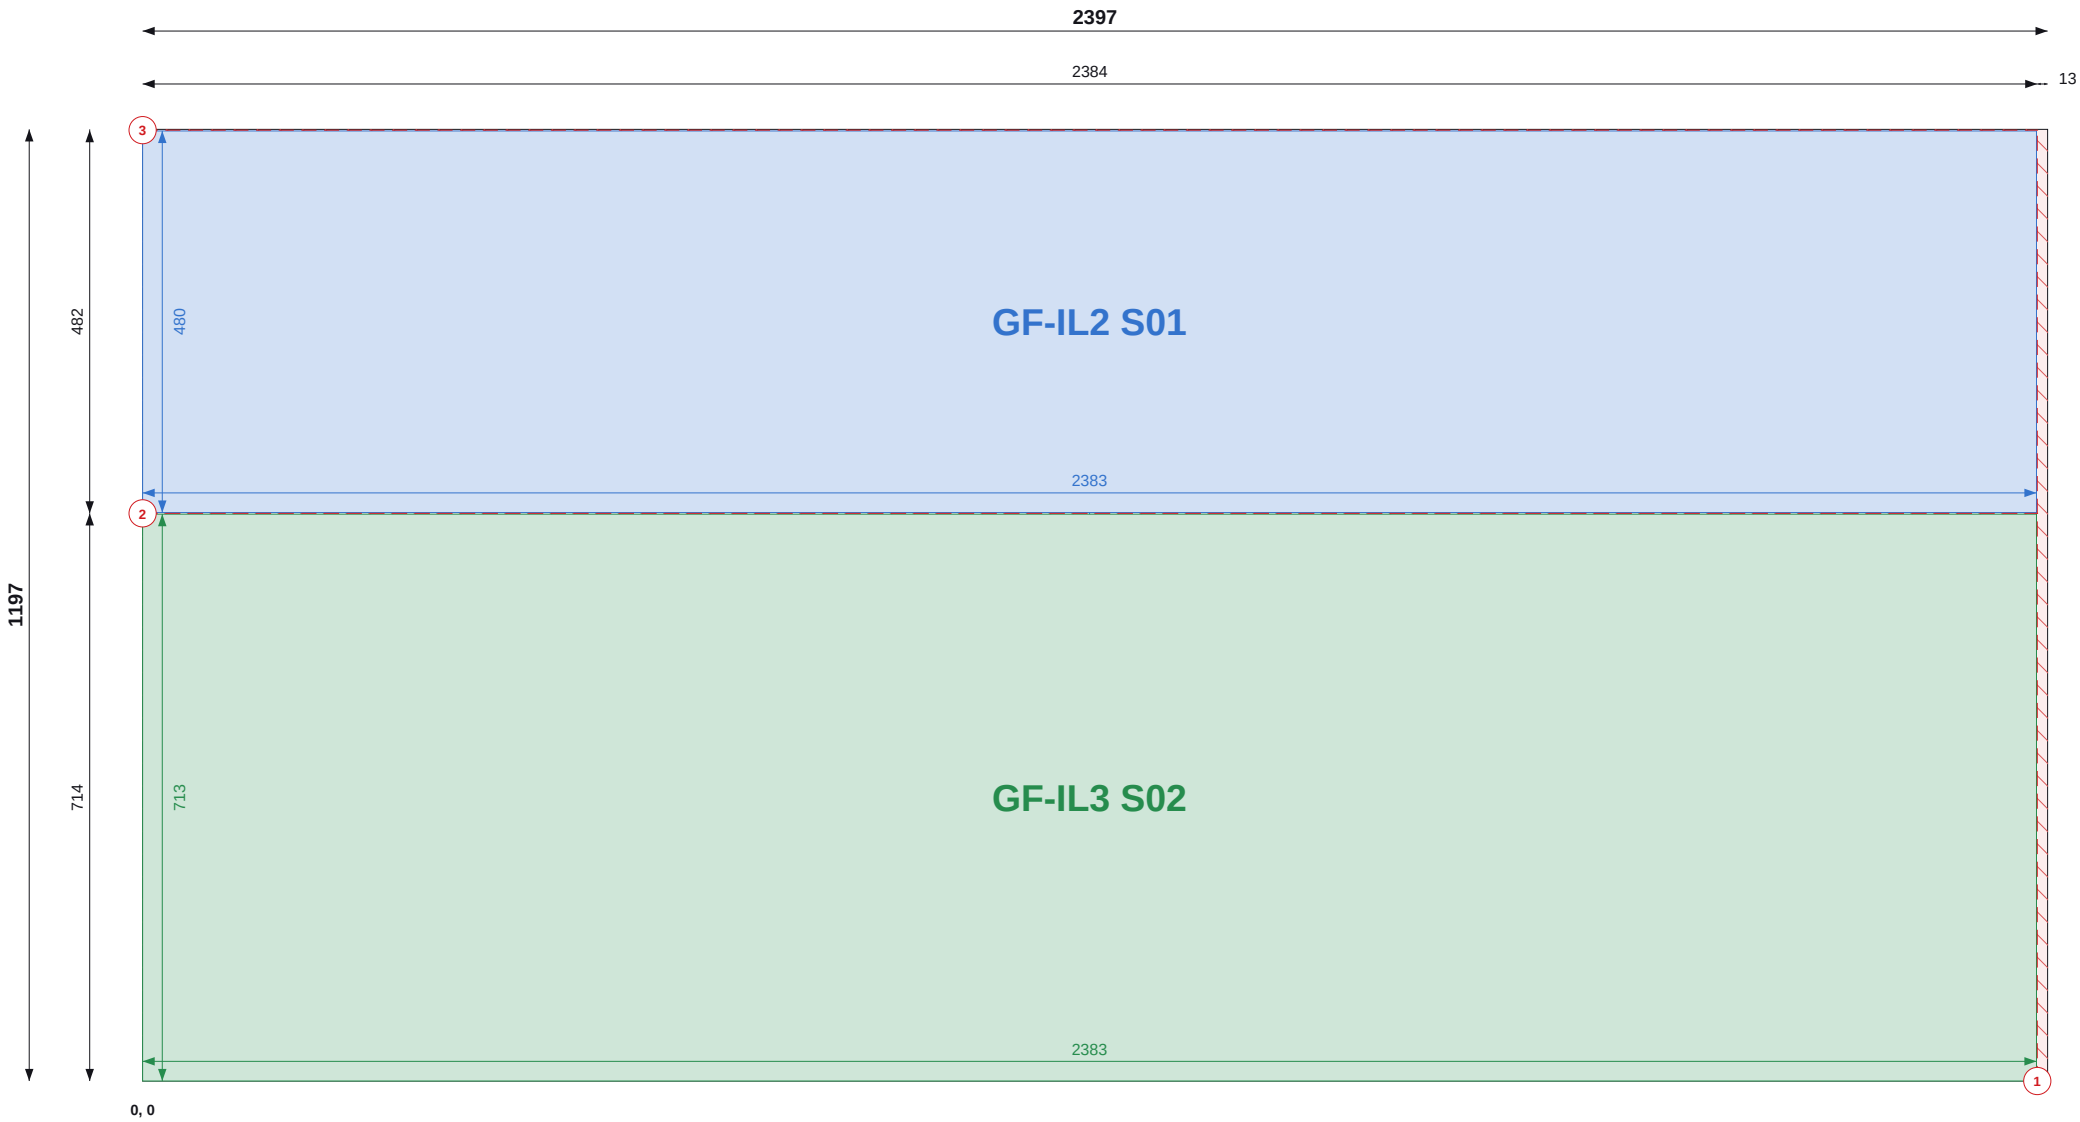

Top / left chains = saw cut positions (to cut centres). Coloured = part size and position.

SHEET 29 OF 38

THIS SHEET

Item	Value
Parts	2
Used / waste	99.1% / 0.03 m2
Reusable offcuts	0
Saw cuts / shared	3 / 1

PIECES (POSITION = BOTTOM-LEFT CORNER)

Label	Size	X, Y
GF-IL2 S01	480 x 2383	0, 715
GF-IL3 S02	713 x 2383	0, 0

NOTES

- Cut from OSB/3 9mm 1197x2397, 2mm saw kerf. Viewed on the face; dimensions from the sheet's bottom-left corner (0,0). Red numbered lines = saw cuts in order, each edge to edge.
- Coloured dimensions belong to the part of that colour: its width and height, and its position from the sheet edges. Raked parts: corner coordinates at each corner.
- Red hatch = waste. Labels = panel + piece mark on the manufacture drawing.

REVISIONS

REV	DATE	DESCRIPTION
C01	13.09.26	Construction issue



TLS TIMBER FRAME

Design & Manufacture

Scan: 3D model + drawings



CLIENT	PROJECT
MP Adams	MP Adams Plot 3, Eckington


DRAWING TITLE
OSB CUTTING - GROUND FLOOR - SHEET 29 OF 38

OSB/3 9mm 1197x2397 | Ground Floor

SCALE	SIZE	DATE	DRAWN
NTS	A3	13.09.26	TS

STATUS	DRAWING No.	REV
CONSTRUCTION	P3-CP-OSB-01 / 29	C01

Do not scale. All dimensions in mm. Check all dimensions on site.

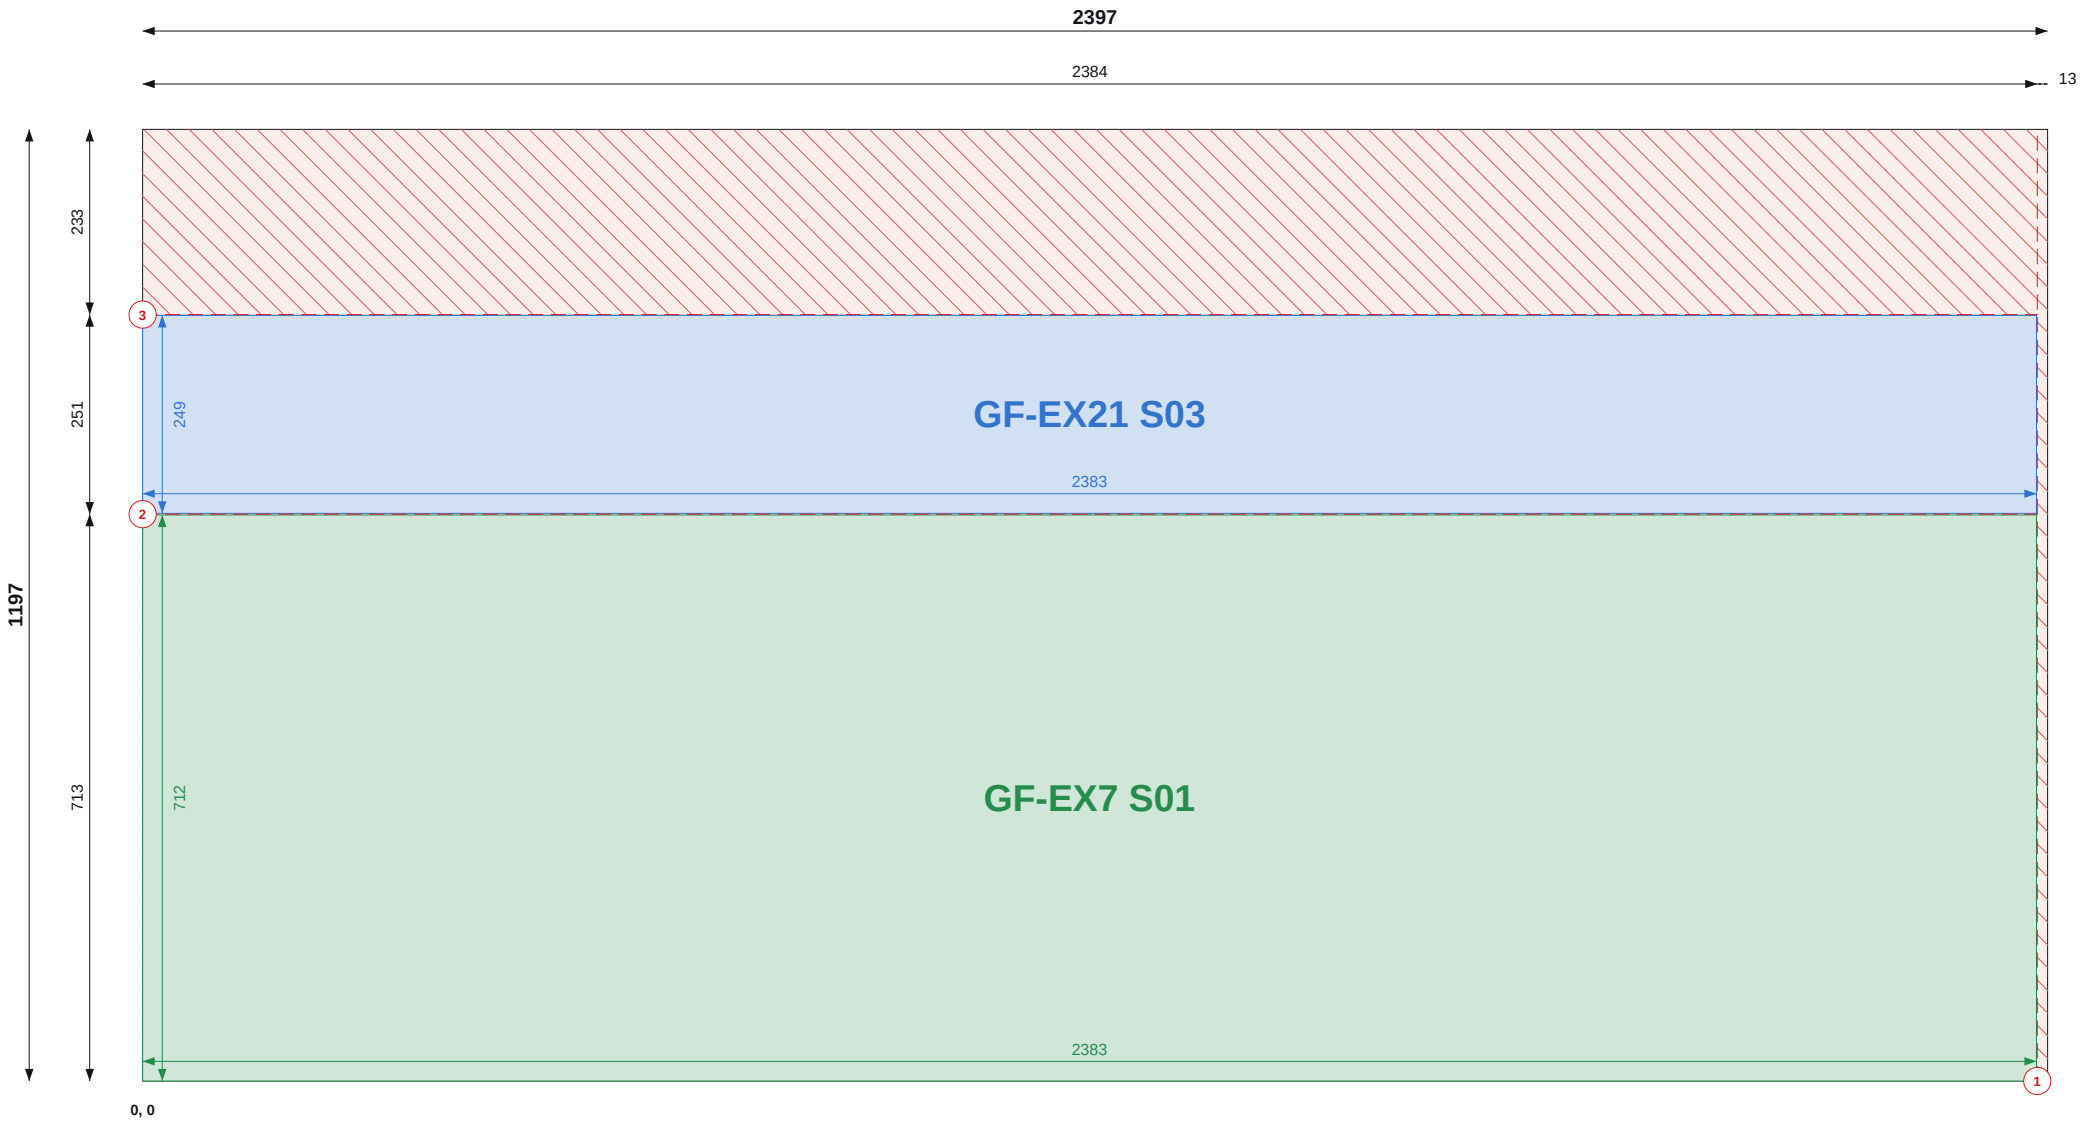

Top / left chains = saw cut positions (to cut centres). Coloured = part size and position.

SHEET 30 OF 38

THIS SHEET

Item	Value
Parts	2
Used / waste	79.8% / 0.58 m2
Reusable offcuts	0
Saw cuts / shared	3 / 1

PIECES (POSITION = BOTTOM-LEFT CORNER)

Label	Size	X, Y
GF-EX21 S03	249 x 2383	0, 714
GF-EX7 S01	712 x 2383	0, 0

NOTES

- Cut from OSB/3 9mm 1197x2397, 2mm saw kerf. Viewed on the face; dimensions from the sheet's bottom-left corner (0,0). Red numbered lines = saw cuts in order, each edge to edge.
- Coloured dimensions belong to the part of that colour: its width and height, and its position from the sheet edges. Raked parts: corner coordinates at each corner.
- Red hatch = waste. Labels = panel + piece mark on the manufacture drawing.

REVISIONS

REV	DATE	DESCRIPTION
C01	13.09.26	Construction issue



TLS TIMBER FRAME

Design & Manufacture

Scan: 3D model + drawings



CLIENT MP Adams	PROJECT MP Adams Plot 3, Eckington
--------------------	---------------------------------------


DRAWING TITLE OSB CUTTING - GROUND FLOOR - SHEET 30 OF 38

OSB/3 9mm 1197x2397 | Ground Floor

SCALE NTS	SIZE A3	DATE 13.09.26	DRAWN TS
--------------	------------	------------------	-------------

STATUS CONSTRUCTION	DRAWING No. P3-CP-OSB-01 / 30	REV C01
-------------------------------	---	-------------------

Do not scale. All dimensions in mm. Check all dimensions on site.

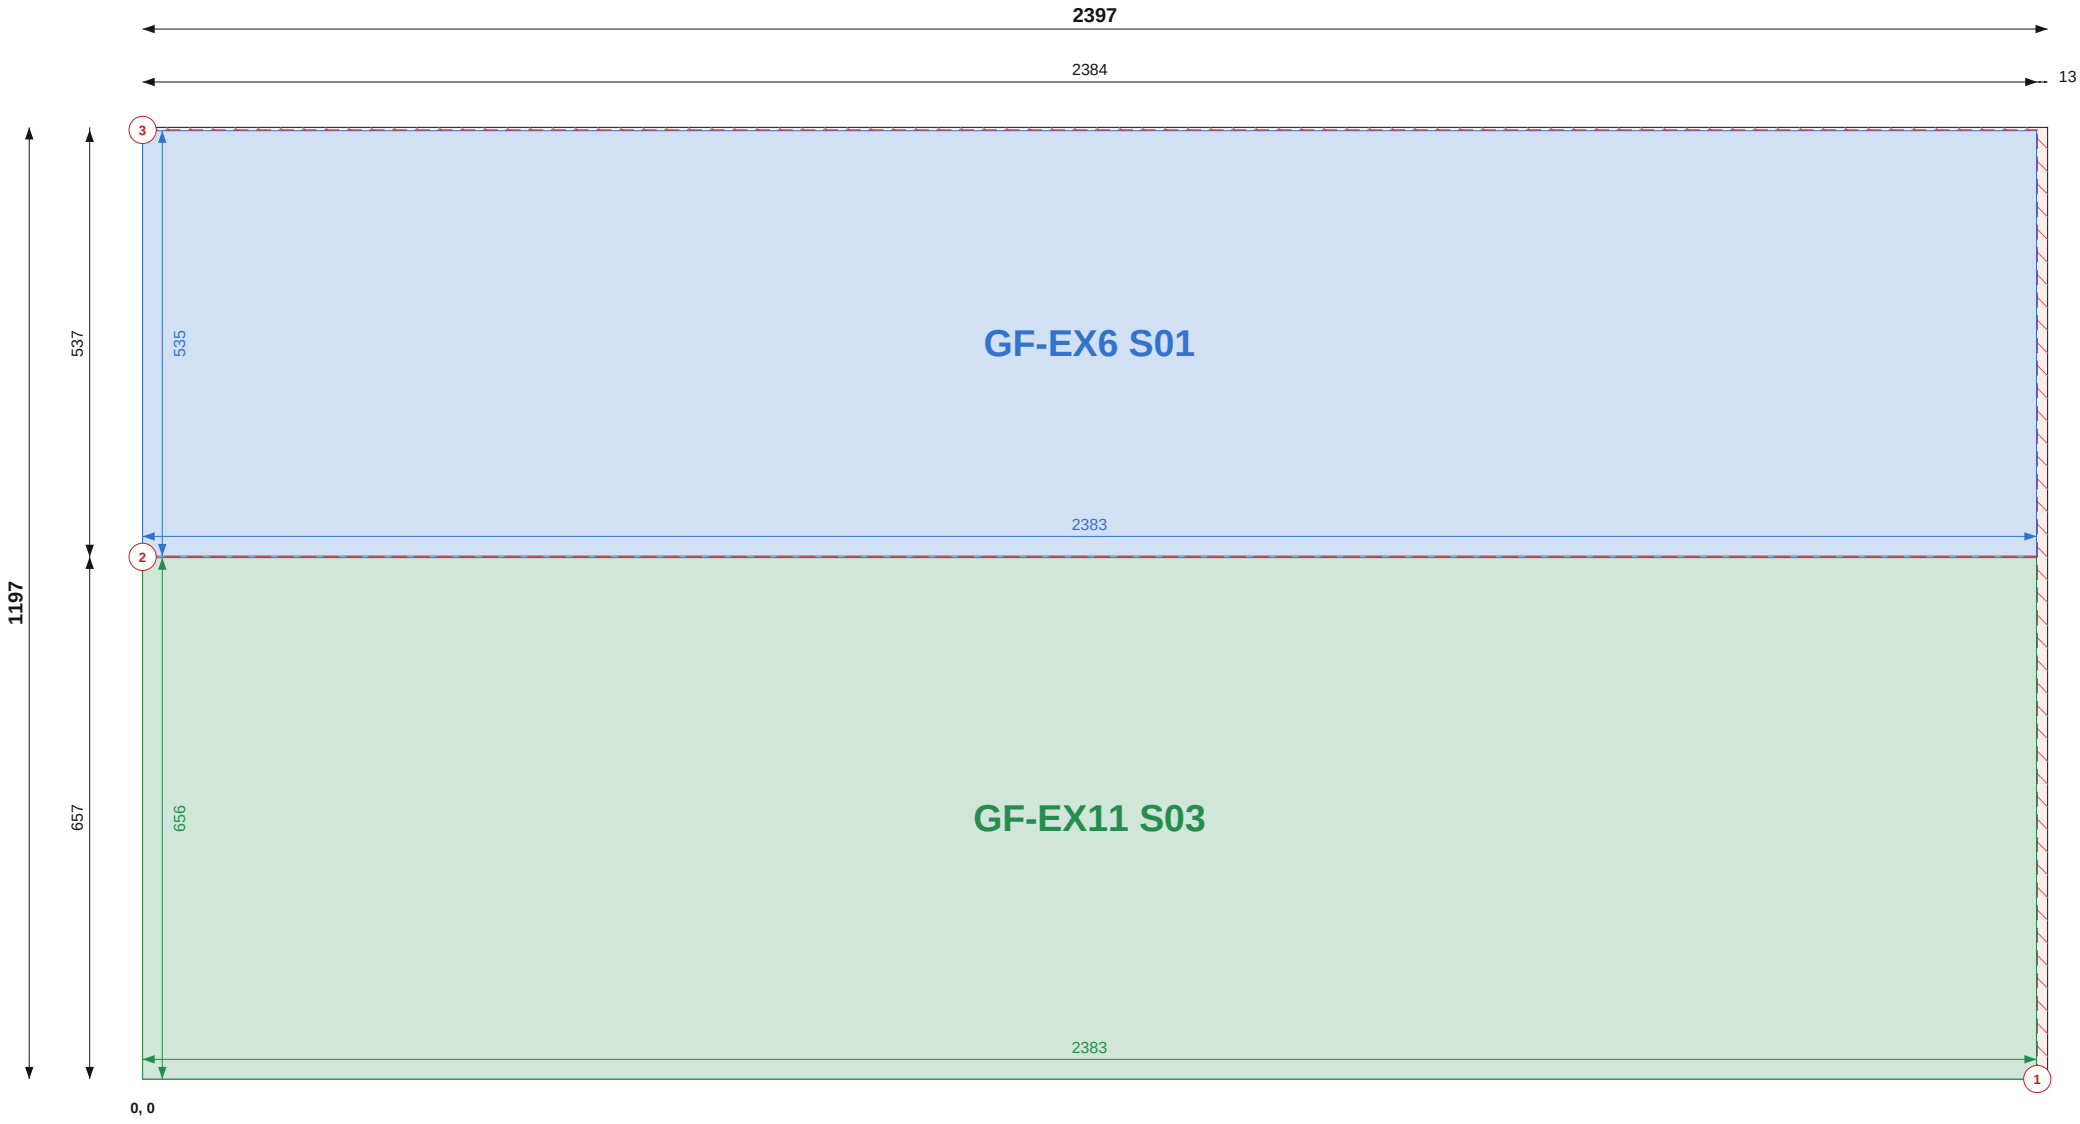

Top / left chains = saw cut positions (to cut centres). Coloured = part size and position.

SHEET 31 OF 38

THIS SHEET

Item	Value
Parts	2
Used / waste	98.9% / 0.03 m2
Reusable offcuts	0
Saw cuts / shared	3 / 1

PIECES (POSITION = BOTTOM-LEFT CORNER)

Label	Size	X, Y
GF-EX6 S01	535 x 2383	0, 658
GF-EX11 S03	656 x 2383	0, 0

NOTES

- Cut from OSB/3 9mm 1197x2397, 2mm saw kerf. Viewed on the face; dimensions from the sheet's bottom-left corner (0,0). Red numbered lines = saw cuts in order, each edge to edge.
- Coloured dimensions belong to the part of that colour: its width and height, and its position from the sheet edges. Raked parts: corner coordinates at each corner.
- Red hatch = waste. Labels = panel + piece mark on the manufacture drawing.

REVISIONS

REV	DATE	DESCRIPTION
C01	13.09.26	Construction issue



TLS TIMBER FRAME
Design & Manufacture
Scan: 3D model + drawings



CLIENT	PROJECT
MP Adams	MP Adams Plot 3, Eckington

DRAWING TITLE


OSB CUTTING - GROUND FLOOR - SHEET 31 OF 38

OSB/3 9mm 1197x2397 | Ground Floor

SCALE	SIZE	DATE	DRAWN
NTS	A3	13.09.26	TS

STATUS	DRAWING No.	REV
CONSTRUCTION	P3-CP-OSB-01 / 31	C01

Do not scale. All dimensions in mm. Check all dimensions on site.

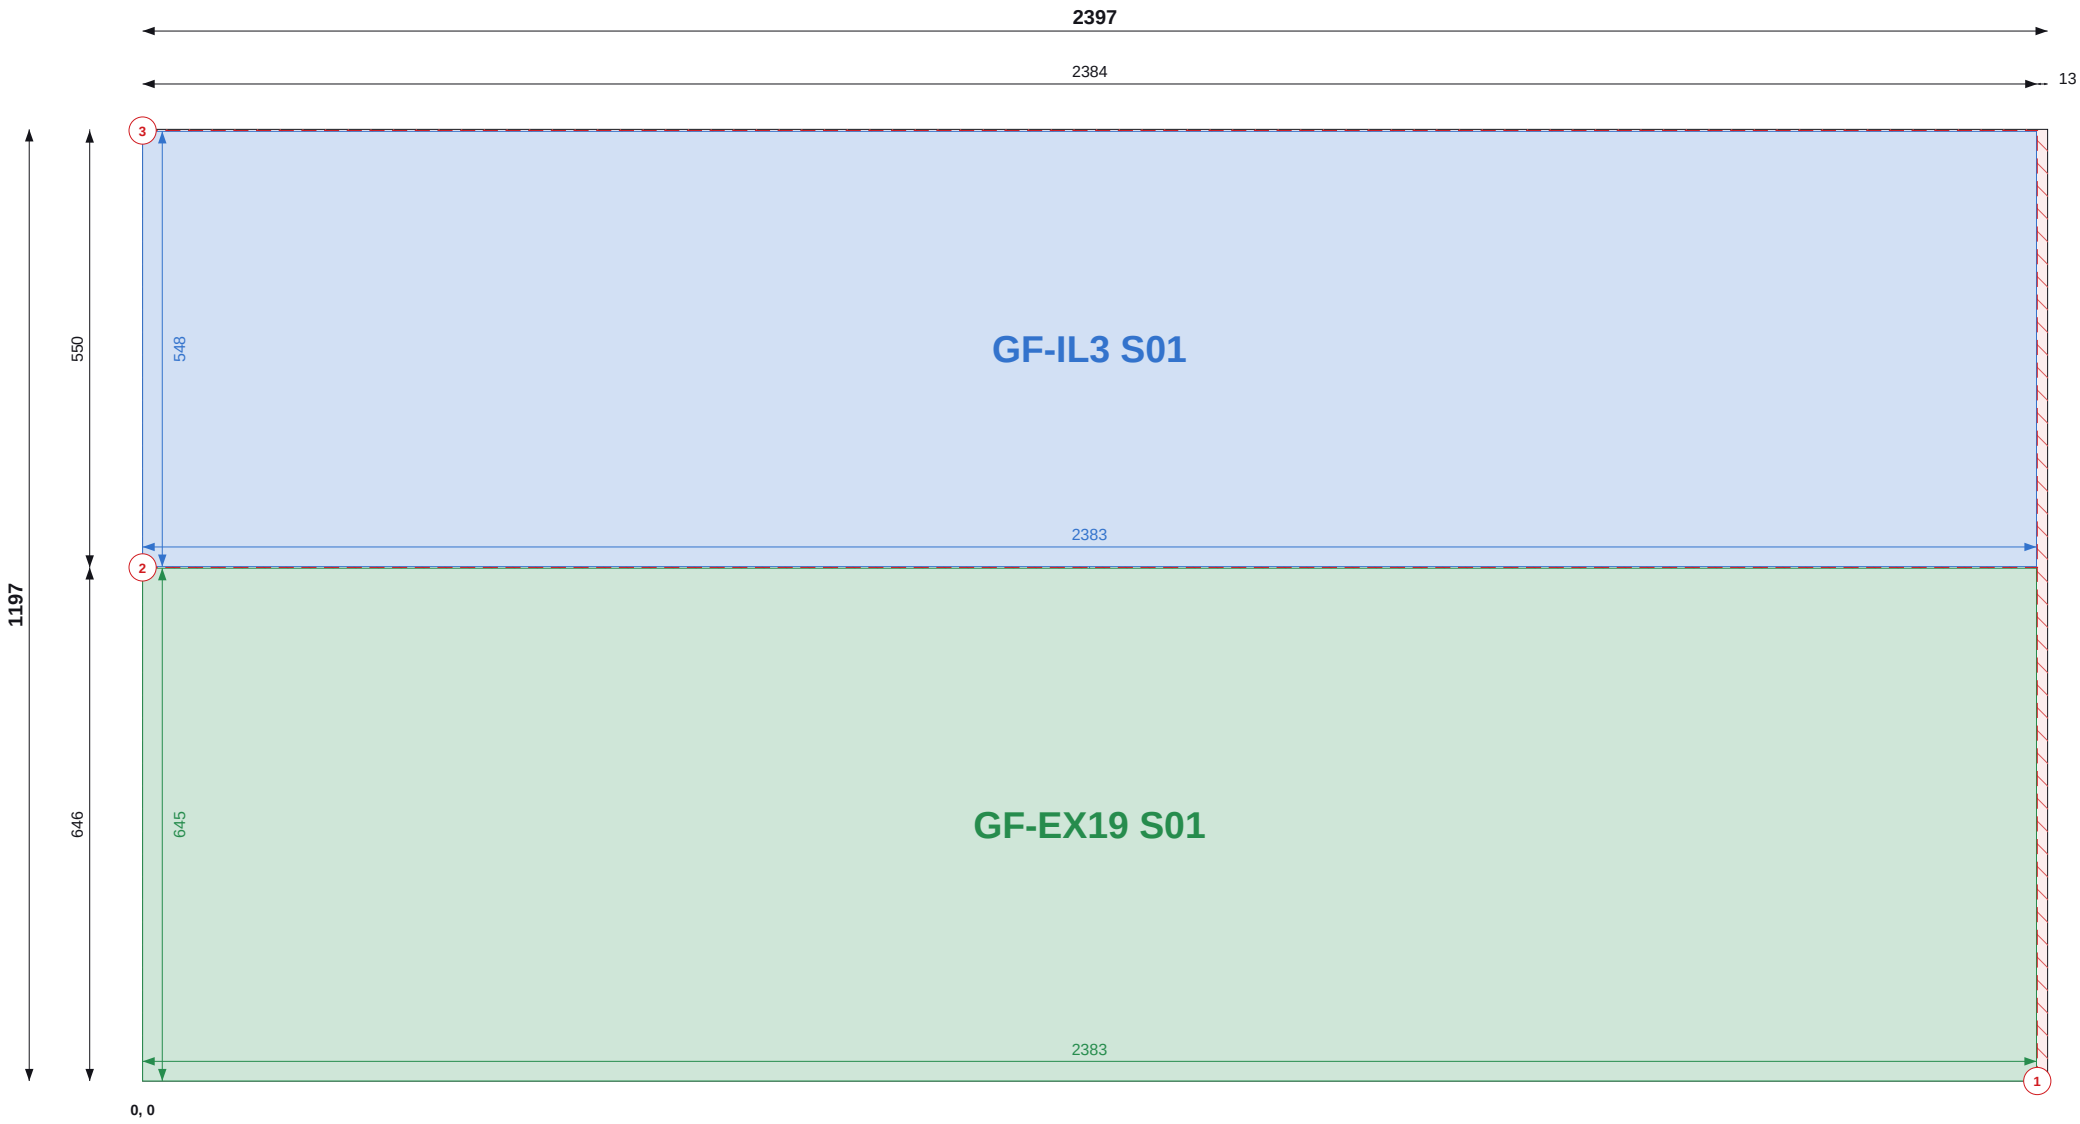

Top / left chains = saw cut positions (to cut centres). Coloured = part size and position.

SHEET 32 OF 38

THIS SHEET

Item	Value
Parts	2
Used / waste	99.0% / 0.03 m2
Reusable offcuts	0
Saw cuts / shared	3 / 1

PIECES (POSITION = BOTTOM-LEFT CORNER)

Label	Size	X, Y
GF-IL3 S01	548 x 2383	0, 647
GF-EX19 S01	645 x 2383	0, 0

NOTES

- Cut from OSB/3 9mm 1197x2397, 2mm saw kerf. Viewed on the face; dimensions from the sheet's bottom-left corner (0,0). Red numbered lines = saw cuts in order, each edge to edge.
- Coloured dimensions belong to the part of that colour: its width and height, and its position from the sheet edges. Raked parts: corner coordinates at each corner.
- Red hatch = waste. Labels = panel + piece mark on the manufacture drawing.

REVISIONS

REV	DATE	DESCRIPTION
C01	13.09.26	Construction issue



TLS TIMBER FRAME

Design & Manufacture

Scan: 3D model + drawings



CLIENT	PROJECT
MP Adams	MP Adams Plot 3, Eckington


DRAWING TITLE
OSB CUTTING - GROUND FLOOR - SHEET 32 OF 38

OSB/3 9mm 1197x2397 | Ground Floor

SCALE	SIZE	DATE	DRAWN
NTS	A3	13.09.26	TS

STATUS	DRAWING No.	REV
CONSTRUCTION	P3-CP-OSB-01 / 32	C01

Do not scale. All dimensions in mm. Check all dimensions on site.

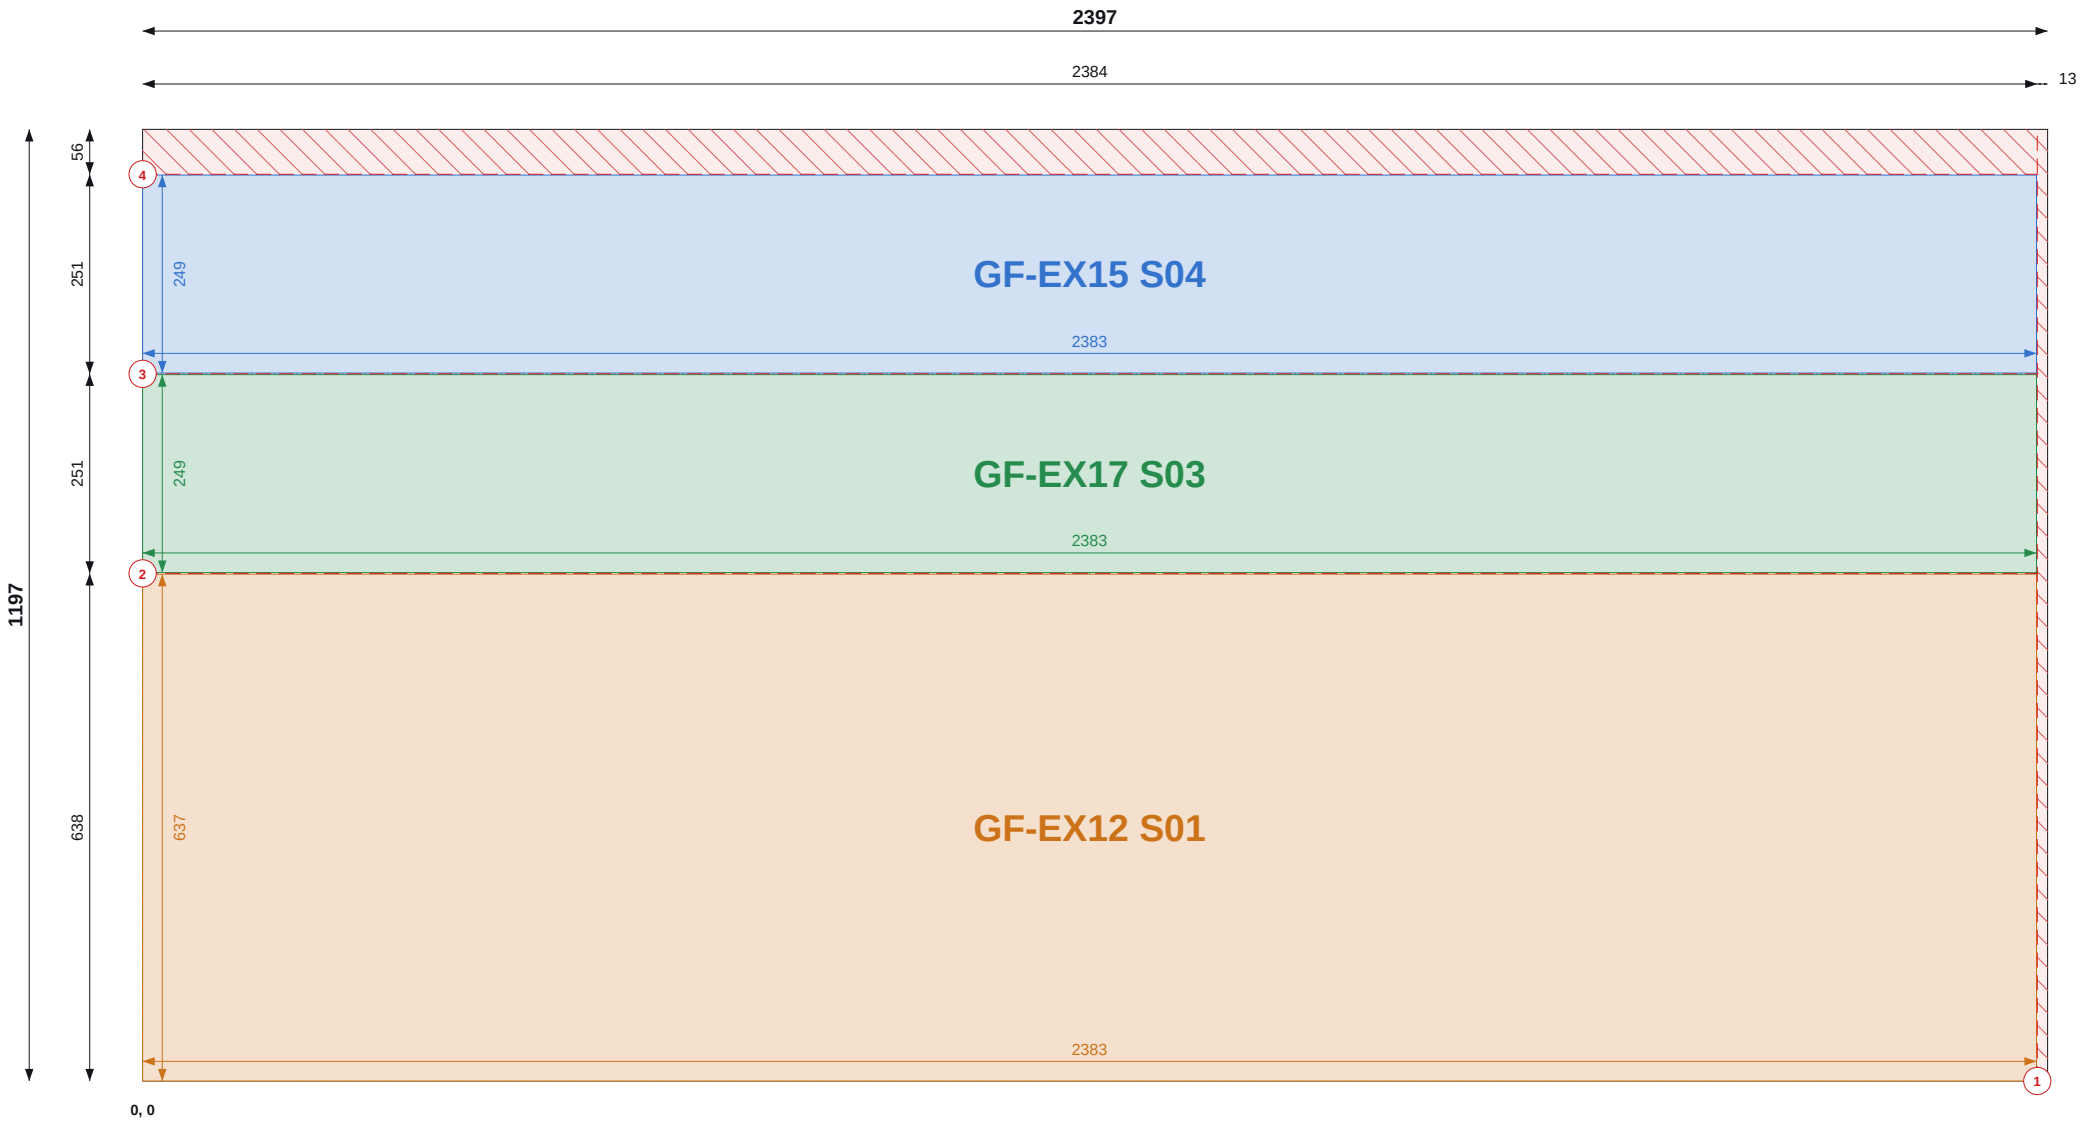

SHEET 33 OF 38

THIS SHEET

Item	Value
Parts	3
Used / waste	94.3% / 0.16 m2
Reusable offcuts	0
Saw cuts / shared	4 / 2

PIECES (POSITION = BOTTOM-LEFT CORNER)

Label	Size	X, Y
GF-EX15 S04	249 x 2383	0, 890
GF-EX17 S03	249 x 2383	0, 639
GF-EX12 S01	637 x 2383	0, 0

NOTES

- Cut from OSB/3 9mm 1197x2397, 2mm saw kerf. Viewed on the face; dimensions from the sheet's bottom-left corner (0,0). Red numbered lines = saw cuts in order, each edge to edge.
- Coloured dimensions belong to the part of that colour: its width and height, and its position from the sheet edges. Raked parts: corner coordinates at each corner.
- Red hatch = waste. Labels = panel + piece mark on the manufacture drawing.

REVISIONS

REV	DATE	DESCRIPTION
C01	13.09.26	Construction issue



TLS TIMBER FRAME

Design & Manufacture

Scan: 3D model + drawings



CLIENT	PROJECT
MP Adams	MP Adams Plot 3, Eckington


DRAWING TITLE
OSB CUTTING - GROUND FLOOR - SHEET 33 OF 38

OSB/3 9mm 1197x2397 | Ground Floor

SCALE	SIZE	DATE	DRAWN
NTS	A3	13.09.26	TS

STATUS	DRAWING No.	REV
CONSTRUCTION	P3-CP-OSB-01 / 33	C01

Do not scale. All dimensions in mm. Check all dimensions on site.

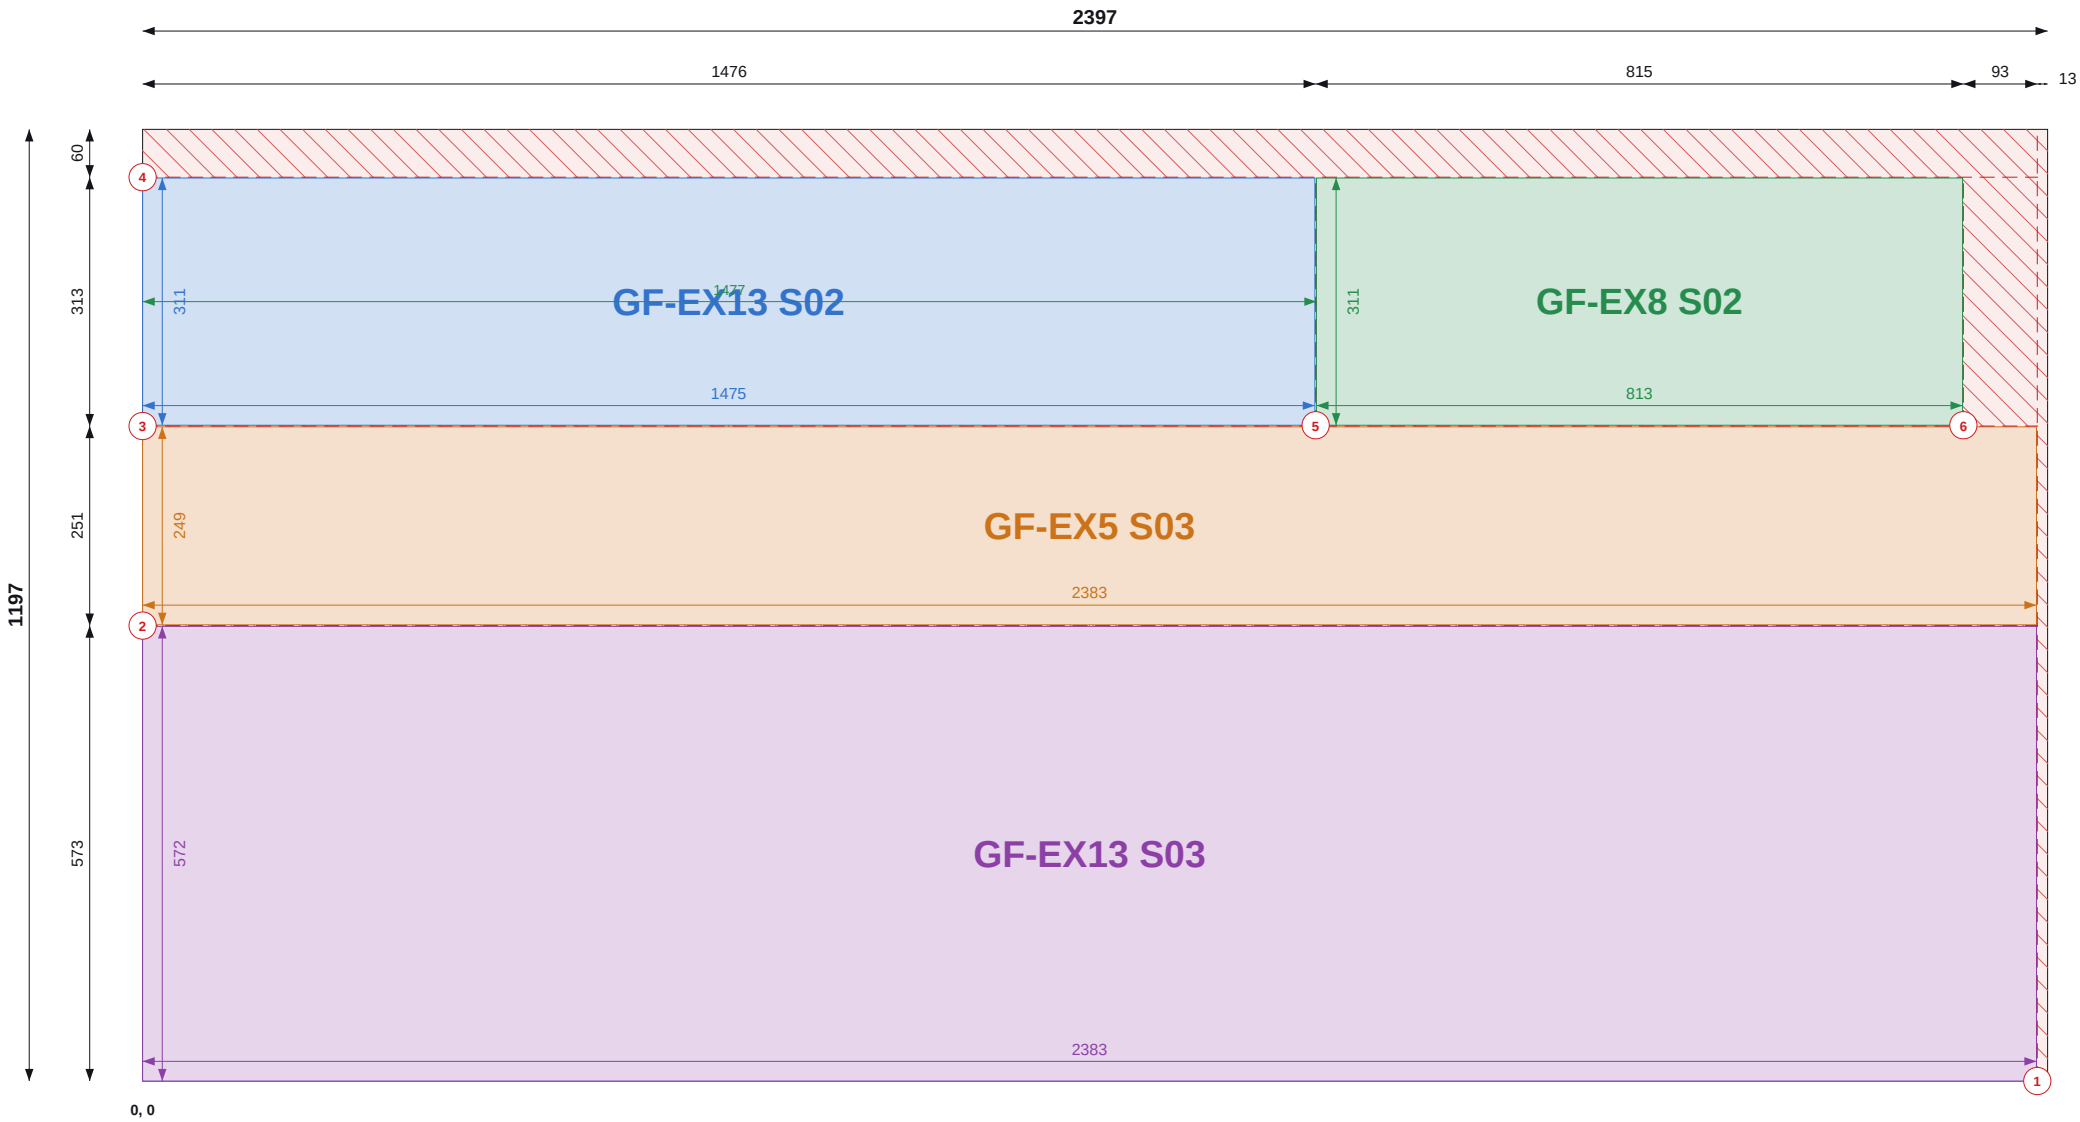

Top / left chains = saw cut positions (to cut centres). Coloured = part size and position.

SHEET 34 OF 38

THIS SHEET

Item	Value
Parts	4
Used / waste	93.0% / 0.20 m2
Reusable offcuts	0
Saw cuts / shared	6 / 3

PIECES (POSITION = BOTTOM-LEFT CORNER)

Label	Size	X, Y
GF-EX13 S02	1475 x 311	0, 825
GF-EX8 S02	813 x 311	1477, 825
GF-EX5 S03	249 x 2383	0, 574
GF-EX13 S03	572 x 2383	0, 0

NOTES

- Cut from OSB/3 9mm 1197x2397, 2mm saw kerf. Viewed on the face; dimensions from the sheet's bottom-left corner (0,0). Red numbered lines = saw cuts in order, each edge to edge.
- Coloured dimensions belong to the part of that colour: its width and height, and its position from the sheet edges. Raked parts: corner coordinates at each corner.
- Red hatch = waste. Labels = panel + piece mark on the manufacture drawing.

REVISIONS

REV	DATE	DESCRIPTION
C01	13.09.26	Construction issue



TLS TIMBER FRAME

Design & Manufacture

Scan: 3D model + drawings



CLIENT	PROJECT
MP Adams	MP Adams Plot 3, Eckington


DRAWING TITLE
OSB CUTTING - GROUND FLOOR - SHEET 34 OF 38

OSB/3 9mm 1197x2397 | Ground Floor

SCALE	SIZE	DATE	DRAWN
NTS	A3	13.09.26	TS

STATUS	DRAWING No.	REV
CONSTRUCTION	P3-CP-OSB-01 / 34	C01

Do not scale. All dimensions in mm. Check all dimensions on site.

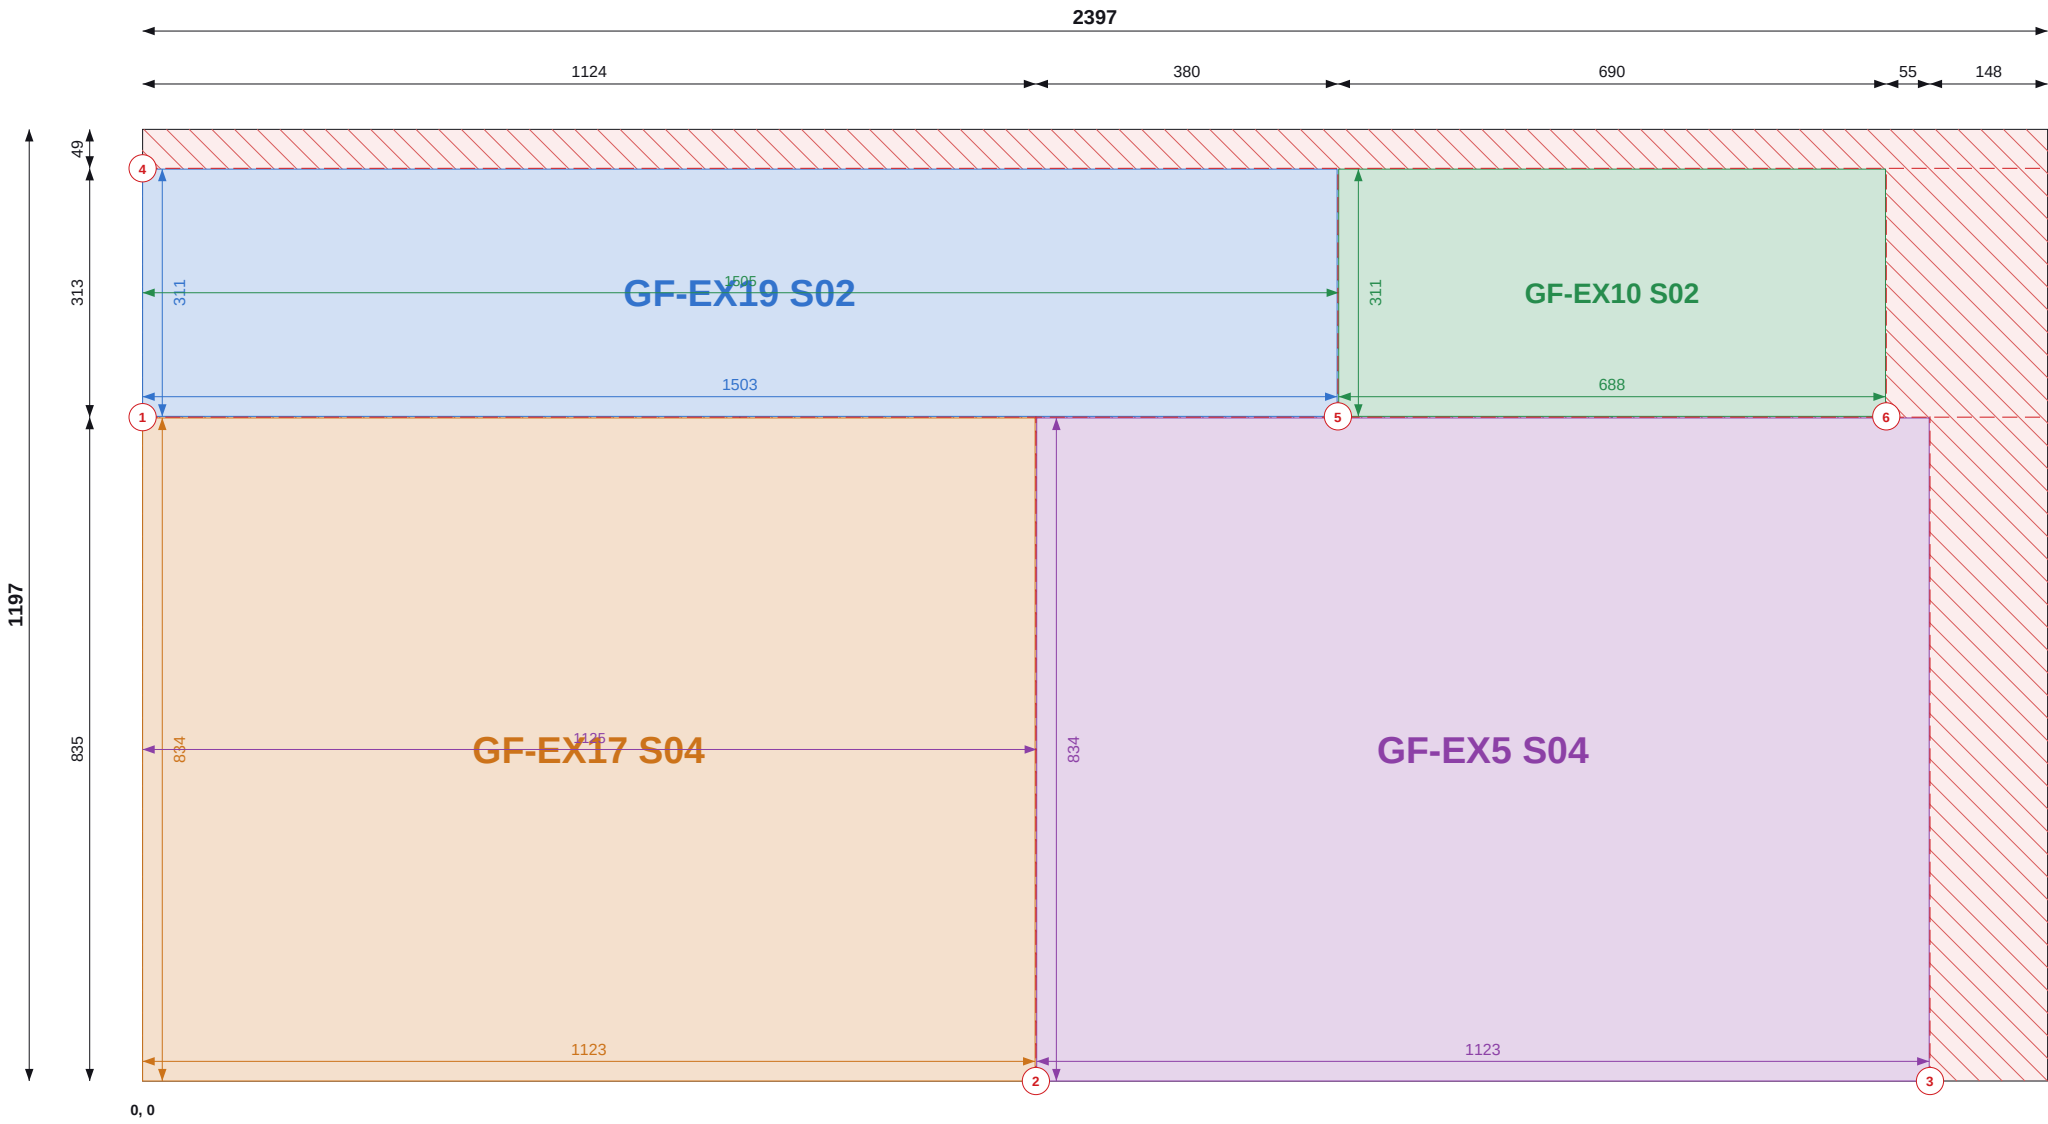

Top / left chains = saw cut positions (to cut centres). Coloured = part size and position.

SHEET 35 OF 38

THIS SHEET

Item	Value
Parts	4
Used / waste	89.0% / 0.31 m2
Reusable offcuts	0
Saw cuts / shared	6 / 3

PIECES (POSITION = BOTTOM-LEFT CORNER)

Label	Size	X, Y
GF-EX19 S02	1503 x 311	0, 836
GF-EX10 S02	688 x 311	1505, 836
GF-EX17 S04	1123 x 834	0, 0
GF-EX5 S04	1123 x 834	1125, 0

NOTES

- Cut from OSB/3 9mm 1197x2397, 2mm saw kerf. Viewed on the face; dimensions from the sheet's bottom-left corner (0,0). Red numbered lines = saw cuts in order, each edge to edge.
- Coloured dimensions belong to the part of that colour: its width and height, and its position from the sheet edges. Raked parts: corner coordinates at each corner.
- Red hatch = waste. Labels = panel + piece mark on the manufacture drawing.

REVISIONS

REV	DATE	DESCRIPTION
C01	13.09.26	Construction issue



TLS TIMBER FRAME

Design & Manufacture

Scan: 3D model + drawings



CLIENT	PROJECT
MP Adams	MP Adams Plot 3, Eckington


DRAWING TITLE
OSB CUTTING - GROUND FLOOR - SHEET 35 OF 38

OSB/3 9mm 1197x2397 | Ground Floor

SCALE	SIZE	DATE	DRAWN
NTS	A3	13.09.26	TS

STATUS	DRAWING No.	REV
CONSTRUCTION	P3-CP-OSB-01 / 35	C01

Do not scale. All dimensions in mm. Check all dimensions on site.

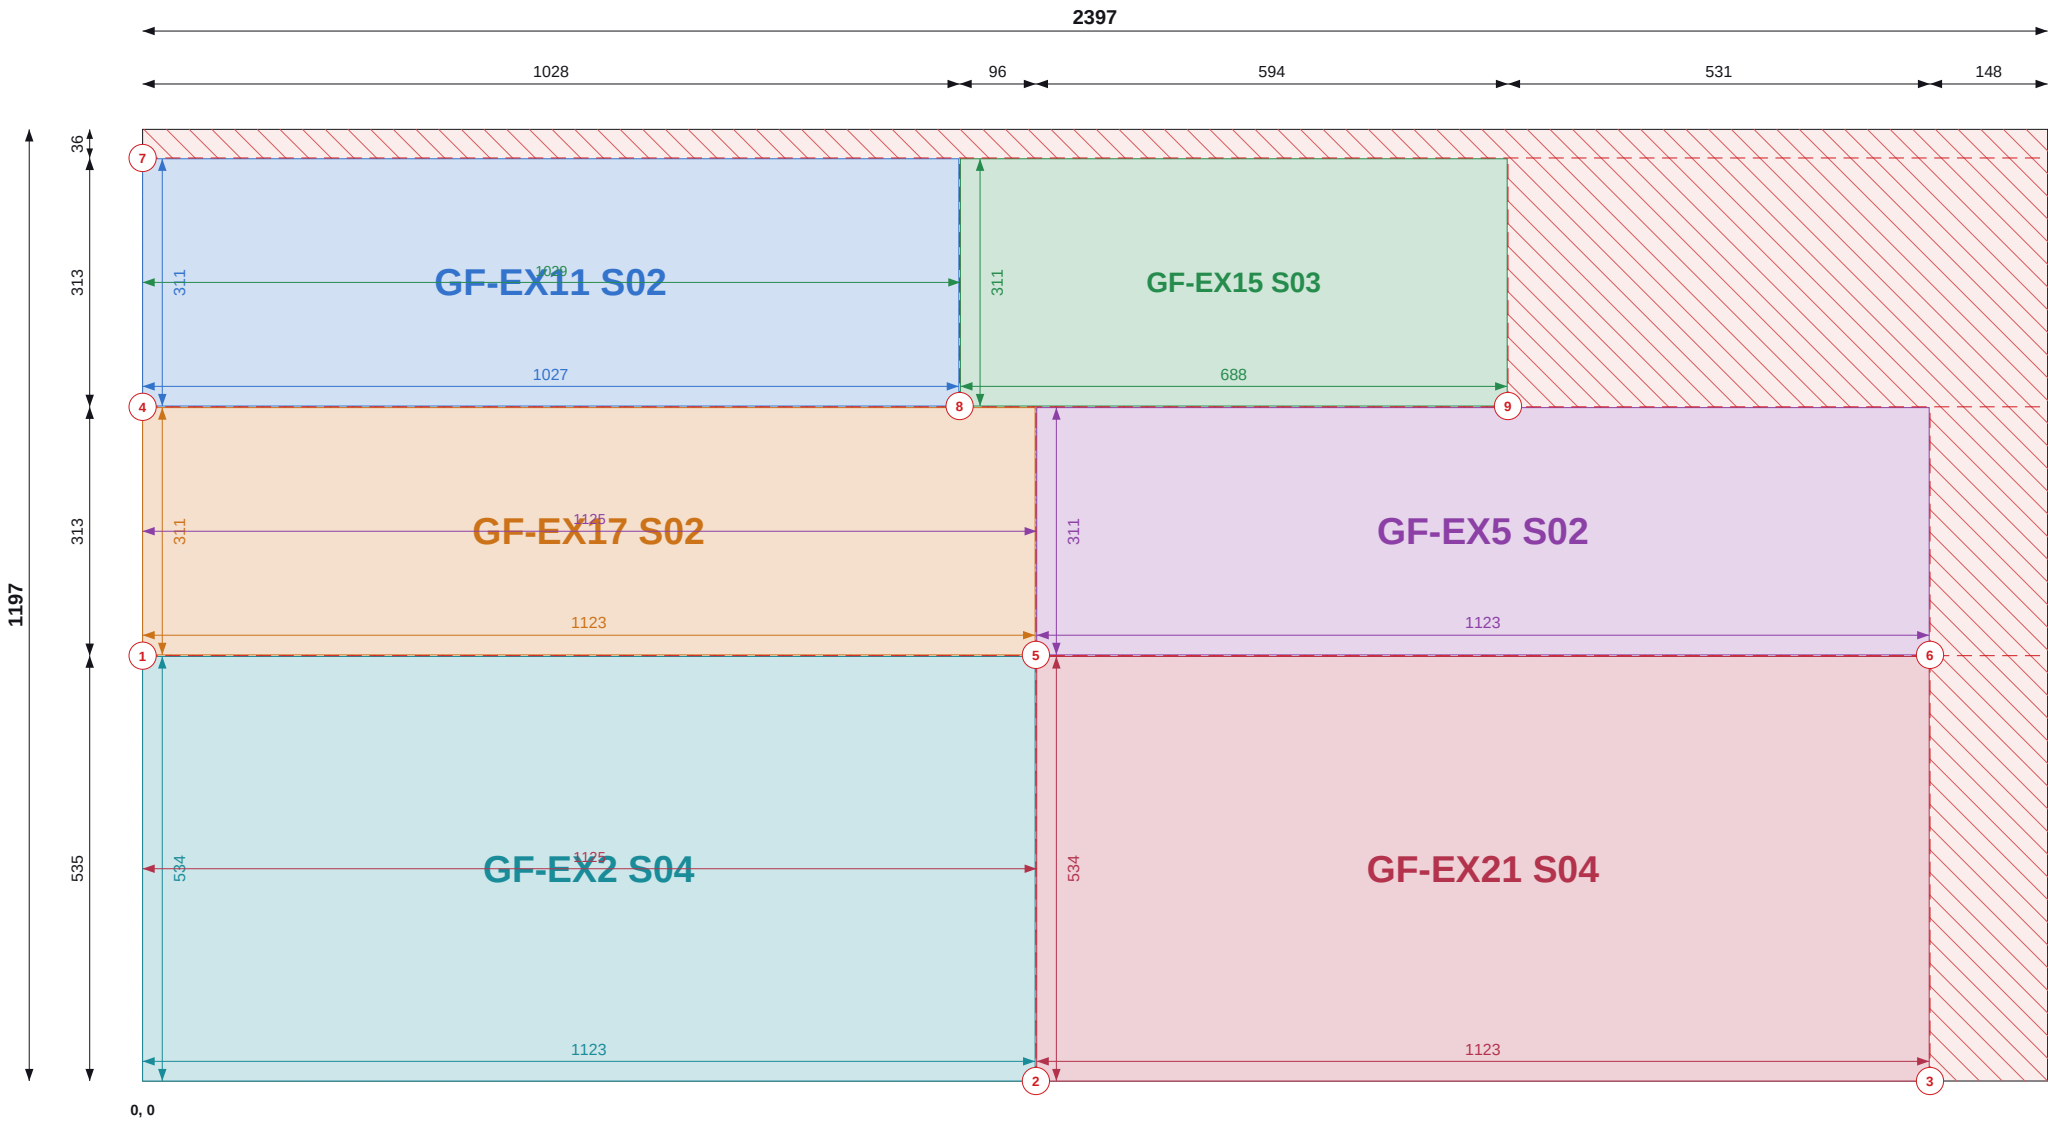

Top / left chains = saw cut positions (to cut centres). Coloured = part size and position.

SHEET 36 OF 38

THIS SHEET

Item	Value
Parts	6
Used / waste	84.7% / 0.44 m2
Reusable offcuts	1
Saw cuts / shared	9 / 5

PIECES (POSITION = BOTTOM-LEFT CORNER)

Label	Size	X, Y
GF-EX11 S02	1027 x 311	0, 849
GF-EX15 S03	688 x 311	1029, 849
GF-EX17 S02	1123 x 311	0, 536
GF-EX5 S02	1123 x 311	1125, 536
GF-EX2 S04	1123 x 534	0, 0
GF-EX21 S04	1123 x 534	1125, 0

NOTES

- Cut from OSB/3 9mm 1197x2397, 2mm saw kerf. Viewed on the face; dimensions from the sheet's bottom-left corner (0,0). Red numbered lines = saw cuts in order, each edge to edge.
- Coloured dimensions belong to the part of that colour: its width and height, and its position from the sheet edges. Raked parts: corner coordinates at each corner.
- Red hatch = waste. Labels = panel + piece mark on the manufacture drawing.

REVISIONS

REV	DATE	DESCRIPTION
C01	13.09.26	Construction issue



TLS TIMBER FRAME

Design & Manufacture

Scan: 3D model + drawings



CLIENT MP Adams	PROJECT MP Adams Plot 3, Eckington
--------------------	---------------------------------------


DRAWING TITLE
OSB CUTTING - GROUND FLOOR - SHEET 36 OF 38

OSB/3 9mm 1197x2397 | Ground Floor

SCALE NTS	SIZE A3	DATE 13.09.26	DRAWN TS
--------------	------------	------------------	-------------

STATUS CONSTRUCTION	DRAWING No. P3-CP-OSB-01 / 36	REV C01
-------------------------------	---	-------------------

Do not scale. All dimensions in mm. Check all dimensions on site.

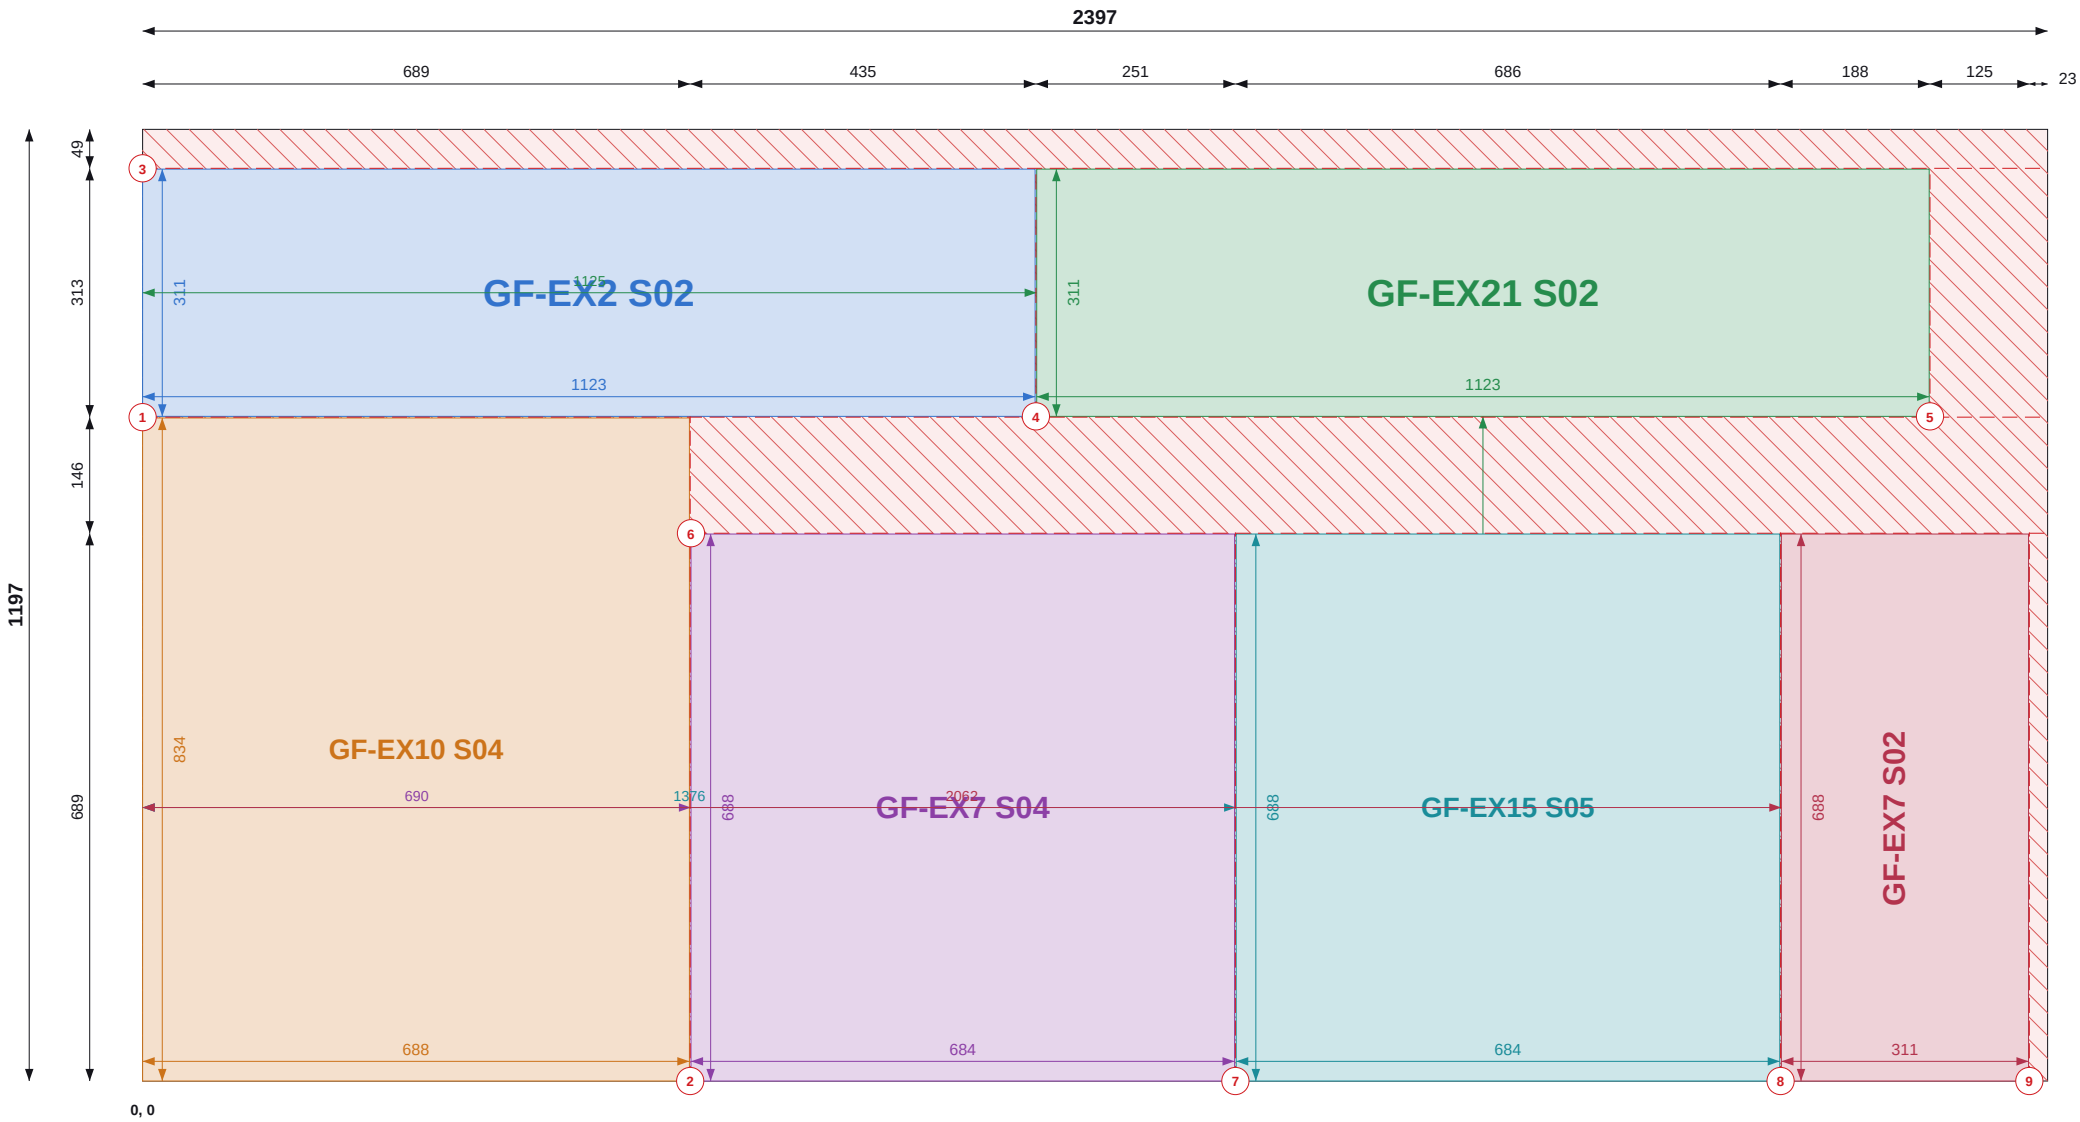

Top / left chains = saw cut positions (to cut centres). Coloured = part size and position.

SHEET 37 OF 38

THIS SHEET

Item	Value
Parts	6
Used / waste	84.6% / 0.44 m2
Reusable offcuts	0
Saw cuts / shared	9 / 5

PIECES (POSITION = BOTTOM-LEFT CORNER)

Label	Size	X, Y
GF-EX2 S02	1123 x 311	0, 836
GF-EX21 S02	1123 x 311	1125, 836
GF-EX10 S04	688 x 834	0, 0
GF-EX7 S04	688 x 684	690, 0
GF-EX15 S05	688 x 684	1376, 0
GF-EX7 S02	688 x 311	2062, 0

NOTES

- Cut from OSB/3 9mm 1197x2397, 2mm saw kerf. Viewed on the face; dimensions from the sheet's bottom-left corner (0,0). Red numbered lines = saw cuts in order, each edge to edge.
- Coloured dimensions belong to the part of that colour: its width and height, and its position from the sheet edges. Raked parts: corner coordinates at each corner.
- Red hatch = waste. Labels = panel + piece mark on the manufacture drawing.

REVISIONS

REV	DATE	DESCRIPTION
C01	13.09.26	Construction issue



TLS TIMBER FRAME

Design & Manufacture

Scan: 3D model + drawings



CLIENT	PROJECT
MP Adams	MP Adams Plot 3, Eckington

DRAWING TITLE


OSB CUTTING - GROUND FLOOR - SHEET 37 OF 38

OSB/3 9mm 1197x2397 | Ground Floor

SCALE	SIZE	DATE	DRAWN
NTS	A3	13.09.26	TS

STATUS	DRAWING No.	REV
CONSTRUCTION	P3-CP-OSB-01 / 37	C01

Do not scale. All dimensions in mm. Check all dimensions on site.

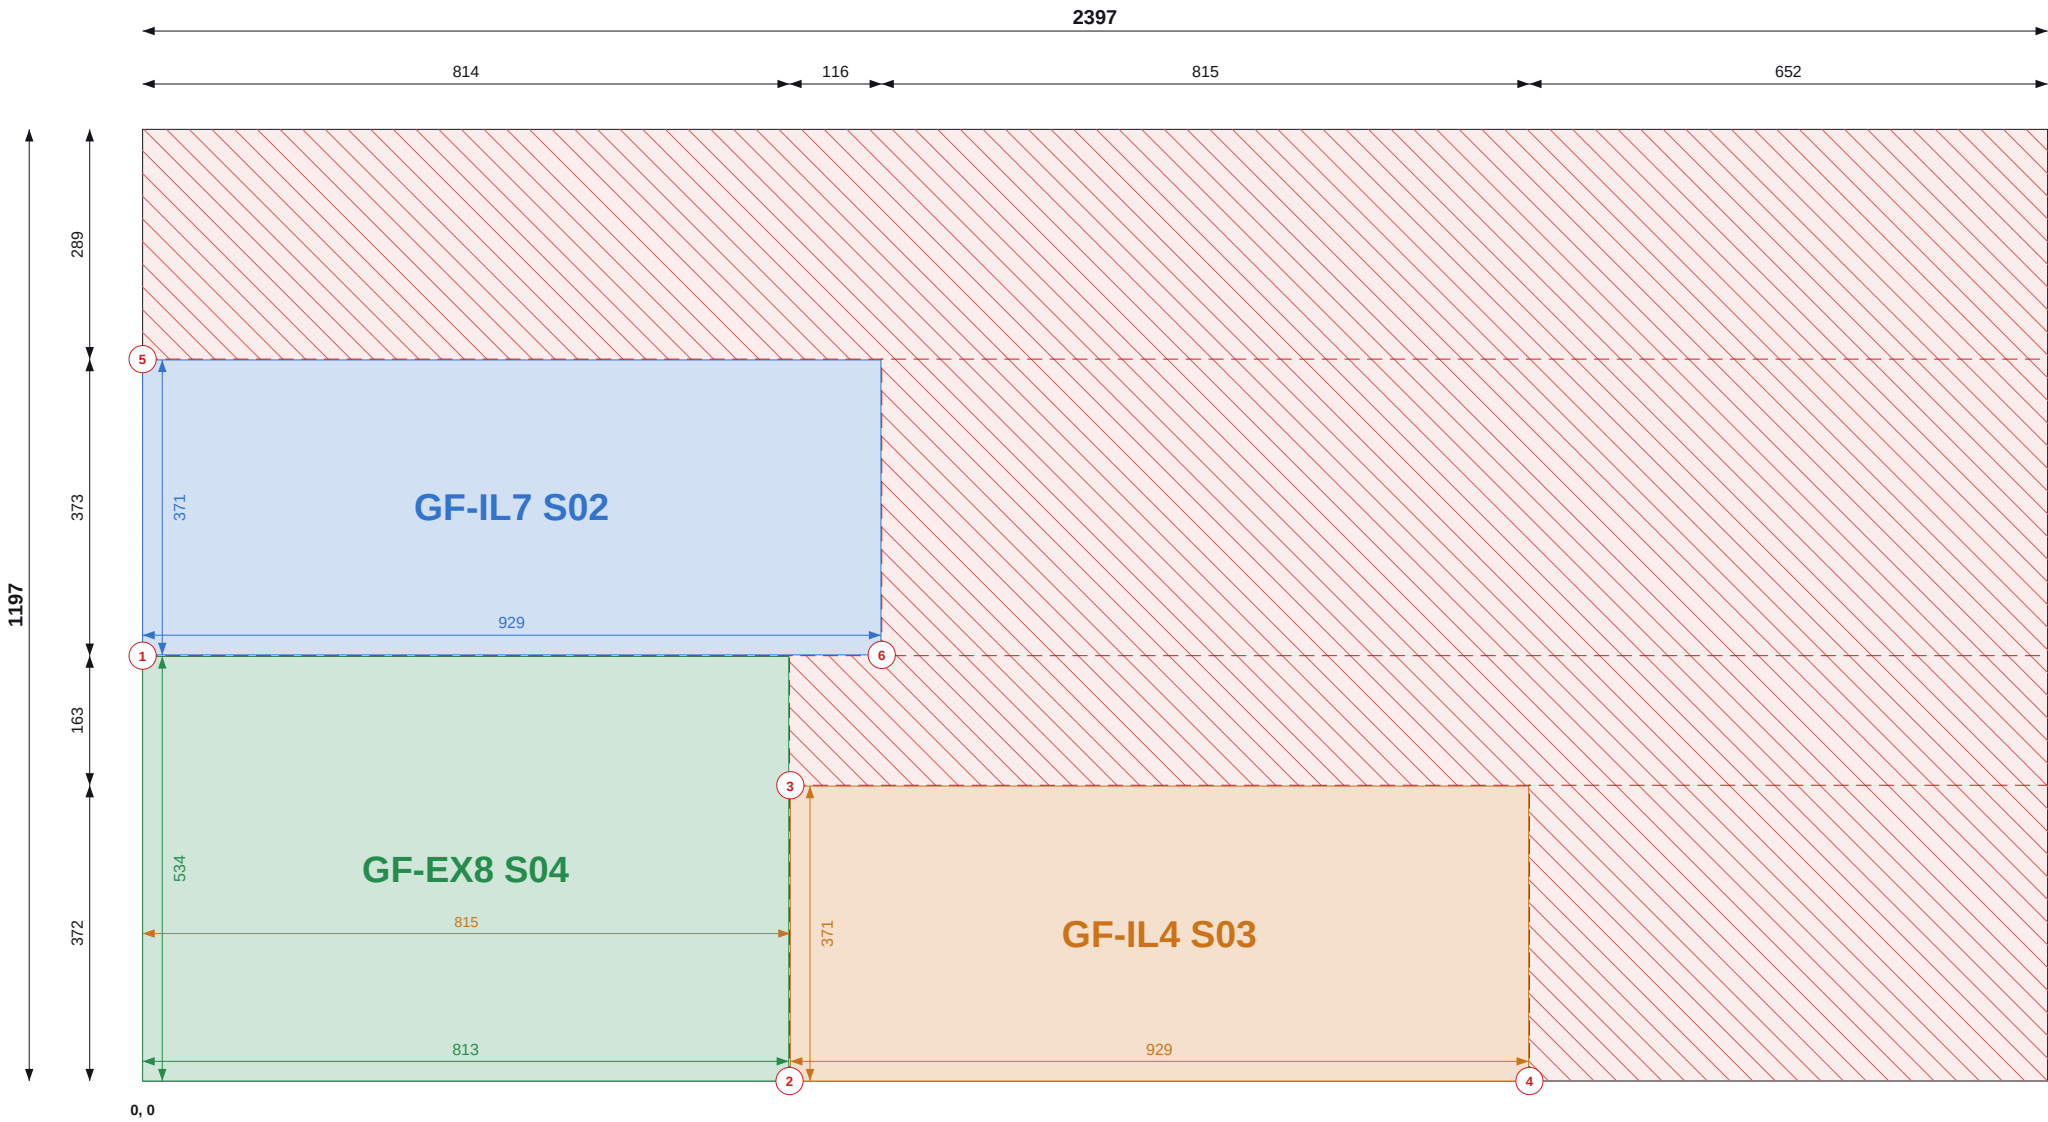

SHEET 38 OF 38

THIS SHEET

Item	Value
Parts	3
Used / waste	39.2% / 1.75 m2
Reusable offcuts	2
Saw cuts / shared	6 / 2

PIECES (POSITION = BOTTOM-LEFT CORNER)

Label	Size	X, Y
GF-IL7 S02	929 x 371	0, 536
GF-EX8 S04	813 x 534	0, 0
GF-IL4 S03	929 x 371	815, 0

NOTES

- Cut from OSB/3 9mm 1197x2397, 2mm saw kerf. Viewed on the face; dimensions from the sheet's bottom-left corner (0,0). Red numbered lines = saw cuts in order, each edge to edge.
- Coloured dimensions belong to the part of that colour: its width and height, and its position from the sheet edges. Raked parts: corner coordinates at each corner.
- Red hatch = waste. Labels = panel + piece mark on the manufacture drawing.

REVISIONS

REV	DATE	DESCRIPTION
C01	13.09.26	Construction issue



TLS TIMBER FRAME

Design & Manufacture

Scan: 3D model + drawings



CLIENT MP Adams	PROJECT MP Adams Plot 3, Eckington
--------------------	---------------------------------------

DRAWING TITLE
OSB CUTTING - GROUND FLOOR - SHEET 38 OF 38

OSB/3 9mm 1197x2397 | Ground Floor

SCALE NTS	SIZE A3	DATE 13.09.26	DRAWN TS
--------------	------------	------------------	-------------

STATUS CONSTRUCTION	DRAWING No. P3-CP-OSB-01 / 38	REV C01
-------------------------------	---	-------------------

Do not scale. All dimensions in mm. Check all dimensions on site.



Top / left chains = saw cut positions (to cut centres). Coloured = part size and position.

SHEET 1 OF 34

THIS SHEET

Item	Value
Parts	1
Used / waste	97.5% / 0.07 m2
Reusable offcuts	0
Saw cuts / shared	1 / 0

PIECES (POSITION = BOTTOM-LEFT CORNER)

Label	Size	X, Y
FF-EX9 S02	1197 x 2337	0, 0

FIRST FLOOR TOTALS

Item	Value
Sheets / pieces	34 / 67
Yield / waste	90.3% / 9.42 m2
Saw cuts / shared / on stock edge	104 / 33 / 105

NOTES

- Cut from OSB/3 9mm 1197x2397, 2mm saw kerf. Viewed on the face; dimensions from the sheet's bottom-left corner (0,0). Red numbered lines = saw cuts in order, each edge to edge.
- Coloured dimensions belong to the part of that colour: its width and height, and its position from the sheet edges. Raked parts: corner coordinates at each corner.
- Red hatch = waste. Labels = panel + piece mark on the manufacture drawing.

REVISIONS

REV	DATE	DESCRIPTION
C01	13.09.26	Construction issue



TLS TIMBER FRAME

Design & Manufacture

Scan: 3D model + drawings




CLIENT	PROJECT
MP Adams	MP Adams Plot 3, Eckington

DRAWING TITLE
OSB CUTTING - FIRST FLOOR - SHEET 1 OF 34
OSB/3 9mm 1197x2397 First Floor

SCALE	SIZE	DATE	DRAWN
NTS	A3	13.09.26	TS

STATUS	DRAWING No.	REV
CONSTRUCTION	P3-CP-OSB-02 / 01	C01

Do not scale. All dimensions in mm. Check all dimensions on site.

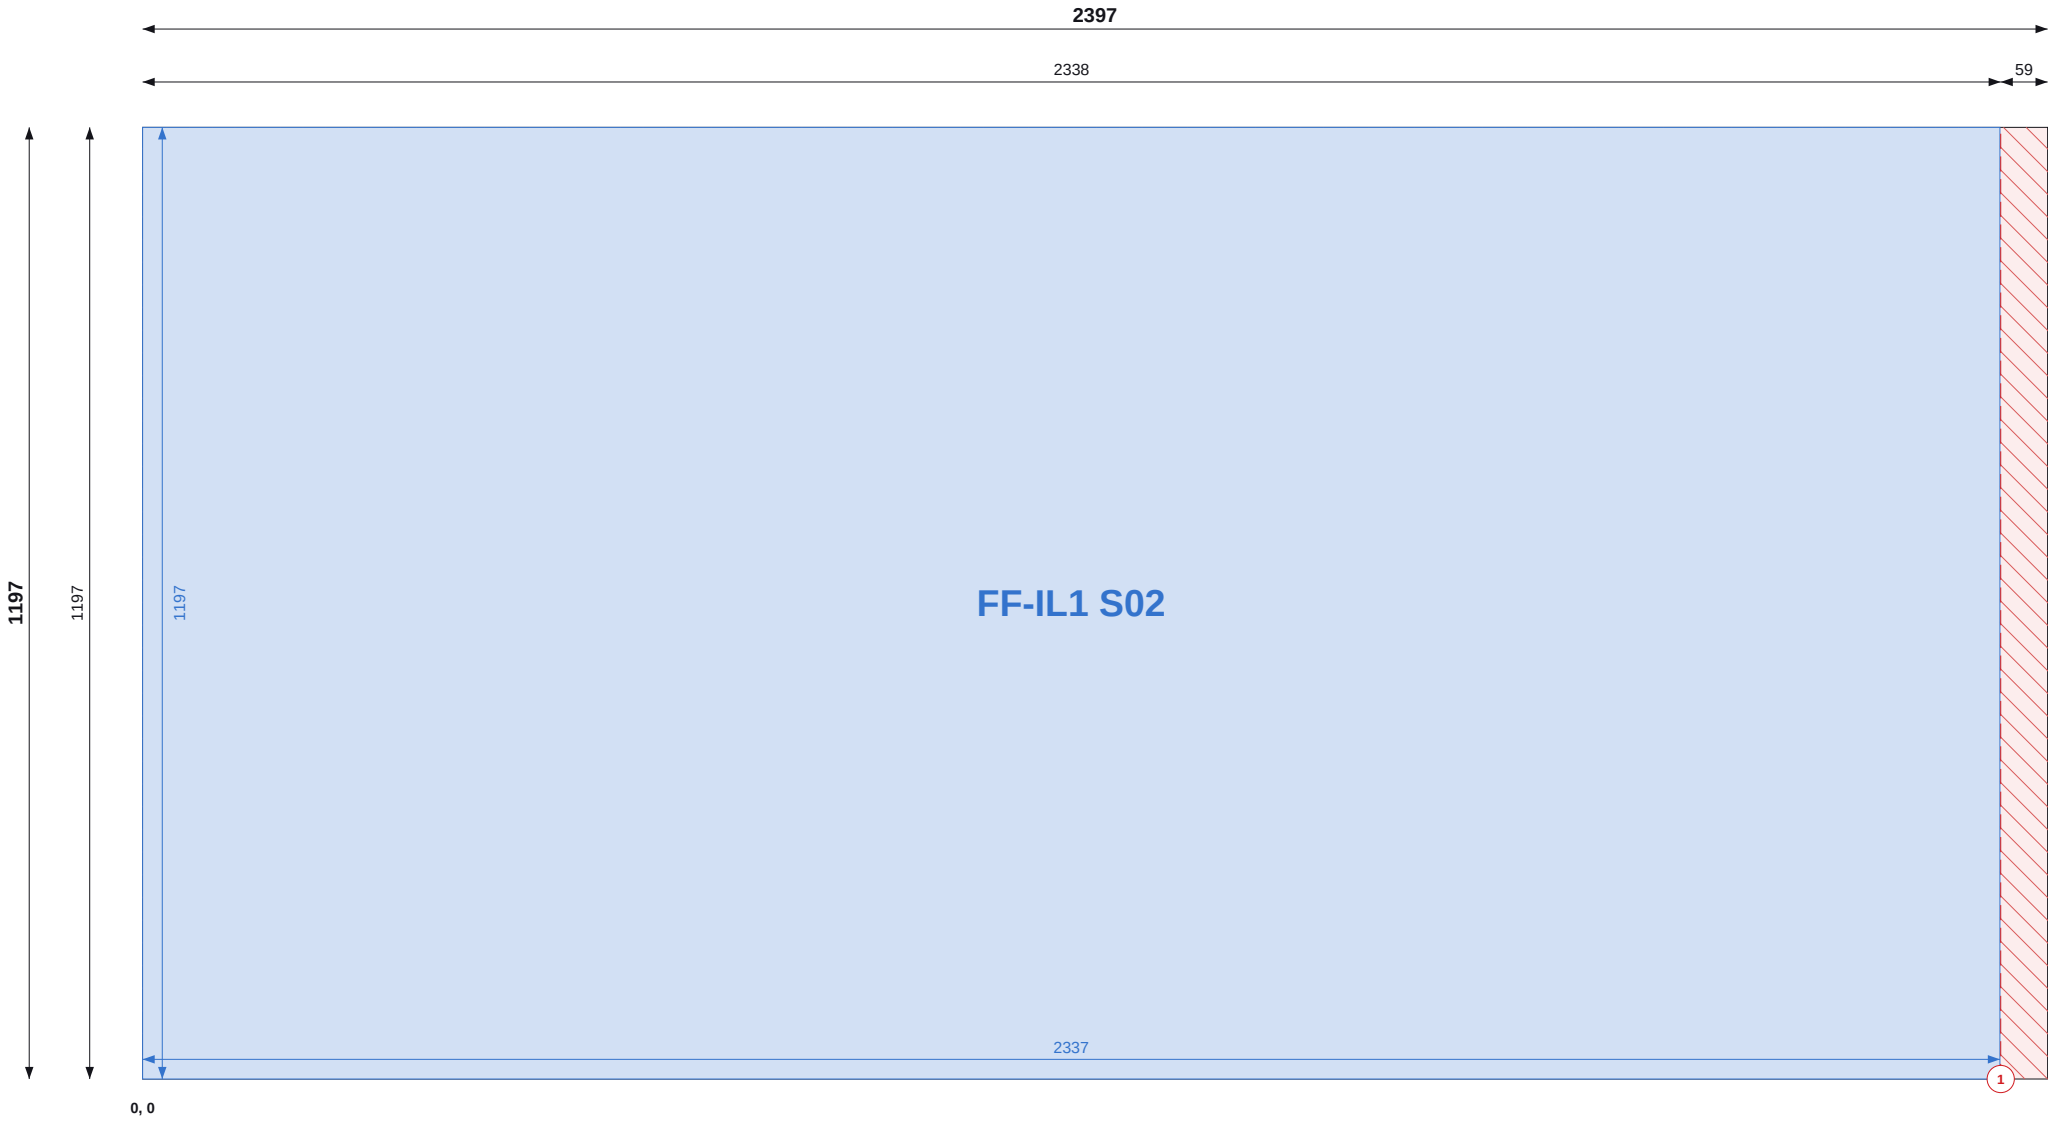

Top / left chains = saw cut positions (to cut centres). Coloured = part size and position.

SHEET 2 OF 34

THIS SHEET

Item	Value
Parts	1
Used / waste	97.5% / 0.07 m2
Reusable offcuts	0
Saw cuts / shared	1 / 0

PIECES (POSITION = BOTTOM-LEFT CORNER)

Label	Size	X, Y
FF-IL1 S02	1197 x 2337	0, 0

NOTES

- Cut from OSB/3 9mm 1197x2397, 2mm saw kerf. Viewed on the face; dimensions from the sheet's bottom-left corner (0,0). Red numbered lines = saw cuts in order, each edge to edge.
- Coloured dimensions belong to the part of that colour: its width and height, and its position from the sheet edges. Raked parts: corner coordinates at each corner.
- Red hatch = waste. Labels = panel + piece mark on the manufacture drawing.

REVISIONS

REV	DATE	DESCRIPTION
C01	13.09.26	Construction issue



TLS TIMBER FRAME

Design & Manufacture

Scan: 3D model + drawings



CLIENT	PROJECT
MP Adams	MP Adams Plot 3, Eckington


DRAWING TITLE
OSB CUTTING - FIRST FLOOR - SHEET 2 OF 34

OSB/3 9mm 1197x2397 | First Floor

SCALE	SIZE	DATE	DRAWN
NTS	A3	13.09.26	TS

STATUS	DRAWING No.	REV
CONSTRUCTION	P3-CP-OSB-02 / 02	C01

Do not scale. All dimensions in mm. Check all dimensions on site.

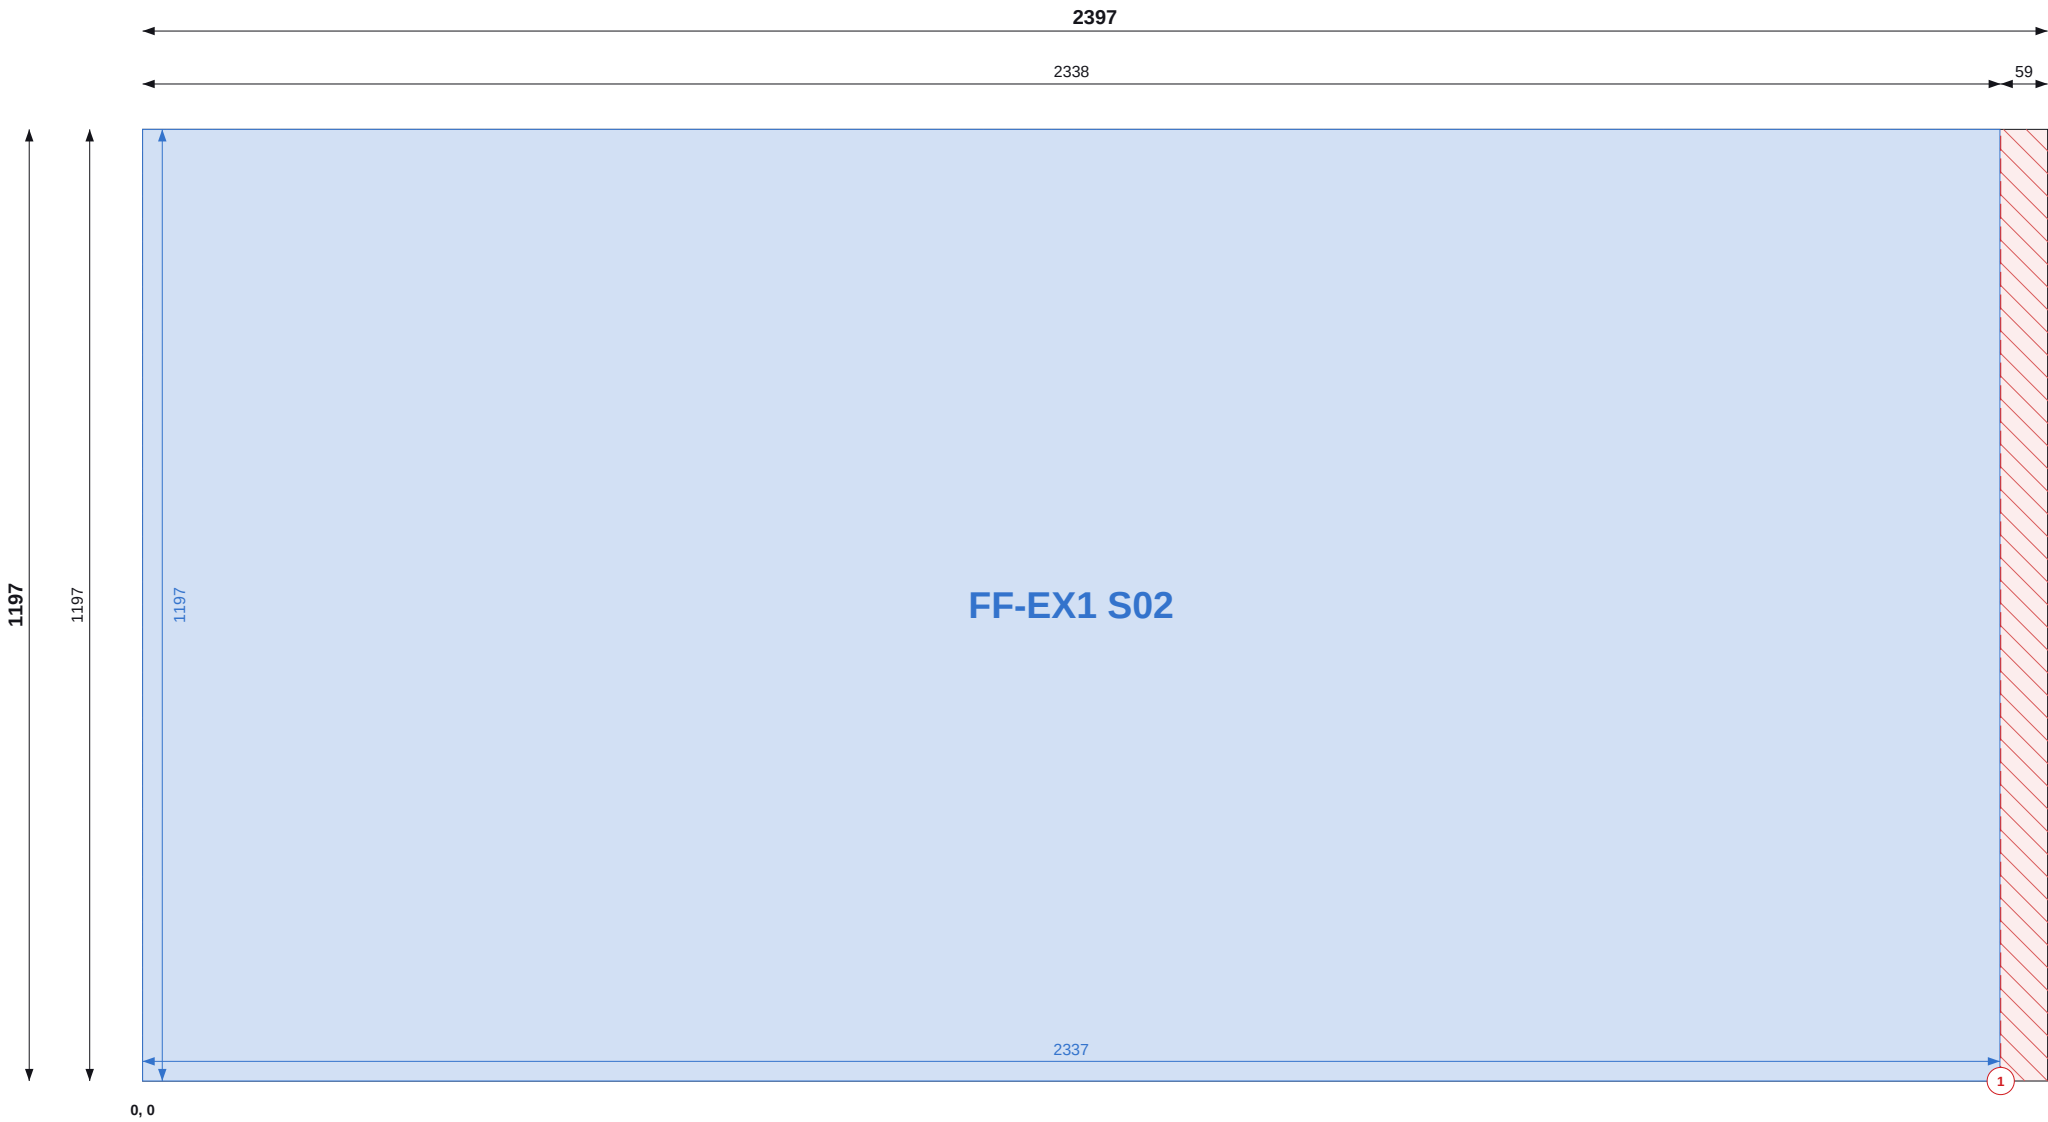

Top / left chains = saw cut positions (to cut centres). Coloured = part size and position.

SHEET 3 OF 34

THIS SHEET

Item	Value
Parts	1
Used / waste	97.5% / 0.07 m2
Reusable offcuts	0
Saw cuts / shared	1 / 0

PIECES (POSITION = BOTTOM-LEFT CORNER)

Label	Size	X, Y
FF-EX1 S02	1197 x 2337	0, 0

NOTES

- Cut from OSB/3 9mm 1197x2397, 2mm saw kerf. Viewed on the face; dimensions from the sheet's bottom-left corner (0,0). Red numbered lines = saw cuts in order, each edge to edge.
- Coloured dimensions belong to the part of that colour: its width and height, and its position from the sheet edges. Raked parts: corner coordinates at each corner.
- Red hatch = waste. Labels = panel + piece mark on the manufacture drawing.

REVISIONS

REV	DATE	DESCRIPTION
C01	13.09.26	Construction issue



TLS TIMBER FRAME
Design & Manufacture
Scan: 3D model + drawings

CLIENT MP Adams	PROJECT MP Adams Plot 3, Eckington
--------------------	---------------------------------------


DRAWING TITLE OSB CUTTING - FIRST FLOOR - SHEET 3 OF 34
--

OSB/3 9mm 1197x2397 | First Floor

SCALE NTS	SIZE A3	DATE 13.09.26	DRAWN TS
--------------	------------	------------------	-------------

STATUS CONSTRUCTION	DRAWING No. P3-CP-OSB-02 / 03	REV C01
------------------------	----------------------------------	------------

Do not scale. All dimensions in mm. Check all dimensions on site.

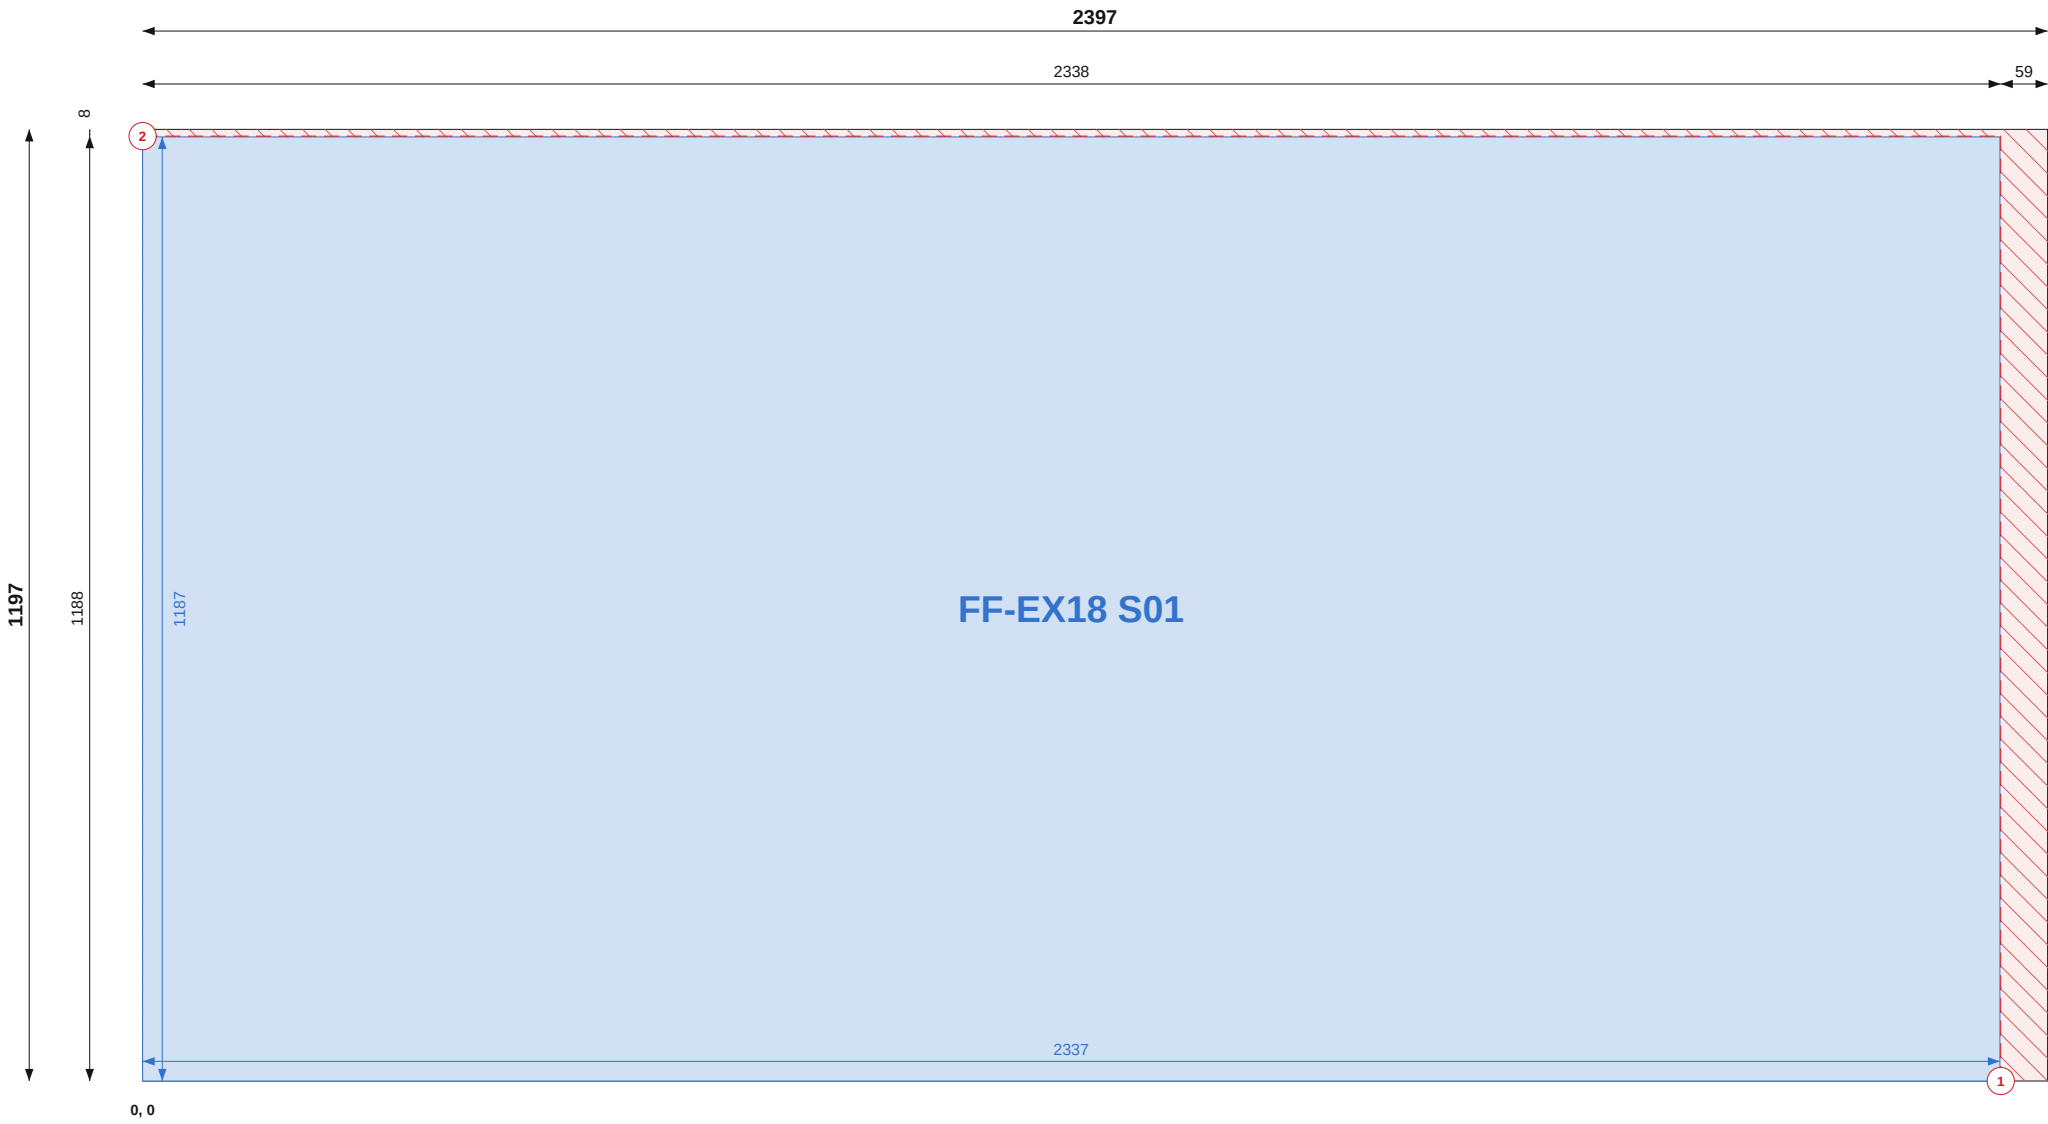

Top / left chains = saw cut positions (to cut centres). Coloured = part size and position.

SHEET 4 OF 34

THIS SHEET

Item	Value
Parts	1
Used / waste	96.7% / 0.09 m2
Reusable offcuts	0
Saw cuts / shared	2 / 0

PIECES (POSITION = BOTTOM-LEFT CORNER)

Label	Size	X, Y
FF-EX18 S01	1187 x 2337	0, 0

NOTES

- Cut from OSB/3 9mm 1197x2397, 2mm saw kerf. Viewed on the face; dimensions from the sheet's bottom-left corner (0,0). Red numbered lines = saw cuts in order, each edge to edge.
- Coloured dimensions belong to the part of that colour: its width and height, and its position from the sheet edges. Raked parts: corner coordinates at each corner.
- Red hatch = waste. Labels = panel + piece mark on the manufacture drawing.

REVISIONS

REV	DATE	DESCRIPTION
C01	13.09.26	Construction issue



TLS TIMBER FRAME
Design & Manufacture
Scan: 3D model + drawings



CLIENT MP Adams	PROJECT MP Adams Plot 3, Eckington
--------------------	---------------------------------------


DRAWING TITLE
OSB CUTTING - FIRST FLOOR - SHEET 4 OF 34

OSB/3 9mm 1197x2397 | First Floor

SCALE NTS	SIZE A3	DATE 13.09.26	DRAWN TS
--------------	------------	------------------	-------------

STATUS CONSTRUCTION	DRAWING No. P3-CP-OSB-02 / 04	REV C01
-------------------------------	---	-------------------

Do not scale. All dimensions in mm. Check all dimensions on site.

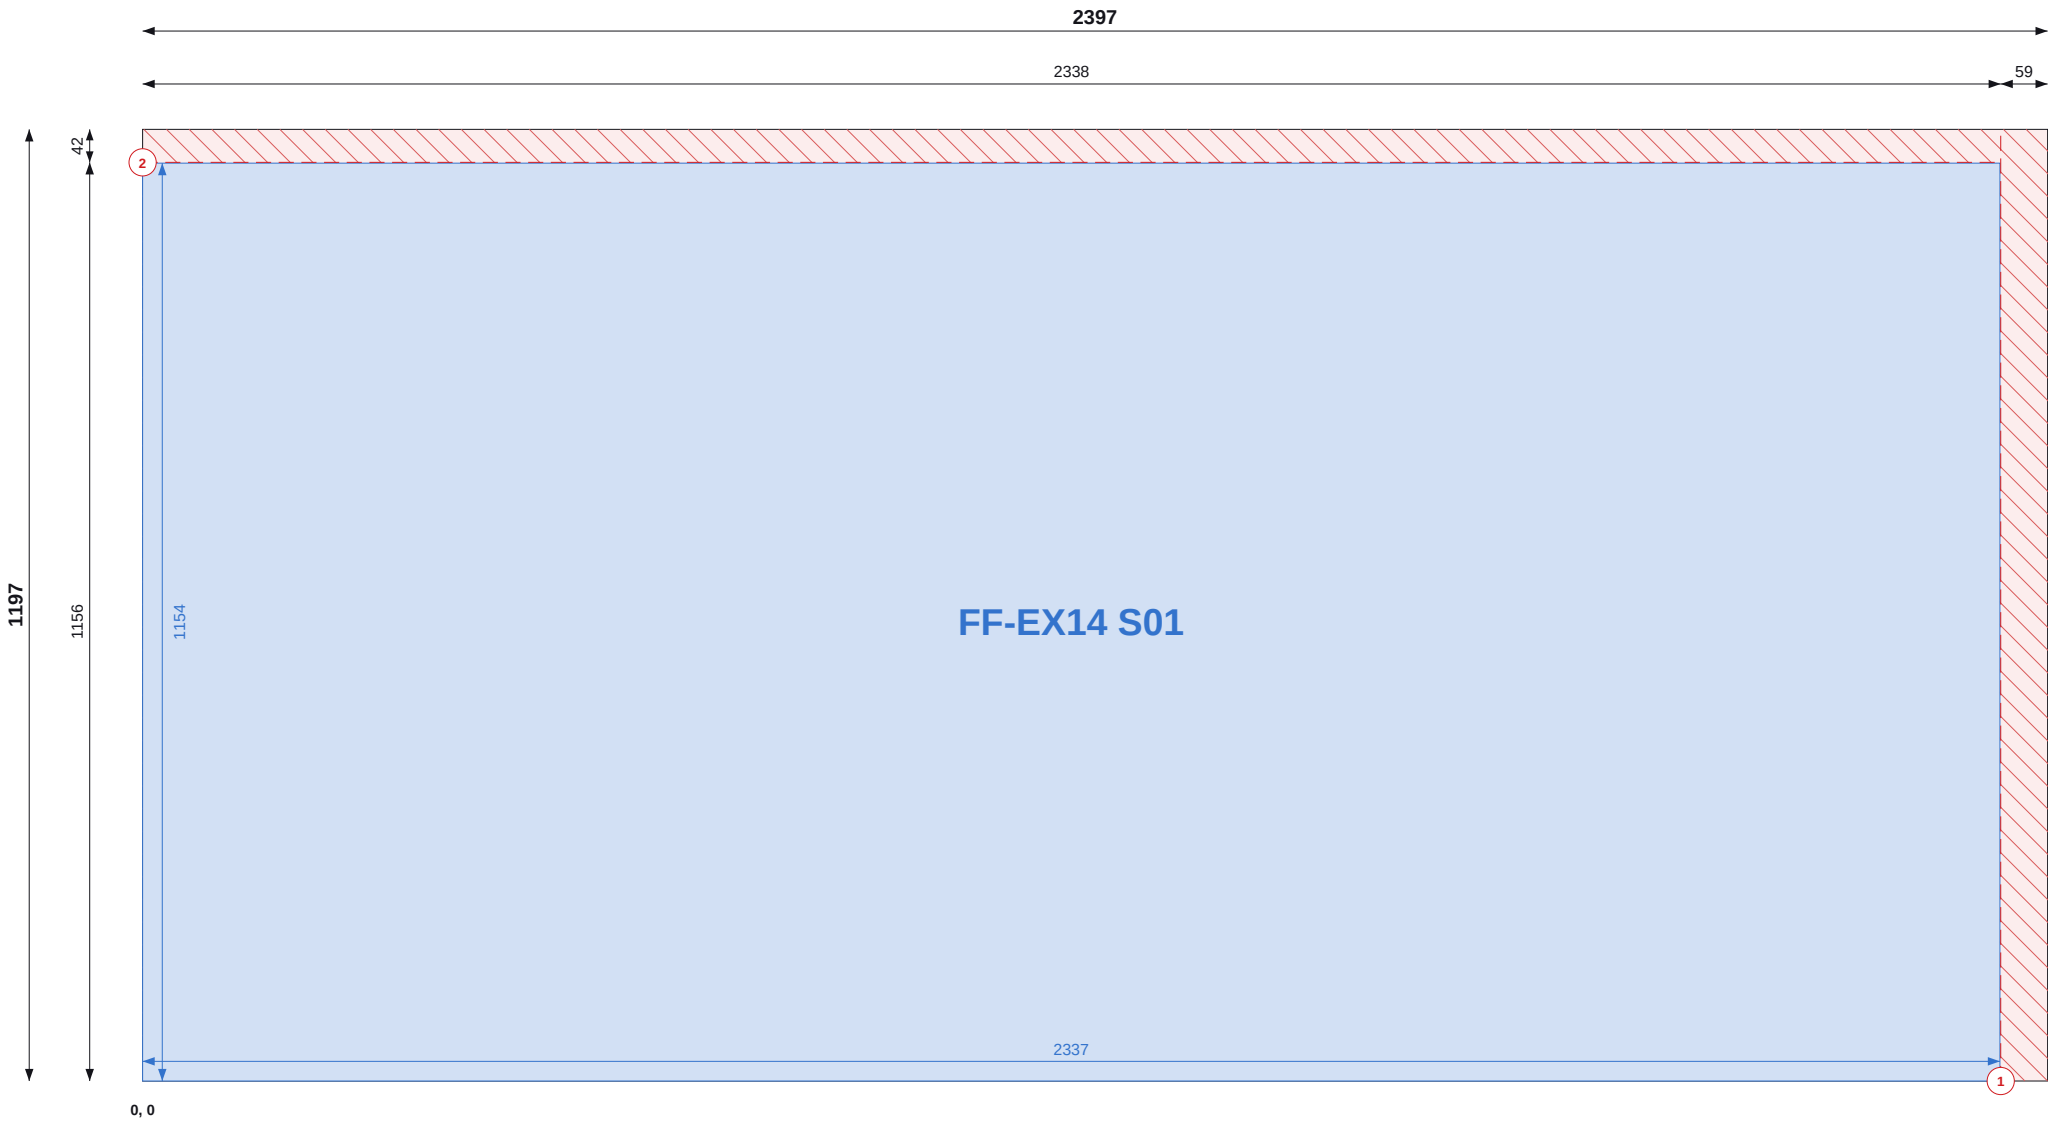

Top / left chains = saw cut positions (to cut centres). Coloured = part size and position.

SHEET 5 OF 34

THIS SHEET

Item	Value
Parts	1
Used / waste	94.0% / 0.17 m2
Reusable offcuts	0
Saw cuts / shared	2 / 0

PIECES (POSITION = BOTTOM-LEFT CORNER)

Label	Size	X, Y
FF-EX14 S01	1154 x 2337	0, 0

NOTES

- Cut from OSB/3 9mm 1197x2397, 2mm saw kerf. Viewed on the face; dimensions from the sheet's bottom-left corner (0,0). Red numbered lines = saw cuts in order, each edge to edge.
- Coloured dimensions belong to the part of that colour: its width and height, and its position from the sheet edges. Raked parts: corner coordinates at each corner.
- Red hatch = waste. Labels = panel + piece mark on the manufacture drawing.

REVISIONS

REV	DATE	DESCRIPTION
C01	13.09.26	Construction issue



TLS TIMBER FRAME

Design & Manufacture

Scan: 3D model + drawings



CLIENT	PROJECT
MP Adams	MP Adams Plot 3, Eckington


DRAWING TITLE
OSB CUTTING - FIRST FLOOR - SHEET 5 OF 34

OSB/3 9mm 1197x2397 | First Floor

SCALE	SIZE	DATE	DRAWN
NTS	A3	13.09.26	TS

STATUS	DRAWING No.	REV
CONSTRUCTION	P3-CP-OSB-02 / 05	C01

Do not scale. All dimensions in mm. Check all dimensions on site.

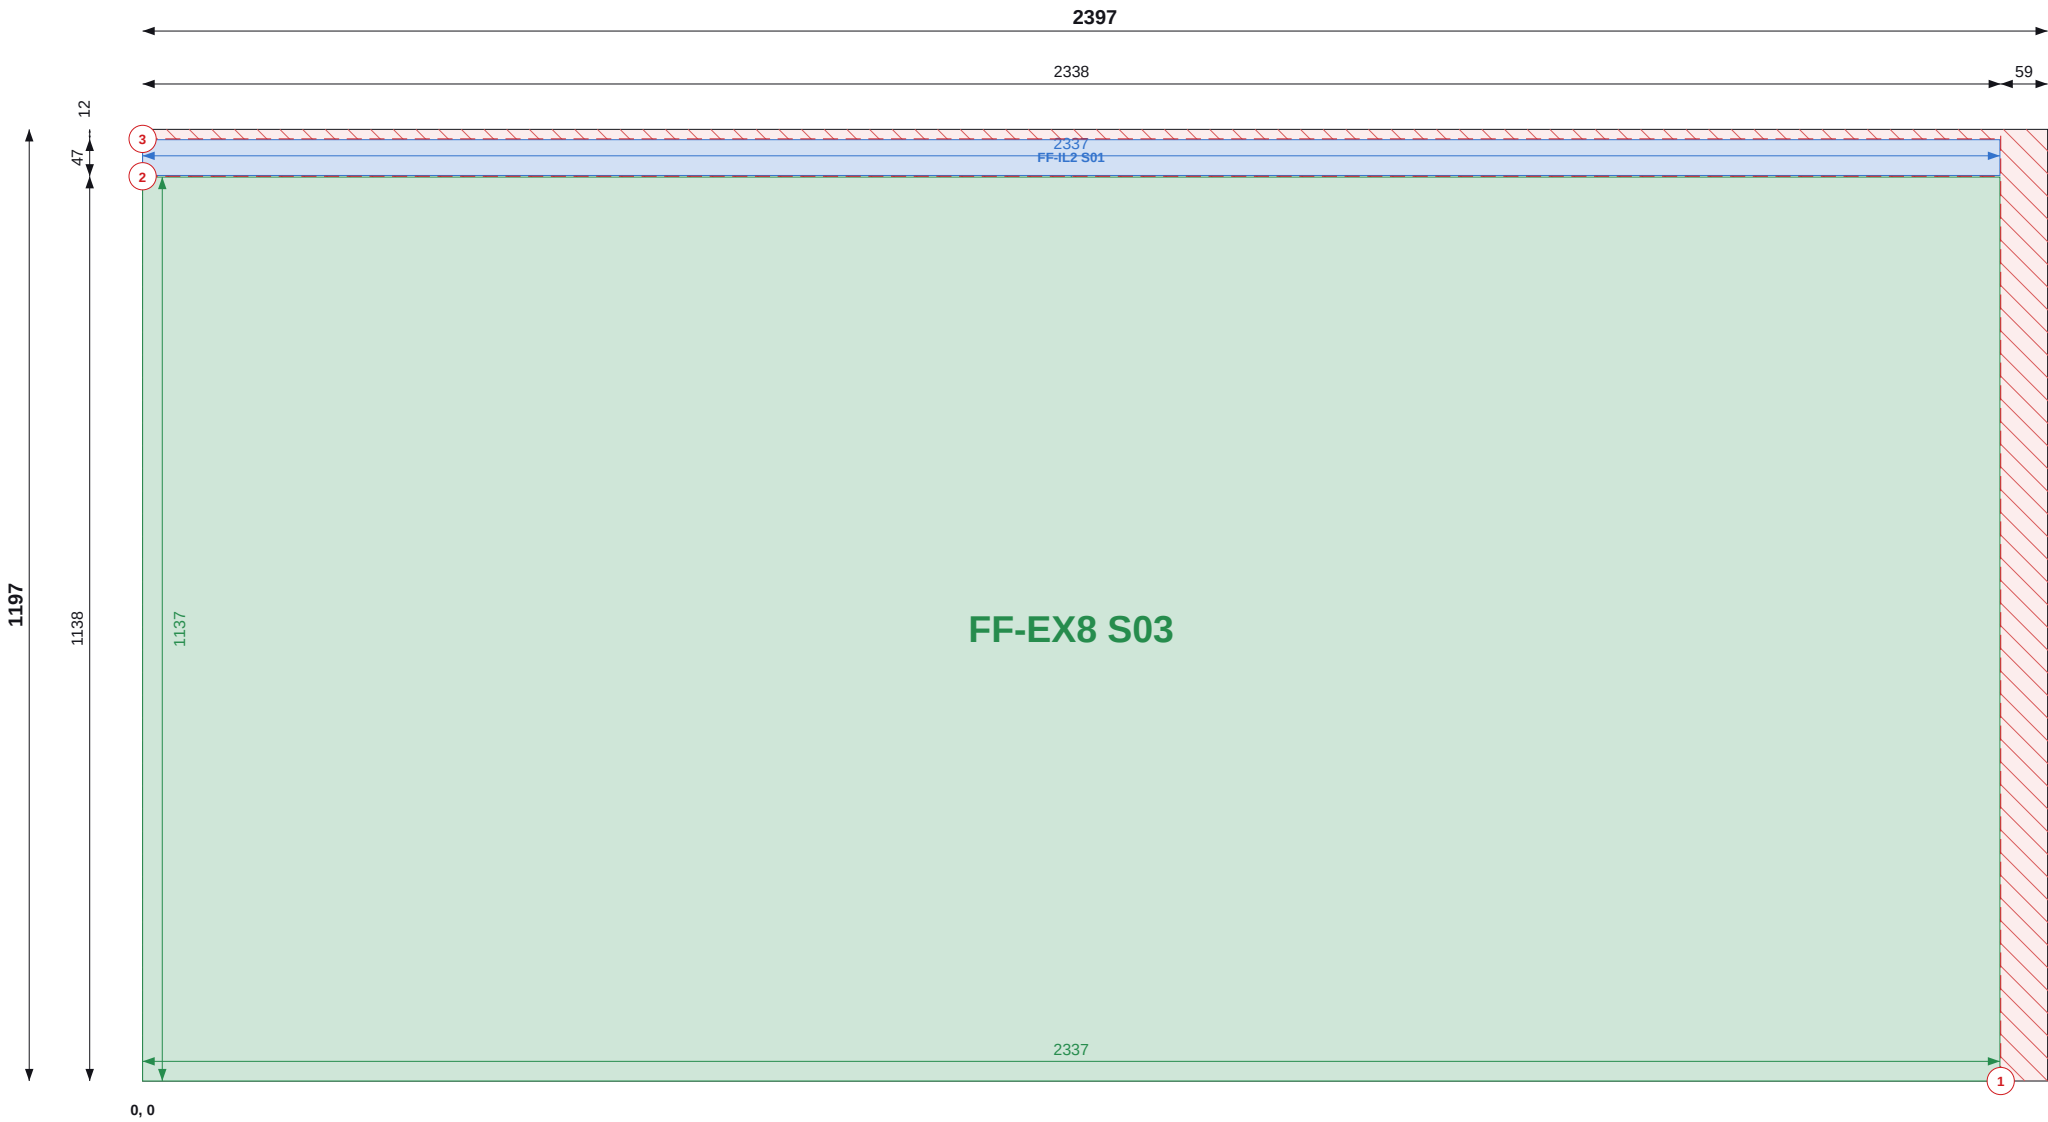

Top / left chains = saw cut positions (to cut centres). Coloured = part size and position.

SHEET 6 OF 34

THIS SHEET

Item	Value
Parts	2
Used / waste	96.3% / 0.11 m2
Reusable offcuts	0
Saw cuts / shared	3 / 1

PIECES (POSITION = BOTTOM-LEFT CORNER)

Label	Size	X, Y
FF-IL2 S01	45 x 2337	0, 1139
FF-EX8 S03	1137 x 2337	0, 0

NOTES

- Cut from OSB/3 9mm 1197x2397, 2mm saw kerf. Viewed on the face; dimensions from the sheet's bottom-left corner (0,0). Red numbered lines = saw cuts in order, each edge to edge.
- Coloured dimensions belong to the part of that colour: its width and height, and its position from the sheet edges. Raked parts: corner coordinates at each corner.
- Red hatch = waste. Labels = panel + piece mark on the manufacture drawing.

REVISIONS

REV	DATE	DESCRIPTION
C01	13.09.26	Construction issue



TLS TIMBER FRAME

Design & Manufacture

Scan: 3D model + drawings



CLIENT	PROJECT
MP Adams	MP Adams Plot 3, Eckington


DRAWING TITLE
OSB CUTTING - FIRST FLOOR - SHEET 6 OF 34

OSB/3 9mm 1197x2397 | First Floor

SCALE	SIZE	DATE	DRAWN
NTS	A3	13.09.26	TS

STATUS	DRAWING No.	REV
CONSTRUCTION	P3-CP-OSB-02 / 06	C01

Do not scale. All dimensions in mm. Check all dimensions on site.

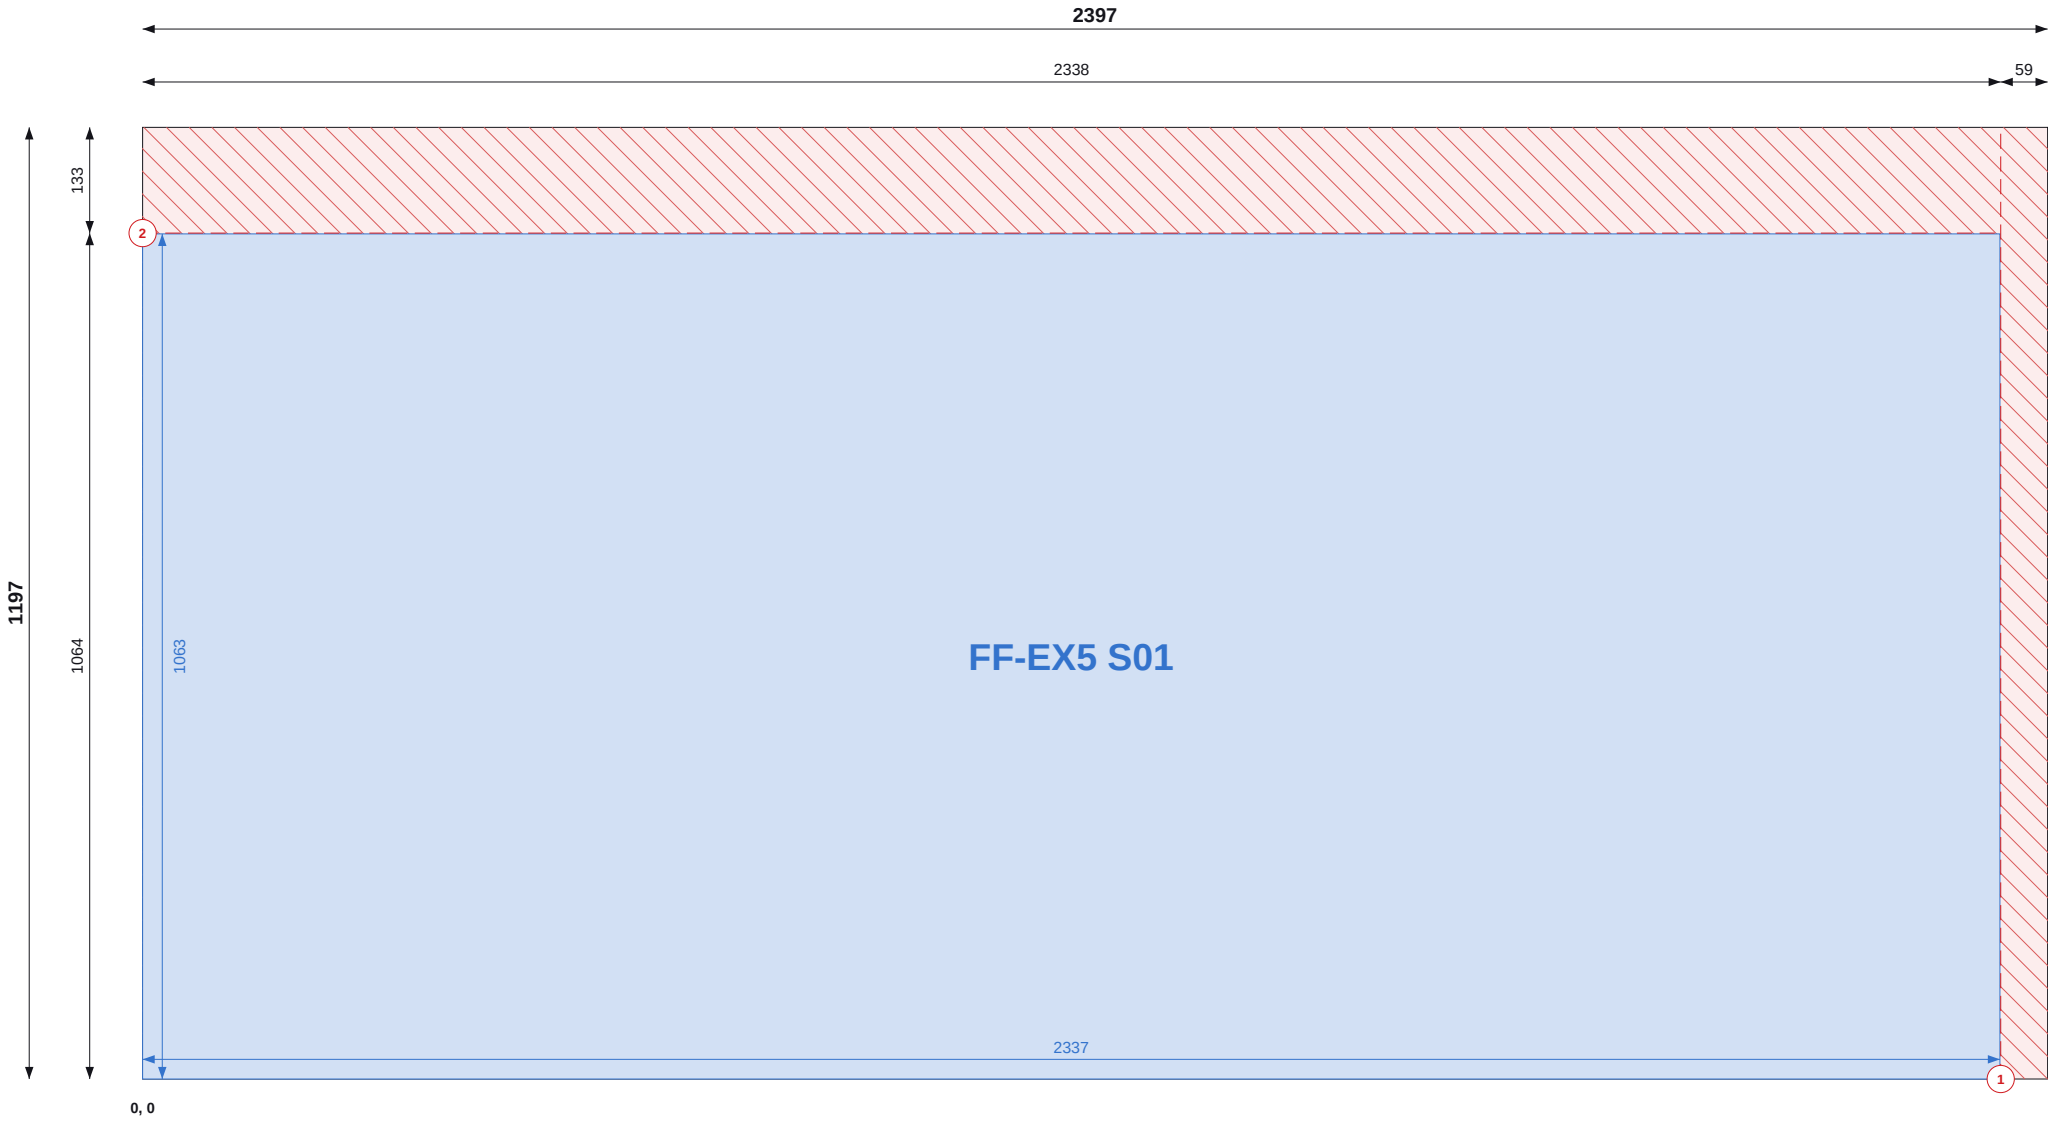

Top / left chains = saw cut positions (to cut centres). Coloured = part size and position.

SHEET 7 OF 34

THIS SHEET

Item	Value
Parts	1
Used / waste	86.6% / 0.38 m2
Reusable offcuts	0
Saw cuts / shared	2 / 0

PIECES (POSITION = BOTTOM-LEFT CORNER)

Label	Size	X, Y
FF-EX5 S01	1063 x 2337	0, 0

NOTES

- Cut from OSB/3 9mm 1197x2397, 2mm saw kerf. Viewed on the face; dimensions from the sheet's bottom-left corner (0,0). Red numbered lines = saw cuts in order, each edge to edge.
- Coloured dimensions belong to the part of that colour: its width and height, and its position from the sheet edges. Raked parts: corner coordinates at each corner.
- Red hatch = waste. Labels = panel + piece mark on the manufacture drawing.

REVISIONS

REV	DATE	DESCRIPTION
C01	13.09.26	Construction issue



TLS TIMBER FRAME

Design & Manufacture

Scan: 3D model + drawings



CLIENT	PROJECT
MP Adams	MP Adams Plot 3, Eckington


DRAWING TITLE
OSB CUTTING - FIRST FLOOR - SHEET 7 OF 34

OSB/3 9mm 1197x2397 | First Floor

SCALE	SIZE	DATE	DRAWN
NTS	A3	13.09.26	TS

STATUS	DRAWING No.	REV
CONSTRUCTION	P3-CP-OSB-02 / 07	C01

Do not scale. All dimensions in mm. Check all dimensions on site.

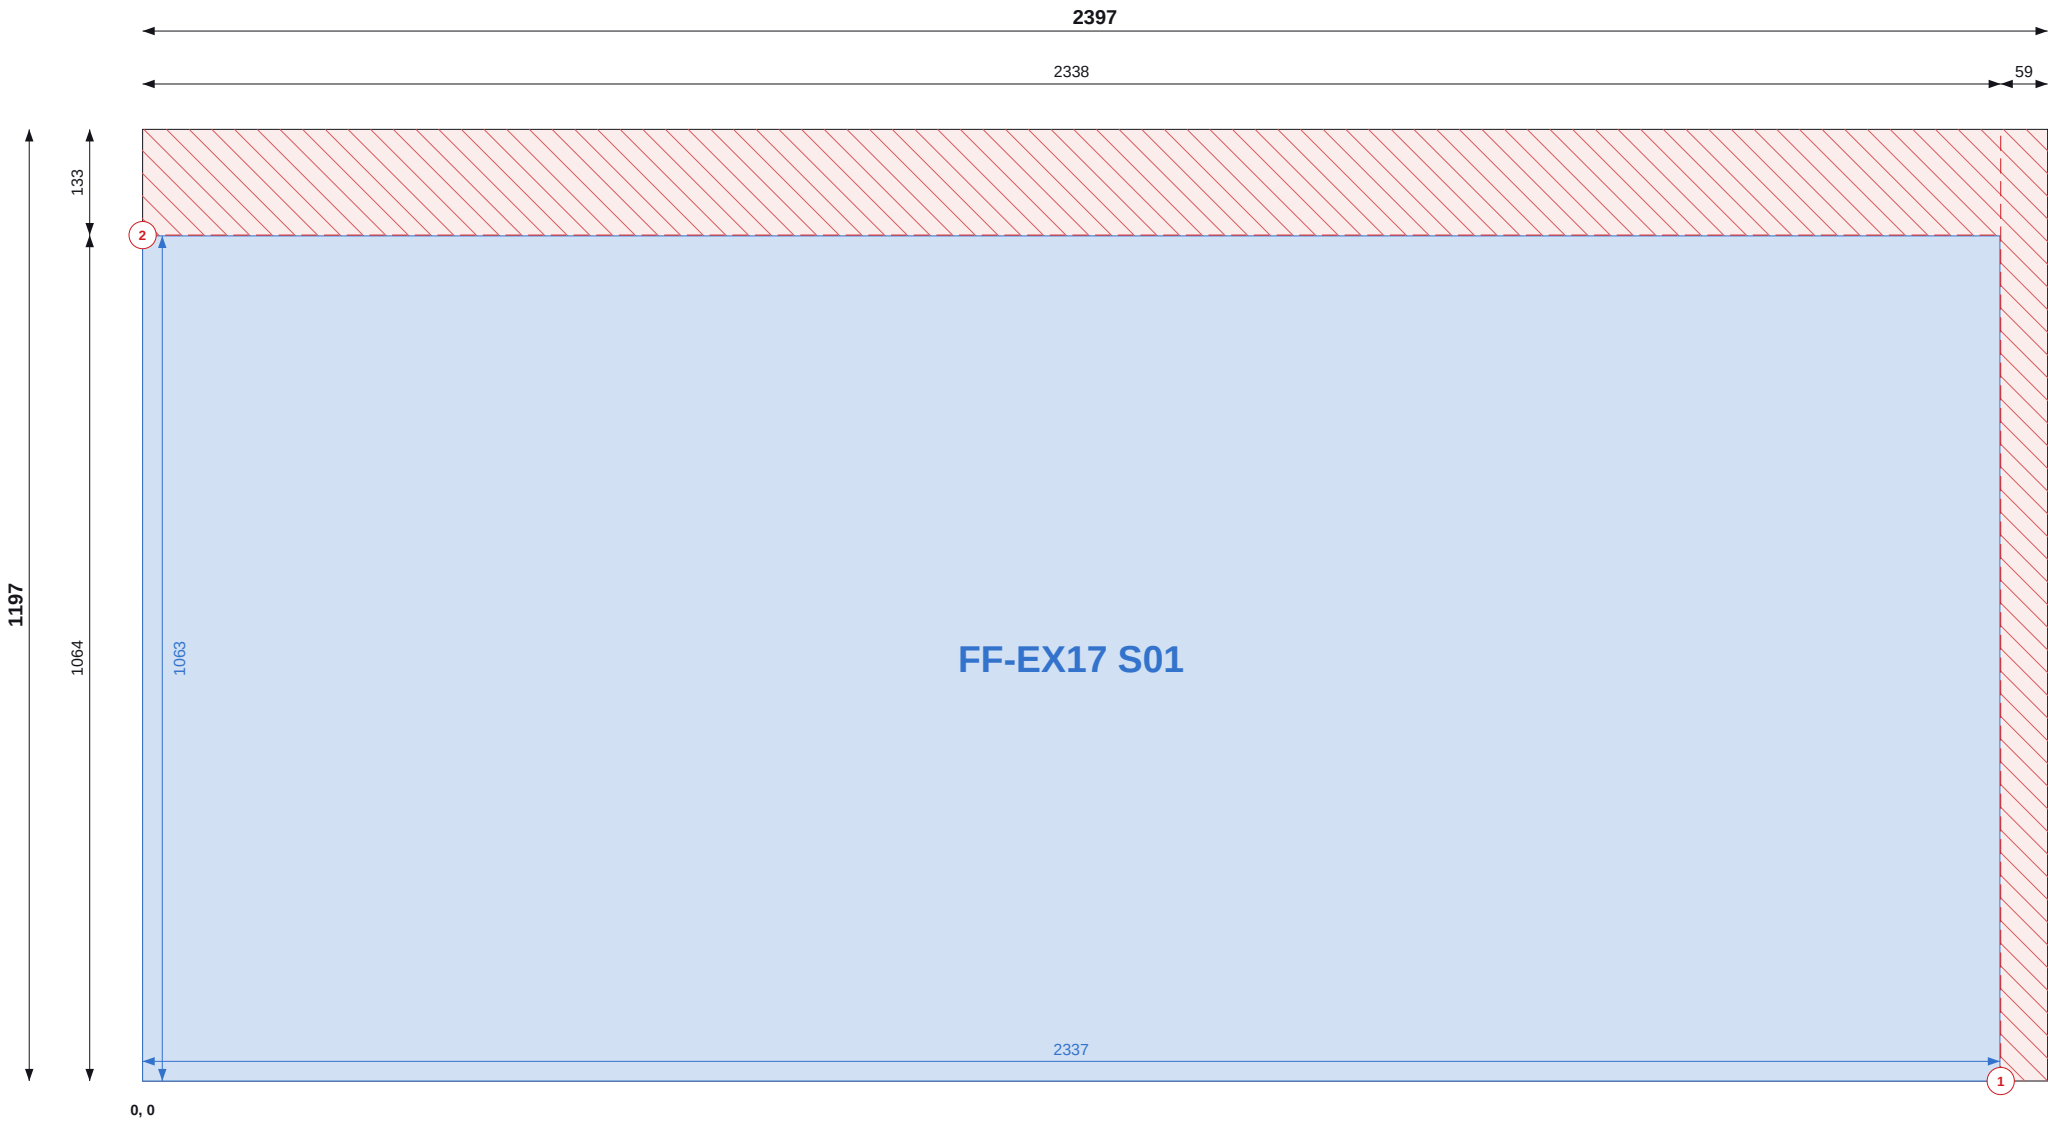

Top / left chains = saw cut positions (to cut centres). Coloured = part size and position.

SHEET 8 OF 34

THIS SHEET

Item	Value
Parts	1
Used / waste	86.6% / 0.38 m2
Reusable offcuts	0
Saw cuts / shared	2 / 0

PIECES (POSITION = BOTTOM-LEFT CORNER)

Label	Size	X, Y
FF-EX17 S01	1063 x 2337	0, 0

NOTES

- Cut from OSB/3 9mm 1197x2397, 2mm saw kerf. Viewed on the face; dimensions from the sheet's bottom-left corner (0,0). Red numbered lines = saw cuts in order, each edge to edge.
- Coloured dimensions belong to the part of that colour: its width and height, and its position from the sheet edges. Raked parts: corner coordinates at each corner.
- Red hatch = waste. Labels = panel + piece mark on the manufacture drawing.

REVISIONS

REV	DATE	DESCRIPTION
C01	13.09.26	Construction issue



TLS TIMBER FRAME

Design & Manufacture

Scan: 3D model + drawings



CLIENT MP Adams	PROJECT MP Adams Plot 3, Eckington
--------------------	---------------------------------------


DRAWING TITLE OSB CUTTING - FIRST FLOOR - SHEET 8 OF 34

OSB/3 9mm 1197x2397 | First Floor

SCALE NTS	SIZE A3	DATE 13.09.26	DRAWN TS
--------------	------------	------------------	-------------

STATUS CONSTRUCTION	DRAWING No. P3-CP-OSB-02 / 08	REV C01
-------------------------------	---	-------------------

Do not scale. All dimensions in mm. Check all dimensions on site.

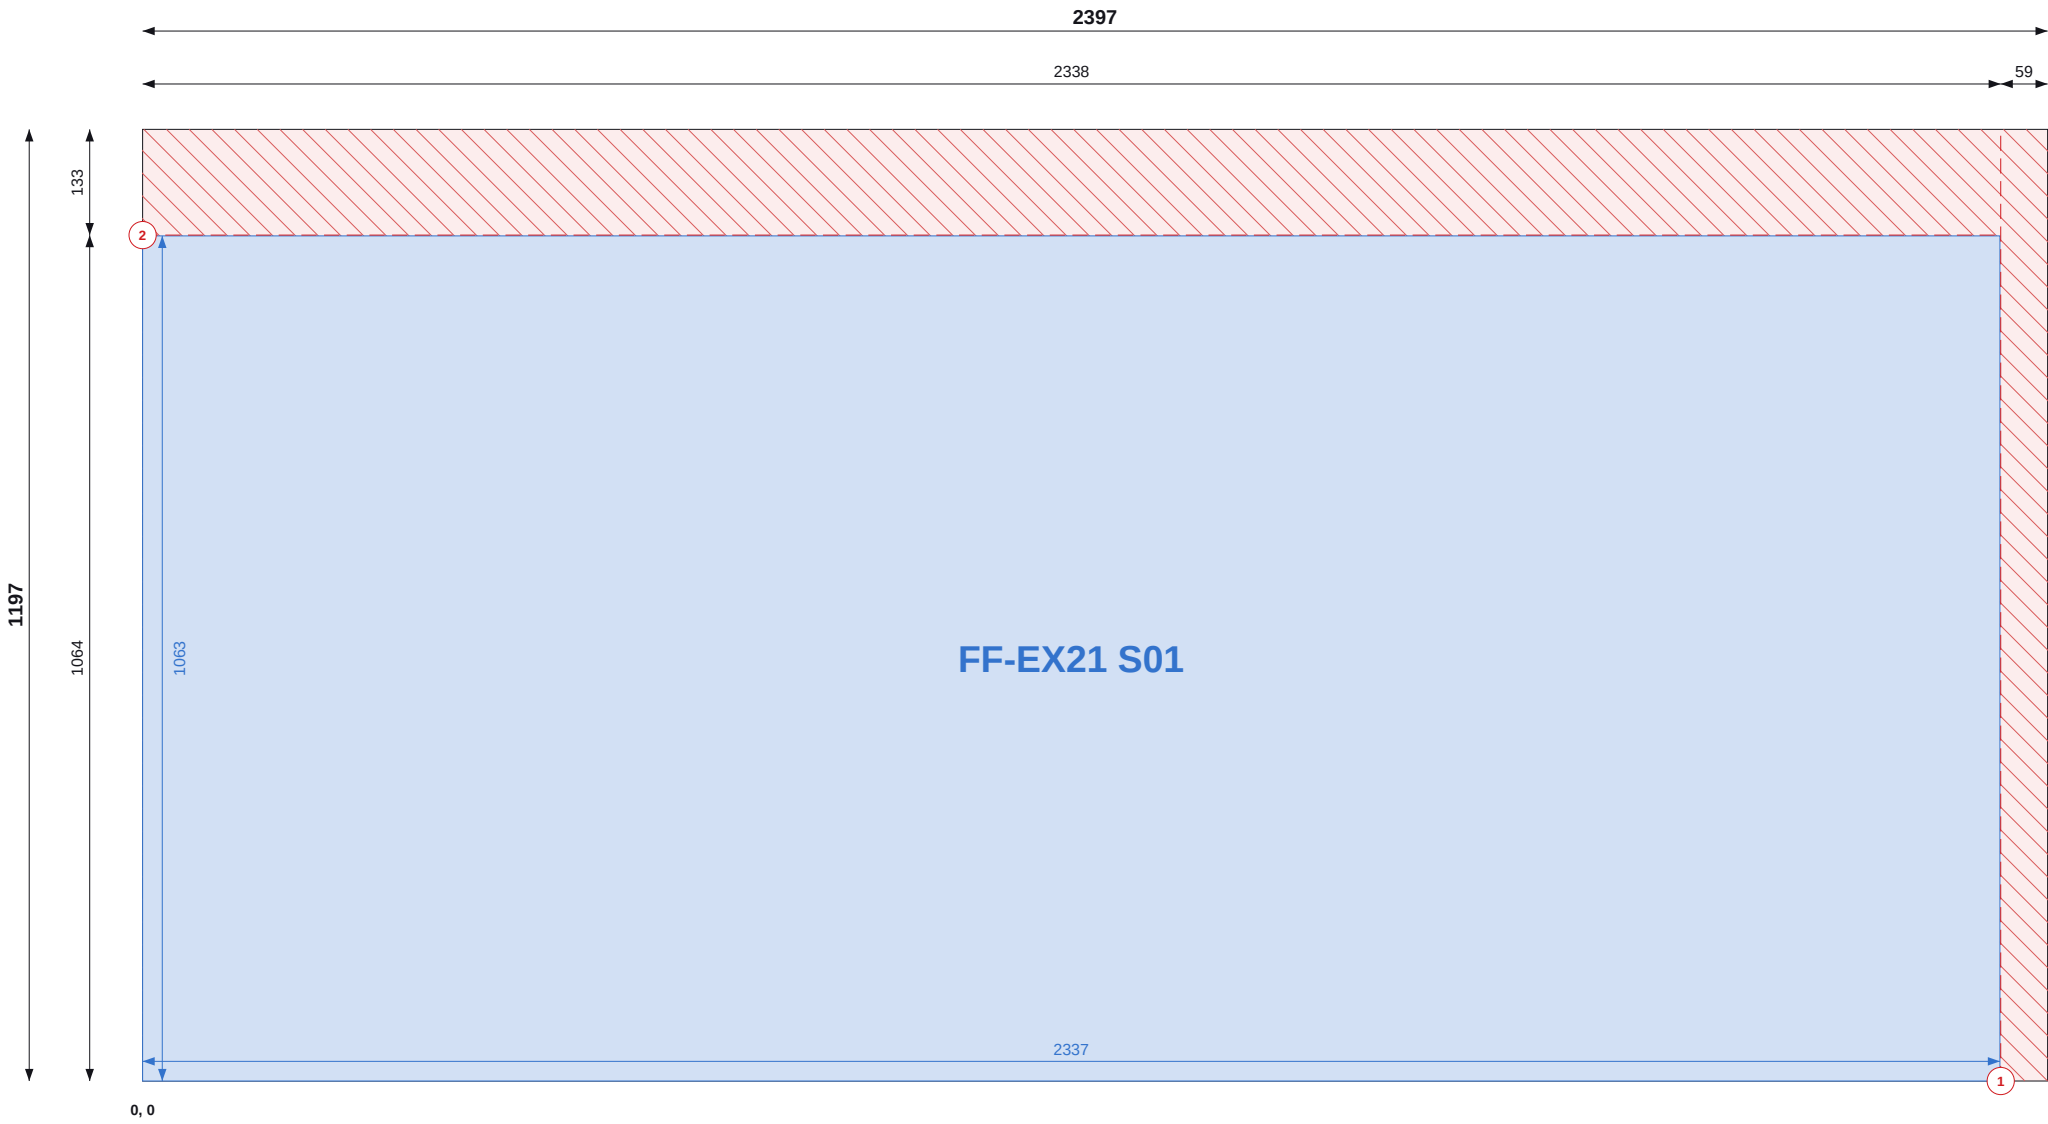

Top / left chains = saw cut positions (to cut centres). Coloured = part size and position.

SHEET 9 OF 34

THIS SHEET

Item	Value
Parts	1
Used / waste	86.6% / 0.38 m2
Reusable offcuts	0
Saw cuts / shared	2 / 0

PIECES (POSITION = BOTTOM-LEFT CORNER)

Label	Size	X, Y
FF-EX21 S01	1063 x 2337	0, 0

NOTES

- Cut from OSB/3 9mm 1197x2397, 2mm saw kerf. Viewed on the face; dimensions from the sheet's bottom-left corner (0,0). Red numbered lines = saw cuts in order, each edge to edge.
- Coloured dimensions belong to the part of that colour: its width and height, and its position from the sheet edges. Raked parts: corner coordinates at each corner.
- Red hatch = waste. Labels = panel + piece mark on the manufacture drawing.

REVISIONS

REV	DATE	DESCRIPTION
C01	13.09.26	Construction issue



TLS TIMBER FRAME

Design & Manufacture

Scan: 3D model + drawings




CLIENT	PROJECT
MP Adams	MP Adams Plot 3, Eckington

DRAWING TITLE			
OSB CUTTING - FIRST FLOOR - SHEET 9 OF 34			
OSB/3 9mm 1197x2397 First Floor			

SCALE	SIZE	DATE	DRAWN
NTS	A3	13.09.26	TS

STATUS	DRAWING No.	REV
CONSTRUCTION	P3-CP-OSB-02 / 09	C01

Do not scale. All dimensions in mm. Check all dimensions on site.

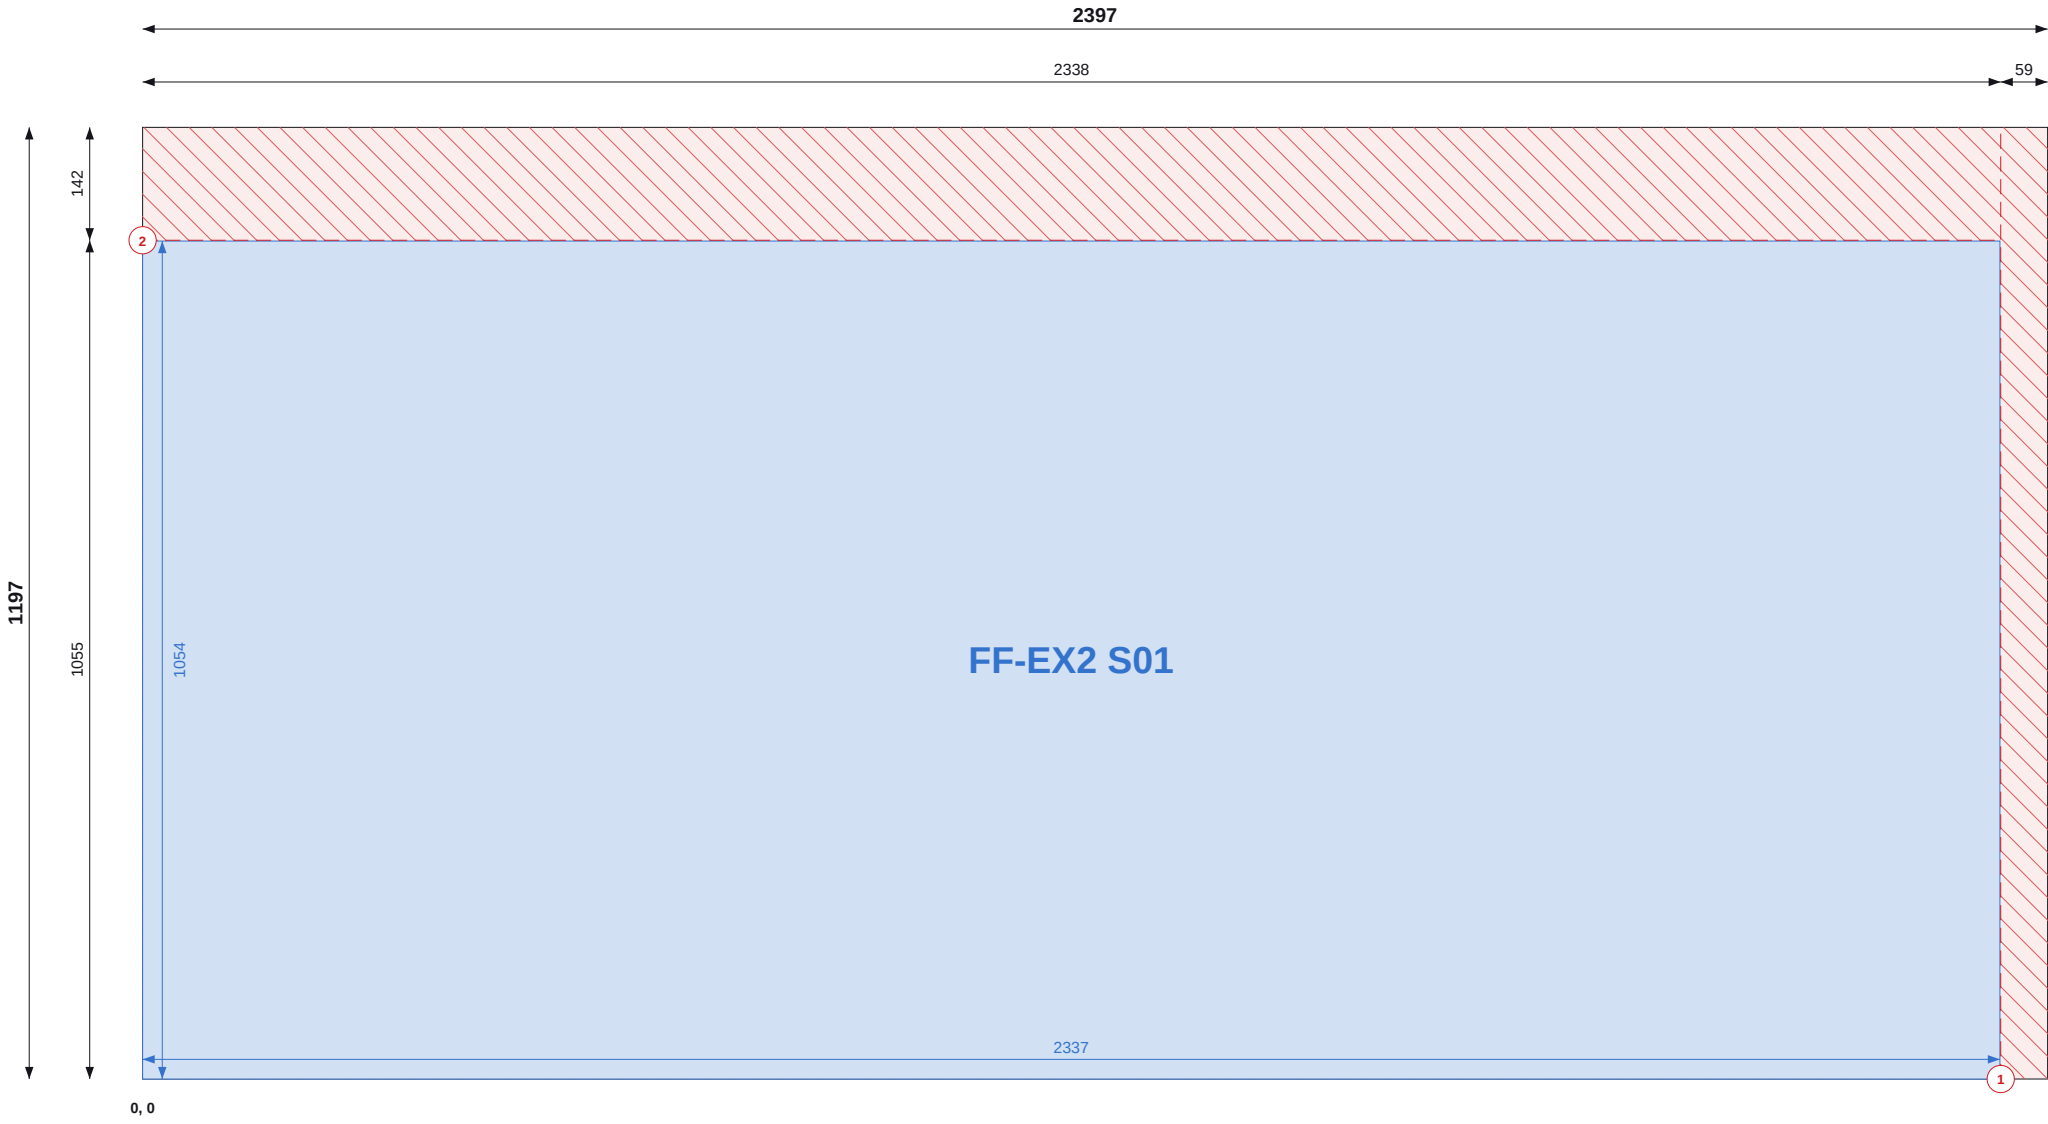

Top / left chains = saw cut positions (to cut centres). Coloured = part size and position.

SHEET 10 OF 34

THIS SHEET

Item	Value
Parts	1
Used / waste	85.8% / 0.41 m2
Reusable offcuts	0
Saw cuts / shared	2 / 0

PIECES (POSITION = BOTTOM-LEFT CORNER)

Label	Size	X, Y
FF-EX2 S01	1054 x 2337	0, 0

NOTES

- Cut from OSB/3 9mm 1197x2397, 2mm saw kerf. Viewed on the face; dimensions from the sheet's bottom-left corner (0,0). Red numbered lines = saw cuts in order, each edge to edge.
- Coloured dimensions belong to the part of that colour: its width and height, and its position from the sheet edges. Raked parts: corner coordinates at each corner.
- Red hatch = waste. Labels = panel + piece mark on the manufacture drawing.

REVISIONS

REV	DATE	DESCRIPTION
C01	13.09.26	Construction issue



TLS TIMBER FRAME
Design & Manufacture
Scan: 3D model + drawings




CLIENT MP Adams	PROJECT MP Adams Plot 3, Eckington
--------------------	---------------------------------------

DRAWING TITLE OSB CUTTING - FIRST FLOOR - SHEET 10 OF 34			
OSB/3 9mm 1197x2397 First Floor			

SCALE NTS	SIZE A3	DATE 13.09.26	DRAWN TS
--------------	------------	------------------	-------------

STATUS CONSTRUCTION	DRAWING No. P3-CP-OSB-02 / 10	REV C01
------------------------	----------------------------------	------------

Do not scale. All dimensions in mm. Check all dimensions on site.

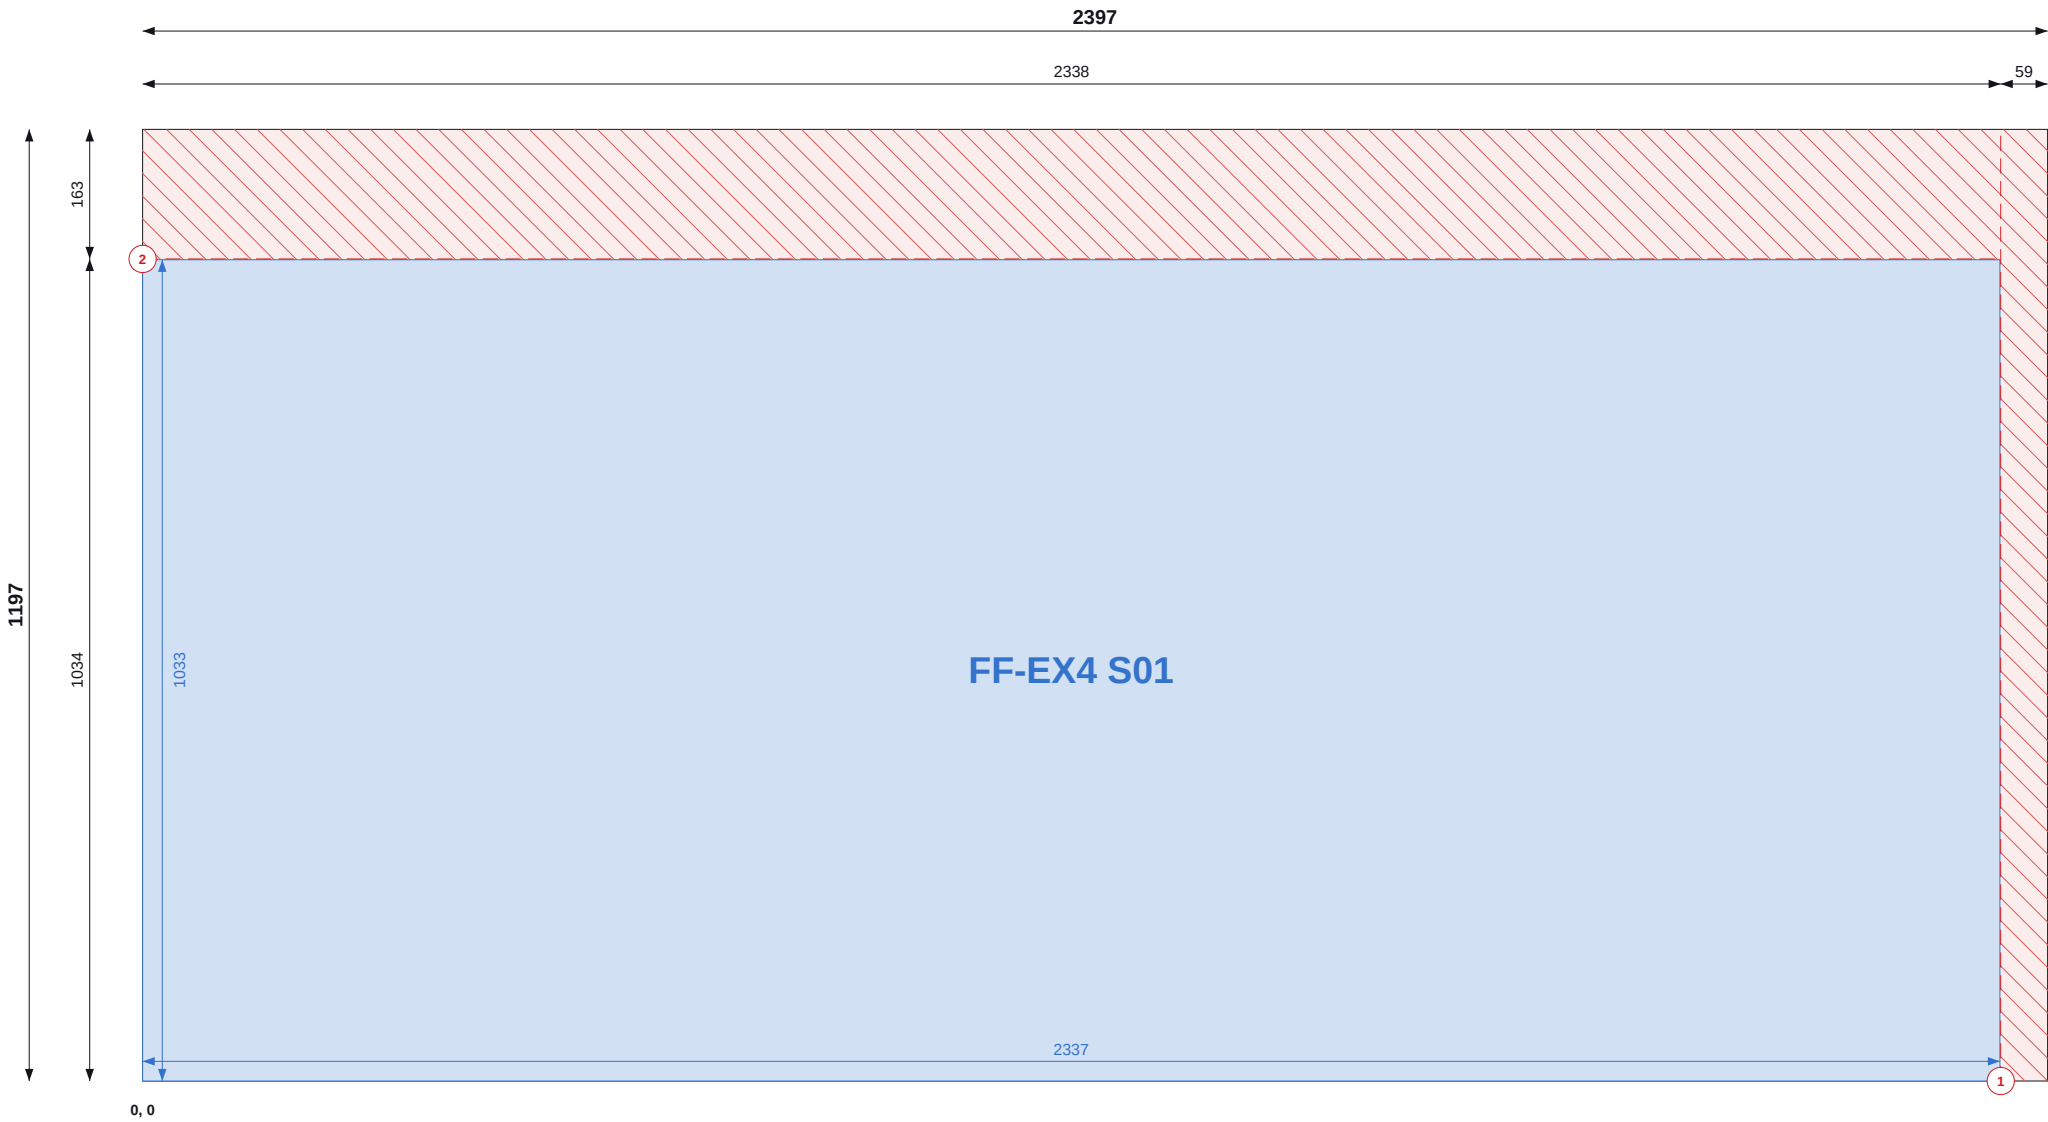

Top / left chains = saw cut positions (to cut centres). Coloured = part size and position.

SHEET 11 OF 34

THIS SHEET

Item	Value
Parts	1
Used / waste	84.1% / 0.46 m2
Reusable offcuts	0
Saw cuts / shared	2 / 0

PIECES (POSITION = BOTTOM-LEFT CORNER)

Label	Size	X, Y
FF-EX4 S01	1033 x 2337	0, 0

NOTES

- Cut from OSB/3 9mm 1197x2397, 2mm saw kerf. Viewed on the face; dimensions from the sheet's bottom-left corner (0,0). Red numbered lines = saw cuts in order, each edge to edge.
- Coloured dimensions belong to the part of that colour: its width and height, and its position from the sheet edges. Raked parts: corner coordinates at each corner.
- Red hatch = waste. Labels = panel + piece mark on the manufacture drawing.

REVISIONS

REV	DATE	DESCRIPTION
C01	13.09.26	Construction issue



TLS TIMBER FRAME
Design & Manufacture
Scan: 3D model + drawings




CLIENT MP Adams	PROJECT MP Adams Plot 3, Eckington
--------------------	---------------------------------------

DRAWING TITLE OSB CUTTING - FIRST FLOOR - SHEET 11 OF 34			
OSB/3 9mm 1197x2397 First Floor			

SCALE NTS	SIZE A3	DATE 13.09.26	DRAWN TS
--------------	------------	------------------	-------------

STATUS CONSTRUCTION	DRAWING No. P3-CP-OSB-02 / 11	REV C01
------------------------	----------------------------------	------------

Do not scale. All dimensions in mm. Check all dimensions on site.

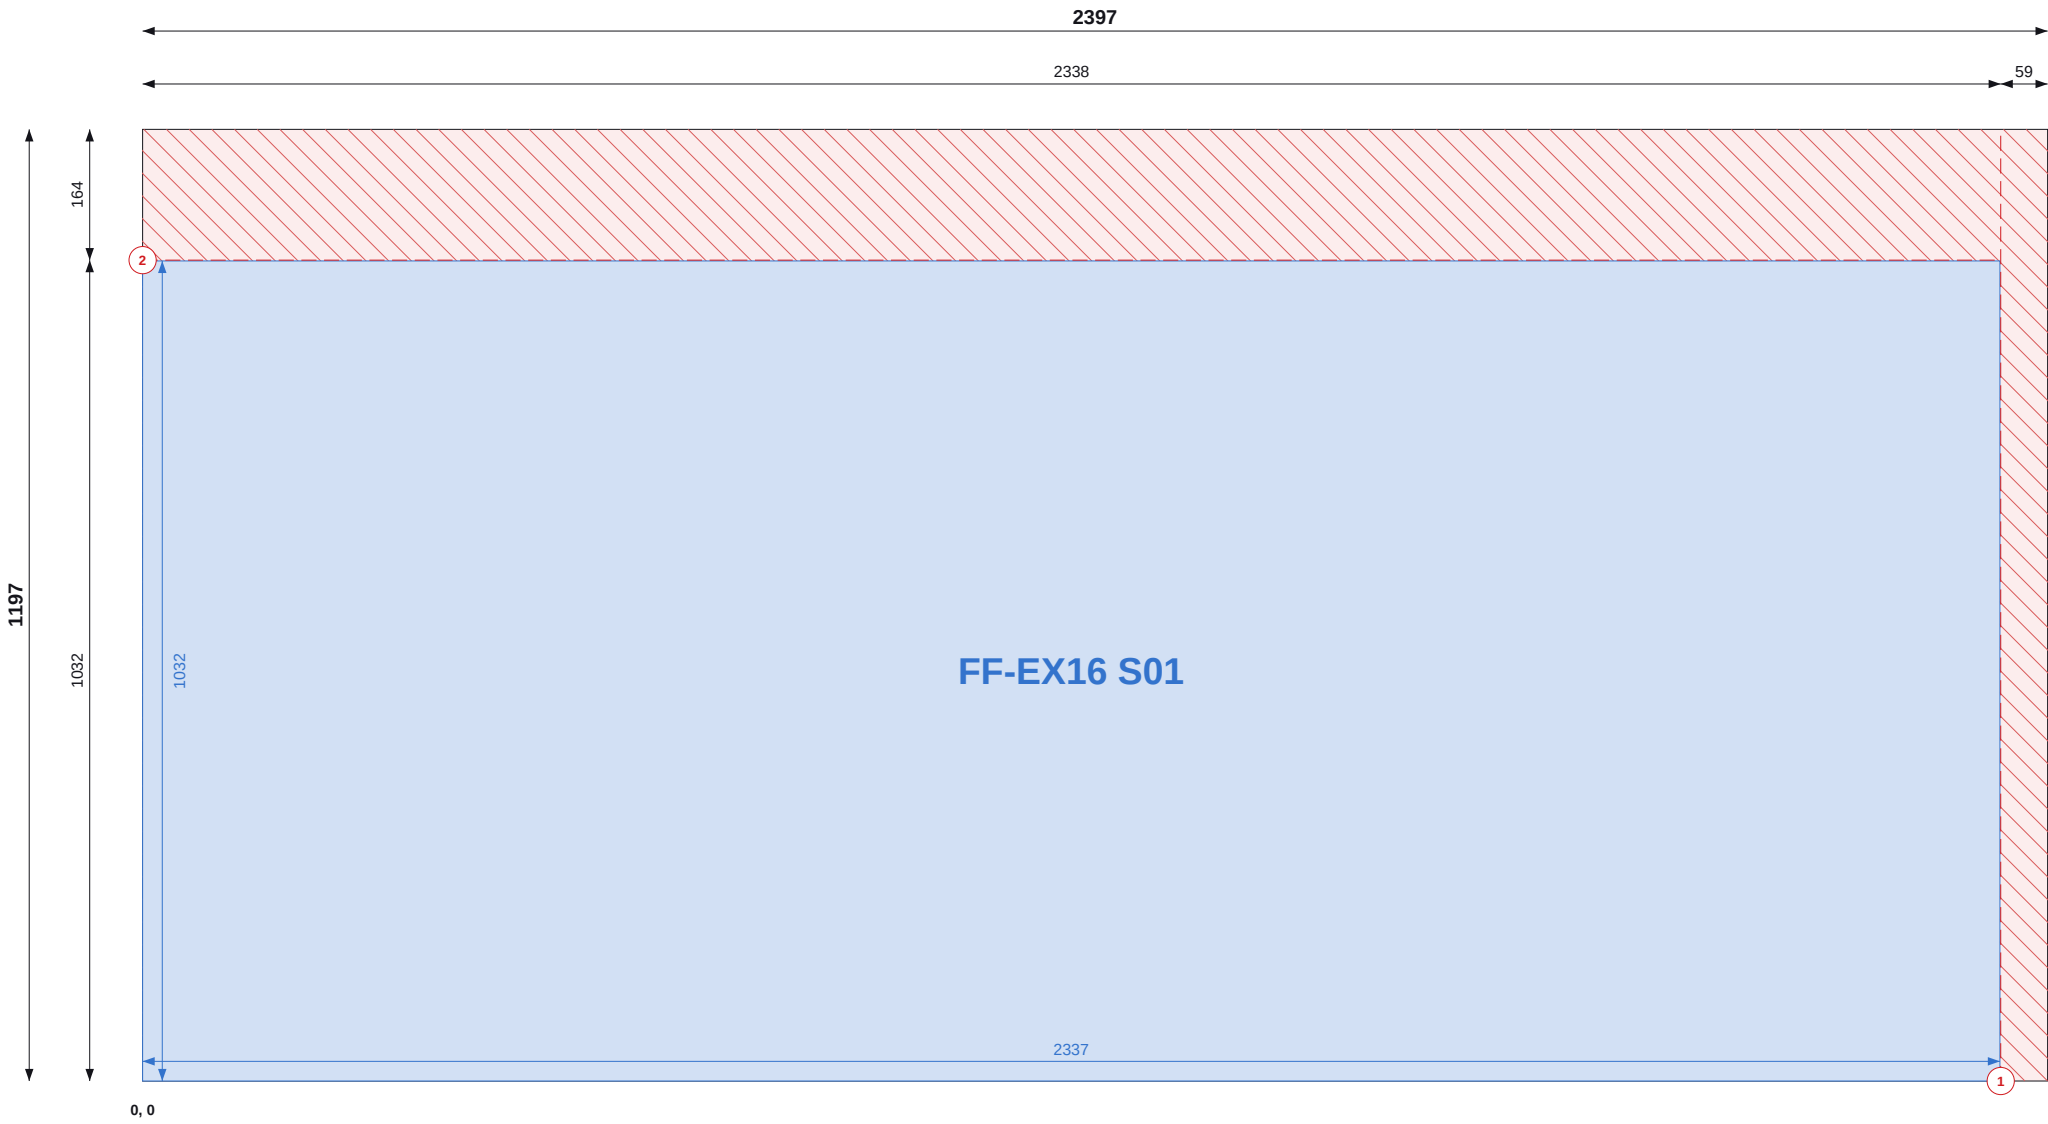

Top / left chains = saw cut positions (to cut centres). Coloured = part size and position.

SHEET 12 OF 34

THIS SHEET

Item	Value
Parts	1
Used / waste	84.0% / 0.46 m2
Reusable offcuts	0
Saw cuts / shared	2 / 0

PIECES (POSITION = BOTTOM-LEFT CORNER)

Label	Size	X, Y
FF-EX16 S01	1032 x 2337	0, 0

NOTES

- Cut from OSB/3 9mm 1197x2397, 2mm saw kerf. Viewed on the face; dimensions from the sheet's bottom-left corner (0,0). Red numbered lines = saw cuts in order, each edge to edge.
- Coloured dimensions belong to the part of that colour: its width and height, and its position from the sheet edges. Raked parts: corner coordinates at each corner.
- Red hatch = waste. Labels = panel + piece mark on the manufacture drawing.

REVISIONS

REV	DATE	DESCRIPTION
C01	13.09.26	Construction issue



TLS TIMBER FRAME

Design & Manufacture

Scan: 3D model + drawings




CLIENT	PROJECT
MP Adams	MP Adams Plot 3, Eckington

DRAWING TITLE			
OSB CUTTING - FIRST FLOOR - SHEET 12 OF 34			
OSB/3 9mm 1197x2397 First Floor			

SCALE	SIZE	DATE	DRAWN
NTS	A3	13.09.26	TS

STATUS	DRAWING No.	REV
CONSTRUCTION	P3-CP-OSB-02 / 12	C01

Do not scale. All dimensions in mm. Check all dimensions on site.

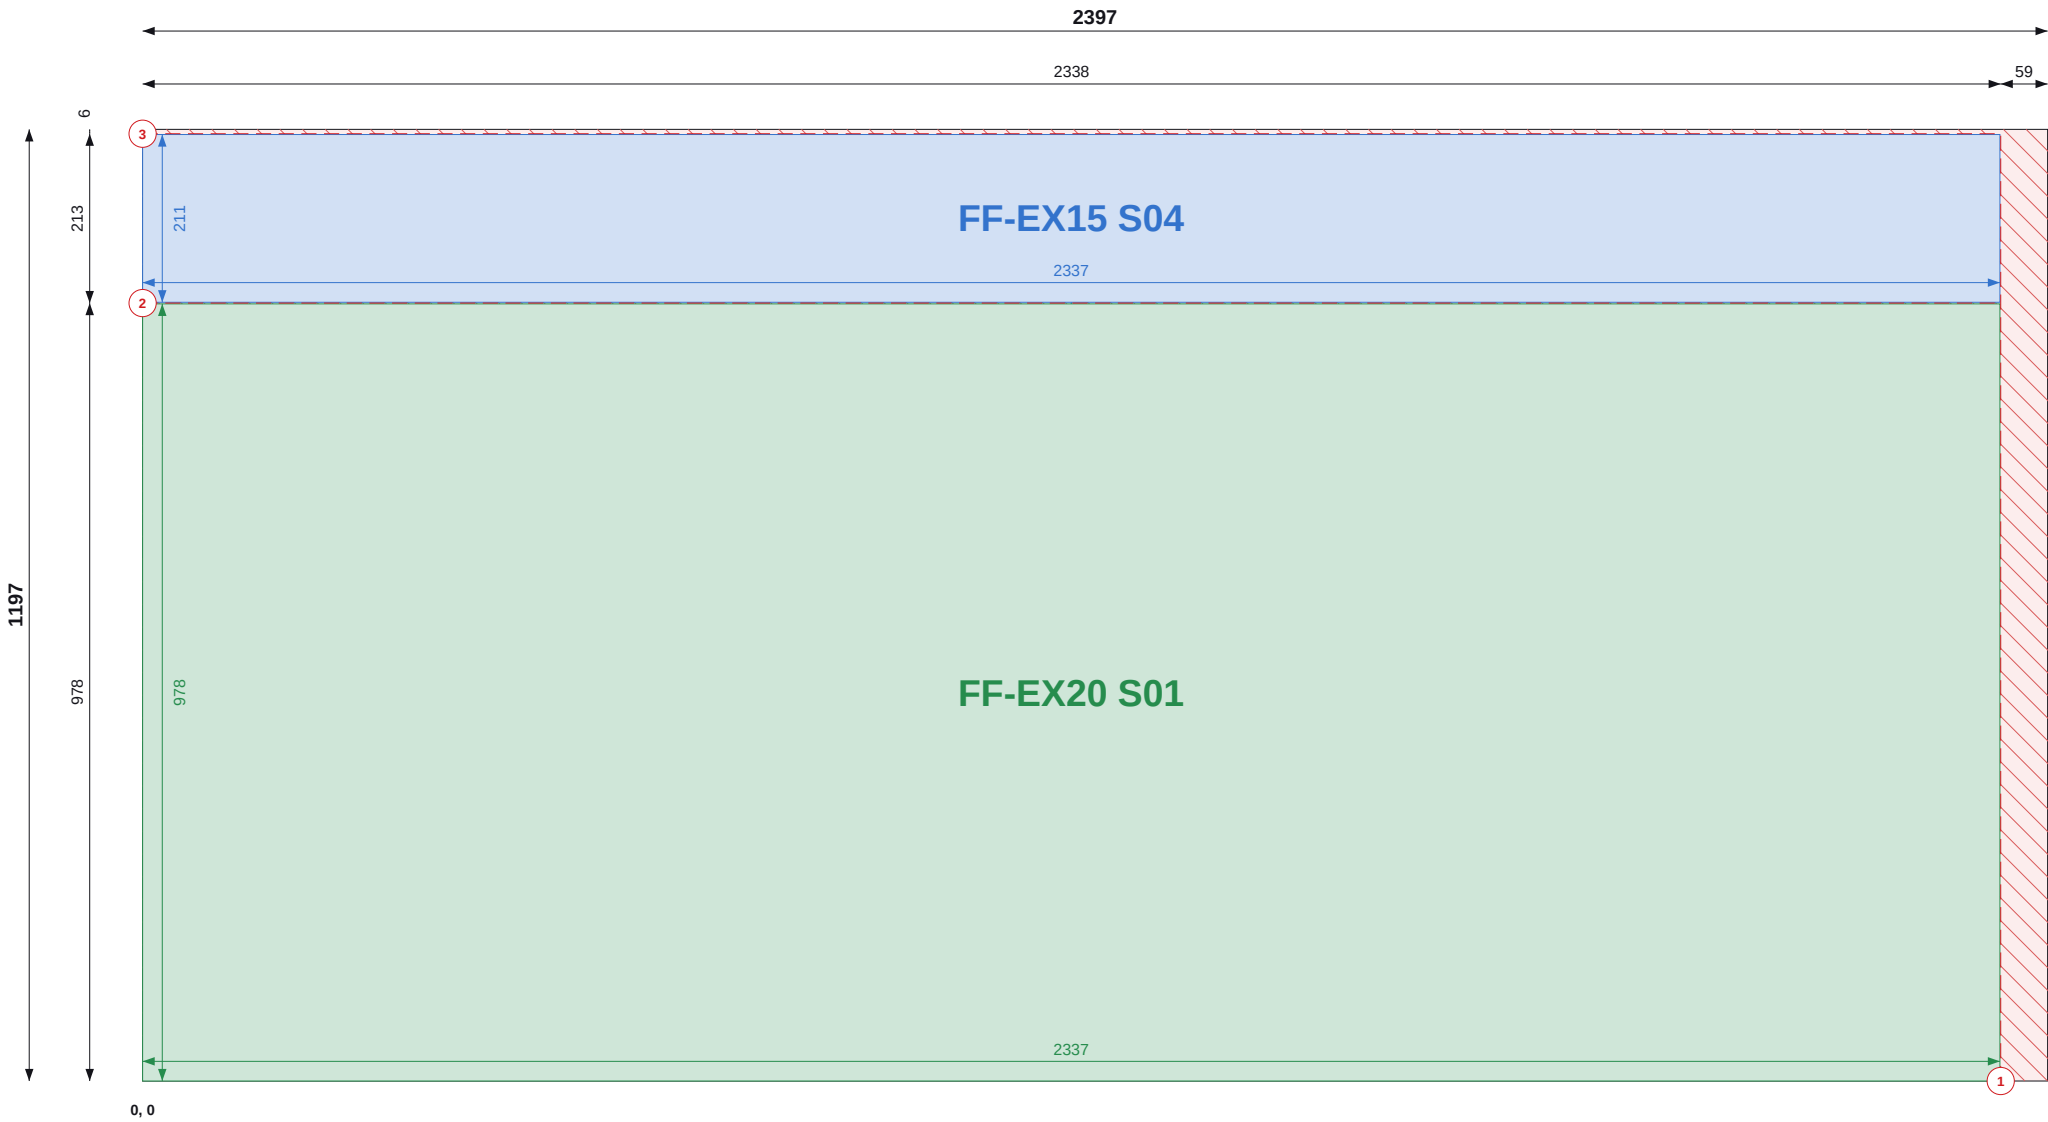

Top / left chains = saw cut positions (to cut centres). Coloured = part size and position.

SHEET 13 OF 34

THIS SHEET

Item	Value
Parts	2
Used / waste	96.8% / 0.09 m2
Reusable offcuts	0
Saw cuts / shared	3 / 1

PIECES (POSITION = BOTTOM-LEFT CORNER)

Label	Size	X, Y
FF-EX15 S04	211 x 2337	0, 980
FF-EX20 S01	978 x 2337	0, 0

NOTES

- Cut from OSB/3 9mm 1197x2397, 2mm saw kerf. Viewed on the face; dimensions from the sheet's bottom-left corner (0,0). Red numbered lines = saw cuts in order, each edge to edge.
- Coloured dimensions belong to the part of that colour: its width and height, and its position from the sheet edges. Raked parts: corner coordinates at each corner.
- Red hatch = waste. Labels = panel + piece mark on the manufacture drawing.

REVISIONS

REV	DATE	DESCRIPTION
C01	13.09.26	Construction issue



TLS TIMBER FRAME

Design & Manufacture

Scan: 3D model + drawings




CLIENT MP Adams	PROJECT MP Adams Plot 3, Eckington
--------------------	---------------------------------------

DRAWING TITLE OSB CUTTING - FIRST FLOOR - SHEET 13 OF 34			
OSB/3 9mm 1197x2397 First Floor			

SCALE NTS	SIZE A3	DATE 13.09.26	DRAWN TS
--------------	------------	------------------	-------------

STATUS CONSTRUCTION	DRAWING No. P3-CP-OSB-02 / 13	REV C01
-------------------------------	---	-------------------

Do not scale. All dimensions in mm. Check all dimensions on site.

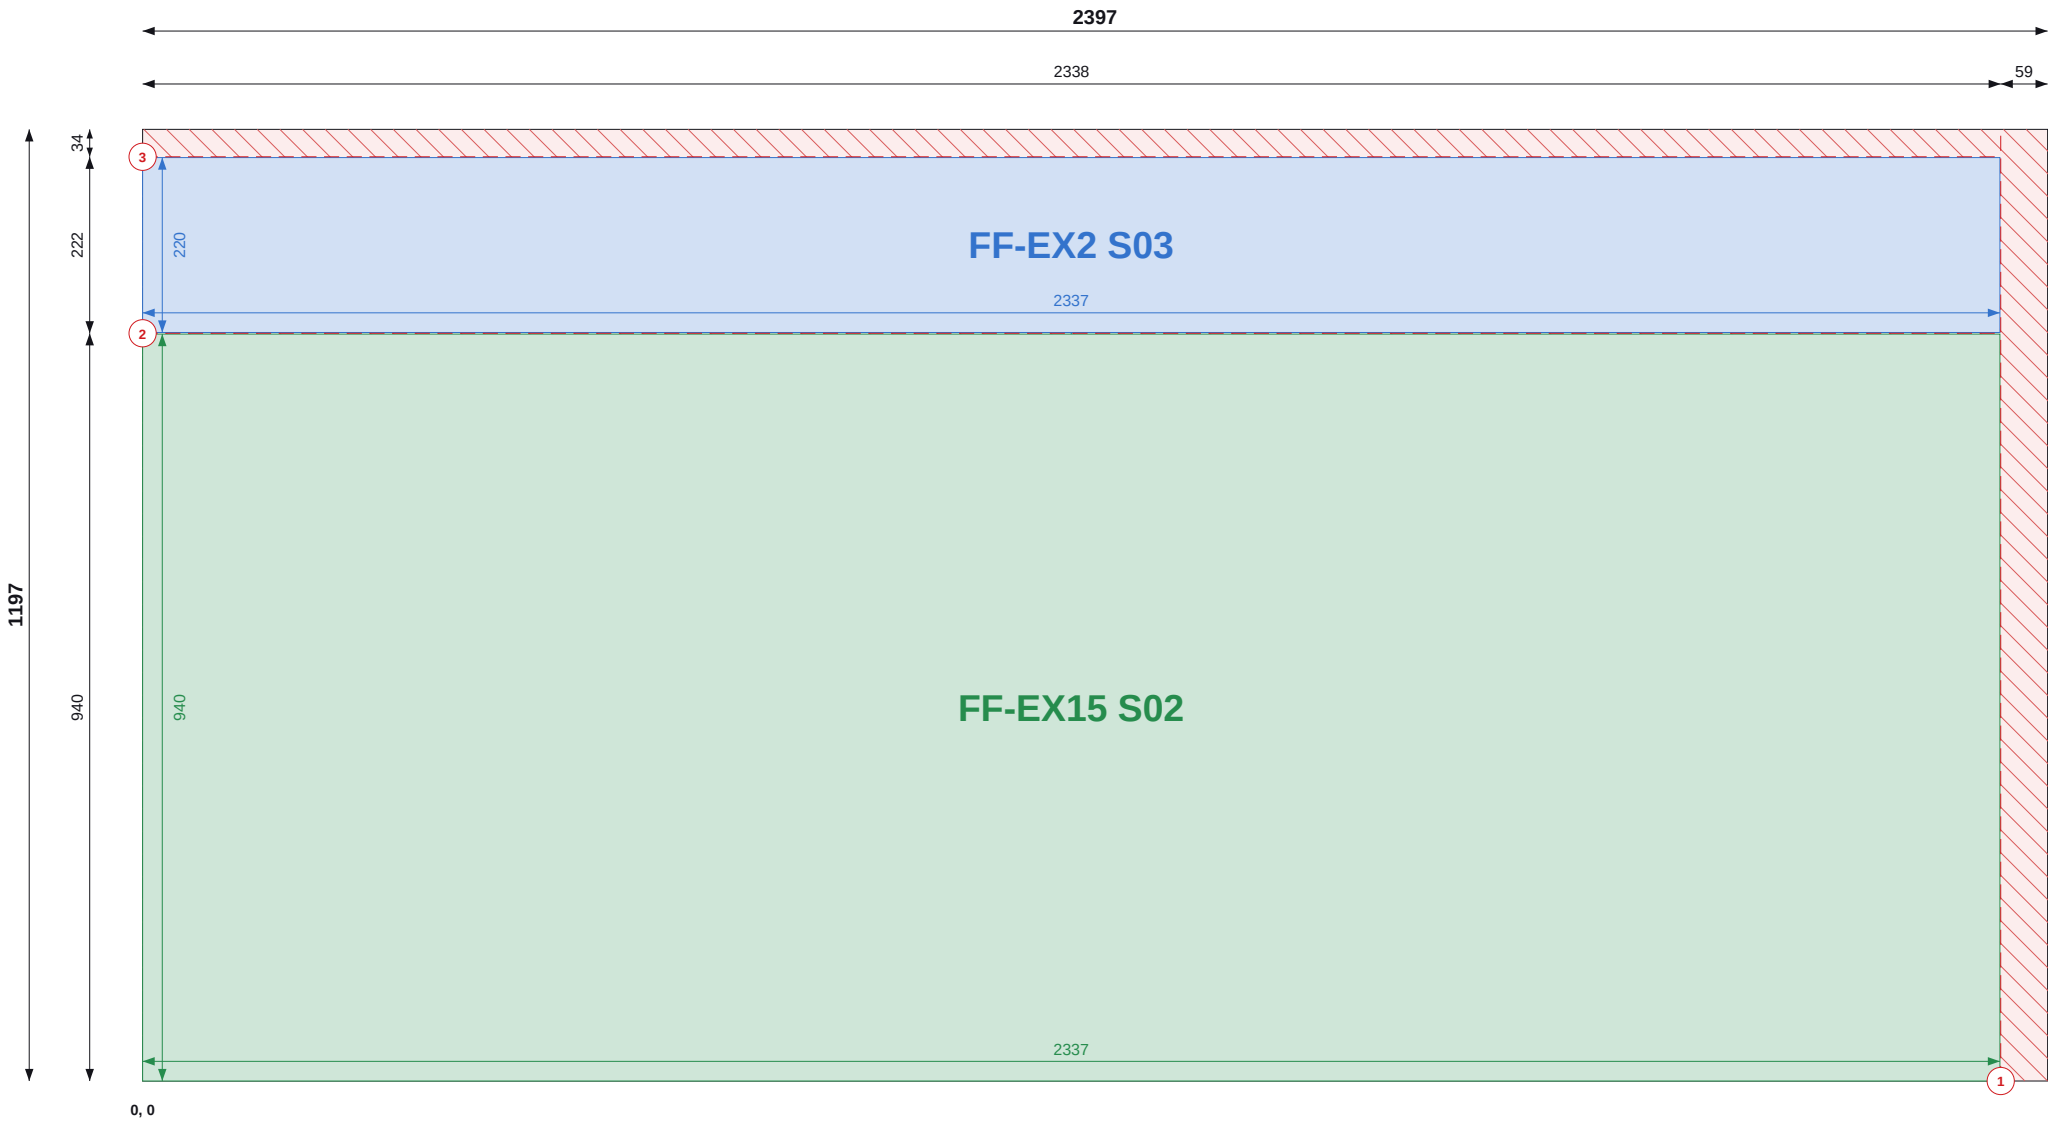

Top / left chains = saw cut positions (to cut centres). Coloured = part size and position.

SHEET 14 OF 34

THIS SHEET

Item	Value
Parts	2
Used / waste	94.4% / 0.16 m2
Reusable offcuts	0
Saw cuts / shared	3 / 1

PIECES (POSITION = BOTTOM-LEFT CORNER)

Label	Size	X, Y
FF-EX2 S03	220 x 2337	0, 942
FF-EX15 S02	940 x 2337	0, 0

NOTES

- Cut from OSB/3 9mm 1197x2397, 2mm saw kerf. Viewed on the face; dimensions from the sheet's bottom-left corner (0,0). Red numbered lines = saw cuts in order, each edge to edge.
- Coloured dimensions belong to the part of that colour: its width and height, and its position from the sheet edges. Raked parts: corner coordinates at each corner.
- Red hatch = waste. Labels = panel + piece mark on the manufacture drawing.

REVISIONS

REV	DATE	DESCRIPTION
C01	13.09.26	Construction issue



TLS TIMBER FRAME

Design & Manufacture

Scan: 3D model + drawings




CLIENT	PROJECT
MP Adams	MP Adams Plot 3, Eckington

DRAWING TITLE
OSB CUTTING - FIRST FLOOR - SHEET 14 OF 34
OSB/3 9mm 1197x2397 First Floor

SCALE	SIZE	DATE	DRAWN
NTS	A3	13.09.26	TS

STATUS	DRAWING No.	REV
CONSTRUCTION	P3-CP-OSB-02 / 14	C01

Do not scale. All dimensions in mm. Check all dimensions on site.

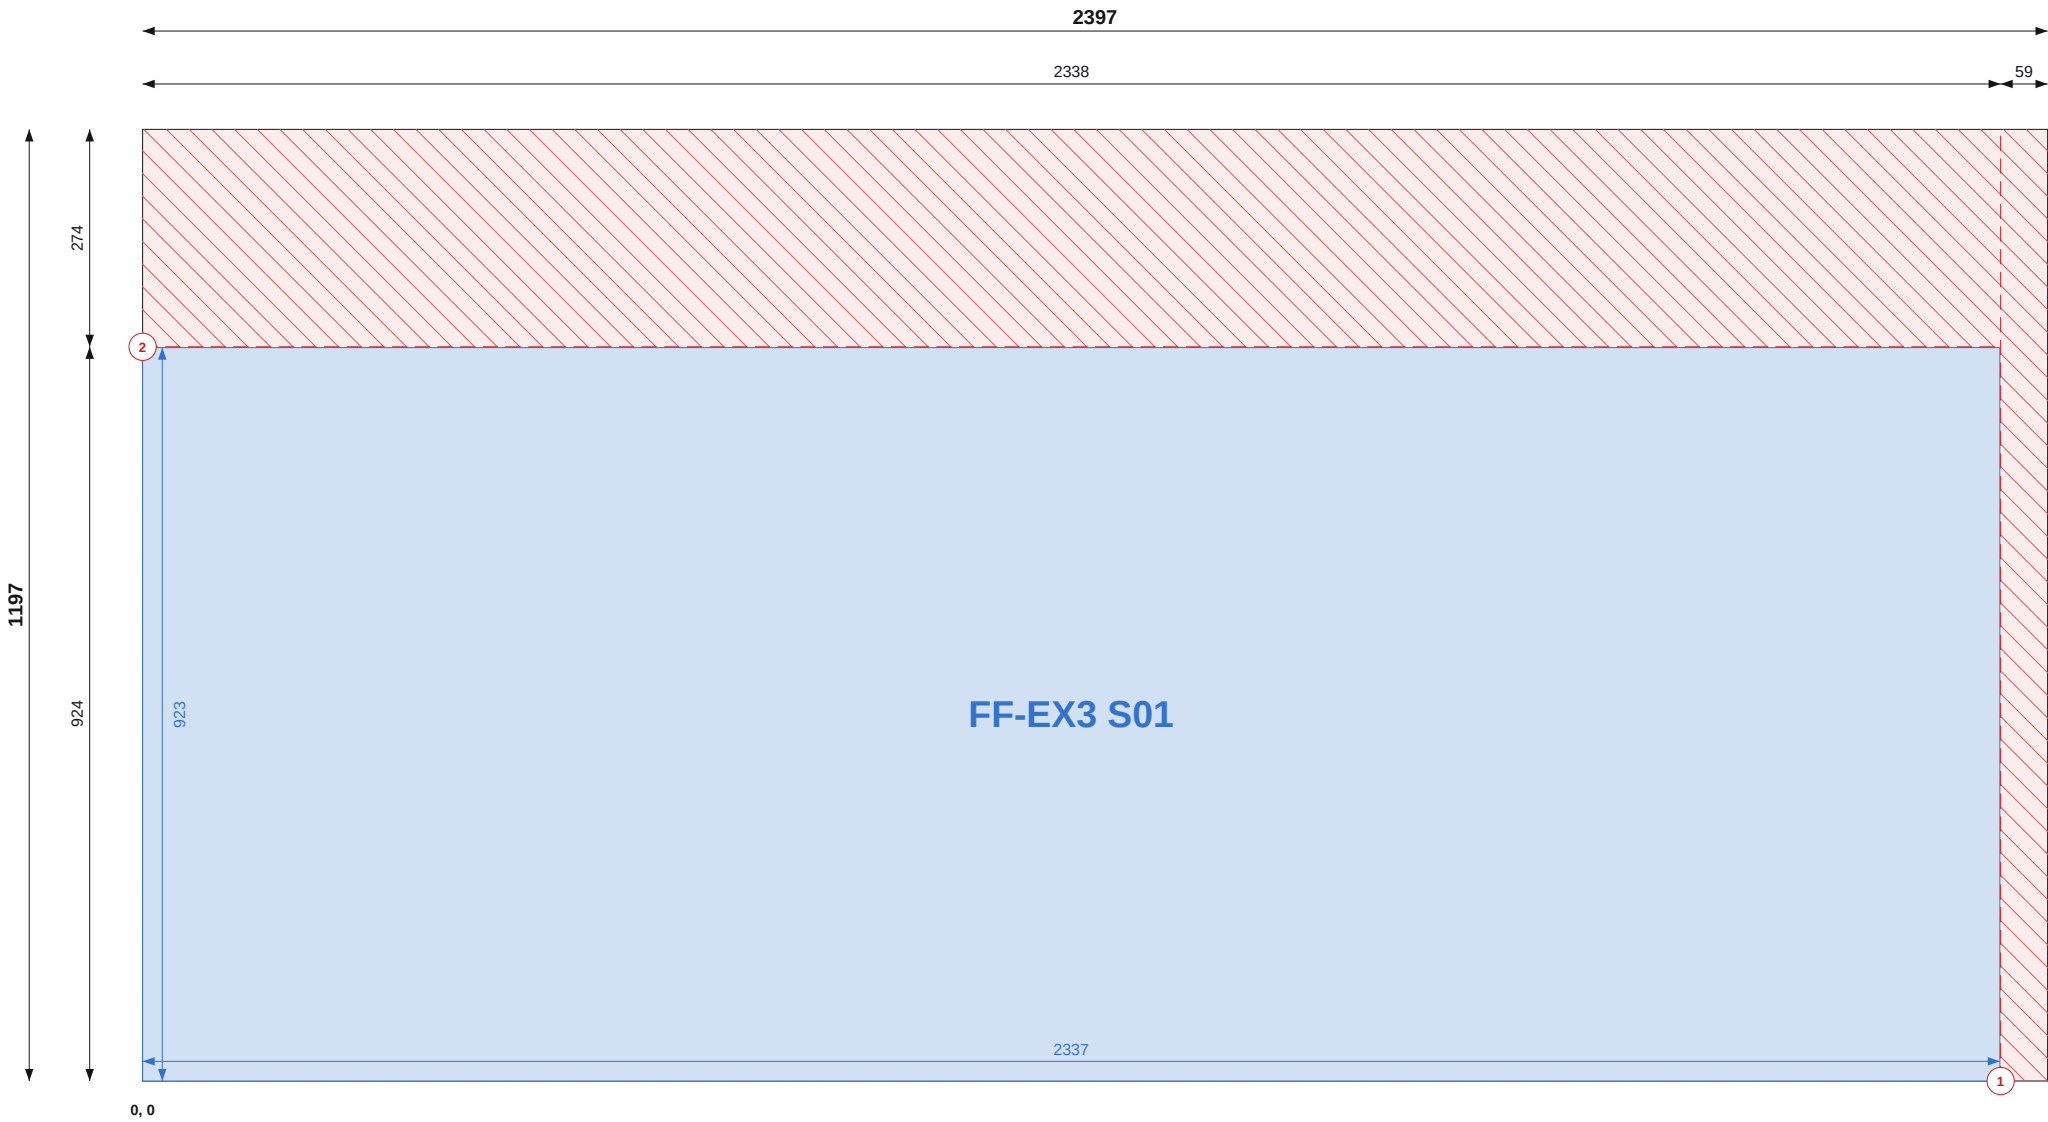

Top / left chains = saw cut positions (to cut centres). Coloured = part size and position.

SHEET 15 OF 34

THIS SHEET

Item	Value
Parts	1
Used / waste	75.1% / 0.71 m2
Reusable offcuts	0
Saw cuts / shared	2 / 0

PIECES (POSITION = BOTTOM-LEFT CORNER)

Label	Size	X, Y
FF-EX3 S01	923 x 2337	0, 0

NOTES

- Cut from OSB/3 9mm 1197x2397, 2mm saw kerf. Viewed on the face; dimensions from the sheet's bottom-left corner (0,0). Red numbered lines = saw cuts in order, each edge to edge.
- Coloured dimensions belong to the part of that colour: its width and height, and its position from the sheet edges. Raked parts: corner coordinates at each corner.
- Red hatch = waste. Labels = panel + piece mark on the manufacture drawing.

REVISIONS

REV	DATE	DESCRIPTION
C01	13.09.26	Construction issue



TLS TIMBER FRAME
Design & Manufacture
Scan: 3D model + drawings



CLIENT MP Adams	PROJECT MP Adams Plot 3, Eckington
--------------------	---------------------------------------


DRAWING TITLE OSB CUTTING - FIRST FLOOR - SHEET 15 OF 34
--

OSB/3 9mm 1197x2397 | First Floor

SCALE NTS	SIZE A3	DATE 13.09.26	DRAWN TS
--------------	------------	------------------	-------------

STATUS CONSTRUCTION	DRAWING No. P3-CP-OSB-02 / 15	REV C01
-------------------------------	---	-------------------

Do not scale. All dimensions in mm. Check all dimensions on site.

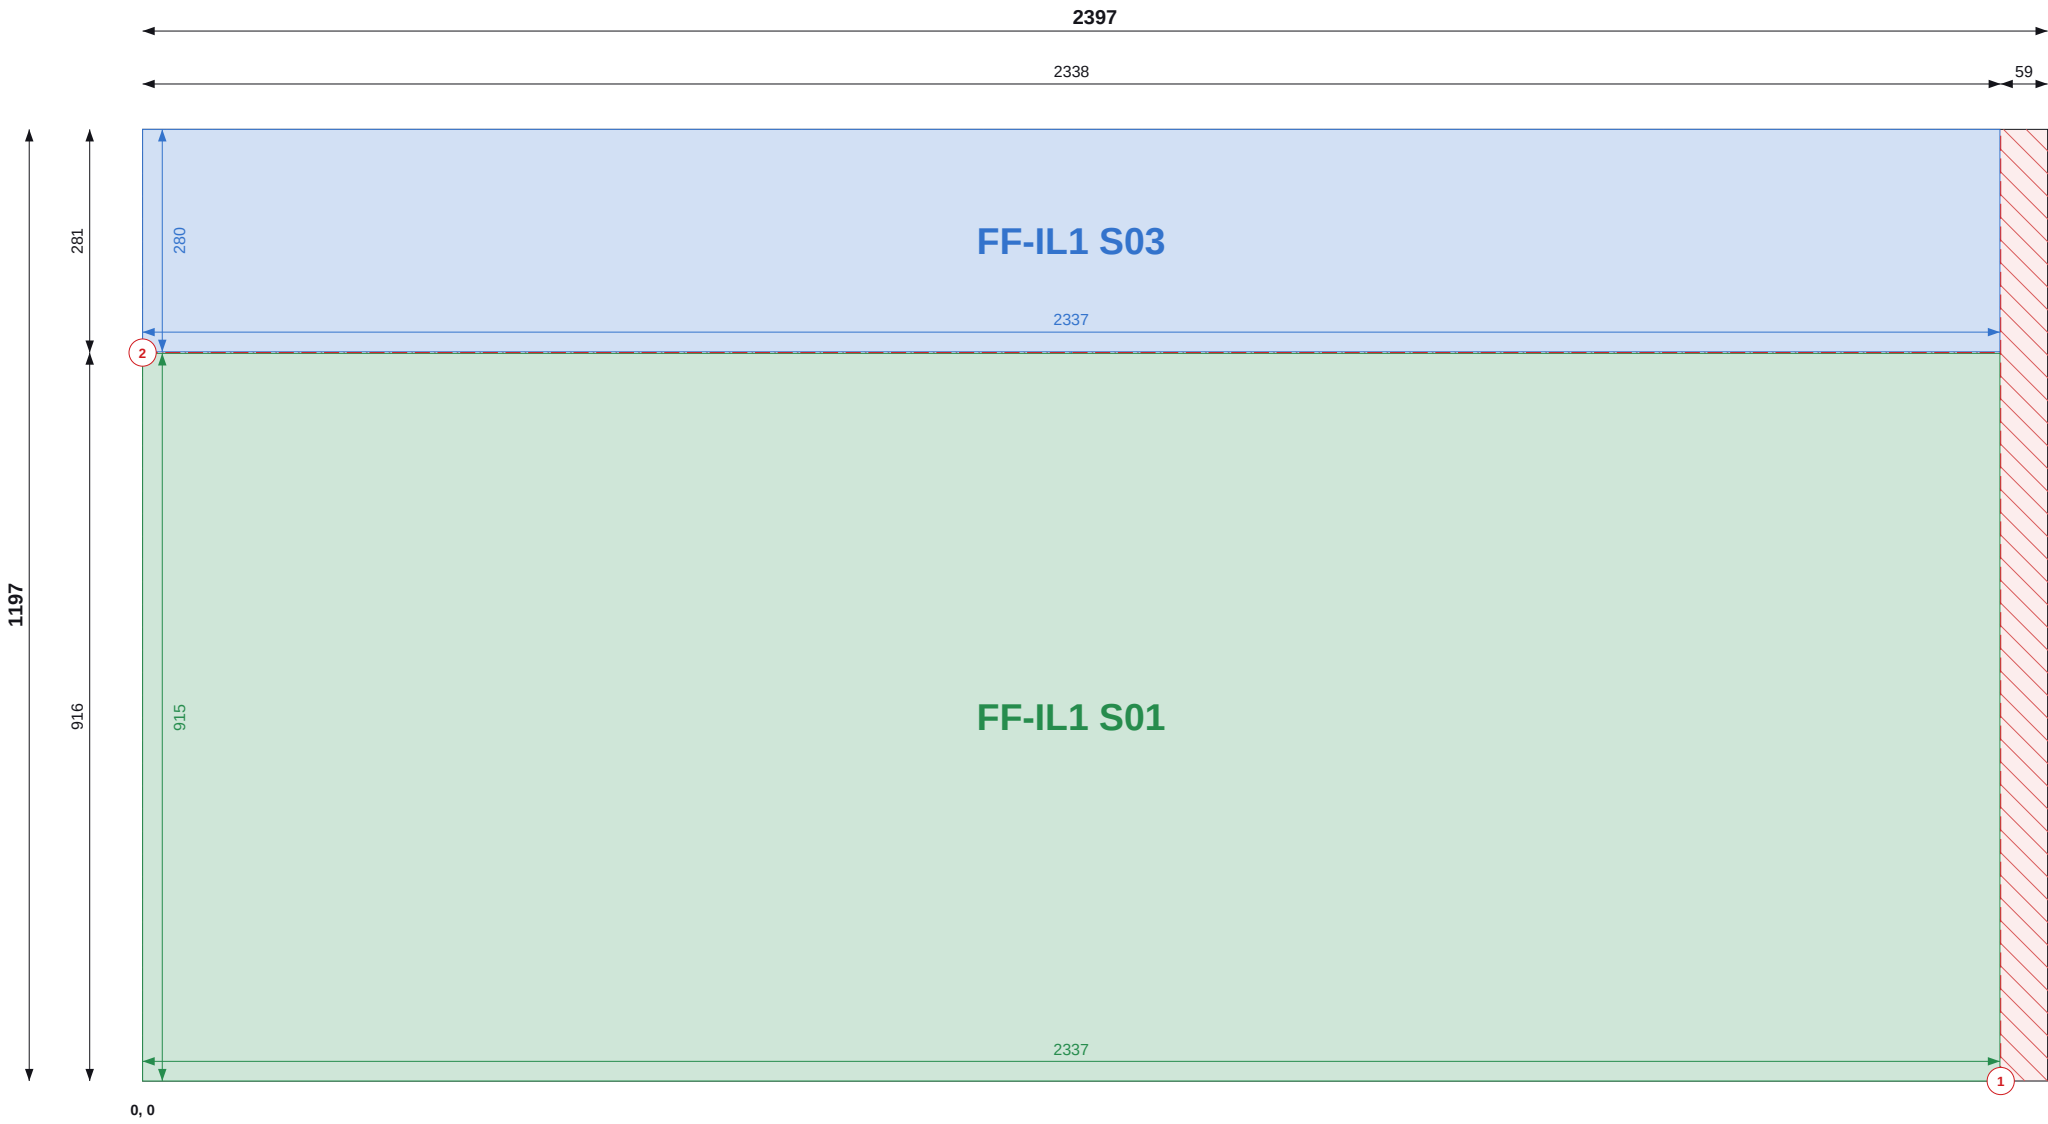

Top / left chains = saw cut positions (to cut centres). Coloured = part size and position.

SHEET 16 OF 34

THIS SHEET

Item	Value
Parts	2
Used / waste	97.3% / 0.08 m2
Reusable offcuts	0
Saw cuts / shared	2 / 1

PIECES (POSITION = BOTTOM-LEFT CORNER)

Label	Size	X, Y
FF-IL1 S03	280 x 2337	0, 917
FF-IL1 S01	915 x 2337	0, 0

NOTES

- Cut from OSB/3 9mm 1197x2397, 2mm saw kerf. Viewed on the face; dimensions from the sheet's bottom-left corner (0,0). Red numbered lines = saw cuts in order, each edge to edge.
- Coloured dimensions belong to the part of that colour: its width and height, and its position from the sheet edges. Raked parts: corner coordinates at each corner.
- Red hatch = waste. Labels = panel + piece mark on the manufacture drawing.

REVISIONS

REV	DATE	DESCRIPTION
C01	13.09.26	Construction issue



TLS TIMBER FRAME

Design & Manufacture

Scan: 3D model + drawings




CLIENT	PROJECT
MP Adams	MP Adams Plot 3, Eckington

DRAWING TITLE			
OSB CUTTING - FIRST FLOOR - SHEET 16 OF 34			
OSB/3 9mm 1197x2397 First Floor			

SCALE	SIZE	DATE	DRAWN
NTS	A3	13.09.26	TS

STATUS	DRAWING No.	REV
CONSTRUCTION	P3-CP-OSB-02 / 16	C01

Do not scale. All dimensions in mm. Check all dimensions on site.

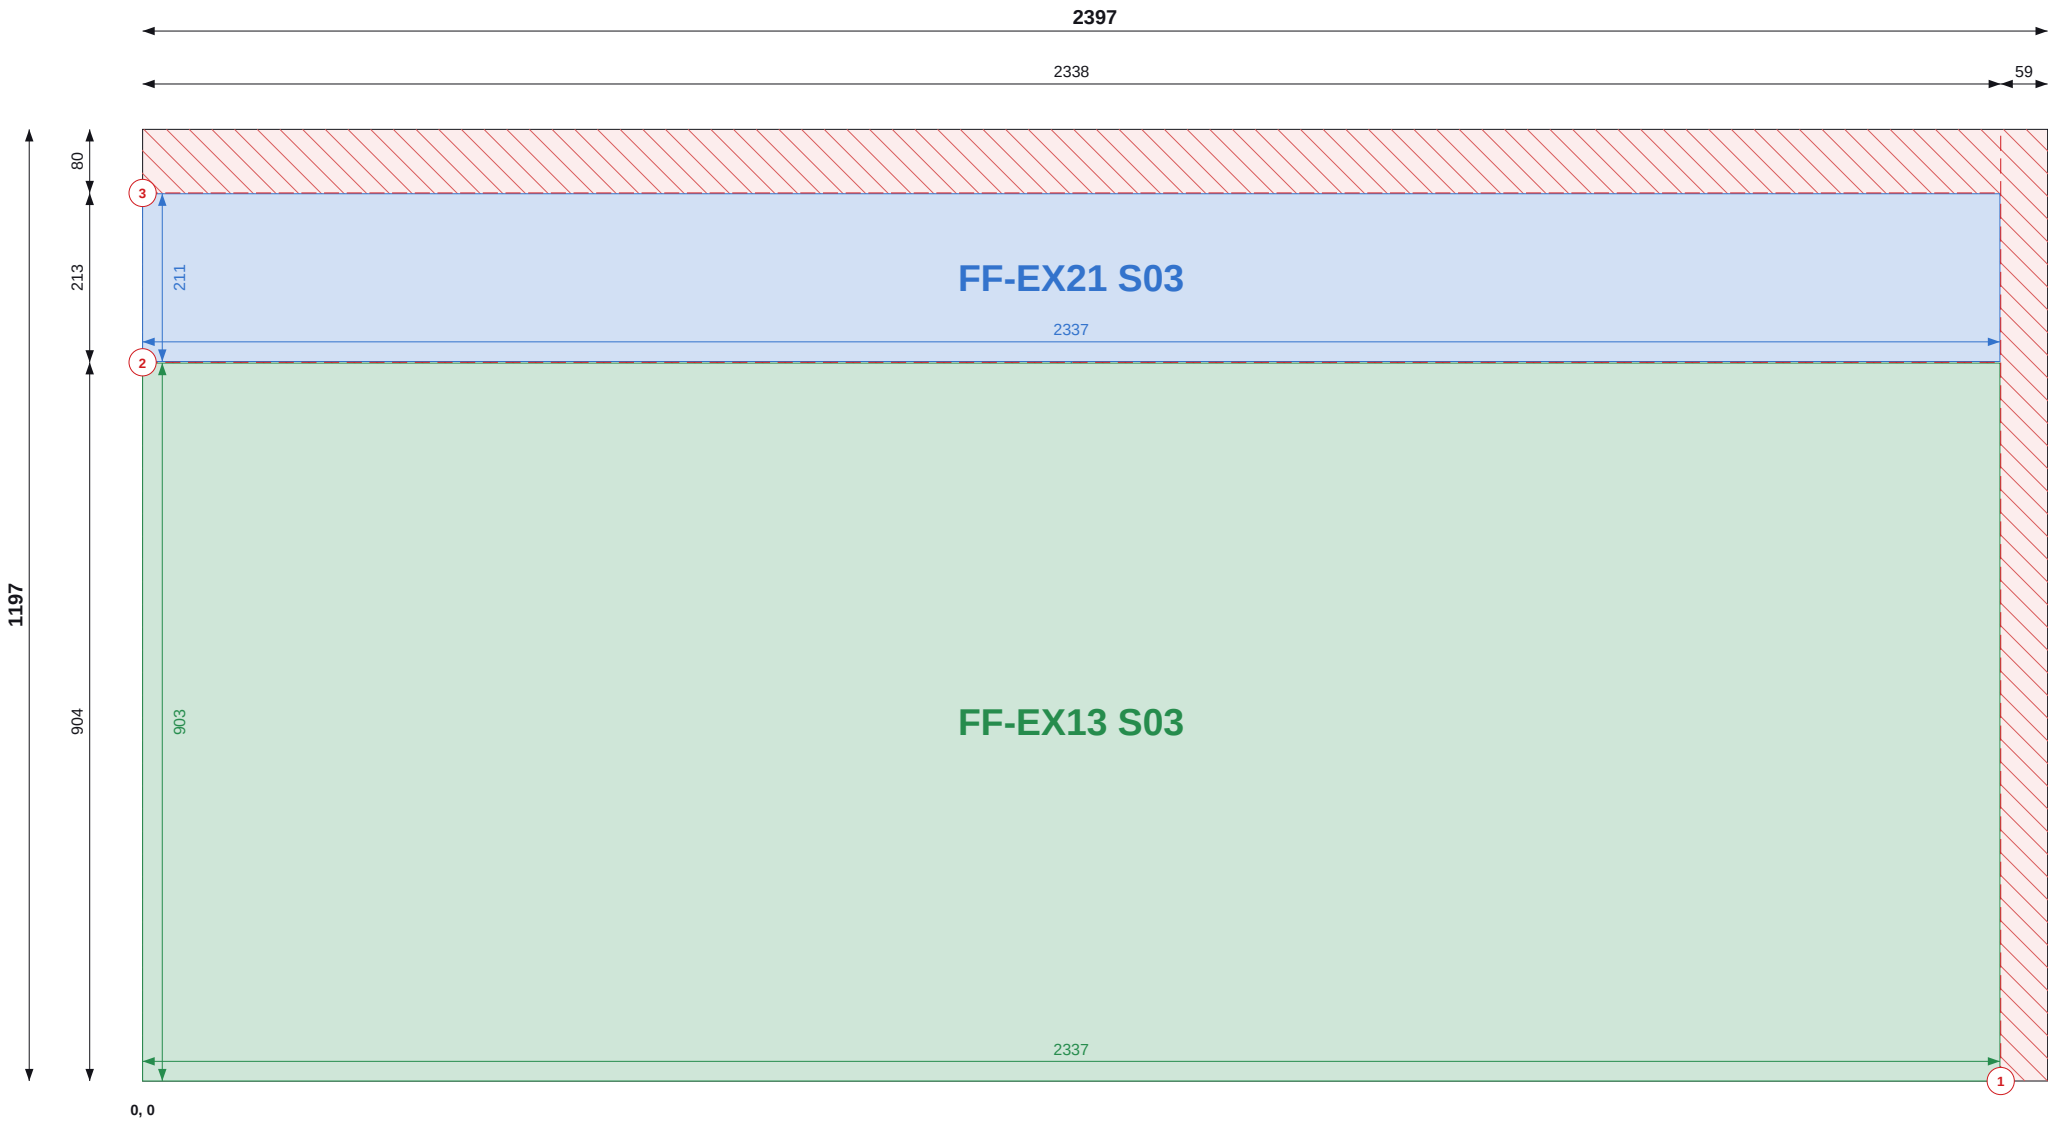

Top / left chains = saw cut positions (to cut centres). Coloured = part size and position.

SHEET 17 OF 34

THIS SHEET

Item	Value
Parts	2
Used / waste	90.7% / 0.27 m2
Reusable offcuts	0
Saw cuts / shared	3 / 1

PIECES (POSITION = BOTTOM-LEFT CORNER)

Label	Size	X, Y
FF-EX21 S03	211 x 2337	0, 905
FF-EX13 S03	903 x 2337	0, 0

NOTES

- Cut from OSB/3 9mm 1197x2397, 2mm saw kerf. Viewed on the face; dimensions from the sheet's bottom-left corner (0,0). Red numbered lines = saw cuts in order, each edge to edge.
- Coloured dimensions belong to the part of that colour: its width and height, and its position from the sheet edges. Raked parts: corner coordinates at each corner.
- Red hatch = waste. Labels = panel + piece mark on the manufacture drawing.

REVISIONS

REV	DATE	DESCRIPTION
C01	13.09.26	Construction issue



TLS TIMBER FRAME

Design & Manufacture

Scan: 3D model + drawings



CLIENT	PROJECT
MP Adams	MP Adams Plot 3, Eckington


DRAWING TITLE
OSB CUTTING - FIRST FLOOR - SHEET 17 OF 34

OSB/3 9mm 1197x2397 | First Floor

SCALE	SIZE	DATE	DRAWN
NTS	A3	13.09.26	TS

STATUS	DRAWING No.	REV
CONSTRUCTION	P3-CP-OSB-02 / 17	C01

Do not scale. All dimensions in mm. Check all dimensions on site.

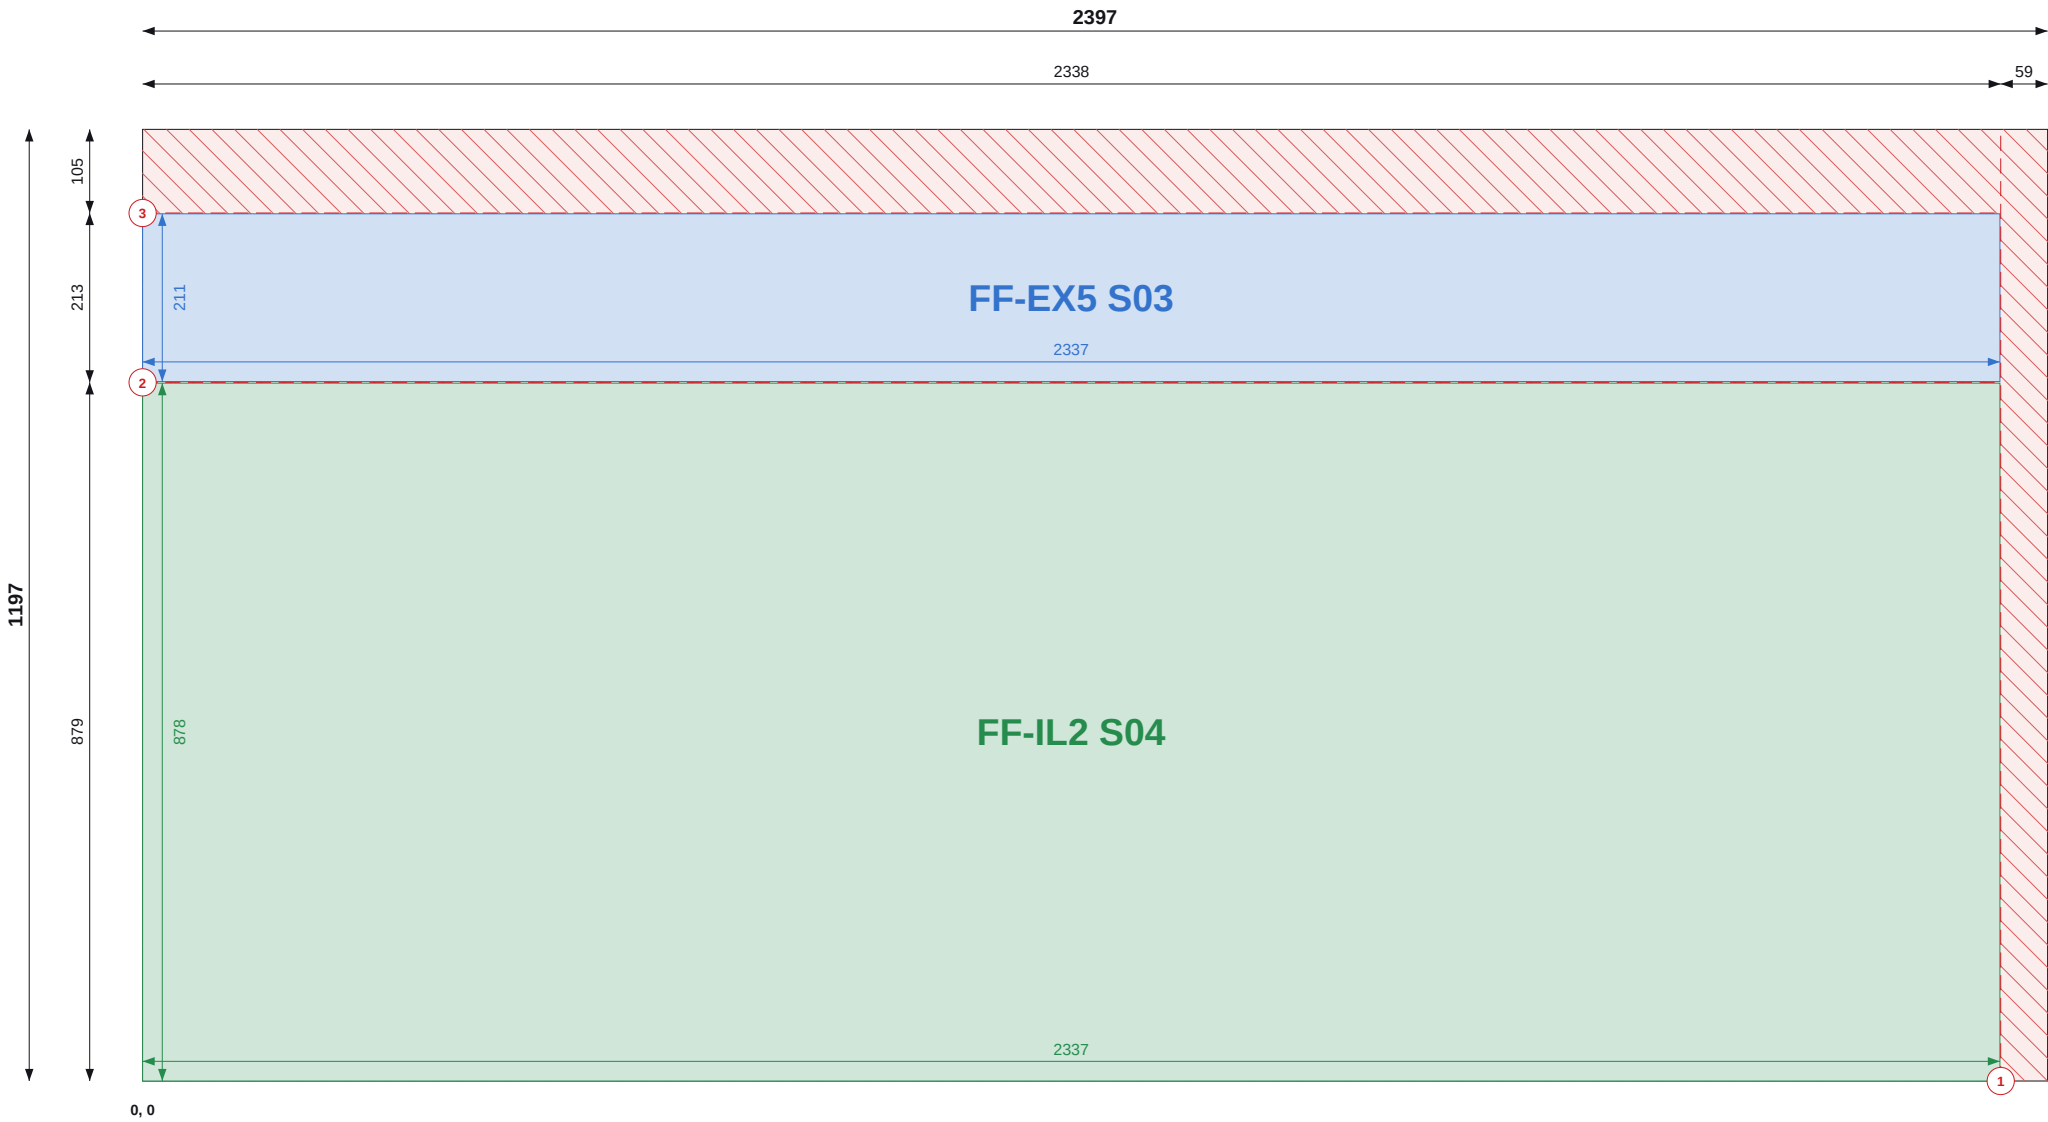

Top / left chains = saw cut positions (to cut centres). Coloured = part size and position.

SHEET 18 OF 34

THIS SHEET

Item	Value
Parts	2
Used / waste	88.7% / 0.32 m2
Reusable offcuts	0
Saw cuts / shared	3 / 1

PIECES (POSITION = BOTTOM-LEFT CORNER)

Label	Size	X, Y
FF-EX5 S03	211 x 2337	0, 880
FF-IL2 S04	878 x 2337	0, 0

NOTES

- Cut from OSB/3 9mm 1197x2397, 2mm saw kerf. Viewed on the face; dimensions from the sheet's bottom-left corner (0,0). Red numbered lines = saw cuts in order, each edge to edge.
- Coloured dimensions belong to the part of that colour: its width and height, and its position from the sheet edges. Raked parts: corner coordinates at each corner.
- Red hatch = waste. Labels = panel + piece mark on the manufacture drawing.

REVISIONS

REV	DATE	DESCRIPTION
C01	13.09.26	Construction issue



TLS TIMBER FRAME

Design & Manufacture

Scan: 3D model + drawings



CLIENT	PROJECT
MP Adams	MP Adams Plot 3, Eckington


DRAWING TITLE
OSB CUTTING - FIRST FLOOR - SHEET 18 OF 34

OSB/3 9mm 1197x2397 | First Floor

SCALE	SIZE	DATE	DRAWN
NTS	A3	13.09.26	TS

STATUS	DRAWING No.	REV
CONSTRUCTION	P3-CP-OSB-02 / 18	C01

Do not scale. All dimensions in mm. Check all dimensions on site.

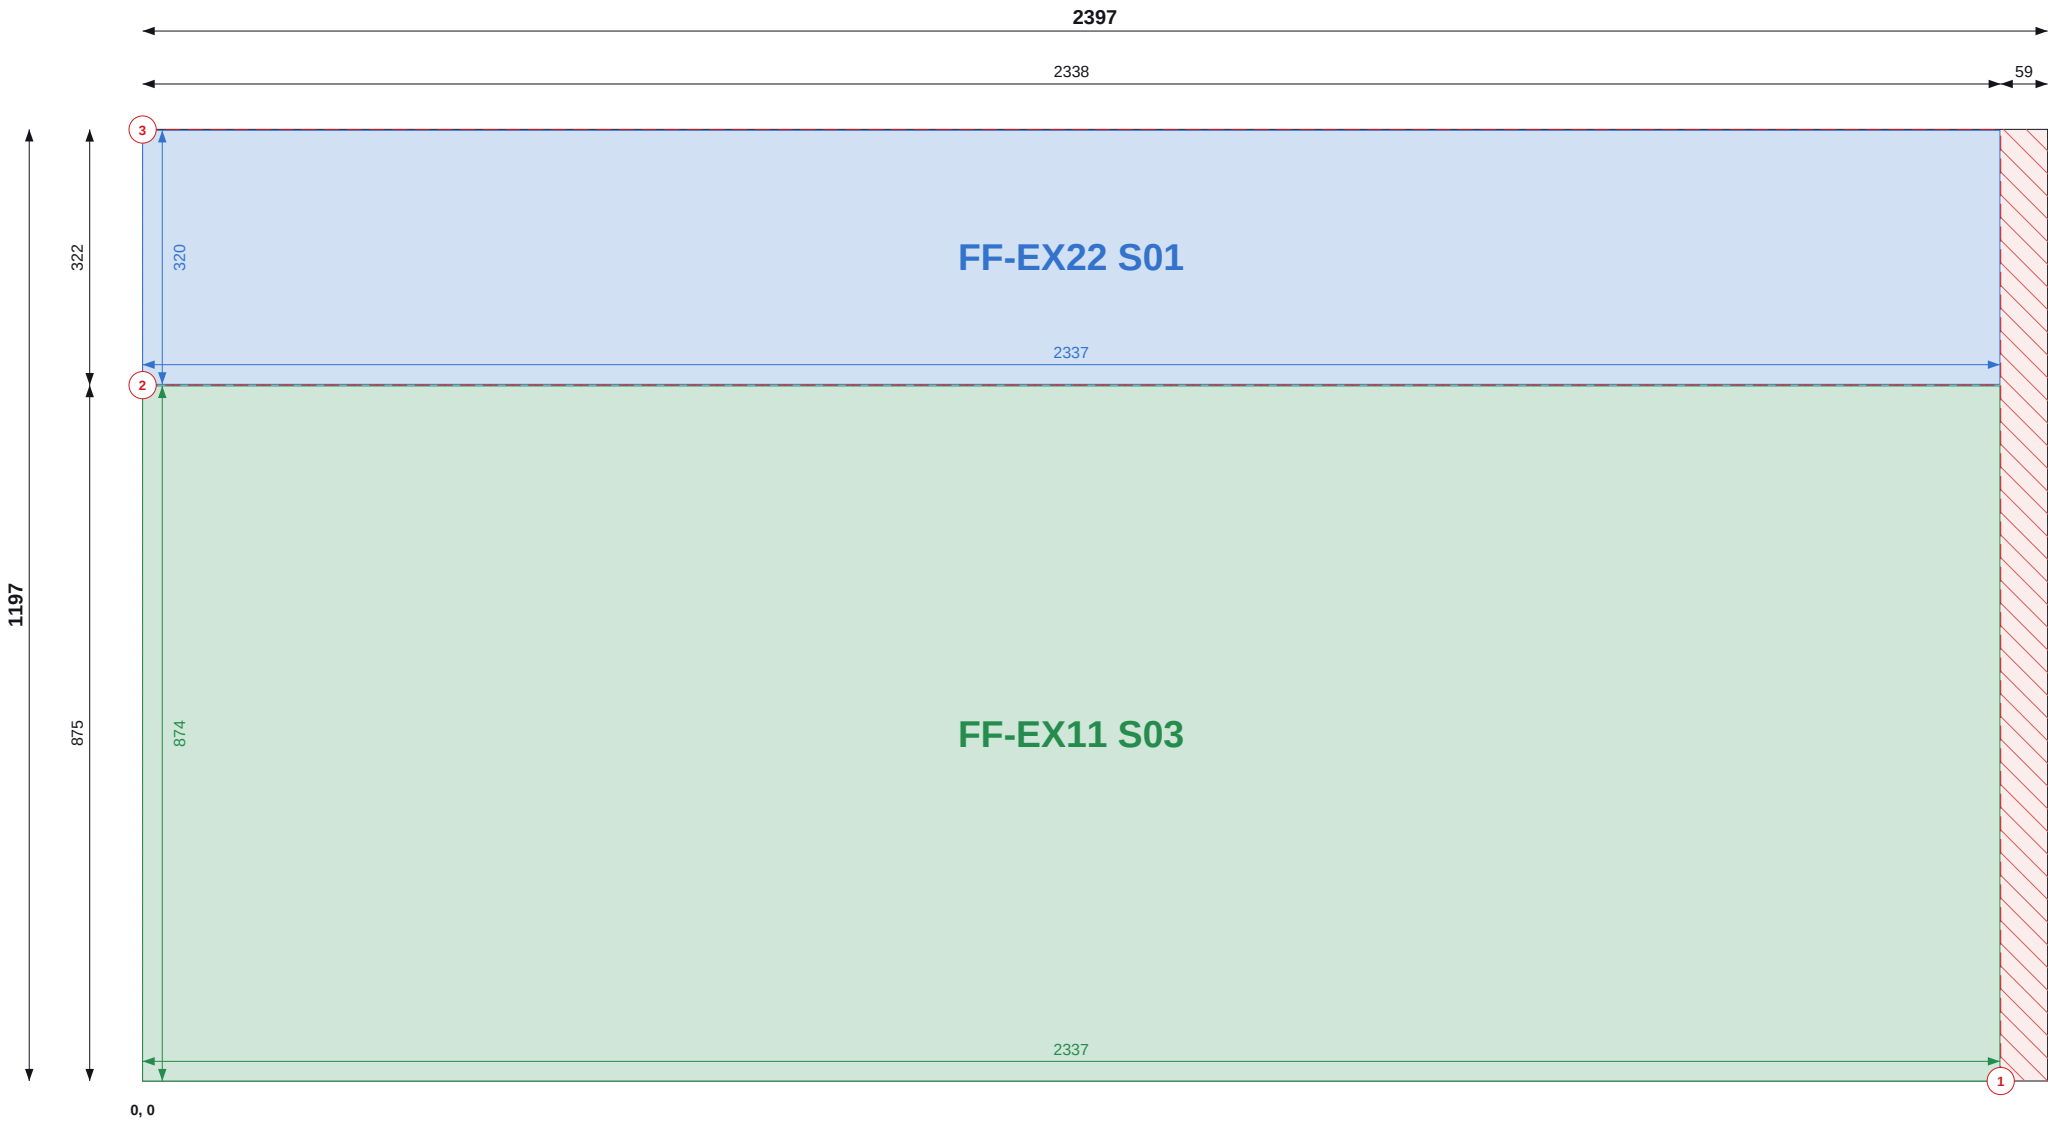

Top / left chains = saw cut positions (to cut centres). Coloured = part size and position.

SHEET 19 OF 34

THIS SHEET

Item	Value
Parts	2
Used / waste	97.2% / 0.08 m2
Reusable offcuts	0
Saw cuts / shared	3 / 1

PIECES (POSITION = BOTTOM-LEFT CORNER)

Label	Size	X, Y
FF-EX22 S01	320 x 2337	0, 876
FF-EX11 S03	874 x 2337	0, 0

NOTES

- Cut from OSB/3 9mm 1197x2397, 2mm saw kerf. Viewed on the face; dimensions from the sheet's bottom-left corner (0,0). Red numbered lines = saw cuts in order, each edge to edge.
- Coloured dimensions belong to the part of that colour: its width and height, and its position from the sheet edges. Raked parts: corner coordinates at each corner.
- Red hatch = waste. Labels = panel + piece mark on the manufacture drawing.

REVISIONS

REV	DATE	DESCRIPTION
C01	13.09.26	Construction issue



TLS TIMBER FRAME

Design & Manufacture

Scan: 3D model + drawings



CLIENT MP Adams	PROJECT MP Adams Plot 3, Eckington
--------------------	---------------------------------------


DRAWING TITLE OSB CUTTING - FIRST FLOOR - SHEET 19 OF 34
--

OSB/3 9mm 1197x2397 | First Floor

SCALE NTS	SIZE A3	DATE 13.09.26	DRAWN TS
--------------	------------	------------------	-------------

STATUS CONSTRUCTION	DRAWING No. P3-CP-OSB-02 / 19	REV C01
-------------------------------	---	-------------------

Do not scale. All dimensions in mm. Check all dimensions on site.

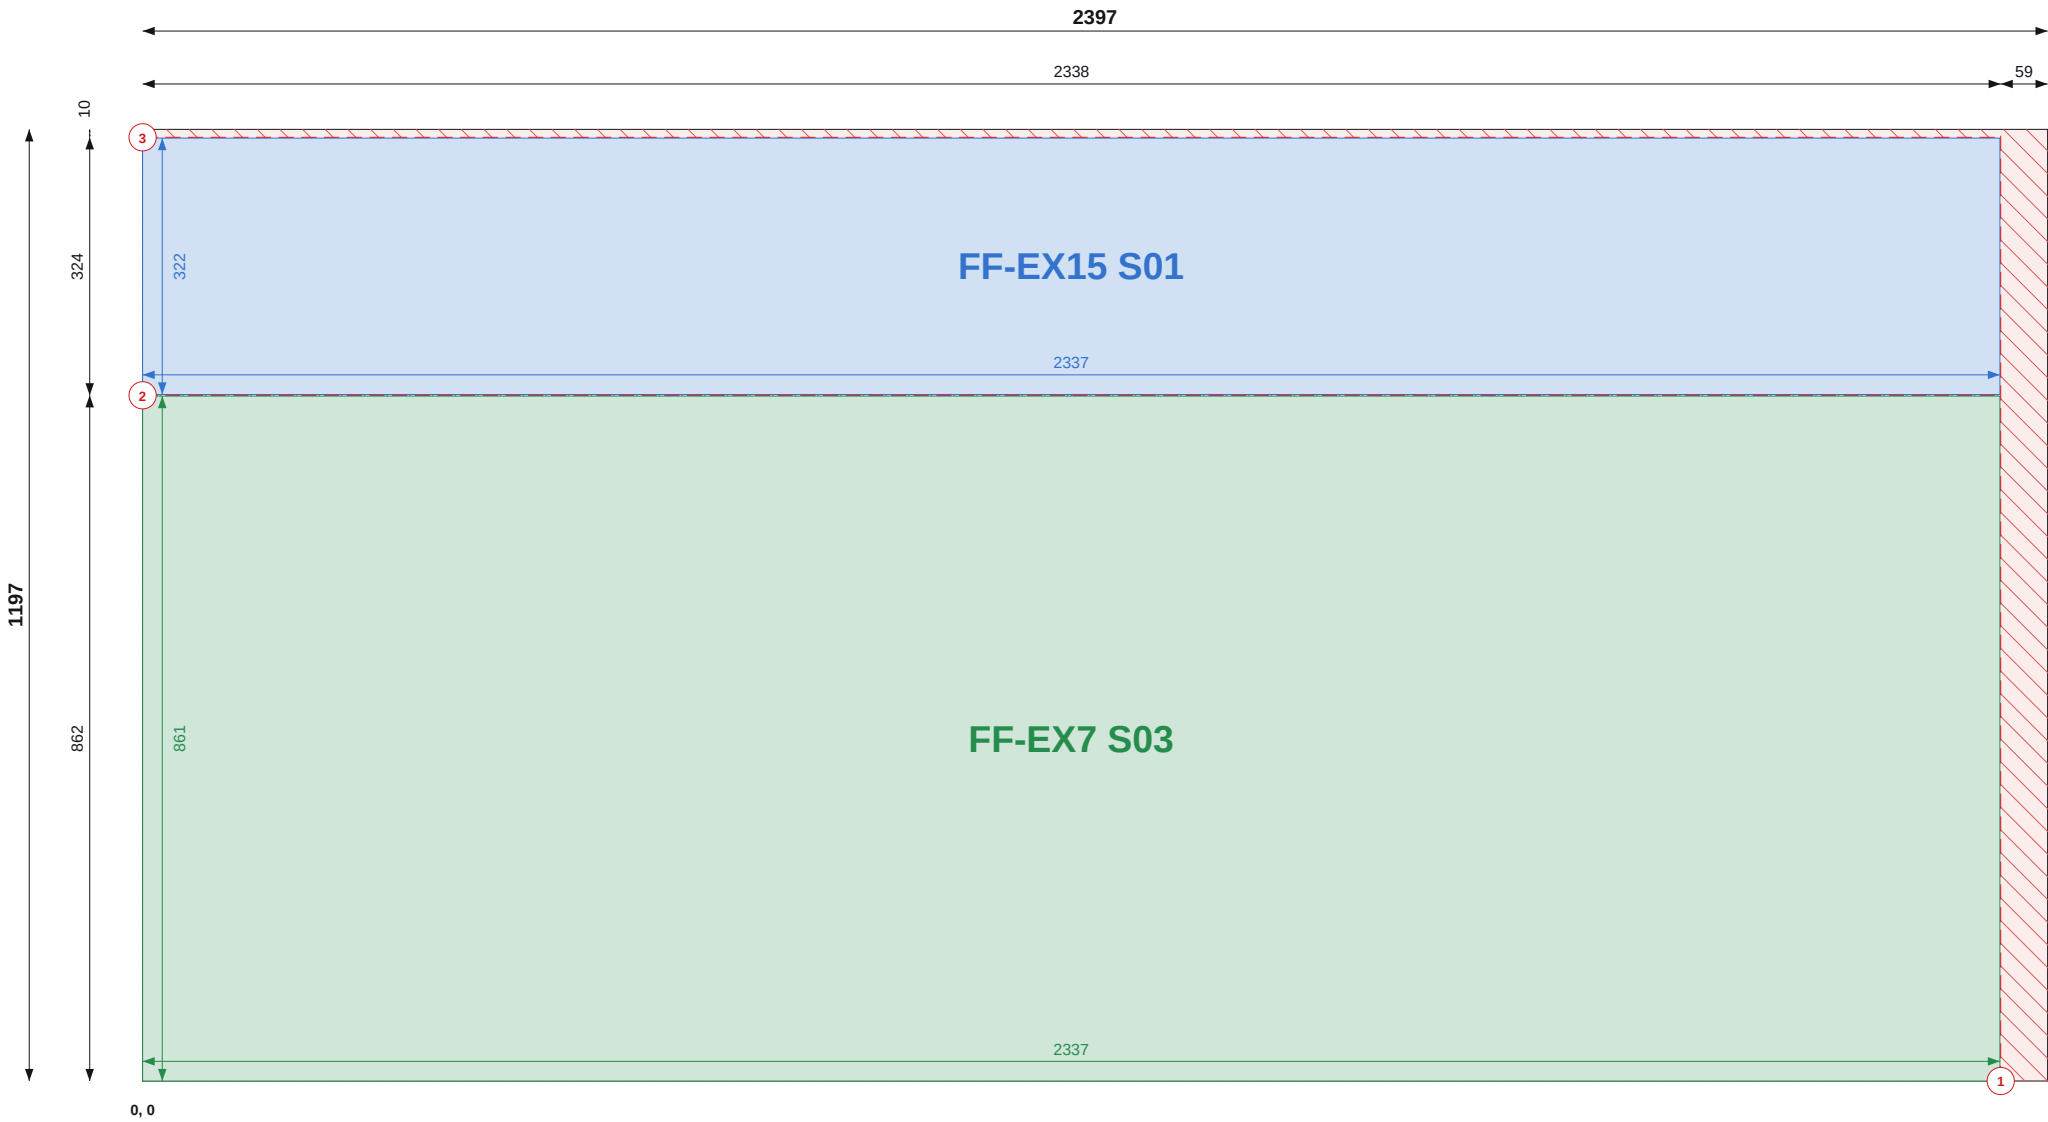

Top / left chains = saw cut positions (to cut centres). Coloured = part size and position.

SHEET 20 OF 34

THIS SHEET

Item	Value
Parts	2
Used / waste	96.4% / 0.10 m2
Reusable offcuts	0
Saw cuts / shared	3 / 1

PIECES (POSITION = BOTTOM-LEFT CORNER)

Label	Size	X, Y
FF-EX15 S01	322 x 2337	0, 863
FF-EX7 S03	861 x 2337	0, 0

NOTES

- Cut from OSB/3 9mm 1197x2397, 2mm saw kerf. Viewed on the face; dimensions from the sheet's bottom-left corner (0,0). Red numbered lines = saw cuts in order, each edge to edge.
- Coloured dimensions belong to the part of that colour: its width and height, and its position from the sheet edges. Raked parts: corner coordinates at each corner.
- Red hatch = waste. Labels = panel + piece mark on the manufacture drawing.

REVISIONS

REV	DATE	DESCRIPTION
C01	13.09.26	Construction issue



TLS TIMBER FRAME

Design & Manufacture

Scan: 3D model + drawings



CLIENT MP Adams	PROJECT MP Adams Plot 3, Eckington
--------------------	---------------------------------------


DRAWING TITLE OSB CUTTING - FIRST FLOOR - SHEET 20 OF 34
--

OSB/3 9mm 1197x2397 | First Floor

SCALE NTS	SIZE A3	DATE 13.09.26	DRAWN TS
--------------	------------	------------------	-------------

STATUS CONSTRUCTION	DRAWING No. P3-CP-OSB-02 / 20	REV C01
-------------------------------	---	-------------------

Do not scale. All dimensions in mm. Check all dimensions on site.

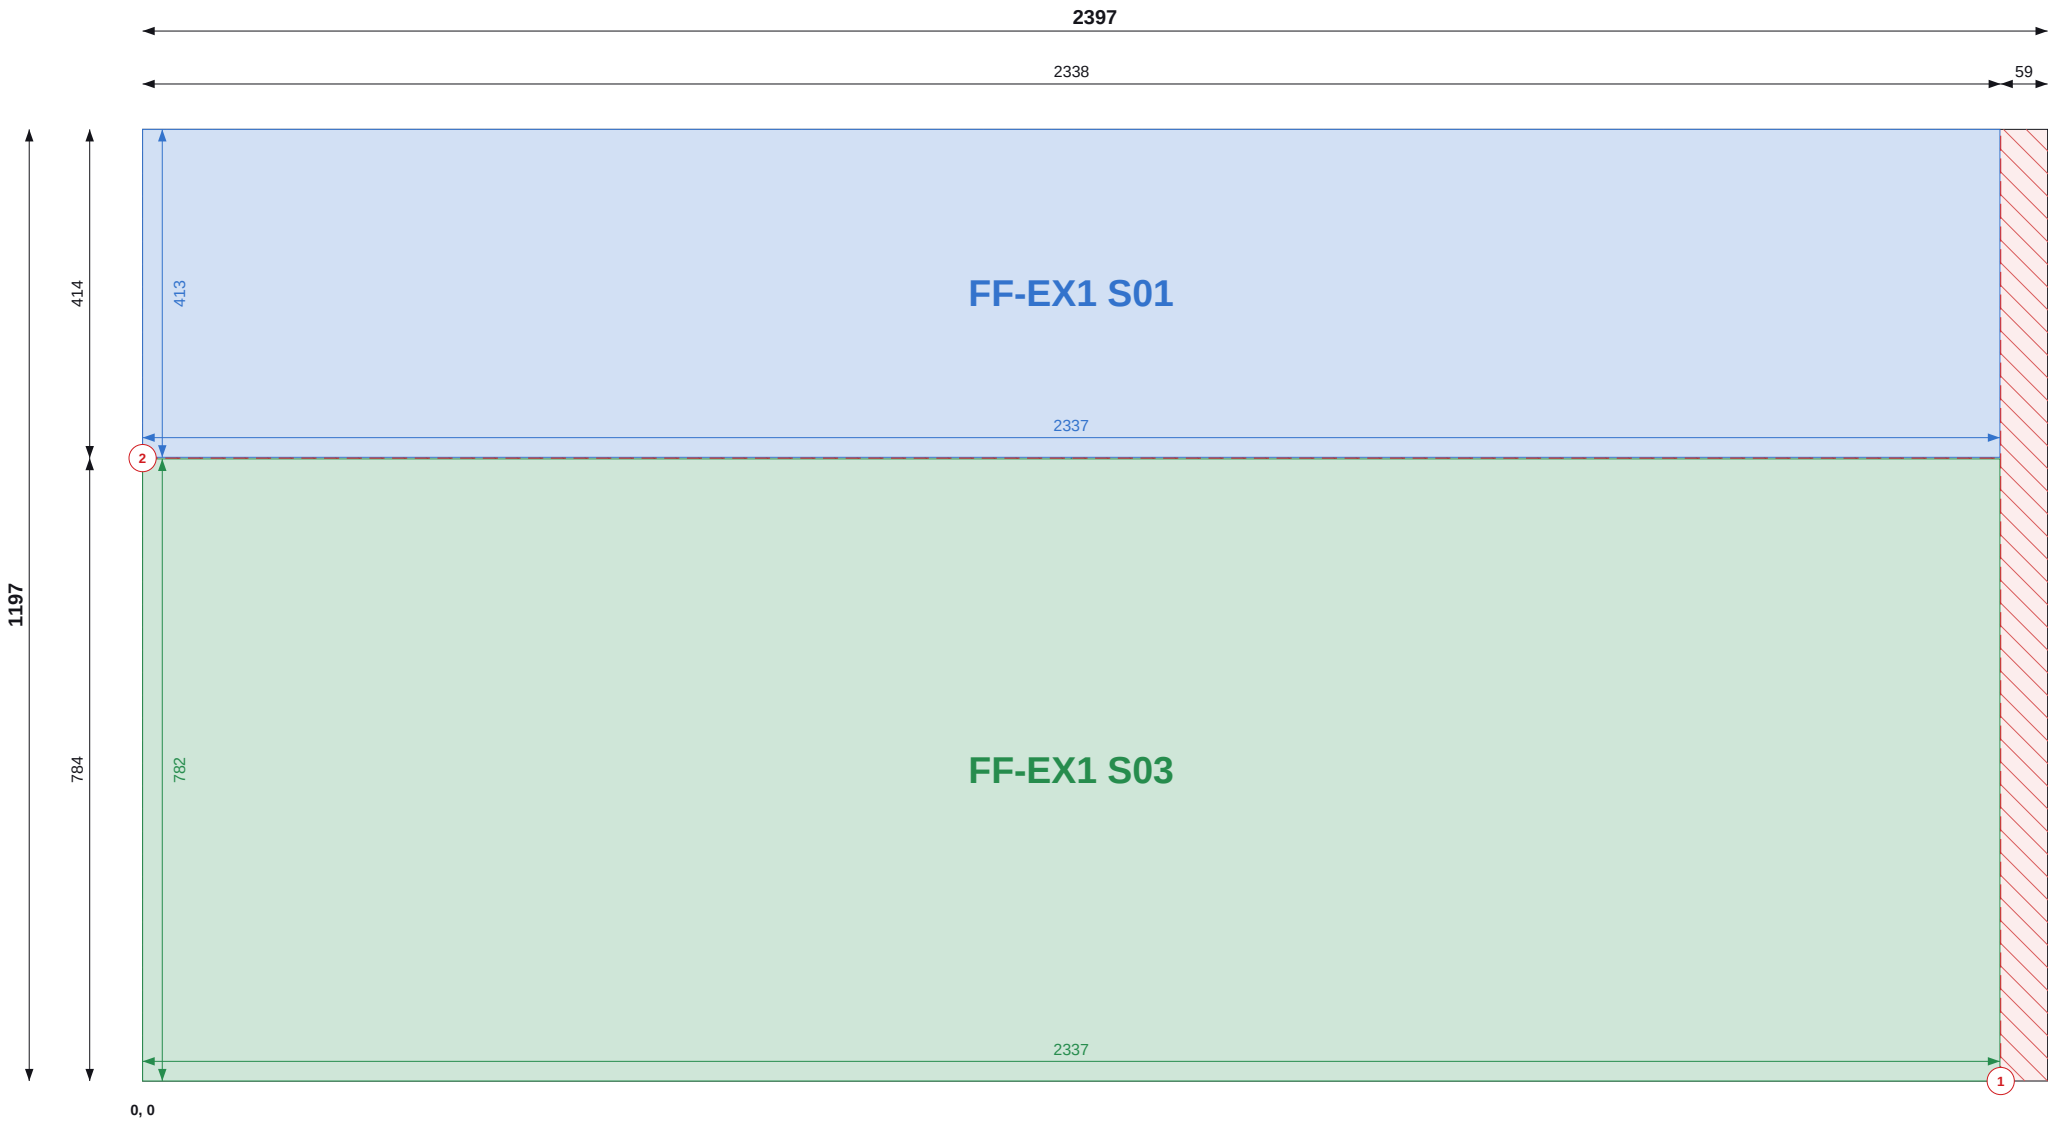

Top / left chains = saw cut positions (to cut centres). Coloured = part size and position.

SHEET 21 OF 34

THIS SHEET

Item	Value
Parts	2
Used / waste	97.3% / 0.08 m2
Reusable offcuts	0
Saw cuts / shared	2 / 1

PIECES (POSITION = BOTTOM-LEFT CORNER)

Label	Size	X, Y
FF-EX1 S01	413 x 2337	0, 784
FF-EX1 S03	782 x 2337	0, 0

NOTES

- Cut from OSB/3 9mm 1197x2397, 2mm saw kerf. Viewed on the face; dimensions from the sheet's bottom-left corner (0,0). Red numbered lines = saw cuts in order, each edge to edge.
- Coloured dimensions belong to the part of that colour: its width and height, and its position from the sheet edges. Raked parts: corner coordinates at each corner.
- Red hatch = waste. Labels = panel + piece mark on the manufacture drawing.

REVISIONS

REV	DATE	DESCRIPTION
C01	13.09.26	Construction issue



TLS TIMBER FRAME

Design & Manufacture

Scan: 3D model + drawings




CLIENT	PROJECT
MP Adams	MP Adams Plot 3, Eckington

DRAWING TITLE			
OSB CUTTING - FIRST FLOOR - SHEET 21 OF 34			
OSB/3 9mm 1197x2397 First Floor			

SCALE	SIZE	DATE	DRAWN
NTS	A3	13.09.26	TS

STATUS	DRAWING No.	REV
CONSTRUCTION	P3-CP-OSB-02 / 21	C01

Do not scale. All dimensions in mm. Check all dimensions on site.

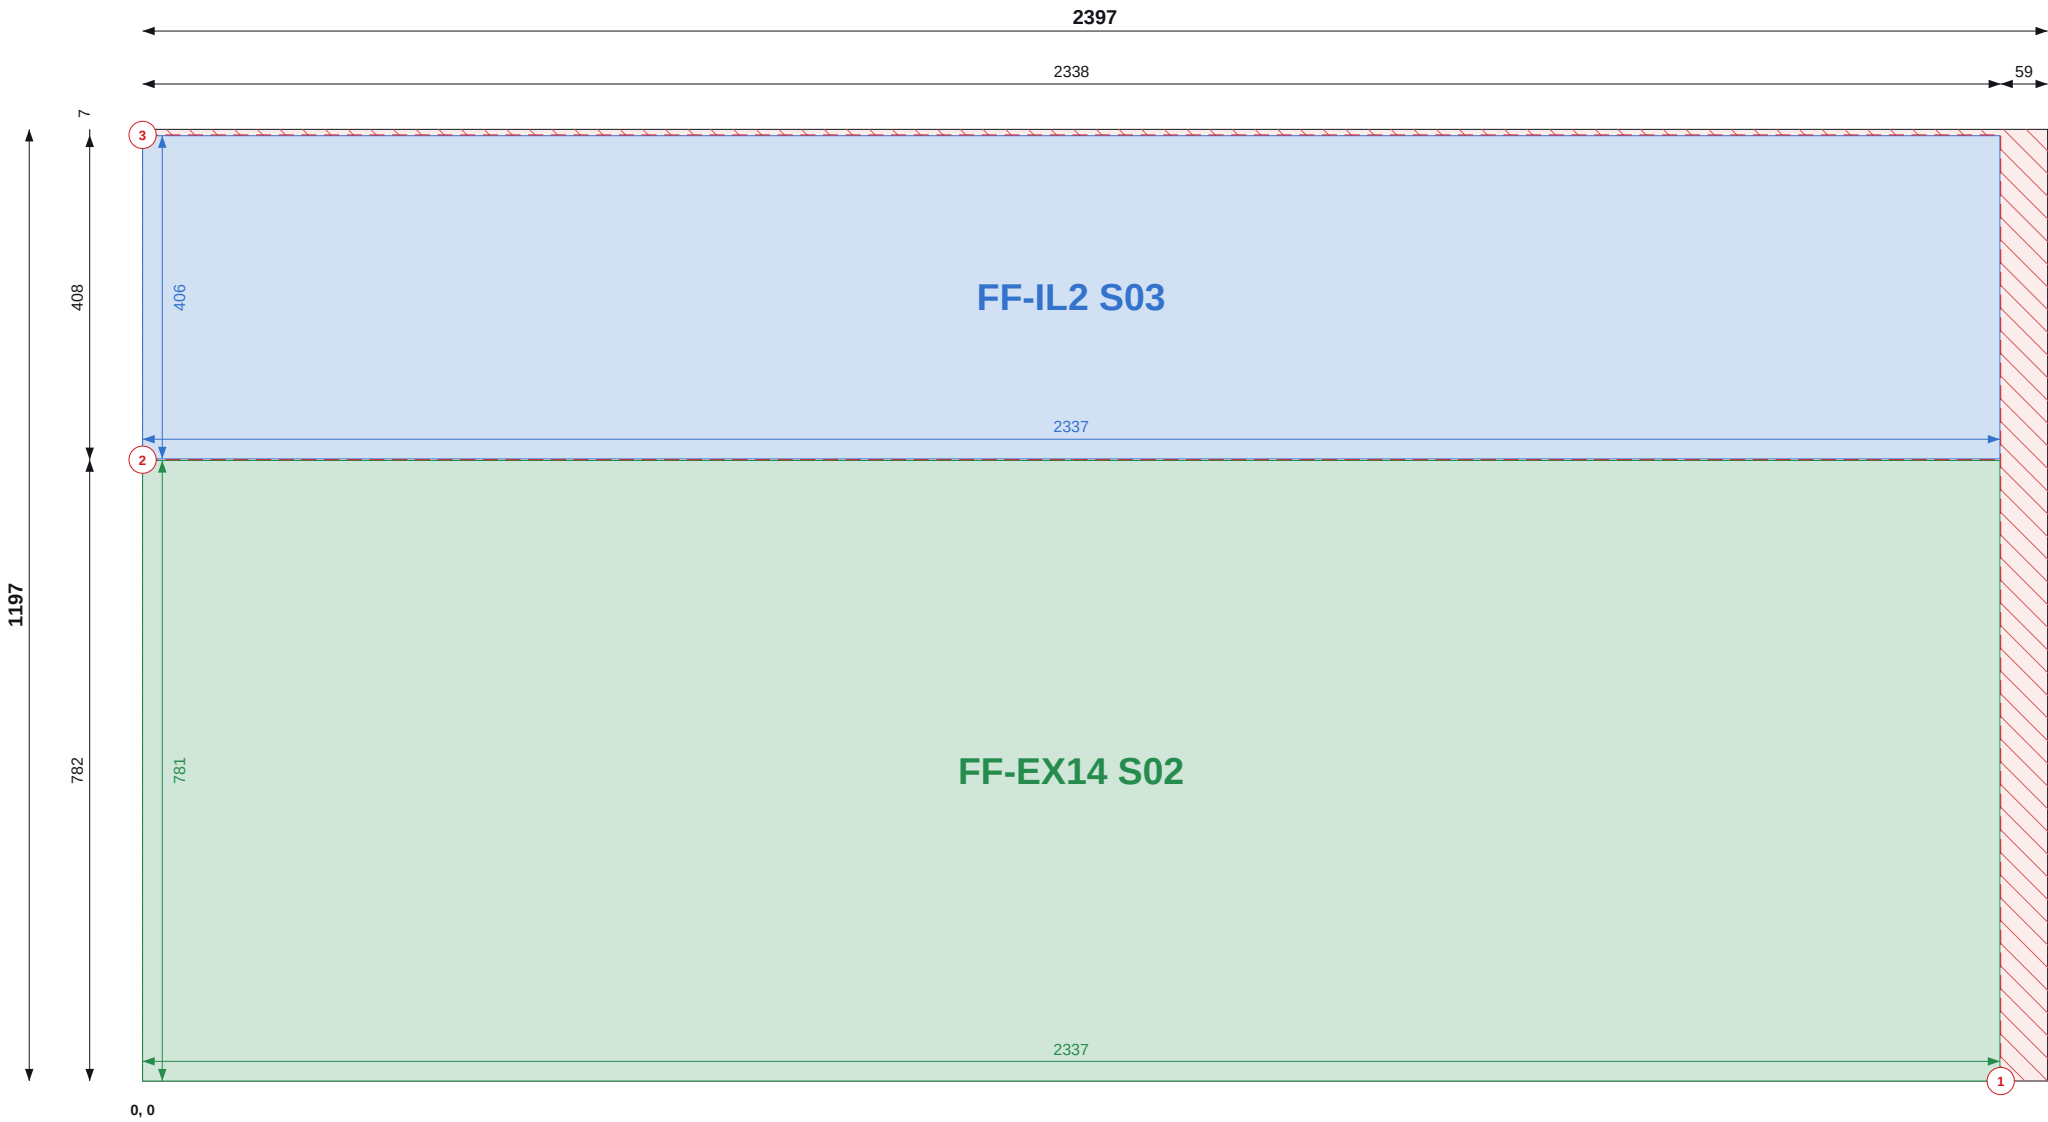

Top / left chains = saw cut positions (to cut centres). Coloured = part size and position.

SHEET 22 OF 34

THIS SHEET

Item	Value
Parts	2
Used / waste	96.7% / 0.10 m2
Reusable offcuts	0
Saw cuts / shared	3 / 1

PIECES (POSITION = BOTTOM-LEFT CORNER)

Label	Size	X, Y
FF-IL2 S03	406 x 2337	0, 783
FF-EX14 S02	781 x 2337	0, 0

NOTES

- Cut from OSB/3 9mm 1197x2397, 2mm saw kerf. Viewed on the face; dimensions from the sheet's bottom-left corner (0,0). Red numbered lines = saw cuts in order, each edge to edge.
- Coloured dimensions belong to the part of that colour: its width and height, and its position from the sheet edges. Raked parts: corner coordinates at each corner.
- Red hatch = waste. Labels = panel + piece mark on the manufacture drawing.

REVISIONS

REV	DATE	DESCRIPTION
C01	13.09.26	Construction issue



TLS TIMBER FRAME

Design & Manufacture

Scan: 3D model + drawings



CLIENT MP Adams	PROJECT MP Adams Plot 3, Eckington
--------------------	---------------------------------------


DRAWING TITLE OSB CUTTING - FIRST FLOOR - SHEET 22 OF 34
--

OSB/3 9mm 1197x2397 | First Floor

SCALE NTS	SIZE A3	DATE 13.09.26	DRAWN TS
--------------	------------	------------------	-------------

STATUS CONSTRUCTION	DRAWING No. P3-CP-OSB-02 / 22	REV C01
-------------------------------	---	-------------------

Do not scale. All dimensions in mm. Check all dimensions on site.

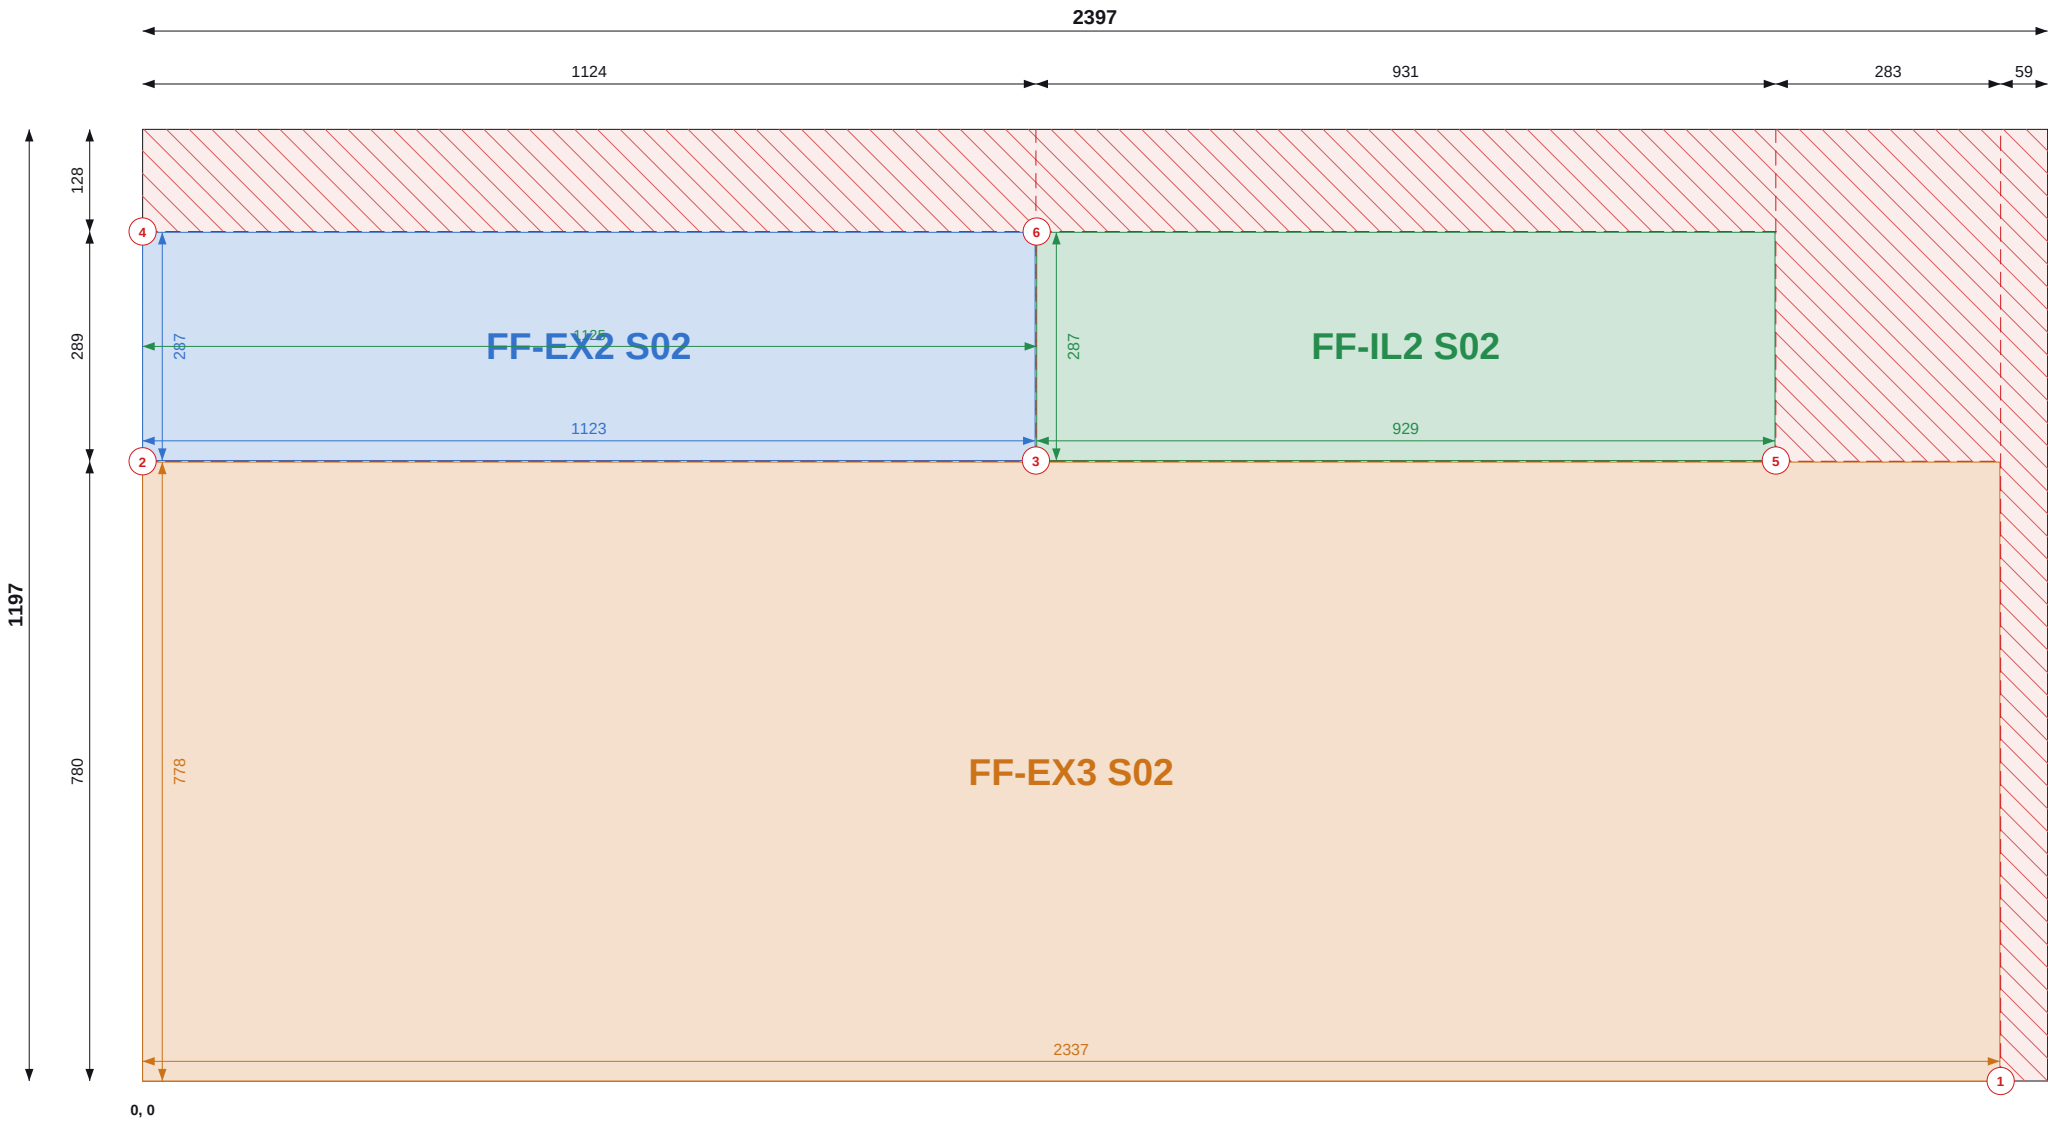

Top / left chains = saw cut positions (to cut centres). Coloured = part size and position.

SHEET 23 OF 34

THIS SHEET

Item	Value
Parts	3
Used / waste	83.9% / 0.46 m2
Reusable offcuts	0
Saw cuts / shared	6 / 2

PIECES (POSITION = BOTTOM-LEFT CORNER)

Label	Size	X, Y
FF-EX2 S02	1123 x 287	0, 780
FF-IL2 S02	929 x 287	1125, 780
FF-EX3 S02	778 x 2337	0, 0

NOTES

1. Cut from OSB/3 9mm 1197x2397, 2mm saw kerf. Viewed on the face; dimensions from the sheet's bottom-left corner (0,0). Red numbered lines = saw cuts in order, each edge to edge.
2. Coloured dimensions belong to the part of that colour: its width and height, and its position from the sheet edges. Raked parts: corner coordinates at each corner.
3. Red hatch = waste. Labels = panel + piece mark on the manufacture drawing.

REVISIONS

REV	DATE	DESCRIPTION
C01	13.09.26	Construction issue



TLS TIMBER FRAME

Design & Manufacture

Scan: 3D model + drawings




CLIENT	PROJECT
MP Adams	MP Adams Plot 3, Eckington

DRAWING TITLE			
OSB CUTTING - FIRST FLOOR - SHEET 23 OF 34			
OSB/3 9mm 1197x2397 First Floor			

SCALE	SIZE	DATE	DRAWN
NTS	A3	13.09.26	TS

STATUS	DRAWING No.	REV
CONSTRUCTION	P3-CP-OSB-02 / 23	C01

Do not scale. All dimensions in mm. Check all dimensions on site.

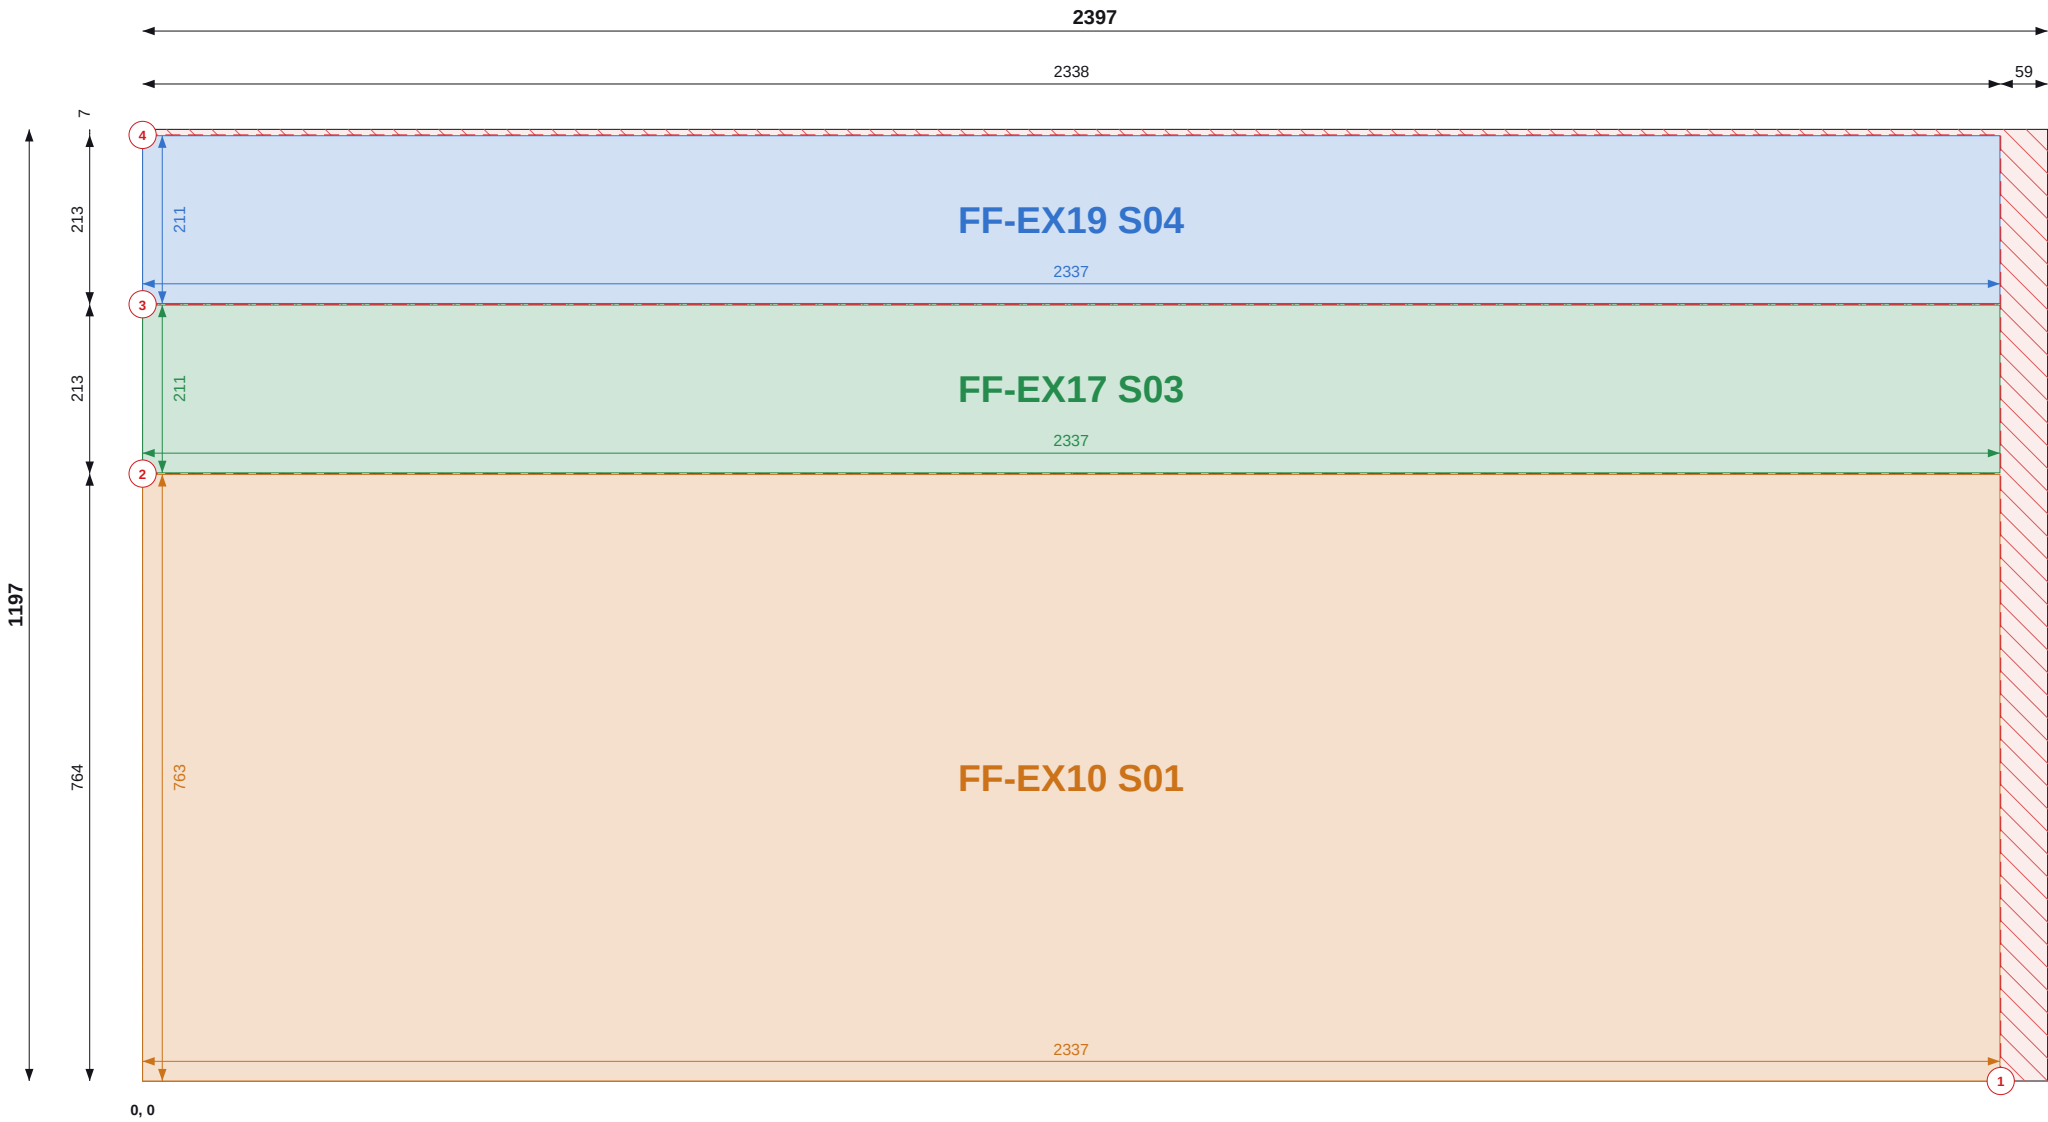

Top / left chains = saw cut positions (to cut centres). Coloured = part size and position.

SHEET 24 OF 34

THIS SHEET

Item	Value
Parts	3
Used / waste	96.5% / 0.10 m2
Reusable offcuts	0
Saw cuts / shared	4 / 2

PIECES (POSITION = BOTTOM-LEFT CORNER)

Label	Size	X, Y
FF-EX19 S04	211 x 2337	0, 978
FF-EX17 S03	211 x 2337	0, 765
FF-EX10 S01	763 x 2337	0, 0

NOTES

- Cut from OSB/3 9mm 1197x2397, 2mm saw kerf. Viewed on the face; dimensions from the sheet's bottom-left corner (0,0). Red numbered lines = saw cuts in order, each edge to edge.
- Coloured dimensions belong to the part of that colour: its width and height, and its position from the sheet edges. Raked parts: corner coordinates at each corner.
- Red hatch = waste. Labels = panel + piece mark on the manufacture drawing.

REVISIONS

REV	DATE	DESCRIPTION
C01	13.09.26	Construction issue



TLS TIMBER FRAME

Design & Manufacture

Scan: 3D model + drawings




CLIENT	PROJECT
MP Adams	MP Adams Plot 3, Eckington

DRAWING TITLE			
OSB CUTTING - FIRST FLOOR - SHEET 24 OF 34			
OSB/3 9mm 1197x2397 First Floor			

SCALE	SIZE	DATE	DRAWN
NTS	A3	13.09.26	TS

STATUS	DRAWING No.	REV
CONSTRUCTION	P3-CP-OSB-02 / 24	C01

Do not scale. All dimensions in mm. Check all dimensions on site.

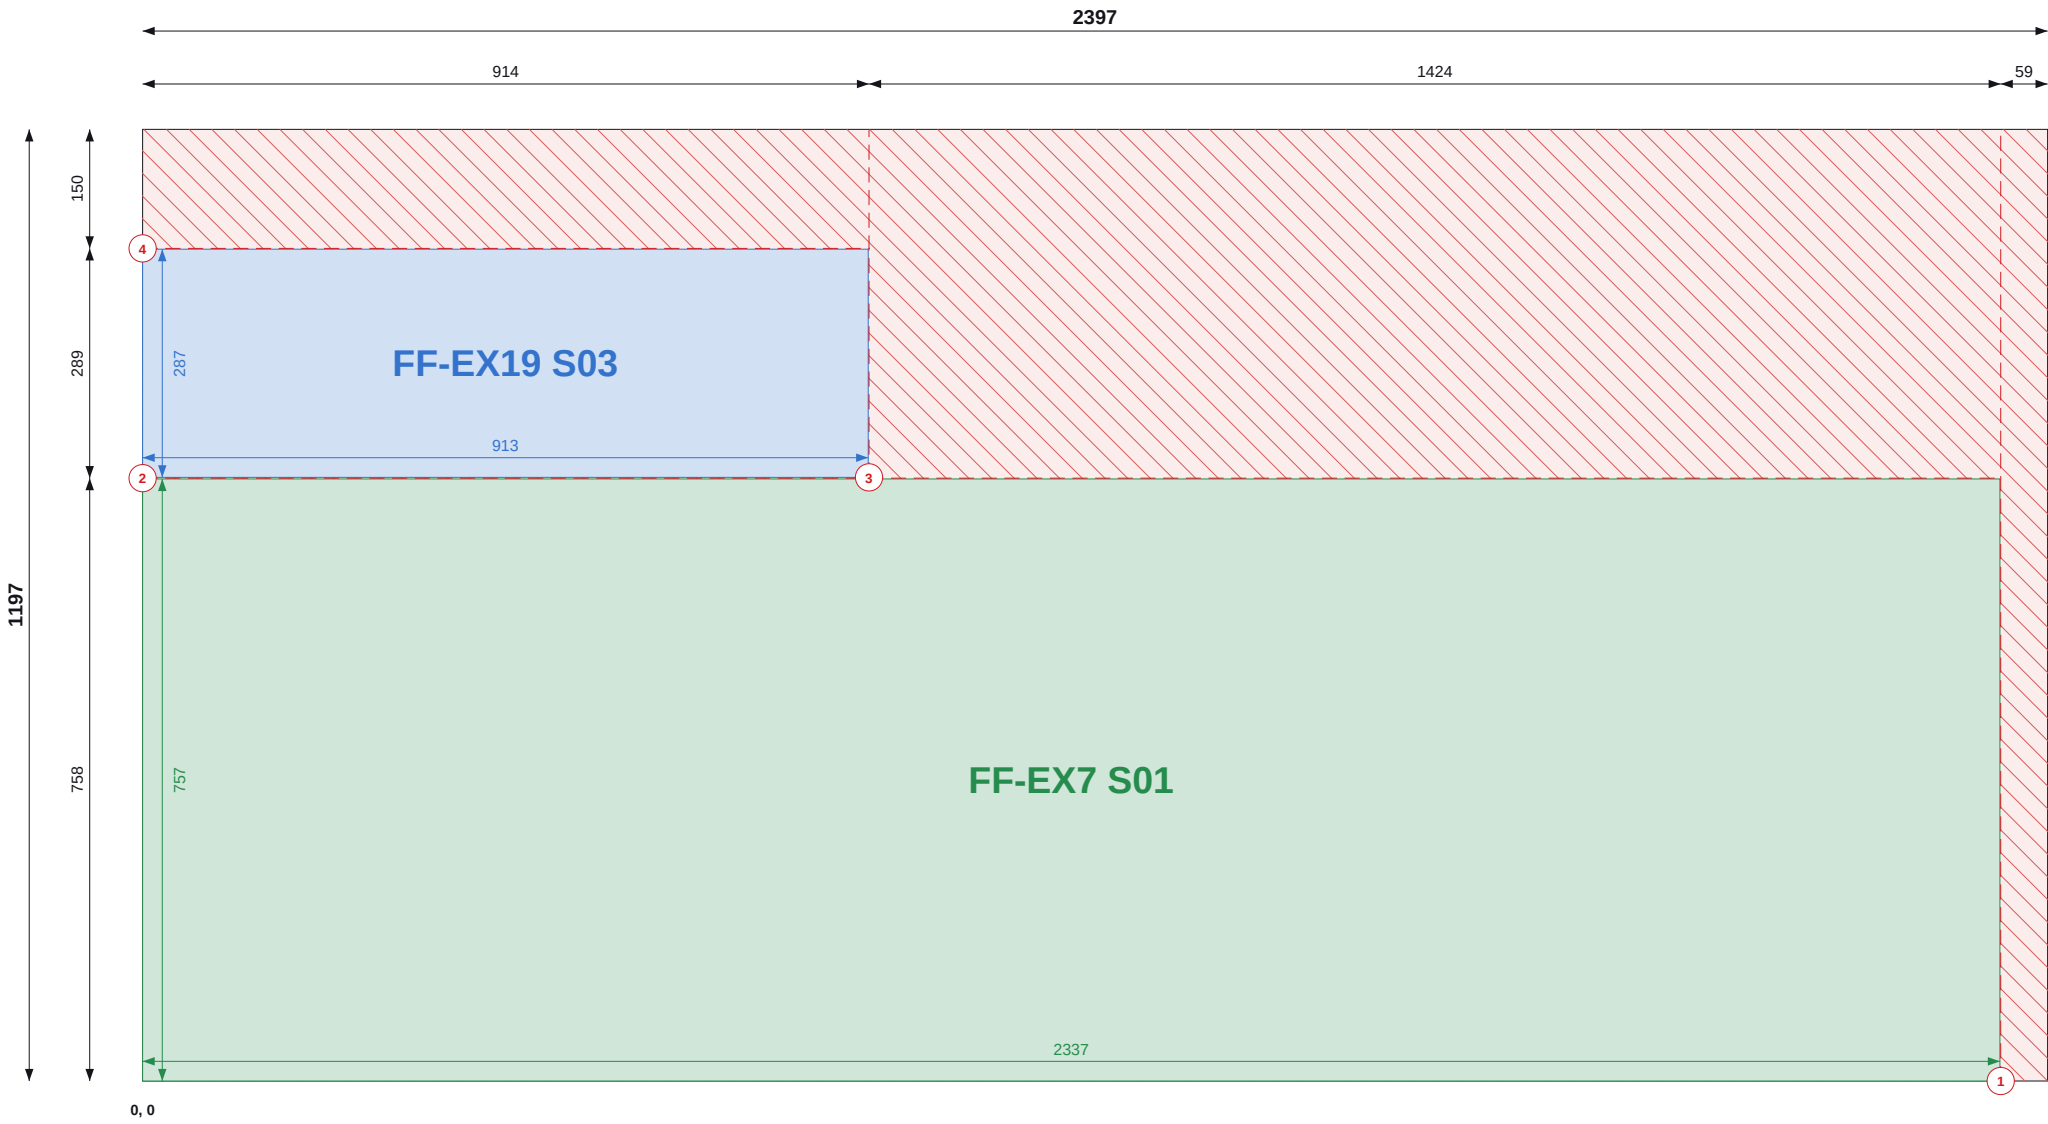

Top / left chains = saw cut positions (to cut centres). Coloured = part size and position.

SHEET 25 OF 34

THIS SHEET

Item	Value
Parts	2
Used / waste	70.8% / 0.84 m2
Reusable offcuts	1
Saw cuts / shared	4 / 1

PIECES (POSITION = BOTTOM-LEFT CORNER)

Label	Size	X, Y
FF-EX19 S03	913 x 287	0, 759
FF-EX7 S01	757 x 2337	0, 0

NOTES

- Cut from OSB/3 9mm 1197x2397, 2mm saw kerf. Viewed on the face; dimensions from the sheet's bottom-left corner (0,0). Red numbered lines = saw cuts in order, each edge to edge.
- Coloured dimensions belong to the part of that colour: its width and height, and its position from the sheet edges. Raked parts: corner coordinates at each corner.
- Red hatch = waste. Labels = panel + piece mark on the manufacture drawing.

REVISIONS

REV	DATE	DESCRIPTION
C01	13.09.26	Construction issue



TLS TIMBER FRAME

Design & Manufacture

Scan: 3D model + drawings



CLIENT	PROJECT
MP Adams	MP Adams Plot 3, Eckington

DRAWING TITLE			
OSB CUTTING - FIRST FLOOR - SHEET 25 OF 34			
OSB/3 9mm 1197x2397 First Floor			

SCALE	SIZE	DATE	DRAWN
NTS	A3	13.09.26	TS

STATUS	DRAWING No.	REV
CONSTRUCTION	P3-CP-OSB-02 / 25	C01

Do not scale. All dimensions in mm. Check all dimensions on site.



Top / left chains = saw cut positions (to cut centres). Coloured = part size and position.

SHEET 26 OF 34

THIS SHEET

Item	Value
Parts	2
Used / waste	97.3% / 0.08 m2
Reusable offcuts	0
Saw cuts / shared	2 / 1

PIECES (POSITION = BOTTOM-LEFT CORNER)

Label	Size	X, Y
FF-EX9 S01	439 x 2337	0, 758
FF-EX9 S03	756 x 2337	0, 0

NOTES

- Cut from OSB/3 9mm 1197x2397, 2mm saw kerf. Viewed on the face; dimensions from the sheet's bottom-left corner (0,0). Red numbered lines = saw cuts in order, each edge to edge.
- Coloured dimensions belong to the part of that colour: its width and height, and its position from the sheet edges. Raked parts: corner coordinates at each corner.
- Red hatch = waste. Labels = panel + piece mark on the manufacture drawing.

REVISIONS

REV	DATE	DESCRIPTION
C01	13.09.26	Construction issue



TLS TIMBER FRAME

Design & Manufacture

Scan: 3D model + drawings




CLIENT MP Adams	PROJECT MP Adams Plot 3, Eckington
--------------------	---------------------------------------

DRAWING TITLE OSB CUTTING - FIRST FLOOR - SHEET 26 OF 34			
OSB/3 9mm 1197x2397 First Floor			

SCALE NTS	SIZE A3	DATE 13.09.26	DRAWN TS
--------------	------------	------------------	-------------

STATUS CONSTRUCTION	DRAWING No. P3-CP-OSB-02 / 26	REV C01
-------------------------------	---	-------------------

Do not scale. All dimensions in mm. Check all dimensions on site.

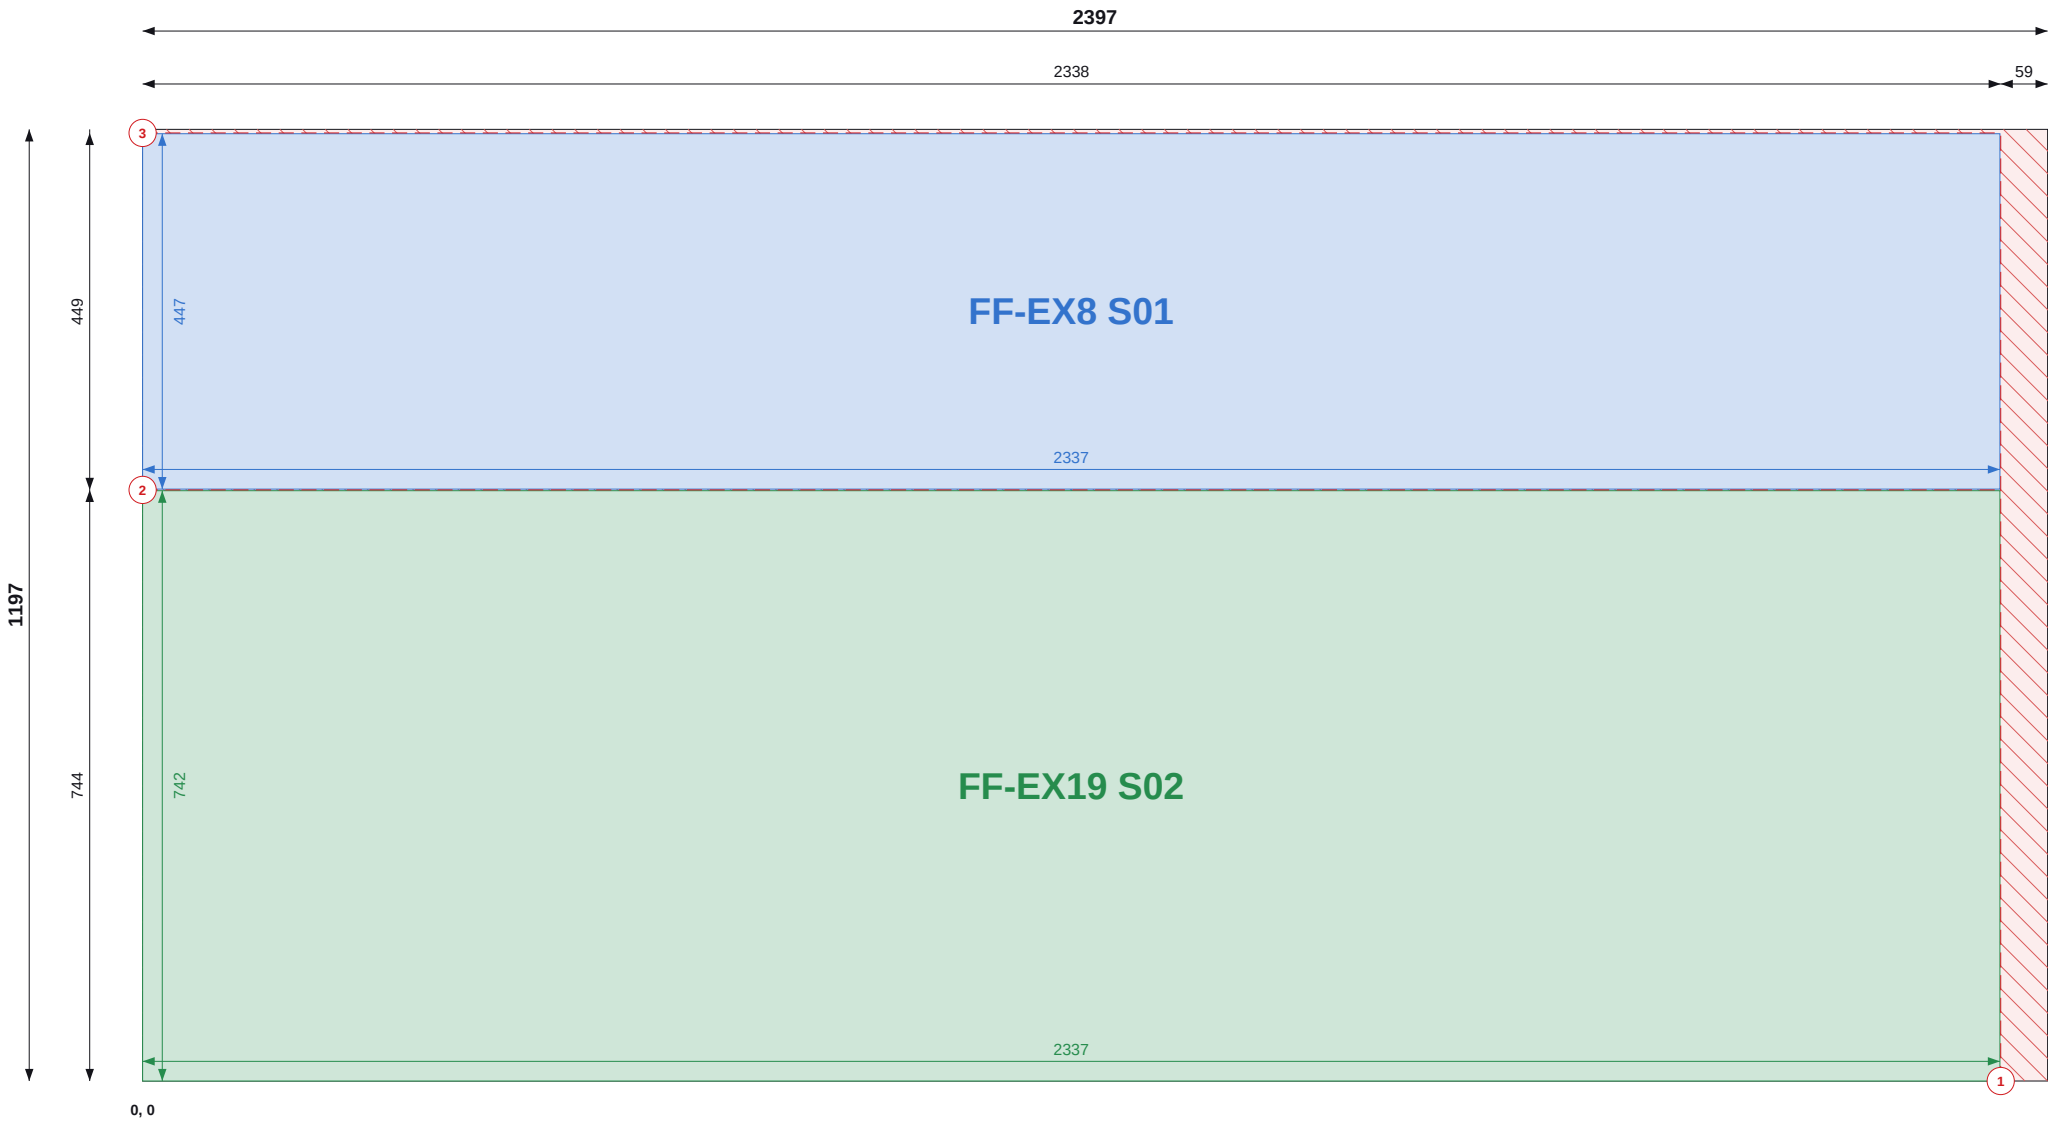

Top / left chains = saw cut positions (to cut centres). Coloured = part size and position.

SHEET 27 OF 34

THIS SHEET

Item	Value
Parts	2
Used / waste	96.9% / 0.09 m2
Reusable offcuts	0
Saw cuts / shared	3 / 1

PIECES (POSITION = BOTTOM-LEFT CORNER)

Label	Size	X, Y
FF-EX8 S01	447 x 2337	0, 744
FF-EX19 S02	742 x 2337	0, 0

NOTES

- Cut from OSB/3 9mm 1197x2397, 2mm saw kerf. Viewed on the face; dimensions from the sheet's bottom-left corner (0,0). Red numbered lines = saw cuts in order, each edge to edge.
- Coloured dimensions belong to the part of that colour: its width and height, and its position from the sheet edges. Raked parts: corner coordinates at each corner.
- Red hatch = waste. Labels = panel + piece mark on the manufacture drawing.

REVISIONS

REV	DATE	DESCRIPTION
C01	13.09.26	Construction issue



TLS TIMBER FRAME

Design & Manufacture

Scan: 3D model + drawings




CLIENT MP Adams	PROJECT MP Adams Plot 3, Eckington
--------------------	---------------------------------------

DRAWING TITLE OSB CUTTING - FIRST FLOOR - SHEET 27 OF 34			
OSB/3 9mm 1197x2397 First Floor			

SCALE NTS	SIZE A3	DATE 13.09.26	DRAWN TS
--------------	------------	------------------	-------------

STATUS CONSTRUCTION	DRAWING No. P3-CP-OSB-02 / 27	REV C01
-------------------------------	---	-------------------

Do not scale. All dimensions in mm. Check all dimensions on site.

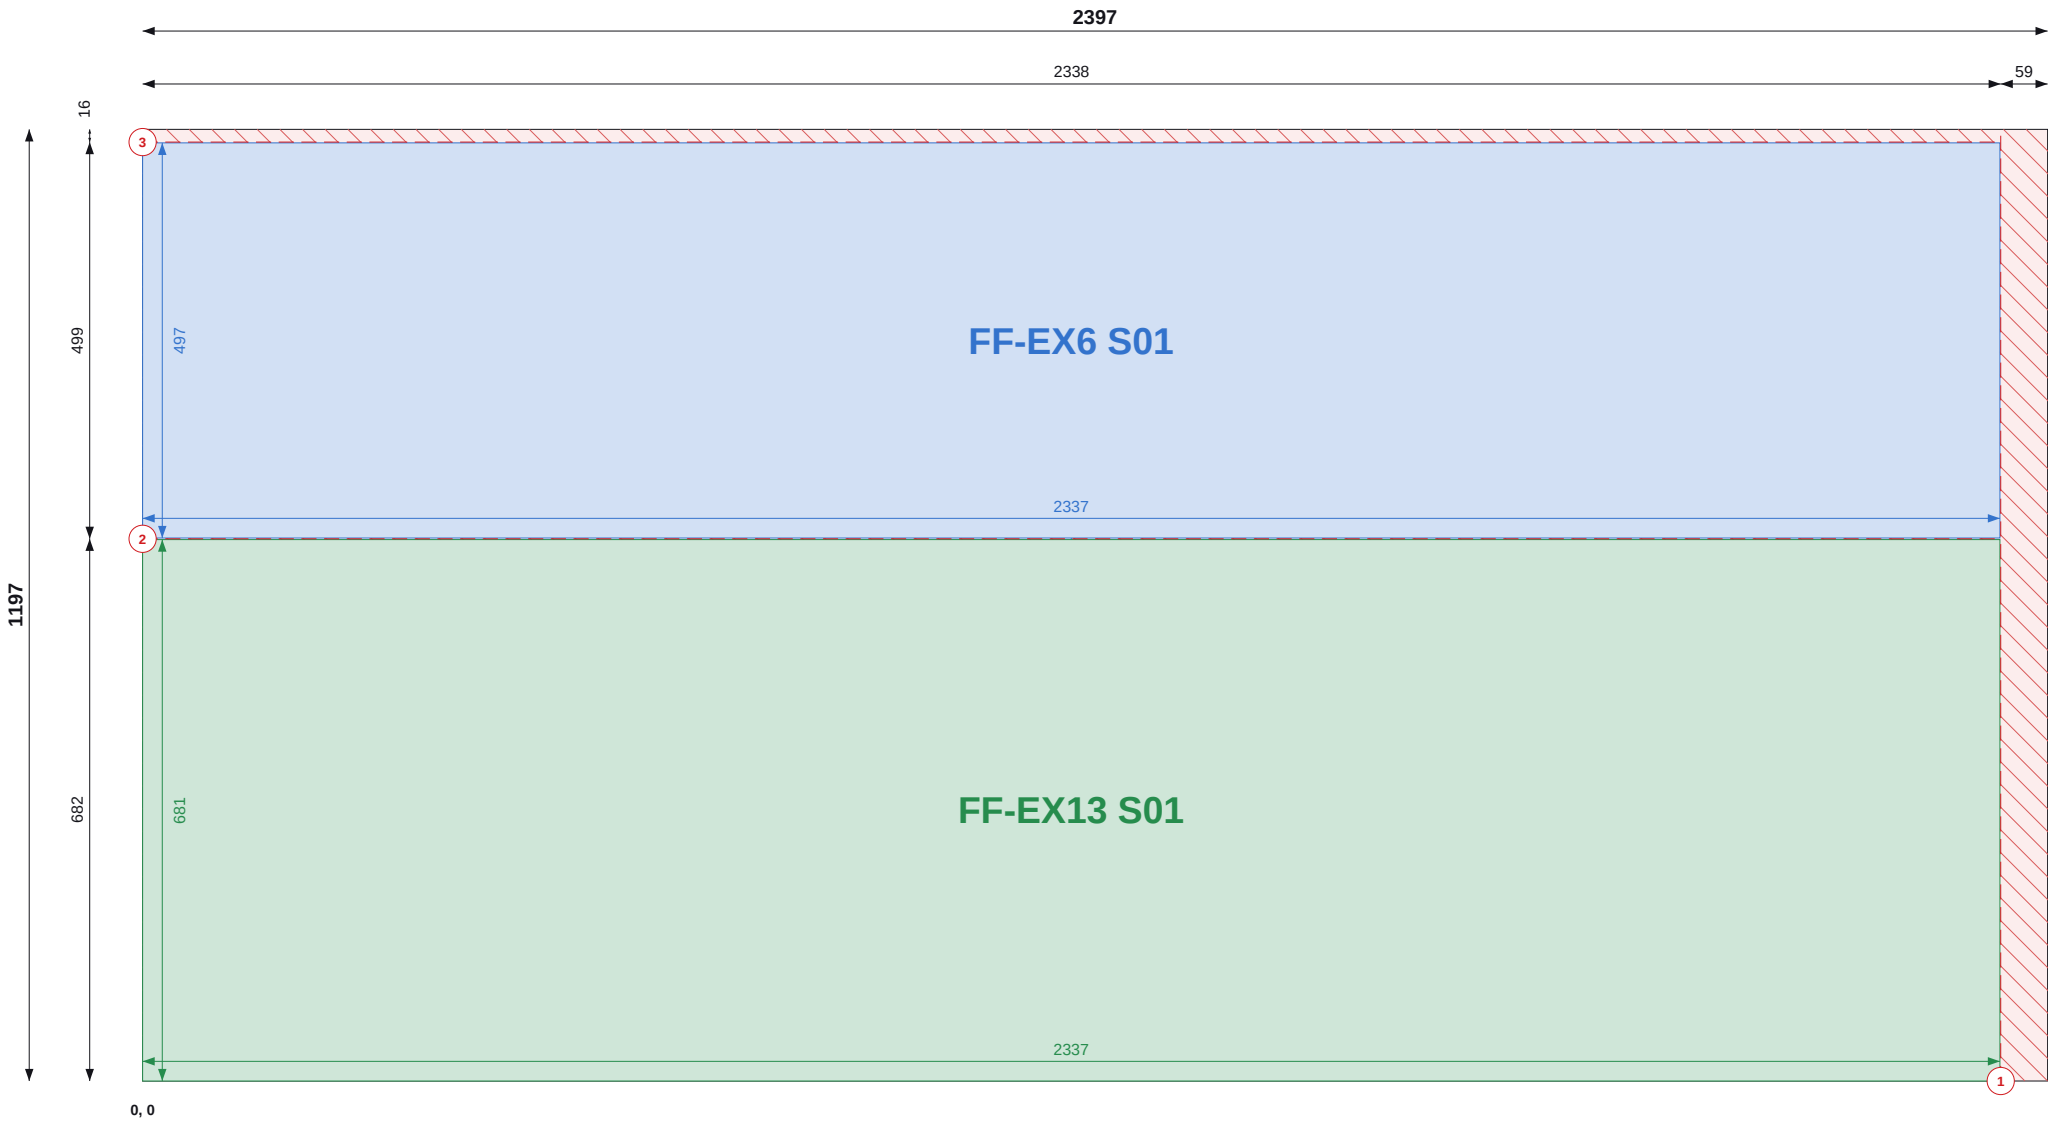

Top / left chains = saw cut positions (to cut centres). Coloured = part size and position.

SHEET 28 OF 34

THIS SHEET

Item	Value
Parts	2
Used / waste	95.9% / 0.12 m2
Reusable offcuts	0
Saw cuts / shared	3 / 1

PIECES (POSITION = BOTTOM-LEFT CORNER)

Label	Size	X, Y
FF-EX6 S01	497 x 2337	0, 683
FF-EX13 S01	681 x 2337	0, 0

NOTES

- Cut from OSB/3 9mm 1197x2397, 2mm saw kerf. Viewed on the face; dimensions from the sheet's bottom-left corner (0,0). Red numbered lines = saw cuts in order, each edge to edge.
- Coloured dimensions belong to the part of that colour: its width and height, and its position from the sheet edges. Raked parts: corner coordinates at each corner.
- Red hatch = waste. Labels = panel + piece mark on the manufacture drawing.

REVISIONS

REV	DATE	DESCRIPTION
C01	13.09.26	Construction issue



TLS TIMBER FRAME

Design & Manufacture

Scan: 3D model + drawings




CLIENT	PROJECT
MP Adams	MP Adams Plot 3, Eckington

DRAWING TITLE			
OSB CUTTING - FIRST FLOOR - SHEET 28 OF 34			
OSB/3 9mm 1197x2397 First Floor			

SCALE	SIZE	DATE	DRAWN
NTS	A3	13.09.26	TS

STATUS	DRAWING No.	REV
CONSTRUCTION	P3-CP-OSB-02 / 28	C01

Do not scale. All dimensions in mm. Check all dimensions on site.

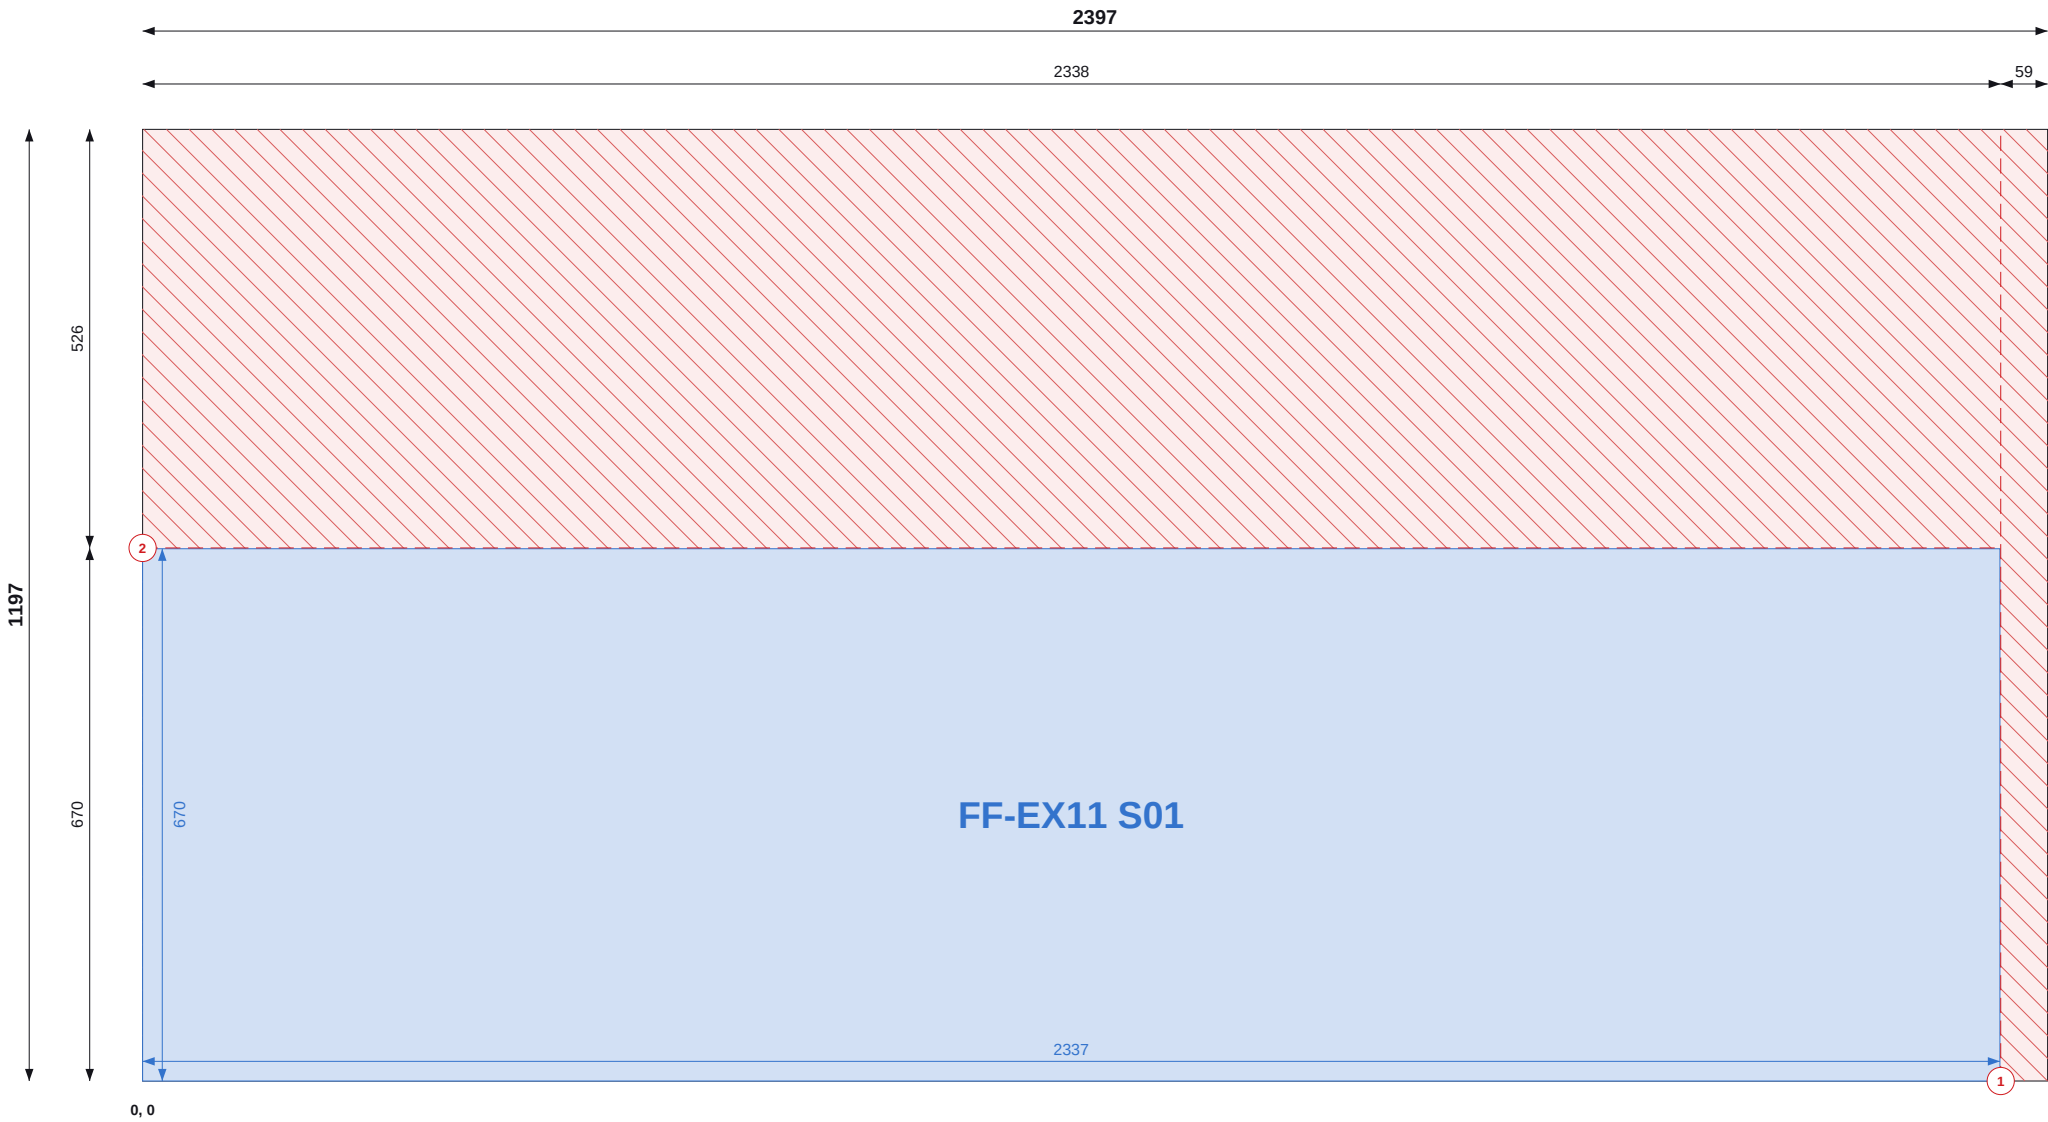

Top / left chains = saw cut positions (to cut centres). Coloured = part size and position.

SHEET 29 OF 34

THIS SHEET

Item	Value
Parts	1
Used / waste	54.5% / 1.30 m2
Reusable offcuts	1
Saw cuts / shared	2 / 0

PIECES (POSITION = BOTTOM-LEFT CORNER)

Label	Size	X, Y
FF-EX11 S01	670 x 2337	0, 0

NOTES

- Cut from OSB/3 9mm 1197x2397, 2mm saw kerf. Viewed on the face; dimensions from the sheet's bottom-left corner (0,0). Red numbered lines = saw cuts in order, each edge to edge.
- Coloured dimensions belong to the part of that colour: its width and height, and its position from the sheet edges. Raked parts: corner coordinates at each corner.
- Red hatch = waste. Labels = panel + piece mark on the manufacture drawing.

REVISIONS

REV	DATE	DESCRIPTION
C01	13.09.26	Construction issue



TLS TIMBER FRAME

Design & Manufacture

Scan: 3D model + drawings



CLIENT	PROJECT
MP Adams	MP Adams Plot 3, Eckington


DRAWING TITLE
OSB CUTTING - FIRST FLOOR - SHEET 29 OF 34

OSB/3 9mm 1197x2397 | First Floor

SCALE	SIZE	DATE	DRAWN
NTS	A3	13.09.26	TS

STATUS	DRAWING No.	REV
CONSTRUCTION	P3-CP-OSB-02 / 29	C01

Do not scale. All dimensions in mm. Check all dimensions on site.

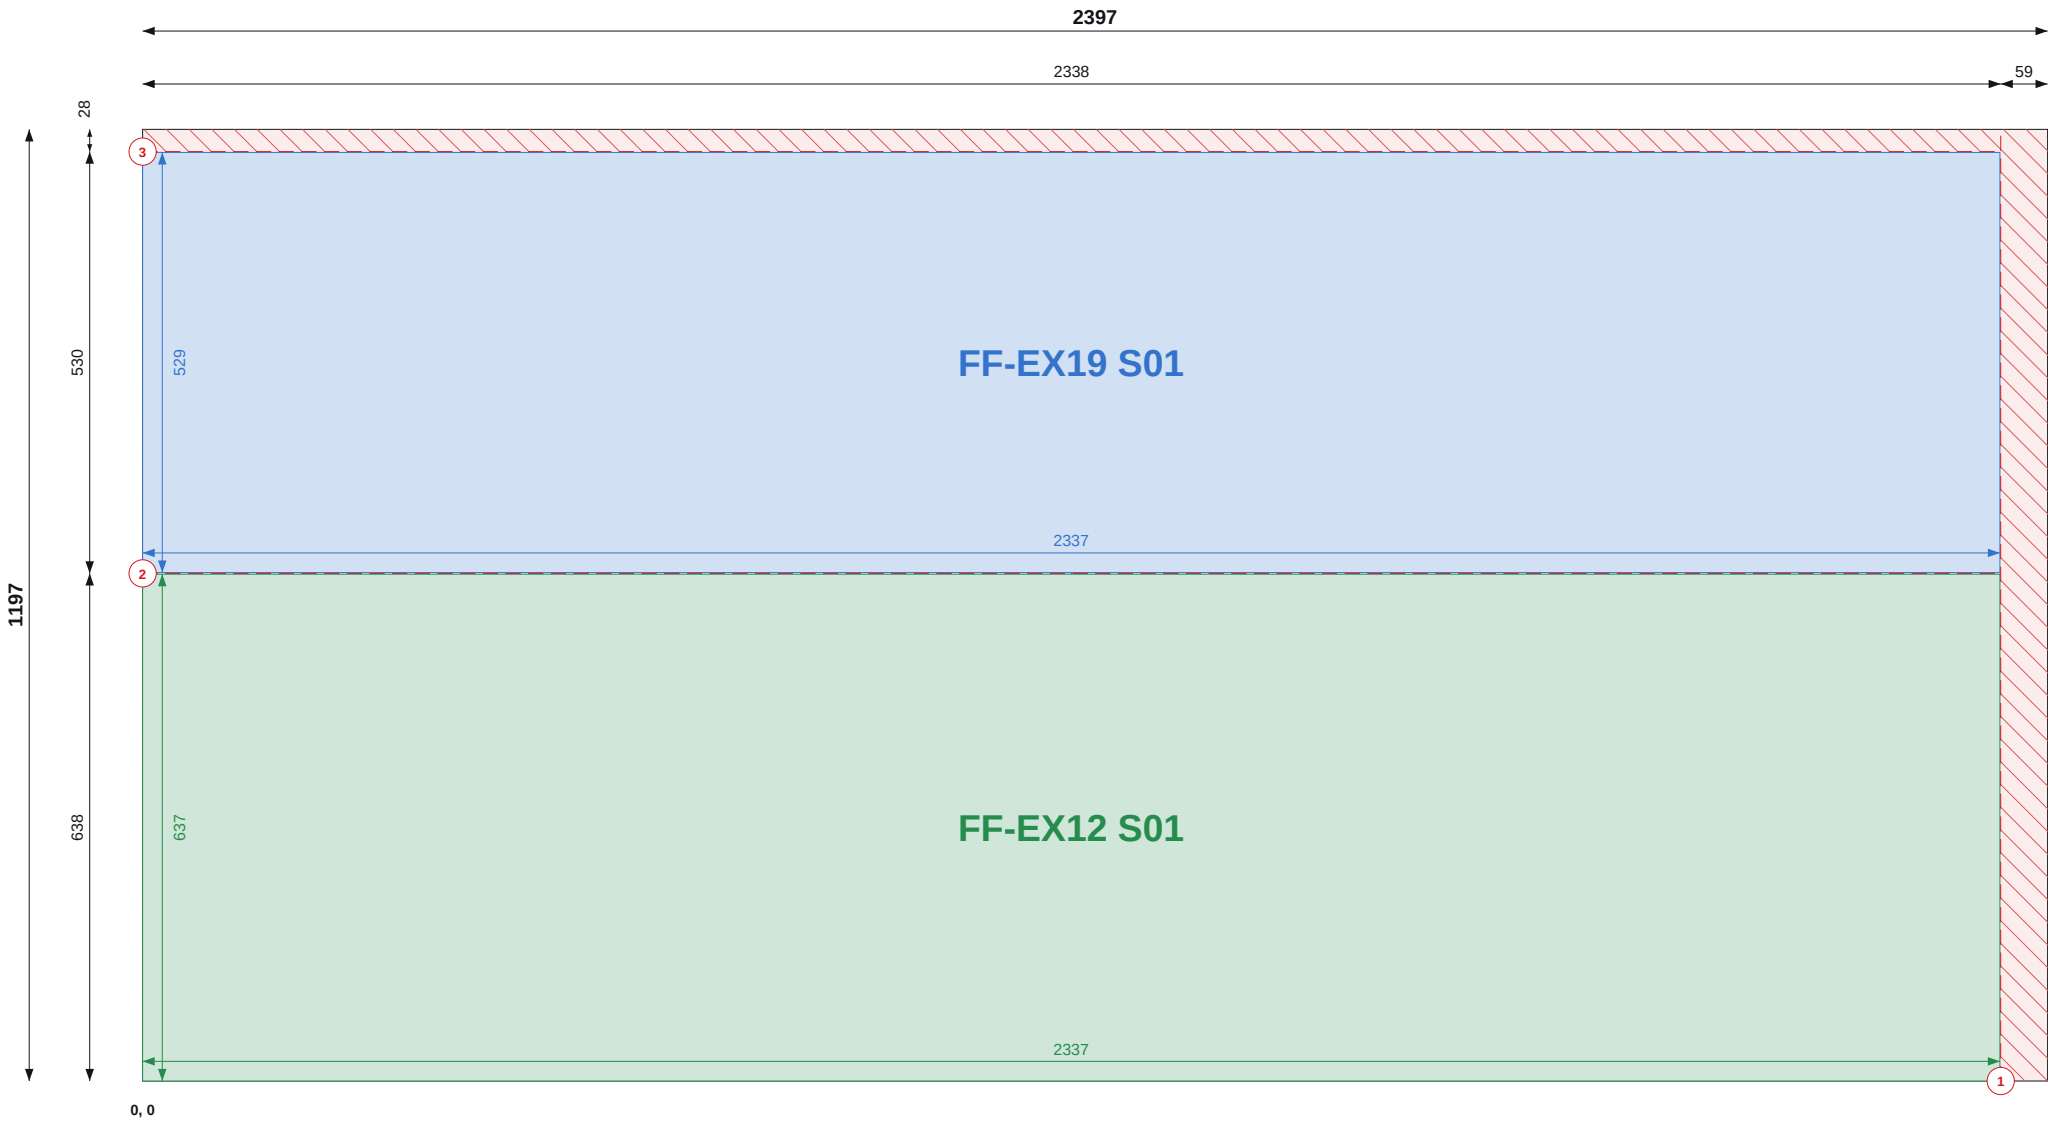

Top / left chains = saw cut positions (to cut centres). Coloured = part size and position.

SHEET 30 OF 34

THIS SHEET

Item	Value
Parts	2
Used / waste	95.0% / 0.14 m2
Reusable offcuts	0
Saw cuts / shared	3 / 1

PIECES (POSITION = BOTTOM-LEFT CORNER)

Label	Size	X, Y
FF-EX19 S01	529 x 2337	0, 639
FF-EX12 S01	637 x 2337	0, 0

NOTES

- Cut from OSB/3 9mm 1197x2397, 2mm saw kerf. Viewed on the face; dimensions from the sheet's bottom-left corner (0,0). Red numbered lines = saw cuts in order, each edge to edge.
- Coloured dimensions belong to the part of that colour: its width and height, and its position from the sheet edges. Raked parts: corner coordinates at each corner.
- Red hatch = waste. Labels = panel + piece mark on the manufacture drawing.

REVISIONS

REV	DATE	DESCRIPTION
C01	13.09.26	Construction issue



TLS TIMBER FRAME

Design & Manufacture

Scan: 3D model + drawings



CLIENT	PROJECT
MP Adams	MP Adams Plot 3, Eckington


DRAWING TITLE
OSB CUTTING - FIRST FLOOR - SHEET 30 OF 34

OSB/3 9mm 1197x2397 | First Floor

SCALE	SIZE	DATE	DRAWN
NTS	A3	13.09.26	TS

STATUS	DRAWING No.	REV
CONSTRUCTION	P3-CP-OSB-02 / 30	C01

Do not scale. All dimensions in mm. Check all dimensions on site.

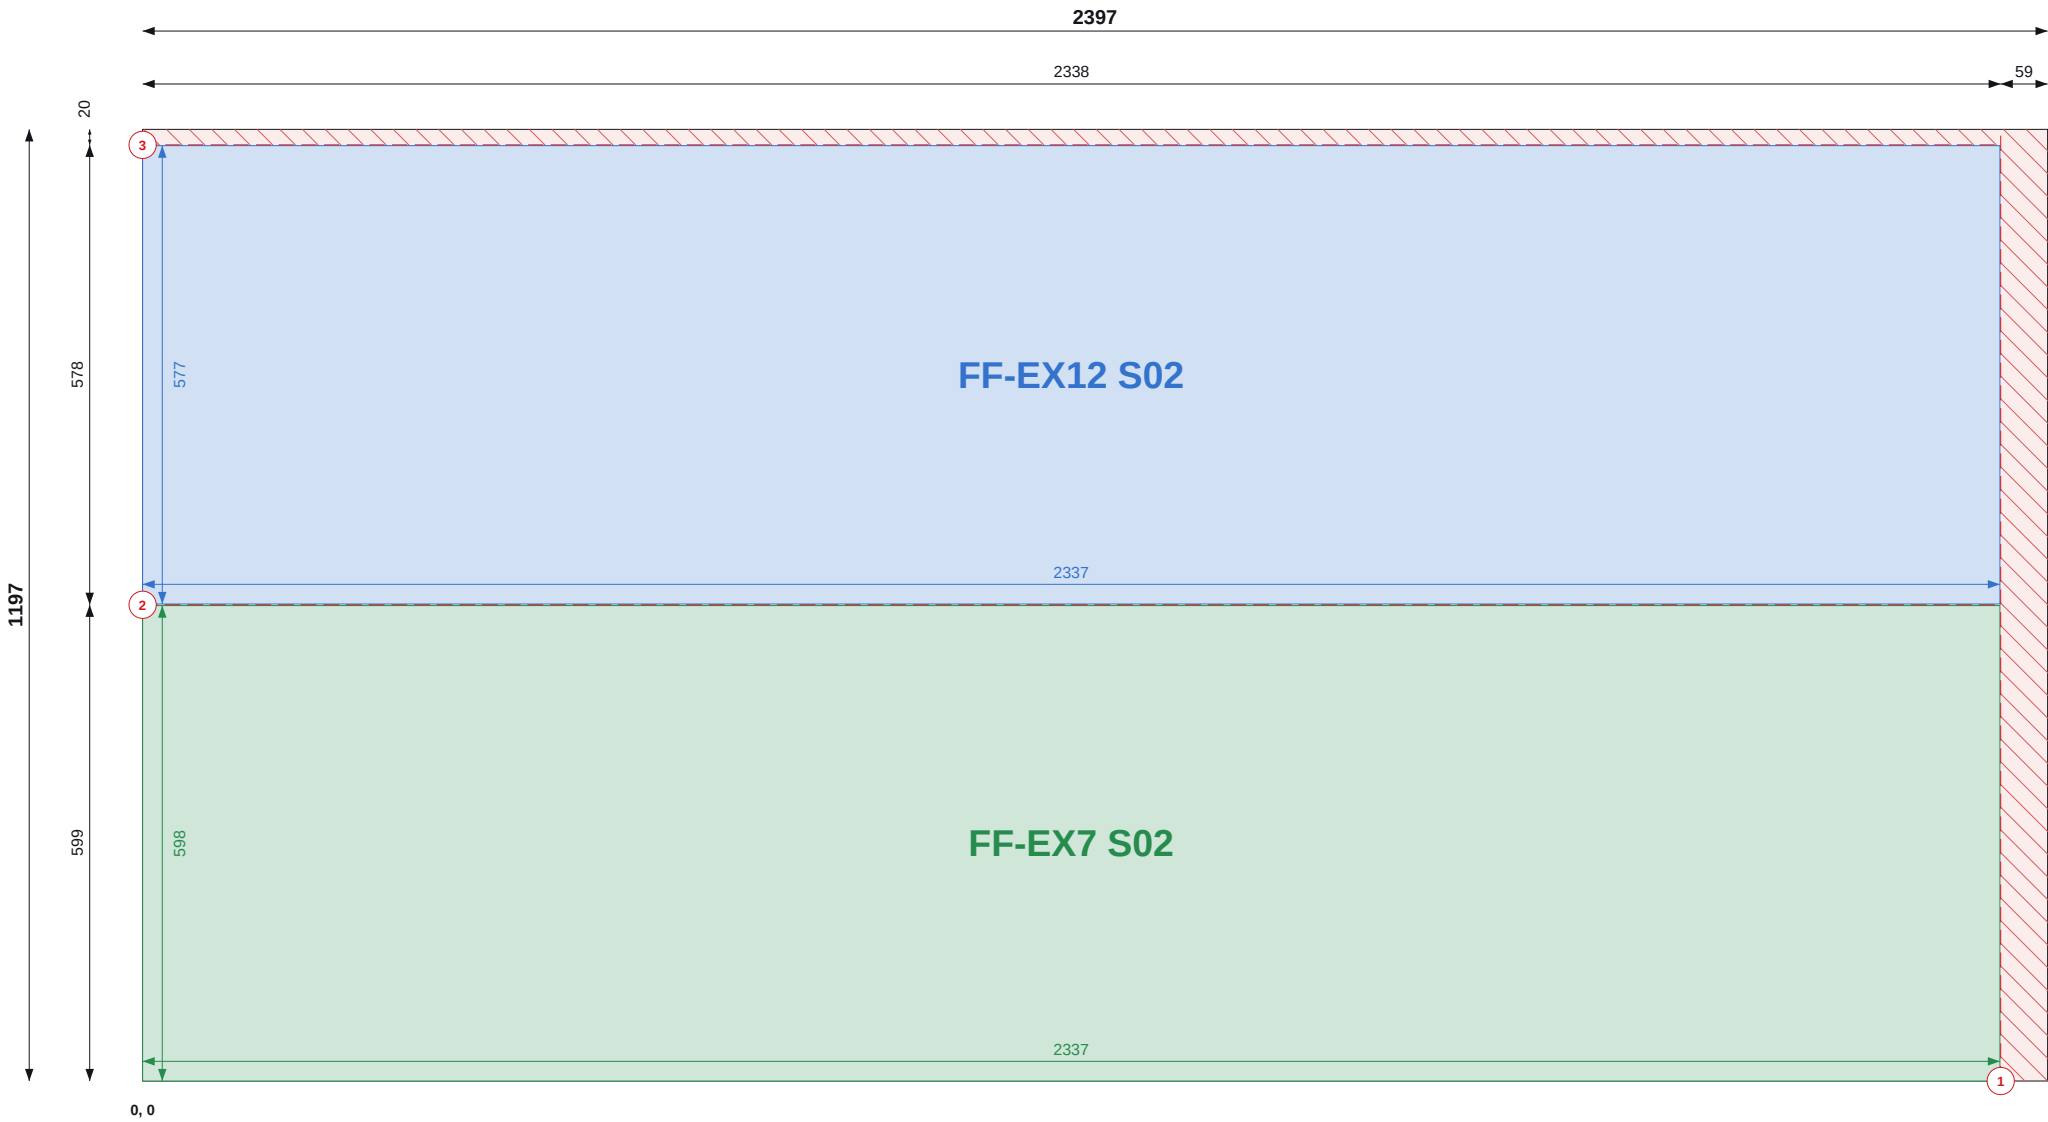

Top / left chains = saw cut positions (to cut centres). Coloured = part size and position.

SHEET 31 OF 34

THIS SHEET

Item	Value
Parts	2
Used / waste	95.7% / 0.12 m2
Reusable offcuts	0
Saw cuts / shared	3 / 1

PIECES (POSITION = BOTTOM-LEFT CORNER)

Label	Size	X, Y
FF-EX12 S02	577 x 2337	0, 600
FF-EX7 S02	598 x 2337	0, 0

NOTES

- Cut from OSB/3 9mm 1197x2397, 2mm saw kerf. Viewed on the face; dimensions from the sheet's bottom-left corner (0,0). Red numbered lines = saw cuts in order, each edge to edge.
- Coloured dimensions belong to the part of that colour: its width and height, and its position from the sheet edges. Raked parts: corner coordinates at each corner.
- Red hatch = waste. Labels = panel + piece mark on the manufacture drawing.

REVISIONS

REV	DATE	DESCRIPTION
C01	13.09.26	Construction issue



TLS TIMBER FRAME

Design & Manufacture

Scan: 3D model + drawings




CLIENT	PROJECT
MP Adams	MP Adams Plot 3, Eckington

DRAWING TITLE			
OSB CUTTING - FIRST FLOOR - SHEET 31 OF 34			
OSB/3 9mm 1197x2397 First Floor			

SCALE	SIZE	DATE	DRAWN
NTS	A3	13.09.26	TS

STATUS	DRAWING No.	REV
CONSTRUCTION	P3-CP-OSB-02 / 31	C01

Do not scale. All dimensions in mm. Check all dimensions on site.

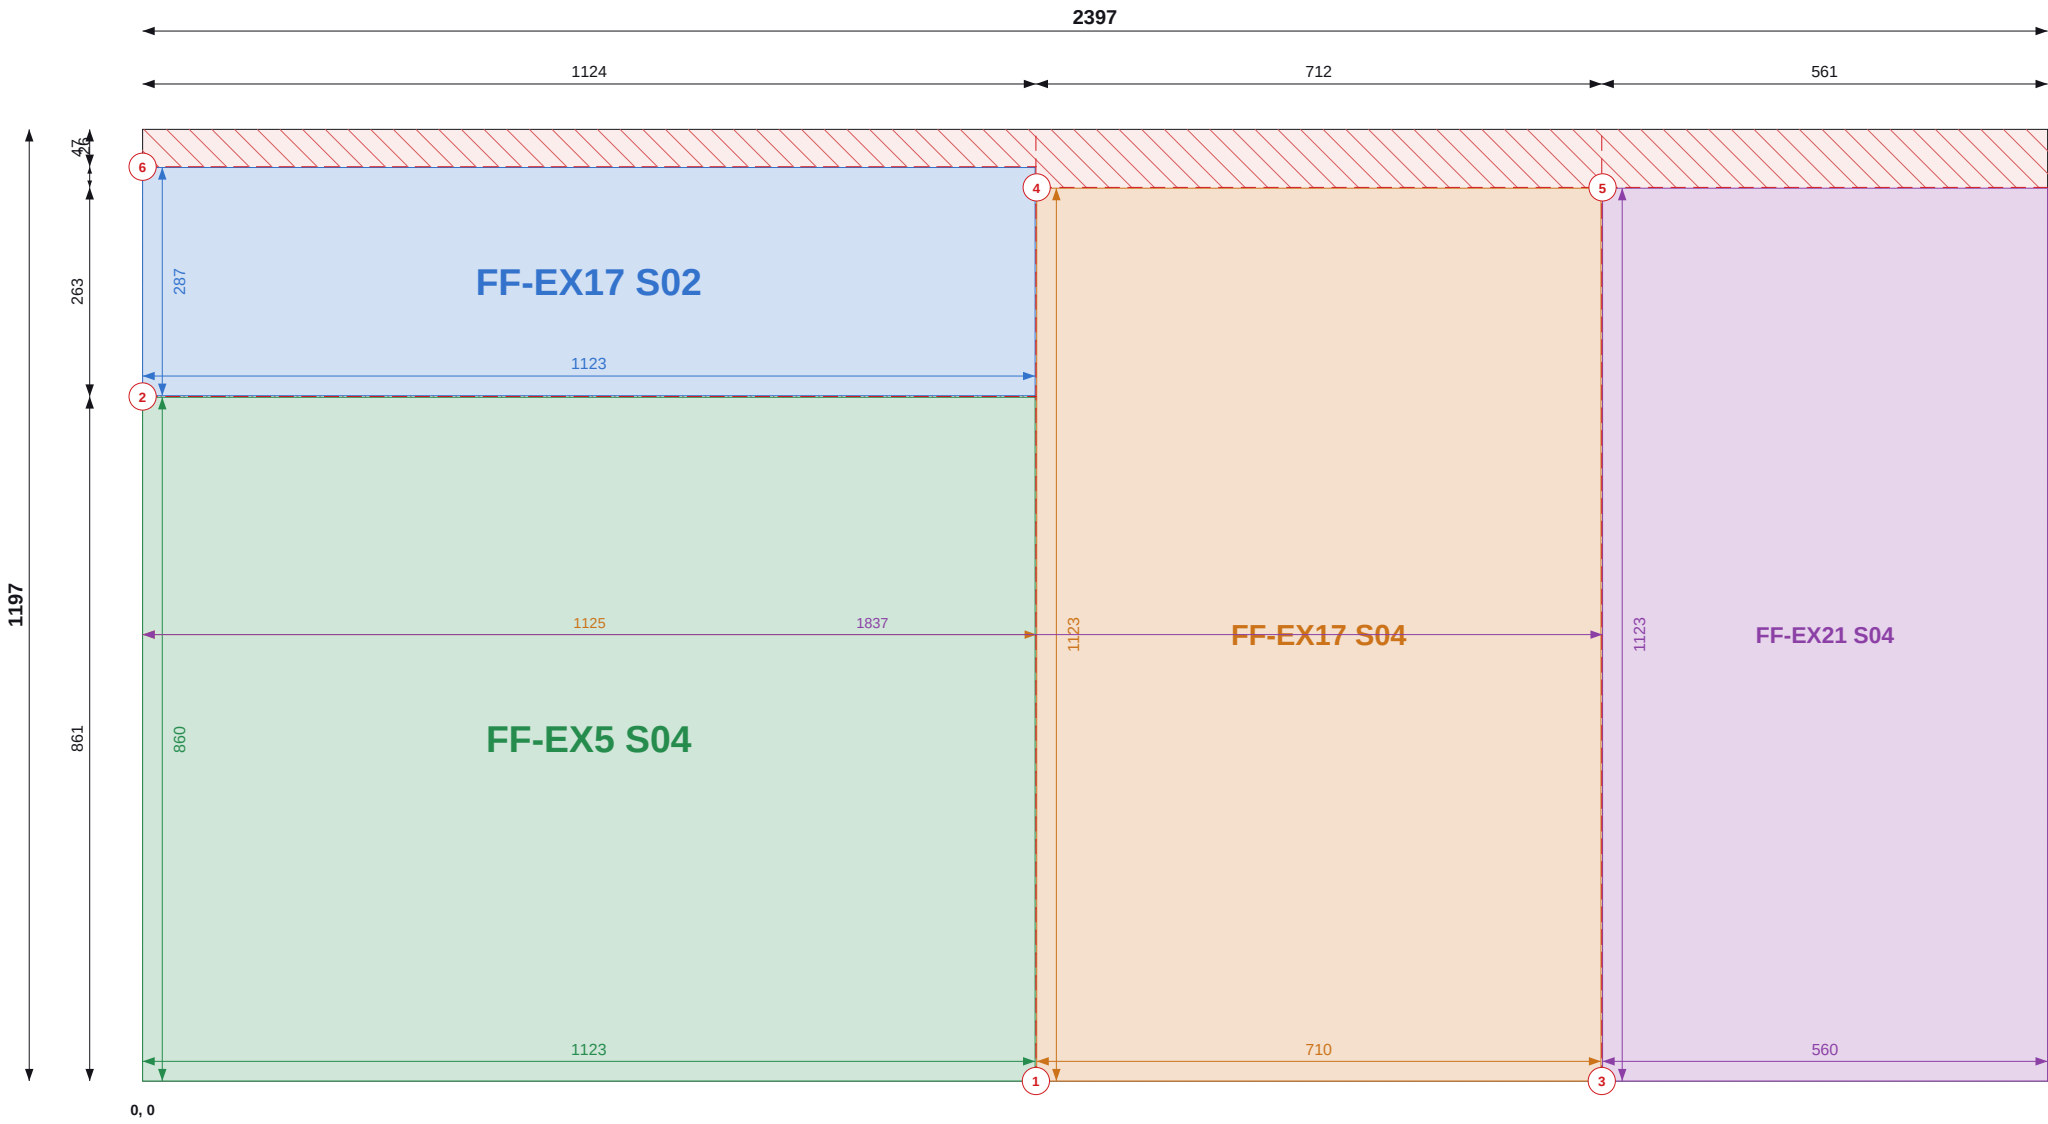

Top / left chains = saw cut positions (to cut centres). Coloured = part size and position.

SHEET 32 OF 34

THIS SHEET

Item	Value
Parts	4
Used / waste	94.6% / 0.15 m2
Reusable offcuts	0
Saw cuts / shared	6 / 3

PIECES (POSITION = BOTTOM-LEFT CORNER)

Label	Size	X, Y
FF-EX17 S02	1123 x 287	0, 862
FF-EX5 S04	1123 x 860	0, 0
FF-EX17 S04	1123 x 710	1125, 0
FF-EX21 S04	1123 x 560	1837, 0

NOTES

- Cut from OSB/3 9mm 1197x2397, 2mm saw kerf. Viewed on the face; dimensions from the sheet's bottom-left corner (0,0). Red numbered lines = saw cuts in order, each edge to edge.
- Coloured dimensions belong to the part of that colour: its width and height, and its position from the sheet edges. Raked parts: corner coordinates at each corner.
- Red hatch = waste. Labels = panel + piece mark on the manufacture drawing.

REVISIONS

REV	DATE	DESCRIPTION
C01	13.09.26	Construction issue



TLS TIMBER FRAME

Design & Manufacture

Scan: 3D model + drawings



CLIENT	PROJECT
MP Adams	MP Adams Plot 3, Eckington

DRAWING TITLE
OSB CUTTING - FIRST FLOOR - SHEET 32 OF 34

OSB/3 9mm 1197x2397 | First Floor

SCALE	SIZE	DATE	DRAWN
NTS	A3	13.09.26	TS

STATUS	DRAWING No.	REV
CONSTRUCTION	P3-CP-OSB-02 / 32	C01

Item	Value
Parts	6
Used / waste	89.2% / 0.31 m2
Reusable offcuts	0
Saw cuts / shared	9 / 5

PIECES (POSITION = BOTTOM-LEFT CORNER)

Label	Size	X, Y
FF-EX5 S02	1123 x 287	0, 851
FF-EX15 S03	688 x 287	1125, 815
FF-EX21 S02	1123 x 287	0, 562
FF-EX2 S04	1123 x 560	0, 0
FF-EX8 S04	813 x 710	1125, 0
FF-EX19 S05	913 x 560	1837, 0

NOTES

1. Cut from OSB/3 9mm 1197x2397, 2mm saw kerf. Viewed on the face; dimensions from the sheet's bottom-left corner (0,0). Red numbered lines = saw cuts in order, each edge to edge.
2. Coloured dimensions belong to the part of that colour: its width and height, and its position from the sheet edges. Raked parts: corner coordinates at each corner.
3. Red hatch = waste. Labels = panel + piece mark on the manufacture drawing.

REVISIONS

REV	DATE	DESCRIPTION
C01	13.09.26	Construction issue



TLS TIMBER FRAME

Design & Manufacture 

Scan: 3D model + drawings



CLIENT	PROJECT
MP Adams	MP Adams Plot 3, Eckington

DRAWING TITLE


OSB CUTTING - FIRST FLOOR - SHEET 33 OF 34

OSB/3 9mm 1197x2397 | First Floor

SCALE	SIZE	DATE	DRAWN
NTS	A3	13.09.26	TS


STATUS	DRAWING No.	REV
CONSTRUCTION	P3-CP-OSB-02 / 33	C01

Do not scale. All dimensions in mm. Check all dimensions on site.

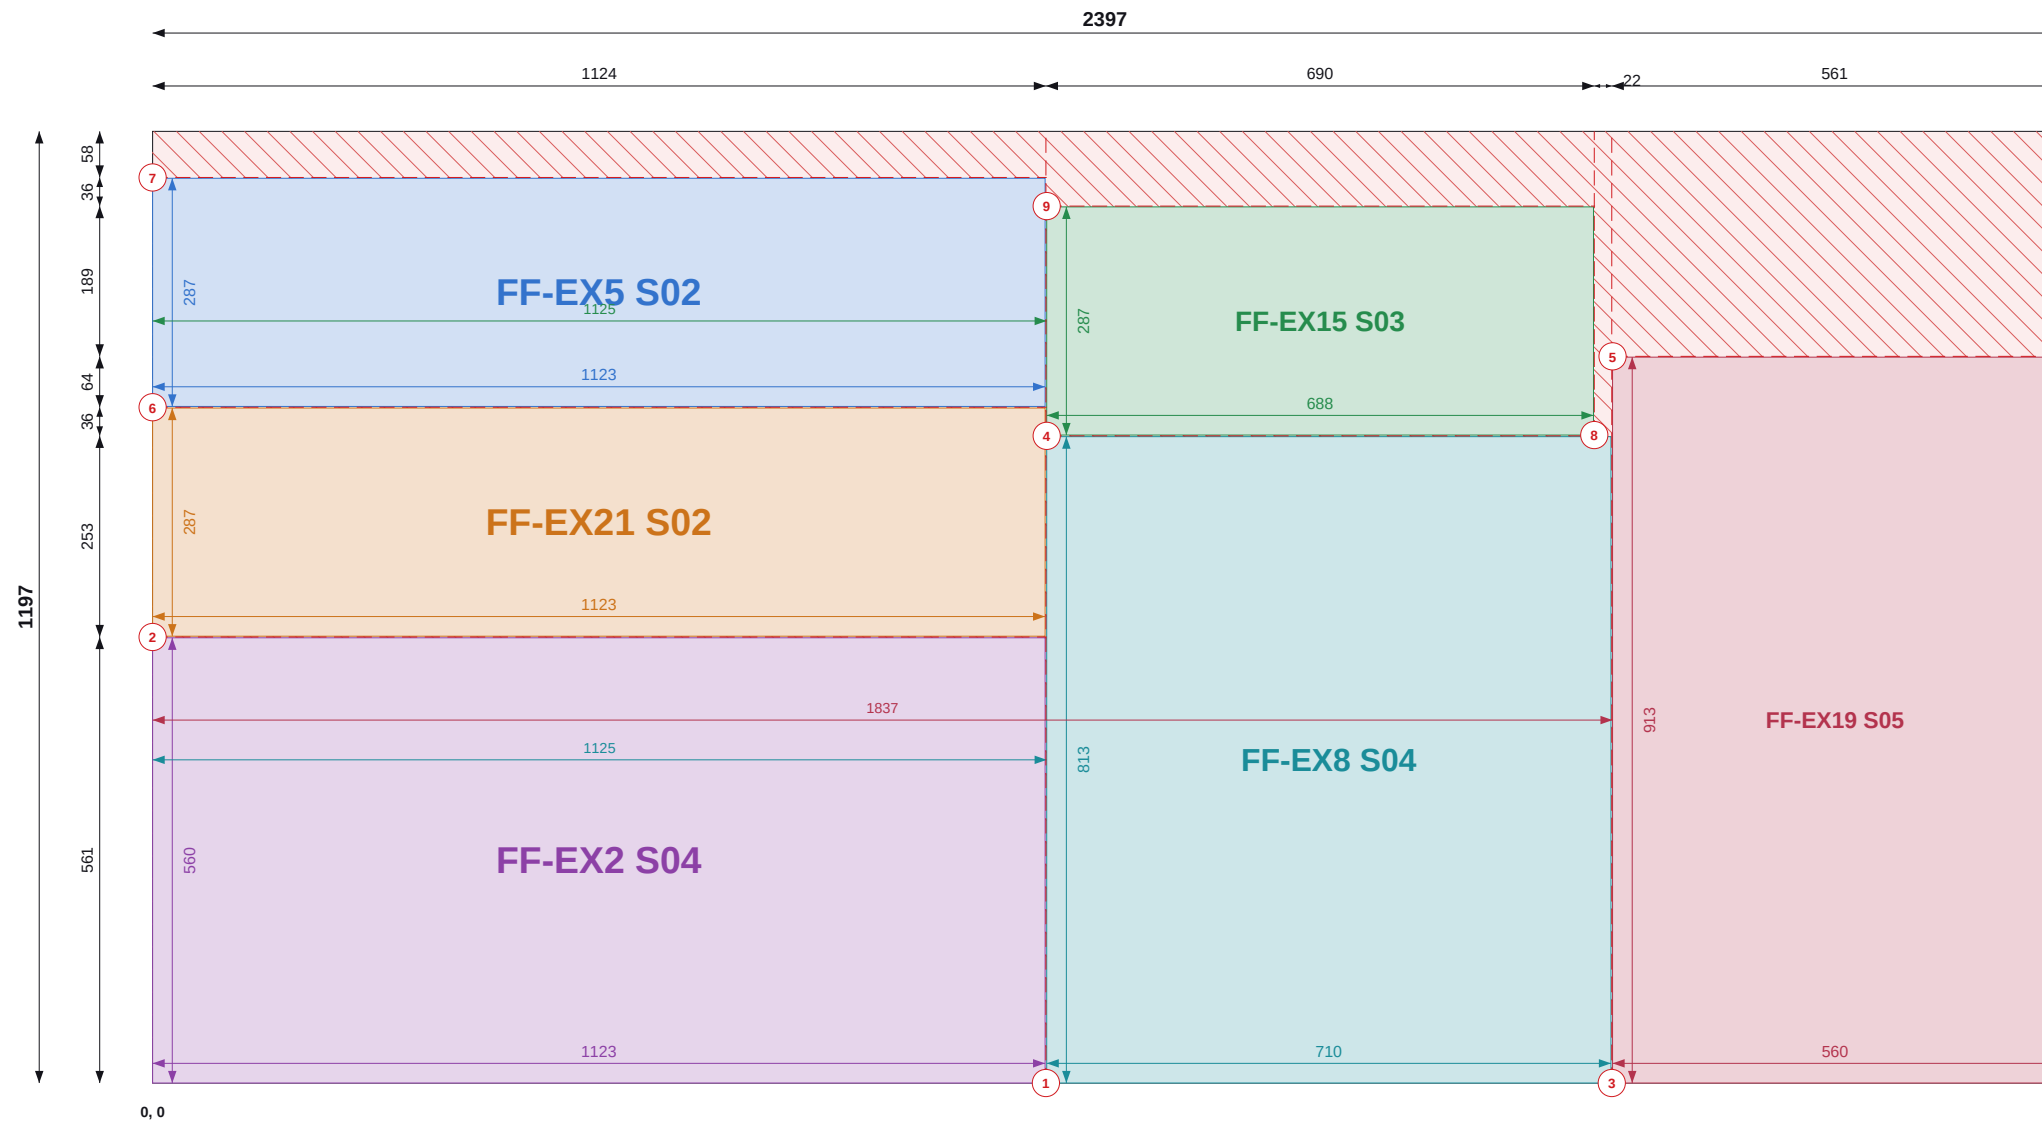

Top / left chains = saw cut positions (to cut centres). Coloured = part size and position.

Do not scale. All dimensions in mm. Check all dimensions on site.

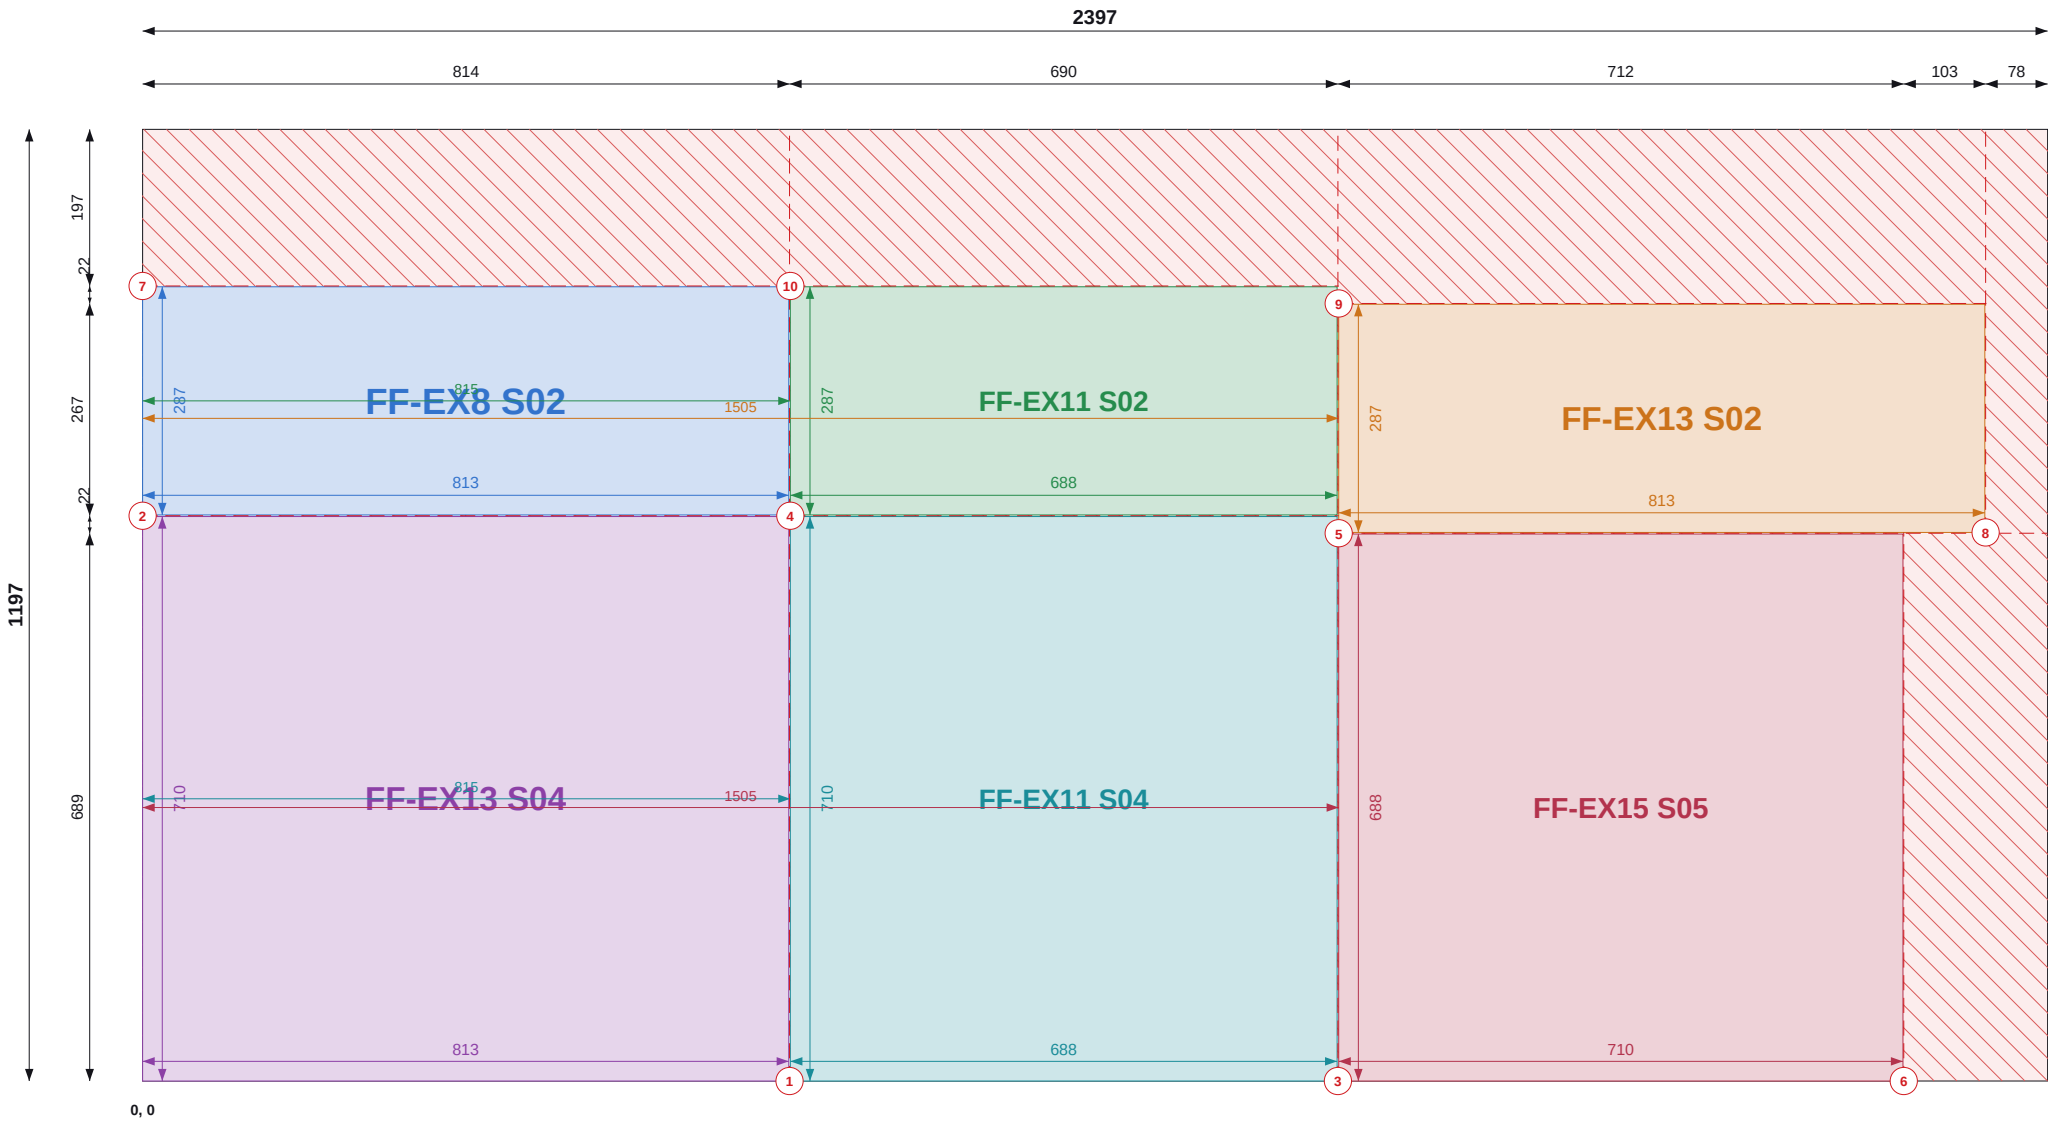

Top / left chains = saw cut positions (to cut centres). Coloured = part size and position.

SHEET 34 OF 34

THIS SHEET

Item	Value
Parts	6
Used / waste	77.3% / 0.65 m2
Reusable offcuts	0
Saw cuts / shared	10 / 5

PIECES (POSITION = BOTTOM-LEFT CORNER)

Label	Size	X, Y
FF-EX8 S02	813 x 287	0, 712
FF-EX11 S02	688 x 287	815, 712
FF-EX13 S02	813 x 287	1505, 690
FF-EX13 S04	813 x 710	0, 0
FF-EX11 S04	688 x 710	815, 0
FF-EX15 S05	688 x 710	1505, 0

NOTES

- Cut from OSB/3 9mm 1197x2397, 2mm saw kerf. Viewed on the face; dimensions from the sheet's bottom-left corner (0,0). Red numbered lines = saw cuts in order, each edge to edge.
- Coloured dimensions belong to the part of that colour: its width and height, and its position from the sheet edges. Raked parts: corner coordinates at each corner.
- Red hatch = waste. Labels = panel + piece mark on the manufacture drawing.

REVISIONS

REV	DATE	DESCRIPTION
C01	13.09.26	Construction issue



TLS TIMBER FRAME

Design & Manufacture

Scan: 3D model + drawings



CLIENT MP Adams	PROJECT MP Adams Plot 3, Eckington
--------------------	---------------------------------------


DRAWING TITLE OSB CUTTING - FIRST FLOOR - SHEET 34 OF 34
--

OSB/3 9mm 1197x2397 | First Floor

SCALE NTS	SIZE A3	DATE 13.09.26	DRAWN TS
--------------	------------	------------------	-------------

STATUS CONSTRUCTION	DRAWING No. P3-CP-OSB-02 / 34	REV C01
-------------------------------	---	-------------------

Do not scale. All dimensions in mm. Check all dimensions on site.

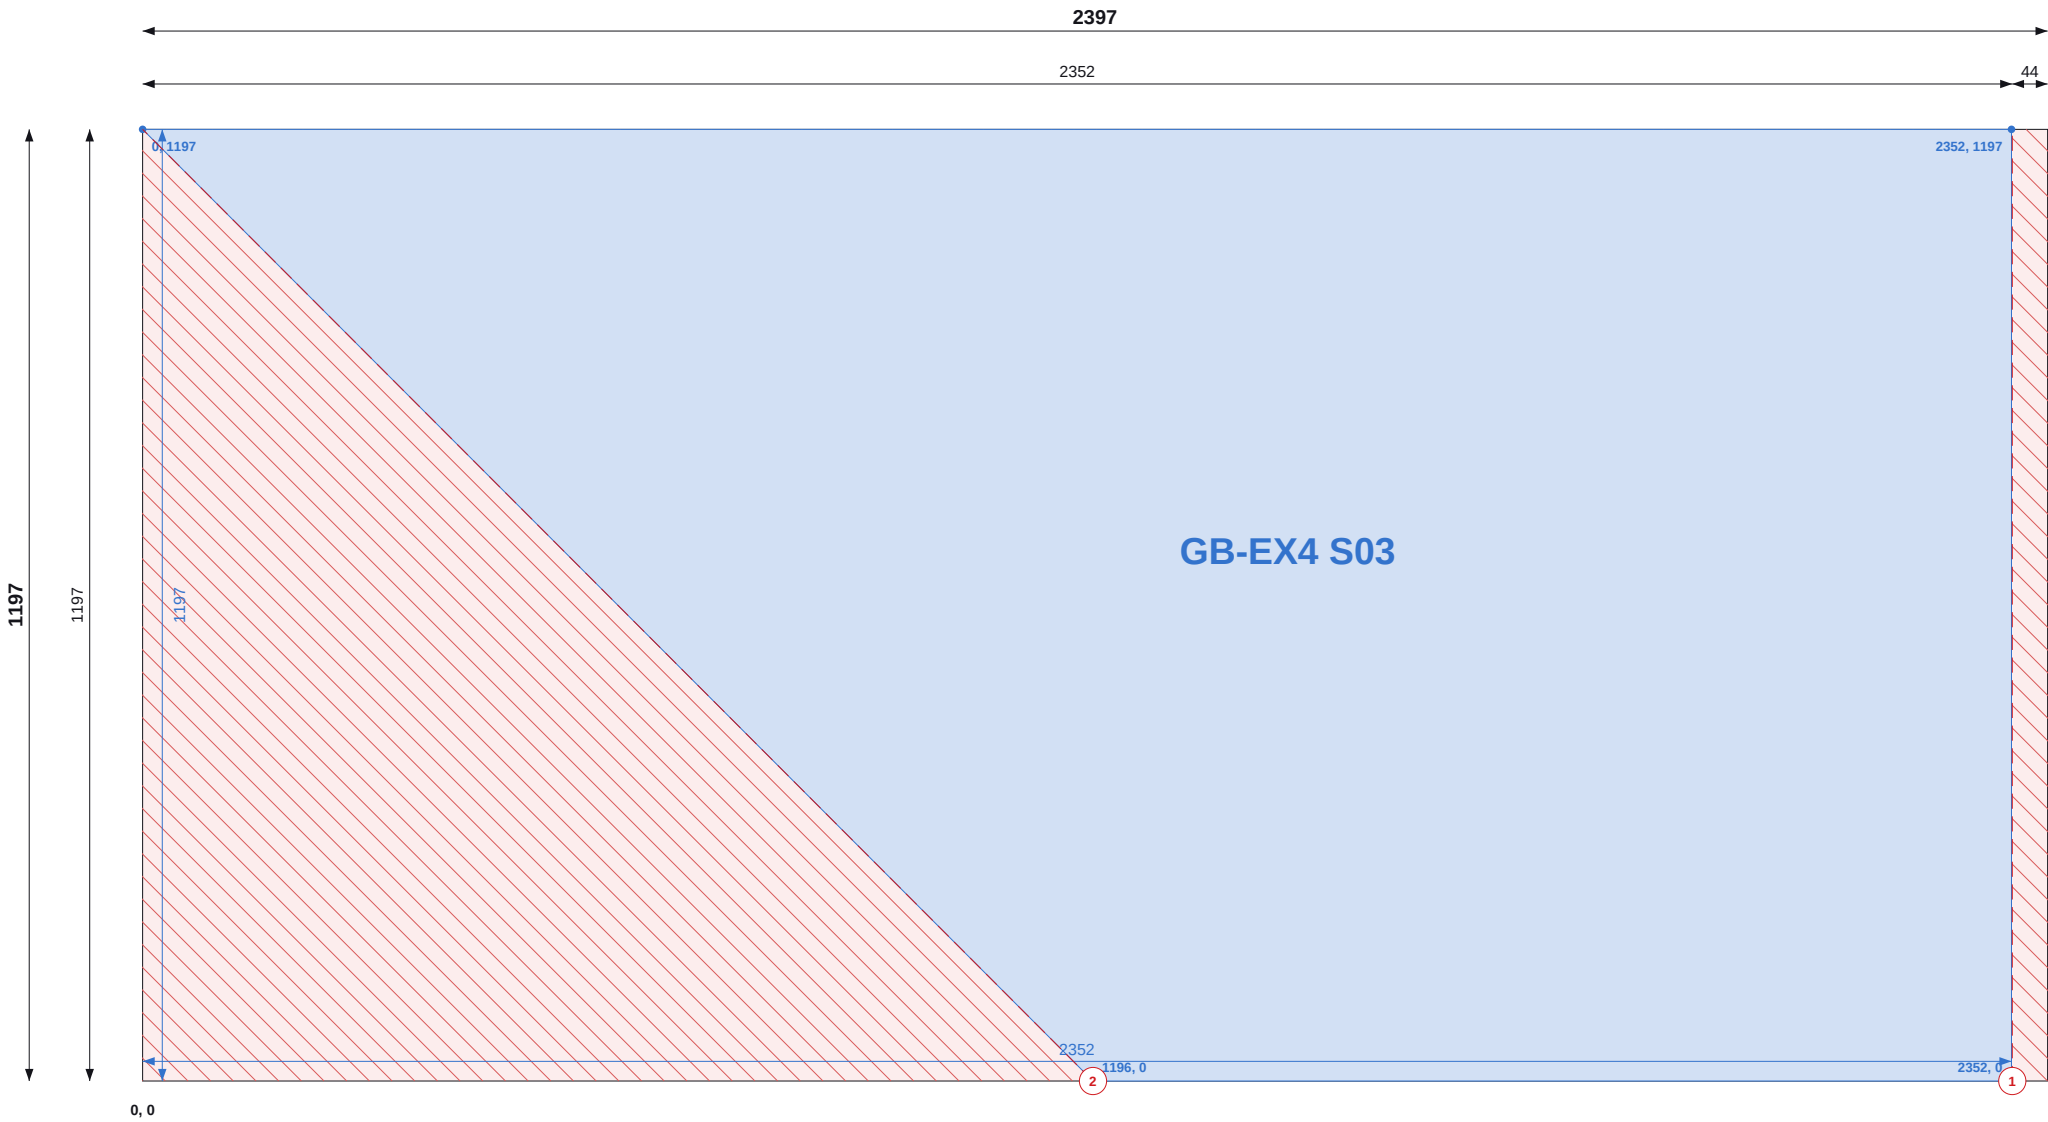

SHEET 1 OF 14

THIS SHEET

Item	Value
Parts	1
Used / waste	73.2% / 0.77 m2
Reusable offcuts	0
Saw cuts / shared	2 / 1

PIECES (POSITION = BOTTOM-LEFT CORNER)

Label	Size	X, Y
GB-EX4 S03	1197 x 2351 rake to 1157	0, 0

GABLES TOTALS

Item	Value
Sheets / pieces	14 / 34
Yield / waste	84.1% / 6.37 m2
Saw cuts / shared / on stock edge	55 / 35 / 55

NOTES

- Cut from OSB/3 9mm 1197x2397, 2mm saw kerf. Viewed on the face; dimensions from the sheet's bottom-left corner (0,0). Red numbered lines = saw cuts in order, each edge to edge.
- Coloured dimensions belong to the part of that colour: its width and height, and its position from the sheet edges. Raked parts: corner coordinates at each corner.
- Red hatch = waste. Labels = panel + piece mark on the manufacture drawing.

REVISIONS

REV	DATE	DESCRIPTION
C01	13.09.26	Construction issue



TLS TIMBER FRAME

Design & Manufacture

Scan: 3D model + drawings



CLIENT MP Adams	PROJECT MP Adams Plot 3, Eckington
--------------------	---------------------------------------


DRAWING TITLE OSB CUTTING - GABLES - SHEET 1 OF 14
--

OSB/3 9mm 1197x2397 | Gables

SCALE NTS	SIZE A3	DATE 13.09.26	DRAWN TS
--------------	------------	------------------	-------------

STATUS CONSTRUCTION	DRAWING No. P3-CP-OSB-03 / 01	REV C01
-------------------------------	---	-------------------

Do not scale. All dimensions in mm. Check all dimensions on site.

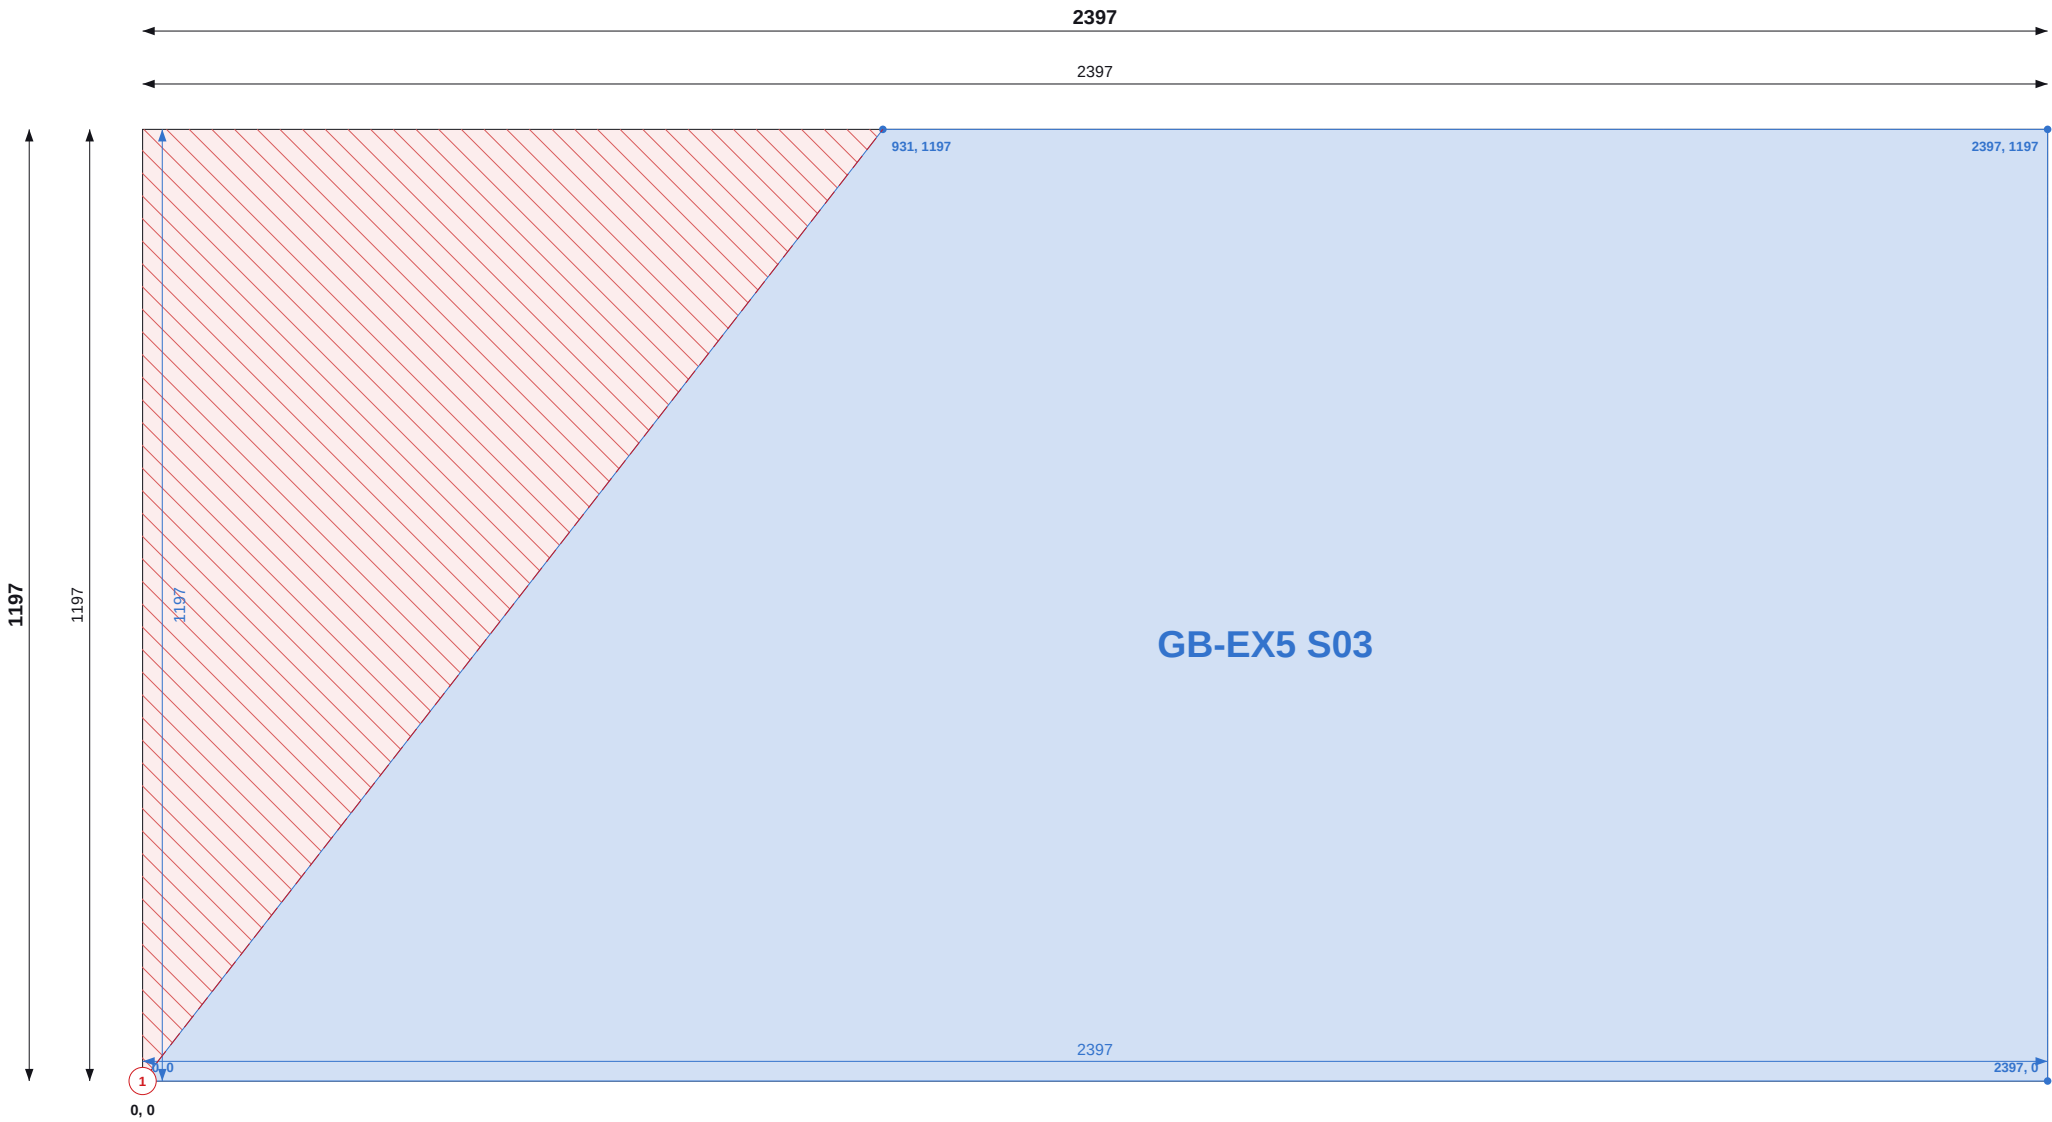

Top / left chains = saw cut positions (to cut centres). Coloured = part size and position.

SHEET 2 OF 14

THIS SHEET

Item	Value
Parts	1
Used / waste	80.6% / 0.56 m2
Reusable offcuts	0
Saw cuts / shared	1 / 1

PIECES (POSITION = BOTTOM-LEFT CORNER)

Label	Size	X, Y
GB-EX5 S03	1197 x 2397 rake to 1466	0, 0

NOTES

- Cut from OSB/3 9mm 1197x2397, 2mm saw kerf. Viewed on the face; dimensions from the sheet's bottom-left corner (0,0). Red numbered lines = saw cuts in order, each edge to edge.
- Coloured dimensions belong to the part of that colour: its width and height, and its position from the sheet edges. Raked parts: corner coordinates at each corner.
- Red hatch = waste. Labels = panel + piece mark on the manufacture drawing.

REVISIONS

REV	DATE	DESCRIPTION
C01	13.09.26	Construction issue



TLS TIMBER FRAME
Design & Manufacture
Scan: 3D model + drawings



CLIENT MP Adams	PROJECT MP Adams Plot 3, Eckington
--------------------	---------------------------------------


DRAWING TITLE OSB CUTTING - GABLES - SHEET 2 OF 14
--

OSB/3 9mm 1197x2397 | Gables

SCALE NTS	SIZE A3	DATE 13.09.26	DRAWN TS
--------------	------------	------------------	-------------

STATUS CONSTRUCTION	DRAWING No. P3-CP-OSB-03 / 02	REV C01
-------------------------------	---	-------------------

Do not scale. All dimensions in mm. Check all dimensions on site.

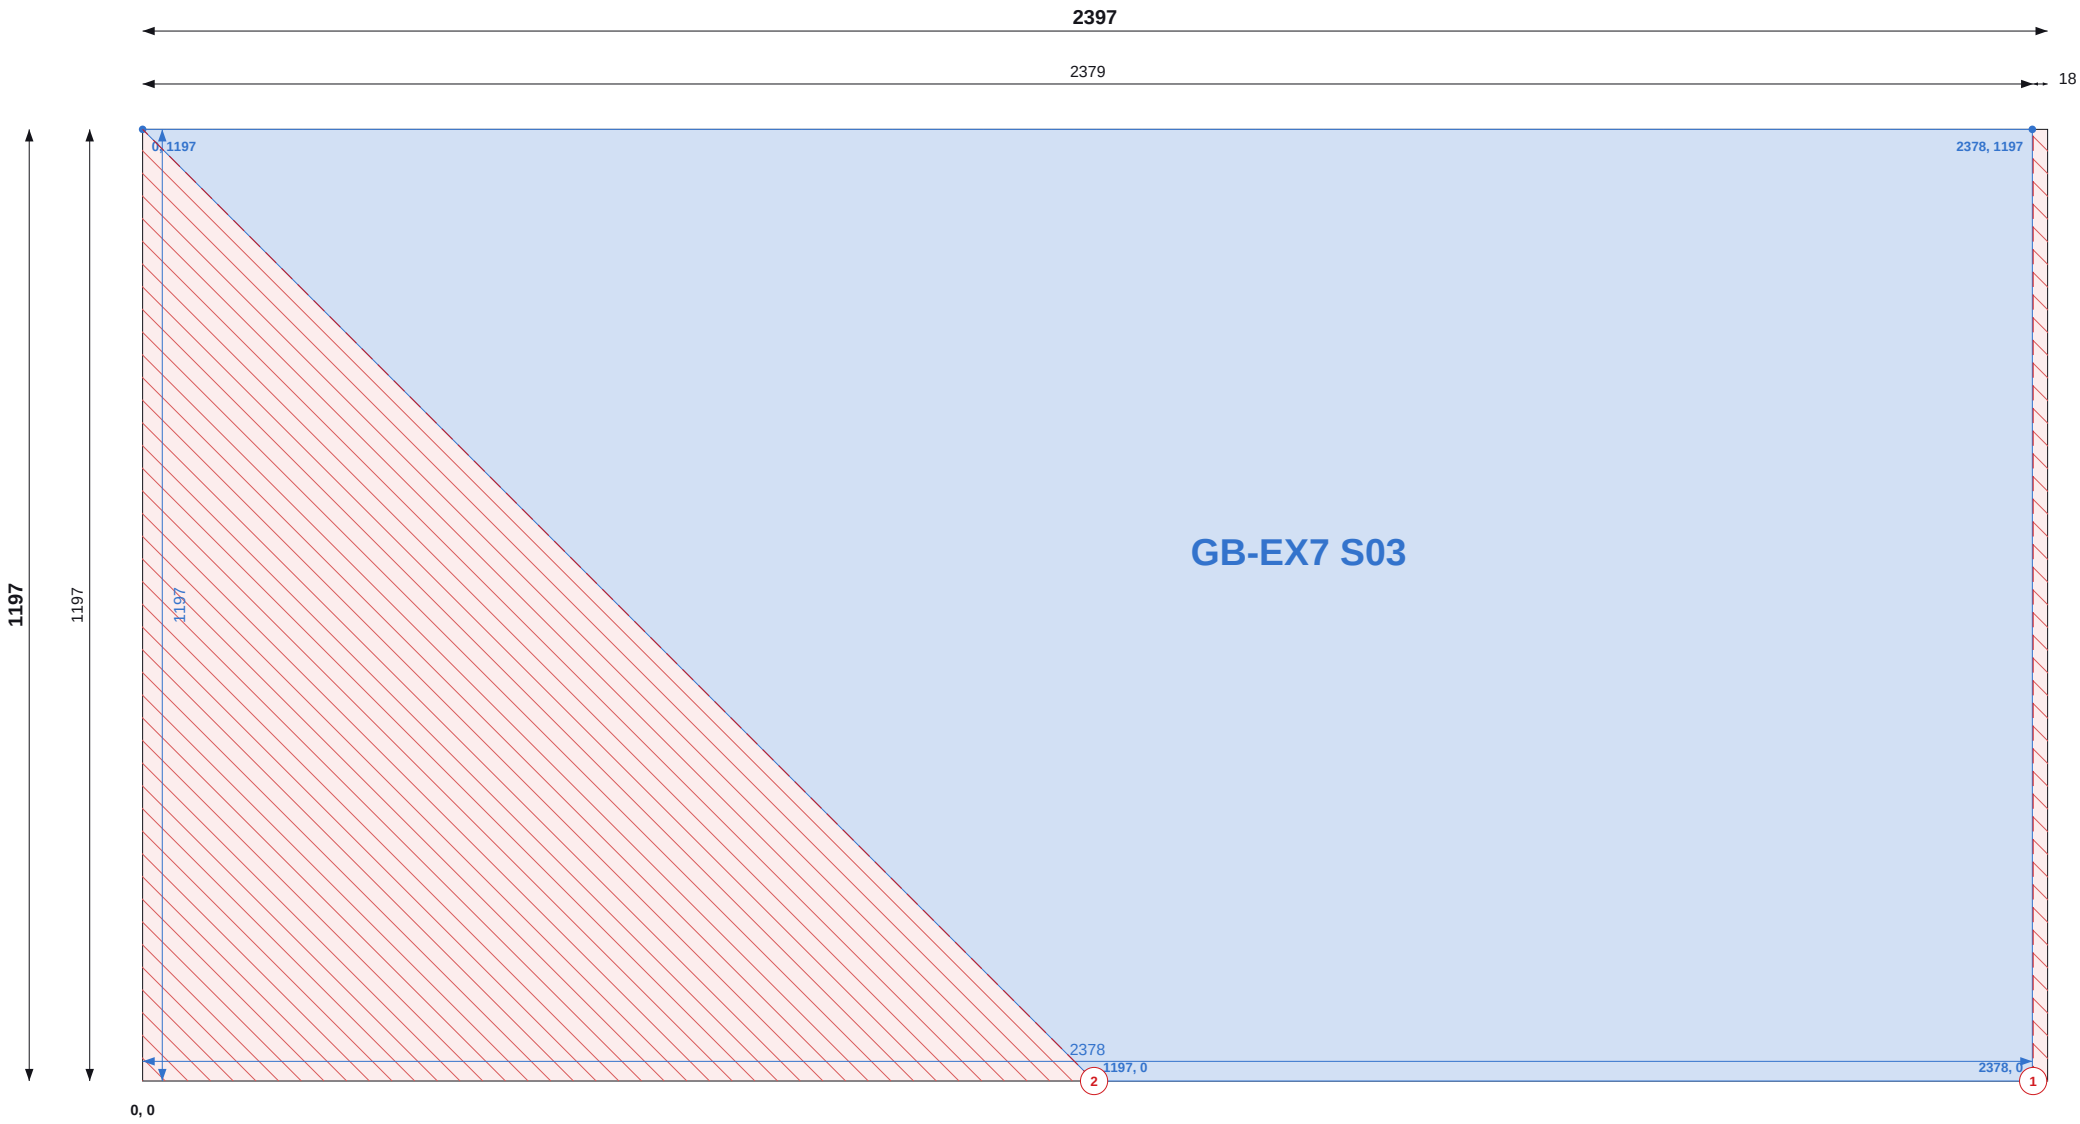

SHEET 3 OF 14

THIS SHEET

Item	Value
Parts	1
Used / waste	74.2% / 0.74 m2
Reusable offcuts	0
Saw cuts / shared	2 / 1

PIECES (POSITION = BOTTOM-LEFT CORNER)

Label	Size	X, Y
GB-EX7 S03	1197 x 2378 rake to 1182	0, 0

NOTES

- Cut from OSB/3 9mm 1197x2397, 2mm saw kerf. Viewed on the face; dimensions from the sheet's bottom-left corner (0,0). Red numbered lines = saw cuts in order, each edge to edge.
- Coloured dimensions belong to the part of that colour: its width and height, and its position from the sheet edges. Raked parts: corner coordinates at each corner.
- Red hatch = waste. Labels = panel + piece mark on the manufacture drawing.

REVISIONS

REV	DATE	DESCRIPTION
C01	13.09.26	Construction issue



TLS TIMBER FRAME

Design & Manufacture

Scan: 3D model + drawings



CLIENT	PROJECT
MP Adams	MP Adams Plot 3, Eckington

DRAWING TITLE
OSB CUTTING - GABLES - SHEET 3 OF 14

OSB/3 9mm 1197x2397 | Gables

SCALE	SIZE	DATE	DRAWN
NTS	A3	13.09.26	TS

STATUS	DRAWING No.	REV
CONSTRUCTION	P3-CP-OSB-03 / 03	C01

Do not scale. All dimensions in mm. Check all dimensions on site.



Top / left chains = saw cut positions (to cut centres). Coloured = part size and position.

SHEET 4 OF 14

THIS SHEET

Item	Value
Parts	1
Used / waste	100.0% / 0.00 m2
Reusable offcuts	0
Saw cuts / shared	0 / 0

PIECES (POSITION = BOTTOM-LEFT CORNER)

Label	Size	X, Y
GB-EX8 S05	1197 x 2397	0, 0

NOTES

- Cut from OSB/3 9mm 1197x2397, 2mm saw kerf. Viewed on the face; dimensions from the sheet's bottom-left corner (0,0). Red numbered lines = saw cuts in order, each edge to edge.
- Coloured dimensions belong to the part of that colour: its width and height, and its position from the sheet edges. Raked parts: corner coordinates at each corner.
- Red hatch = waste. Labels = panel + piece mark on the manufacture drawing.

REVISIONS

REV	DATE	DESCRIPTION
C01	13.09.26	Construction issue



TLS TIMBER FRAME

Design & Manufacture

Scan: 3D model + drawings



CLIENT	PROJECT
MP Adams	MP Adams Plot 3, Eckington


DRAWING TITLE
OSB CUTTING - GABLES - SHEET 4 OF 14

OSB/3 9mm 1197x2397 | Gables

SCALE	SIZE	DATE	DRAWN
NTS	A3	13.09.26	TS

STATUS	DRAWING No.	REV
CONSTRUCTION	P3-CP-OSB-03 / 04	C01

Do not scale. All dimensions in mm. Check all dimensions on site.

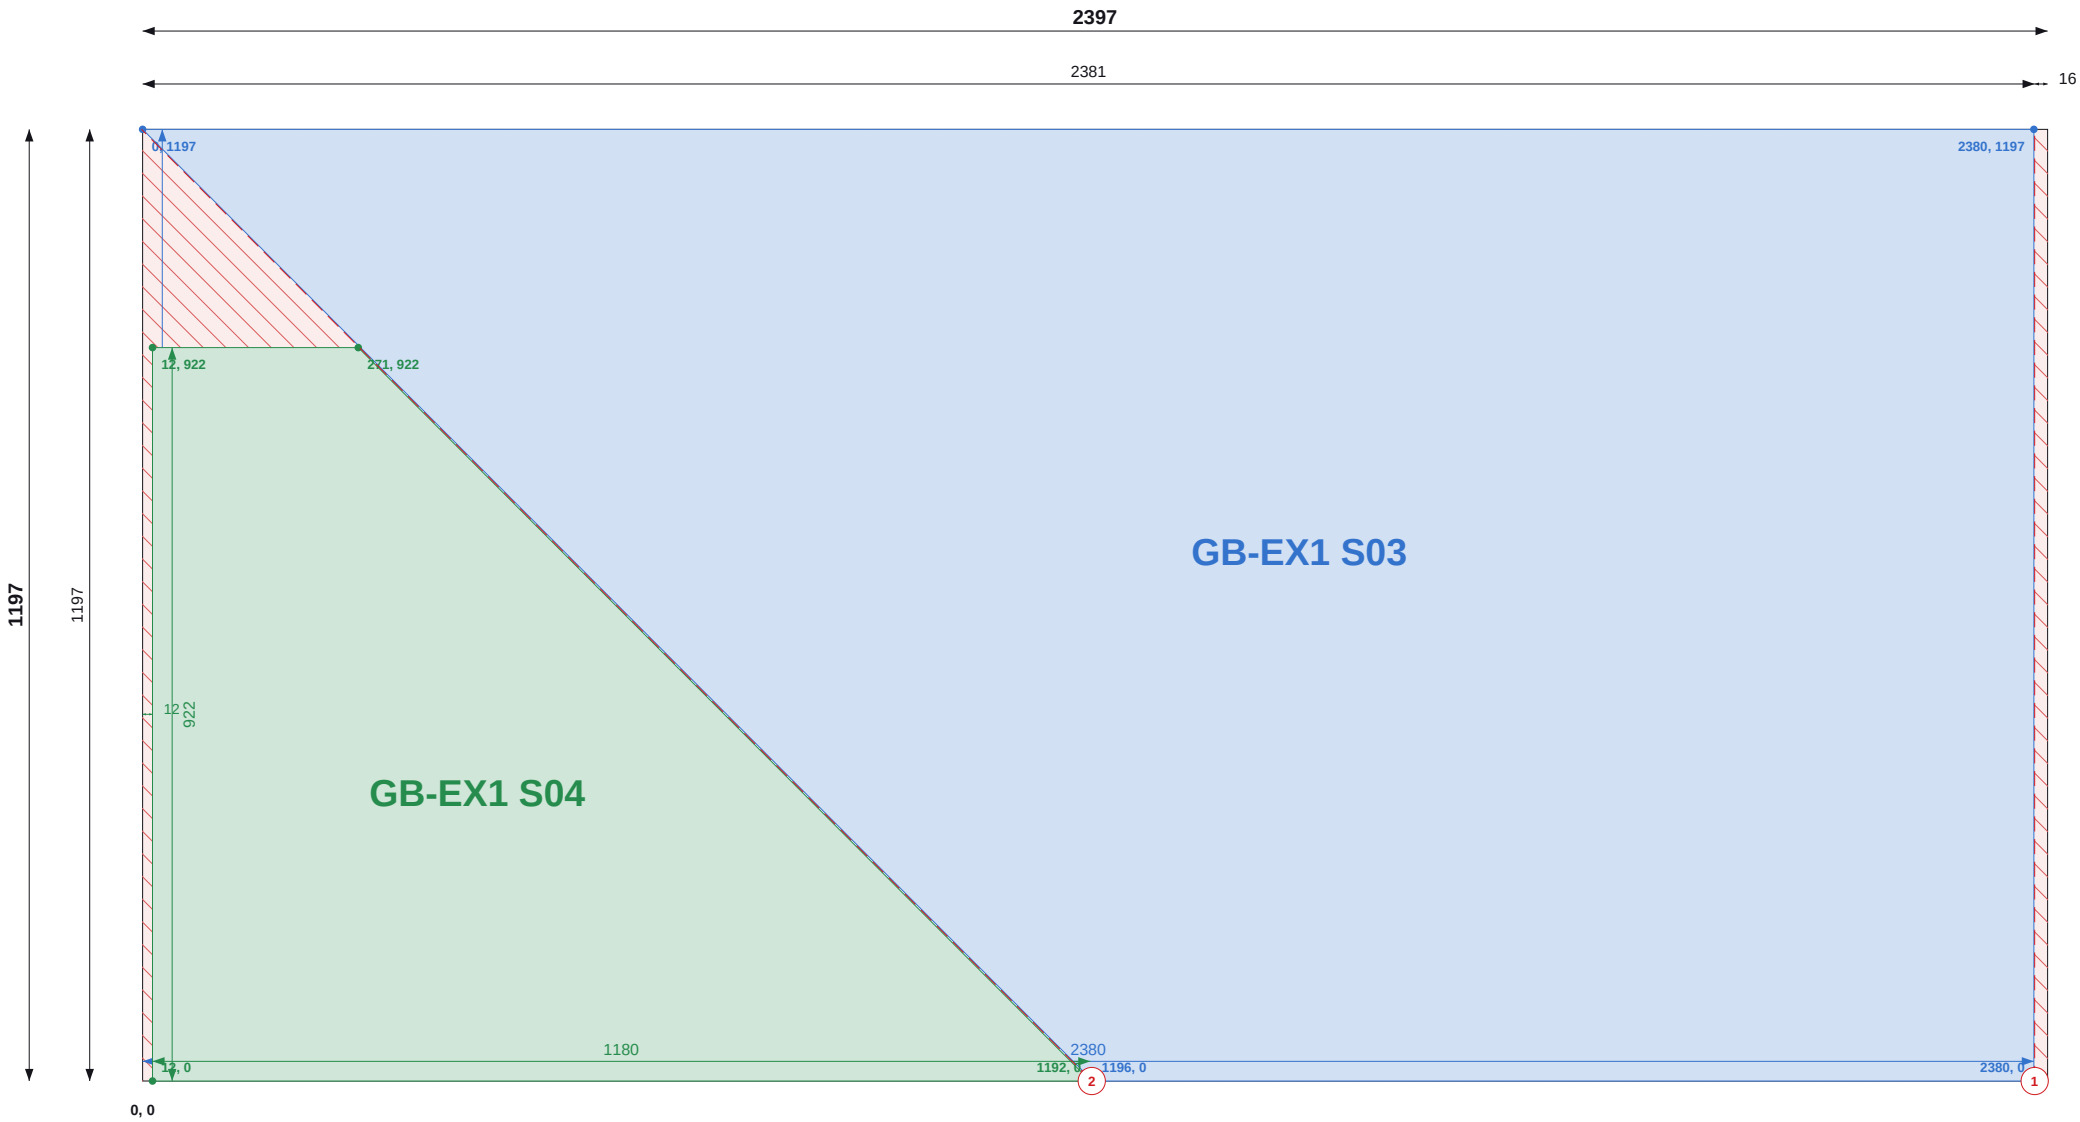

Top / left chains = saw cut positions (to cut centres). Coloured = part size and position.

SHEET 5 OF 14

THIS SHEET

Item	Value
Parts	2
Used / waste	97.5% / 0.07 m2
Reusable offcuts	0
Saw cuts / shared	2 / 1

PIECES (POSITION = BOTTOM-LEFT CORNER)

Label	Size	X, Y
GB-EX1 S03	1197 x 2380 rake to 1185	0, 0
GB-EX1 S04	922 x 1180 rake to 260	12, 0

NOTES

- Cut from OSB/3 9mm 1197x2397, 2mm saw kerf. Viewed on the face; dimensions from the sheet's bottom-left corner (0,0). Red numbered lines = saw cuts in order, each edge to edge.
- Coloured dimensions belong to the part of that colour: its width and height, and its position from the sheet edges. Raked parts: corner coordinates at each corner.
- Red hatch = waste. Labels = panel + piece mark on the manufacture drawing.

REVISIONS

REV	DATE	DESCRIPTION
C01	13.09.26	Construction issue



TLS TIMBER FRAME

Design & Manufacture

Scan: 3D model + drawings



CLIENT	PROJECT
MP Adams	MP Adams Plot 3, Eckington

DRAWING TITLE
OSB CUTTING - GABLES - SHEET 5 OF 14

OSB/3 9mm 1197x2397 | Gables

SCALE	SIZE	DATE	DRAWN
NTS	A3	13.09.26	TS

STATUS	DRAWING No.	REV
CONSTRUCTION	P3-CP-OSB-03 / 05	C01

Item	Value
Parts	3
Used / waste	71.8% / 0.81 m2
Reusable offcuts	0
Saw cuts / shared	8 / 5

PIECES (POSITION = BOTTOM-LEFT CORNER)

Label	Size	X, Y
GB-EX2 S03	833 x 833 rake to 3	1288, 254
GB-EX8 S01	1197 x 587 rake to 580	0, 0
GB-EX9 S02	922 x 1172 rake to 252	1199, 0

NOTES

1. Cut from OSB/3 9mm 1197x2397, 2mm saw kerf. Viewed on the face; dimensions from the sheet's bottom-left corner (0,0). Red numbered lines = saw cuts in order, each edge to edge.
2. Coloured dimensions belong to the part of that colour: its width and height, and its position from the sheet edges. Raked parts: corner coordinates at each corner.
3. Red hatch = waste. Labels = panel + piece mark on the manufacture drawing.

REVISIONS

REV	DATE	DESCRIPTION
C01	13.09.26	Construction issue



TLS TIMBER FRAME

Design & Manufacture

Scan: 3D model + drawings



CLIENT	PROJECT
MP Adams	MP Adams Plot 3, Eckington


DRAWING TITLE

OSB CUTTING - GABLES - SHEET 6 OF 14

OSB/3 9mm 1197x2397 | Gables


SCALE	SIZE	DATE	DRAWN
NTS	A3	13.09.26	TS

STATUS	DRAWING No.	REV
CONSTRUCTION	P3-CP-OSB-03 / 06	C01

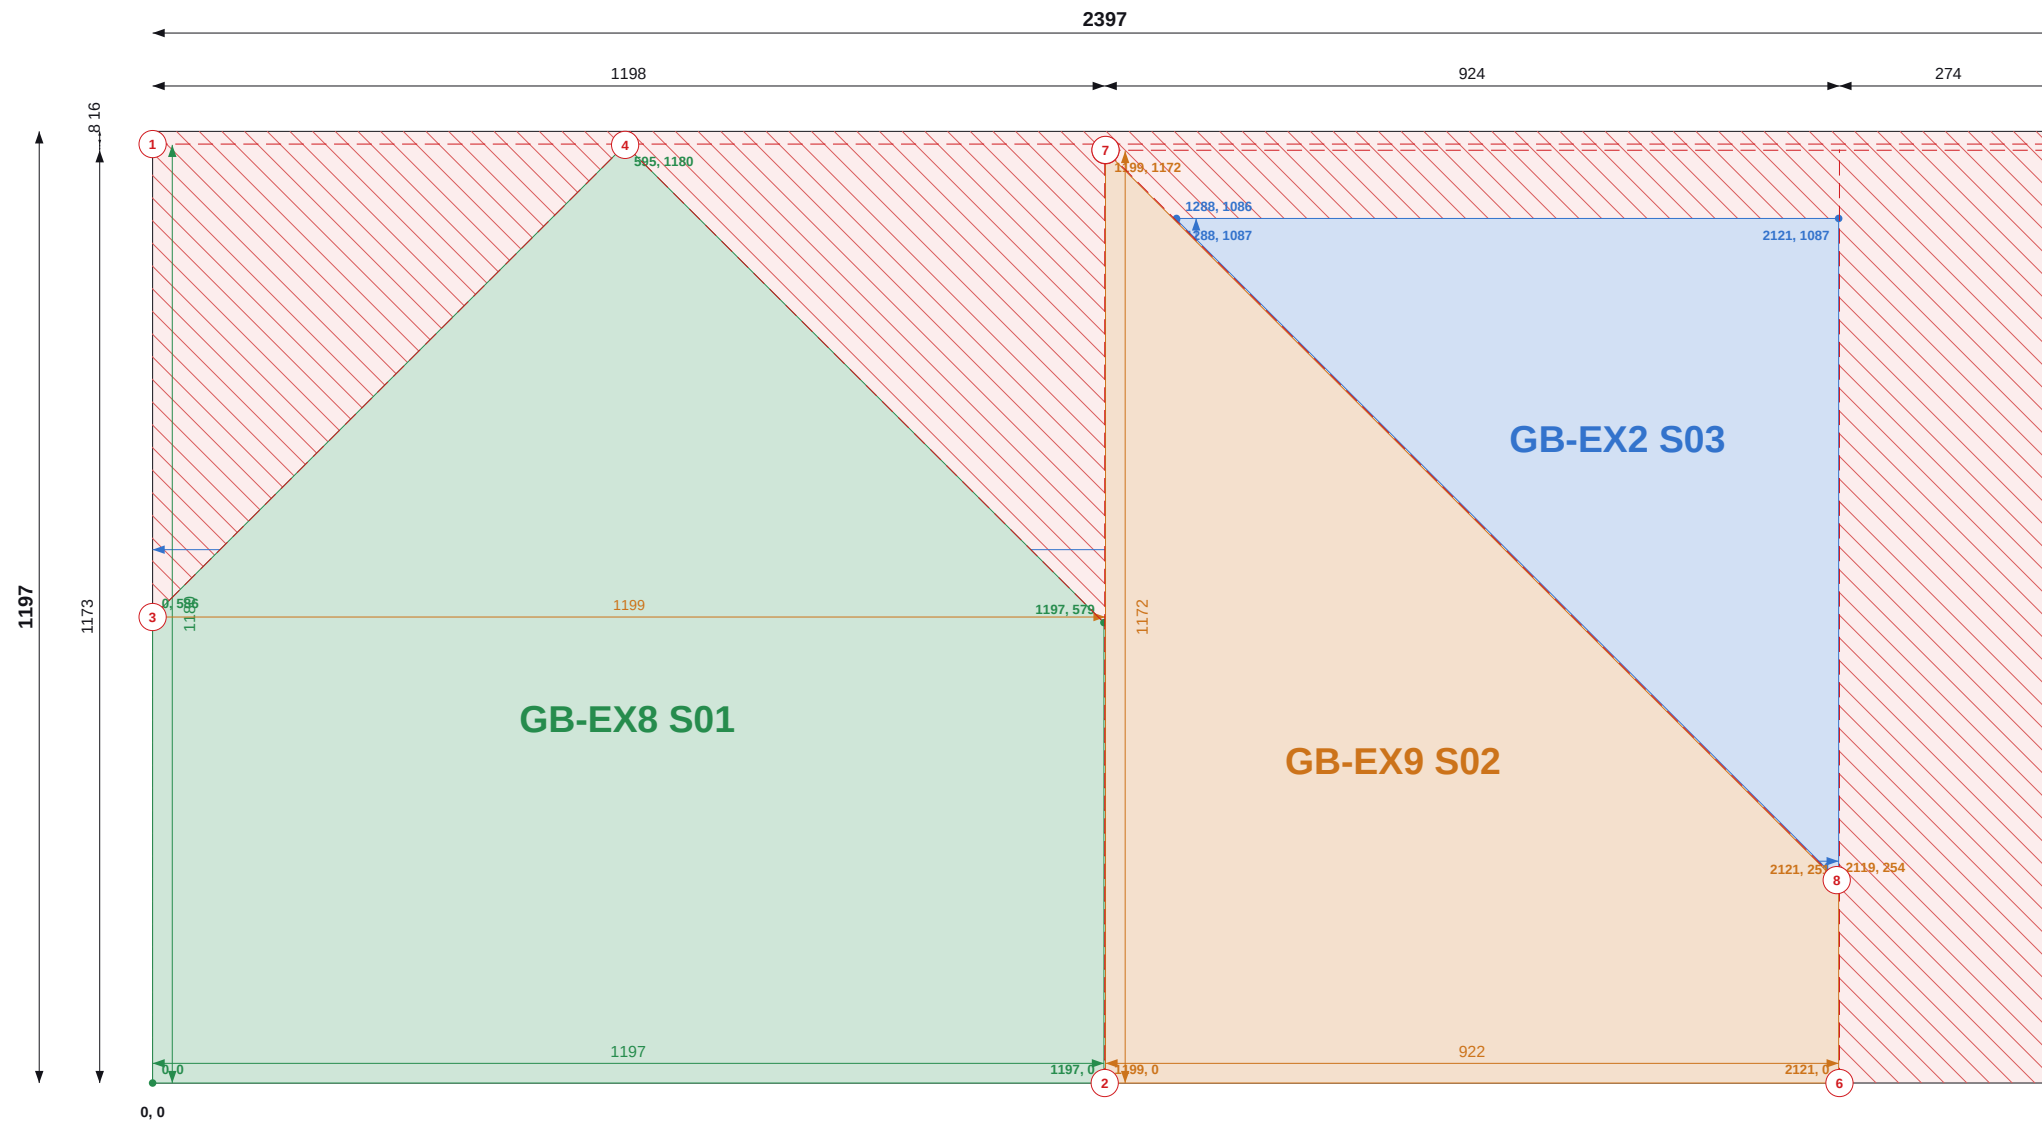

Top / left chains = saw cut positions (to cut centres). Coloured = part size and position.

Do not scale. All dimensions in mm. Check all dimensions on site.

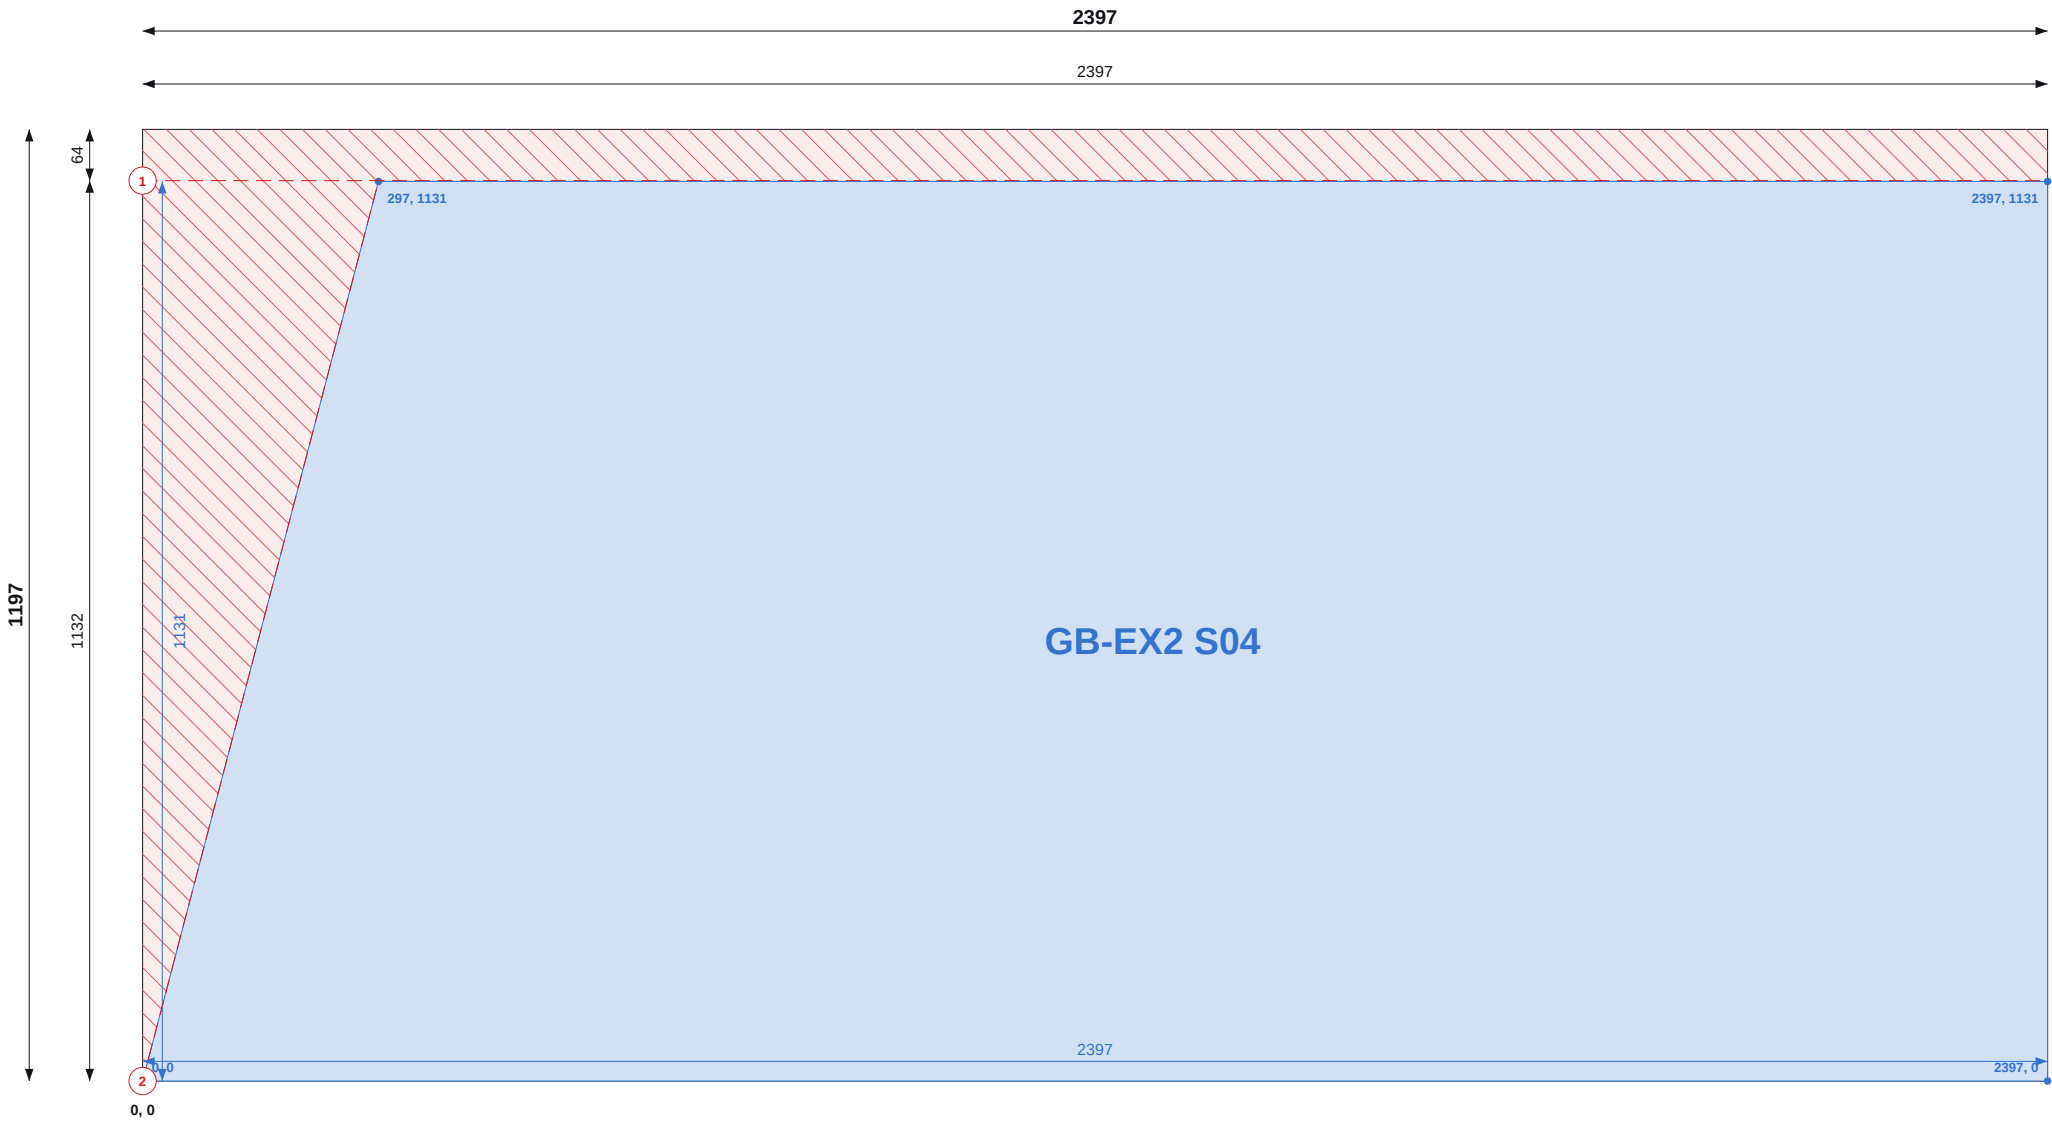

Top / left chains = saw cut positions (to cut centres). Coloured = part size and position.

SHEET 7 OF 14

THIS SHEET

Item	Value
Parts	1
Used / waste	88.7% / 0.32 m2
Reusable offcuts	0
Saw cuts / shared	2 / 1

PIECES (POSITION = BOTTOM-LEFT CORNER)

Label	Size	X, Y
GB-EX2 S04	1131 x 2397 rake to 2100	0, 0

NOTES

- Cut from OSB/3 9mm 1197x2397, 2mm saw kerf. Viewed on the face; dimensions from the sheet's bottom-left corner (0,0). Red numbered lines = saw cuts in order, each edge to edge.
- Coloured dimensions belong to the part of that colour: its width and height, and its position from the sheet edges. Raked parts: corner coordinates at each corner.
- Red hatch = waste. Labels = panel + piece mark on the manufacture drawing.

REVISIONS

REV	DATE	DESCRIPTION
C01	13.09.26	Construction issue



TLS TIMBER FRAME

Design & Manufacture

Scan: 3D model + drawings



CLIENT	PROJECT
MP Adams	MP Adams Plot 3, Eckington


DRAWING TITLE
OSB CUTTING - GABLES - SHEET 7 OF 14

OSB/3 9mm 1197x2397 | Gables

SCALE	SIZE	DATE	DRAWN
NTS	A3	13.09.26	TS

STATUS	DRAWING No.	REV
CONSTRUCTION	P3-CP-OSB-03 / 07	C01

Do not scale. All dimensions in mm. Check all dimensions on site.

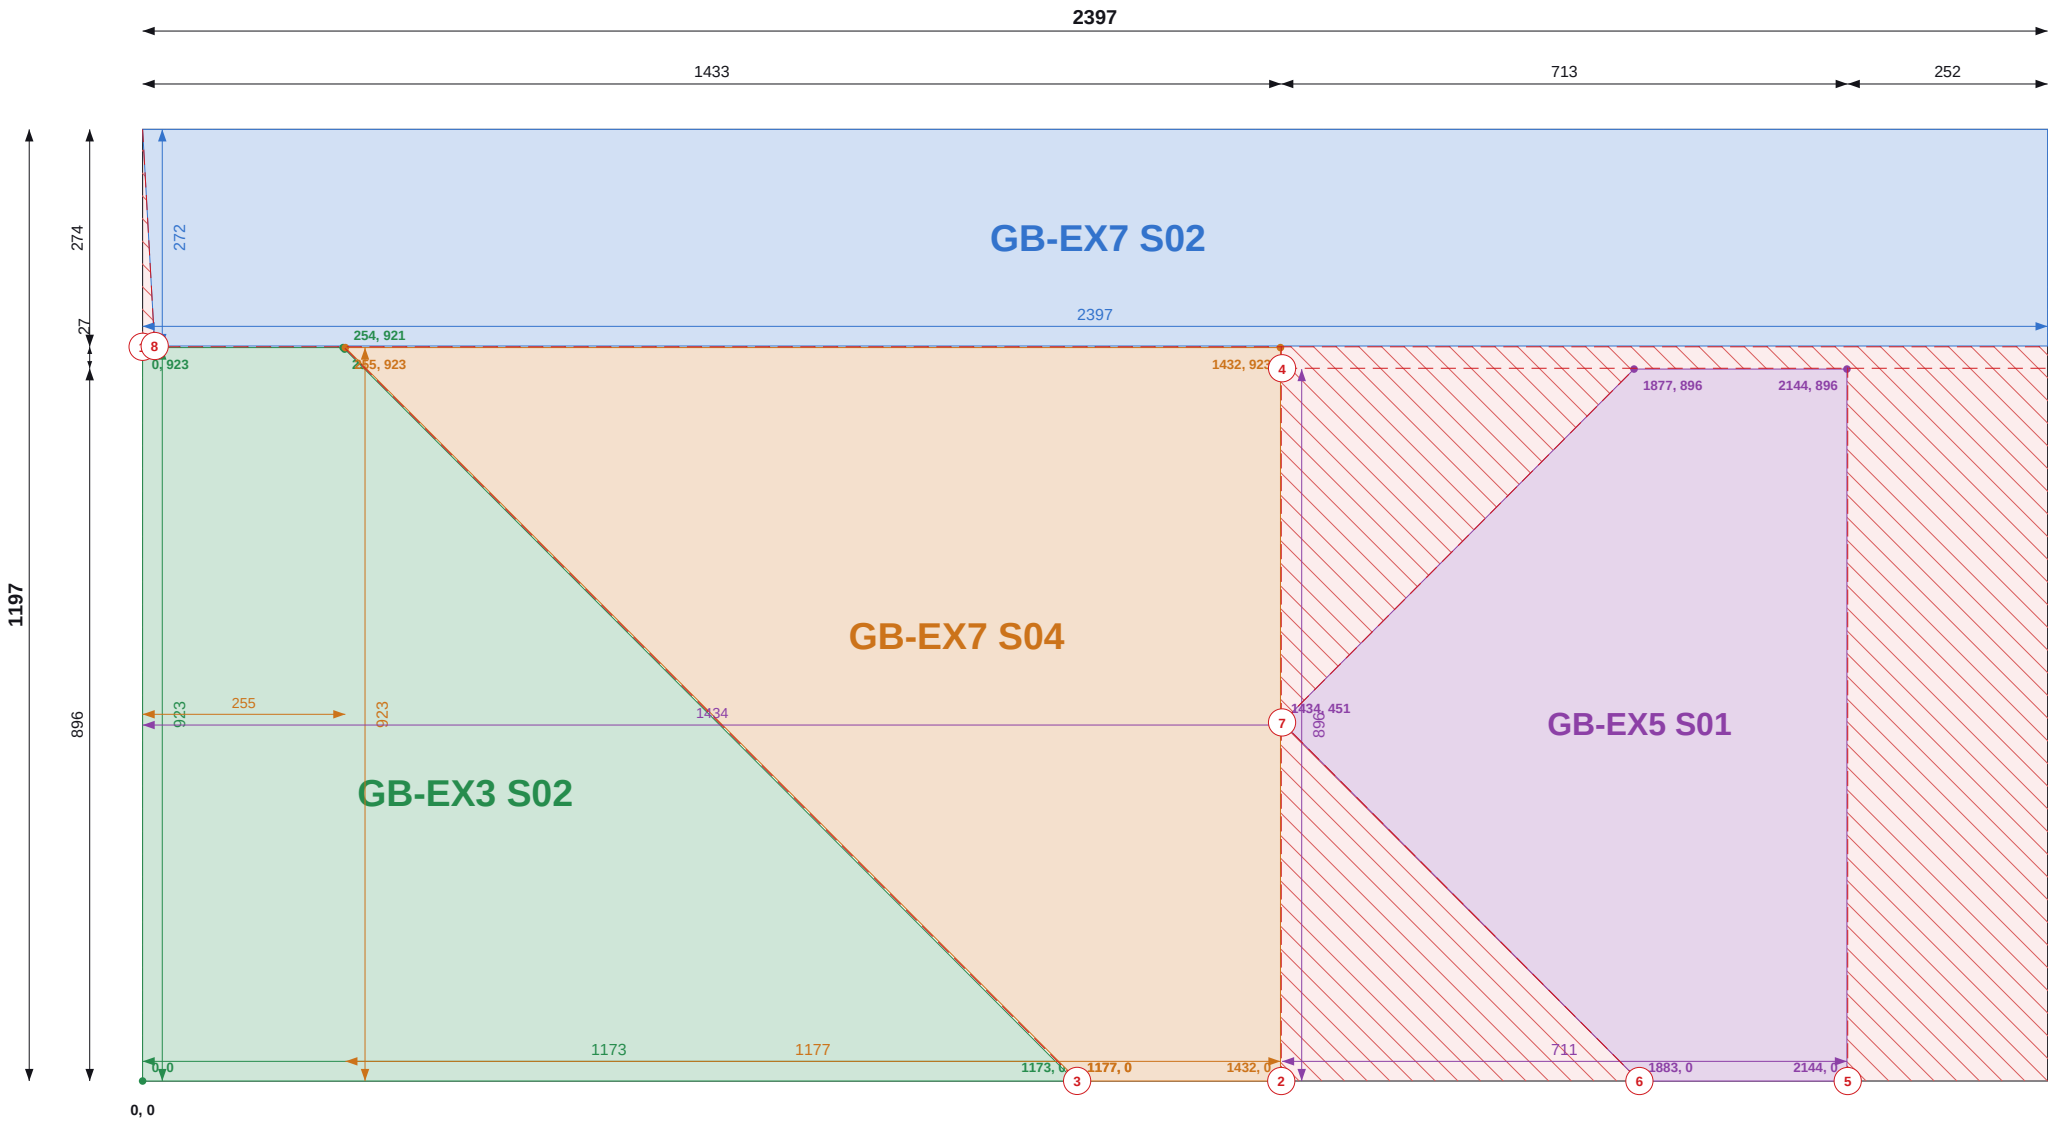

Top / left chains = saw cut positions (to cut centres). Coloured = part size and position.

SHEET 8 OF 14

THIS SHEET

Item	Value
Parts	4
Used / waste	83.8% / 0.46 m2
Reusable offcuts	0
Saw cuts / shared	8 / 6

PIECES (POSITION = BOTTOM-LEFT CORNER)

Label	Size	X, Y
GB-EX7 S02	272 x 2397	0, 925
GB-EX3 S02	923 x 1173 rake to 253	0, 0
GB-EX7 S04	923 x 1177 rake to 255	255, 0
GB-EX5 S01	896 x 269 rake to 262	1434, 0

NOTES

- Cut from OSB/3 9mm 1197x2397, 2mm saw kerf. Viewed on the face; dimensions from the sheet's bottom-left corner (0,0). Red numbered lines = saw cuts in order, each edge to edge.
- Coloured dimensions belong to the part of that colour: its width and height, and its position from the sheet edges. Raked parts: corner coordinates at each corner.
- Red hatch = waste. Labels = panel + piece mark on the manufacture drawing.

REVISIONS

REV	DATE	DESCRIPTION
C01	13.09.26	Construction issue



TLS TIMBER FRAME
Design & Manufacture
Scan: 3D model + drawings



CLIENT MP Adams	PROJECT MP Adams Plot 3, Eckington
--------------------	---------------------------------------


DRAWING TITLE
OSB CUTTING - GABLES - SHEET 8 OF 14

OSB/3 9mm 1197x2397 | Gables

SCALE NTS	SIZE A3	DATE 13.09.26	DRAWN TS
--------------	------------	------------------	-------------

STATUS CONSTRUCTION	DRAWING No. P3-CP-OSB-03 / 08	REV C01
-------------------------------	---	-------------------

Do not scale. All dimensions in mm. Check all dimensions on site.

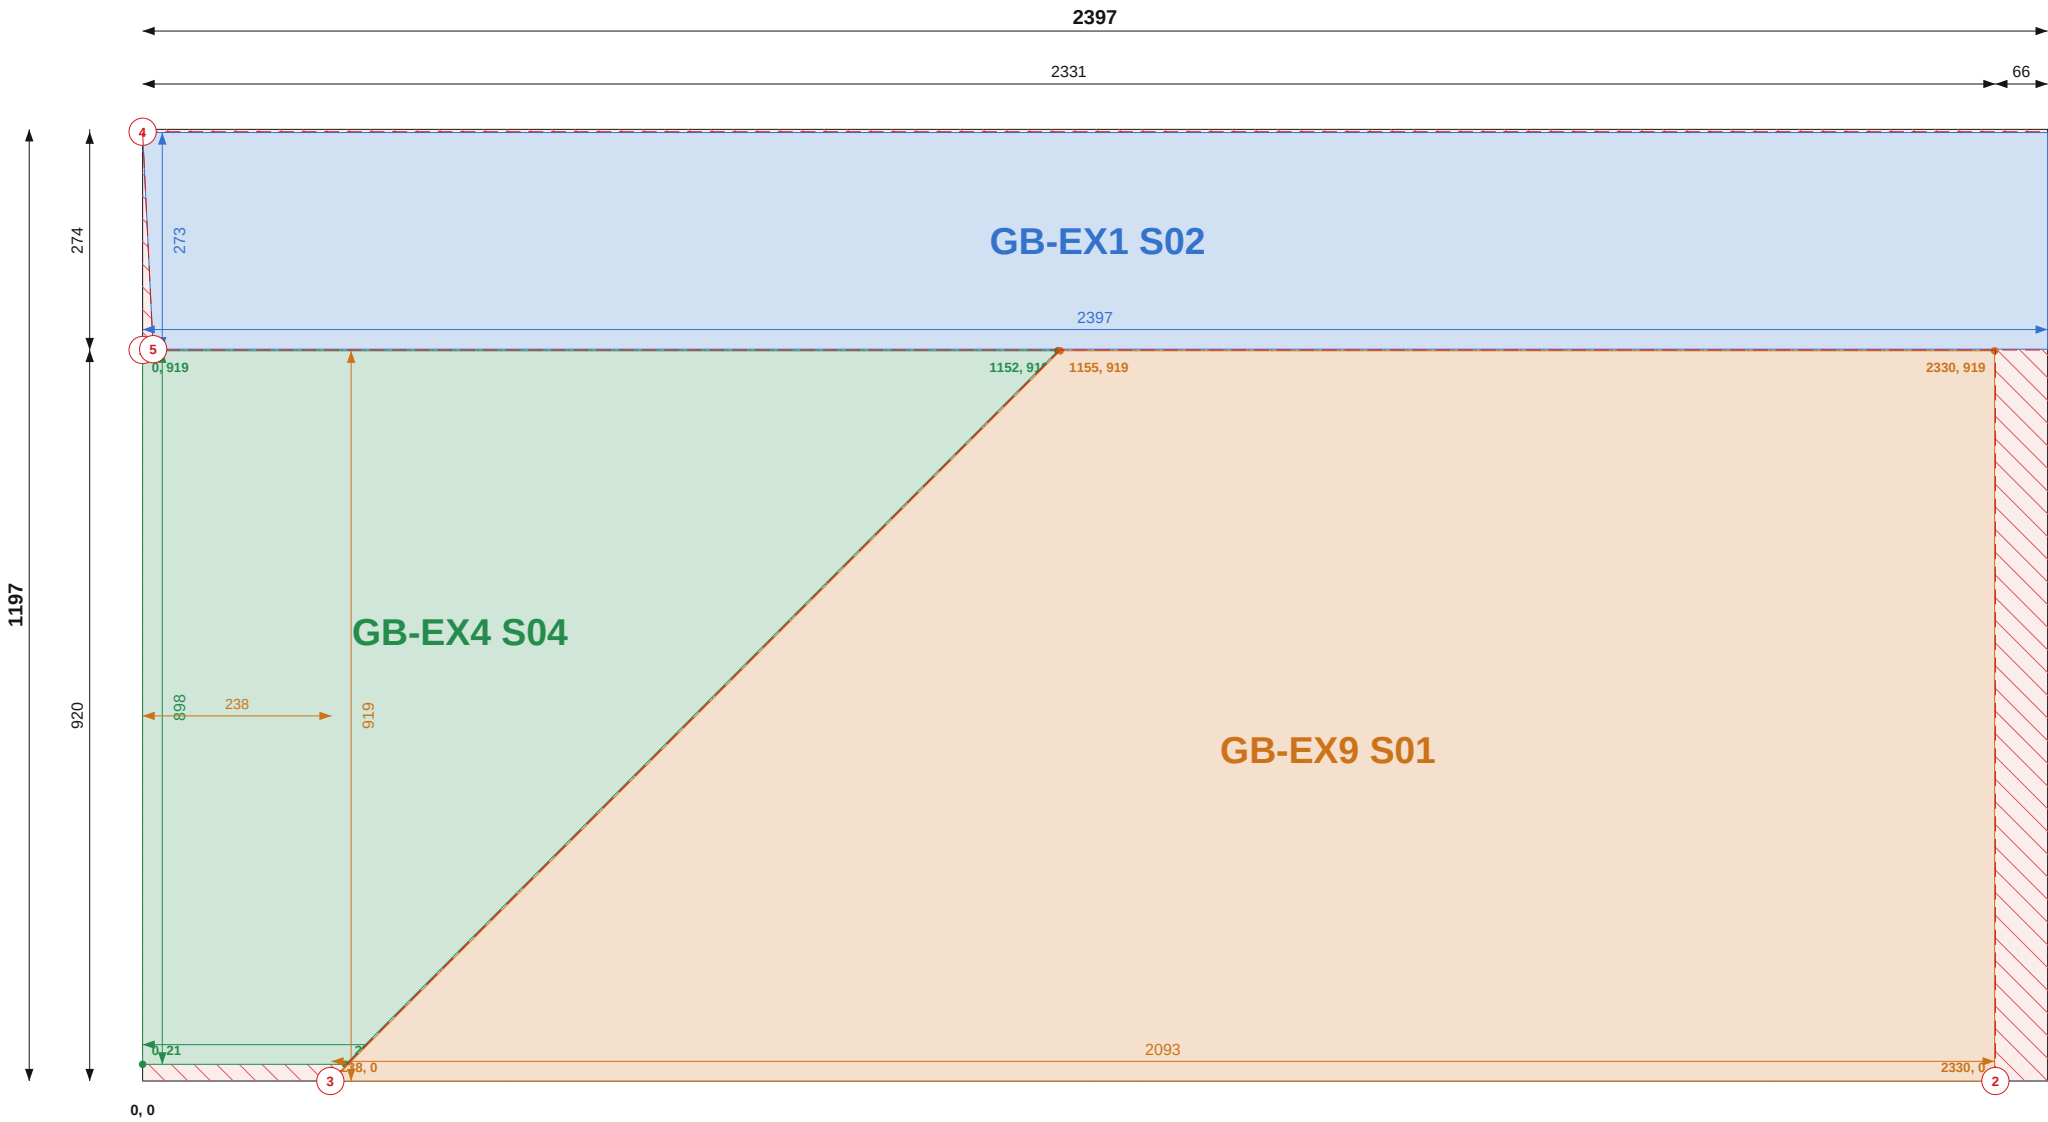

Top / left chains = saw cut positions (to cut centres). Coloured = part size and position.

SHEET 9 OF 14

THIS SHEET

Item	Value
Parts	3
Used / waste	97.0% / 0.09 m2
Reusable offcuts	0
Saw cuts / shared	5 / 3

PIECES (POSITION = BOTTOM-LEFT CORNER)

Label	Size	X, Y
GB-EX1 S02	273 x 2397	0, 921
GB-EX4 S04	898 x 1152 rake to 257	0, 21
GB-EX9 S01	919 x 2093 rake to 1177	238, 0

NOTES

- Cut from OSB/3 9mm 1197x2397, 2mm saw kerf. Viewed on the face; dimensions from the sheet's bottom-left corner (0,0). Red numbered lines = saw cuts in order, each edge to edge.
- Coloured dimensions belong to the part of that colour: its width and height, and its position from the sheet edges. Raked parts: corner coordinates at each corner.
- Red hatch = waste. Labels = panel + piece mark on the manufacture drawing.

REVISIONS

REV	DATE	DESCRIPTION
C01	13.09.26	Construction issue



TLS TIMBER FRAME

Design & Manufacture

Scan: 3D model + drawings



CLIENT	PROJECT
MP Adams	MP Adams Plot 3, Eckington


DRAWING TITLE
OSB CUTTING - GABLES - SHEET 9 OF 14

OSB/3 9mm 1197x2397 | Gables

SCALE	SIZE	DATE	DRAWN
NTS	A3	13.09.26	TS

STATUS	DRAWING No.	REV
CONSTRUCTION	P3-CP-OSB-03 / 09	C01

Do not scale. All dimensions in mm. Check all dimensions on site.

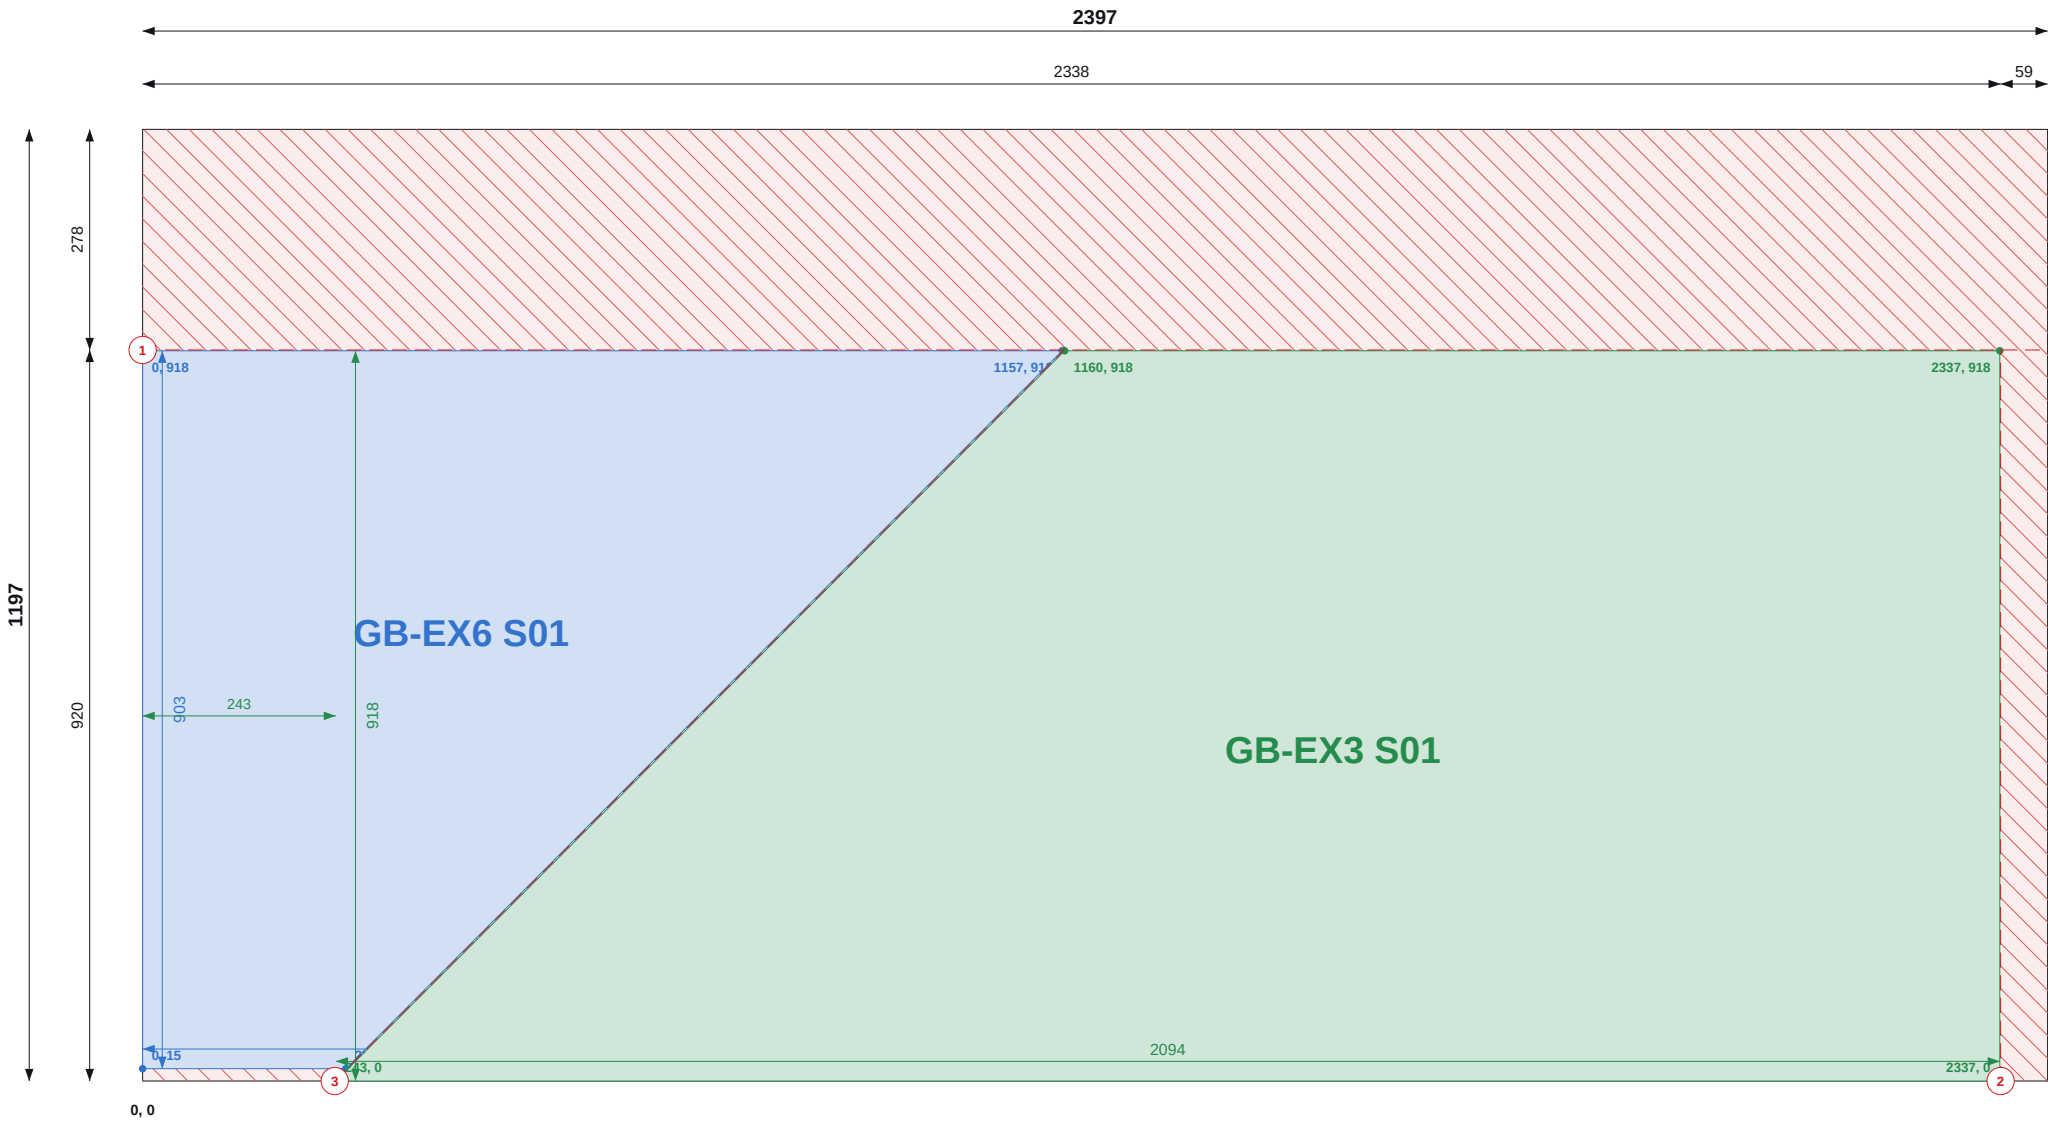

Top / left chains = saw cut positions (to cut centres). Coloured = part size and position.

SHEET 10 OF 14

THIS SHEET

Item	Value
Parts	2
Used / waste	74.6% / 0.73 m2
Reusable offcuts	0
Saw cuts / shared	3 / 1

PIECES (POSITION = BOTTOM-LEFT CORNER)

Label	Size	X, Y
GB-EX6 S01	903 x 1157 rake to 257	0, 15
GB-EX3 S01	918 x 2094 rake to 1178	243, 0

NOTES

- Cut from OSB/3 9mm 1197x2397, 2mm saw kerf. Viewed on the face; dimensions from the sheet's bottom-left corner (0,0). Red numbered lines = saw cuts in order, each edge to edge.
- Coloured dimensions belong to the part of that colour: its width and height, and its position from the sheet edges. Raked parts: corner coordinates at each corner.
- Red hatch = waste. Labels = panel + piece mark on the manufacture drawing.

REVISIONS

REV	DATE	DESCRIPTION
C01	13.09.26	Construction issue



TLS TIMBER FRAME

Design & Manufacture

Scan: 3D model + drawings



CLIENT	PROJECT
MP Adams	MP Adams Plot 3, Eckington

DRAWING TITLE
OSB CUTTING - GABLES - SHEET 10 OF 14

OSB/3 9mm 1197x2397 | Gables

SCALE	SIZE	DATE	DRAWN
NTS	A3	13.09.26	TS

STATUS	DRAWING No.	REV
CONSTRUCTION	P3-CP-OSB-03 / 10	C01

Do not scale. All dimensions in mm. Check all dimensions on site.



Top / left chains = saw cut positions (to cut centres). Coloured = part size and position.

SHEET 12 OF 14

THIS SHEET

Item	Value
Parts	2
Used / waste	95.3% / 0.14 m2
Reusable offcuts	0
Saw cuts / shared	2 / 2

PIECES (POSITION = BOTTOM-LEFT CORNER)

Label	Size	X, Y
GB-EX8 S06	321 x 2397	0, 876
GB-EX8 S04	874 x 2397 rake to 2100	0, 0

NOTES

- Cut from OSB/3 9mm 1197x2397, 2mm saw kerf. Viewed on the face; dimensions from the sheet's bottom-left corner (0,0). Red numbered lines = saw cuts in order, each edge to edge.
- Coloured dimensions belong to the part of that colour: its width and height, and its position from the sheet edges. Raked parts: corner coordinates at each corner.
- Red hatch = waste. Labels = panel + piece mark on the manufacture drawing.

REVISIONS

REV	DATE	DESCRIPTION
C01	13.09.26	Construction issue



TLS TIMBER FRAME

Design & Manufacture

Scan: 3D model + drawings



CLIENT	PROJECT
MP Adams	MP Adams Plot 3, Eckington


DRAWING TITLE
OSB CUTTING - GABLES - SHEET 12 OF 14

OSB/3 9mm 1197x2397 | Gables

SCALE	SIZE	DATE	DRAWN
NTS	A3	13.09.26	TS

STATUS	DRAWING No.	REV
CONSTRUCTION	P3-CP-OSB-03 / 12	C01

Do not scale. All dimensions in mm. Check all dimensions on site.

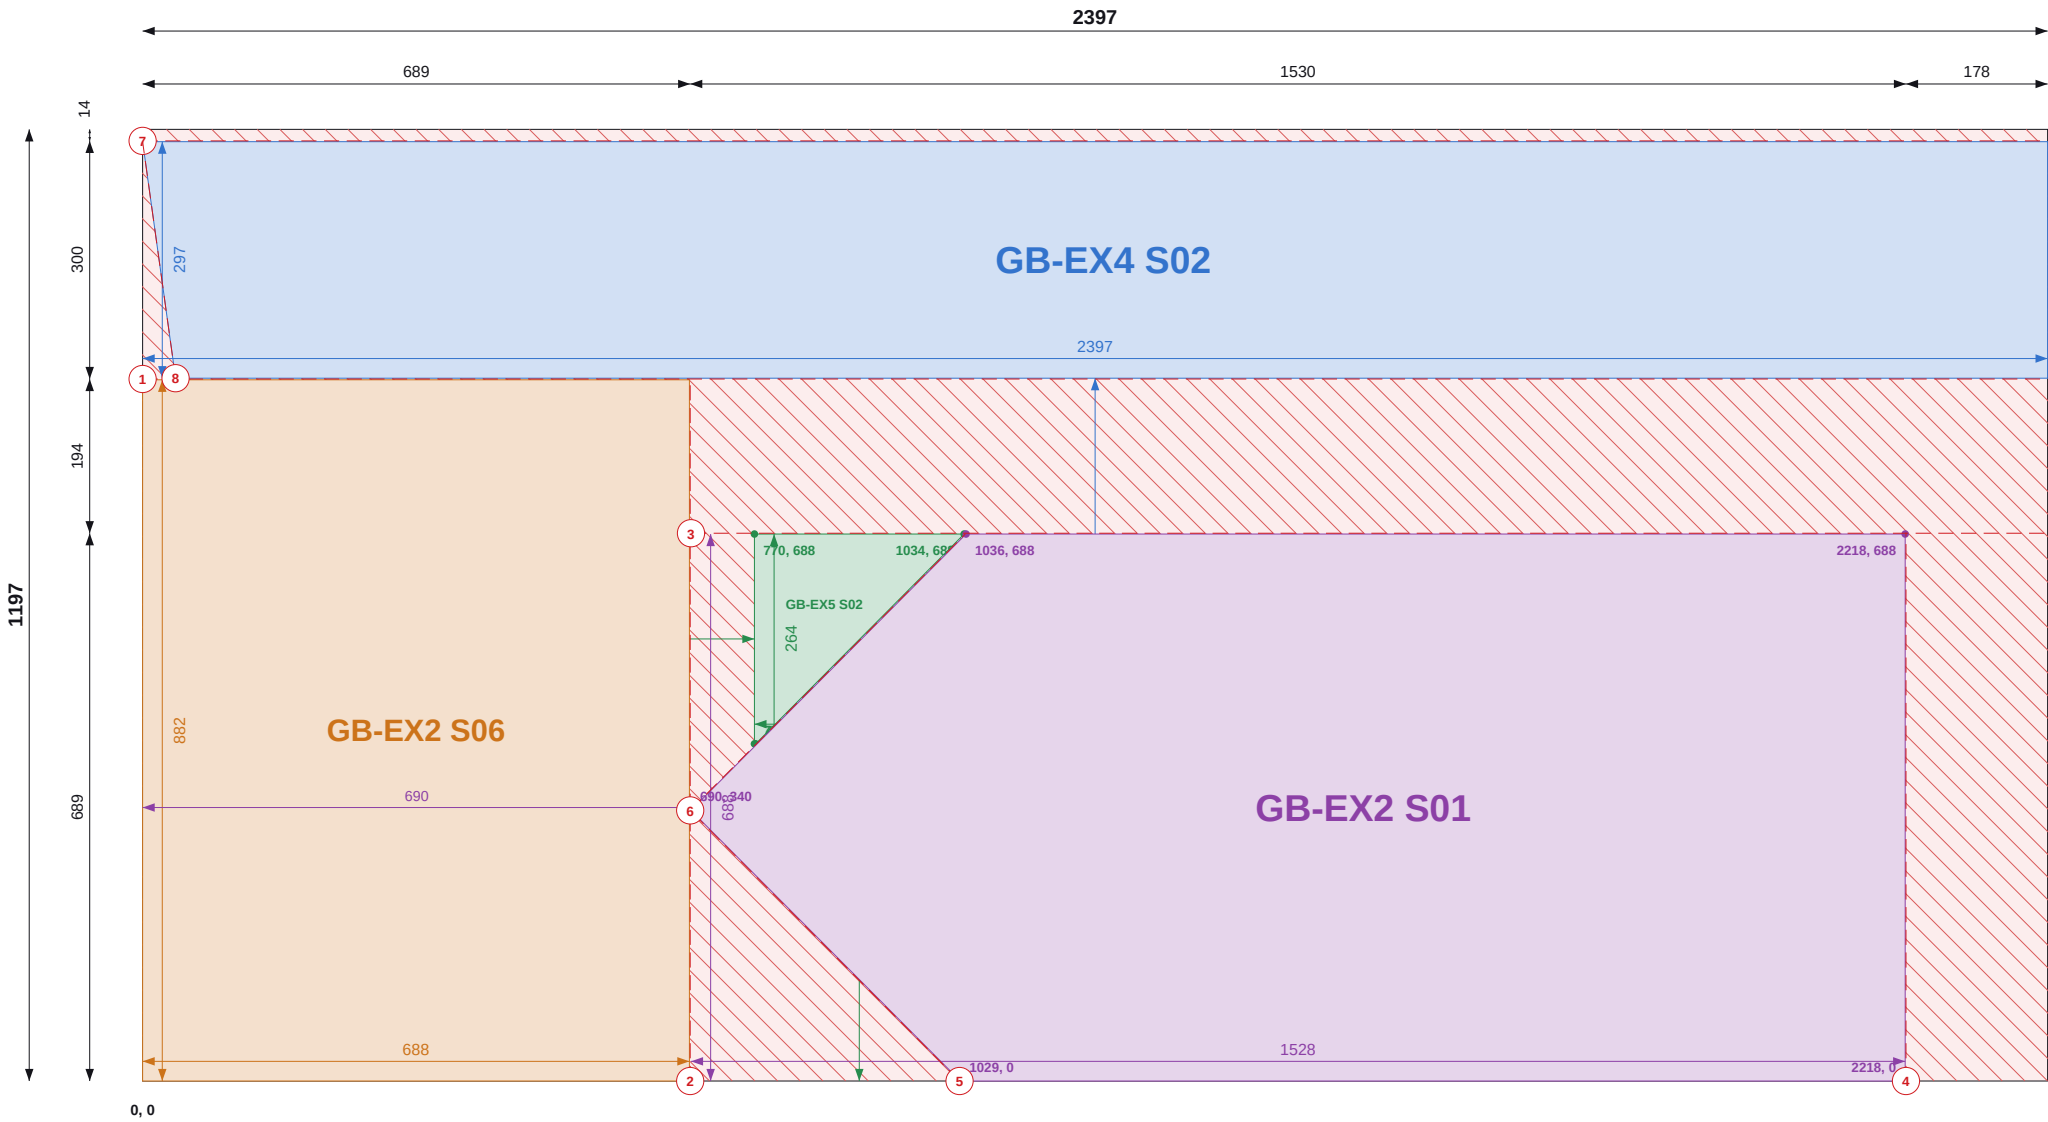

Top / left chains = saw cut positions (to cut centres). Coloured = part size and position.

SHEET 13 OF 14

THIS SHEET

Item	Value
Parts	4
Used / waste	79.5% / 0.59 m2
Reusable offcuts	0
Saw cuts / shared	8 / 5

PIECES (POSITION = BOTTOM-LEFT CORNER)

Label	Size	X, Y
GB-EX4 S02	297 x 2397	0, 884
GB-EX5 S02	264 x 264 rake to 3	770, 424
GB-EX2 S06	688 x 882	0, 0
GB-EX2 S01	688 x 1190 rake to 1183	690, 0

NOTES

1. Cut from OSB/3 9mm 1197x2397, 2mm saw kerf. Viewed on the face; dimensions from the sheet's bottom-left corner (0,0). Red numbered lines = saw cuts in order, each edge to edge.
2. Coloured dimensions belong to the part of that colour: its width and height, and its position from the sheet edges. Raked parts: corner coordinates at each corner.
3. Red hatch = waste. Labels = panel + piece mark on the manufacture drawing.

REVISIONS

REV	DATE	DESCRIPTION
C01	13.09.26	Construction issue



TLS TIMBER FRAME

Design & Manufacture

Scan: 3D model + drawings



CLIENT	PROJECT
MP Adams	MP Adams Plot 3, Eckington


DRAWING TITLE
OSB CUTTING - GABLES - SHEET 13 OF 14

OSB/3 9mm 1197x2397 | Gables

SCALE	SIZE	DATE	DRAWN
NTS	A3	13.09.26	TS

STATUS	DRAWING No.	REV
CONSTRUCTION	P3-CP-OSB-03 / 13	C01

Do not scale. All dimensions in mm. Check all dimensions on site.

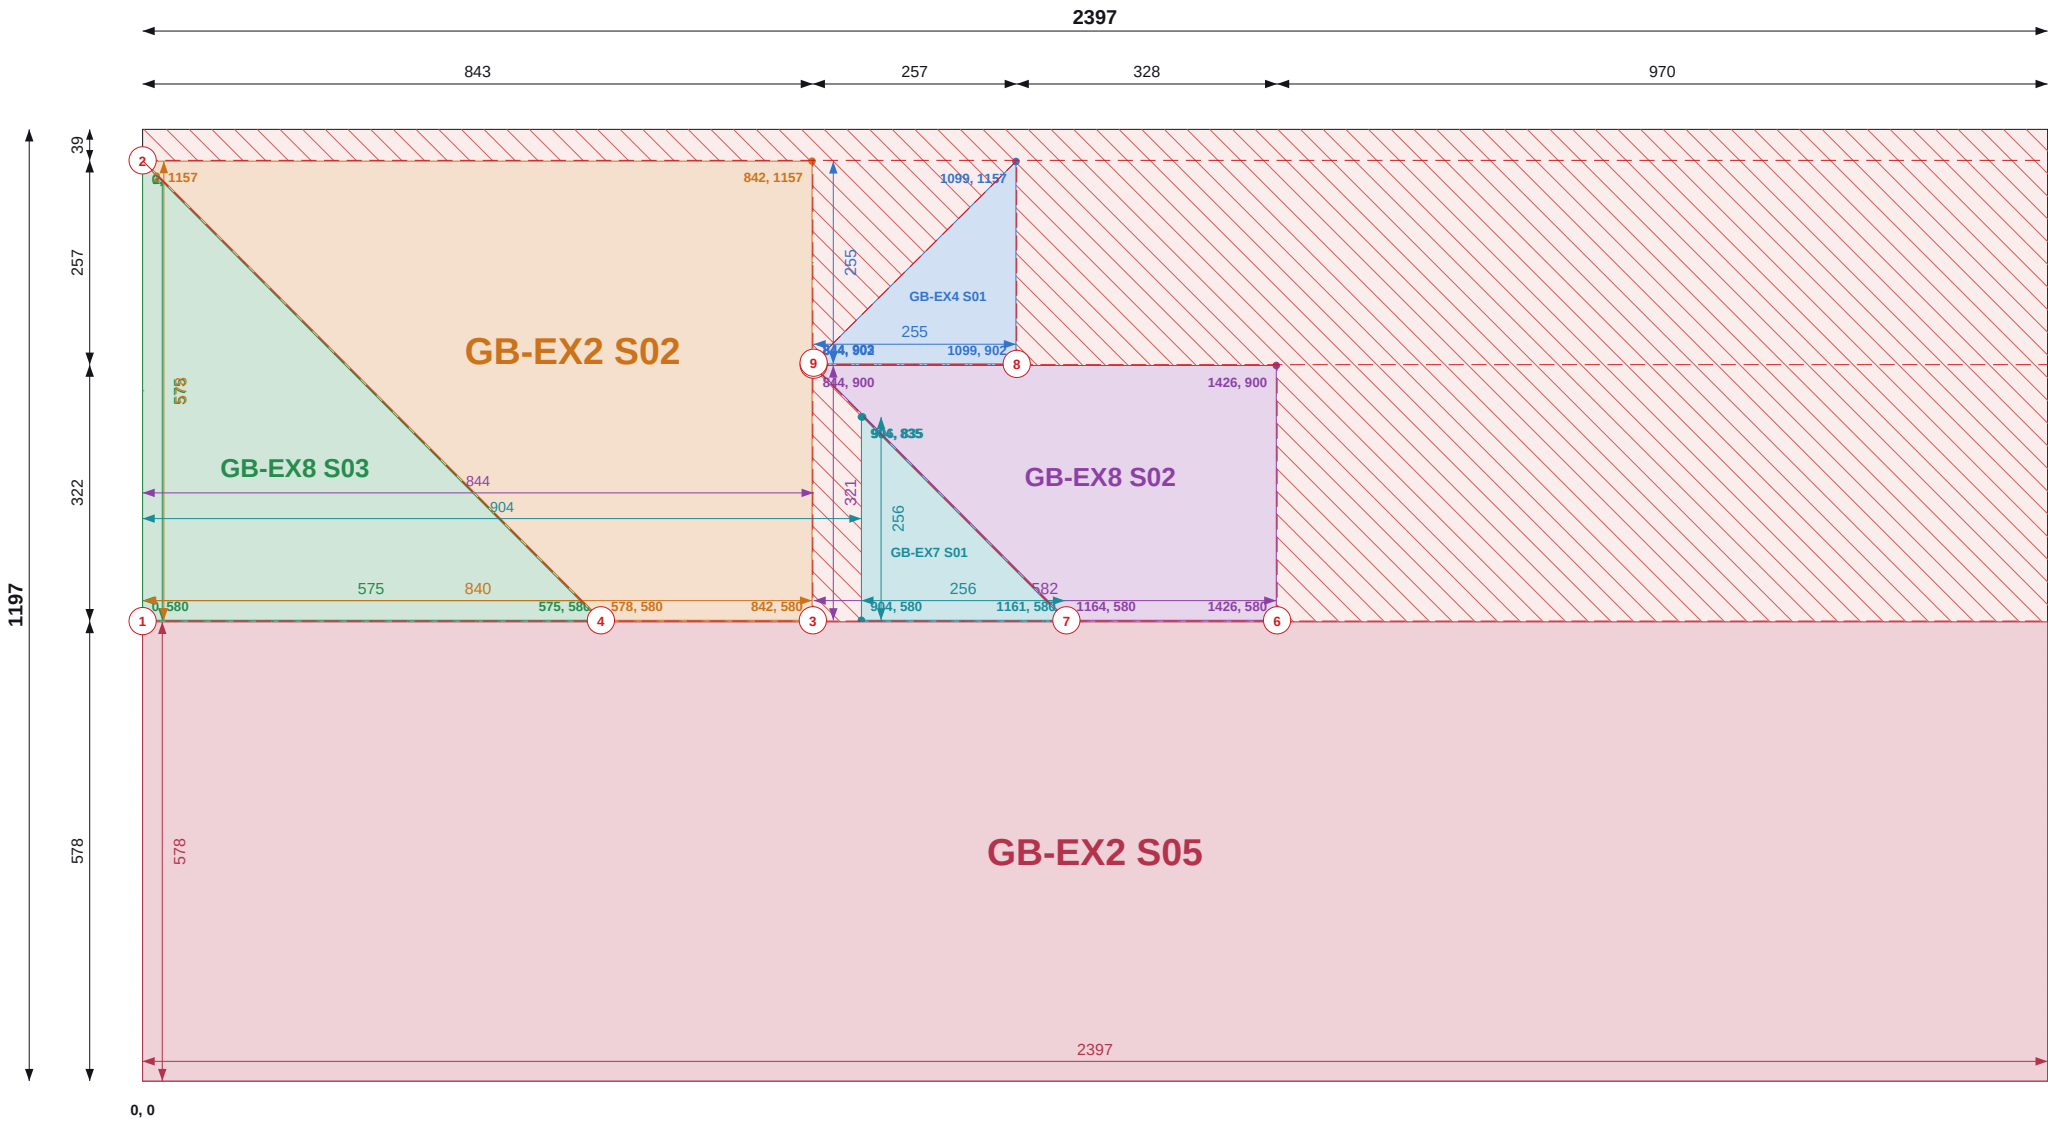

Top / left chains = saw cut positions (to cut centres). Coloured = part size and position.

SHEET 14 OF 14

THIS SHEET

Item	Value
Parts	6
Used / waste	72.1% / 0.80 m2
Reusable offcuts	1
Saw cuts / shared	9 / 6

PIECES (POSITION = BOTTOM-LEFT CORNER)

Label	Size	X, Y
GB-EX4 S01	255 x 255 rake to 3	844, 902
GB-EX8 S03	575 x 575 rake to 3	0, 580
GB-EX2 S02	578 x 840 rake to 265	2, 580
GB-EX8 S02	321 x 582 rake to 264	844, 580
GB-EX7 S01	256 x 256 rake to 3	904, 580
GB-EX2 S05	578 x 2397	0, 0

NOTES

- Cut from OSB/3 9mm 1197x2397, 2mm saw kerf. Viewed on the face; dimensions from the sheet's bottom-left corner (0,0). Red numbered lines = saw cuts in order, each edge to edge.
- Coloured dimensions belong to the part of that colour: its width and height, and its position from the sheet edges. Raked parts: corner coordinates at each corner.
- Red hatch = waste. Labels = panel + piece mark on the manufacture drawing.

REVISIONS

REV	DATE	DESCRIPTION
C01	13.09.26	Construction issue



TLS TIMBER FRAME

Design & Manufacture

Scan: 3D model + drawings



CLIENT	PROJECT
MP Adams	MP Adams Plot 3, Eckington

DRAWING TITLE
OSB CUTTING - GABLES - SHEET 14 OF 14

OSB/3 9mm 1197x2397 | Gables

SCALE	SIZE	DATE	DRAWN
NTS	A3	13.09.26	TS

STATUS	DRAWING No.	REV
CONSTRUCTION	P3-CP-OSB-03 / 14	C01