


Do not scale. All dimensions in mm. Check all dimensions on site.

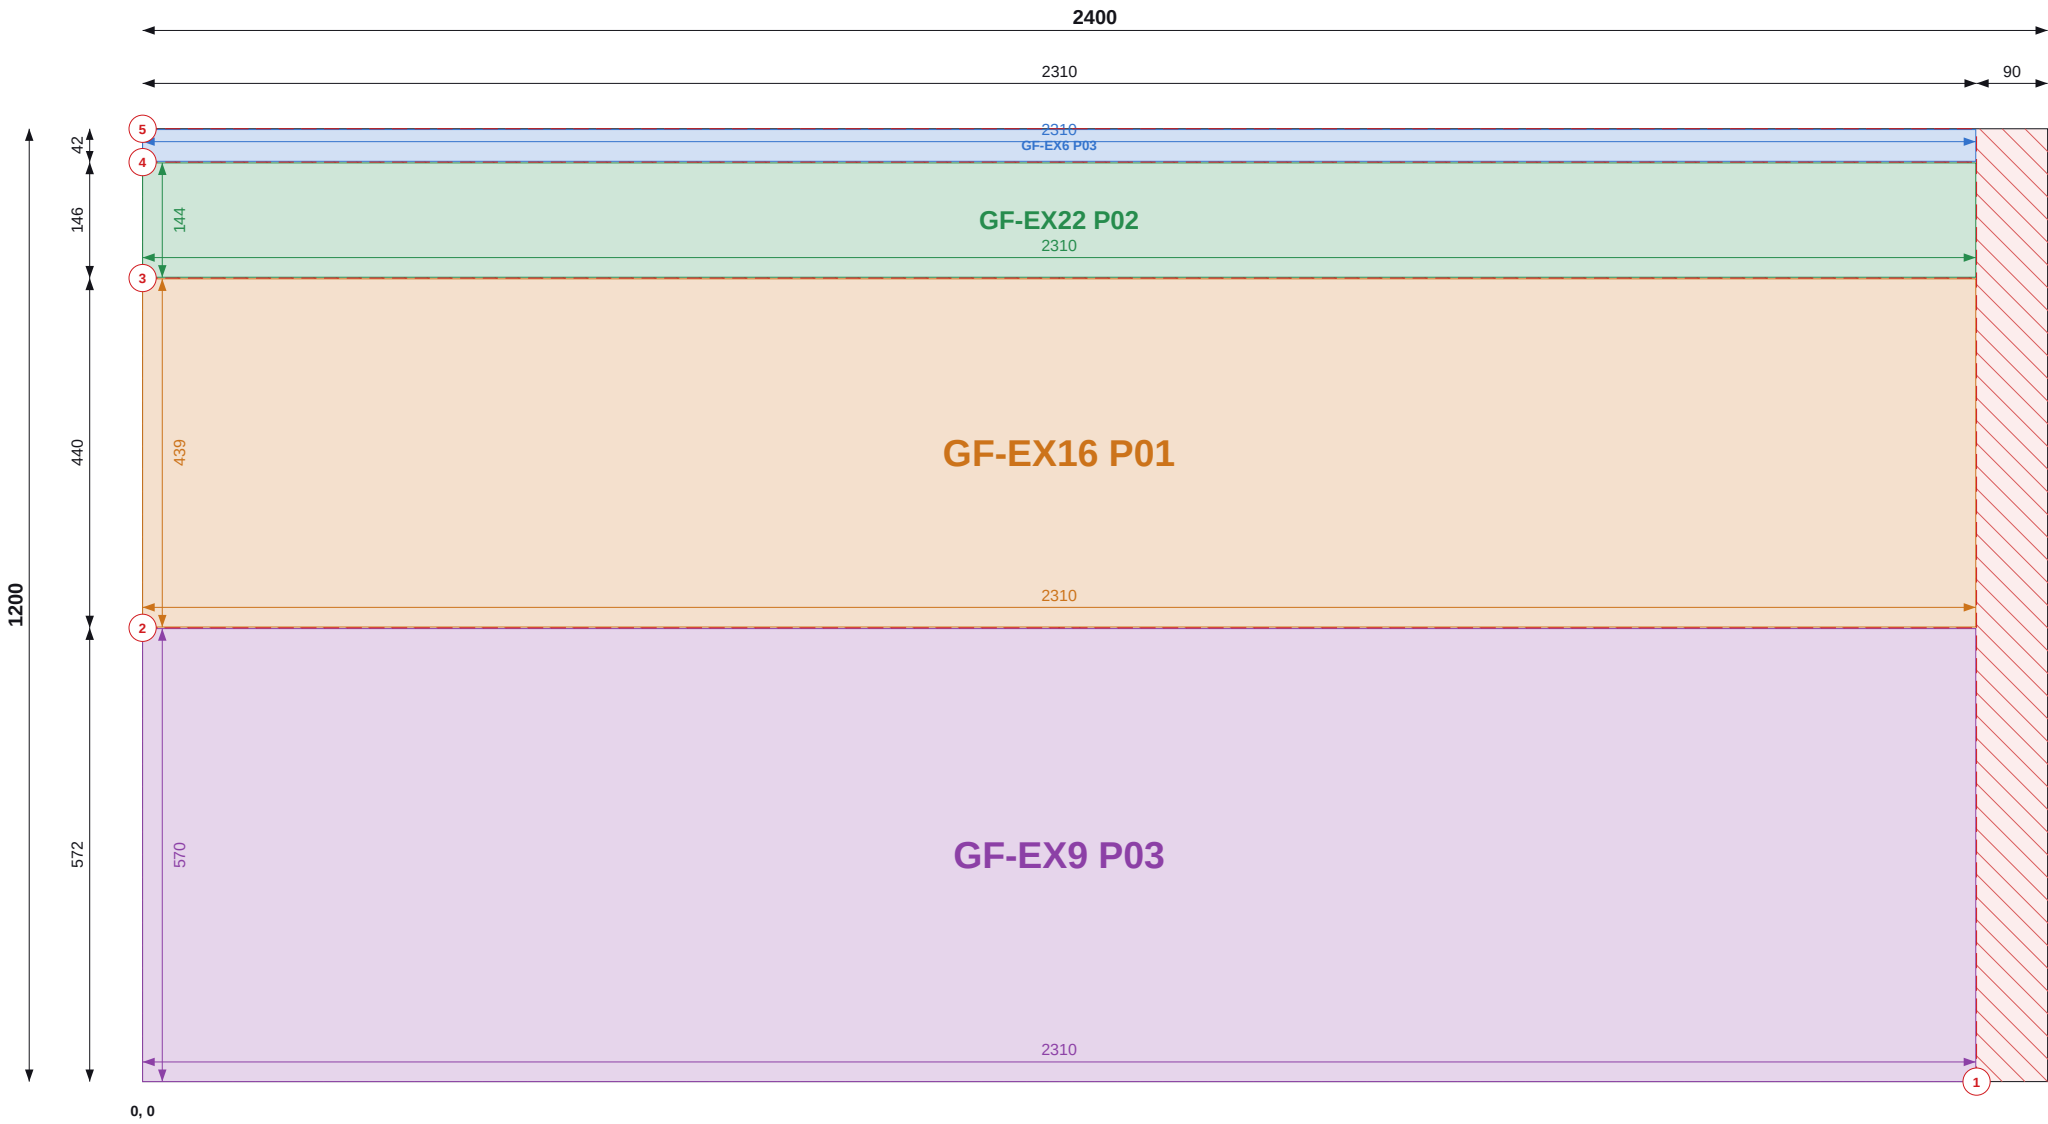

Top / left chains = saw cut positions (to cut centres). Coloured = part size and position.

SHEET 1 OF 21

THIS SHEET

| Item              | Value           |
|-------------------|-----------------|
| Parts             | 4               |
| Used / waste      | 95.7% / 0.12 m2 |
| Reusable offcuts  | 0               |
| Saw cuts / shared | 5 / 3           |

PIECES (POSITION = BOTTOM-LEFT CORNER)

| Label       | Size       | X, Y    |
|-------------|------------|---------|
| GF-EX6 P03  | 40 x 2310  | 0, 1159 |
| GF-EX22 P02 | 144 x 2310 | 0, 1013 |
| GF-EX16 P01 | 439 x 2310 | 0, 572  |
| GF-EX9 P03  | 570 x 2310 | 0, 0    |

GROUND FLOOR TOTALS

| Item                              | Value           |
|-----------------------------------|-----------------|
| Sheets / pieces                   | 21 / 154        |
| Yield / waste                     | 90.8% / 5.55 m2 |
| Saw cuts / shared / on stock edge | 187 / 133 / 111 |

NOTES

- Cut from PIR 120mm 1200x2400, 2mm saw kerf. Viewed on the face; dimensions from the sheet's bottom-left corner (0,0). Red numbered lines = saw cuts in order, each edge to edge.
- Coloured dimensions belong to the part of that colour: its width and height, and its position from the sheet edges. Raked parts: corner coordinates at each corner.
- Red hatch = waste. Labels = panel + piece mark on the manufacture drawing.

REVISIONS

| REV | DATE     | DESCRIPTION        |
|-----|----------|--------------------|
| C01 | 13.09.26 | Construction issue |



TLS  
TIMBER FRAME DESIGN SUITE

TLS TIMBER FRAME

Design & Manufacture

Scan: 3D model + drawings




|          |                            |
|----------|----------------------------|
| CLIENT   | PROJECT                    |
| MP Adams | MP Adams Plot 3, Eckington |

|                                            |  |  |  |
|--------------------------------------------|--|--|--|
| DRAWING TITLE                              |  |  |  |
| PIR CUTTING - GROUND FLOOR - SHEET 1 OF 21 |  |  |  |
| PIR 120mm 1200x2400   Ground Floor         |  |  |  |

|       |      |          |       |
|-------|------|----------|-------|
| SCALE | SIZE | DATE     | DRAWN |
| NTS   | A3   | 13.09.26 | TS    |

|              |                   |     |
|--------------|-------------------|-----|
| STATUS       | DRAWING No.       | REV |
| CONSTRUCTION | P3-CP-PIR-01 / 01 | C01 |

Do not scale. All dimensions in mm. Check all dimensions on site.

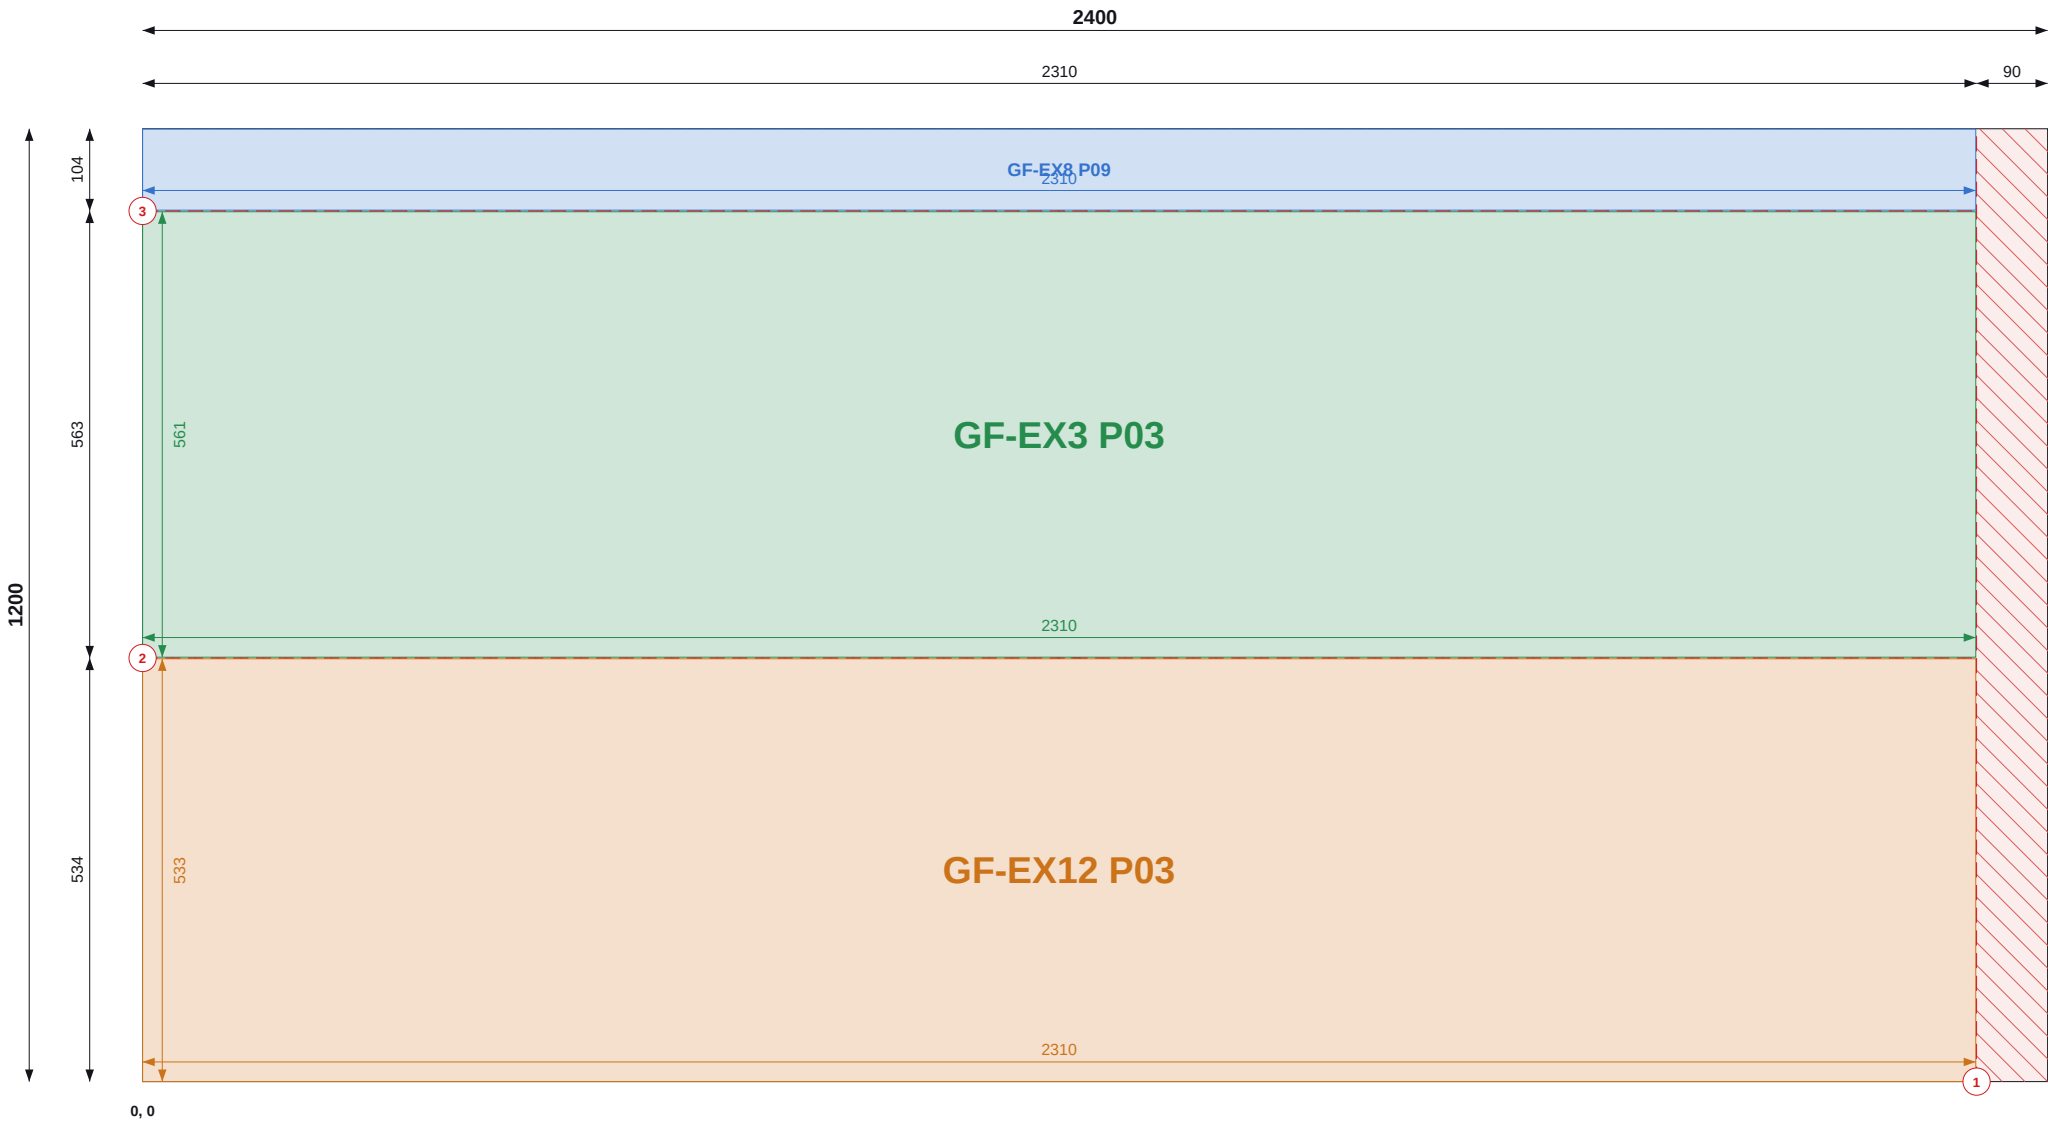

Top / left chains = saw cut positions (to cut centres). Coloured = part size and position.

SHEET 2 OF 21

THIS SHEET

| Item              | Value           |
|-------------------|-----------------|
| Parts             | 3               |
| Used / waste      | 95.9% / 0.12 m2 |
| Reusable offcuts  | 0               |
| Saw cuts / shared | 3 / 2           |

PIECES (POSITION = BOTTOM-LEFT CORNER)

| Label       | Size       | X, Y    |
|-------------|------------|---------|
| GF-EX8 P09  | 102 x 2310 | 0, 1098 |
| GF-EX3 P03  | 561 x 2310 | 0, 535  |
| GF-EX12 P03 | 533 x 2310 | 0, 0    |

NOTES

- Cut from PIR 120mm 1200x2400, 2mm saw kerf. Viewed on the face; dimensions from the sheet's bottom-left corner (0,0). Red numbered lines = saw cuts in order, each edge to edge.
- Coloured dimensions belong to the part of that colour: its width and height, and its position from the sheet edges. Raked parts: corner coordinates at each corner.
- Red hatch = waste. Labels = panel + piece mark on the manufacture drawing.

REVISIONS

| REV | DATE     | DESCRIPTION        |
|-----|----------|--------------------|
| C01 | 13.09.26 | Construction issue |



TLS TIMBER FRAME

Design & Manufacture

Scan: 3D model + drawings



|          |                            |
|----------|----------------------------|
| CLIENT   | PROJECT                    |
| MP Adams | MP Adams Plot 3, Eckington |


DRAWING TITLE  
**PIR CUTTING - GROUND FLOOR - SHEET 2 OF 21**

PIR 120mm 1200x2400 | Ground Floor

|       |      |          |       |
|-------|------|----------|-------|
| SCALE | SIZE | DATE     | DRAWN |
| NTS   | A3   | 13.09.26 | TS    |

|              |                          |            |
|--------------|--------------------------|------------|
| STATUS       | DRAWING No.              | REV        |
| CONSTRUCTION | <b>P3-CP-PIR-01 / 02</b> | <b>C01</b> |

Do not scale. All dimensions in mm. Check all dimensions on site.

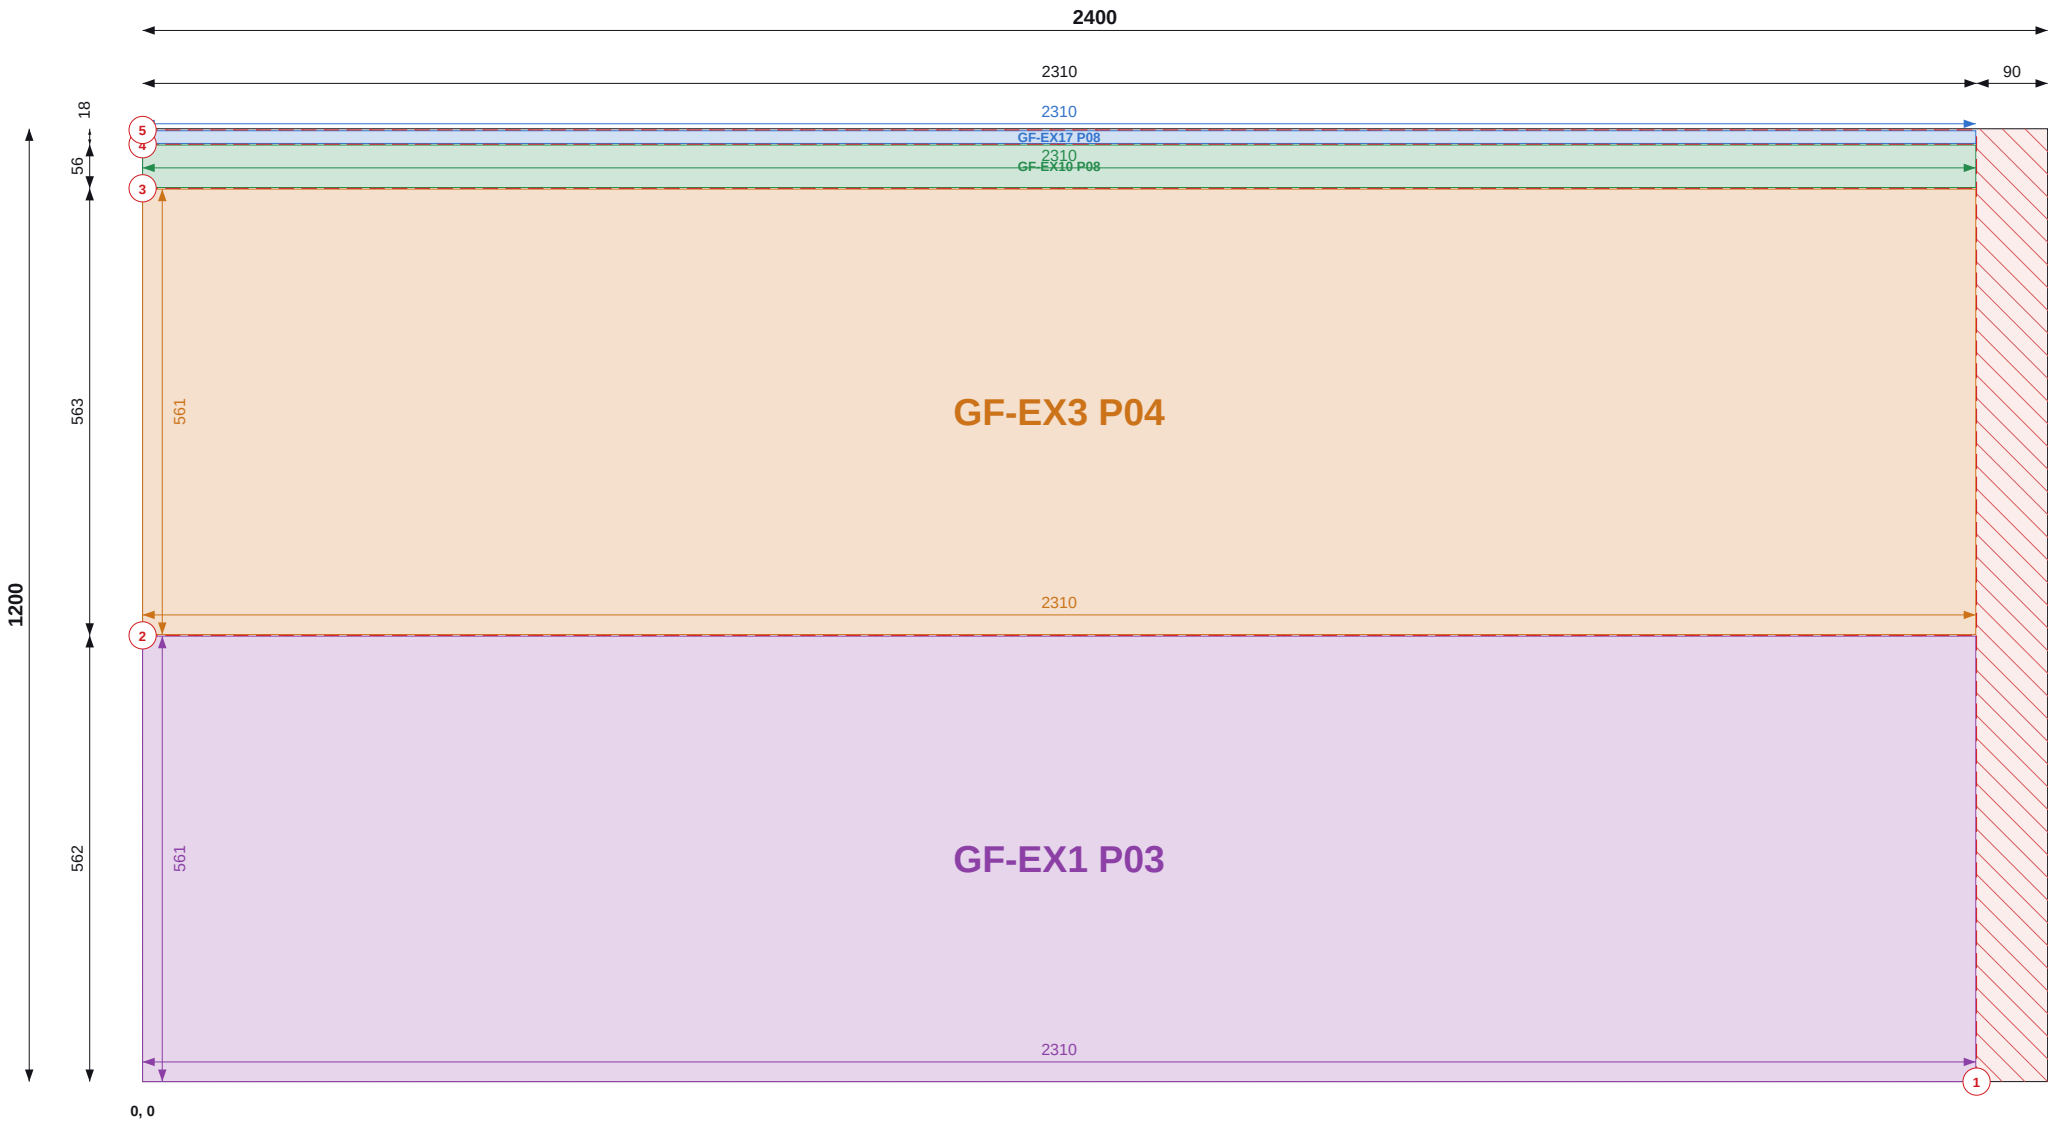

Top / left chains = saw cut positions (to cut centres). Coloured = part size and position.

SHEET 3 OF 21

THIS SHEET

| Item              | Value           |
|-------------------|-----------------|
| Parts             | 4               |
| Used / waste      | 95.5% / 0.13 m2 |
| Reusable offcuts  | 0               |
| Saw cuts / shared | 5 / 3           |

PIECES (POSITION = BOTTOM-LEFT CORNER)

| Label       | Size       | X, Y    |
|-------------|------------|---------|
| GF-EX17 P08 | 16 x 2310  | 0, 1181 |
| GF-EX10 P08 | 53 x 2310  | 0, 1126 |
| GF-EX3 P04  | 561 x 2310 | 0, 563  |
| GF-EX1 P03  | 561 x 2310 | 0, 0    |

NOTES

- Cut from PIR 120mm 1200x2400, 2mm saw kerf. Viewed on the face; dimensions from the sheet's bottom-left corner (0,0). Red numbered lines = saw cuts in order, each edge to edge.
- Coloured dimensions belong to the part of that colour: its width and height, and its position from the sheet edges. Raked parts: corner coordinates at each corner.
- Red hatch = waste. Labels = panel + piece mark on the manufacture drawing.

REVISIONS

| REV | DATE     | DESCRIPTION        |
|-----|----------|--------------------|
| C01 | 13.09.26 | Construction issue |



TLS TIMBER FRAME  
Design & Manufacture  
Scan: 3D model + drawings



|                    |                                       |
|--------------------|---------------------------------------|
| CLIENT<br>MP Adams | PROJECT<br>MP Adams Plot 3, Eckington |
|--------------------|---------------------------------------|


DRAWING TITLE  
**PIR CUTTING - GROUND FLOOR - SHEET 3 OF 21**

PIR 120mm 1200x2400 | Ground Floor

|              |            |                  |             |
|--------------|------------|------------------|-------------|
| SCALE<br>NTS | SIZE<br>A3 | DATE<br>13.09.26 | DRAWN<br>TS |
|--------------|------------|------------------|-------------|

|                               |                                         |                   |
|-------------------------------|-----------------------------------------|-------------------|
| STATUS<br><b>CONSTRUCTION</b> | DRAWING No.<br><b>P3-CP-PIR-01 / 03</b> | REV<br><b>C01</b> |
|-------------------------------|-----------------------------------------|-------------------|

Do not scale. All dimensions in mm. Check all dimensions on site.

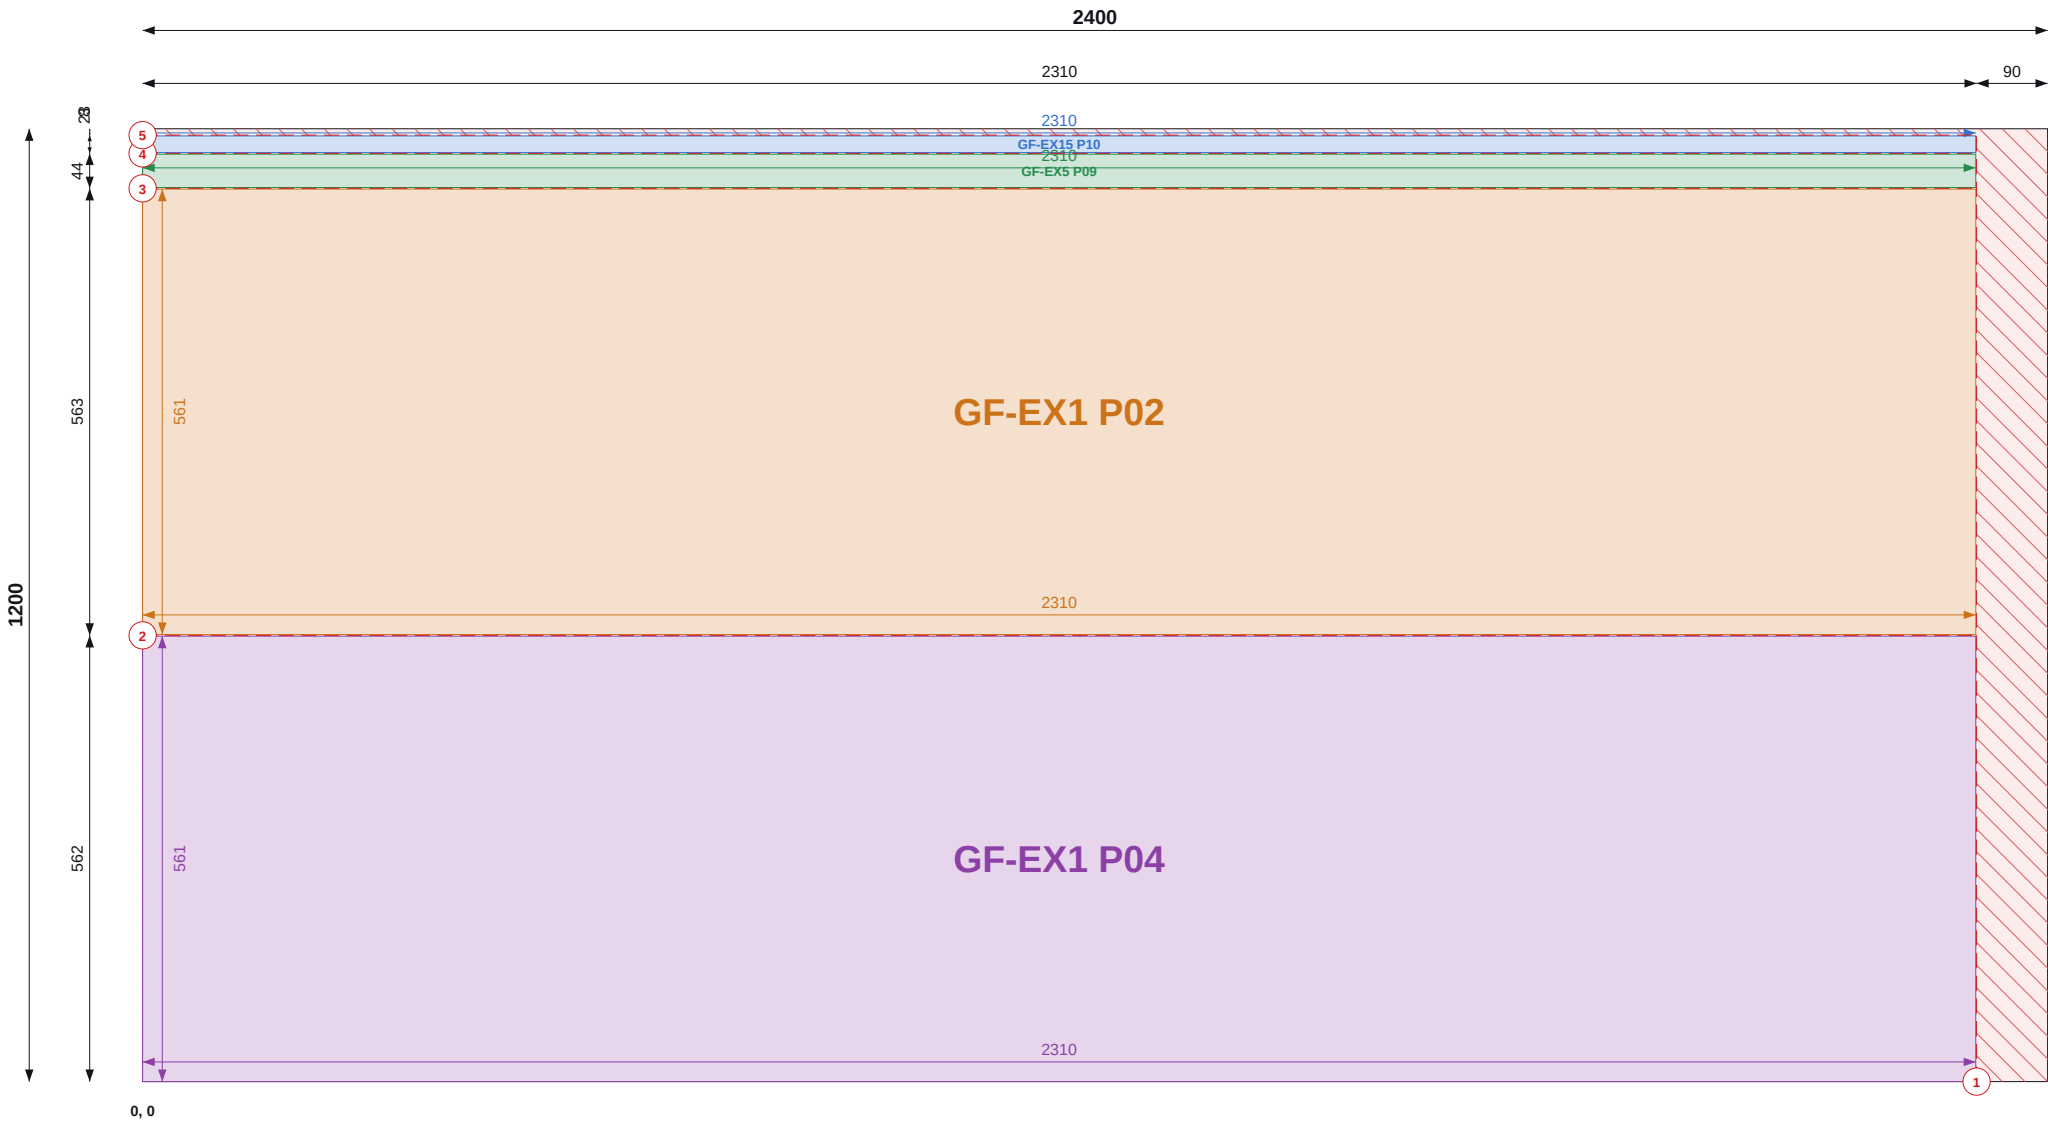

Top / left chains = saw cut positions (to cut centres). Coloured = part size and position.

SHEET 4 OF 21

THIS SHEET

| Item              | Value           |
|-------------------|-----------------|
| Parts             | 4               |
| Used / waste      | 95.0% / 0.14 m2 |
| Reusable offcuts  | 0               |
| Saw cuts / shared | 5 / 3           |

PIECES (POSITION = BOTTOM-LEFT CORNER)

| Label       | Size       | X, Y    |
|-------------|------------|---------|
| GF-EX15 P10 | 21 x 2310  | 0, 1170 |
| GF-EX5 P09  | 42 x 2310  | 0, 1126 |
| GF-EX1 P02  | 561 x 2310 | 0, 563  |
| GF-EX1 P04  | 561 x 2310 | 0, 0    |

NOTES

- Cut from PIR 120mm 1200x2400, 2mm saw kerf. Viewed on the face; dimensions from the sheet's bottom-left corner (0,0). Red numbered lines = saw cuts in order, each edge to edge.
- Coloured dimensions belong to the part of that colour: its width and height, and its position from the sheet edges. Raked parts: corner coordinates at each corner.
- Red hatch = waste. Labels = panel + piece mark on the manufacture drawing.

REVISIONS

| REV | DATE     | DESCRIPTION        |
|-----|----------|--------------------|
| C01 | 13.09.26 | Construction issue |



TLS TIMBER FRAME

Design & Manufacture

Scan: 3D model + drawings



|          |                            |
|----------|----------------------------|
| CLIENT   | PROJECT                    |
| MP Adams | MP Adams Plot 3, Eckington |


|                                            |
|--------------------------------------------|
| DRAWING TITLE                              |
| PIR CUTTING - GROUND FLOOR - SHEET 4 OF 21 |

PIR 120mm 1200x2400 | Ground Floor

|       |      |          |       |
|-------|------|----------|-------|
| SCALE | SIZE | DATE     | DRAWN |
| NTS   | A3   | 13.09.26 | TS    |

|              |                   |     |
|--------------|-------------------|-----|
| STATUS       | DRAWING No.       | REV |
| CONSTRUCTION | P3-CP-PIR-01 / 04 | C01 |

Do not scale. All dimensions in mm. Check all dimensions on site.

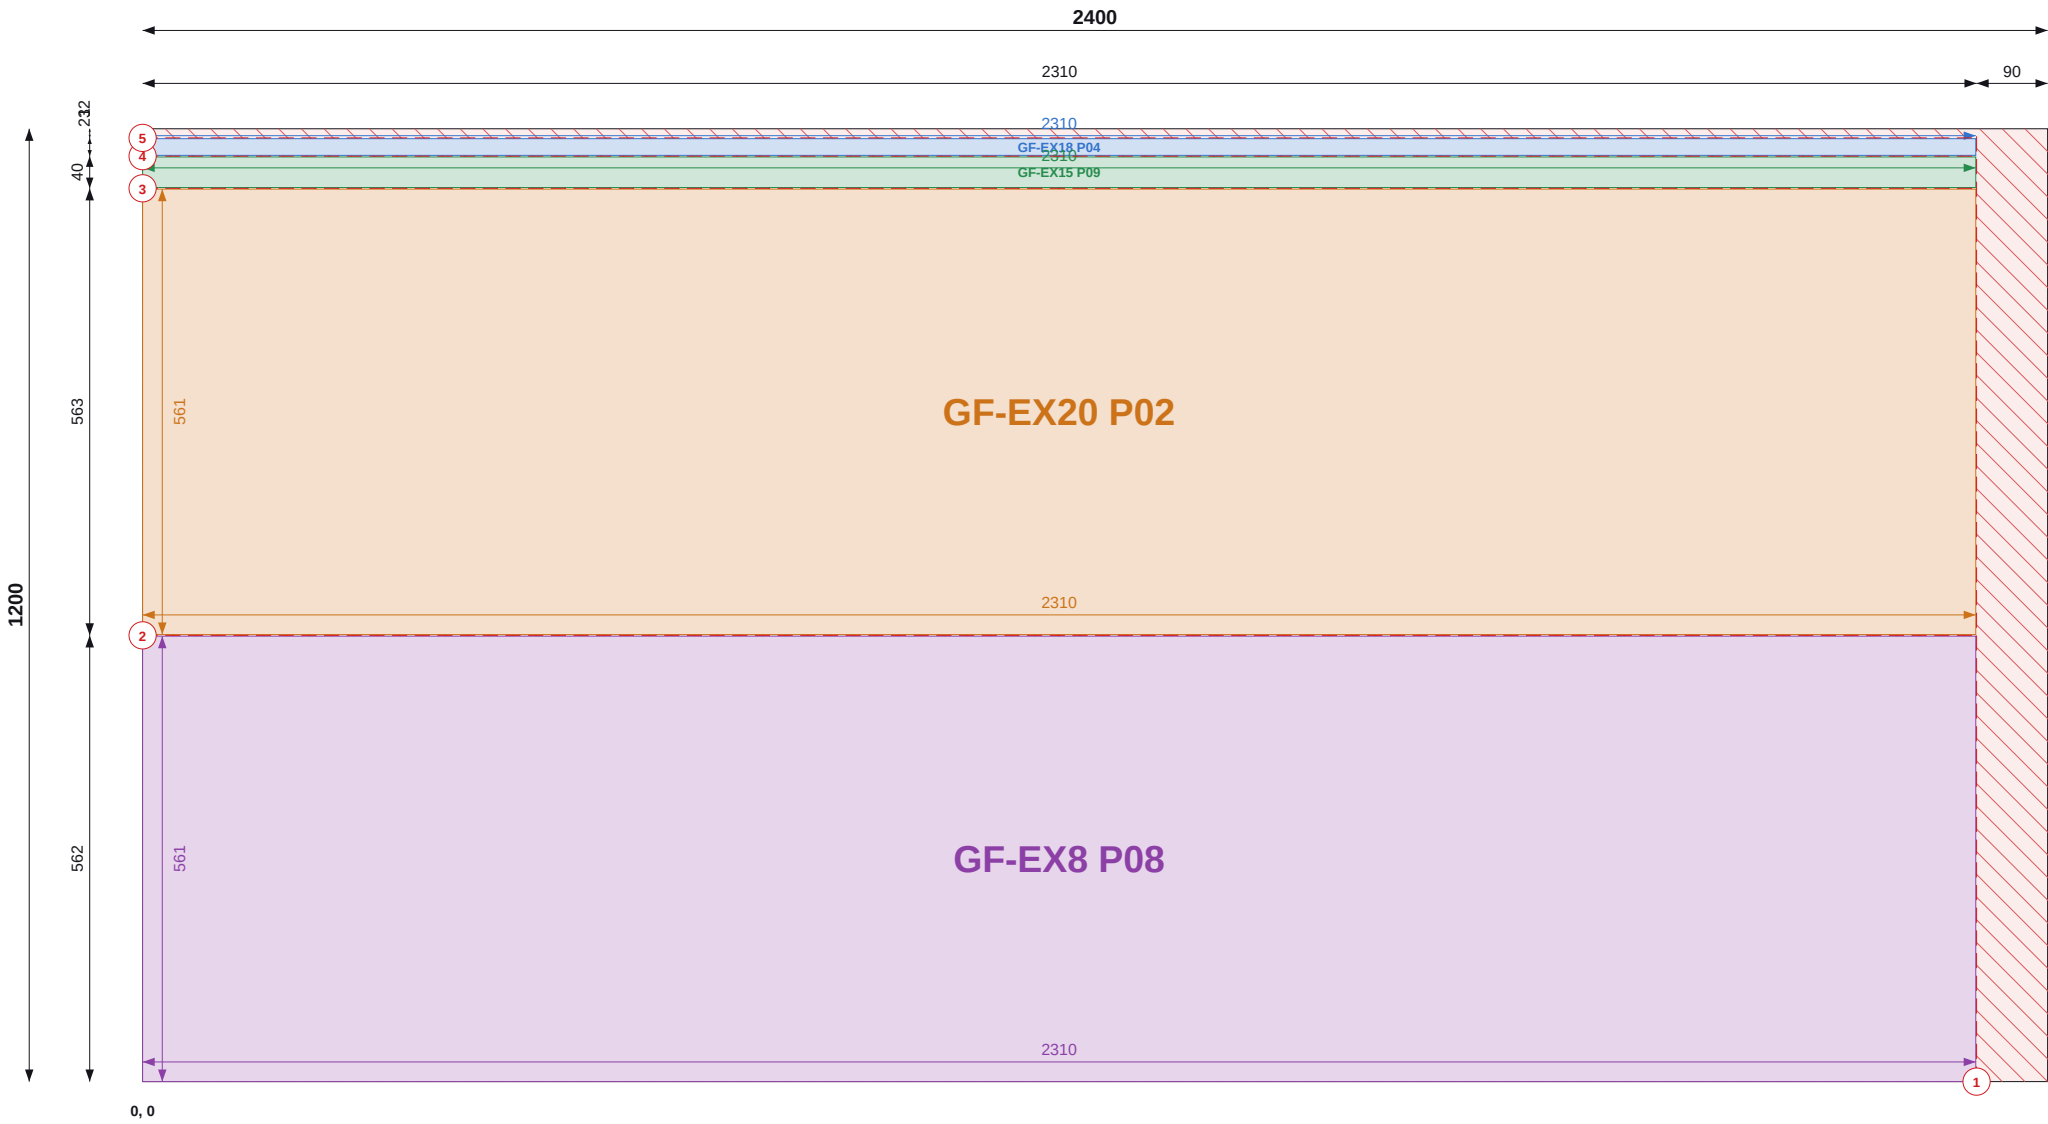

Top / left chains = saw cut positions (to cut centres). Coloured = part size and position.

SHEET 5 OF 21

THIS SHEET

| Item              | Value           |
|-------------------|-----------------|
| Parts             | 4               |
| Used / waste      | 94.7% / 0.15 m2 |
| Reusable offcuts  | 0               |
| Saw cuts / shared | 5 / 3           |

PIECES (POSITION = BOTTOM-LEFT CORNER)

| Label       | Size       | X, Y    |
|-------------|------------|---------|
| GF-EX18 P04 | 21 x 2310  | 0, 1166 |
| GF-EX15 P09 | 38 x 2310  | 0, 1126 |
| GF-EX20 P02 | 561 x 2310 | 0, 563  |
| GF-EX8 P08  | 561 x 2310 | 0, 0    |

NOTES

- Cut from PIR 120mm 1200x2400, 2mm saw kerf. Viewed on the face; dimensions from the sheet's bottom-left corner (0,0). Red numbered lines = saw cuts in order, each edge to edge.
- Coloured dimensions belong to the part of that colour: its width and height, and its position from the sheet edges. Raked parts: corner coordinates at each corner.
- Red hatch = waste. Labels = panel + piece mark on the manufacture drawing.

REVISIONS

| REV | DATE     | DESCRIPTION        |
|-----|----------|--------------------|
| C01 | 13.09.26 | Construction issue |



TLS TIMBER FRAME

Design & Manufacture

Scan: 3D model + drawings



|          |                            |
|----------|----------------------------|
| CLIENT   | PROJECT                    |
| MP Adams | MP Adams Plot 3, Eckington |


|                                            |
|--------------------------------------------|
| DRAWING TITLE                              |
| PIR CUTTING - GROUND FLOOR - SHEET 5 OF 21 |

PIR 120mm 1200x2400 | Ground Floor

|       |      |          |       |
|-------|------|----------|-------|
| SCALE | SIZE | DATE     | DRAWN |
| NTS   | A3   | 13.09.26 | TS    |

|              |                   |     |
|--------------|-------------------|-----|
| STATUS       | DRAWING No.       | REV |
| CONSTRUCTION | P3-CP-PIR-01 / 05 | C01 |

Do not scale. All dimensions in mm. Check all dimensions on site.

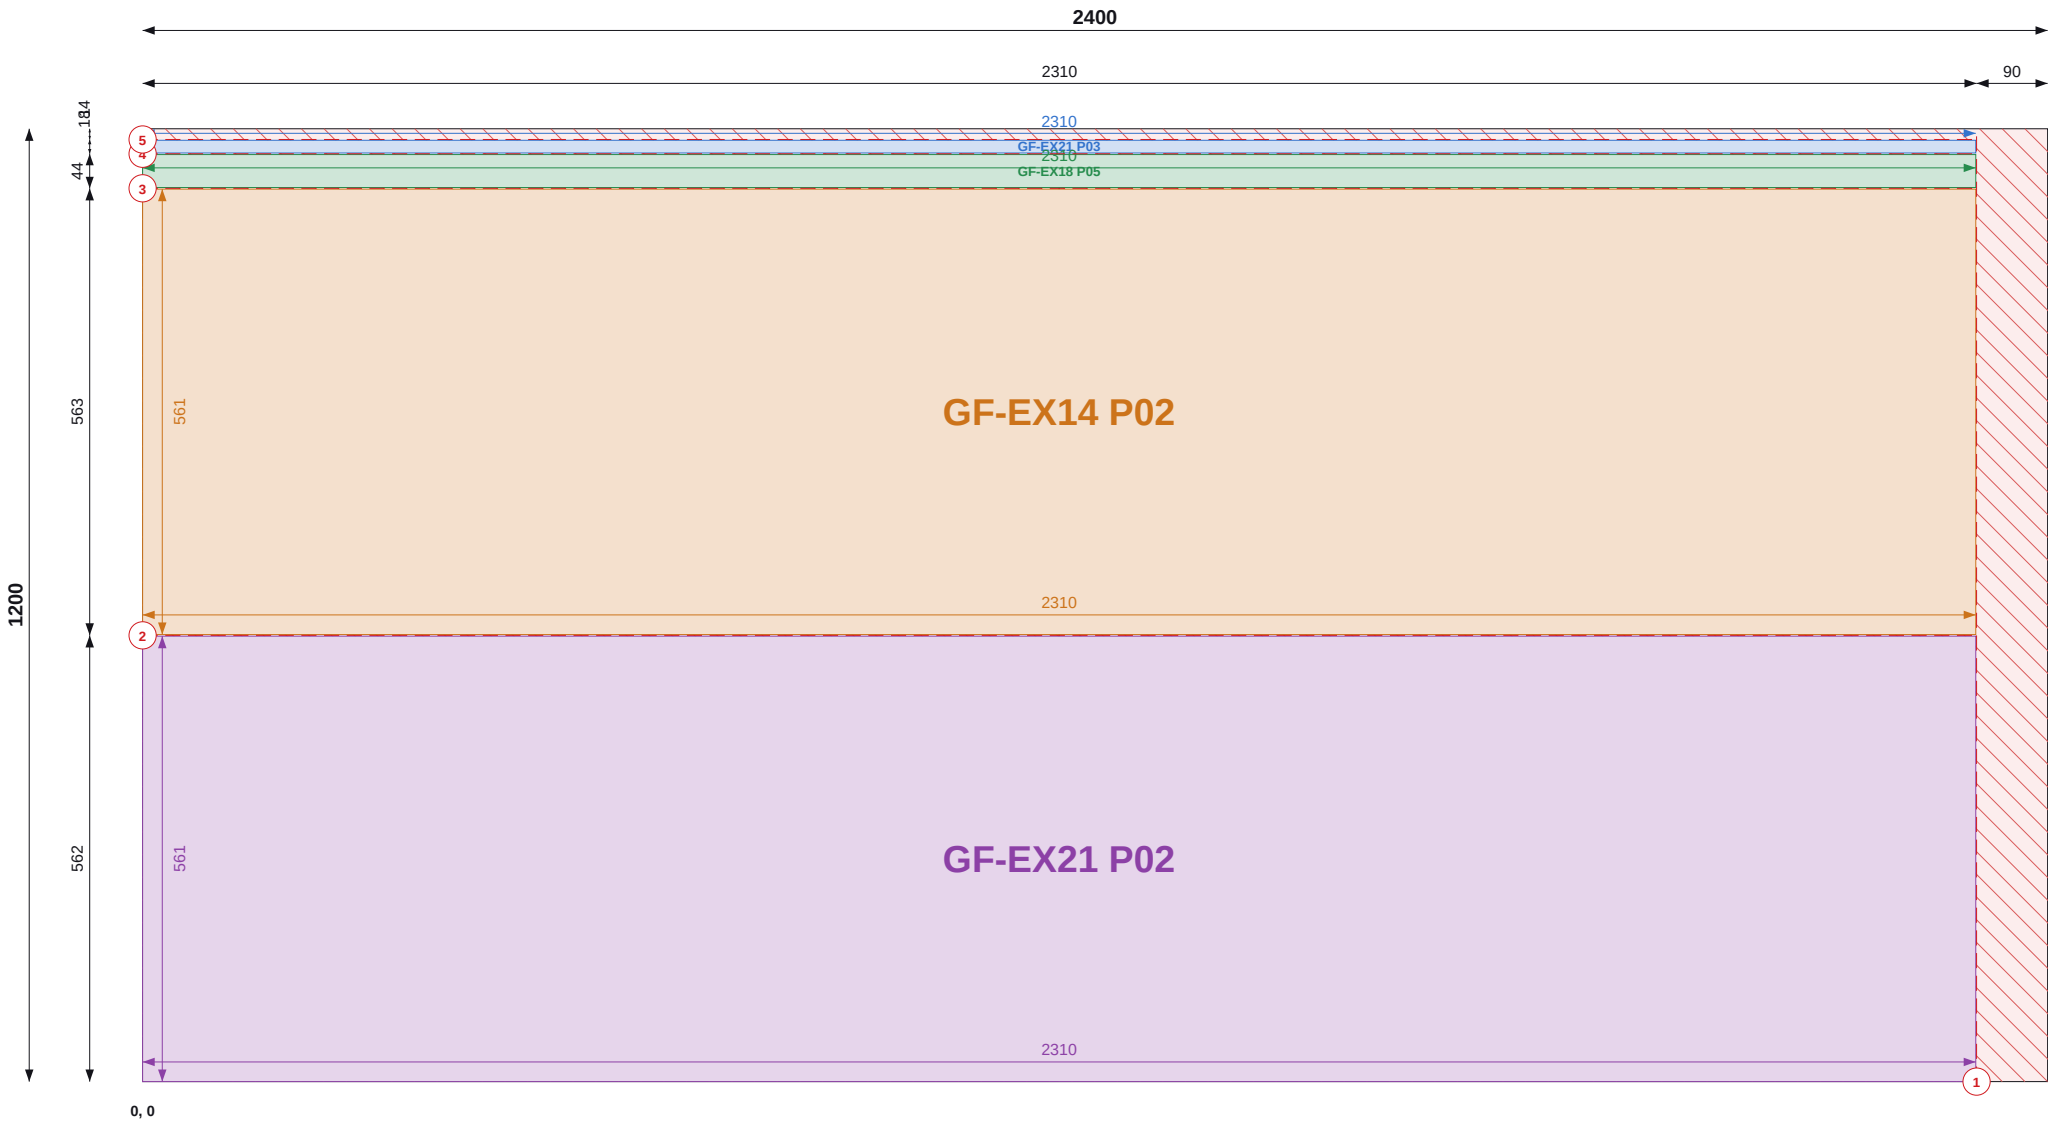

Top / left chains = saw cut positions (to cut centres). Coloured = part size and position.

## SHEET 6 OF 21

### THIS SHEET

| Item              | Value           |
|-------------------|-----------------|
| Parts             | 4               |
| Used / waste      | 94.6% / 0.16 m2 |
| Reusable offcuts  | 0               |
| Saw cuts / shared | 5 / 3           |

### PIECES (POSITION = BOTTOM-LEFT CORNER)

| Label       | Size       | X, Y    |
|-------------|------------|---------|
| GF-EX21 P03 | 16 x 2310  | 0, 1169 |
| GF-EX18 P05 | 41 x 2310  | 0, 1126 |
| GF-EX14 P02 | 561 x 2310 | 0, 563  |
| GF-EX21 P02 | 561 x 2310 | 0, 0    |

### NOTES

- Cut from PIR 120mm 1200x2400, 2mm saw kerf. Viewed on the face; dimensions from the sheet's bottom-left corner (0,0). Red numbered lines = saw cuts in order, each edge to edge.
- Coloured dimensions belong to the part of that colour: its width and height, and its position from the sheet edges. Raked parts: corner coordinates at each corner.
- Red hatch = waste. Labels = panel + piece mark on the manufacture drawing.

### REVISIONS

| REV | DATE     | DESCRIPTION        |
|-----|----------|--------------------|
| C01 | 13.09.26 | Construction issue |



TLS TIMBER FRAME

Design & Manufacture

Scan: 3D model + drawings




|          |                            |
|----------|----------------------------|
| CLIENT   | PROJECT                    |
| MP Adams | MP Adams Plot 3, Eckington |

|                                            |  |  |  |
|--------------------------------------------|--|--|--|
| DRAWING TITLE                              |  |  |  |
| PIR CUTTING - GROUND FLOOR - SHEET 6 OF 21 |  |  |  |
| PIR 120mm 1200x2400   Ground Floor         |  |  |  |

|       |      |          |       |
|-------|------|----------|-------|
| SCALE | SIZE | DATE     | DRAWN |
| NTS   | A3   | 13.09.26 | TS    |

|              |                   |     |
|--------------|-------------------|-----|
| STATUS       | DRAWING No.       | REV |
| CONSTRUCTION | P3-CP-PIR-01 / 06 | C01 |

Do not scale. All dimensions in mm. Check all dimensions on site.

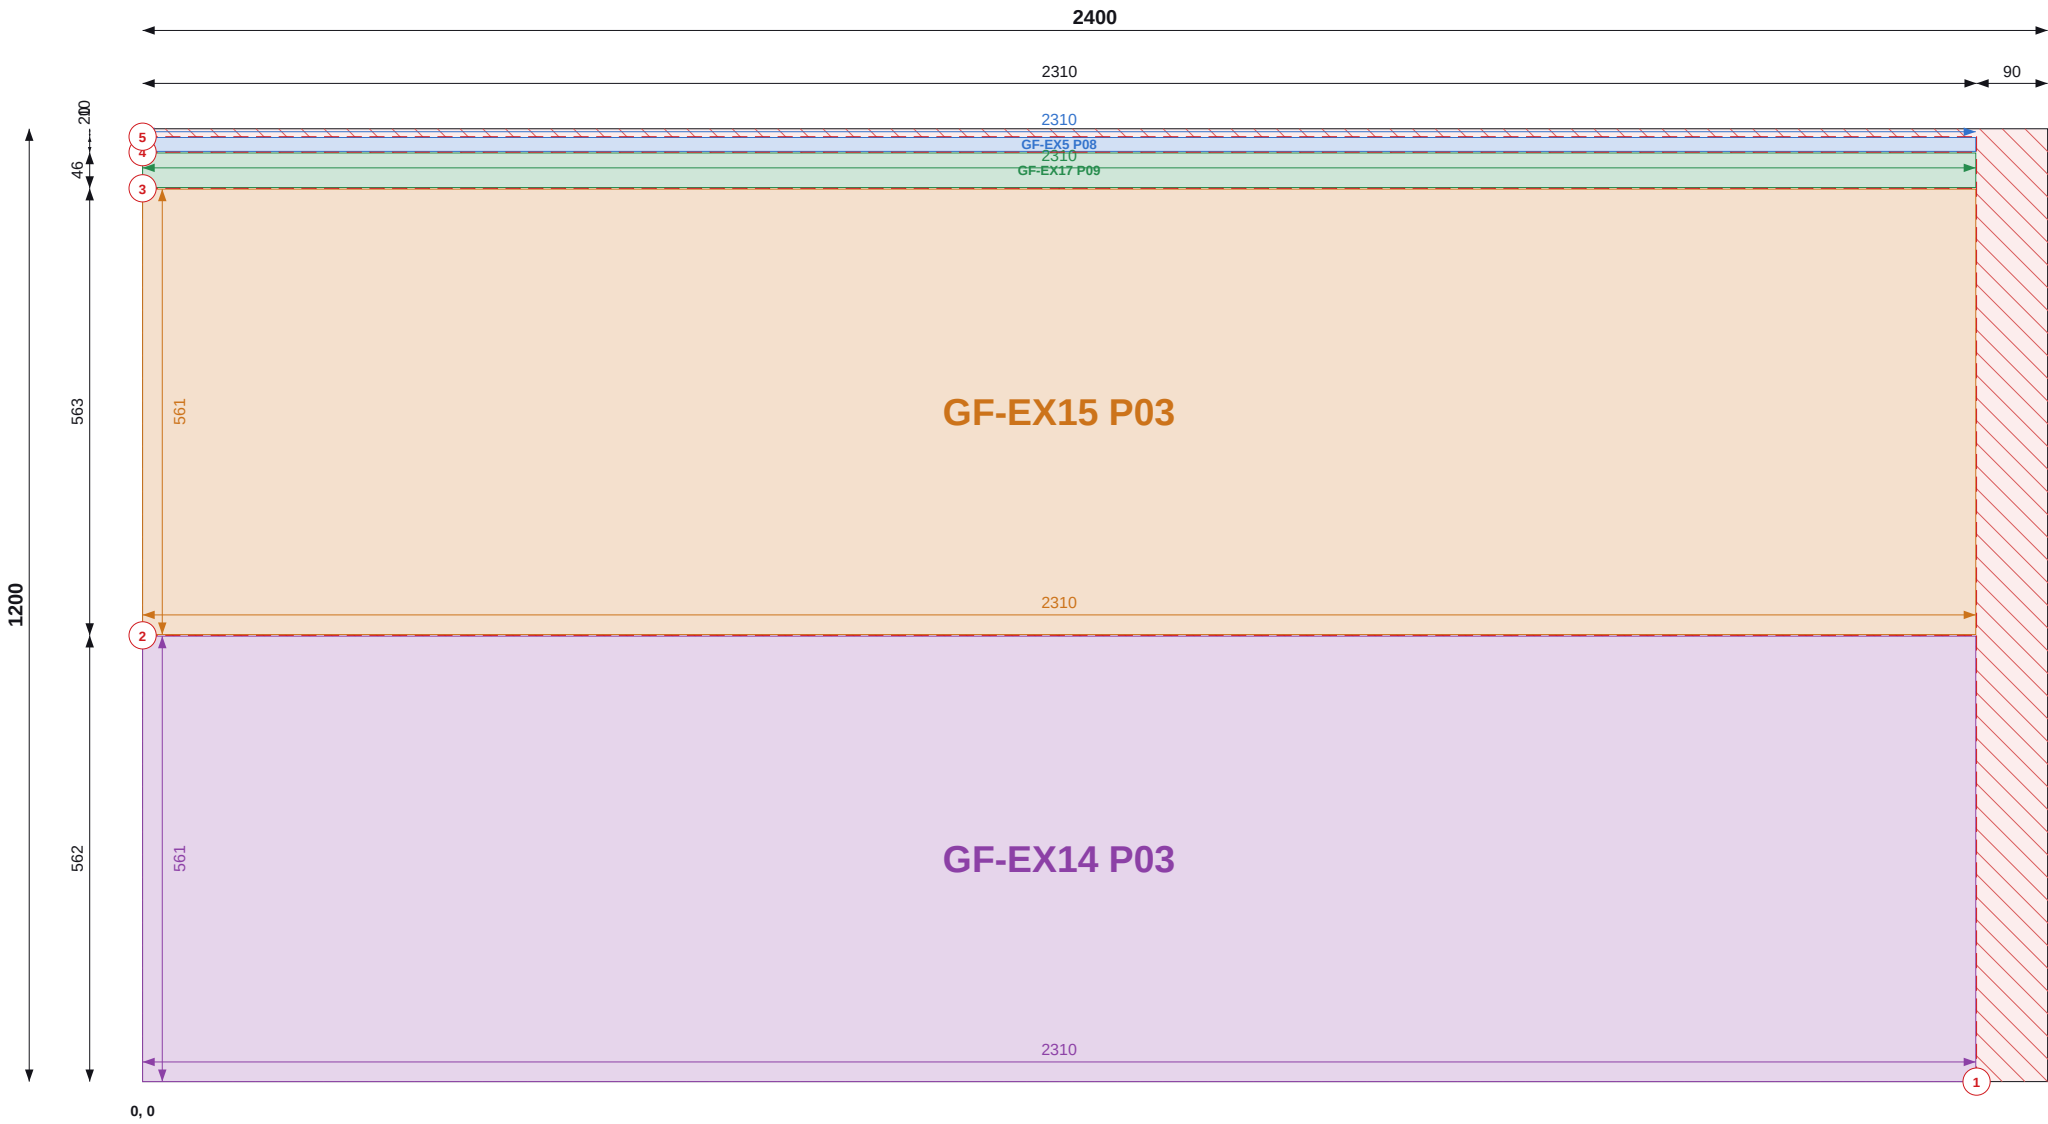

Top / left chains = saw cut positions (to cut centres). Coloured = part size and position.

SHEET 7 OF 21

THIS SHEET

| Item              | Value           |
|-------------------|-----------------|
| Parts             | 4               |
| Used / waste      | 94.9% / 0.15 m2 |
| Reusable offcuts  | 0               |
| Saw cuts / shared | 5 / 3           |

PIECES (POSITION = BOTTOM-LEFT CORNER)

| Label       | Size       | X, Y    |
|-------------|------------|---------|
| GF-EX5 P08  | 17 x 2310  | 0, 1171 |
| GF-EX17 P09 | 43 x 2310  | 0, 1126 |
| GF-EX15 P03 | 561 x 2310 | 0, 563  |
| GF-EX14 P03 | 561 x 2310 | 0, 0    |

NOTES

- Cut from PIR 120mm 1200x2400, 2mm saw kerf. Viewed on the face; dimensions from the sheet's bottom-left corner (0,0). Red numbered lines = saw cuts in order, each edge to edge.
- Coloured dimensions belong to the part of that colour: its width and height, and its position from the sheet edges. Raked parts: corner coordinates at each corner.
- Red hatch = waste. Labels = panel + piece mark on the manufacture drawing.

REVISIONS

| REV | DATE     | DESCRIPTION        |
|-----|----------|--------------------|
| C01 | 13.09.26 | Construction issue |



TLS TIMBER FRAME

Design & Manufacture

Scan: 3D model + drawings




|          |                            |
|----------|----------------------------|
| CLIENT   | PROJECT                    |
| MP Adams | MP Adams Plot 3, Eckington |

|                                            |
|--------------------------------------------|
| DRAWING TITLE                              |
| PIR CUTTING - GROUND FLOOR - SHEET 7 OF 21 |
| PIR 120mm 1200x2400   Ground Floor         |

|       |      |          |       |
|-------|------|----------|-------|
| SCALE | SIZE | DATE     | DRAWN |
| NTS   | A3   | 13.09.26 | TS    |

|              |                   |     |
|--------------|-------------------|-----|
| STATUS       | DRAWING No.       | REV |
| CONSTRUCTION | P3-CP-PIR-01 / 07 | C01 |

Do not scale. All dimensions in mm. Check all dimensions on site.

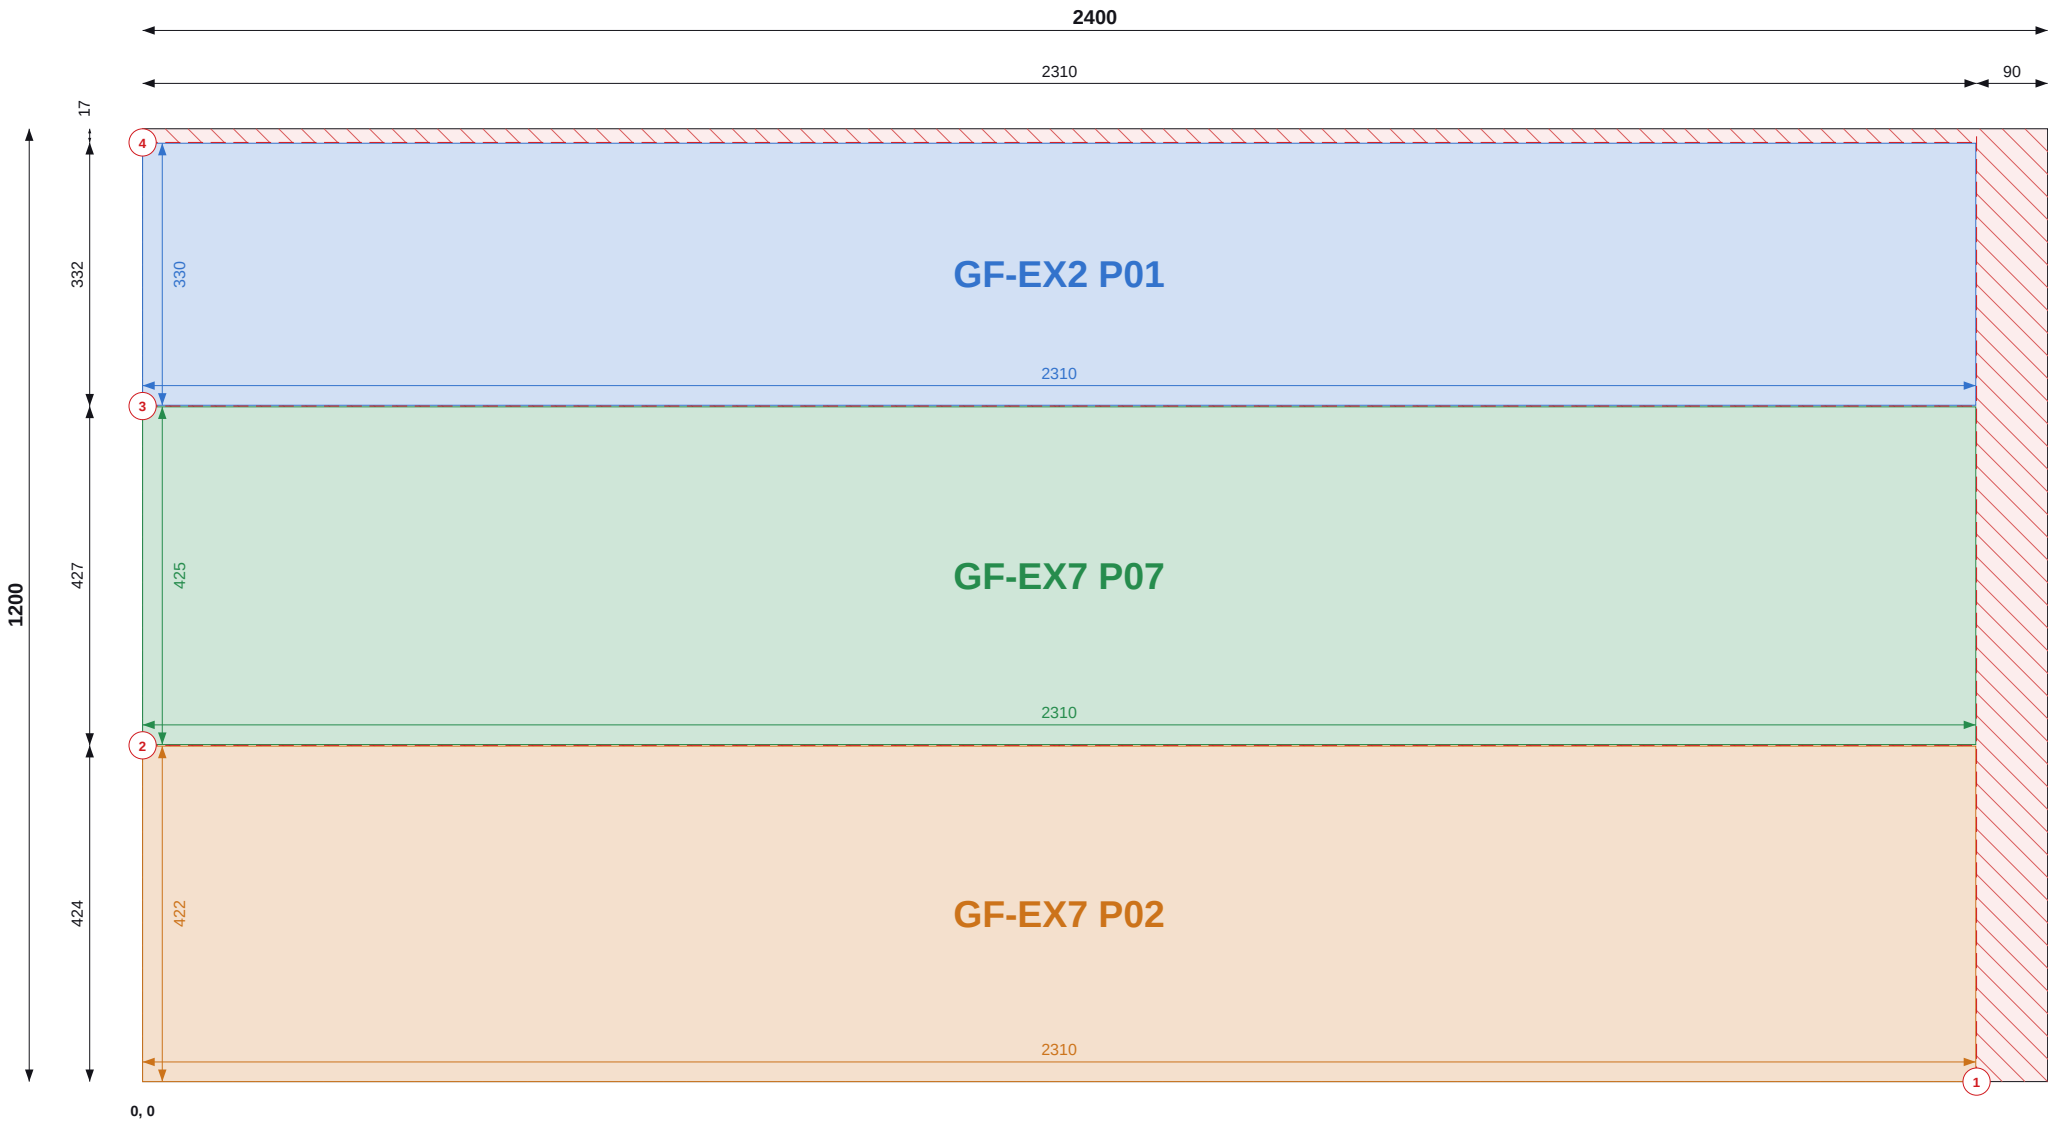

Top / left chains = saw cut positions (to cut centres). Coloured = part size and position.

SHEET 8 OF 21

THIS SHEET

| Item              | Value           |
|-------------------|-----------------|
| Parts             | 3               |
| Used / waste      | 94.4% / 0.16 m2 |
| Reusable offcuts  | 0               |
| Saw cuts / shared | 4 / 2           |

PIECES (POSITION = BOTTOM-LEFT CORNER)

| Label      | Size       | X, Y   |
|------------|------------|--------|
| GF-EX2 P01 | 330 x 2310 | 0, 852 |
| GF-EX7 P07 | 425 x 2310 | 0, 424 |
| GF-EX7 P02 | 422 x 2310 | 0, 0   |

NOTES

- Cut from PIR 120mm 1200x2400, 2mm saw kerf. Viewed on the face; dimensions from the sheet's bottom-left corner (0,0). Red numbered lines = saw cuts in order, each edge to edge.
- Coloured dimensions belong to the part of that colour: its width and height, and its position from the sheet edges. Raked parts: corner coordinates at each corner.
- Red hatch = waste. Labels = panel + piece mark on the manufacture drawing.

REVISIONS

| REV | DATE     | DESCRIPTION        |
|-----|----------|--------------------|
| C01 | 13.09.26 | Construction issue |



TLS TIMBER FRAME

Design & Manufacture

Scan: 3D model + drawings



|          |                            |
|----------|----------------------------|
| CLIENT   | PROJECT                    |
| MP Adams | MP Adams Plot 3, Eckington |


DRAWING TITLE  
**PIR CUTTING - GROUND FLOOR - SHEET 8 OF 21**

PIR 120mm 1200x2400 | Ground Floor

|       |      |          |       |
|-------|------|----------|-------|
| SCALE | SIZE | DATE     | DRAWN |
| NTS   | A3   | 13.09.26 | TS    |

|              |                          |            |
|--------------|--------------------------|------------|
| STATUS       | DRAWING No.              | REV        |
| CONSTRUCTION | <b>P3-CP-PIR-01 / 08</b> | <b>C01</b> |

Do not scale. All dimensions in mm. Check all dimensions on site.

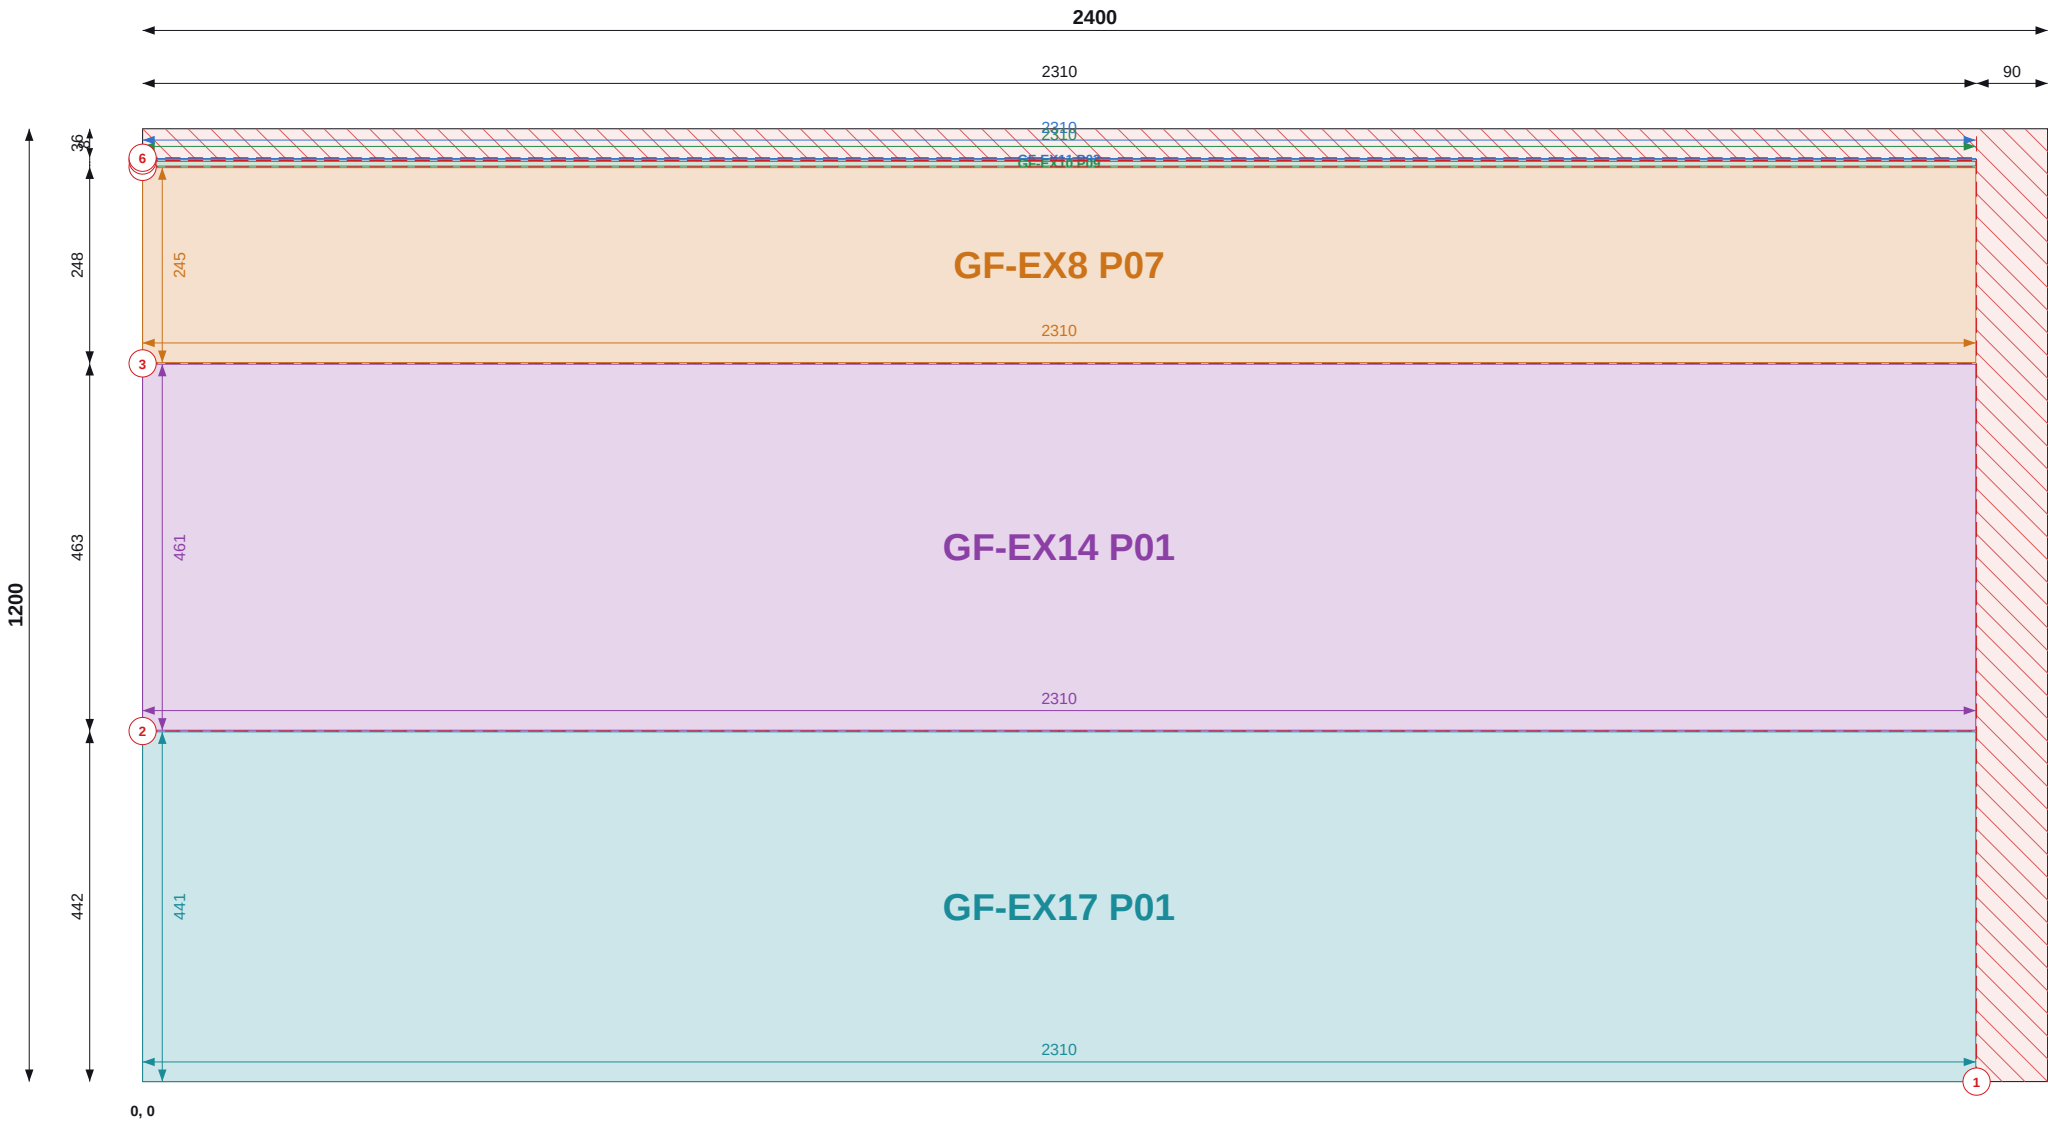

Top / left chains = saw cut positions (to cut centres). Coloured = part size and position.

SHEET 9 OF 21

THIS SHEET

| Item              | Value           |
|-------------------|-----------------|
| Parts             | 5               |
| Used / waste      | 92.6% / 0.21 m2 |
| Reusable offcuts  | 0               |
| Saw cuts / shared | 6 / 4           |

PIECES (POSITION = BOTTOM-LEFT CORNER)

| Label       | Size       | X, Y    |
|-------------|------------|---------|
| GF-EX11 P03 | 1 x 2310   | 0, 1161 |
| GF-EX10 P09 | 6 x 2310   | 0, 1153 |
| GF-EX8 P07  | 245 x 2310 | 0, 905  |
| GF-EX14 P01 | 461 x 2310 | 0, 443  |
| GF-EX17 P01 | 441 x 2310 | 0, 0    |

NOTES

- Cut from PIR 120mm 1200x2400, 2mm saw kerf. Viewed on the face; dimensions from the sheet's bottom-left corner (0,0). Red numbered lines = saw cuts in order, each edge to edge.
- Coloured dimensions belong to the part of that colour: its width and height, and its position from the sheet edges. Raked parts: corner coordinates at each corner.
- Red hatch = waste. Labels = panel + piece mark on the manufacture drawing.

REVISIONS

| REV | DATE     | DESCRIPTION        |
|-----|----------|--------------------|
| C01 | 13.09.26 | Construction issue |



**TLS TIMBER FRAME**  
Design & Manufacture  
Scan: 3D model + drawings



|                    |                                       |
|--------------------|---------------------------------------|
| CLIENT<br>MP Adams | PROJECT<br>MP Adams Plot 3, Eckington |
|--------------------|---------------------------------------|


DRAWING TITLE  
**PIR CUTTING - GROUND FLOOR - SHEET 9 OF 21**

PIR 120mm 1200x2400 | Ground Floor

|              |            |                  |             |
|--------------|------------|------------------|-------------|
| SCALE<br>NTS | SIZE<br>A3 | DATE<br>13.09.26 | DRAWN<br>TS |
|--------------|------------|------------------|-------------|

|                               |                                         |                   |
|-------------------------------|-----------------------------------------|-------------------|
| STATUS<br><b>CONSTRUCTION</b> | DRAWING No.<br><b>P3-CP-PIR-01 / 09</b> | REV<br><b>C01</b> |
|-------------------------------|-----------------------------------------|-------------------|

Do not scale. All dimensions in mm. Check all dimensions on site.

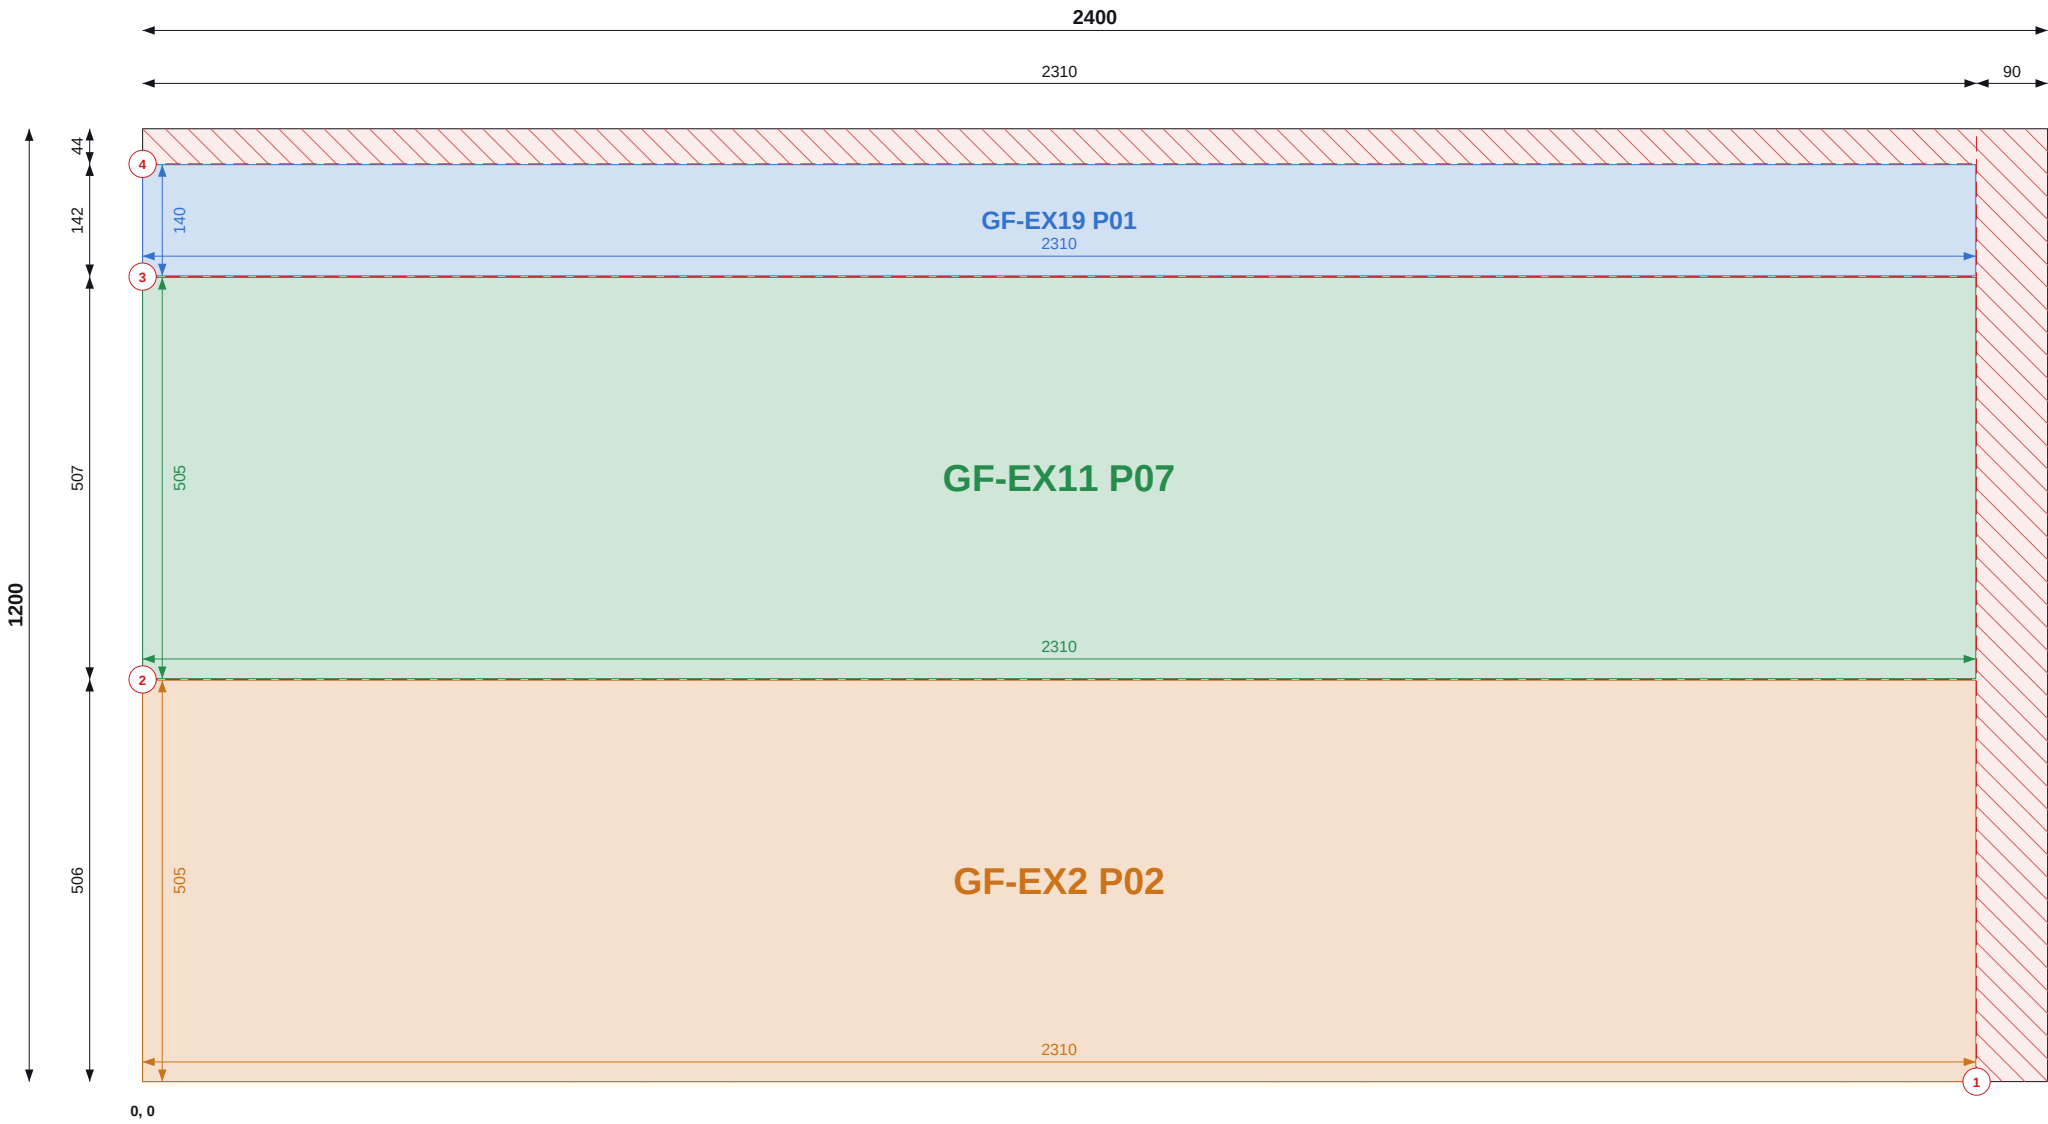

Top / left chains = saw cut positions (to cut centres). Coloured = part size and position.

SHEET 10 OF 21

THIS SHEET

| Item              | Value           |
|-------------------|-----------------|
| Parts             | 3               |
| Used / waste      | 92.3% / 0.22 m2 |
| Reusable offcuts  | 0               |
| Saw cuts / shared | 4 / 2           |

PIECES (POSITION = BOTTOM-LEFT CORNER)

| Label       | Size       | X, Y    |
|-------------|------------|---------|
| GF-EX19 P01 | 140 x 2310 | 0, 1015 |
| GF-EX11 P07 | 505 x 2310 | 0, 507  |
| GF-EX2 P02  | 505 x 2310 | 0, 0    |

NOTES

- Cut from PIR 120mm 1200x2400, 2mm saw kerf. Viewed on the face; dimensions from the sheet's bottom-left corner (0,0). Red numbered lines = saw cuts in order, each edge to edge.
- Coloured dimensions belong to the part of that colour: its width and height, and its position from the sheet edges. Raked parts: corner coordinates at each corner.
- Red hatch = waste. Labels = panel + piece mark on the manufacture drawing.

REVISIONS

| REV | DATE     | DESCRIPTION        |
|-----|----------|--------------------|
| C01 | 13.09.26 | Construction issue |



TLS TIMBER FRAME

Design & Manufacture

Scan: 3D model + drawings




|          |                            |
|----------|----------------------------|
| CLIENT   | PROJECT                    |
| MP Adams | MP Adams Plot 3, Eckington |

|                                             |  |  |  |
|---------------------------------------------|--|--|--|
| DRAWING TITLE                               |  |  |  |
| PIR CUTTING - GROUND FLOOR - SHEET 10 OF 21 |  |  |  |
| PIR 120mm 1200x2400   Ground Floor          |  |  |  |

|       |      |          |       |
|-------|------|----------|-------|
| SCALE | SIZE | DATE     | DRAWN |
| NTS   | A3   | 13.09.26 | TS    |

|              |                   |     |
|--------------|-------------------|-----|
| STATUS       | DRAWING No.       | REV |
| CONSTRUCTION | P3-CP-PIR-01 / 10 | C01 |

Do not scale. All dimensions in mm. Check all dimensions on site.

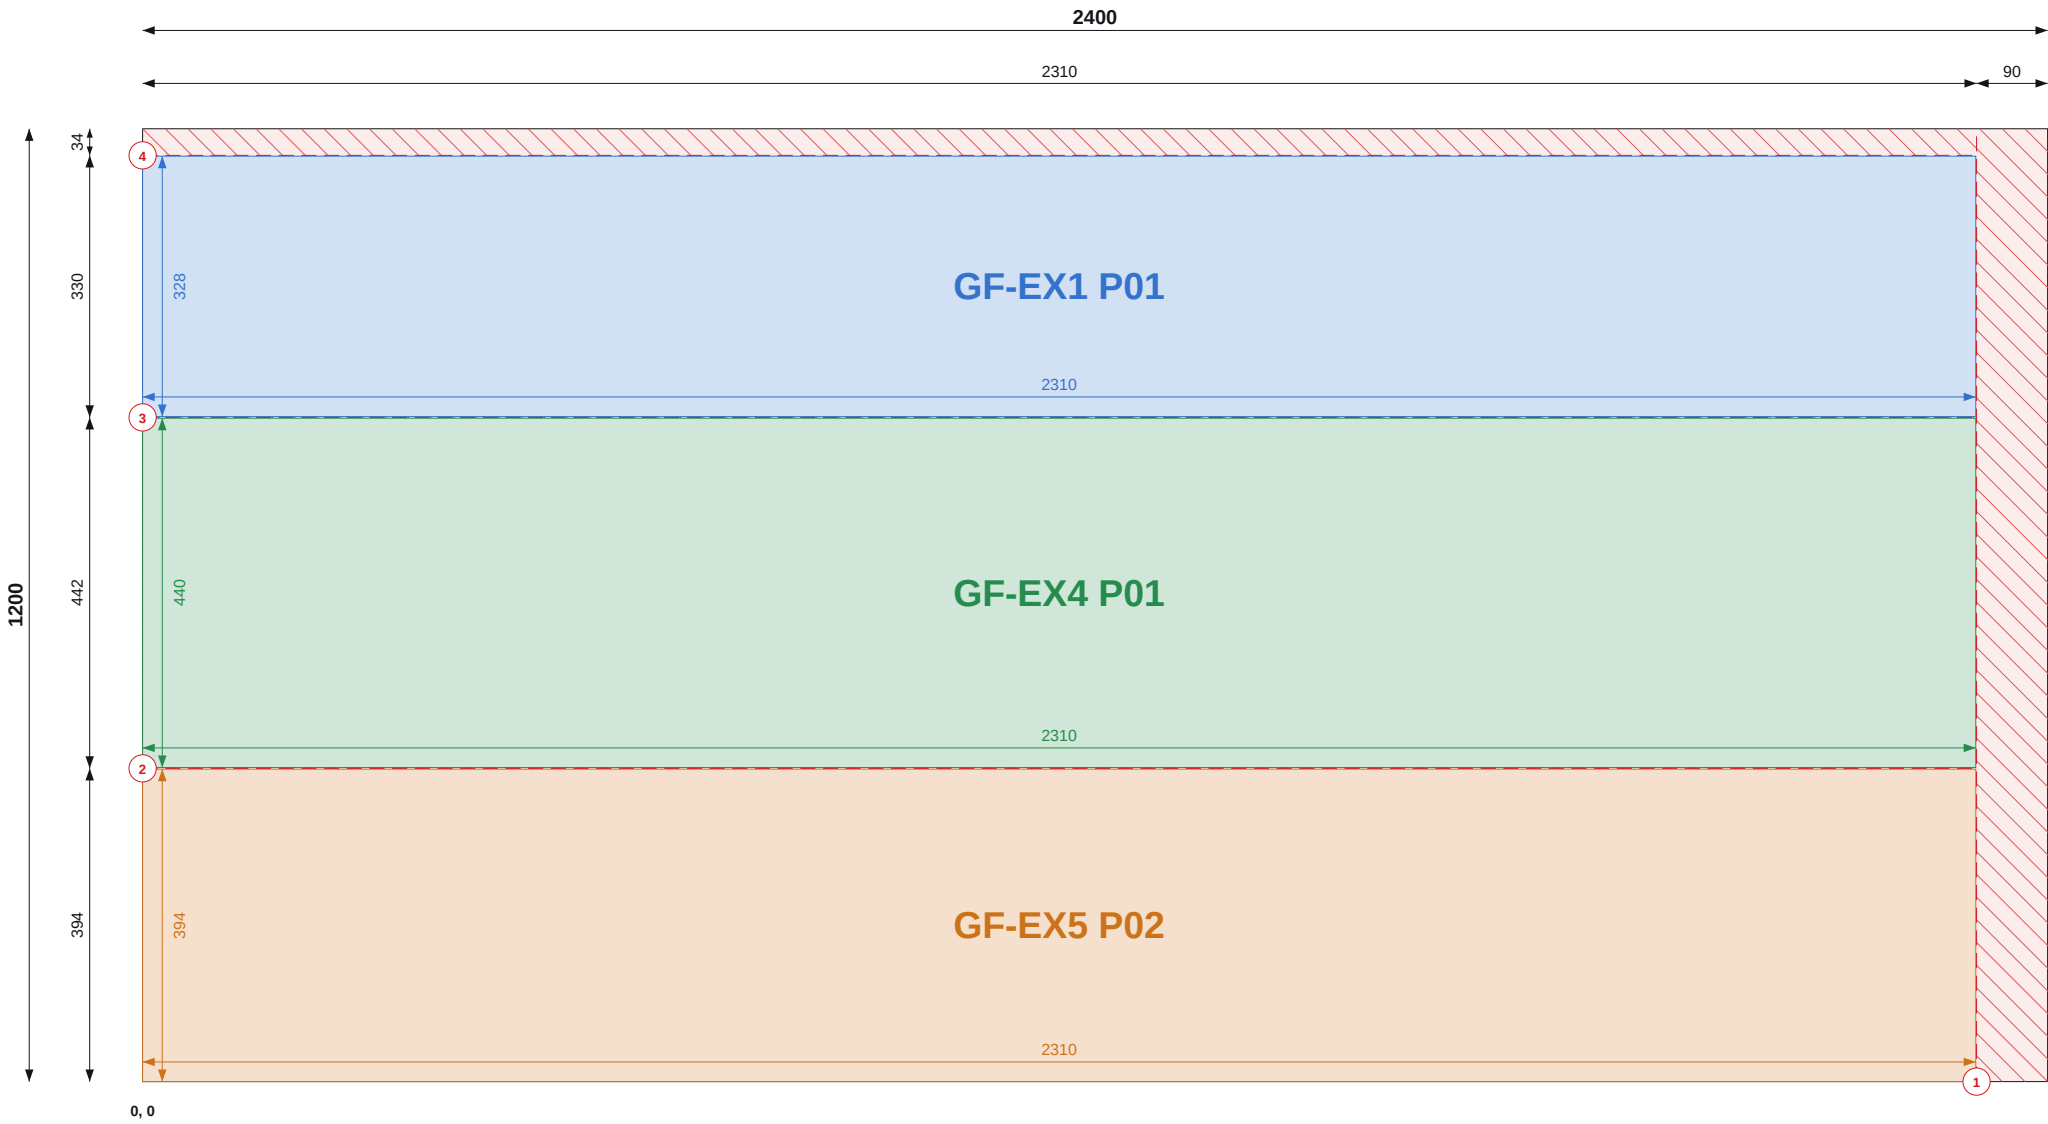

Top / left chains = saw cut positions (to cut centres). Coloured = part size and position.

SHEET 11 OF 21

THIS SHEET

| Item              | Value           |
|-------------------|-----------------|
| Parts             | 3               |
| Used / waste      | 93.1% / 0.20 m2 |
| Reusable offcuts  | 0               |
| Saw cuts / shared | 4 / 2           |

PIECES (POSITION = BOTTOM-LEFT CORNER)

| Label      | Size       | X, Y   |
|------------|------------|--------|
| GF-EX1 P01 | 328 x 2310 | 0, 837 |
| GF-EX4 P01 | 440 x 2310 | 0, 396 |
| GF-EX5 P02 | 394 x 2310 | 0, 0   |

NOTES

- Cut from PIR 120mm 1200x2400, 2mm saw kerf. Viewed on the face; dimensions from the sheet's bottom-left corner (0,0). Red numbered lines = saw cuts in order, each edge to edge.
- Coloured dimensions belong to the part of that colour: its width and height, and its position from the sheet edges. Raked parts: corner coordinates at each corner.
- Red hatch = waste. Labels = panel + piece mark on the manufacture drawing.

REVISIONS

| REV | DATE     | DESCRIPTION        |
|-----|----------|--------------------|
| C01 | 13.09.26 | Construction issue |



TLS TIMBER FRAME  
Design & Manufacture  
Scan: 3D model + drawings



|                    |                                       |
|--------------------|---------------------------------------|
| CLIENT<br>MP Adams | PROJECT<br>MP Adams Plot 3, Eckington |
|--------------------|---------------------------------------|


DRAWING TITLE  
**PIR CUTTING - GROUND FLOOR - SHEET 11 OF 21**

PIR 120mm 1200x2400 | Ground Floor

|              |            |                  |             |
|--------------|------------|------------------|-------------|
| SCALE<br>NTS | SIZE<br>A3 | DATE<br>13.09.26 | DRAWN<br>TS |
|--------------|------------|------------------|-------------|

|                               |                                         |                   |
|-------------------------------|-----------------------------------------|-------------------|
| STATUS<br><b>CONSTRUCTION</b> | DRAWING No.<br><b>P3-CP-PIR-01 / 11</b> | REV<br><b>C01</b> |
|-------------------------------|-----------------------------------------|-------------------|

Do not scale. All dimensions in mm. Check all dimensions on site.

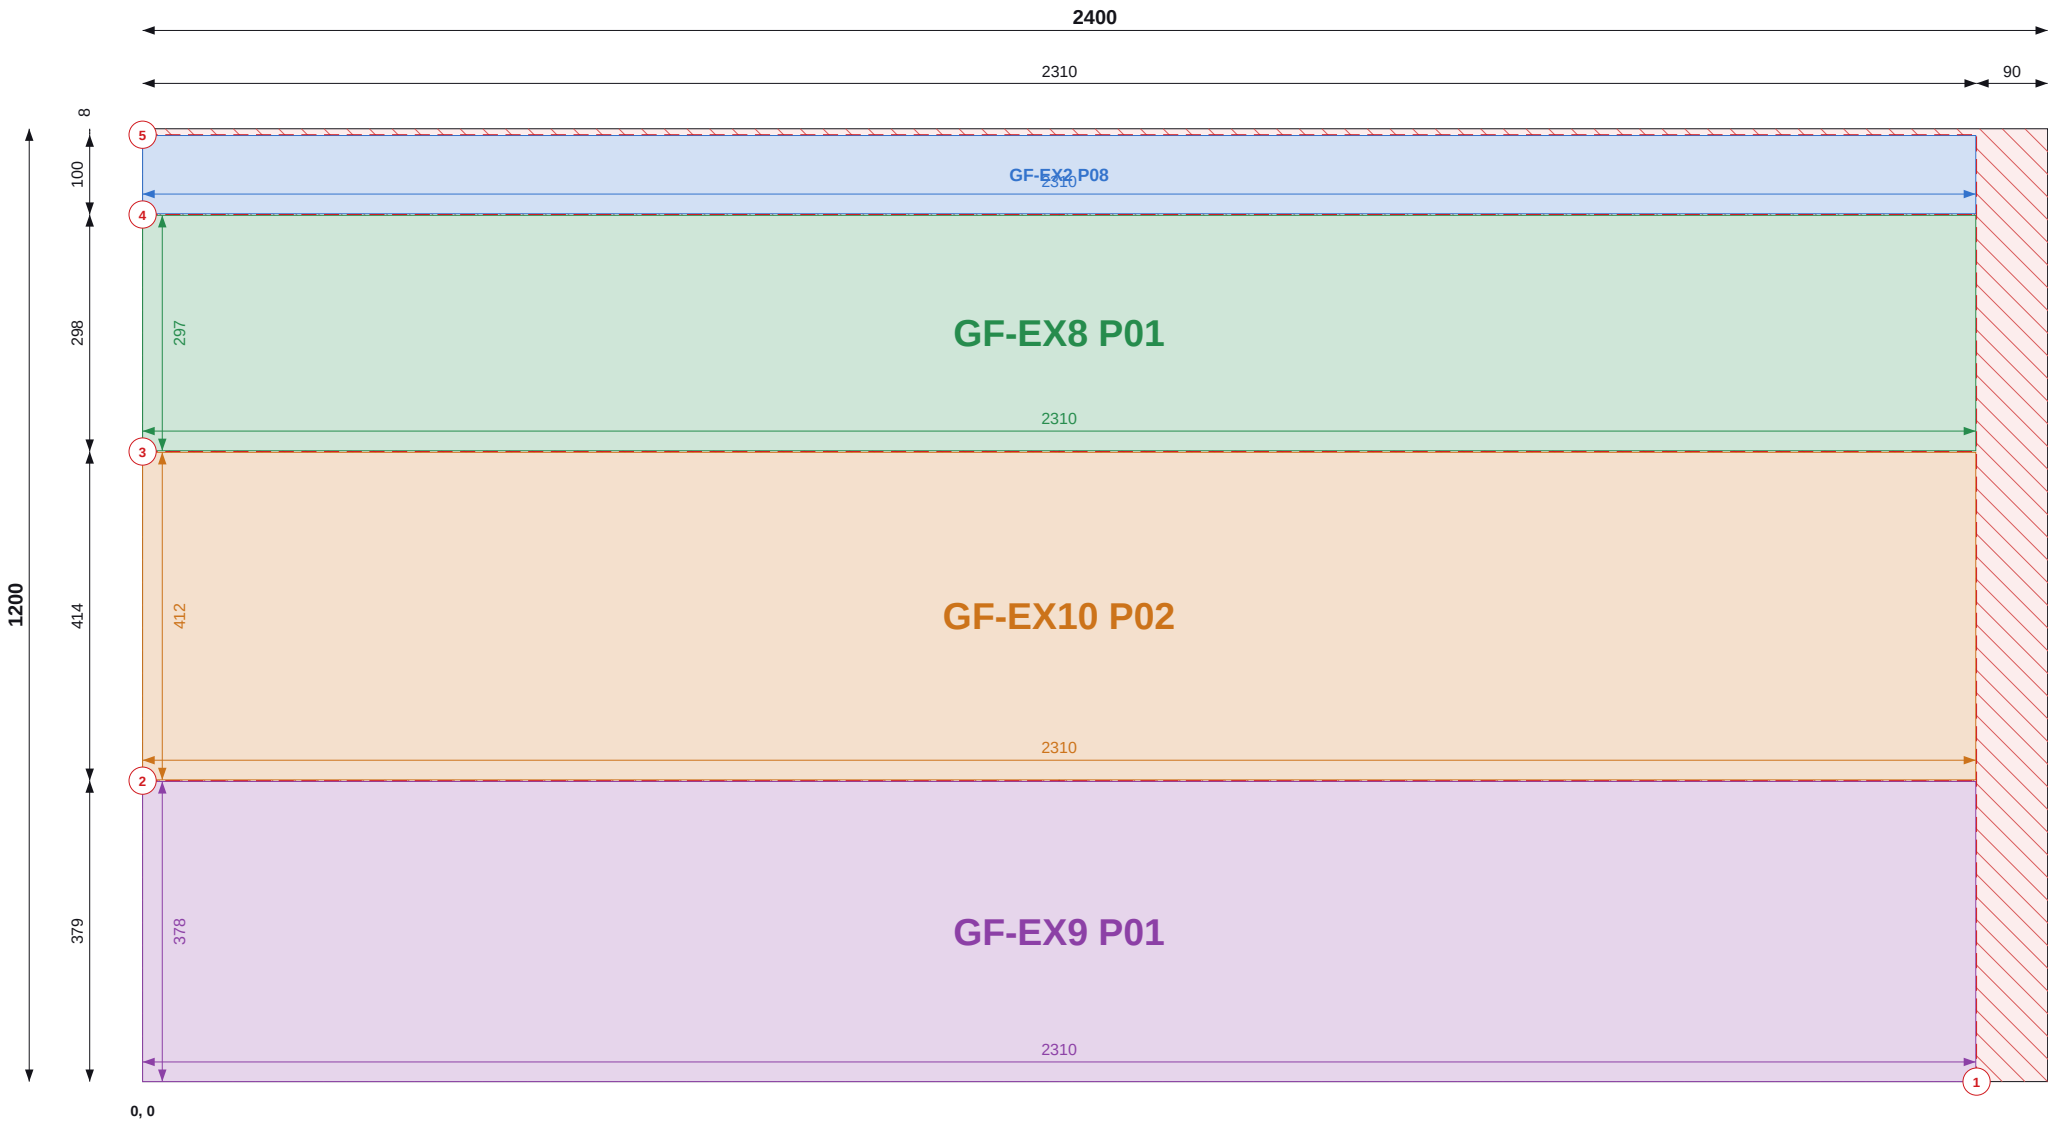

Top / left chains = saw cut positions (to cut centres). Coloured = part size and position.

SHEET 12 OF 21

THIS SHEET

| Item              | Value           |
|-------------------|-----------------|
| Parts             | 4               |
| Used / waste      | 95.1% / 0.14 m2 |
| Reusable offcuts  | 0               |
| Saw cuts / shared | 5 / 3           |

PIECES (POSITION = BOTTOM-LEFT CORNER)

| Label       | Size       | X, Y    |
|-------------|------------|---------|
| GF-EX2 P08  | 99 x 2310  | 0, 1093 |
| GF-EX8 P01  | 297 x 2310 | 0, 794  |
| GF-EX10 P02 | 412 x 2310 | 0, 380  |
| GF-EX9 P01  | 378 x 2310 | 0, 0    |

NOTES

- Cut from PIR 120mm 1200x2400, 2mm saw kerf. Viewed on the face; dimensions from the sheet's bottom-left corner (0,0). Red numbered lines = saw cuts in order, each edge to edge.
- Coloured dimensions belong to the part of that colour: its width and height, and its position from the sheet edges. Raked parts: corner coordinates at each corner.
- Red hatch = waste. Labels = panel + piece mark on the manufacture drawing.

REVISIONS

| REV | DATE     | DESCRIPTION        |
|-----|----------|--------------------|
| C01 | 13.09.26 | Construction issue |



TLS TIMBER FRAME  
Design & Manufacture  
Scan: 3D model + drawings



|                    |                                       |
|--------------------|---------------------------------------|
| CLIENT<br>MP Adams | PROJECT<br>MP Adams Plot 3, Eckington |
|--------------------|---------------------------------------|


DRAWING TITLE  
**PIR CUTTING - GROUND FLOOR - SHEET 12 OF 21**

PIR 120mm 1200x2400 | Ground Floor

|              |            |                  |             |
|--------------|------------|------------------|-------------|
| SCALE<br>NTS | SIZE<br>A3 | DATE<br>13.09.26 | DRAWN<br>TS |
|--------------|------------|------------------|-------------|

|                               |                                         |                   |
|-------------------------------|-----------------------------------------|-------------------|
| STATUS<br><b>CONSTRUCTION</b> | DRAWING No.<br><b>P3-CP-PIR-01 / 12</b> | REV<br><b>C01</b> |
|-------------------------------|-----------------------------------------|-------------------|

Do not scale. All dimensions in mm. Check all dimensions on site.

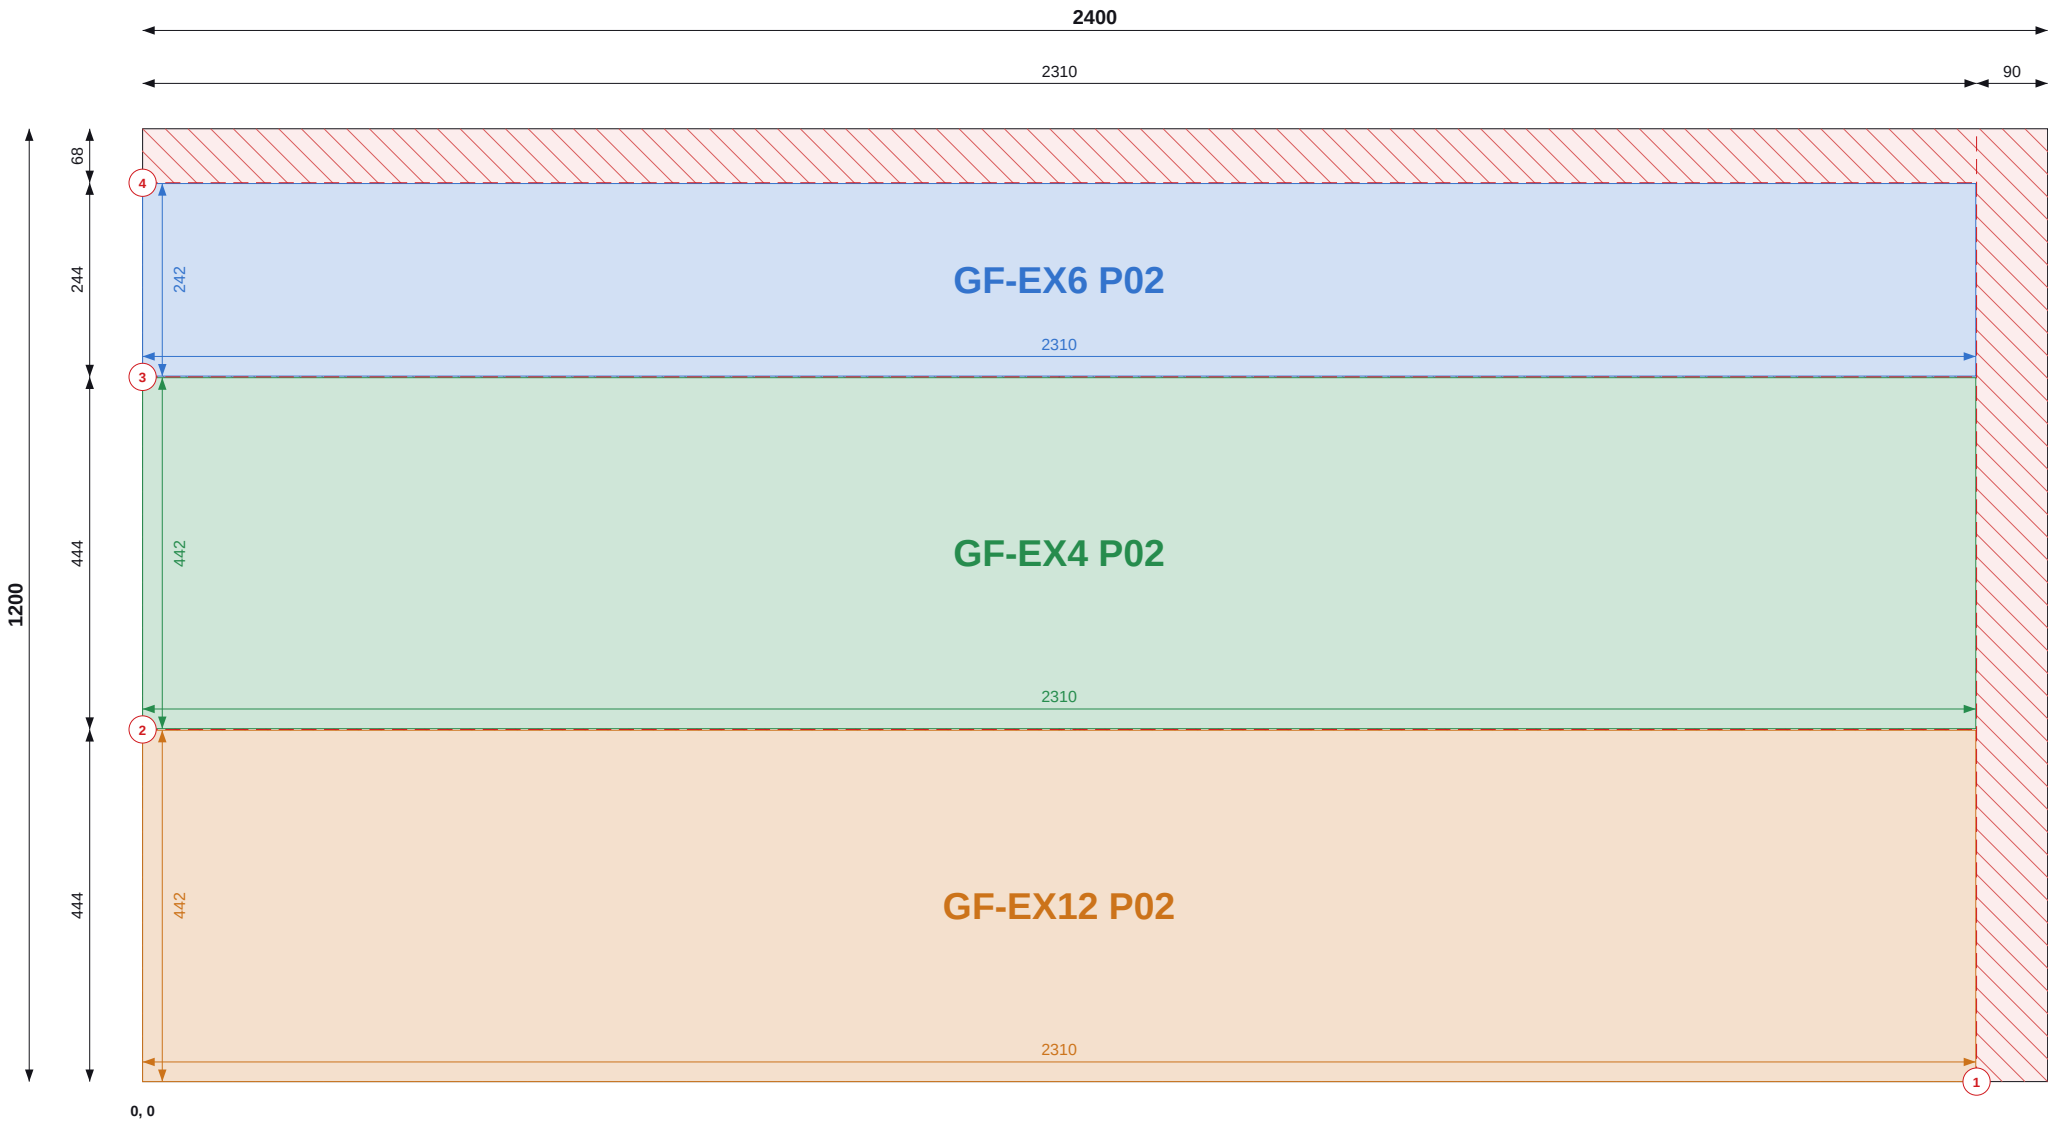

Top / left chains = saw cut positions (to cut centres). Coloured = part size and position.

SHEET 13 OF 21

THIS SHEET

| Item              | Value           |
|-------------------|-----------------|
| Parts             | 3               |
| Used / waste      | 90.4% / 0.28 m2 |
| Reusable offcuts  | 0               |
| Saw cuts / shared | 4 / 2           |

PIECES (POSITION = BOTTOM-LEFT CORNER)

| Label       | Size       | X, Y   |
|-------------|------------|--------|
| GF-EX6 P02  | 242 x 2310 | 0, 889 |
| GF-EX4 P02  | 442 x 2310 | 0, 444 |
| GF-EX12 P02 | 442 x 2310 | 0, 0   |

NOTES

1. Cut from PIR 120mm 1200x2400, 2mm saw kerf. Viewed on the face; dimensions from the sheet's bottom-left corner (0,0). Red numbered lines = saw cuts in order, each edge to edge.
2. Coloured dimensions belong to the part of that colour: its width and height, and its position from the sheet edges. Raked parts: corner coordinates at each corner.
3. Red hatch = waste. Labels = panel + piece mark on the manufacture drawing.

REVISIONS

| REV | DATE     | DESCRIPTION        |
|-----|----------|--------------------|
| C01 | 13.09.26 | Construction issue |



TLS TIMBER FRAME

Design & Manufacture

Scan: 3D model + drawings



|          |                            |
|----------|----------------------------|
| CLIENT   | PROJECT                    |
| MP Adams | MP Adams Plot 3, Eckington |


DRAWING TITLE  
**PIR CUTTING - GROUND FLOOR - SHEET 13 OF 21**

PIR 120mm 1200x2400 | Ground Floor

|       |      |          |       |
|-------|------|----------|-------|
| SCALE | SIZE | DATE     | DRAWN |
| NTS   | A3   | 13.09.26 | TS    |

|              |                          |            |
|--------------|--------------------------|------------|
| STATUS       | DRAWING No.              | REV        |
| CONSTRUCTION | <b>P3-CP-PIR-01 / 13</b> | <b>C01</b> |

Do not scale. All dimensions in mm. Check all dimensions on site.

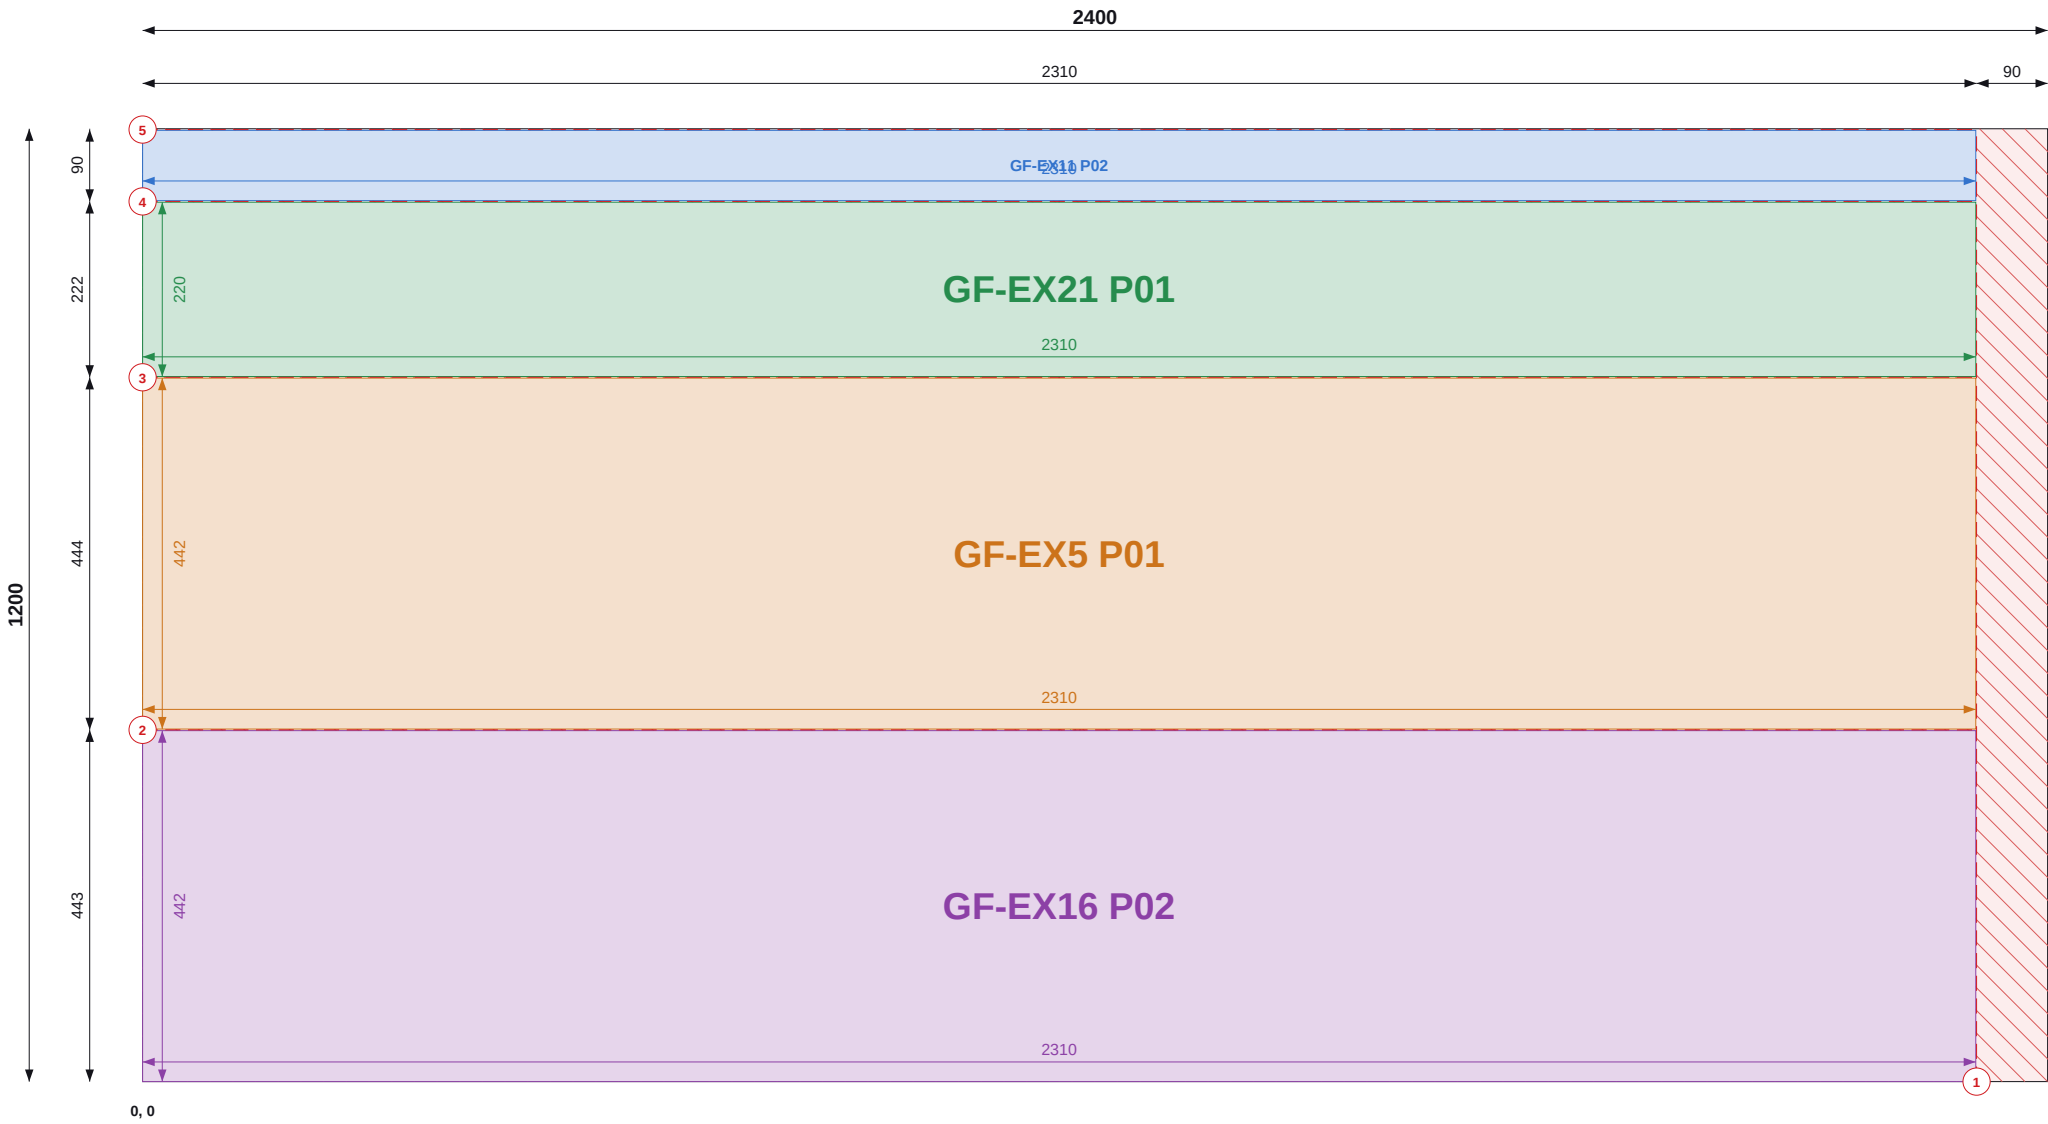

Top / left chains = saw cut positions (to cut centres). Coloured = part size and position.

SHEET 14 OF 21

THIS SHEET

| Item              | Value           |
|-------------------|-----------------|
| Parts             | 4               |
| Used / waste      | 95.6% / 0.13 m2 |
| Reusable offcuts  | 0               |
| Saw cuts / shared | 5 / 3           |

PIECES (POSITION = BOTTOM-LEFT CORNER)

| Label       | Size       | X, Y    |
|-------------|------------|---------|
| GF-EX11 P02 | 89 x 2310  | 0, 1109 |
| GF-EX21 P01 | 220 x 2310 | 0, 888  |
| GF-EX5 P01  | 442 x 2310 | 0, 444  |
| GF-EX16 P02 | 442 x 2310 | 0, 0    |

NOTES

- Cut from PIR 120mm 1200x2400, 2mm saw kerf. Viewed on the face; dimensions from the sheet's bottom-left corner (0,0). Red numbered lines = saw cuts in order, each edge to edge.
- Coloured dimensions belong to the part of that colour: its width and height, and its position from the sheet edges. Raked parts: corner coordinates at each corner.
- Red hatch = waste. Labels = panel + piece mark on the manufacture drawing.

REVISIONS

| REV | DATE     | DESCRIPTION        |
|-----|----------|--------------------|
| C01 | 13.09.26 | Construction issue |



TLS TIMBER FRAME

Design & Manufacture

Scan: 3D model + drawings



|          |                            |
|----------|----------------------------|
| CLIENT   | PROJECT                    |
| MP Adams | MP Adams Plot 3, Eckington |


DRAWING TITLE  
**PIR CUTTING - GROUND FLOOR - SHEET 14 OF 21**

PIR 120mm 1200x2400 | Ground Floor

|       |      |          |       |
|-------|------|----------|-------|
| SCALE | SIZE | DATE     | DRAWN |
| NTS   | A3   | 13.09.26 | TS    |

|              |                          |            |
|--------------|--------------------------|------------|
| STATUS       | DRAWING No.              | REV        |
| CONSTRUCTION | <b>P3-CP-PIR-01 / 14</b> | <b>C01</b> |

Do not scale. All dimensions in mm. Check all dimensions on site.

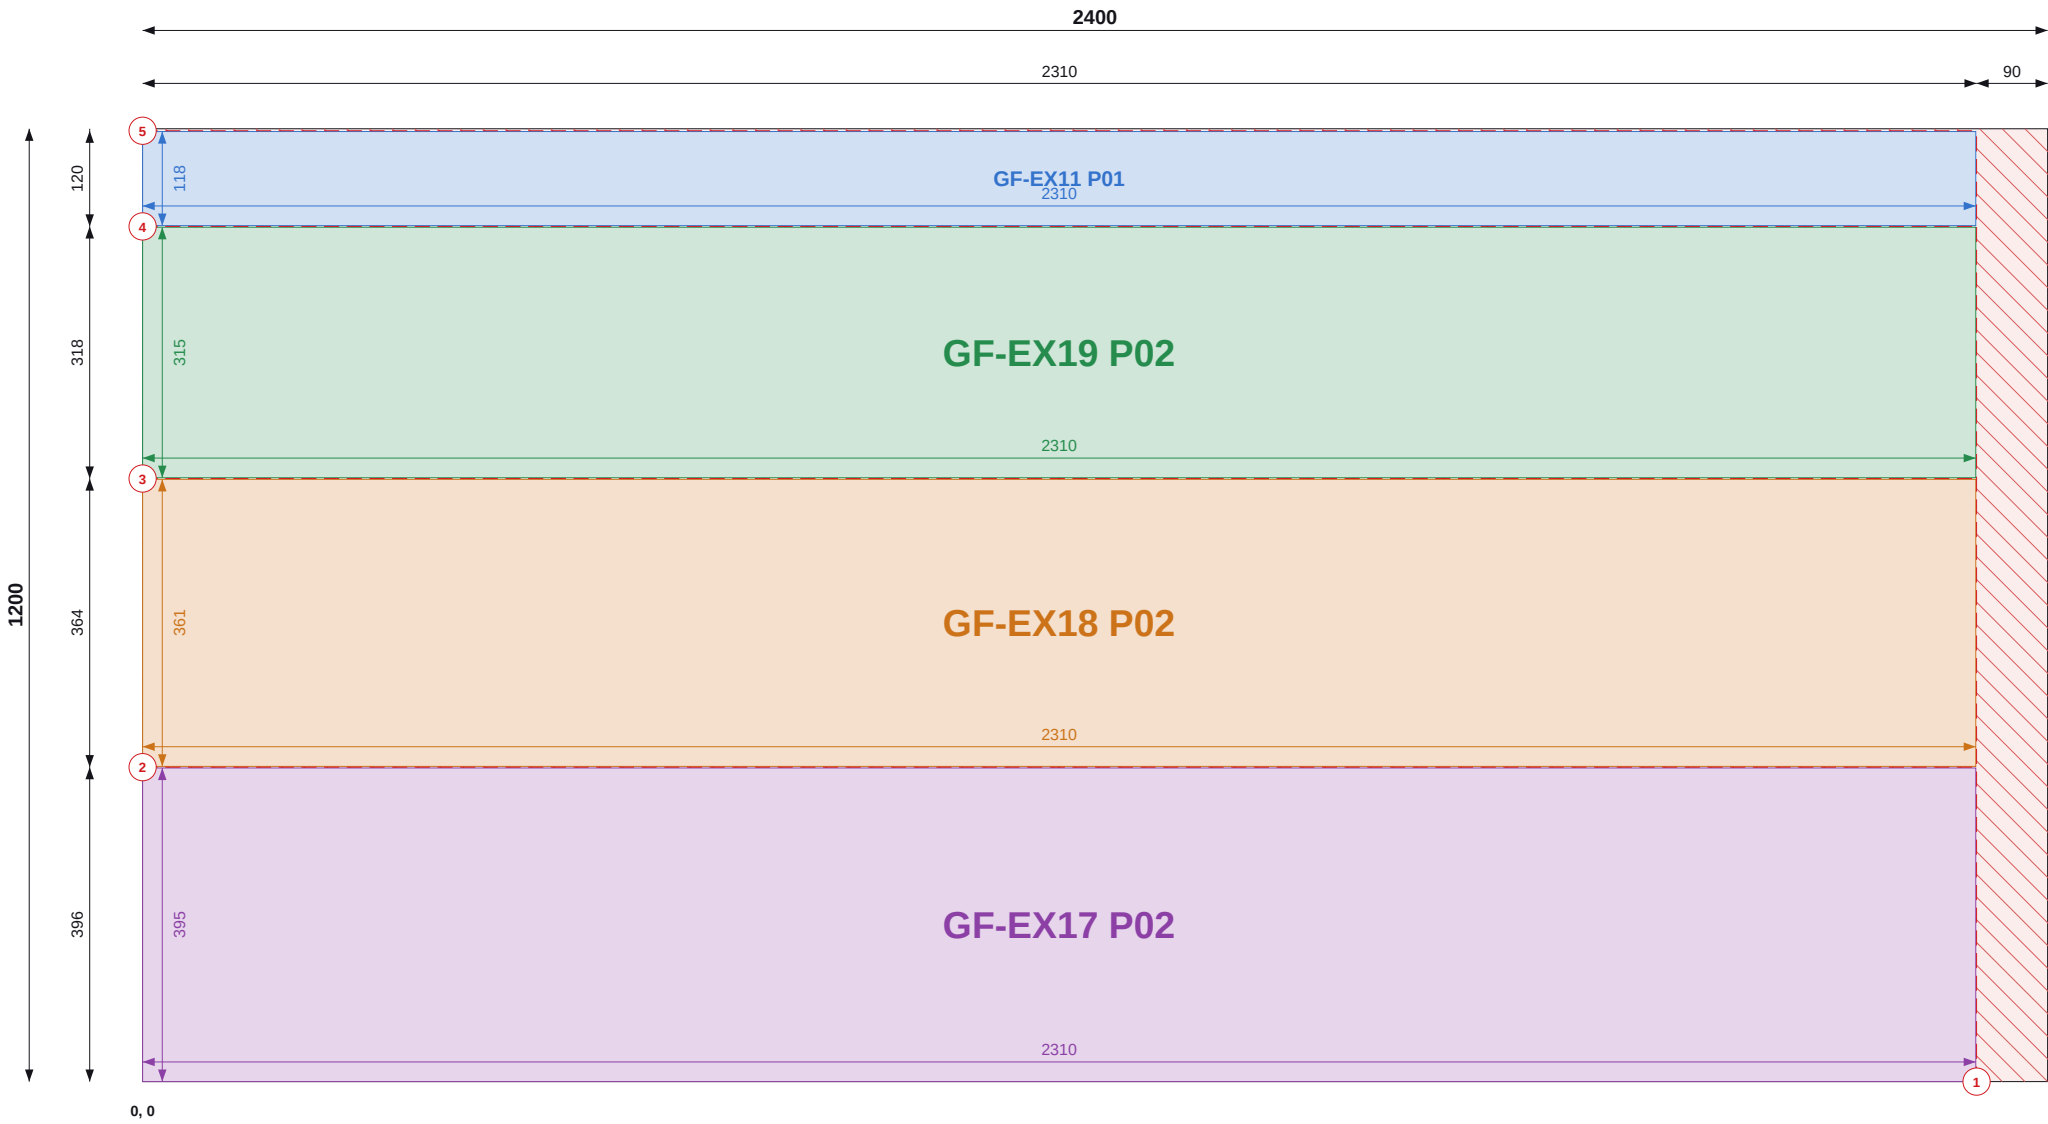

Top / left chains = saw cut positions (to cut centres). Coloured = part size and position.

SHEET 15 OF 21

THIS SHEET

| Item              | Value           |
|-------------------|-----------------|
| Parts             | 4               |
| Used / waste      | 95.5% / 0.13 m2 |
| Reusable offcuts  | 0               |
| Saw cuts / shared | 5 / 3           |

PIECES (POSITION = BOTTOM-LEFT CORNER)

| Label       | Size       | X, Y    |
|-------------|------------|---------|
| GF-EX11 P01 | 118 x 2310 | 0, 1078 |
| GF-EX19 P02 | 315 x 2310 | 0, 760  |
| GF-EX18 P02 | 361 x 2310 | 0, 397  |
| GF-EX17 P02 | 395 x 2310 | 0, 0    |

NOTES

- Cut from PIR 120mm 1200x2400, 2mm saw kerf. Viewed on the face; dimensions from the sheet's bottom-left corner (0,0). Red numbered lines = saw cuts in order, each edge to edge.
- Coloured dimensions belong to the part of that colour: its width and height, and its position from the sheet edges. Raked parts: corner coordinates at each corner.
- Red hatch = waste. Labels = panel + piece mark on the manufacture drawing.

REVISIONS

| REV | DATE     | DESCRIPTION        |
|-----|----------|--------------------|
| C01 | 13.09.26 | Construction issue |



TLS TIMBER FRAME

Design & Manufacture

Scan: 3D model + drawings




|          |                            |
|----------|----------------------------|
| CLIENT   | PROJECT                    |
| MP Adams | MP Adams Plot 3, Eckington |

|                                             |
|---------------------------------------------|
| DRAWING TITLE                               |
| PIR CUTTING - GROUND FLOOR - SHEET 15 OF 21 |
| PIR 120mm 1200x2400   Ground Floor          |

|       |      |          |       |
|-------|------|----------|-------|
| SCALE | SIZE | DATE     | DRAWN |
| NTS   | A3   | 13.09.26 | TS    |

|              |                   |     |
|--------------|-------------------|-----|
| STATUS       | DRAWING No.       | REV |
| CONSTRUCTION | P3-CP-PIR-01 / 15 | C01 |

Do not scale. All dimensions in mm. Check all dimensions on site.

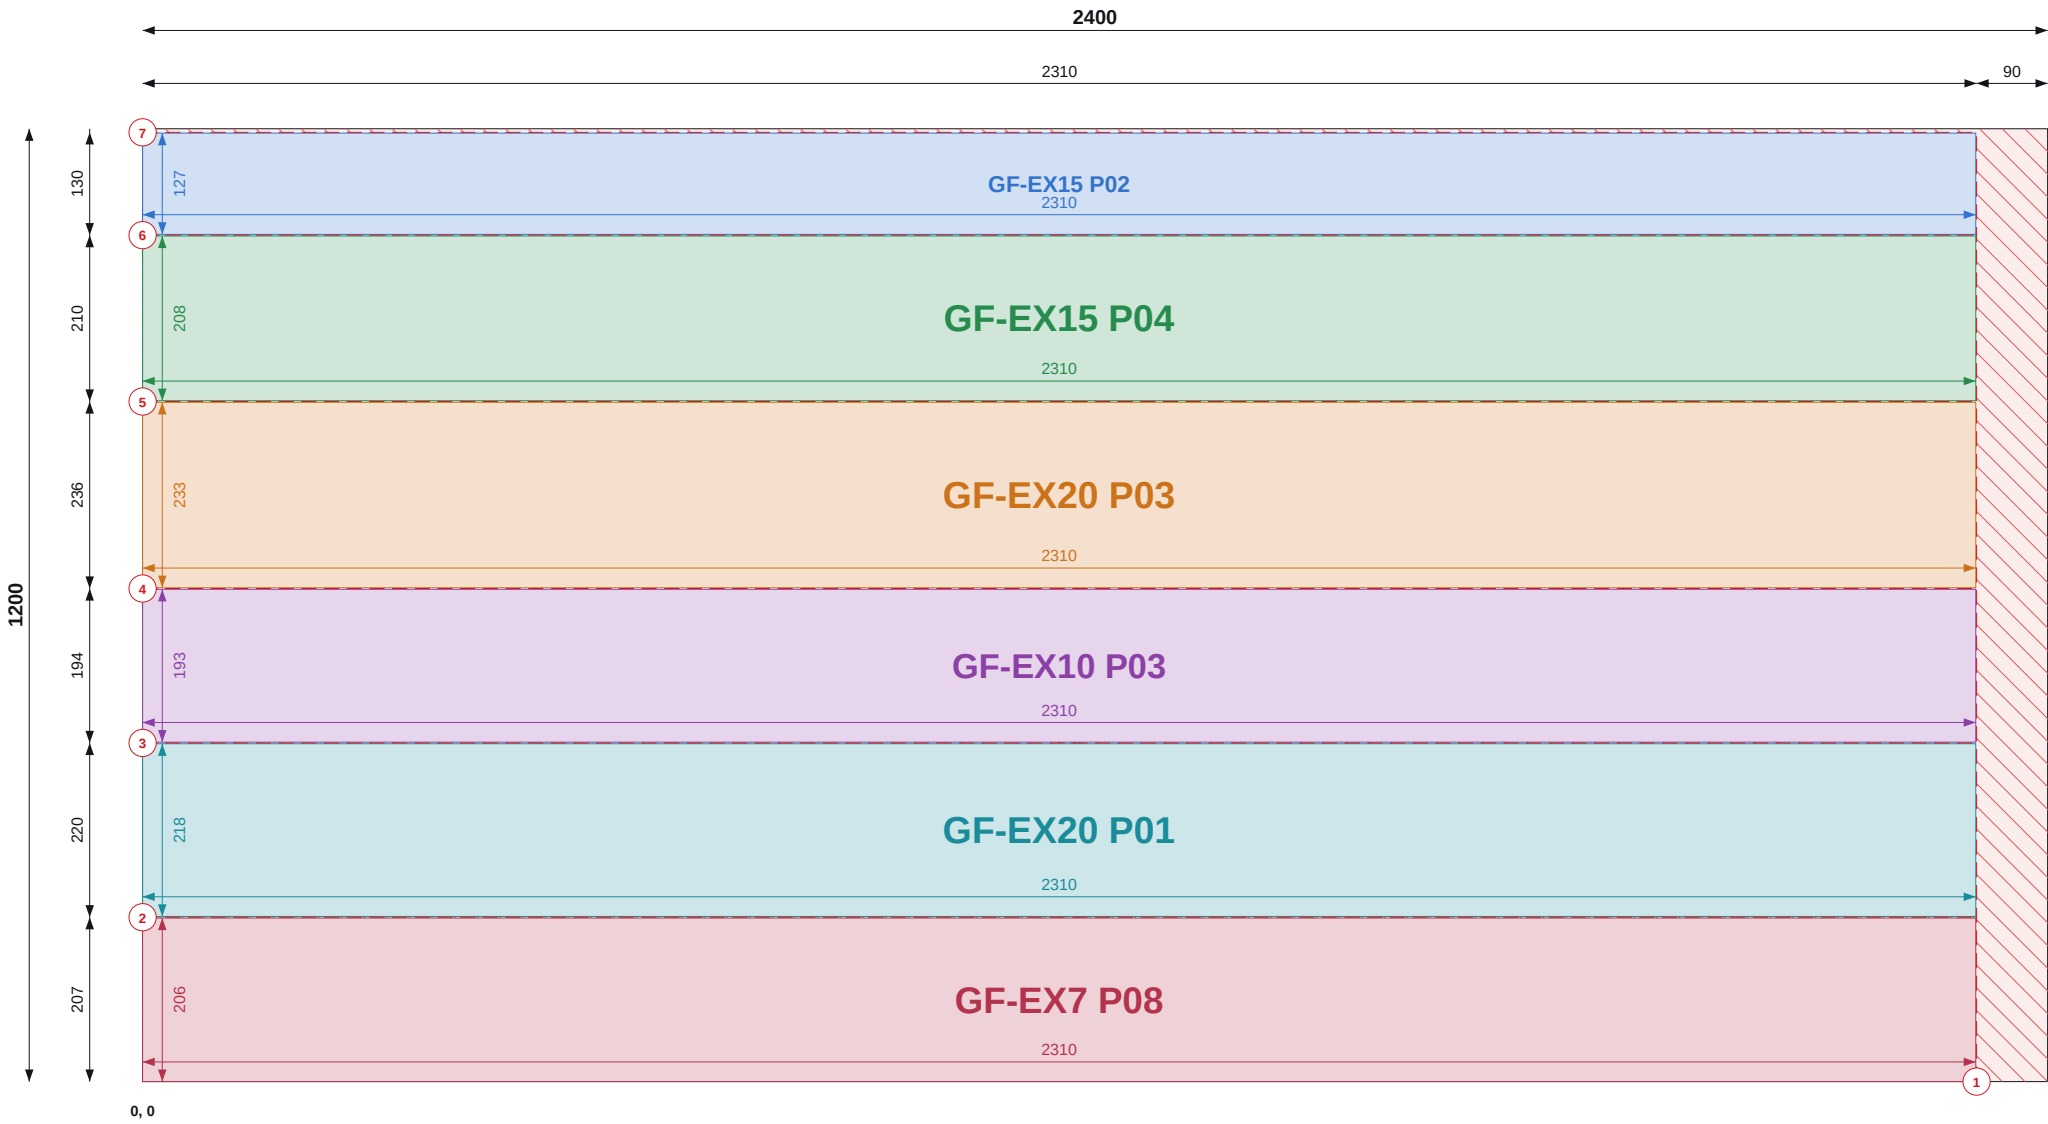

Top / left chains = saw cut positions (to cut centres). Coloured = part size and position.

## SHEET 16 OF 21

### THIS SHEET

| Item              | Value           |
|-------------------|-----------------|
| Parts             | 6               |
| Used / waste      | 95.0% / 0.14 m2 |
| Reusable offcuts  | 0               |
| Saw cuts / shared | 7 / 5           |

### PIECES (POSITION = BOTTOM-LEFT CORNER)

| Label       | Size       | X, Y    |
|-------------|------------|---------|
| GF-EX15 P02 | 127 x 2310 | 0, 1067 |
| GF-EX15 P04 | 208 x 2310 | 0, 857  |
| GF-EX20 P03 | 233 x 2310 | 0, 622  |
| GF-EX10 P03 | 193 x 2310 | 0, 427  |
| GF-EX20 P01 | 218 x 2310 | 0, 208  |
| GF-EX7 P08  | 206 x 2310 | 0, 0    |

### NOTES

- Cut from PIR 120mm 1200x2400, 2mm saw kerf. Viewed on the face; dimensions from the sheet's bottom-left corner (0,0). Red numbered lines = saw cuts in order, each edge to edge.
- Coloured dimensions belong to the part of that colour: its width and height, and its position from the sheet edges. Raked parts: corner coordinates at each corner.
- Red hatch = waste. Labels = panel + piece mark on the manufacture drawing.

### REVISIONS

| REV | DATE     | DESCRIPTION        |
|-----|----------|--------------------|
| C01 | 13.09.26 | Construction issue |



TLS TIMBER FRAME

Design & Manufacture

Scan: 3D model + drawings



|          |                            |
|----------|----------------------------|
| CLIENT   | PROJECT                    |
| MP Adams | MP Adams Plot 3, Eckington |


|                                             |
|---------------------------------------------|
| DRAWING TITLE                               |
| PIR CUTTING - GROUND FLOOR - SHEET 16 OF 21 |

PIR 120mm 1200x2400 | Ground Floor

|       |      |          |       |
|-------|------|----------|-------|
| SCALE | SIZE | DATE     | DRAWN |
| NTS   | A3   | 13.09.26 | TS    |

|              |                   |     |
|--------------|-------------------|-----|
| STATUS       | DRAWING No.       | REV |
| CONSTRUCTION | P3-CP-PIR-01 / 16 | C01 |

Do not scale. All dimensions in mm. Check all dimensions on site.

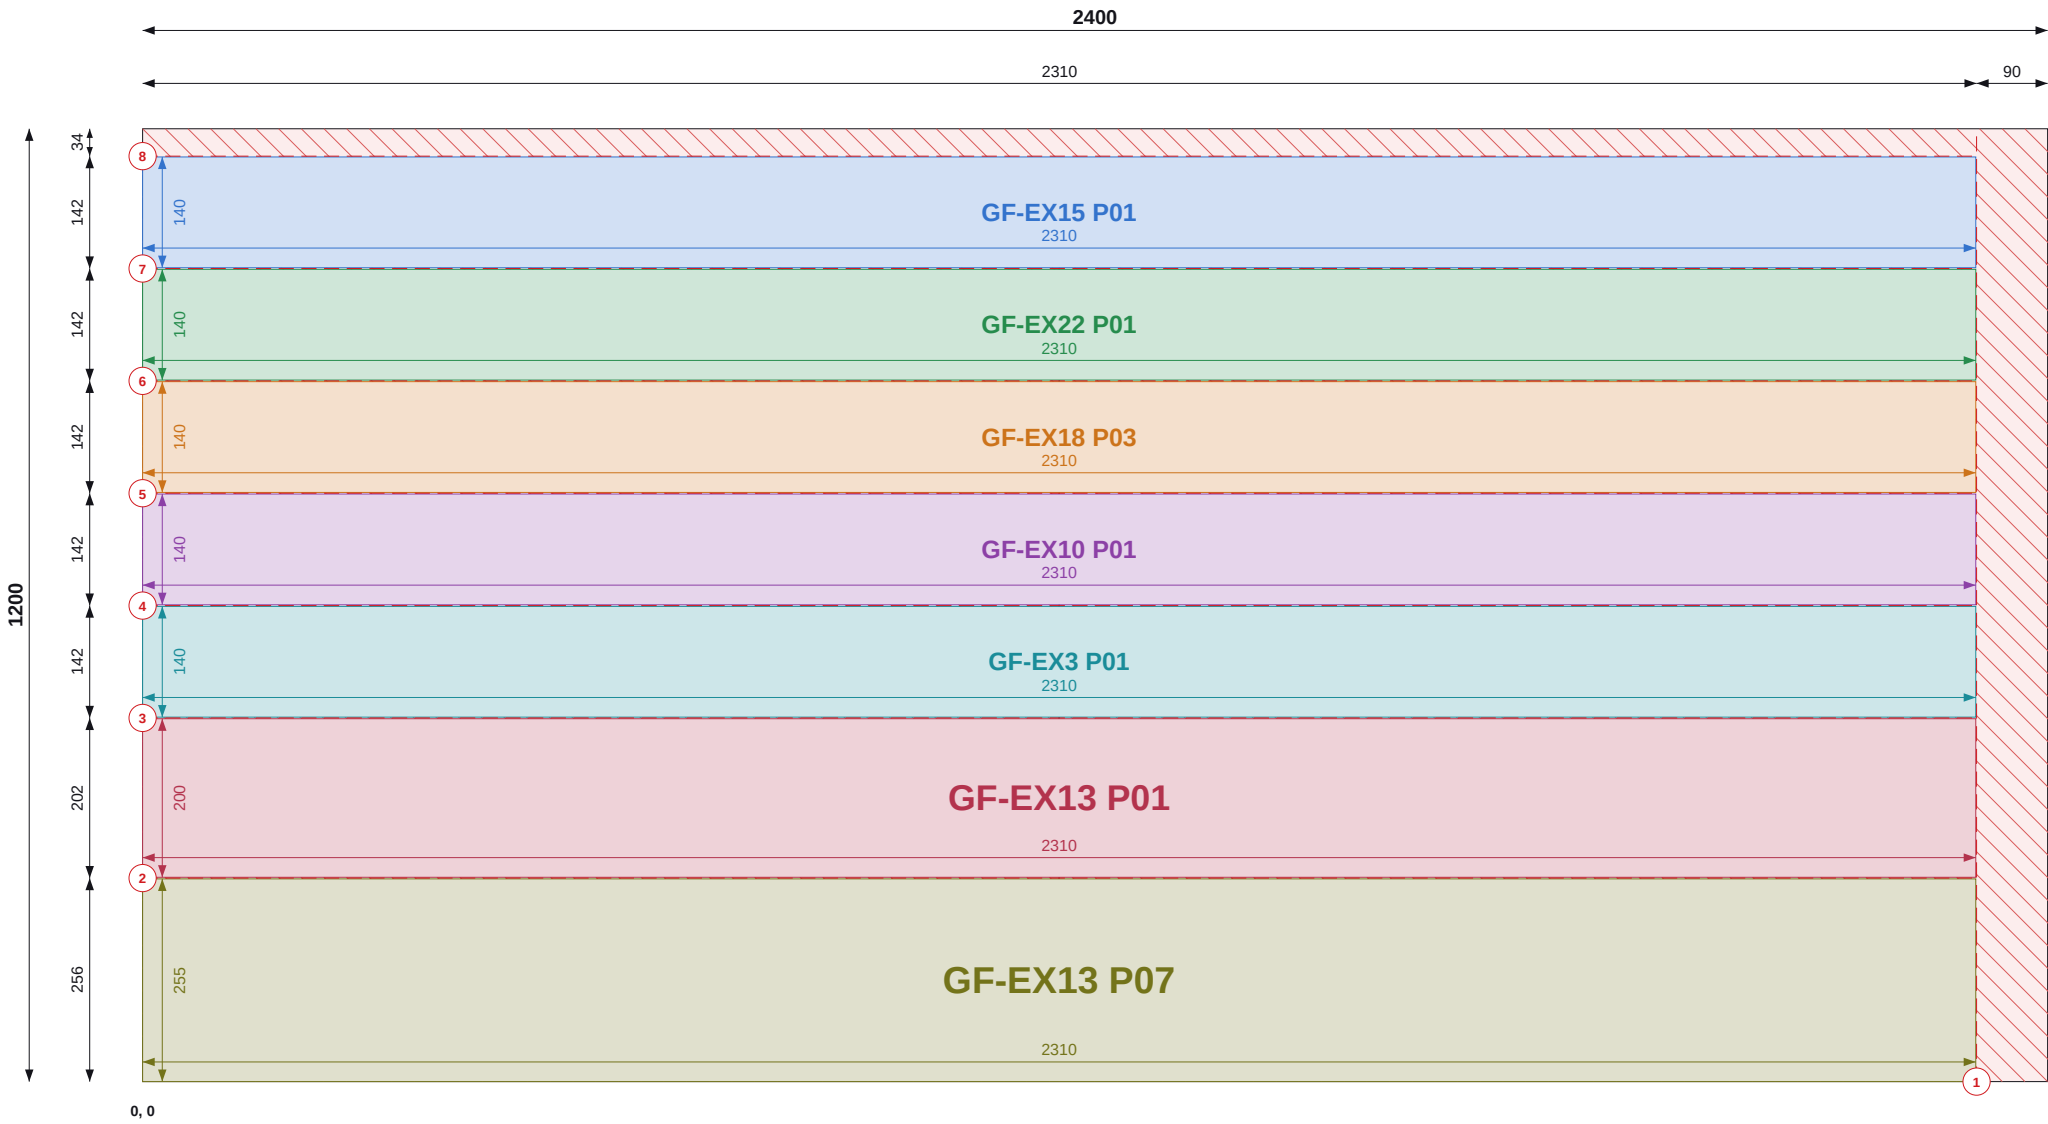

Top / left chains = saw cut positions (to cut centres). Coloured = part size and position.

SHEET 17 OF 21

THIS SHEET

| Item              | Value           |
|-------------------|-----------------|
| Parts             | 7               |
| Used / waste      | 92.4% / 0.22 m2 |
| Reusable offcuts  | 0               |
| Saw cuts / shared | 8 / 6           |

PIECES (POSITION = BOTTOM-LEFT CORNER)

| Label       | Size       | X, Y    |
|-------------|------------|---------|
| GF-EX15 P01 | 140 x 2310 | 0, 1025 |
| GF-EX22 P01 | 140 x 2310 | 0, 883  |
| GF-EX18 P03 | 140 x 2310 | 0, 742  |
| GF-EX10 P01 | 140 x 2310 | 0, 600  |
| GF-EX3 P01  | 140 x 2310 | 0, 459  |
| GF-EX13 P01 | 200 x 2310 | 0, 257  |
| GF-EX13 P07 | 255 x 2310 | 0, 0    |

NOTES

- Cut from PIR 120mm 1200x2400, 2mm saw kerf. Viewed on the face; dimensions from the sheet's bottom-left corner (0,0). Red numbered lines = saw cuts in order, each edge to edge.
- Coloured dimensions belong to the part of that colour: its width and height, and its position from the sheet edges. Raked parts: corner coordinates at each corner.
- Red hatch = waste. Labels = panel + piece mark on the manufacture drawing.

REVISIONS

| REV | DATE     | DESCRIPTION        |
|-----|----------|--------------------|
| C01 | 13.09.26 | Construction issue |



TLS TIMBER FRAME

Design & Manufacture

Scan: 3D model + drawings




|          |                            |
|----------|----------------------------|
| CLIENT   | PROJECT                    |
| MP Adams | MP Adams Plot 3, Eckington |

|                                             |  |  |  |
|---------------------------------------------|--|--|--|
| DRAWING TITLE                               |  |  |  |
| PIR CUTTING - GROUND FLOOR - SHEET 17 OF 21 |  |  |  |
| PIR 120mm 1200x2400   Ground Floor          |  |  |  |

|       |      |          |       |
|-------|------|----------|-------|
| SCALE | SIZE | DATE     | DRAWN |
| NTS   | A3   | 13.09.26 | TS    |

|              |                   |     |
|--------------|-------------------|-----|
| STATUS       | DRAWING No.       | REV |
| CONSTRUCTION | P3-CP-PIR-01 / 17 | C01 |

Do not scale. All dimensions in mm. Check all dimensions on site.

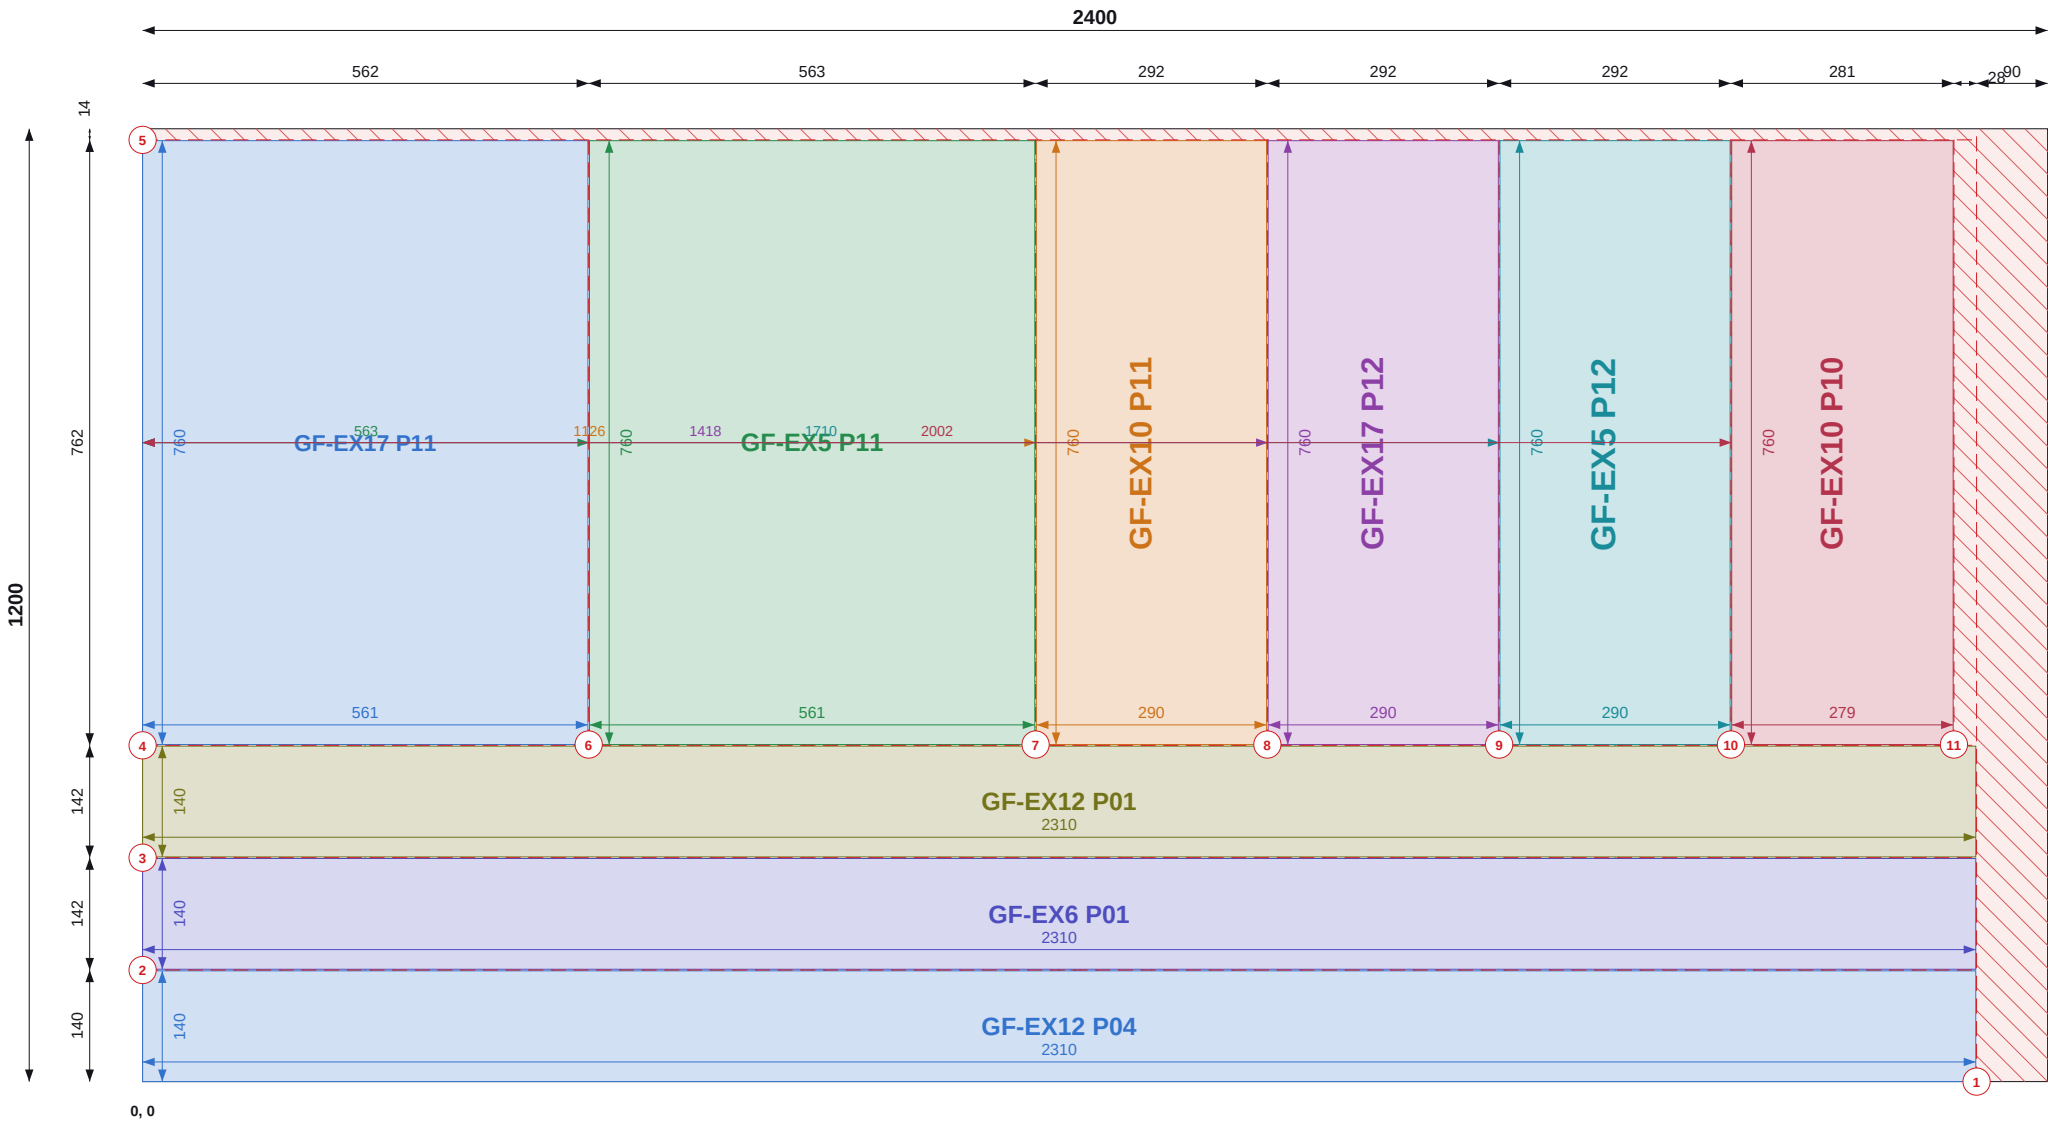

Top / left chains = saw cut positions (to cut centres). Coloured = part size and position.

SHEET 18 OF 21

THIS SHEET

| Item              | Value           |
|-------------------|-----------------|
| Parts             | 9               |
| Used / waste      | 93.5% / 0.19 m2 |
| Reusable offcuts  | 0               |
| Saw cuts / shared | 11 / 8          |

PIECES (POSITION = BOTTOM-LEFT CORNER)

| Label       | Size       | X, Y      |
|-------------|------------|-----------|
| GF-EX17 P11 | 561 x 760  | 0, 425    |
| GF-EX5 P11  | 561 x 760  | 563, 425  |
| GF-EX10 P11 | 290 x 760  | 1126, 425 |
| GF-EX17 P12 | 290 x 760  | 1418, 425 |
| GF-EX5 P12  | 290 x 760  | 1710, 425 |
| GF-EX10 P10 | 279 x 760  | 2002, 425 |
| GF-EX12 P01 | 140 x 2310 | 0, 283    |
| GF-EX6 P01  | 140 x 2310 | 0, 142    |
| GF-EX12 P04 | 140 x 2310 | 0, 0      |

NOTES

- Cut from PIR 120mm 1200x2400, 2mm saw kerf. Viewed on the face; dimensions from the sheet's bottom-left corner (0,0). Red numbered lines = saw cuts in order, each edge to edge.
- Coloured dimensions belong to the part of that colour: its width and height, and its position from the sheet edges. Raked parts: corner coordinates at each corner.
- Red hatch = waste. Labels = panel + piece mark on the manufacture drawing.

REVISIONS

| REV | DATE     | DESCRIPTION        |
|-----|----------|--------------------|
| C01 | 13.09.26 | Construction issue |



TLS TIMBER FRAME

Design & Manufacture

Scan: 3D model + drawings



CLIENT

MP Adams

PROJECT

MP Adams Plot 3, Eckington

DRAWING TITLE


PIR CUTTING - GROUND FLOOR - SHEET 18 OF 21

PIR 120mm 1200x2400 | Ground Floor

| SCALE | SIZE | DATE     | DRAWN |
|-------|------|----------|-------|
| NTS   | A3   | 13.09.26 | TS    |

| STATUS       | DRAWING No.       | REV |
|--------------|-------------------|-----|
| CONSTRUCTION | P3-CP-PIR-01 / 18 | C01 |

Do not scale. All dimensions in mm. Check all dimensions on site.

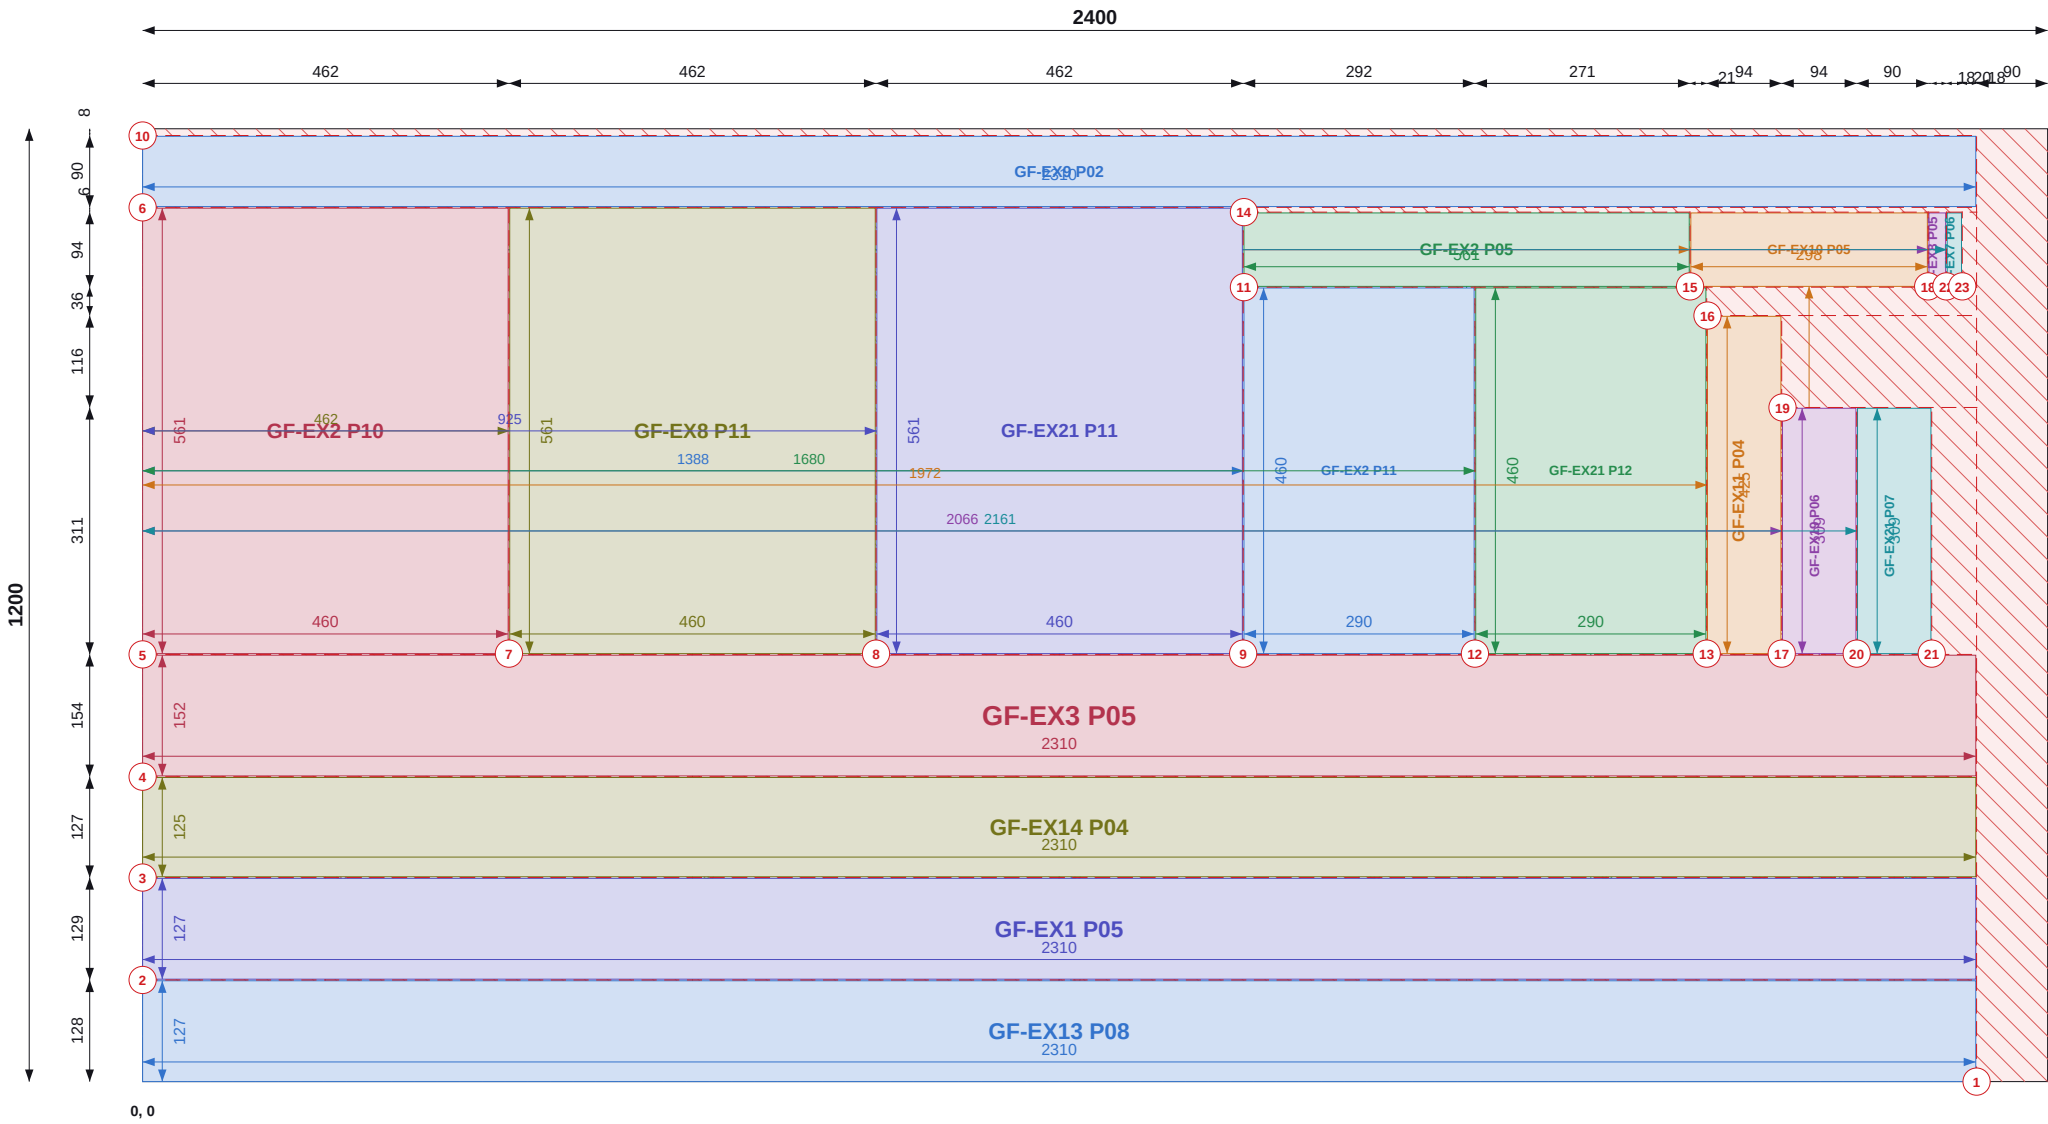

Top / left chains = saw cut positions (to cut centres). Coloured = part size and position.

SHEET 19 OF 21

THIS SHEET

| Item              | Value           |
|-------------------|-----------------|
| Parts             | 17              |
| Used / waste      | 92.1% / 0.23 m2 |
| Reusable offcuts  | 0               |
| Saw cuts / shared | 23 / 16         |

PIECES (POSITION = BOTTOM-LEFT CORNER)

| Label       | Size       | X, Y       |
|-------------|------------|------------|
| GF-EX9 P02  | 89 x 2310  | 0, 1102    |
| GF-EX2 P05  | 561 x 93   | 1388, 1001 |
| GF-EX10 P05 | 298 x 93   | 1951, 1001 |
| GF-EX8 P05  | 21 x 93    | 2251, 1001 |
| GF-EX7 P06  | 18 x 93    | 2274, 1001 |
| GF-EX2 P10  | 561 x 460  | 0, 539     |
| GF-EX8 P11  | 561 x 460  | 462, 539   |
| GF-EX21 P11 | 561 x 460  | 925, 539   |
| GF-EX2 P11  | 290 x 460  | 1388, 539  |
| GF-EX21 P12 | 290 x 460  | 1680, 539  |
| GF-EX11 P04 | 425 x 93   | 1972, 539  |
| GF-EX19 P06 | 309 x 93   | 2066, 539  |
| GF-EX21 P07 | 309 x 93   | 2161, 539  |
| GF-EX3 P05  | 152 x 2310 | 0, 385     |
| GF-EX14 P04 | 125 x 2310 | 0, 258     |
| GF-EX1 P05  | 127 x 2310 | 0, 129     |
| GF-EX13 P08 | 127 x 2310 | 0, 0       |

NOTES

- Cut from PIR 120mm 1200x2400, 2mm saw kerf. Viewed on the face; dimensions from the sheet's bottom-left corner (0,0). Red numbered lines = saw cuts in order, each edge to edge.
- Coloured dimensions belong to the part of that colour: its width and height, and its position from the sheet edges. Raked parts: corner coordinates at each corner.
- Red hatch = waste. Labels = panel + piece mark on the manufacture drawing.

REVISIONS

| REV | DATE     | DESCRIPTION        |
|-----|----------|--------------------|
| C01 | 13.09.26 | Construction issue |



TLS TIMBER FRAME

Design & Manufacture

Scan: 3D model + drawings



CLIENT

MP Adams

PROJECT

MP Adams Plot 3, Eckington

DRAWING TITLE


PIR CUTTING - GROUND FLOOR - SHEET 19 OF 21

PIR 120mm 1200x2400 | Ground Floor

| SCALE | SIZE | DATE     | DRAWN |
|-------|------|----------|-------|
| NTS   | A3   | 13.09.26 | TS    |

| STATUS       | DRAWING No.       | REV |
|--------------|-------------------|-----|
| CONSTRUCTION | P3-CP-PIR-01 / 19 | C01 |

Do not scale. All dimensions in mm. Check all dimensions on site.

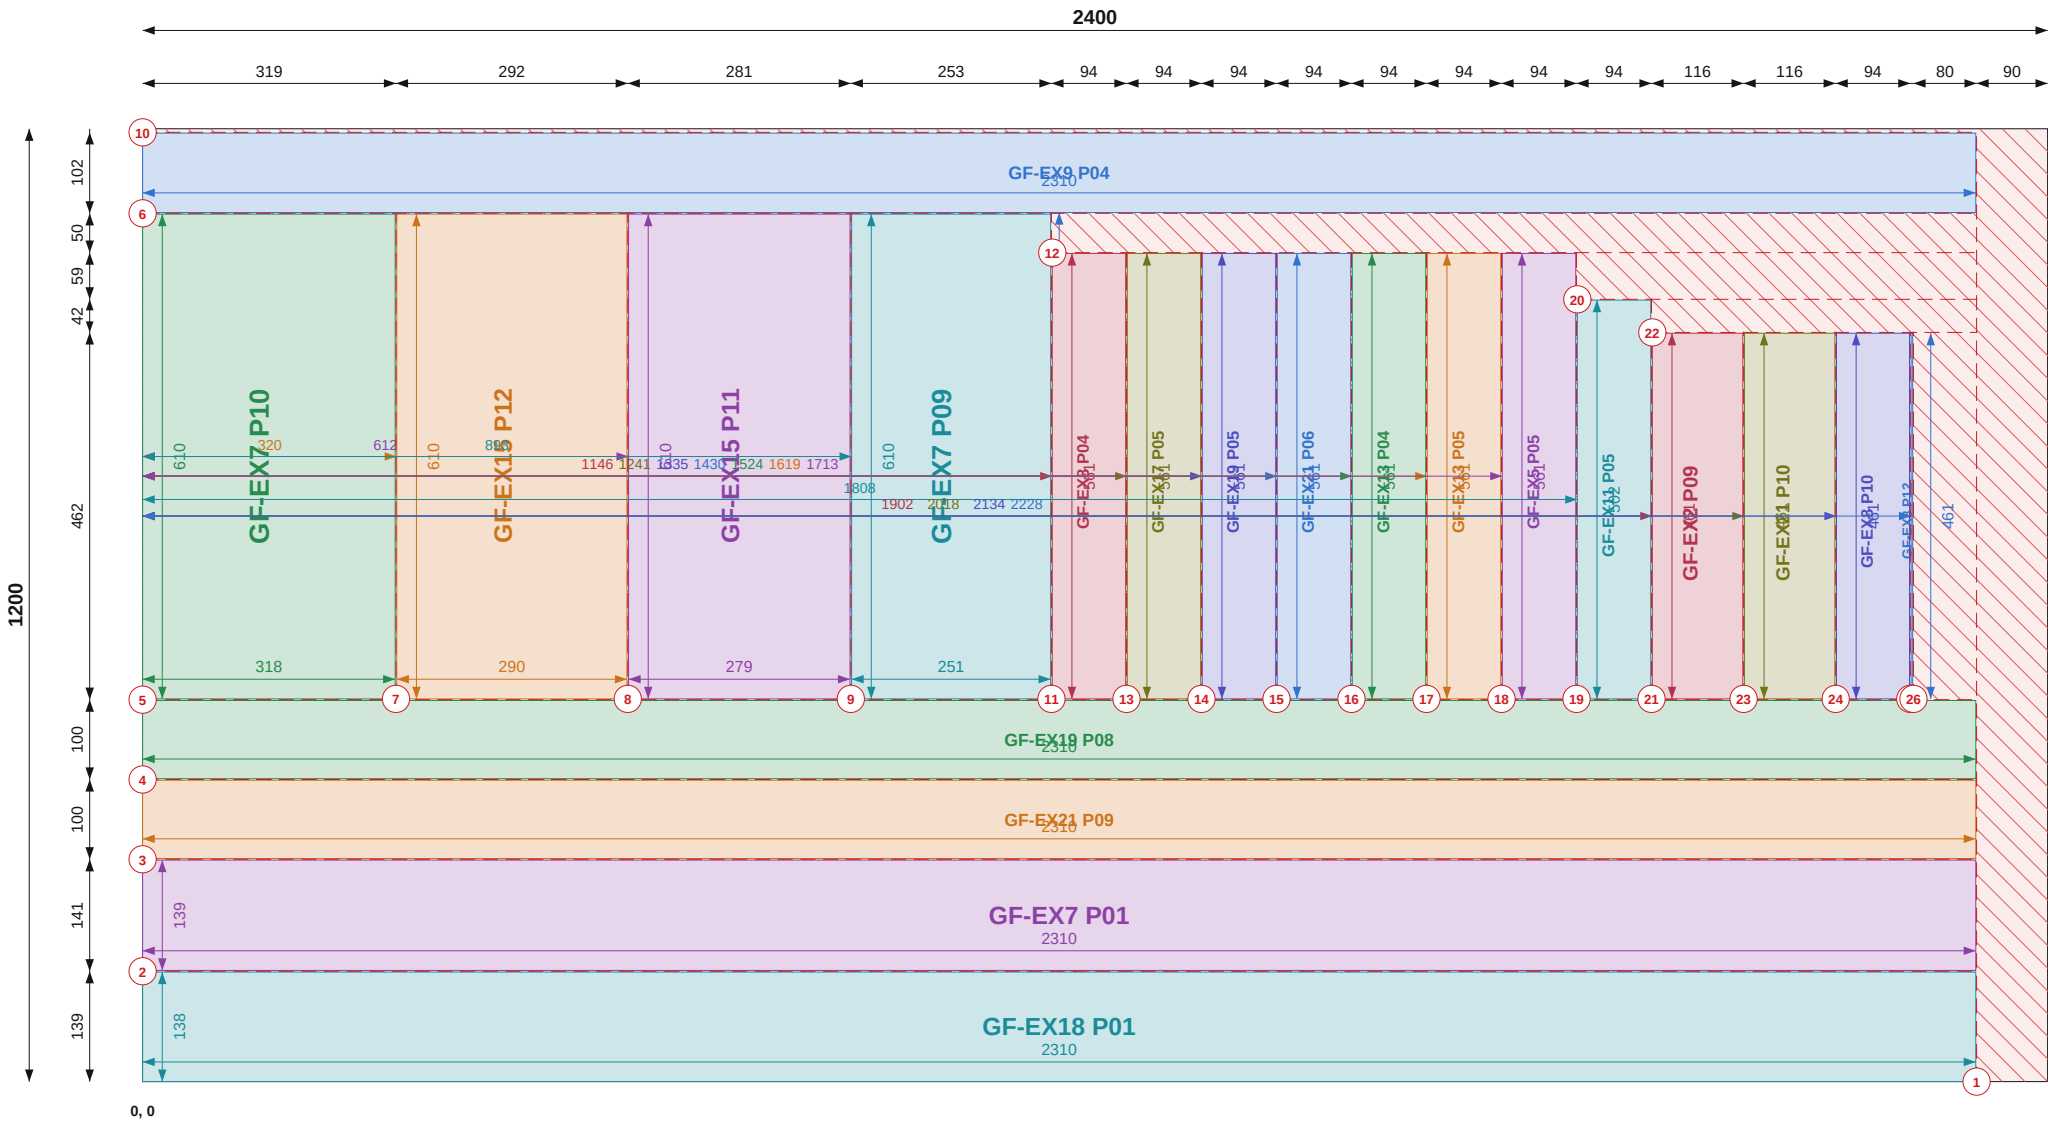

SHEET 20 OF 21

THIS SHEET

| Item              | Value           |
|-------------------|-----------------|
| Parts             | 21              |
| Used / waste      | 89.5% / 0.30 m2 |
| Reusable offcuts  | 0               |
| Saw cuts / shared | 26 / 20         |

PIECES (POSITION = BOTTOM-LEFT CORNER)

| Label       | Size       | X, Y      |
|-------------|------------|-----------|
| GF-EX9 P04  | 100 x 2310 | 0, 1095   |
| GF-EX7 P10  | 318 x 610  | 0, 482    |
| GF-EX15 P12 | 290 x 610  | 320, 482  |
| GF-EX15 P11 | 279 x 610  | 612, 482  |
| GF-EX7 P09  | 251 x 610  | 893, 482  |
| GF-EX8 P04  | 561 x 93   | 1146, 482 |
| GF-EX17 P05 | 561 x 93   | 1241, 482 |
| GF-EX19 P05 | 561 x 93   | 1335, 482 |
| GF-EX21 P06 | 561 x 93   | 1430, 482 |
| GF-EX13 P04 | 561 x 93   | 1524, 482 |
| GF-EX13 P05 | 561 x 93   | 1619, 482 |
| GF-EX5 P05  | 561 x 93   | 1713, 482 |
| GF-EX11 P05 | 502 x 93   | 1808, 482 |
| GF-EX2 P09  | 114 x 460  | 1902, 482 |
| GF-EX21 P10 | 114 x 460  | 2018, 482 |
| GF-EX8 P10  | 92 x 460   | 2134, 482 |
| GF-EX8 P12  | 2 x 460    | 2228, 482 |
| GF-EX19 P08 | 99 x 2310  | 0, 382    |
| GF-EX21 P09 | 99 x 2310  | 0, 281    |
| GF-EX7 P01  | 139 x 2310 | 0, 140    |
| GF-EX18 P01 | 138 x 2310 | 0, 0      |

NOTES

- Cut from PIR 120mm 1200x2400, 2mm saw kerf. Viewed on the face; dimensions from the sheet's bottom-left corner (0,0). Red numbered lines = saw cuts in order, each edge to edge.
- Coloured dimensions belong to the part of that colour: its width and height, and its position from the sheet edges. Raked parts: corner coordinates at each corner.
- Red hatch = waste. Labels = panel + piece mark on the manufacture drawing.

REVISIONS

| REV | DATE     | DESCRIPTION        |
|-----|----------|--------------------|
| C01 | 13.09.26 | Construction issue |



TLS TIMBER FRAME

Design & Manufacture

Scan: 3D model + drawings



|          |                            |
|----------|----------------------------|
| CLIENT   | PROJECT                    |
| MP Adams | MP Adams Plot 3, Eckington |

|                                             |
|---------------------------------------------|
| DRAWING TITLE                               |
| PIR CUTTING - GROUND FLOOR - SHEET 20 OF 21 |

PIR 120mm 1200x2400 | Ground Floor

|       |      |          |       |
|-------|------|----------|-------|
| SCALE | SIZE | DATE     | DRAWN |
| NTS   | A3   | 13.09.26 | TS    |

|              |                   |     |
|--------------|-------------------|-----|
| STATUS       | DRAWING No.       | REV |
| CONSTRUCTION | P3-CP-PIR-01 / 20 | C01 |

| Item              | Value           |
|-------------------|-----------------|
| Parts             | 38              |
| Used / waste      | 29.7% / 2.03 m2 |
| Reusable offcuts  | 1               |
| Saw cuts / shared | 42 / 37         |

## PIECES (POSITION = BOTTOM-LEFT CORNER)

| Label       | Size       | X, Y      |
|-------------|------------|-----------|
| GF-EX15 P07 | 309 x 93   | 0, 987    |
| GF-EX5 P06  | 309 x 93   | 311, 987  |
| GF-EX7 P04  | 270 x 93   | 622, 987  |
| GF-EX2 P04  | 133 x 93   | 894, 987  |
| GF-EX21 P05 | 133 x 93   | 1029, 987 |
| GF-EX17 P04 | 133 x 93   | 1164, 987 |
| GF-EX5 P04  | 133 x 93   | 1299, 987 |
| GF-EX8 P03  | 111 x 93   | 1434, 987 |
| GF-EX7 P03  | 18 x 93    | 1547, 987 |
| GF-EX2 P07  | 18 x 93    | 1567, 987 |
| GF-EX2 P03  | 18 x 93    | 1587, 987 |
| GF-EX11 P06 | 18 x 93    | 1607, 987 |
| GF-EX8 P02  | 18 x 93    | 1627, 987 |
| GF-EX10 P04 | 18 x 93    | 1647, 987 |
| GF-EX10 P07 | 18 x 93    | 1667, 987 |
| GF-EX8 P06  | 18 x 93    | 1687, 987 |
| GF-EX17 P07 | 18 x 93    | 1707, 987 |
| GF-EX17 P03 | 18 x 93    | 1727, 987 |
| GF-EX21 P04 | 18 x 93    | 1747, 987 |
| GF-EX19 P07 | 18 x 93    | 1767, 987 |
| GF-EX21 P08 | 18 x 93    | 1787, 987 |
| GF-EX19 P03 | 18 x 93    | 1807, 987 |
| GF-EX13 P02 | 18 x 93    | 1827, 987 |
| GF-EX13 P06 | 18 x 93    | 1847, 987 |
| GF-EX15 P05 | 18 x 93    | 1867, 987 |
| GF-EX15 P08 | 18 x 93    | 1887, 987 |
| GF-EX5 P07  | 18 x 93    | 1907, 987 |
| GF-EX5 P03  | 18 x 93    | 1927, 987 |
| GF-EX19 P04 | 513 x 93   | 0, 892    |
| GF-EX15 P06 | 298 x 93   | 515, 892  |
| GF-EX7 P05  | 337 x 93   | 815, 892  |
| GF-EX2 P06  | 309 x 93   | 1154, 892 |
| GF-EX10 P06 | 309 x 93   | 1465, 892 |
| GF-EX17 P06 | 309 x 93   | 1776, 892 |
| GF-EX13 P03 | 208 x 93   | 2087, 892 |
| GF-EX17 P10 | 114 x 760  | 0, 130    |
| GF-EX5 P10  | 114 x 760  | 116, 130  |
| GF-EX3 P02  | 128 x 2310 | 0, 0      |

## NOTES

1. Cut from PIR 120mm 1200x2400, 2mm saw kerf. Viewed on the face; dimensions from the sheet's bottom-left corner (0,0). Red numbered lines = saw cuts in order, each edge to edge.
2. Coloured dimensions belong to the part of that colour: its width and height, and its position from the sheet edges. Raked parts: corner coordinates at each corner.
3. Red hatch = waste. Labels = panel + piece mark on the manufacture drawing.

## REVISIONS

| REV | DATE     | DESCRIPTION        |
|-----|----------|--------------------|
| C01 | 13.09.26 | Construction issue |



**TLS TIMBER FRAME**

Design &amp; Manufacture

Scan: 3D model + drawings



|          |                            |
|----------|----------------------------|
| CLIENT   | PROJECT                    |
| MP Adams | MP Adams Plot 3, Eckington |


DRAWING TITLE

**PIR CUTTING - GROUND FLOOR - SHEET 21 OF 21**

PIR 120mm 1200x2400 | Ground Floor


|       |      |          |       |
|-------|------|----------|-------|
| SCALE | SIZE | DATE     | DRAWN |
| NTS   | A3   | 13.09.26 | TS    |

|              |                   |     |
|--------------|-------------------|-----|
| STATUS       | DRAWING No.       | REV |
| CONSTRUCTION | P3-CP-PIR-01 / 21 | C01 |

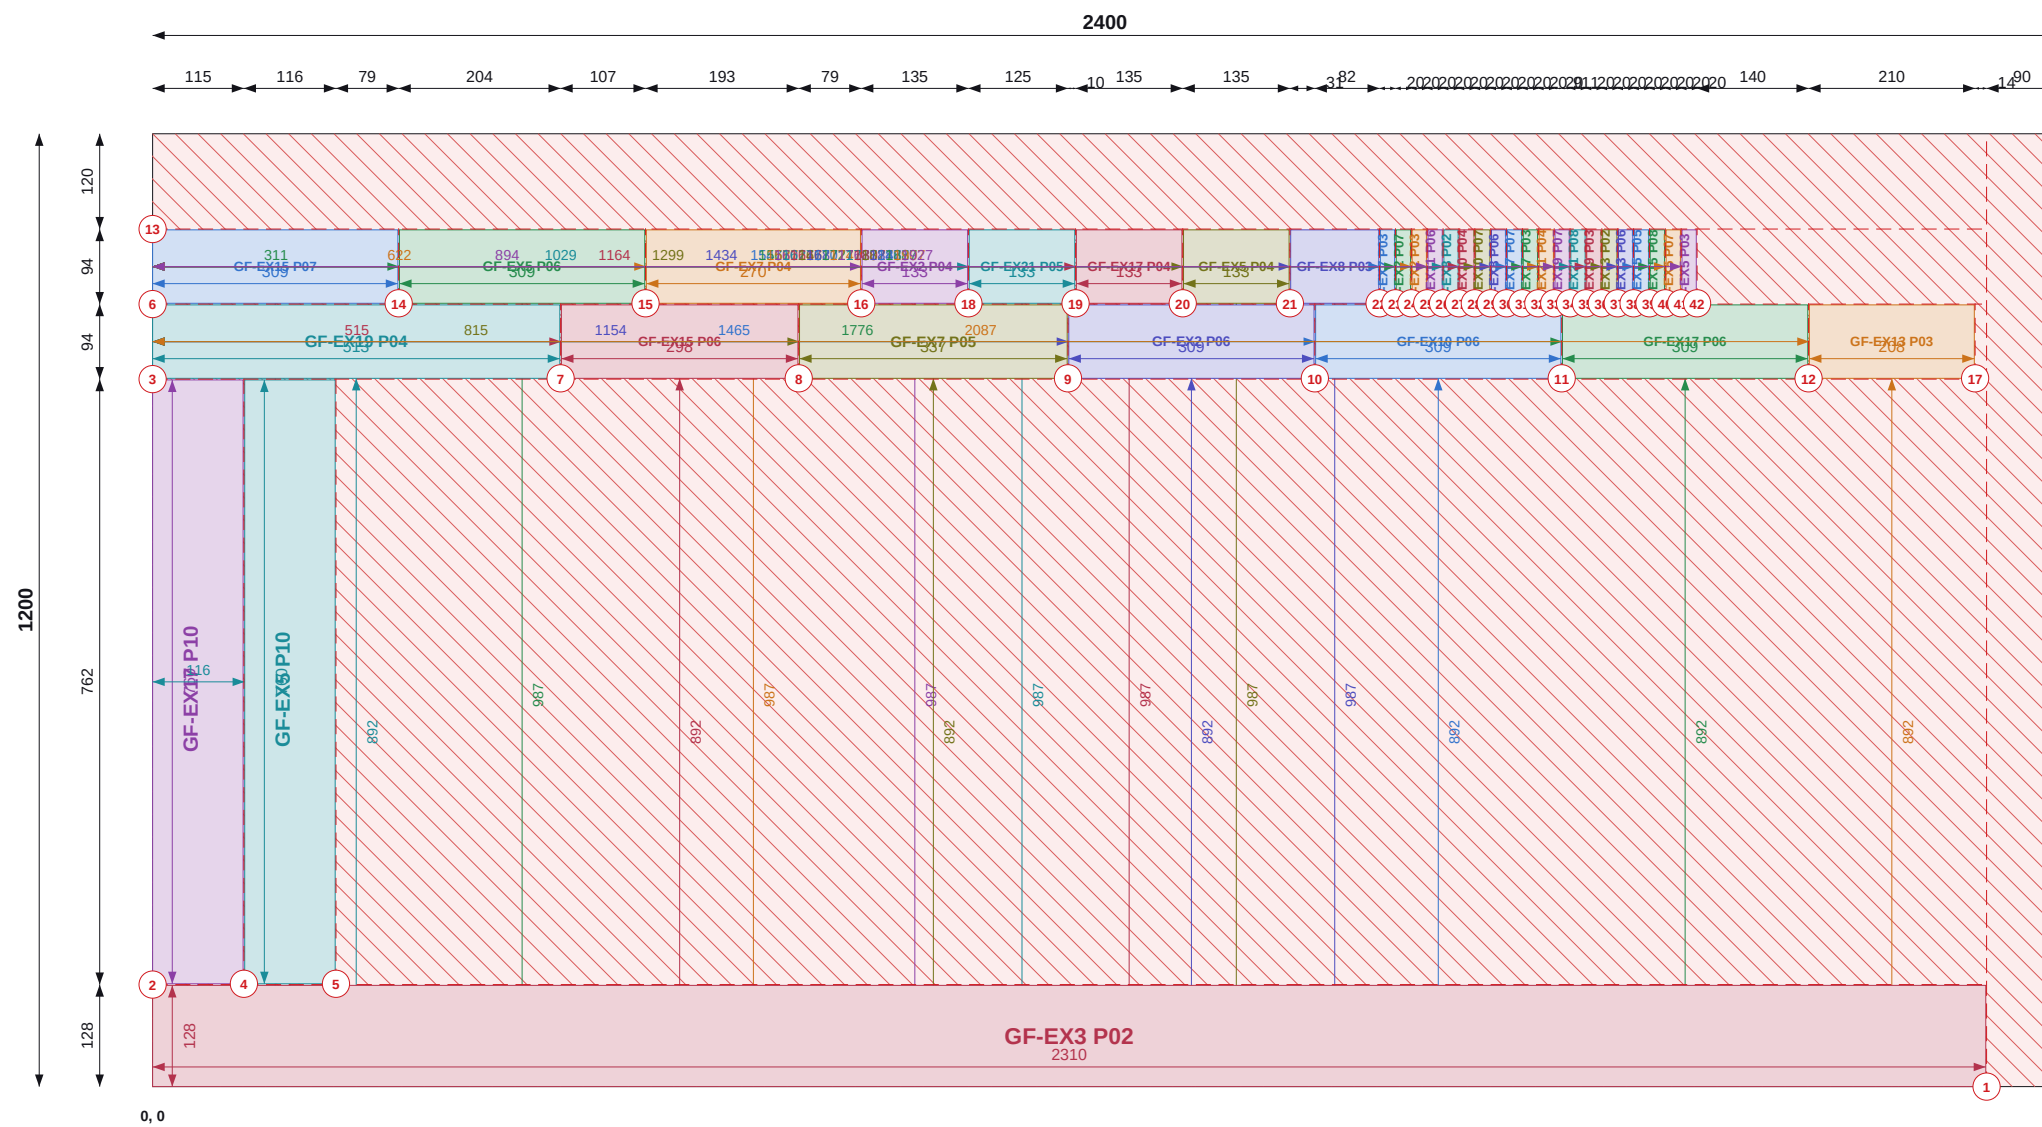

Top / left chains = saw cut positions (to cut centres). Coloured = part size and position.

Do not scale. All dimensions in mm. Check all dimensions on site.

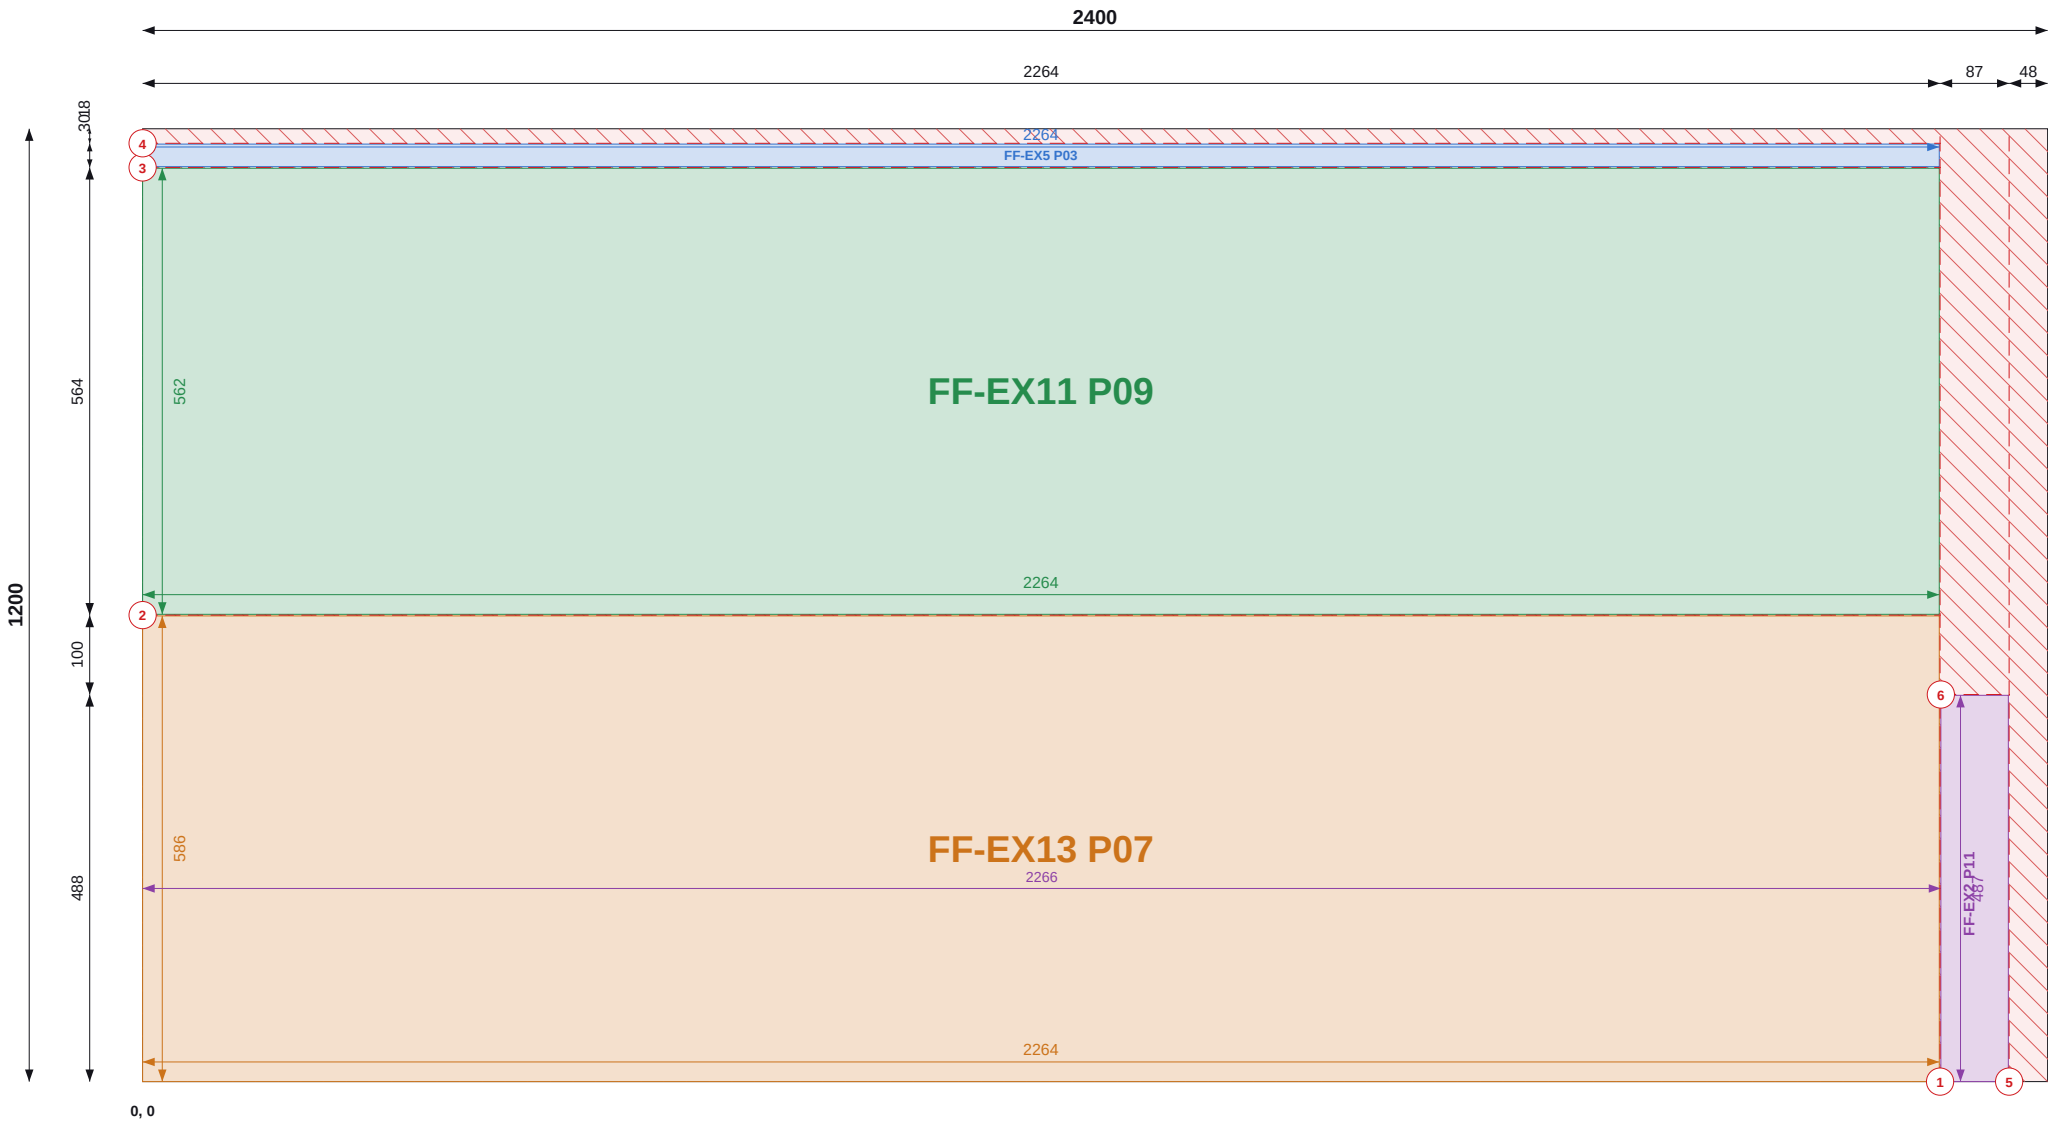

Top / left chains = saw cut positions (to cut centres). Coloured = part size and position.

SHEET 1 OF 23

THIS SHEET

| Item              | Value           |
|-------------------|-----------------|
| Parts             | 4               |
| Used / waste      | 93.9% / 0.18 m2 |
| Reusable offcuts  | 0               |
| Saw cuts / shared | 6 / 3           |

PIECES (POSITION = BOTTOM-LEFT CORNER)

| Label       | Size       | X, Y    |
|-------------|------------|---------|
| FF-EX5 P03  | 28 x 2264  | 0, 1152 |
| FF-EX11 P09 | 562 x 2264 | 0, 588  |
| FF-EX13 P07 | 586 x 2264 | 0, 0    |
| FF-EX2 P11  | 85 x 487   | 2266, 0 |

FIRST FLOOR TOTALS

| Item                              | Value           |
|-----------------------------------|-----------------|
| Sheets / pieces                   | 23 / 164        |
| Yield / waste                     | 90.6% / 6.21 m2 |
| Saw cuts / shared / on stock edge | 195 / 141 / 141 |

NOTES

- Cut from PIR 120mm 1200x2400, 2mm saw kerf. Viewed on the face; dimensions from the sheet's bottom-left corner (0,0). Red numbered lines = saw cuts in order, each edge to edge.
- Coloured dimensions belong to the part of that colour: its width and height, and its position from the sheet edges. Raked parts: corner coordinates at each corner.
- Red hatch = waste. Labels = panel + piece mark on the manufacture drawing.

REVISIONS

| REV | DATE     | DESCRIPTION        |
|-----|----------|--------------------|
| C01 | 13.09.26 | Construction issue |



TLS TIMBER FRAME

Design & Manufacture

Scan: 3D model + drawings



|          |                            |
|----------|----------------------------|
| CLIENT   | PROJECT                    |
| MP Adams | MP Adams Plot 3, Eckington |


DRAWING TITLE  
PIR CUTTING - FIRST FLOOR - SHEET 1 OF 23

PIR 120mm 1200x2400 | First Floor

|       |      |          |       |
|-------|------|----------|-------|
| SCALE | SIZE | DATE     | DRAWN |
| NTS   | A3   | 13.09.26 | TS    |

|              |                   |     |
|--------------|-------------------|-----|
| STATUS       | DRAWING No.       | REV |
| CONSTRUCTION | P3-CP-PIR-02 / 01 | C01 |

Do not scale. All dimensions in mm. Check all dimensions on site.

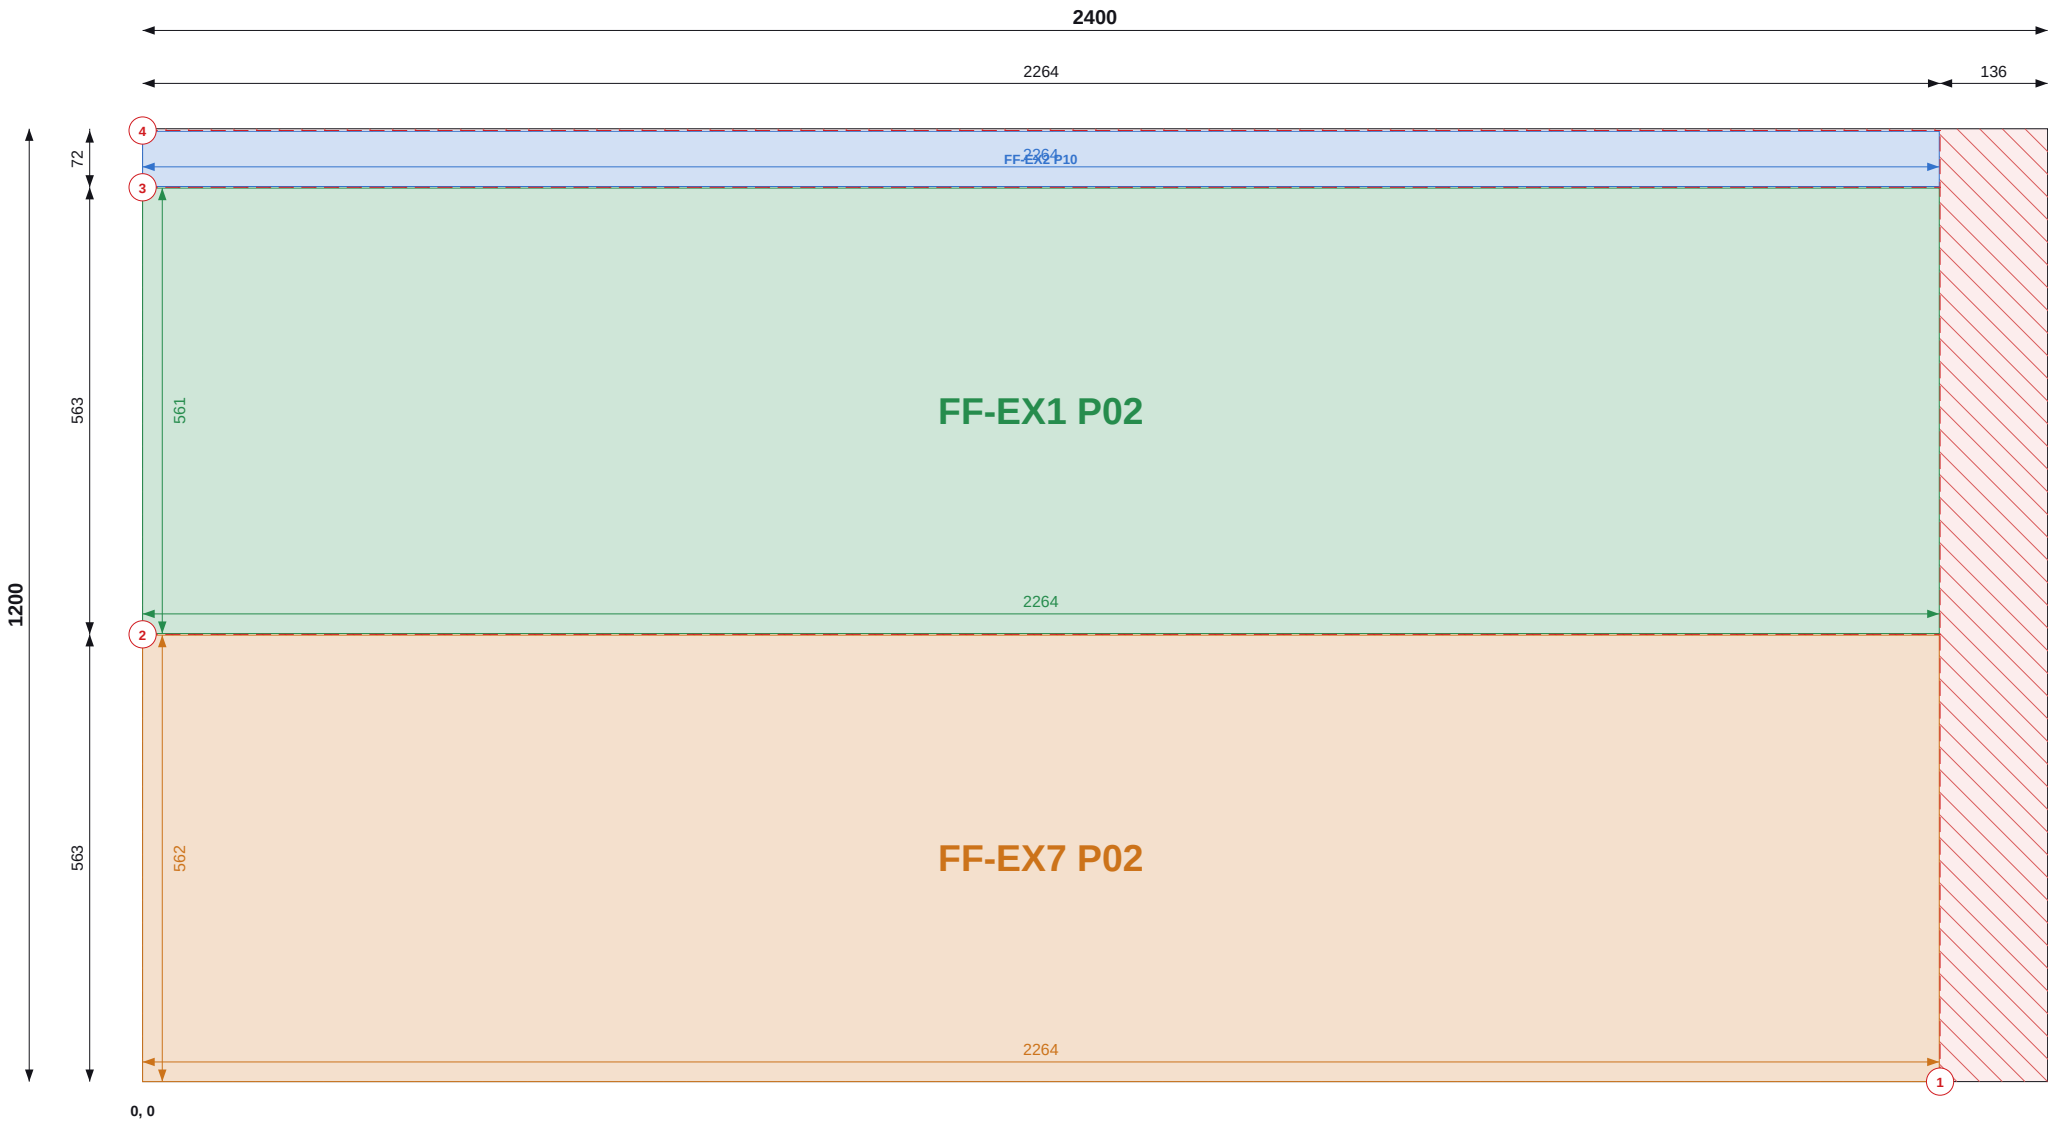

Top / left chains = saw cut positions (to cut centres). Coloured = part size and position.

SHEET 2 OF 23

THIS SHEET

| Item              | Value           |
|-------------------|-----------------|
| Parts             | 3               |
| Used / waste      | 93.7% / 0.18 m2 |
| Reusable offcuts  | 0               |
| Saw cuts / shared | 4 / 2           |

PIECES (POSITION = BOTTOM-LEFT CORNER)

| Label      | Size       | X, Y    |
|------------|------------|---------|
| FF-EX2 P10 | 70 x 2264  | 0, 1127 |
| FF-EX1 P02 | 561 x 2264 | 0, 564  |
| FF-EX7 P02 | 562 x 2264 | 0, 0    |

NOTES

- Cut from PIR 120mm 1200x2400, 2mm saw kerf. Viewed on the face; dimensions from the sheet's bottom-left corner (0,0). Red numbered lines = saw cuts in order, each edge to edge.
- Coloured dimensions belong to the part of that colour: its width and height, and its position from the sheet edges. Raked parts: corner coordinates at each corner.
- Red hatch = waste. Labels = panel + piece mark on the manufacture drawing.

REVISIONS

| REV | DATE     | DESCRIPTION        |
|-----|----------|--------------------|
| C01 | 13.09.26 | Construction issue |



TLS TIMBER FRAME

Design & Manufacture

Scan: 3D model + drawings



|          |                            |
|----------|----------------------------|
| CLIENT   | PROJECT                    |
| MP Adams | MP Adams Plot 3, Eckington |

DRAWING TITLE  
**PIR CUTTING - FIRST FLOOR - SHEET 2 OF 23**

PIR 120mm 1200x2400 | First Floor

|       |      |          |       |
|-------|------|----------|-------|
| SCALE | SIZE | DATE     | DRAWN |
| NTS   | A3   | 13.09.26 | TS    |

|              |                          |            |
|--------------|--------------------------|------------|
| STATUS       | DRAWING No.              | REV        |
| CONSTRUCTION | <b>P3-CP-PIR-02 / 02</b> | <b>C01</b> |

| Item              | Value           |
|-------------------|-----------------|
| Parts             | 3               |
| Used / waste      | 92.9% / 0.20 m2 |
| Reusable offcuts  | 0               |
| Saw cuts / shared | 4 / 2           |

## PIECES (POSITION = BOTTOM-LEFT CORNER)

| Label       | Size       | X, Y    |
|-------------|------------|---------|
| FF-EX15 P09 | 61 x 2264  | 0, 1126 |
| FF-EX1 P04  | 561 x 2264 | 0, 563  |
| FF-EX1 P03  | 561 x 2264 | 0, 0    |

## NOTES

1. Cut from PIR 120mm 1200x2400, 2mm saw kerf. Viewed on the face; dimensions from the sheet's bottom-left corner (0,0). Red numbered lines = saw cuts in order, each edge to edge.
2. Coloured dimensions belong to the part of that colour: its width and height, and its position from the sheet edges. Raked parts: corner coordinates at each corner.
3. Red hatch = waste. Labels = panel + piece mark on the manufacture drawing.

## REVISIONS

| REV | DATE     | DESCRIPTION        |
|-----|----------|--------------------|
| C01 | 13.09.26 | Construction issue |



**TLS TIMBER FRAME**

Design &amp; Manufacture

Scan: 3D model + drawings



|                    |                                       |
|--------------------|---------------------------------------|
| CLIENT<br>MP Adams | PROJECT<br>MP Adams Plot 3, Eckington |
|--------------------|---------------------------------------|

DRAWING TITLE


**PIR CUTTING - FIRST FLOOR - SHEET 3 OF 23**

PIR 120mm 1200x2400 | First Floor

|       |      |          |       |
|-------|------|----------|-------|
| SCALE | SIZE | DATE     | DRAWN |
| NTS   | A3   | 13.09.26 | TS    |


|              |                   |     |
|--------------|-------------------|-----|
| STATUS       | DRAWING No.       | REV |
| CONSTRUCTION | P3-CP-PIR-02 / 03 | C01 |

Do not scale. All dimensions in mm. Check all dimensions on site.

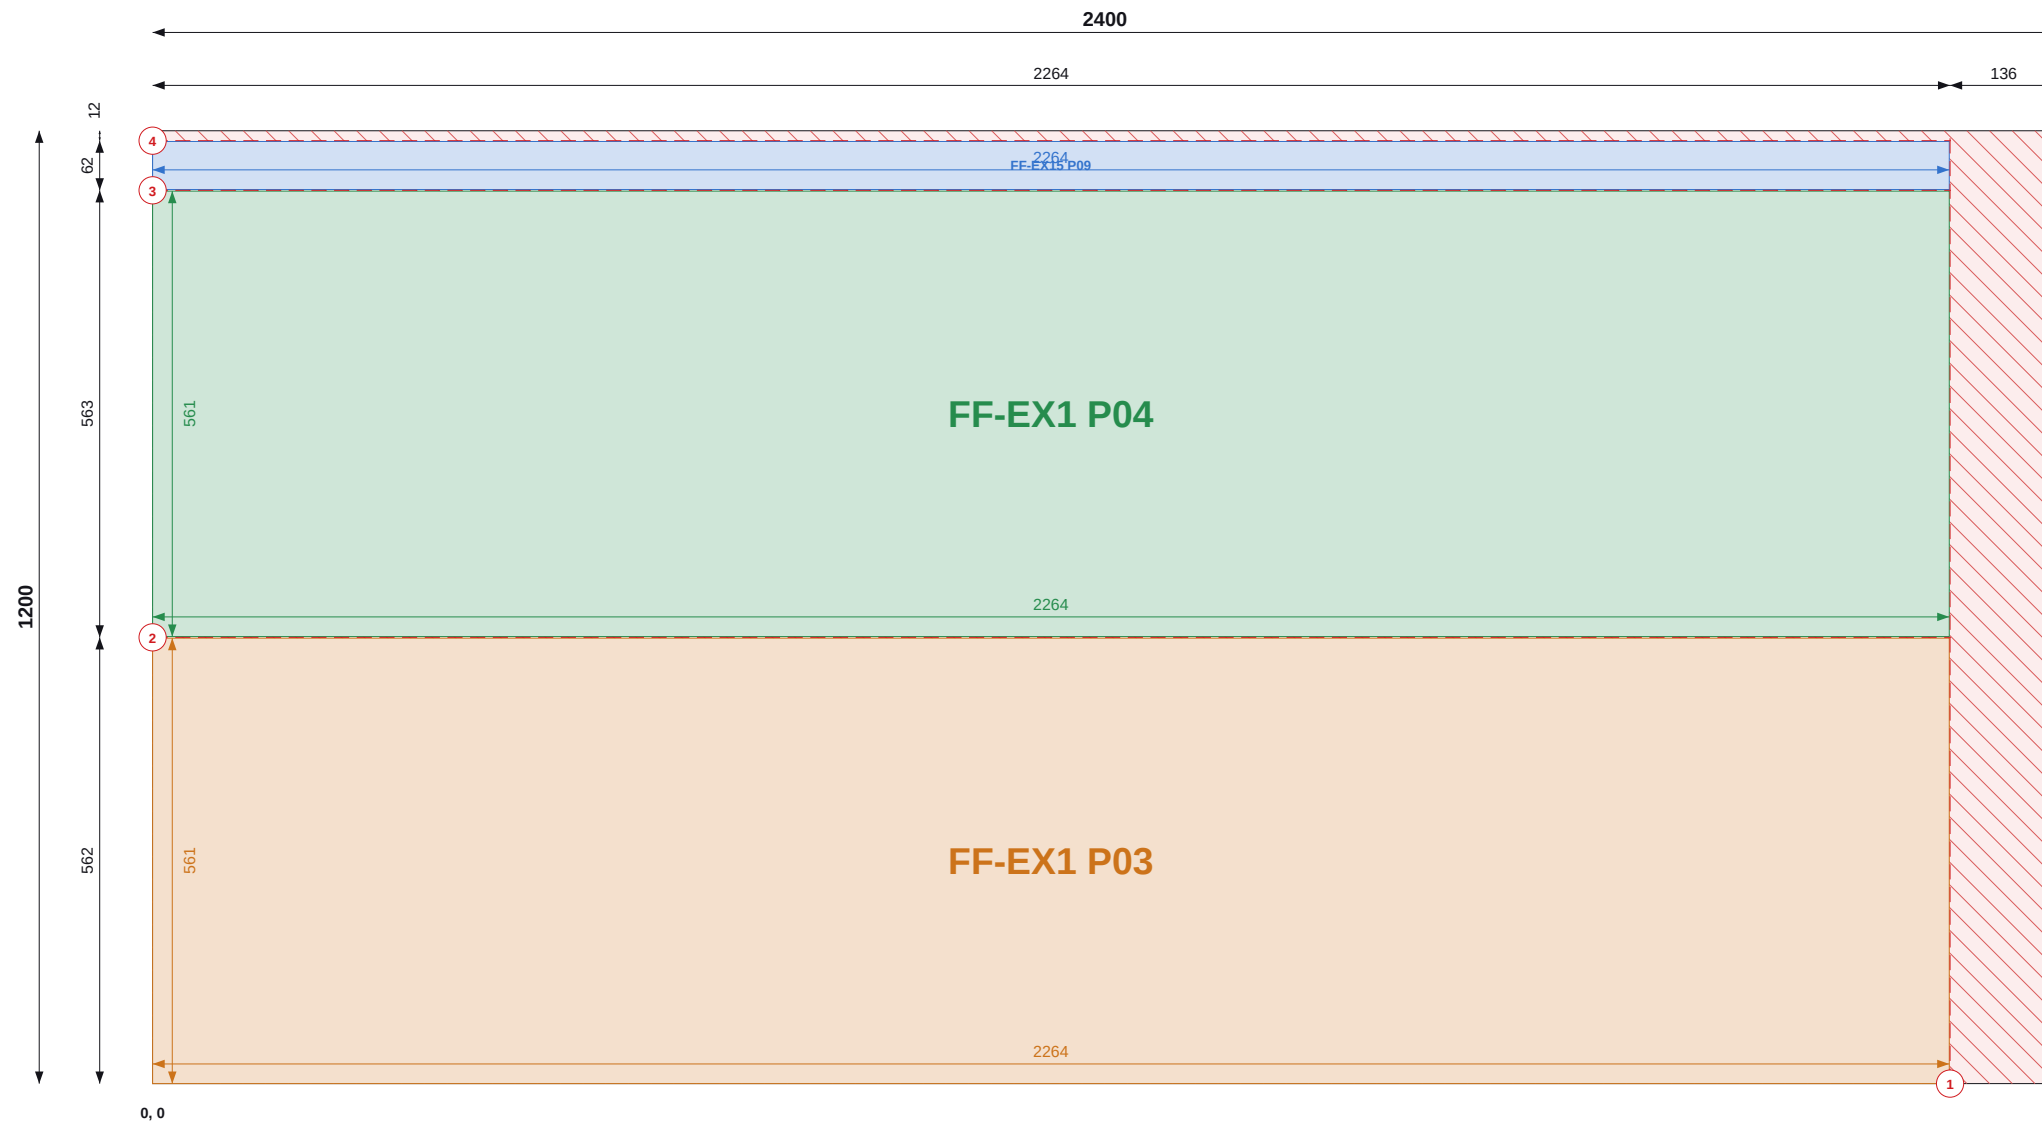

Top / left chains = saw cut positions (to cut centres). Coloured = part size and position.

Do not scale. All dimensions in mm. Check all dimensions on site.

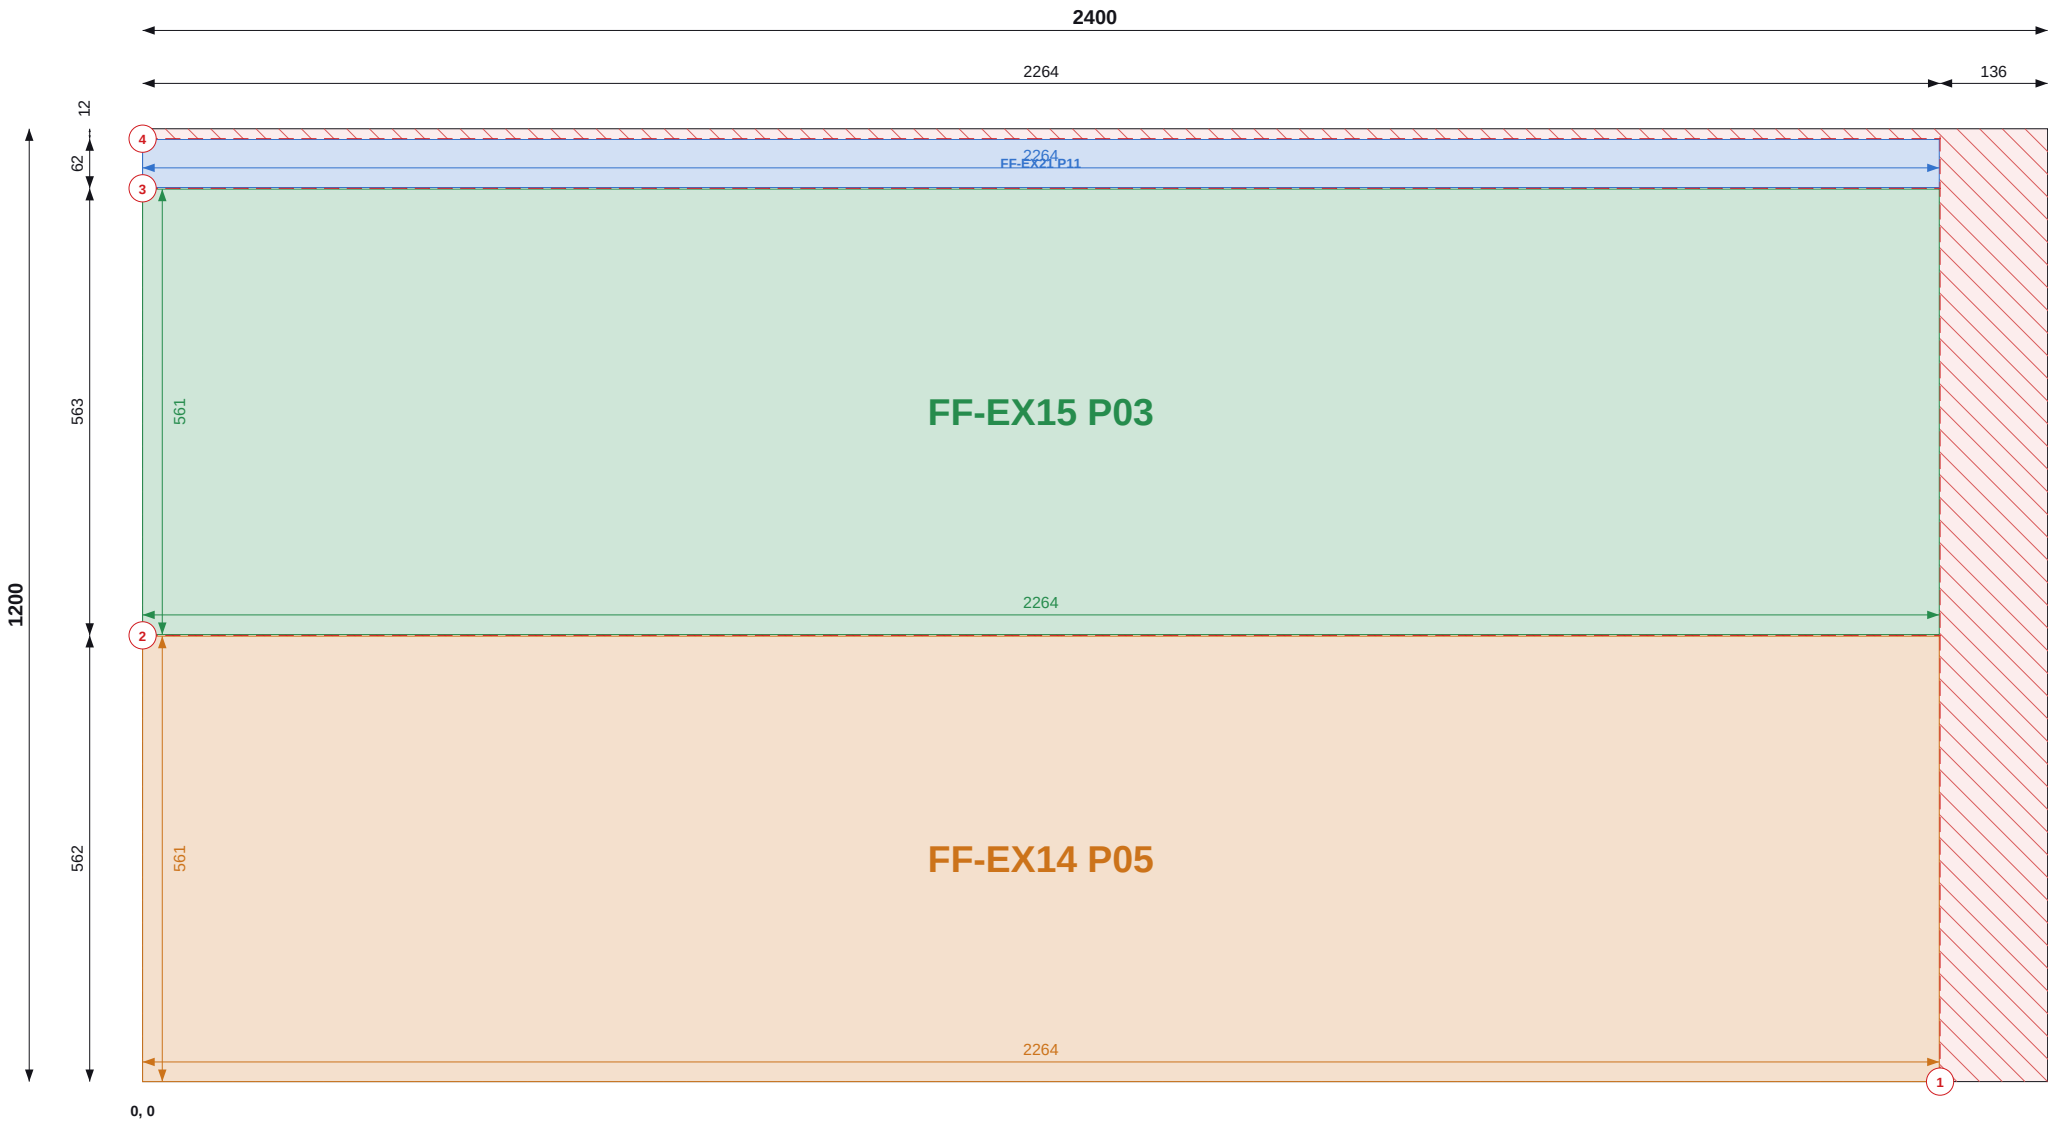

Top / left chains = saw cut positions (to cut centres). Coloured = part size and position.

SHEET 4 OF 23

THIS SHEET

| Item              | Value           |
|-------------------|-----------------|
| Parts             | 3               |
| Used / waste      | 92.9% / 0.20 m2 |
| Reusable offcuts  | 0               |
| Saw cuts / shared | 4 / 2           |

PIECES (POSITION = BOTTOM-LEFT CORNER)

| Label       | Size       | X, Y    |
|-------------|------------|---------|
| FF-EX21 P11 | 61 x 2264  | 0, 1126 |
| FF-EX15 P03 | 561 x 2264 | 0, 563  |
| FF-EX14 P05 | 561 x 2264 | 0, 0    |

NOTES

1. Cut from PIR 120mm 1200x2400, 2mm saw kerf. Viewed on the face; dimensions from the sheet's bottom-left corner (0,0). Red numbered lines = saw cuts in order, each edge to edge.
2. Coloured dimensions belong to the part of that colour: its width and height, and its position from the sheet edges. Raked parts: corner coordinates at each corner.
3. Red hatch = waste. Labels = panel + piece mark on the manufacture drawing.

REVISIONS

| REV | DATE     | DESCRIPTION        |
|-----|----------|--------------------|
| C01 | 13.09.26 | Construction issue |



TLS TIMBER FRAME

Design & Manufacture

Scan: 3D model + drawings



|          |                            |
|----------|----------------------------|
| CLIENT   | PROJECT                    |
| MP Adams | MP Adams Plot 3, Eckington |


|                                           |
|-------------------------------------------|
| DRAWING TITLE                             |
| PIR CUTTING - FIRST FLOOR - SHEET 4 OF 23 |

PIR 120mm 1200x2400 | First Floor

|       |      |          |       |
|-------|------|----------|-------|
| SCALE | SIZE | DATE     | DRAWN |
| NTS   | A3   | 13.09.26 | TS    |

|              |                   |     |
|--------------|-------------------|-----|
| STATUS       | DRAWING No.       | REV |
| CONSTRUCTION | P3-CP-PIR-02 / 04 | C01 |

Do not scale. All dimensions in mm. Check all dimensions on site.

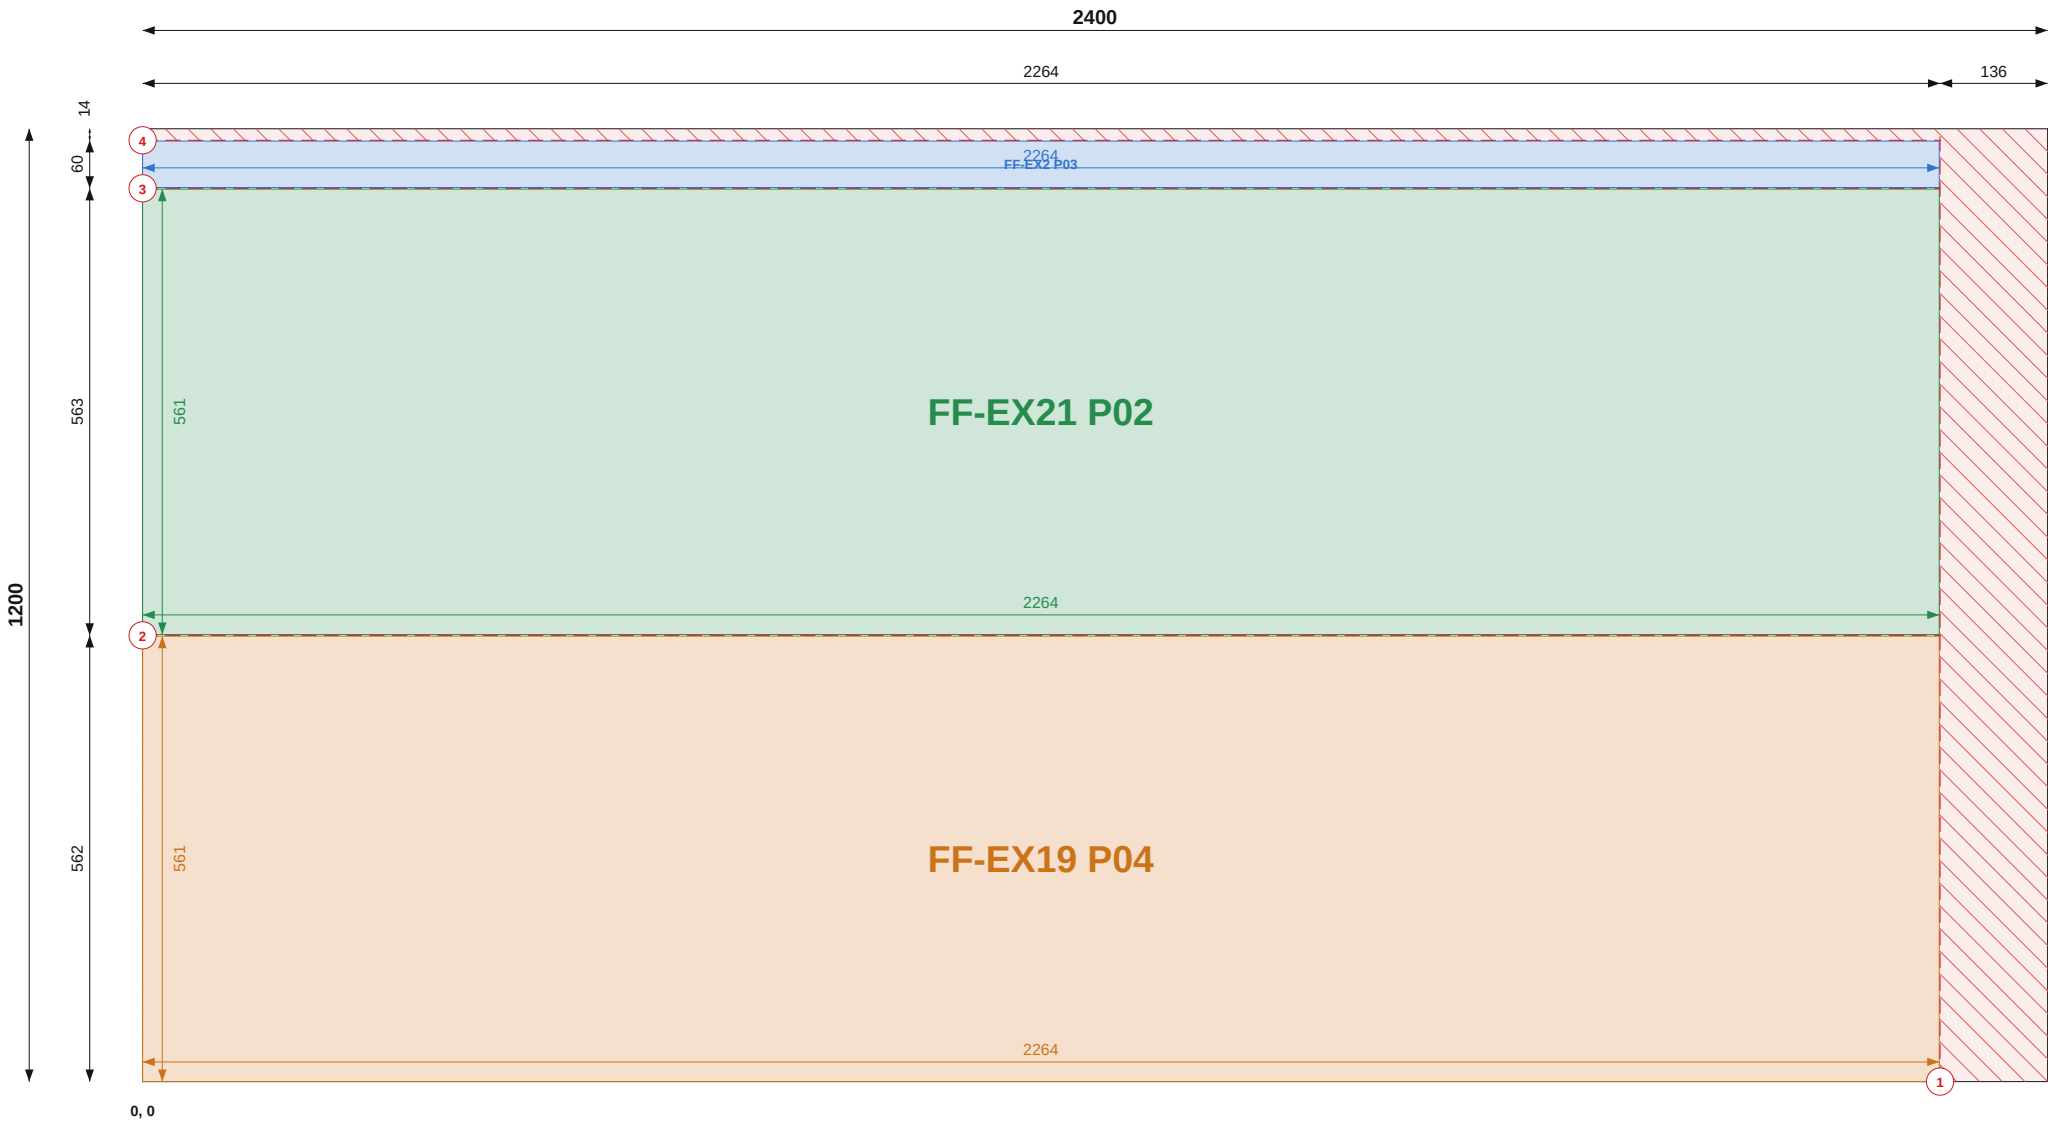

Top / left chains = saw cut positions (to cut centres). Coloured = part size and position.

SHEET 5 OF 23

THIS SHEET

| Item              | Value           |
|-------------------|-----------------|
| Parts             | 3               |
| Used / waste      | 92.8% / 0.21 m2 |
| Reusable offcuts  | 0               |
| Saw cuts / shared | 4 / 2           |

PIECES (POSITION = BOTTOM-LEFT CORNER)

| Label       | Size       | X, Y    |
|-------------|------------|---------|
| FF-EX2 P03  | 59 x 2264  | 0, 1126 |
| FF-EX21 P02 | 561 x 2264 | 0, 563  |
| FF-EX19 P04 | 561 x 2264 | 0, 0    |

NOTES

- Cut from PIR 120mm 1200x2400, 2mm saw kerf. Viewed on the face; dimensions from the sheet's bottom-left corner (0,0). Red numbered lines = saw cuts in order, each edge to edge.
- Coloured dimensions belong to the part of that colour: its width and height, and its position from the sheet edges. Raked parts: corner coordinates at each corner.
- Red hatch = waste. Labels = panel + piece mark on the manufacture drawing.

REVISIONS

| REV | DATE     | DESCRIPTION        |
|-----|----------|--------------------|
| C01 | 13.09.26 | Construction issue |



TLS TIMBER FRAME

Design & Manufacture

Scan: 3D model + drawings




|          |                            |
|----------|----------------------------|
| CLIENT   | PROJECT                    |
| MP Adams | MP Adams Plot 3, Eckington |

|                                           |  |  |  |
|-------------------------------------------|--|--|--|
| DRAWING TITLE                             |  |  |  |
| PIR CUTTING - FIRST FLOOR - SHEET 5 OF 23 |  |  |  |
| PIR 120mm 1200x2400   First Floor         |  |  |  |

|       |      |          |       |
|-------|------|----------|-------|
| SCALE | SIZE | DATE     | DRAWN |
| NTS   | A3   | 13.09.26 | TS    |

|              |                   |     |
|--------------|-------------------|-----|
| STATUS       | DRAWING No.       | REV |
| CONSTRUCTION | P3-CP-PIR-02 / 05 | C01 |

Do not scale. All dimensions in mm. Check all dimensions on site.

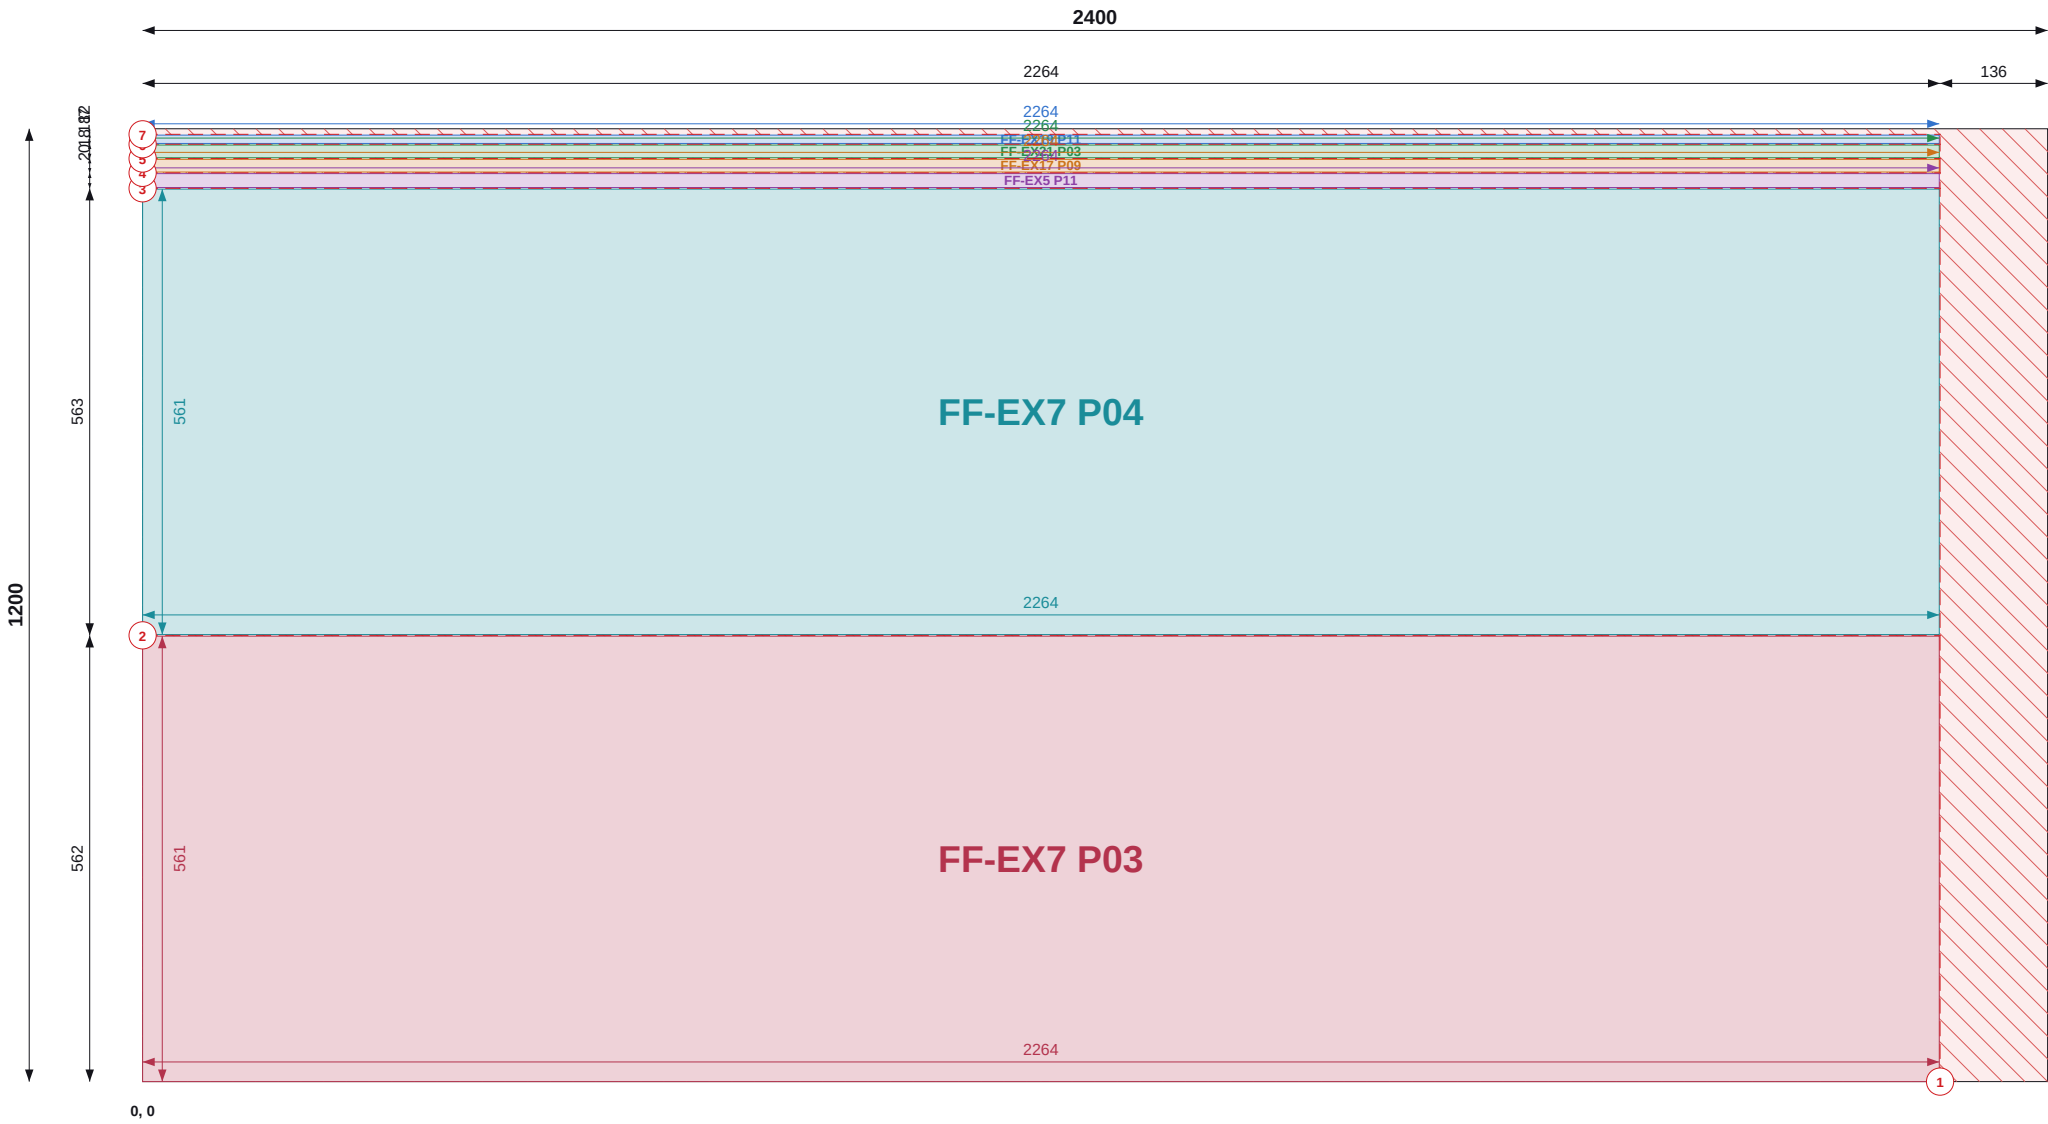

Top / left chains = saw cut positions (to cut centres). Coloured = part size and position.

SHEET 6 OF 23

THIS SHEET

| Item              | Value           |
|-------------------|-----------------|
| Parts             | 6               |
| Used / waste      | 92.9% / 0.20 m2 |
| Reusable offcuts  | 0               |
| Saw cuts / shared | 7 / 5           |

PIECES (POSITION = BOTTOM-LEFT CORNER)

| Label       | Size       | X, Y    |
|-------------|------------|---------|
| FF-EX19 P11 | 11 x 2264  | 0, 1181 |
| FF-EX21 P03 | 16 x 2264  | 0, 1163 |
| FF-EX17 P09 | 16 x 2264  | 0, 1145 |
| FF-EX5 P11  | 17 x 2264  | 0, 1126 |
| FF-EX7 P04  | 561 x 2264 | 0, 563  |
| FF-EX7 P03  | 561 x 2264 | 0, 0    |

NOTES

- Cut from PIR 120mm 1200x2400, 2mm saw kerf. Viewed on the face; dimensions from the sheet's bottom-left corner (0,0). Red numbered lines = saw cuts in order, each edge to edge.
- Coloured dimensions belong to the part of that colour: its width and height, and its position from the sheet edges. Raked parts: corner coordinates at each corner.
- Red hatch = waste. Labels = panel + piece mark on the manufacture drawing.

REVISIONS

| REV | DATE     | DESCRIPTION        |
|-----|----------|--------------------|
| C01 | 13.09.26 | Construction issue |



TLS TIMBER FRAME

Design & Manufacture

Scan: 3D model + drawings



|          |                            |
|----------|----------------------------|
| CLIENT   | PROJECT                    |
| MP Adams | MP Adams Plot 3, Eckington |


|                                           |
|-------------------------------------------|
| DRAWING TITLE                             |
| PIR CUTTING - FIRST FLOOR - SHEET 6 OF 23 |

PIR 120mm 1200x2400 | First Floor

|       |      |          |       |
|-------|------|----------|-------|
| SCALE | SIZE | DATE     | DRAWN |
| NTS   | A3   | 13.09.26 | TS    |

|              |                   |     |
|--------------|-------------------|-----|
| STATUS       | DRAWING No.       | REV |
| CONSTRUCTION | P3-CP-PIR-02 / 06 | C01 |

Do not scale. All dimensions in mm. Check all dimensions on site.

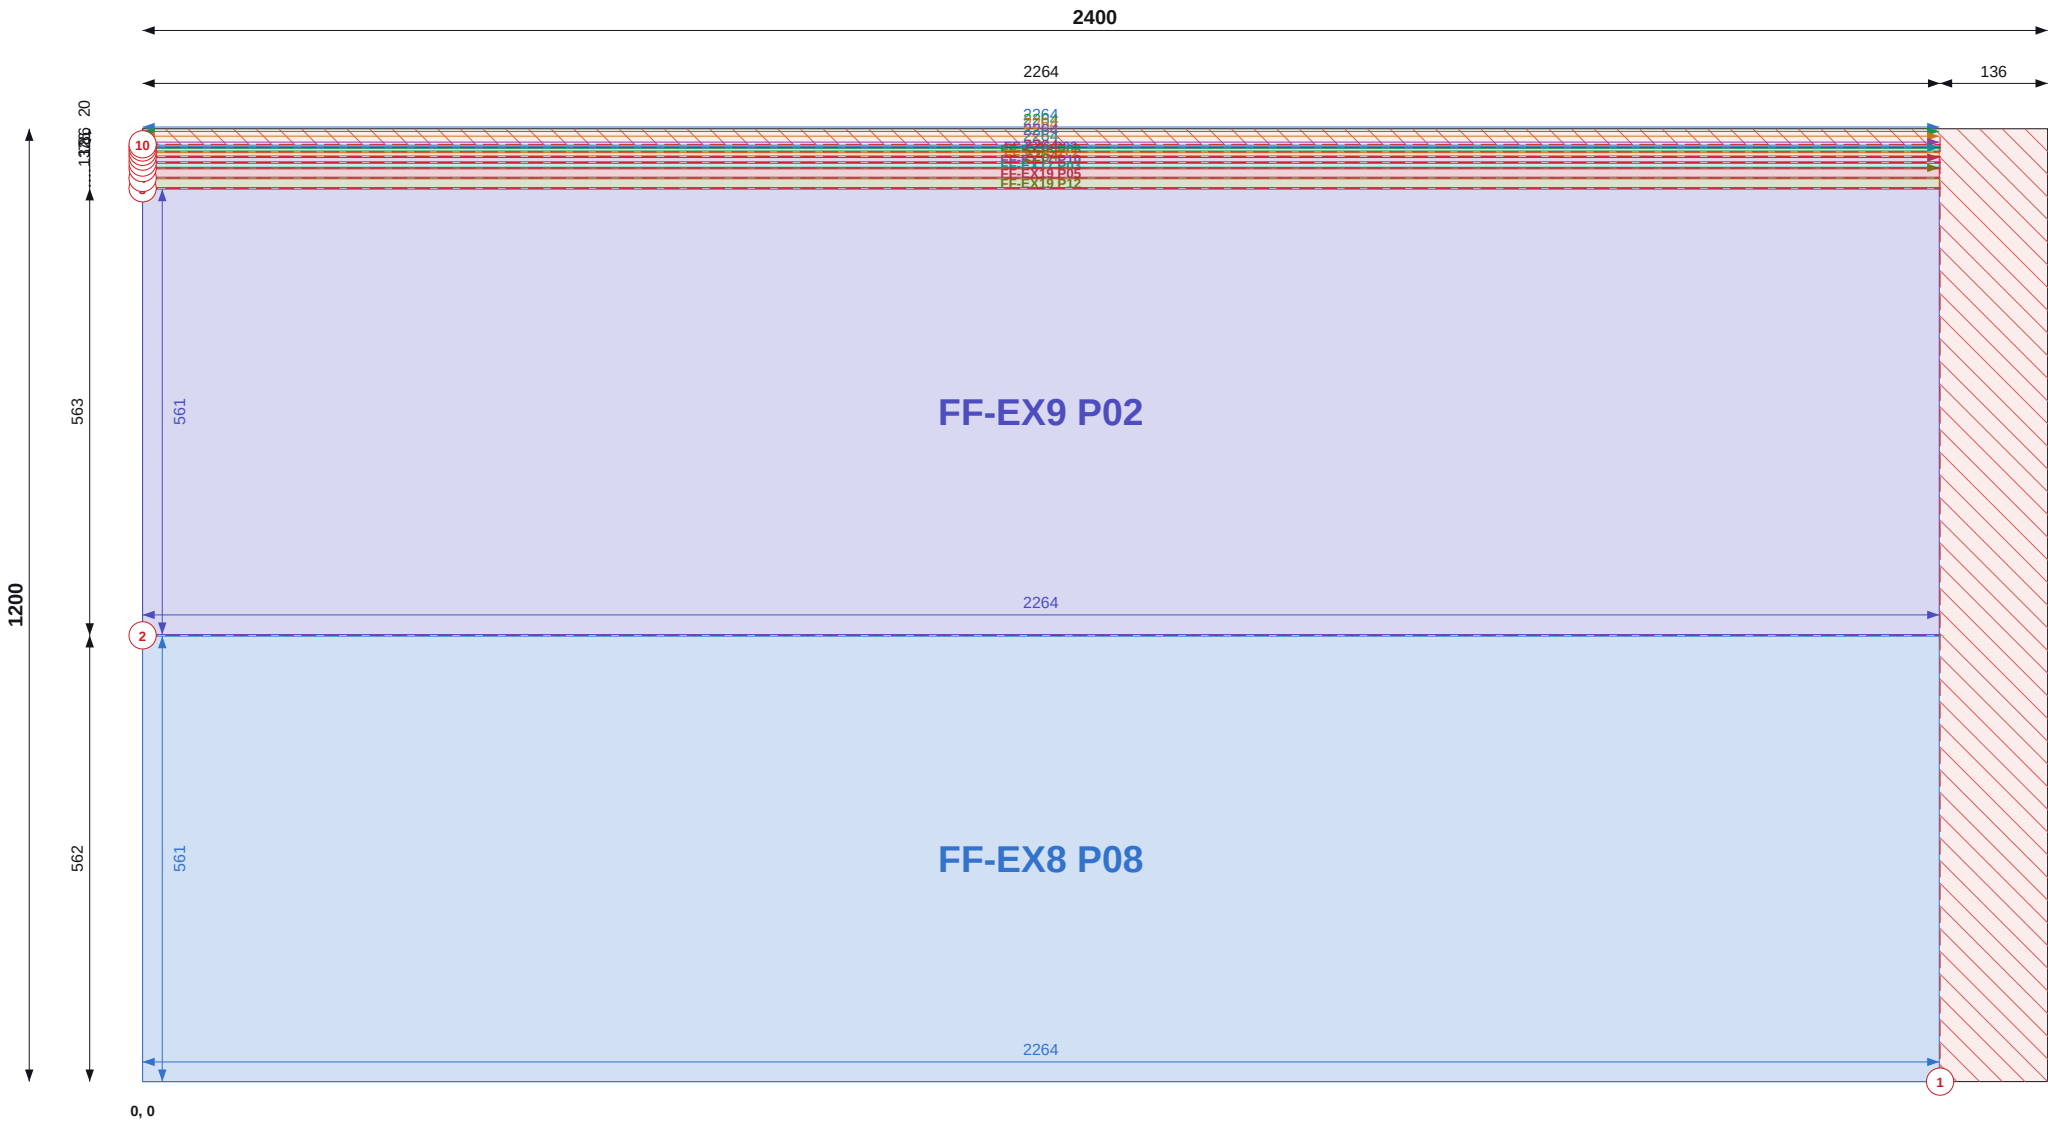

Top / left chains = saw cut positions (to cut centres). Coloured = part size and position.

SHEET 7 OF 23

THIS SHEET

| Item              | Value           |
|-------------------|-----------------|
| Parts             | 9               |
| Used / waste      | 91.4% / 0.25 m2 |
| Reusable offcuts  | 0               |
| Saw cuts / shared | 10 / 8          |

PIECES (POSITION = BOTTOM-LEFT CORNER)

| Label       | Size       | X, Y    |
|-------------|------------|---------|
| FF-EX6 P03  | 2 x 2264   | 0, 1177 |
| FF-EX18 P06 | 3 x 2264   | 0, 1172 |
| FF-EX5 P12  | 4 x 2264   | 0, 1166 |
| FF-EX17 P10 | 5 x 2264   | 0, 1158 |
| FF-EX17 P03 | 5 x 2264   | 0, 1151 |
| FF-EX19 P05 | 10 x 2264  | 0, 1139 |
| FF-EX19 P12 | 11 x 2264  | 0, 1126 |
| FF-EX9 P02  | 561 x 2264 | 0, 563  |
| FF-EX8 P08  | 561 x 2264 | 0, 0    |

NOTES

- Cut from PIR 120mm 1200x2400, 2mm saw kerf. Viewed on the face; dimensions from the sheet's bottom-left corner (0,0). Red numbered lines = saw cuts in order, each edge to edge.
- Coloured dimensions belong to the part of that colour: its width and height, and its position from the sheet edges. Raked parts: corner coordinates at each corner.
- Red hatch = waste. Labels = panel + piece mark on the manufacture drawing.

REVISIONS

| REV | DATE     | DESCRIPTION        |
|-----|----------|--------------------|
| C01 | 13.09.26 | Construction issue |



TLS TIMBER FRAME

Design & Manufacture

Scan: 3D model + drawings



|          |                            |
|----------|----------------------------|
| CLIENT   | PROJECT                    |
| MP Adams | MP Adams Plot 3, Eckington |


DRAWING TITLE  
**PIR CUTTING - FIRST FLOOR - SHEET 7 OF 23**

PIR 120mm 1200x2400 | First Floor

|       |      |          |       |
|-------|------|----------|-------|
| SCALE | SIZE | DATE     | DRAWN |
| NTS   | A3   | 13.09.26 | TS    |

|              |                          |            |
|--------------|--------------------------|------------|
| STATUS       | DRAWING No.              | REV        |
| CONSTRUCTION | <b>P3-CP-PIR-02 / 07</b> | <b>C01</b> |

Do not scale. All dimensions in mm. Check all dimensions on site.

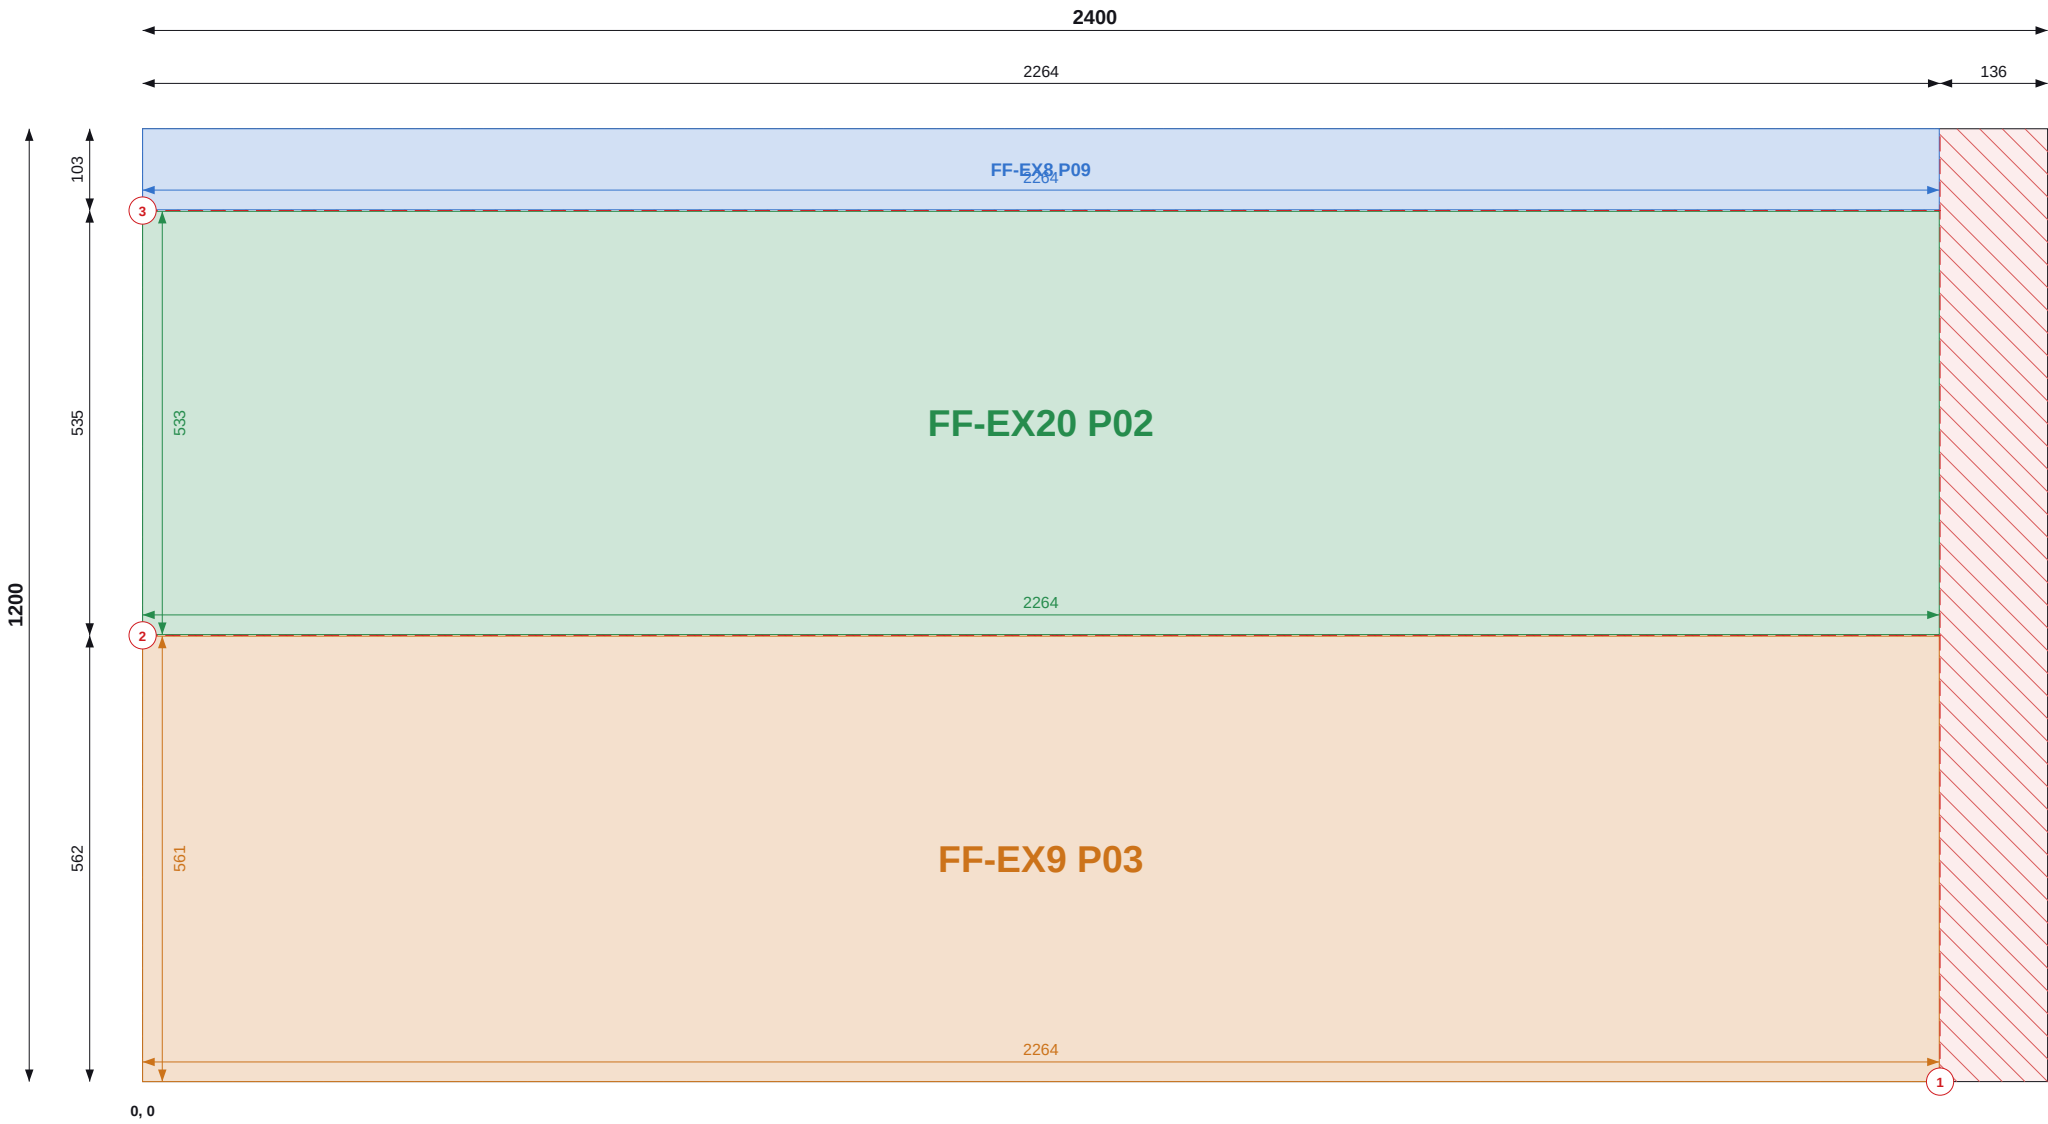

Top / left chains = saw cut positions (to cut centres). Coloured = part size and position.

## SHEET 8 OF 23

### THIS SHEET

| Item              | Value           |
|-------------------|-----------------|
| Parts             | 3               |
| Used / waste      | 94.0% / 0.17 m2 |
| Reusable offcuts  | 0               |
| Saw cuts / shared | 3 / 2           |

### PIECES (POSITION = BOTTOM-LEFT CORNER)

| Label       | Size       | X, Y    |
|-------------|------------|---------|
| FF-EX8 P09  | 102 x 2264 | 0, 1098 |
| FF-EX20 P02 | 533 x 2264 | 0, 563  |
| FF-EX9 P03  | 561 x 2264 | 0, 0    |

### NOTES

- Cut from PIR 120mm 1200x2400, 2mm saw kerf. Viewed on the face; dimensions from the sheet's bottom-left corner (0,0). Red numbered lines = saw cuts in order, each edge to edge.
- Coloured dimensions belong to the part of that colour: its width and height, and its position from the sheet edges. Raked parts: corner coordinates at each corner.
- Red hatch = waste. Labels = panel + piece mark on the manufacture drawing.

### REVISIONS

| REV | DATE     | DESCRIPTION        |
|-----|----------|--------------------|
| C01 | 13.09.26 | Construction issue |



TLS TIMBER FRAME

Design & Manufacture

Scan: 3D model + drawings



|          |                            |
|----------|----------------------------|
| CLIENT   | PROJECT                    |
| MP Adams | MP Adams Plot 3, Eckington |


|                                           |
|-------------------------------------------|
| DRAWING TITLE                             |
| PIR CUTTING - FIRST FLOOR - SHEET 8 OF 23 |

PIR 120mm 1200x2400 | First Floor

|       |      |          |       |
|-------|------|----------|-------|
| SCALE | SIZE | DATE     | DRAWN |
| NTS   | A3   | 13.09.26 | TS    |

|              |                   |     |
|--------------|-------------------|-----|
| STATUS       | DRAWING No.       | REV |
| CONSTRUCTION | P3-CP-PIR-02 / 08 | C01 |

Do not scale. All dimensions in mm. Check all dimensions on site.

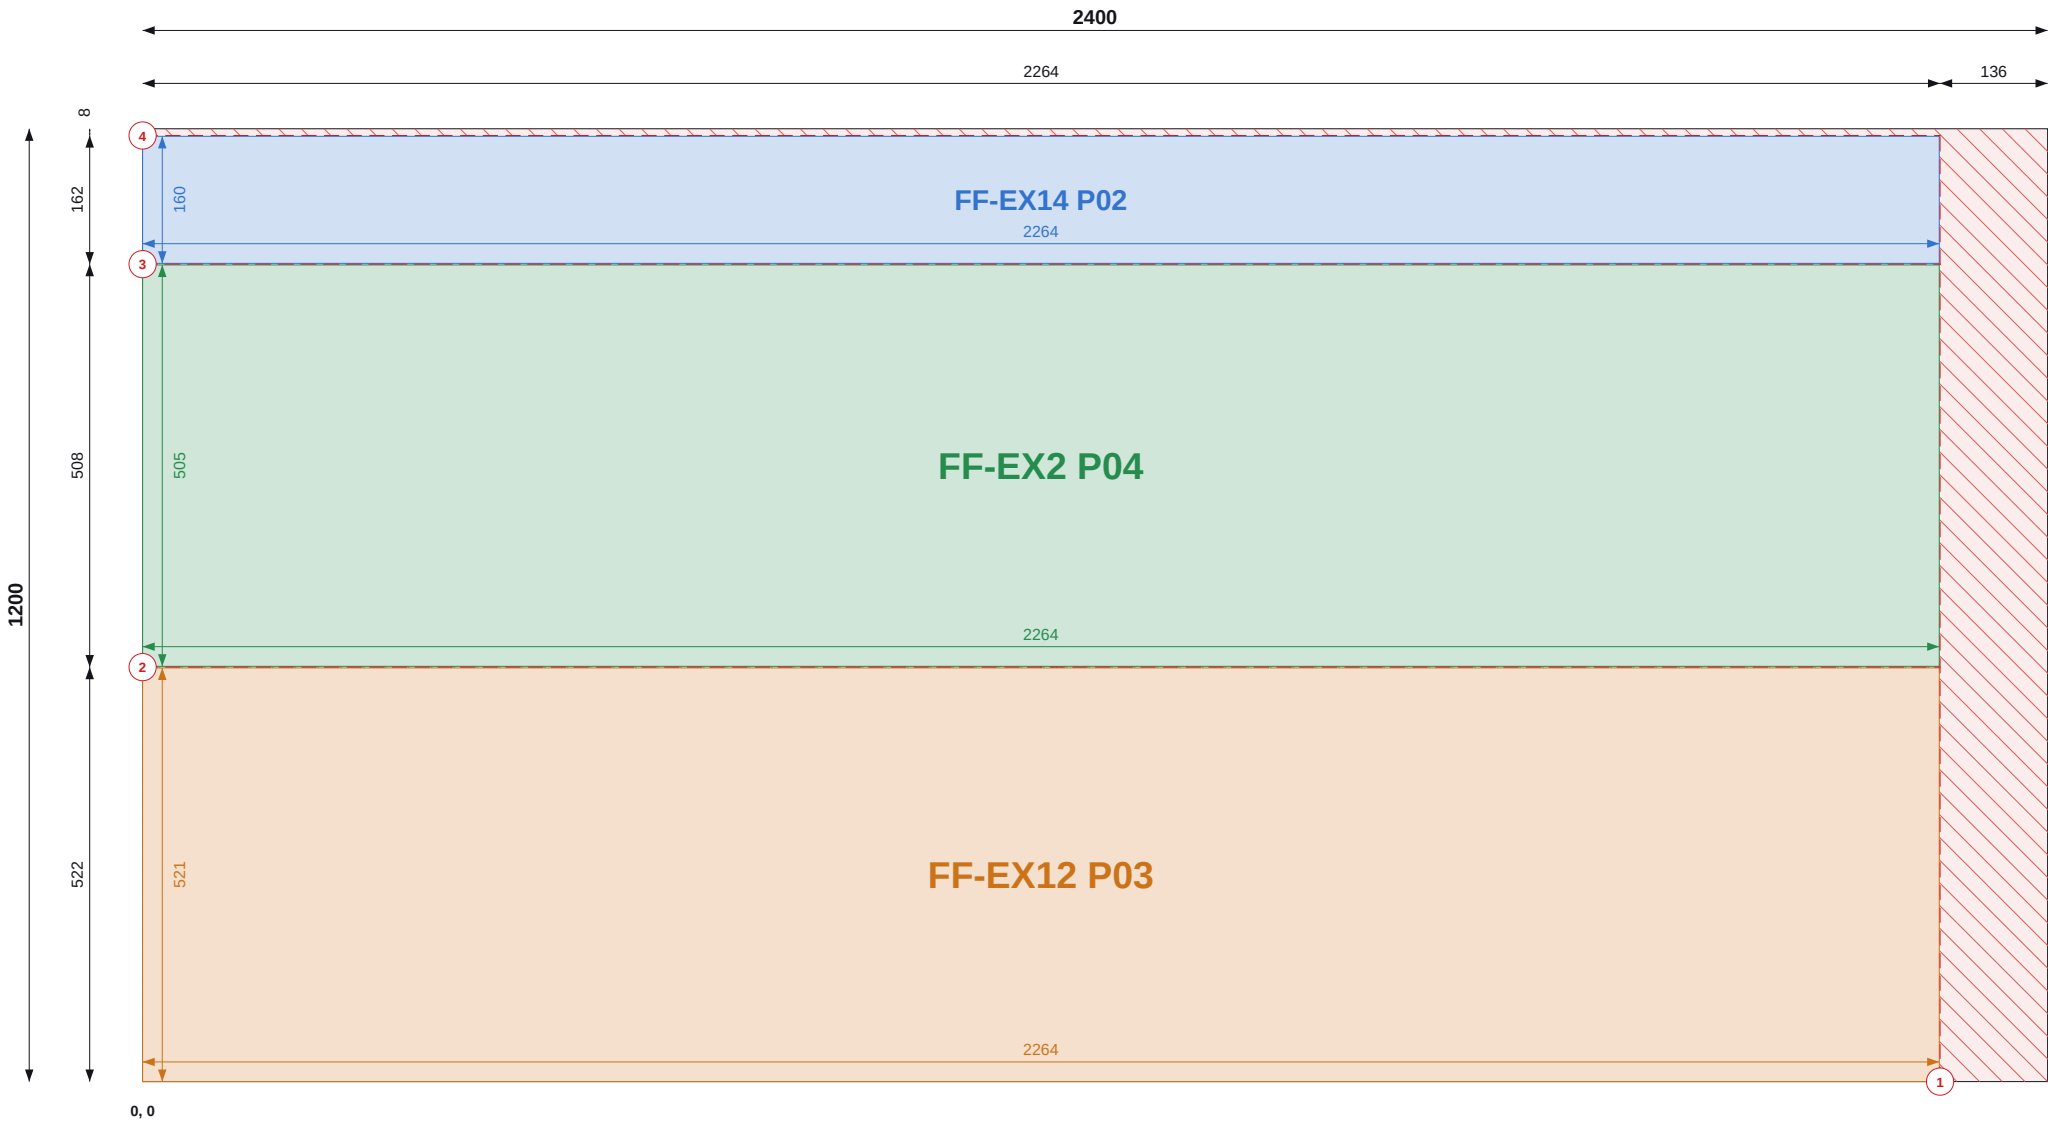

Top / left chains = saw cut positions (to cut centres). Coloured = part size and position.

## SHEET 9 OF 23

### THIS SHEET

| Item              | Value           |
|-------------------|-----------------|
| Parts             | 3               |
| Used / waste      | 93.3% / 0.19 m2 |
| Reusable offcuts  | 0               |
| Saw cuts / shared | 4 / 2           |

### PIECES (POSITION = BOTTOM-LEFT CORNER)

| Label       | Size       | X, Y    |
|-------------|------------|---------|
| FF-EX14 P02 | 160 x 2264 | 0, 1030 |
| FF-EX2 P04  | 505 x 2264 | 0, 523  |
| FF-EX12 P03 | 521 x 2264 | 0, 0    |

### NOTES

- Cut from PIR 120mm 1200x2400, 2mm saw kerf. Viewed on the face; dimensions from the sheet's bottom-left corner (0,0). Red numbered lines = saw cuts in order, each edge to edge.
- Coloured dimensions belong to the part of that colour: its width and height, and its position from the sheet edges. Raked parts: corner coordinates at each corner.
- Red hatch = waste. Labels = panel + piece mark on the manufacture drawing.

### REVISIONS

| REV | DATE     | DESCRIPTION        |
|-----|----------|--------------------|
| C01 | 13.09.26 | Construction issue |



TLS TIMBER FRAME

Design & Manufacture

Scan: 3D model + drawings




|          |                            |
|----------|----------------------------|
| CLIENT   | PROJECT                    |
| MP Adams | MP Adams Plot 3, Eckington |

|                                                  |
|--------------------------------------------------|
| DRAWING TITLE                                    |
| <b>PIR CUTTING - FIRST FLOOR - SHEET 9 OF 23</b> |
| PIR 120mm 1200x2400   First Floor                |

|       |      |          |       |
|-------|------|----------|-------|
| SCALE | SIZE | DATE     | DRAWN |
| NTS   | A3   | 13.09.26 | TS    |

|              |                          |     |
|--------------|--------------------------|-----|
| STATUS       | DRAWING No.              | REV |
| CONSTRUCTION | <b>P3-CP-PIR-02 / 09</b> | C01 |

Do not scale. All dimensions in mm. Check all dimensions on site.

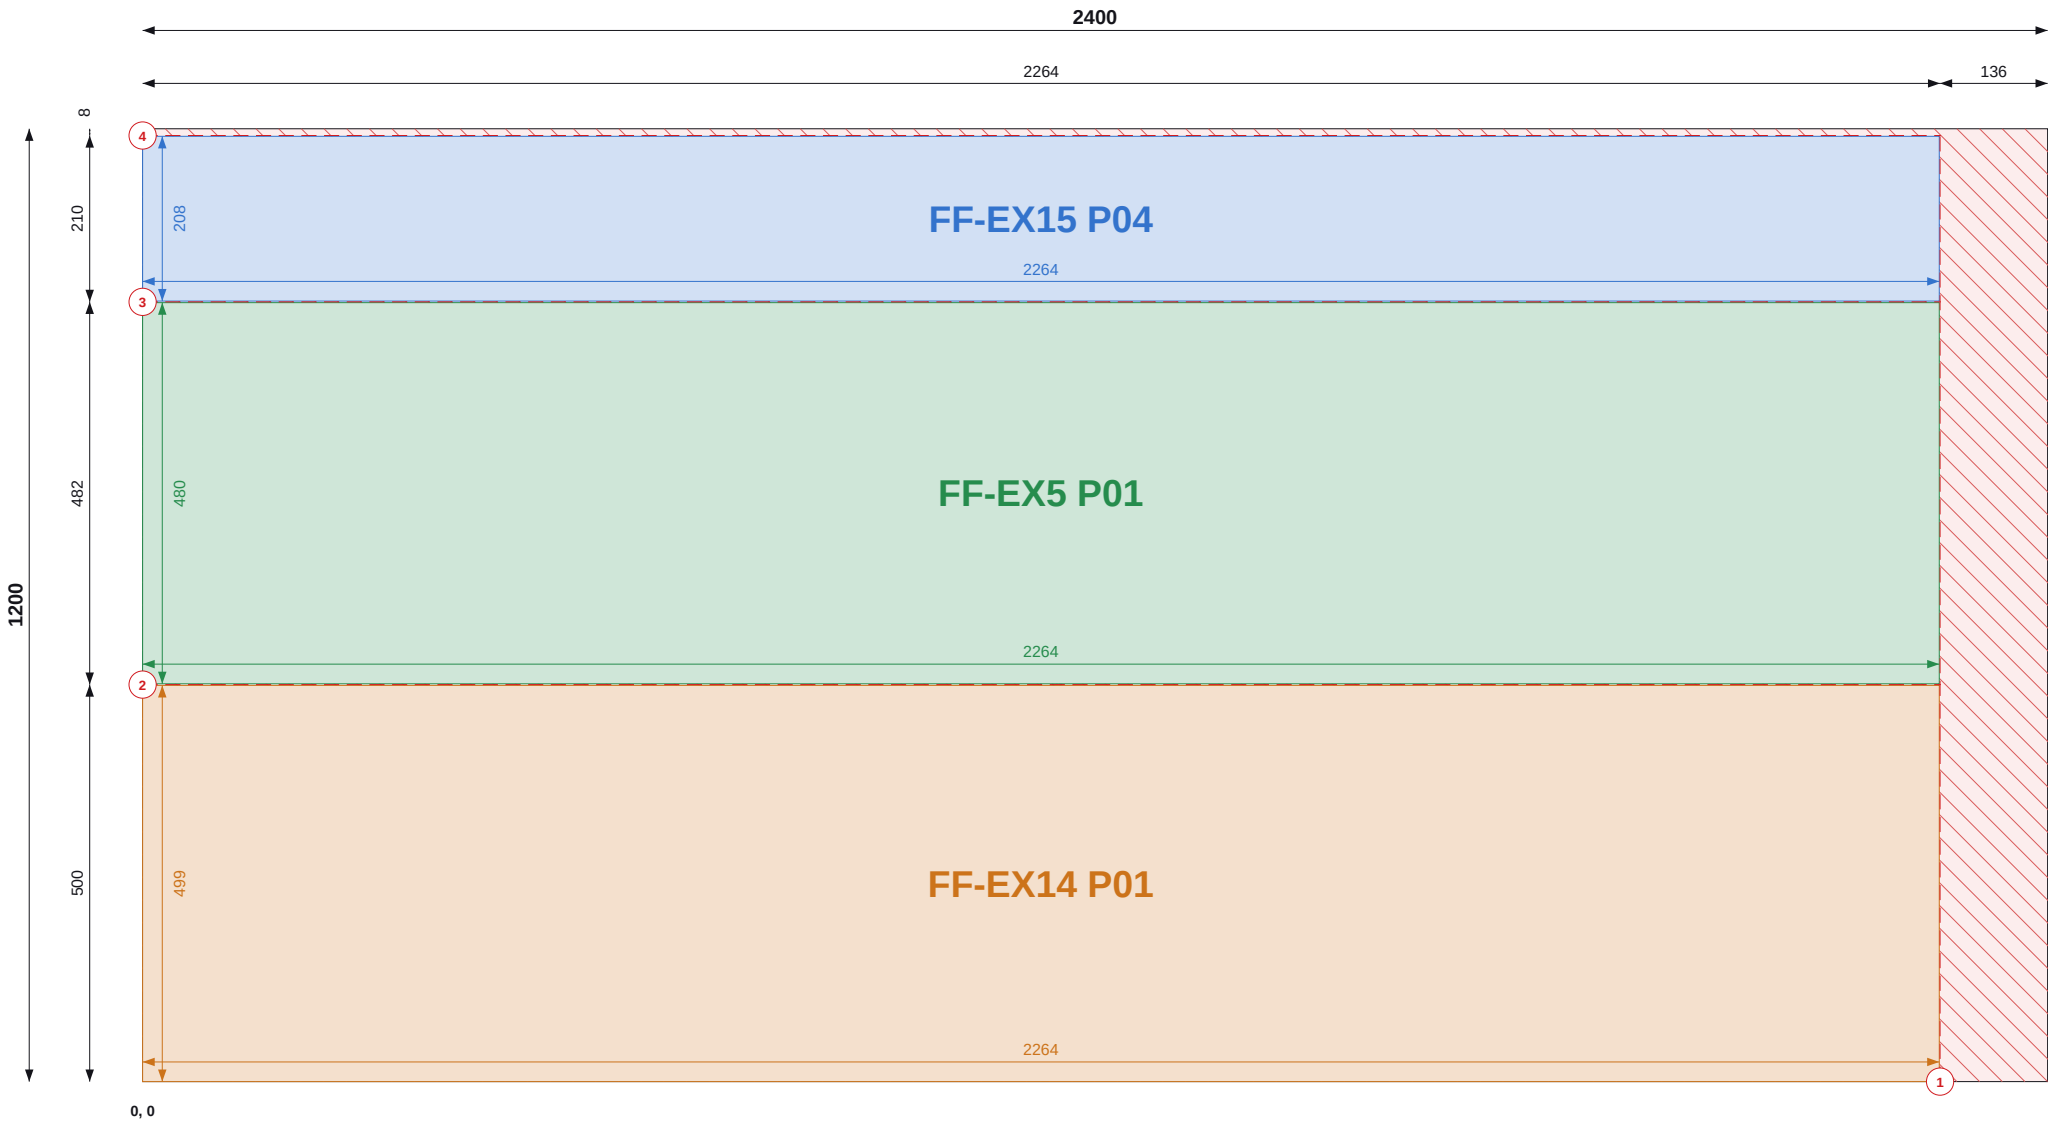

Top / left chains = saw cut positions (to cut centres). Coloured = part size and position.

## SHEET 10 OF 23

### THIS SHEET

| Item              | Value           |
|-------------------|-----------------|
| Parts             | 3               |
| Used / waste      | 93.3% / 0.19 m2 |
| Reusable offcuts  | 0               |
| Saw cuts / shared | 4 / 2           |

### PIECES (POSITION = BOTTOM-LEFT CORNER)

| Label       | Size       | X, Y   |
|-------------|------------|--------|
| FF-EX15 P04 | 208 x 2264 | 0, 983 |
| FF-EX5 P01  | 480 x 2264 | 0, 501 |
| FF-EX14 P01 | 499 x 2264 | 0, 0   |

### NOTES

- Cut from PIR 120mm 1200x2400, 2mm saw kerf. Viewed on the face; dimensions from the sheet's bottom-left corner (0,0). Red numbered lines = saw cuts in order, each edge to edge.
- Coloured dimensions belong to the part of that colour: its width and height, and its position from the sheet edges. Raked parts: corner coordinates at each corner.
- Red hatch = waste. Labels = panel + piece mark on the manufacture drawing.

### REVISIONS

| REV | DATE     | DESCRIPTION        |
|-----|----------|--------------------|
| C01 | 13.09.26 | Construction issue |



TLS TIMBER FRAME

Design & Manufacture

Scan: 3D model + drawings




|          |                            |
|----------|----------------------------|
| CLIENT   | PROJECT                    |
| MP Adams | MP Adams Plot 3, Eckington |

|                                            |  |  |  |
|--------------------------------------------|--|--|--|
| DRAWING TITLE                              |  |  |  |
| PIR CUTTING - FIRST FLOOR - SHEET 10 OF 23 |  |  |  |
| PIR 120mm 1200x2400   First Floor          |  |  |  |

|       |      |          |       |
|-------|------|----------|-------|
| SCALE | SIZE | DATE     | DRAWN |
| NTS   | A3   | 13.09.26 | TS    |

|              |                   |     |
|--------------|-------------------|-----|
| STATUS       | DRAWING No.       | REV |
| CONSTRUCTION | P3-CP-PIR-02 / 10 | C01 |

Do not scale. All dimensions in mm. Check all dimensions on site.

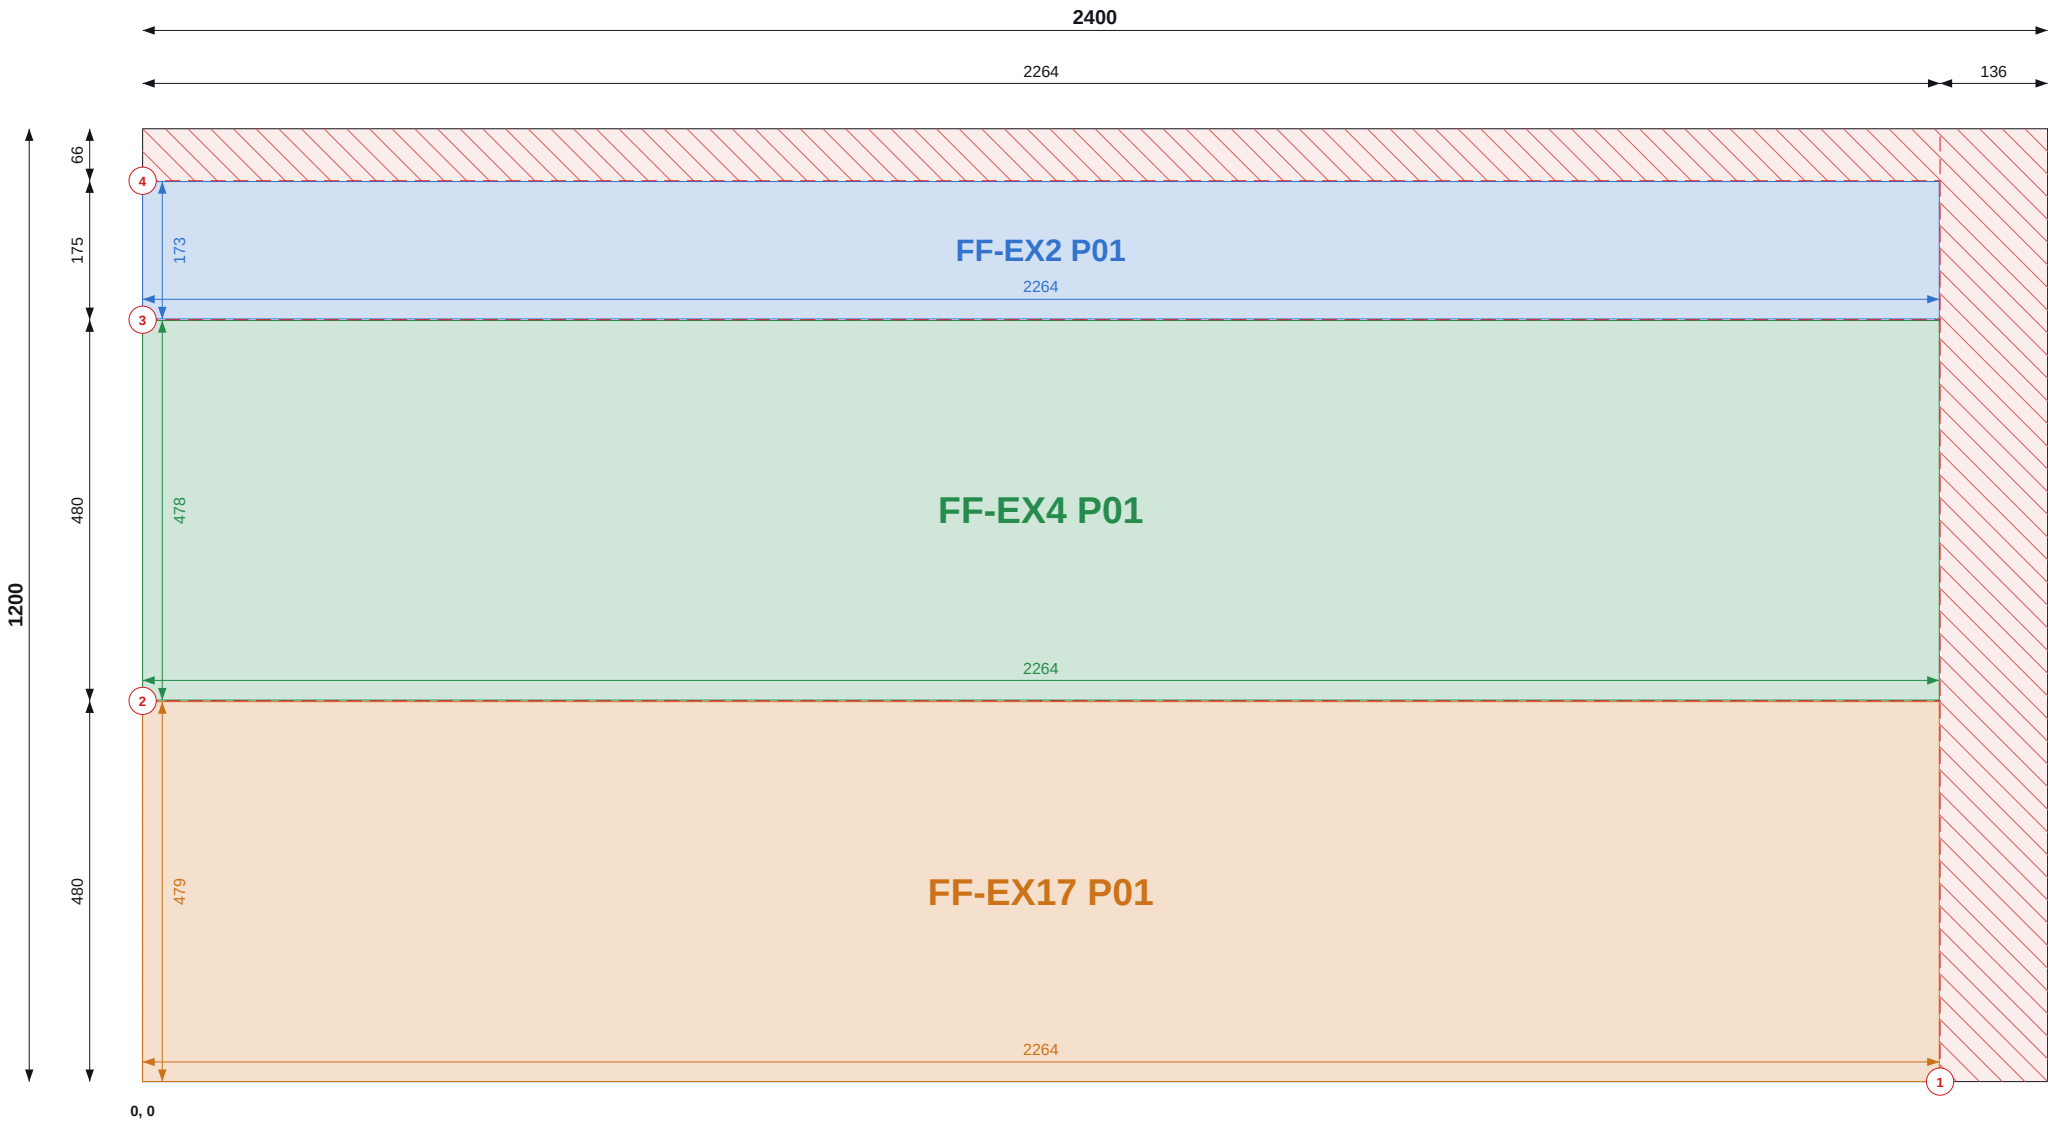

Top / left chains = saw cut positions (to cut centres). Coloured = part size and position.

SHEET 11 OF 23

THIS SHEET

| Item              | Value           |
|-------------------|-----------------|
| Parts             | 3               |
| Used / waste      | 88.8% / 0.32 m2 |
| Reusable offcuts  | 0               |
| Saw cuts / shared | 4 / 2           |

PIECES (POSITION = BOTTOM-LEFT CORNER)

| Label       | Size       | X, Y   |
|-------------|------------|--------|
| FF-EX2 P01  | 173 x 2264 | 0, 960 |
| FF-EX4 P01  | 478 x 2264 | 0, 481 |
| FF-EX17 P01 | 479 x 2264 | 0, 0   |

NOTES

- Cut from PIR 120mm 1200x2400, 2mm saw kerf. Viewed on the face; dimensions from the sheet's bottom-left corner (0,0). Red numbered lines = saw cuts in order, each edge to edge.
- Coloured dimensions belong to the part of that colour: its width and height, and its position from the sheet edges. Raked parts: corner coordinates at each corner.
- Red hatch = waste. Labels = panel + piece mark on the manufacture drawing.

REVISIONS

| REV | DATE     | DESCRIPTION        |
|-----|----------|--------------------|
| C01 | 13.09.26 | Construction issue |



TLS TIMBER FRAME

Design & Manufacture

Scan: 3D model + drawings




|          |                            |
|----------|----------------------------|
| CLIENT   | PROJECT                    |
| MP Adams | MP Adams Plot 3, Eckington |

|                                            |  |  |  |
|--------------------------------------------|--|--|--|
| DRAWING TITLE                              |  |  |  |
| PIR CUTTING - FIRST FLOOR - SHEET 11 OF 23 |  |  |  |
| PIR 120mm 1200x2400   First Floor          |  |  |  |

|       |      |          |       |
|-------|------|----------|-------|
| SCALE | SIZE | DATE     | DRAWN |
| NTS   | A3   | 13.09.26 | TS    |

|              |                   |     |
|--------------|-------------------|-----|
| STATUS       | DRAWING No.       | REV |
| CONSTRUCTION | P3-CP-PIR-02 / 11 | C01 |

Do not scale. All dimensions in mm. Check all dimensions on site.

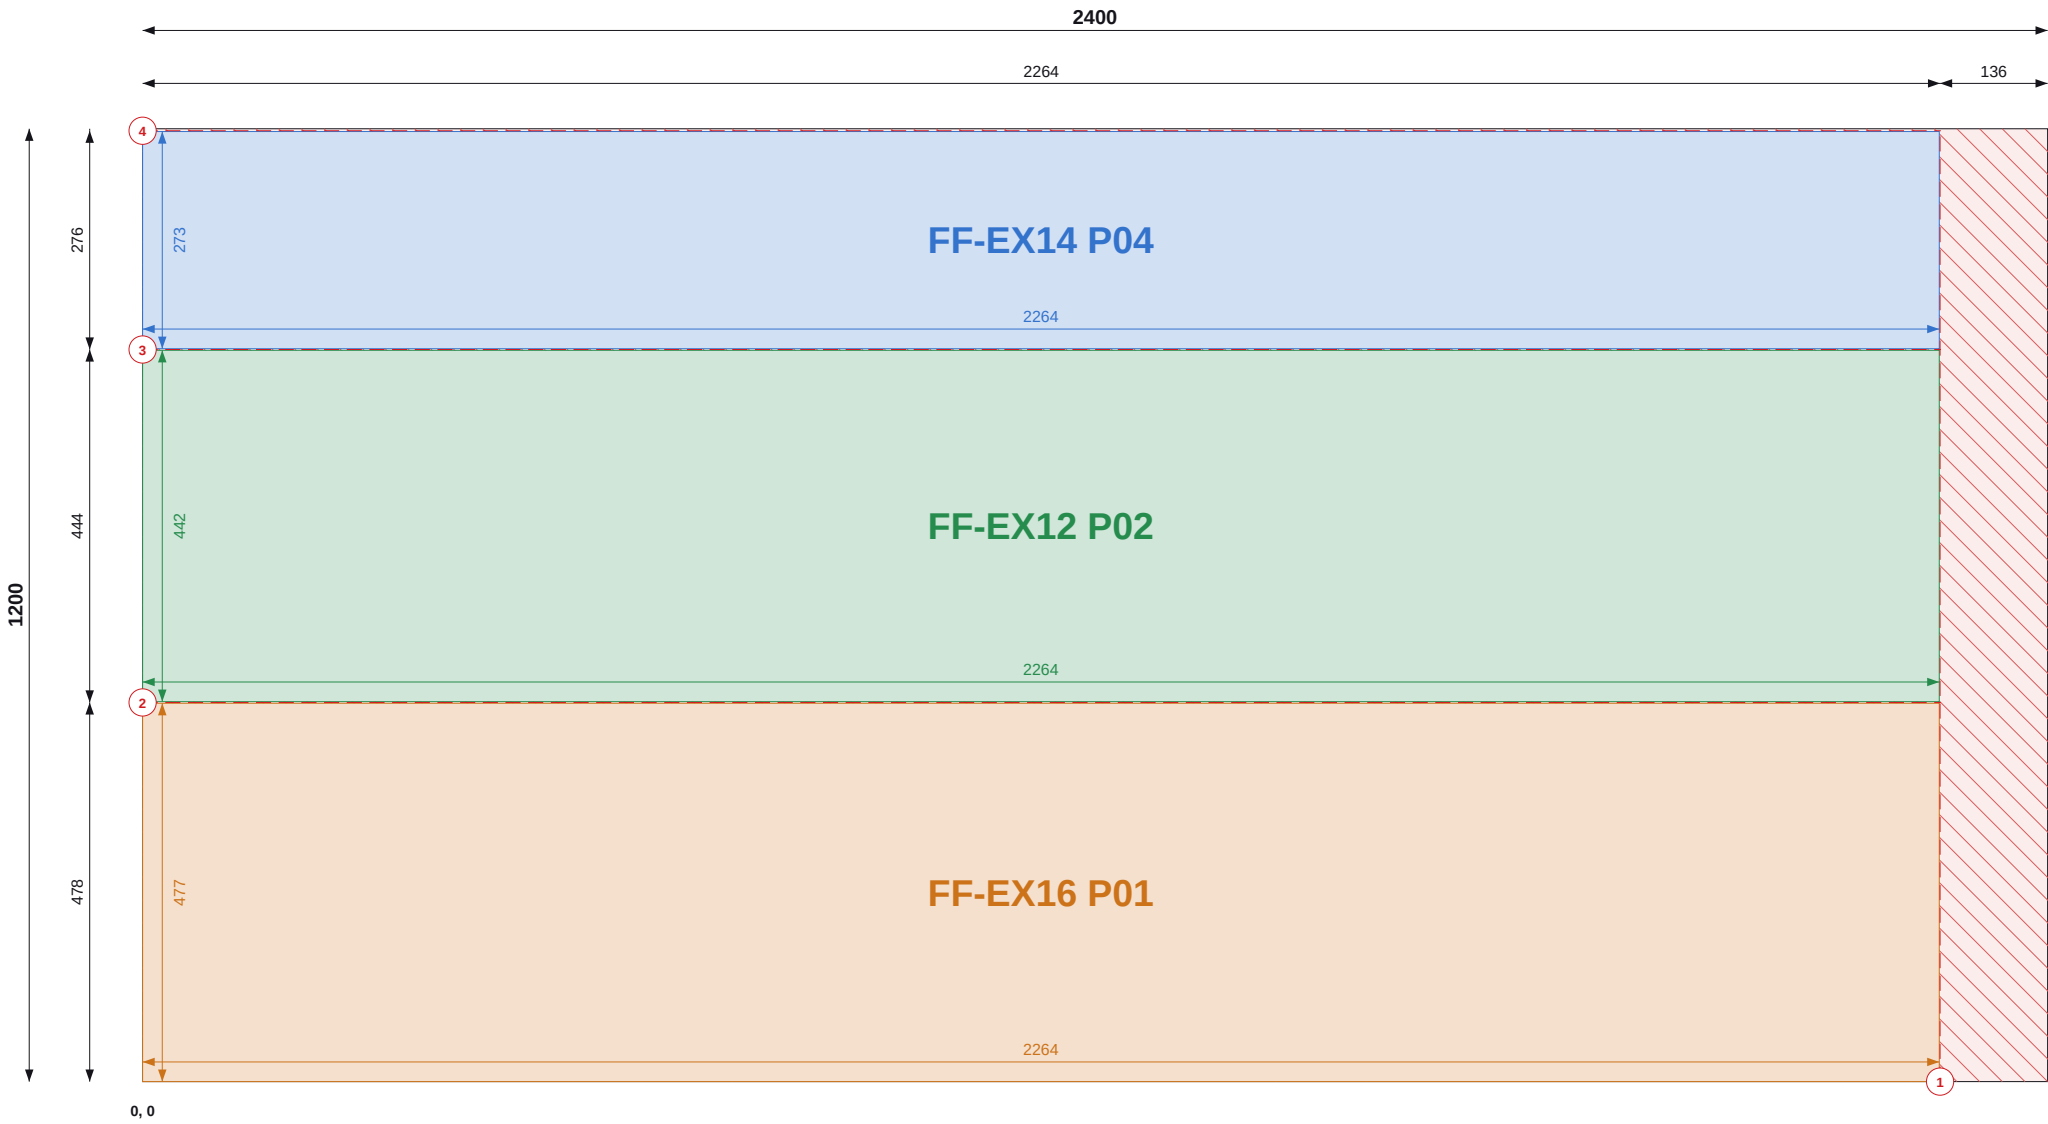

SHEET 12 OF 23

THIS SHEET

| Item              | Value           |
|-------------------|-----------------|
| Parts             | 3               |
| Used / waste      | 93.7% / 0.18 m2 |
| Reusable offcuts  | 0               |
| Saw cuts / shared | 4 / 2           |

PIECES (POSITION = BOTTOM-LEFT CORNER)

| Label       | Size       | X, Y   |
|-------------|------------|--------|
| FF-EX14 P04 | 273 x 2264 | 0, 923 |
| FF-EX12 P02 | 442 x 2264 | 0, 479 |
| FF-EX16 P01 | 477 x 2264 | 0, 0   |

NOTES

- Cut from PIR 120mm 1200x2400, 2mm saw kerf. Viewed on the face; dimensions from the sheet's bottom-left corner (0,0). Red numbered lines = saw cuts in order, each edge to edge.
- Coloured dimensions belong to the part of that colour: its width and height, and its position from the sheet edges. Raked parts: corner coordinates at each corner.
- Red hatch = waste. Labels = panel + piece mark on the manufacture drawing.

REVISIONS

| REV | DATE     | DESCRIPTION        |
|-----|----------|--------------------|
| C01 | 13.09.26 | Construction issue |



TLS TIMBER FRAME

Design & Manufacture

Scan: 3D model + drawings



|          |                            |
|----------|----------------------------|
| CLIENT   | PROJECT                    |
| MP Adams | MP Adams Plot 3, Eckington |


|                                            |
|--------------------------------------------|
| DRAWING TITLE                              |
| PIR CUTTING - FIRST FLOOR - SHEET 12 OF 23 |

PIR 120mm 1200x2400 | First Floor

|       |      |          |       |
|-------|------|----------|-------|
| SCALE | SIZE | DATE     | DRAWN |
| NTS   | A3   | 13.09.26 | TS    |

|              |                   |     |
|--------------|-------------------|-----|
| STATUS       | DRAWING No.       | REV |
| CONSTRUCTION | P3-CP-PIR-02 / 12 | C01 |

Do not scale. All dimensions in mm. Check all dimensions on site.

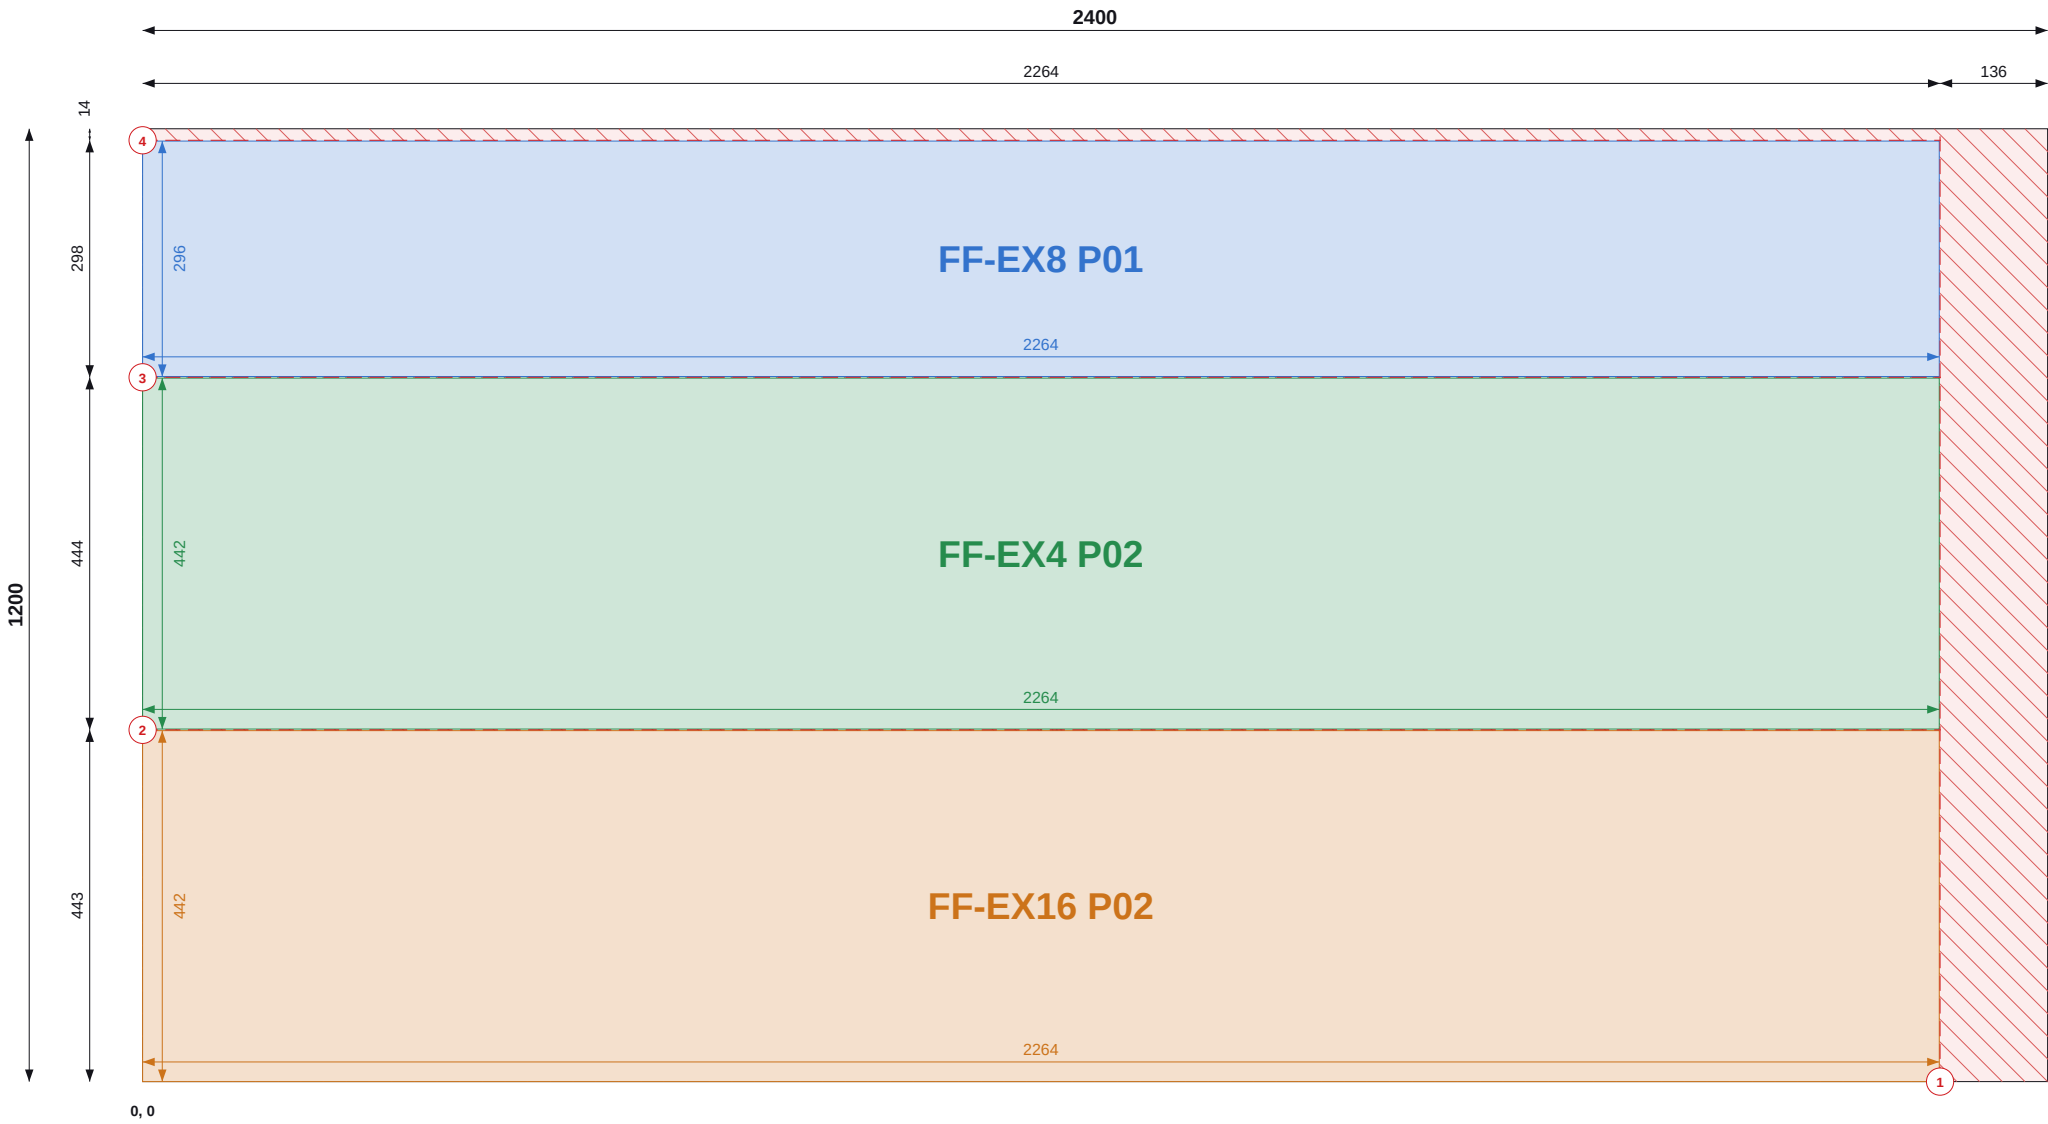

Top / left chains = saw cut positions (to cut centres). Coloured = part size and position.

SHEET 13 OF 23

THIS SHEET

| Item              | Value           |
|-------------------|-----------------|
| Parts             | 3               |
| Used / waste      | 92.8% / 0.21 m2 |
| Reusable offcuts  | 0               |
| Saw cuts / shared | 4 / 2           |

PIECES (POSITION = BOTTOM-LEFT CORNER)

| Label       | Size       | X, Y   |
|-------------|------------|--------|
| FF-EX8 P01  | 296 x 2264 | 0, 888 |
| FF-EX4 P02  | 442 x 2264 | 0, 444 |
| FF-EX16 P02 | 442 x 2264 | 0, 0   |

NOTES

- Cut from PIR 120mm 1200x2400, 2mm saw kerf. Viewed on the face; dimensions from the sheet's bottom-left corner (0,0). Red numbered lines = saw cuts in order, each edge to edge.
- Coloured dimensions belong to the part of that colour: its width and height, and its position from the sheet edges. Raked parts: corner coordinates at each corner.
- Red hatch = waste. Labels = panel + piece mark on the manufacture drawing.

REVISIONS

| REV | DATE     | DESCRIPTION        |
|-----|----------|--------------------|
| C01 | 13.09.26 | Construction issue |



TLS TIMBER FRAME

Design & Manufacture

Scan: 3D model + drawings



|          |                            |
|----------|----------------------------|
| CLIENT   | PROJECT                    |
| MP Adams | MP Adams Plot 3, Eckington |


|                                            |
|--------------------------------------------|
| DRAWING TITLE                              |
| PIR CUTTING - FIRST FLOOR - SHEET 13 OF 23 |

PIR 120mm 1200x2400 | First Floor

|       |      |          |       |
|-------|------|----------|-------|
| SCALE | SIZE | DATE     | DRAWN |
| NTS   | A3   | 13.09.26 | TS    |

|              |                   |     |
|--------------|-------------------|-----|
| STATUS       | DRAWING No.       | REV |
| CONSTRUCTION | P3-CP-PIR-02 / 13 | C01 |

Do not scale. All dimensions in mm. Check all dimensions on site.

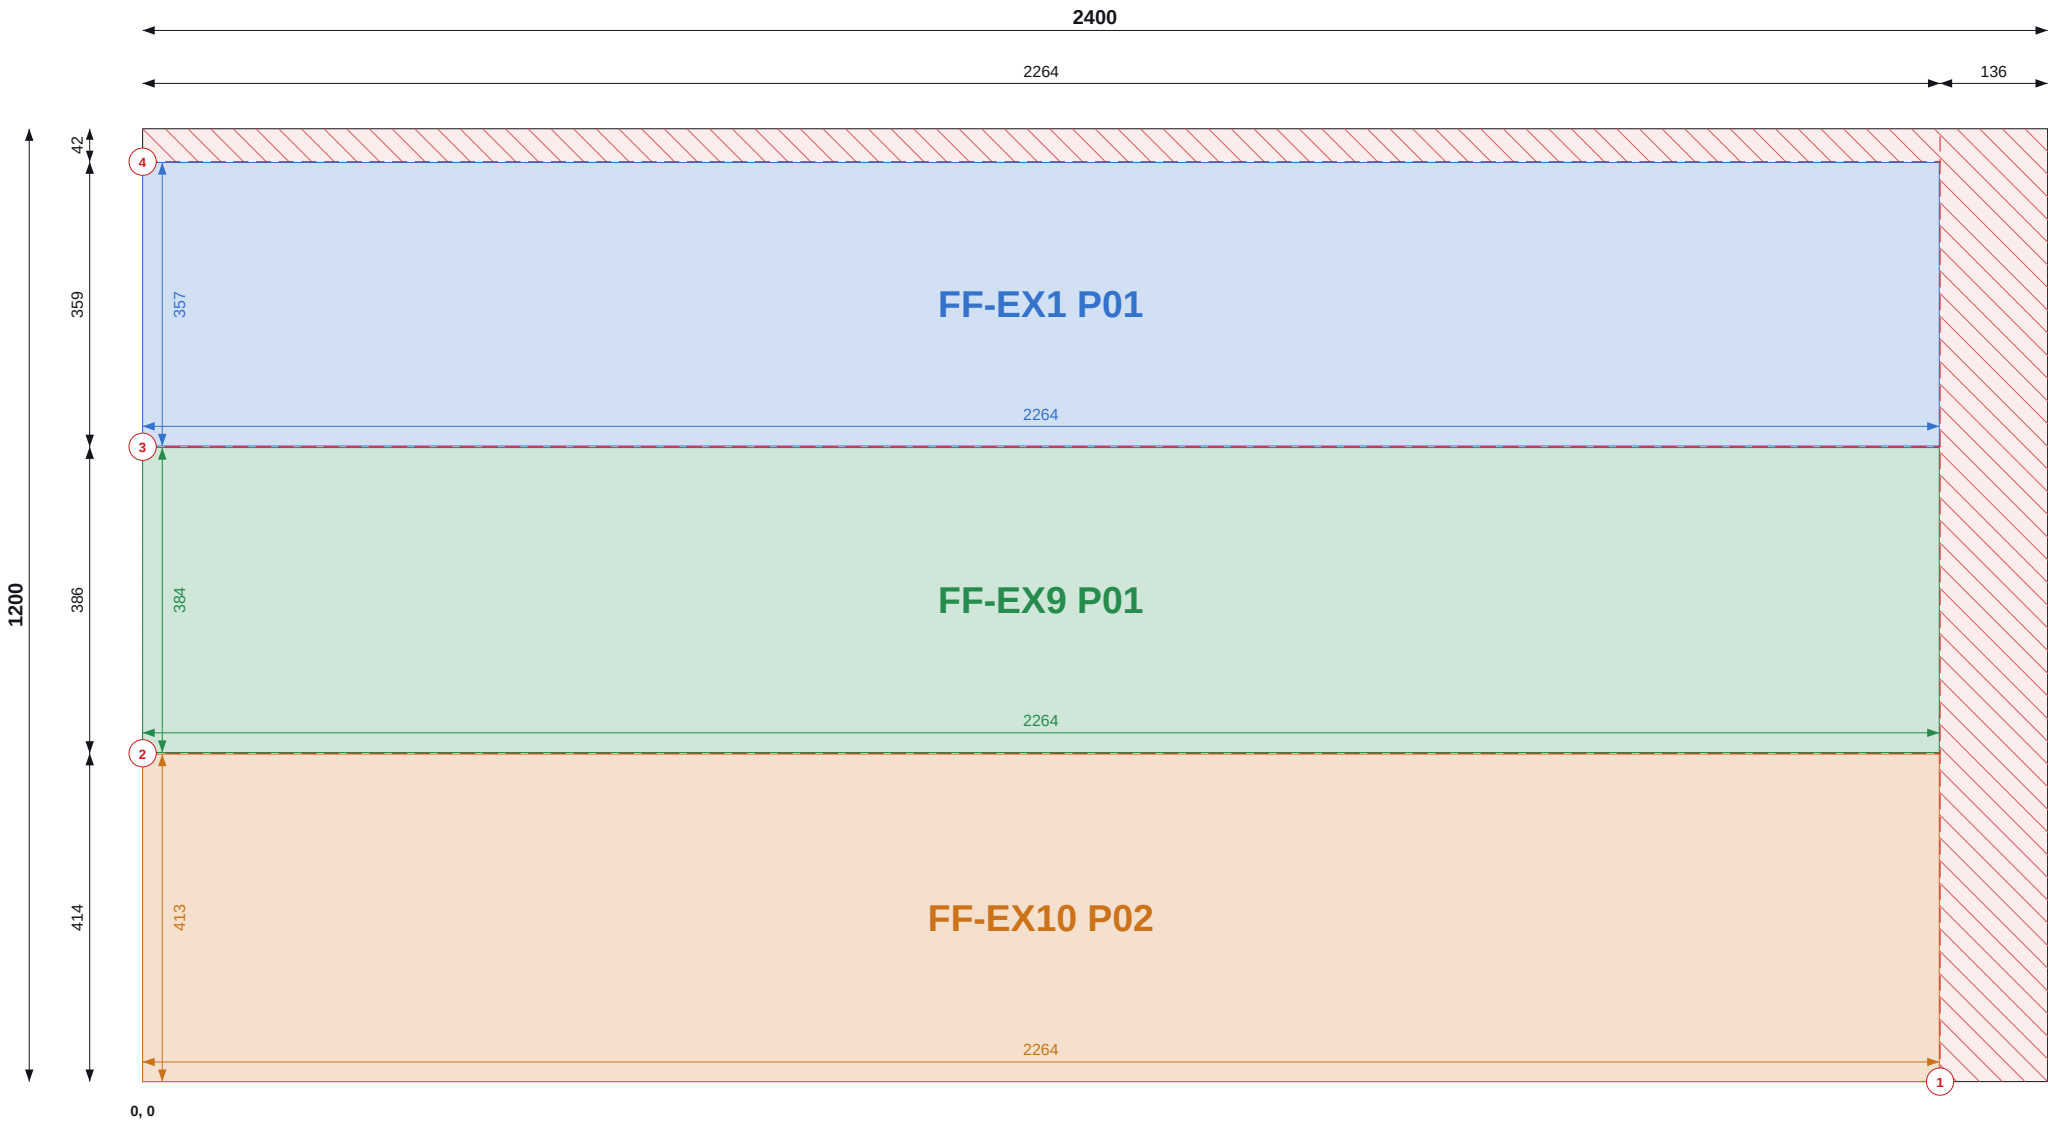

Top / left chains = saw cut positions (to cut centres). Coloured = part size and position.

SHEET 14 OF 23

THIS SHEET

| Item              | Value           |
|-------------------|-----------------|
| Parts             | 3               |
| Used / waste      | 90.7% / 0.27 m2 |
| Reusable offcuts  | 0               |
| Saw cuts / shared | 4 / 2           |

PIECES (POSITION = BOTTOM-LEFT CORNER)

| Label       | Size       | X, Y   |
|-------------|------------|--------|
| FF-EX1 P01  | 357 x 2264 | 0, 800 |
| FF-EX9 P01  | 384 x 2264 | 0, 415 |
| FF-EX10 P02 | 413 x 2264 | 0, 0   |

NOTES

- Cut from PIR 120mm 1200x2400, 2mm saw kerf. Viewed on the face; dimensions from the sheet's bottom-left corner (0,0). Red numbered lines = saw cuts in order, each edge to edge.
- Coloured dimensions belong to the part of that colour: its width and height, and its position from the sheet edges. Raked parts: corner coordinates at each corner.
- Red hatch = waste. Labels = panel + piece mark on the manufacture drawing.

REVISIONS

| REV | DATE     | DESCRIPTION        |
|-----|----------|--------------------|
| C01 | 13.09.26 | Construction issue |



TLS TIMBER FRAME  
Design & Manufacture  
Scan: 3D model + drawings



|                    |                                       |
|--------------------|---------------------------------------|
| CLIENT<br>MP Adams | PROJECT<br>MP Adams Plot 3, Eckington |
|--------------------|---------------------------------------|

DRAWING TITLE  
**PIR CUTTING - FIRST FLOOR - SHEET 14 OF 23**

PIR 120mm 1200x2400 | First Floor

|              |            |                  |             |
|--------------|------------|------------------|-------------|
| SCALE<br>NTS | SIZE<br>A3 | DATE<br>13.09.26 | DRAWN<br>TS |
|--------------|------------|------------------|-------------|

|                               |                                         |                   |
|-------------------------------|-----------------------------------------|-------------------|
| STATUS<br><b>CONSTRUCTION</b> | DRAWING No.<br><b>P3-CP-PIR-02 / 14</b> | REV<br><b>C01</b> |
|-------------------------------|-----------------------------------------|-------------------|

| Item              | Value           |
|-------------------|-----------------|
| Parts             | 37              |
| Used / waste      | 92.3% / 0.22 m2 |
| Reusable offcuts  | 0               |
| Saw cuts / shared | 39 / 36         |

## PIECES (POSITION = BOTTOM-LEFT CORNER)

| Label       | Size       | X, Y       |
|-------------|------------|------------|
| FF-EX11 P06 | 284 x 69   | 0, 1121    |
| FF-EX15 P06 | 260 x 69   | 286, 1121  |
| FF-EX13 P05 | 255 x 69   | 548, 1121  |
| FF-EX19 P08 | 130 x 69   | 805, 1121  |
| FF-EX8 P03  | 111 x 69   | 937, 1121  |
| FF-EX2 P06  | 104 x 69   | 1050, 1121 |
| FF-EX17 P05 | 95 x 69    | 1156, 1121 |
| FF-EX21 P05 | 95 x 69    | 1253, 1121 |
| FF-EX5 P05  | 95 x 69    | 1350, 1121 |
| FF-EX19 P09 | 65 x 69    | 1447, 1121 |
| FF-EX21 P08 | 57 x 69    | 1513, 1121 |
| FF-EX5 P08  | 55 x 69    | 1572, 1121 |
| FF-EX21 P07 | 42 x 69    | 1629, 1121 |
| FF-EX5 P07  | 42 x 69    | 1673, 1121 |
| FF-EX8 P05  | 21 x 69    | 1716, 1121 |
| FF-EX11 P04 | 18 x 69    | 1739, 1121 |
| FF-EX11 P07 | 18 x 69    | 1759, 1121 |
| FF-EX13 P03 | 18 x 69    | 1779, 1121 |
| FF-EX13 P06 | 18 x 69    | 1799, 1121 |
| FF-EX15 P05 | 18 x 69    | 1819, 1121 |
| FF-EX15 P08 | 18 x 69    | 1839, 1121 |
| FF-EX17 P04 | 18 x 69    | 1859, 1121 |
| FF-EX17 P08 | 18 x 69    | 1879, 1121 |
| FF-EX19 P06 | 18 x 69    | 1899, 1121 |
| FF-EX19 P10 | 18 x 69    | 1919, 1121 |
| FF-EX2 P05  | 18 x 69    | 1939, 1121 |
| FF-EX2 P09  | 18 x 69    | 1959, 1121 |
| FF-EX21 P04 | 18 x 69    | 1979, 1121 |
| FF-EX21 P10 | 18 x 69    | 1999, 1121 |
| FF-EX5 P04  | 18 x 69    | 2019, 1121 |
| FF-EX5 P10  | 18 x 69    | 2039, 1121 |
| FF-EX8 P02  | 18 x 69    | 2059, 1121 |
| FF-EX8 P06  | 18 x 69    | 2079, 1121 |
| FF-EX19 P01 | 155 x 2264 | 0, 964     |
| FF-EX5 P02  | 288 x 2264 | 0, 674     |
| FF-EX17 P02 | 313 x 2264 | 0, 359     |
| FF-EX13 P01 | 357 x 2264 | 0, 0       |

## NOTES

1. Cut from PIR 120mm 1200x2400, 2mm saw kerf. Viewed on the face; dimensions from the sheet's bottom-left corner (0,0). Red numbered lines = saw cuts in order, each edge to edge.
2. Coloured dimensions belong to the part of that colour: its width and height, and its position from the sheet edges. Raked labels: corner coordinates at each corner.
3. Red hatch = waste. Labels = panel + piece mark on the manufacture drawing.

## REVISIONS

| REV | DATE     | DESCRIPTION        |
|-----|----------|--------------------|
| C01 | 13.09.26 | Construction issue |



**TLS TIMBER FRAME** 

Design &amp; Manufacture

Scan: 3D model + drawings



CLIENT

MP Adams

|         |
|---------|
| PROJECT |
|---------|

MP Adams Plot 3, Eckington

DRAWING TITLE

**PIR CUTTING - FIRST FLOOR - SHEET 15 OF 23**


PIR 120mm 1200x2400 | First Floor

|       |      |          |       |
|-------|------|----------|-------|
| SCALE | SIZE | DATE     | DRAWN |
| NTS   | A3   | 13.09.26 | TS    |

|              |                   |     |
|--------------|-------------------|-----|
| STATUS       | DRAWING No.       | REV |
| CONSTRUCTION | P3-CP-PIR-02 / 15 | C01 |

Do not scale. All dimensions in mm. Check all dimensions on site.

Do not scale. All dimensions in mm. Check all dimensions on site.

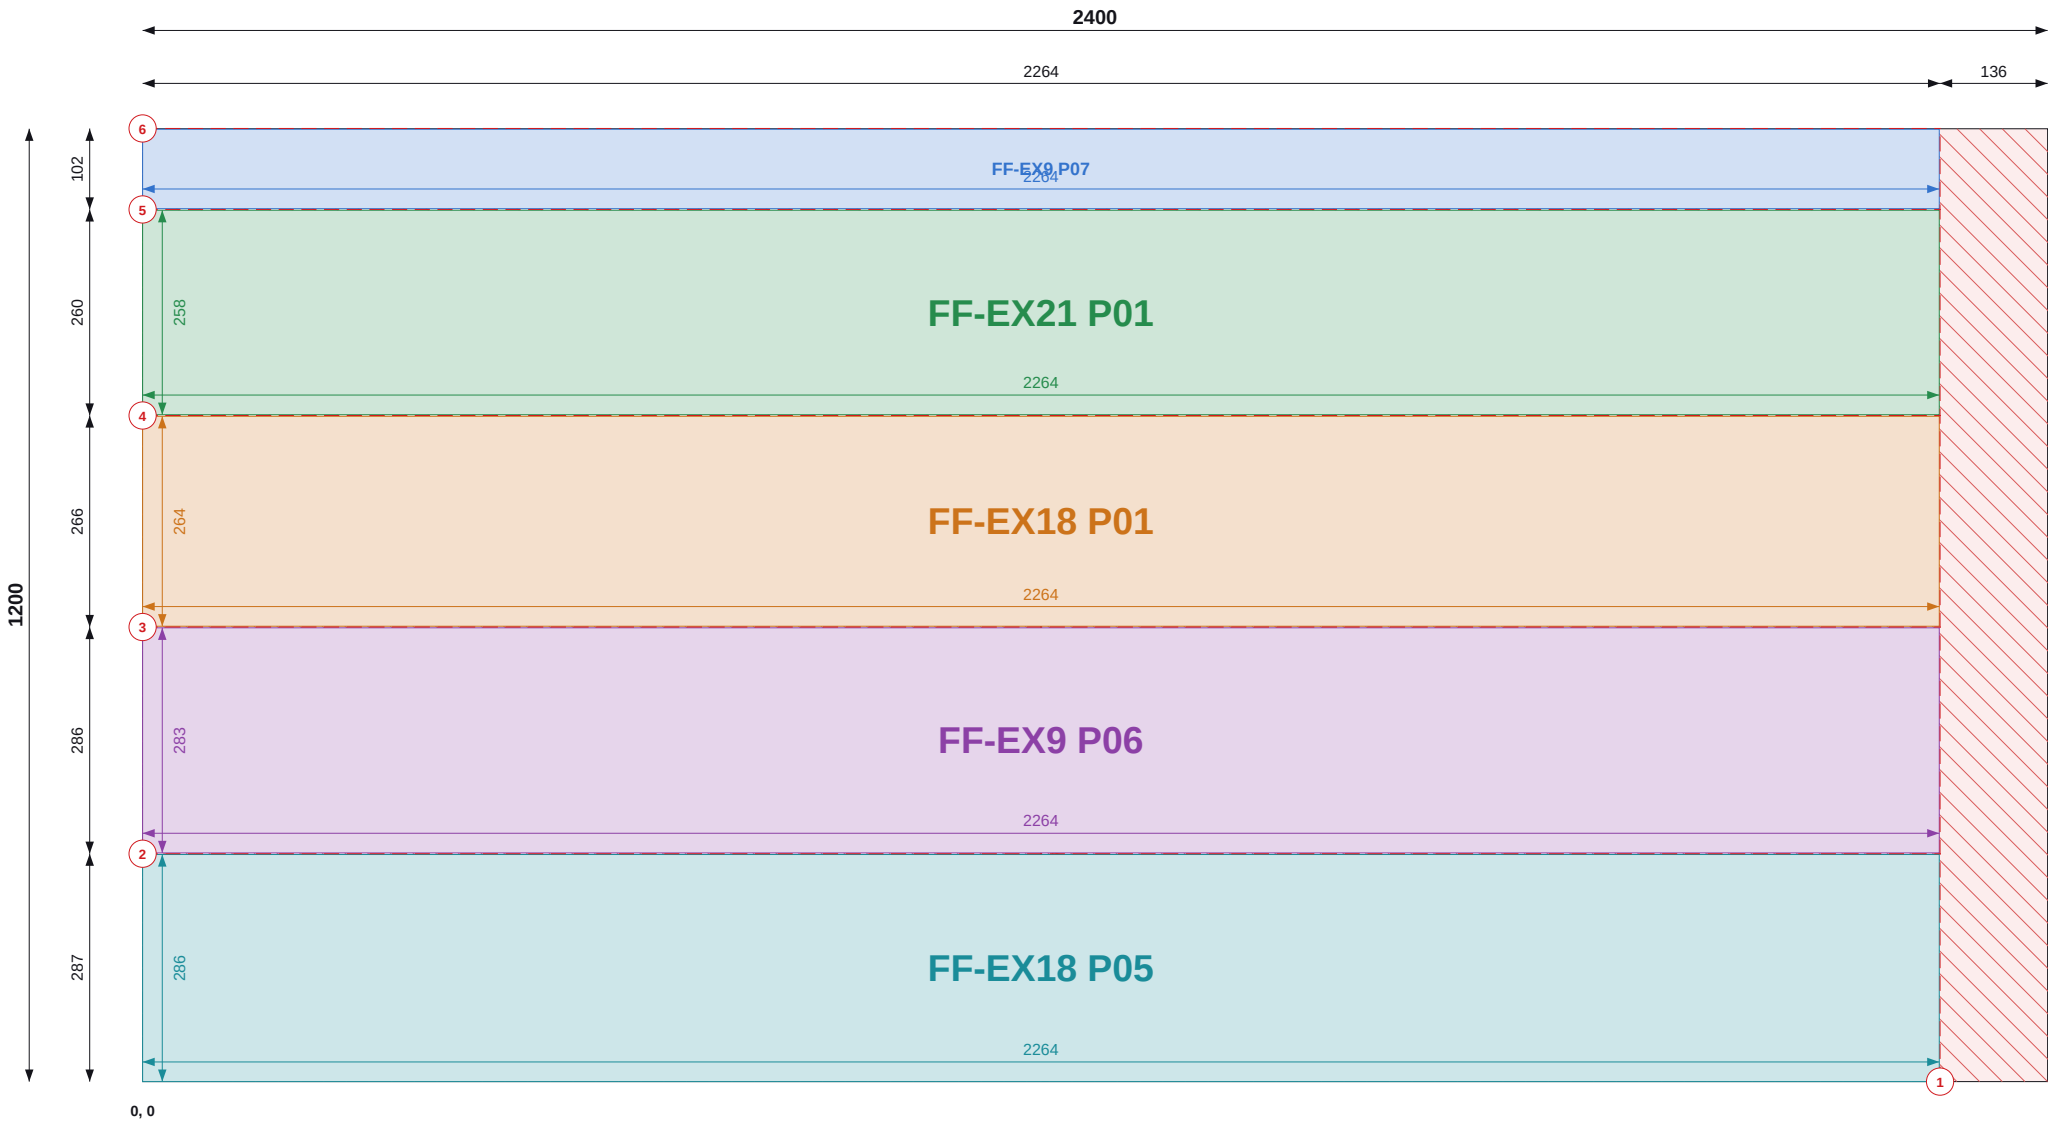

Top / left chains = saw cut positions (to cut centres). Coloured = part size and position.

SHEET 16 OF 23

THIS SHEET

| Item              | Value           |
|-------------------|-----------------|
| Parts             | 5               |
| Used / waste      | 93.6% / 0.18 m2 |
| Reusable offcuts  | 0               |
| Saw cuts / shared | 6 / 4           |

PIECES (POSITION = BOTTOM-LEFT CORNER)

| Label       | Size       | X, Y    |
|-------------|------------|---------|
| FF-EX9 P07  | 100 x 2264 | 0, 1099 |
| FF-EX21 P01 | 258 x 2264 | 0, 840  |
| FF-EX18 P01 | 264 x 2264 | 0, 574  |
| FF-EX9 P06  | 283 x 2264 | 0, 288  |
| FF-EX18 P05 | 286 x 2264 | 0, 0    |

NOTES

- Cut from PIR 120mm 1200x2400, 2mm saw kerf. Viewed on the face; dimensions from the sheet's bottom-left corner (0,0). Red numbered lines = saw cuts in order, each edge to edge.
- Coloured dimensions belong to the part of that colour: its width and height, and its position from the sheet edges. Raked parts: corner coordinates at each corner.
- Red hatch = waste. Labels = panel + piece mark on the manufacture drawing.

REVISIONS

| REV | DATE     | DESCRIPTION        |
|-----|----------|--------------------|
| C01 | 13.09.26 | Construction issue |



TLS TIMBER FRAME

Design & Manufacture

Scan: 3D model + drawings




|          |                            |
|----------|----------------------------|
| CLIENT   | PROJECT                    |
| MP Adams | MP Adams Plot 3, Eckington |

|                                            |  |  |  |
|--------------------------------------------|--|--|--|
| DRAWING TITLE                              |  |  |  |
| PIR CUTTING - FIRST FLOOR - SHEET 16 OF 23 |  |  |  |
| PIR 120mm 1200x2400   First Floor          |  |  |  |

|       |      |          |       |
|-------|------|----------|-------|
| SCALE | SIZE | DATE     | DRAWN |
| NTS   | A3   | 13.09.26 | TS    |

|              |                   |     |
|--------------|-------------------|-----|
| STATUS       | DRAWING No.       | REV |
| CONSTRUCTION | P3-CP-PIR-02 / 16 | C01 |

Do not scale. All dimensions in mm. Check all dimensions on site.

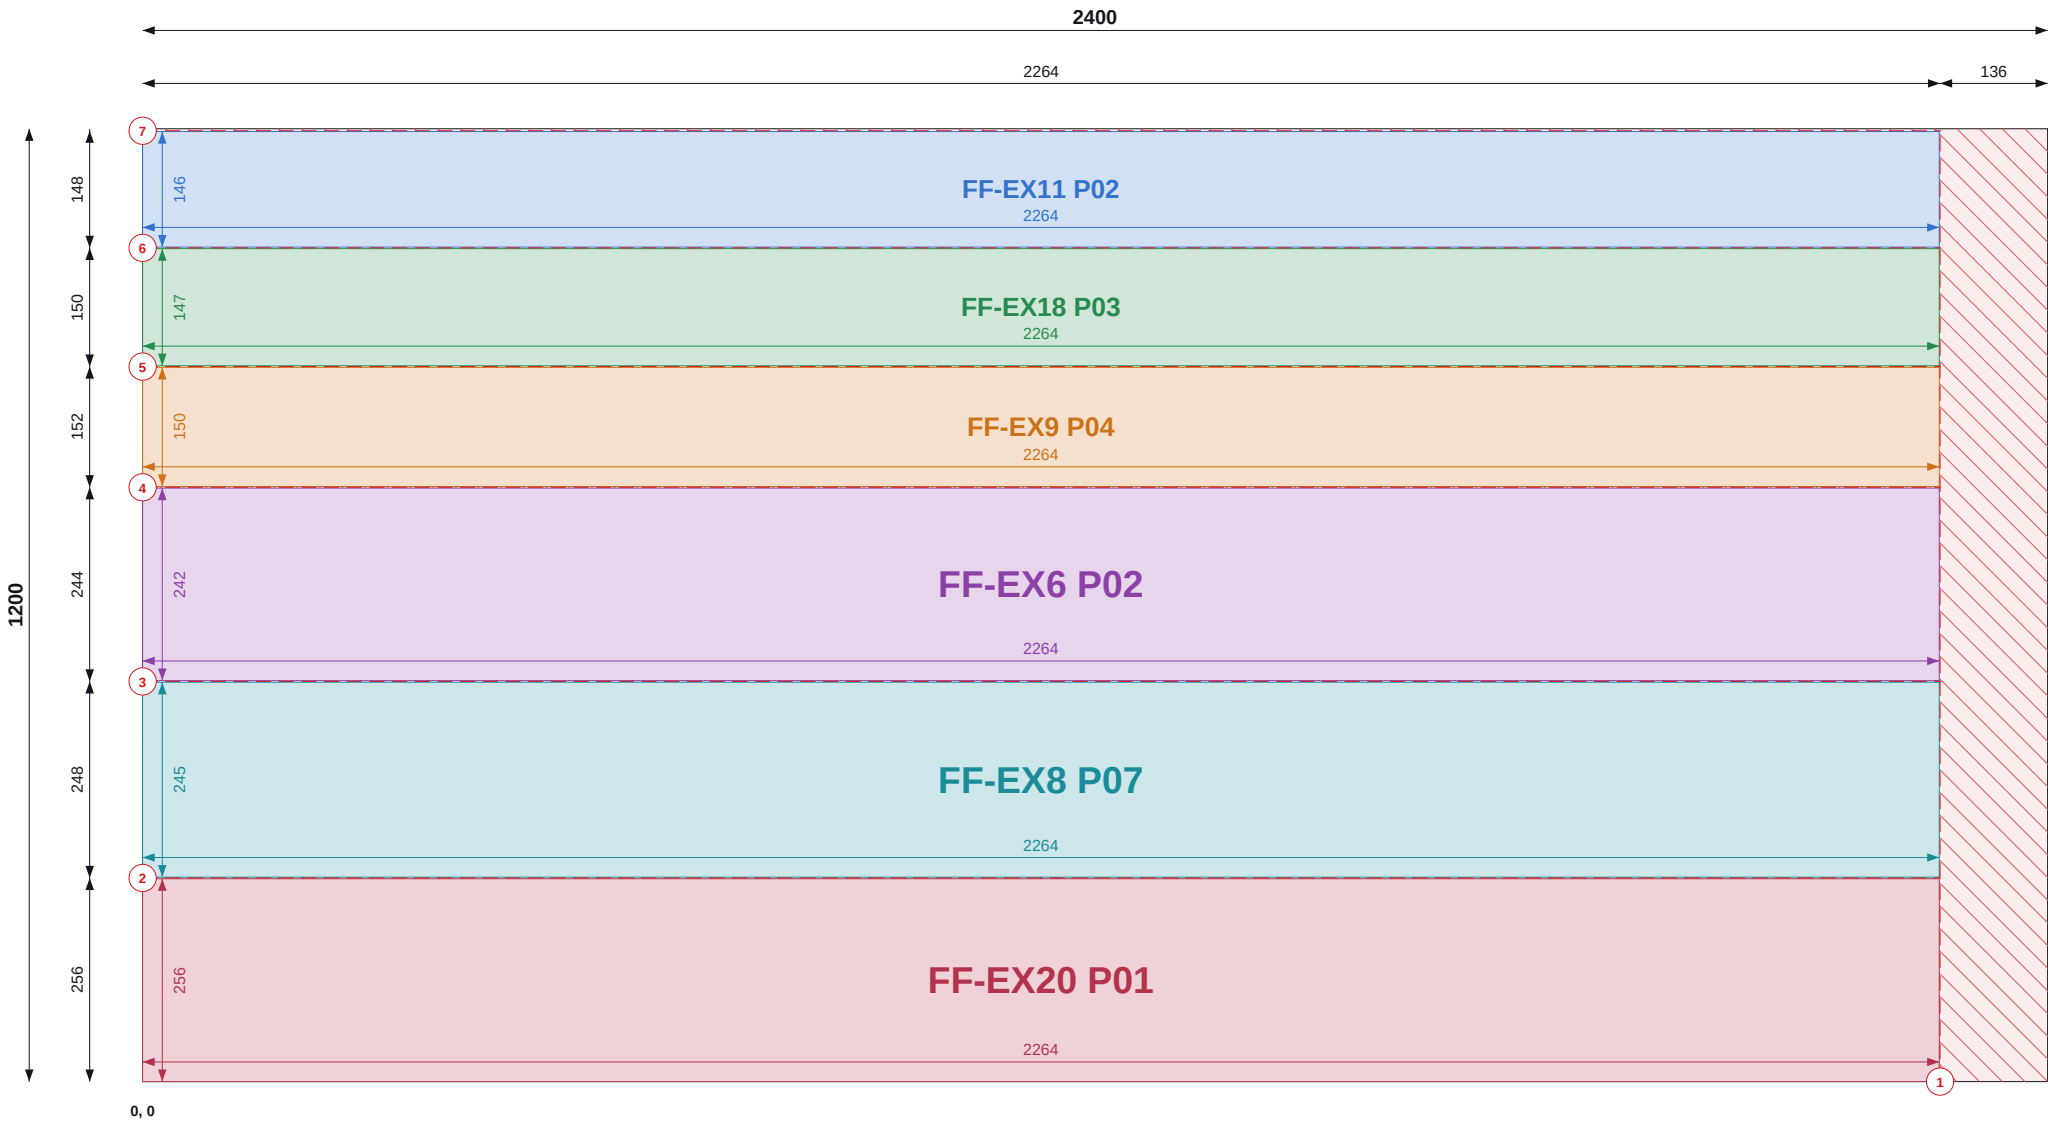

Top / left chains = saw cut positions (to cut centres). Coloured = part size and position.

SHEET 17 OF 23

THIS SHEET

| Item              | Value           |
|-------------------|-----------------|
| Parts             | 6               |
| Used / waste      | 93.3% / 0.19 m2 |
| Reusable offcuts  | 0               |
| Saw cuts / shared | 7 / 5           |

PIECES (POSITION = BOTTOM-LEFT CORNER)

| Label       | Size       | X, Y    |
|-------------|------------|---------|
| FF-EX11 P02 | 146 x 2264 | 0, 1051 |
| FF-EX18 P03 | 147 x 2264 | 0, 901  |
| FF-EX9 P04  | 150 x 2264 | 0, 749  |
| FF-EX6 P02  | 242 x 2264 | 0, 505  |
| FF-EX8 P07  | 245 x 2264 | 0, 258  |
| FF-EX20 P01 | 256 x 2264 | 0, 0    |

NOTES

- Cut from PIR 120mm 1200x2400, 2mm saw kerf. Viewed on the face; dimensions from the sheet's bottom-left corner (0,0). Red numbered lines = saw cuts in order, each edge to edge.
- Coloured dimensions belong to the part of that colour: its width and height, and its position from the sheet edges. Raked parts: corner coordinates at each corner.
- Red hatch = waste. Labels = panel + piece mark on the manufacture drawing.

REVISIONS

| REV | DATE     | DESCRIPTION        |
|-----|----------|--------------------|
| C01 | 13.09.26 | Construction issue |



TLS TIMBER FRAME

Design & Manufacture

Scan: 3D model + drawings



|          |                            |
|----------|----------------------------|
| CLIENT   | PROJECT                    |
| MP Adams | MP Adams Plot 3, Eckington |


|                                            |
|--------------------------------------------|
| DRAWING TITLE                              |
| PIR CUTTING - FIRST FLOOR - SHEET 17 OF 23 |

PIR 120mm 1200x2400 | First Floor

|       |      |          |       |
|-------|------|----------|-------|
| SCALE | SIZE | DATE     | DRAWN |
| NTS   | A3   | 13.09.26 | TS    |

|              |                   |     |
|--------------|-------------------|-----|
| STATUS       | DRAWING No.       | REV |
| CONSTRUCTION | P3-CP-PIR-02 / 17 | C01 |

Do not scale. All dimensions in mm. Check all dimensions on site.

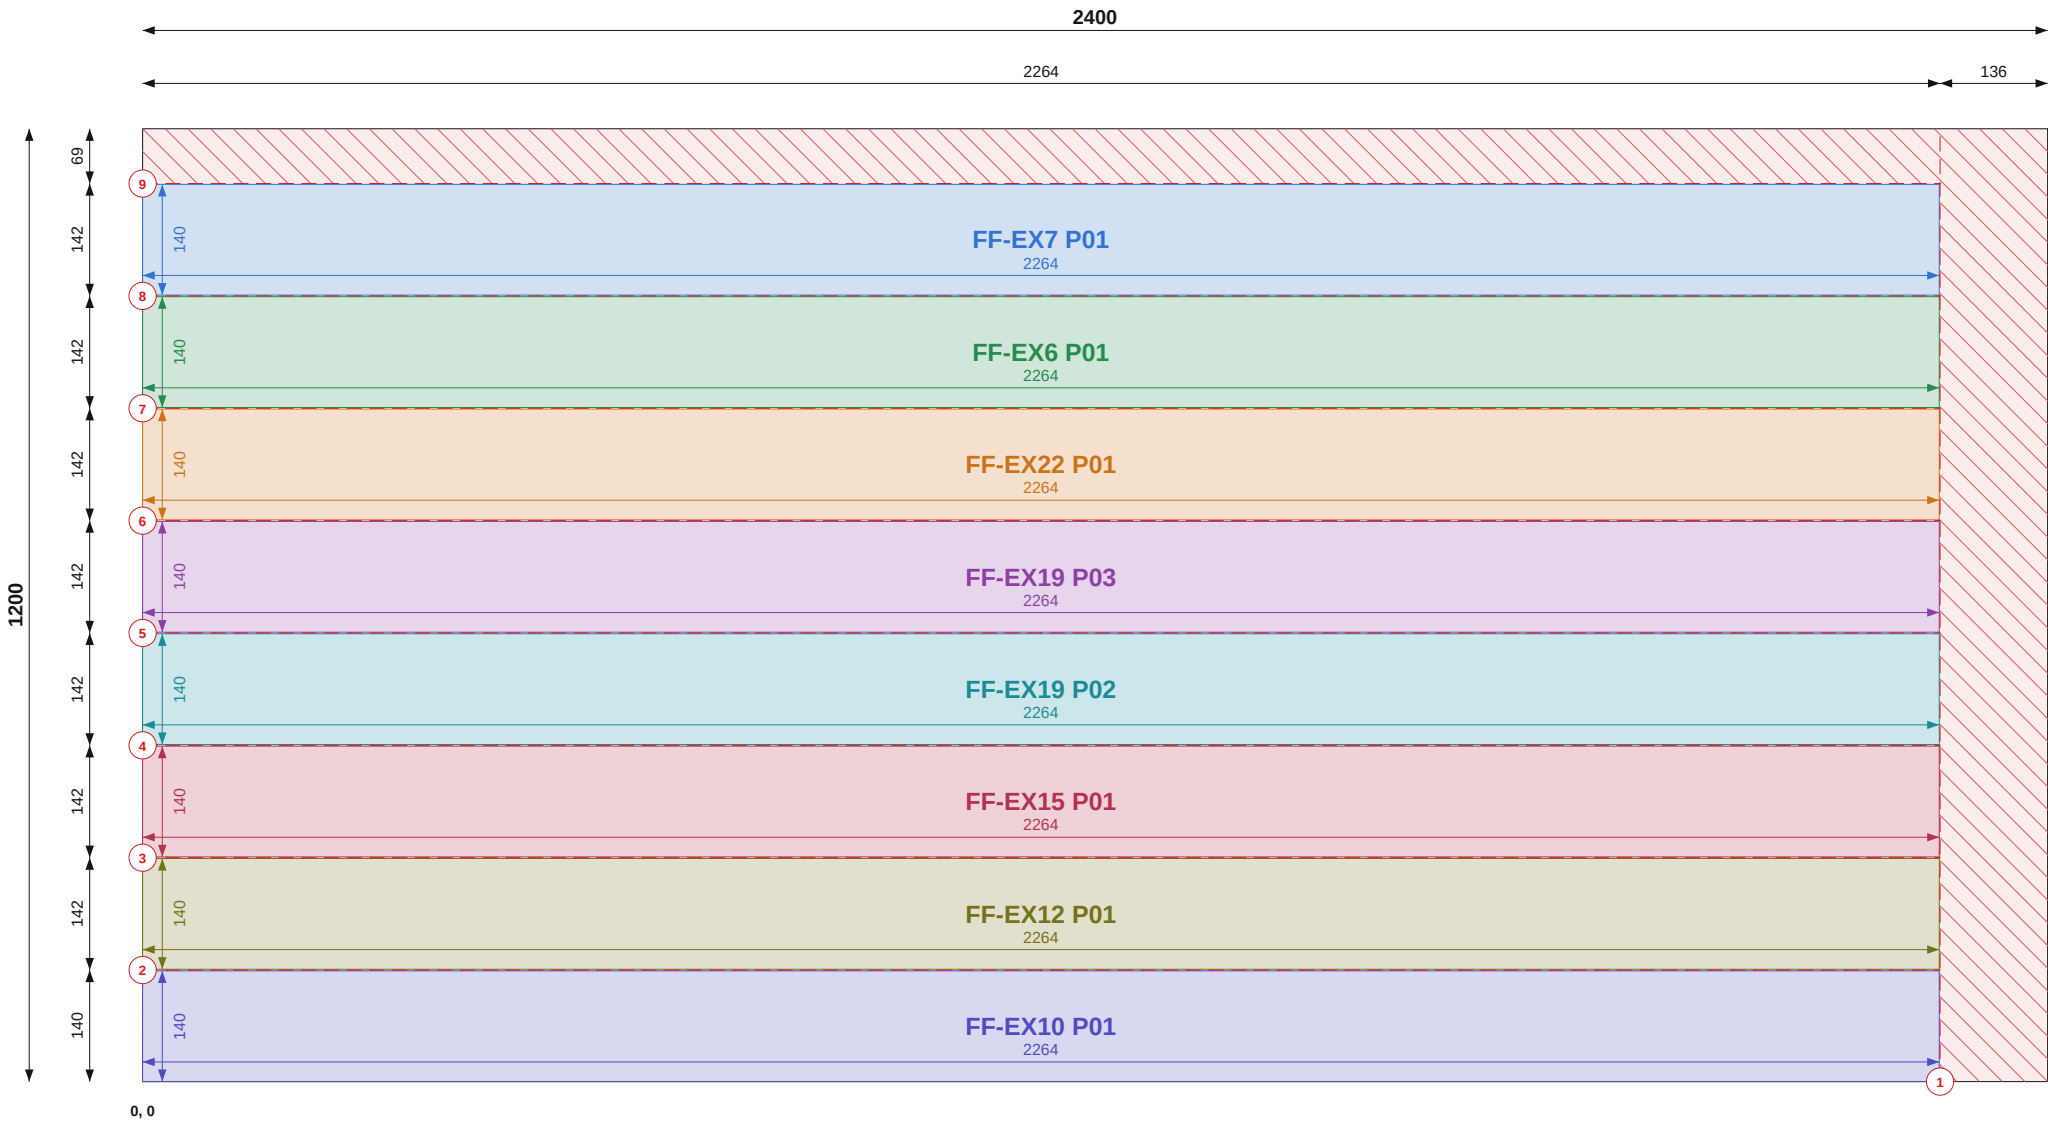

Top / left chains = saw cut positions (to cut centres). Coloured = part size and position.

SHEET 18 OF 23

THIS SHEET

| Item              | Value           |
|-------------------|-----------------|
| Parts             | 8               |
| Used / waste      | 87.7% / 0.35 m2 |
| Reusable offcuts  | 0               |
| Saw cuts / shared | 9 / 7           |

PIECES (POSITION = BOTTOM-LEFT CORNER)

| Label       | Size       | X, Y   |
|-------------|------------|--------|
| FF-EX7 P01  | 140 x 2264 | 0, 991 |
| FF-EX6 P01  | 140 x 2264 | 0, 849 |
| FF-EX22 P01 | 140 x 2264 | 0, 708 |
| FF-EX19 P03 | 140 x 2264 | 0, 566 |
| FF-EX19 P02 | 140 x 2264 | 0, 425 |
| FF-EX15 P01 | 140 x 2264 | 0, 283 |
| FF-EX12 P01 | 140 x 2264 | 0, 142 |
| FF-EX10 P01 | 140 x 2264 | 0, 0   |

NOTES

- Cut from PIR 120mm 1200x2400, 2mm saw kerf. Viewed on the face; dimensions from the sheet's bottom-left corner (0,0). Red numbered lines = saw cuts in order, each edge to edge.
- Coloured dimensions belong to the part of that colour: its width and height, and its position from the sheet edges. Raked parts: corner coordinates at each corner.
- Red hatch = waste. Labels = panel + piece mark on the manufacture drawing.

REVISIONS

| REV | DATE     | DESCRIPTION        |
|-----|----------|--------------------|
| C01 | 13.09.26 | Construction issue |



TLS TIMBER FRAME

Design & Manufacture

Scan: 3D model + drawings



|          |                            |
|----------|----------------------------|
| CLIENT   | PROJECT                    |
| MP Adams | MP Adams Plot 3, Eckington |


|                                            |
|--------------------------------------------|
| DRAWING TITLE                              |
| PIR CUTTING - FIRST FLOOR - SHEET 18 OF 23 |

PIR 120mm 1200x2400 | First Floor

|       |      |          |       |
|-------|------|----------|-------|
| SCALE | SIZE | DATE     | DRAWN |
| NTS   | A3   | 13.09.26 | TS    |

|              |                   |     |
|--------------|-------------------|-----|
| STATUS       | DRAWING No.       | REV |
| CONSTRUCTION | P3-CP-PIR-02 / 18 | C01 |

Do not scale. All dimensions in mm. Check all dimensions on site.

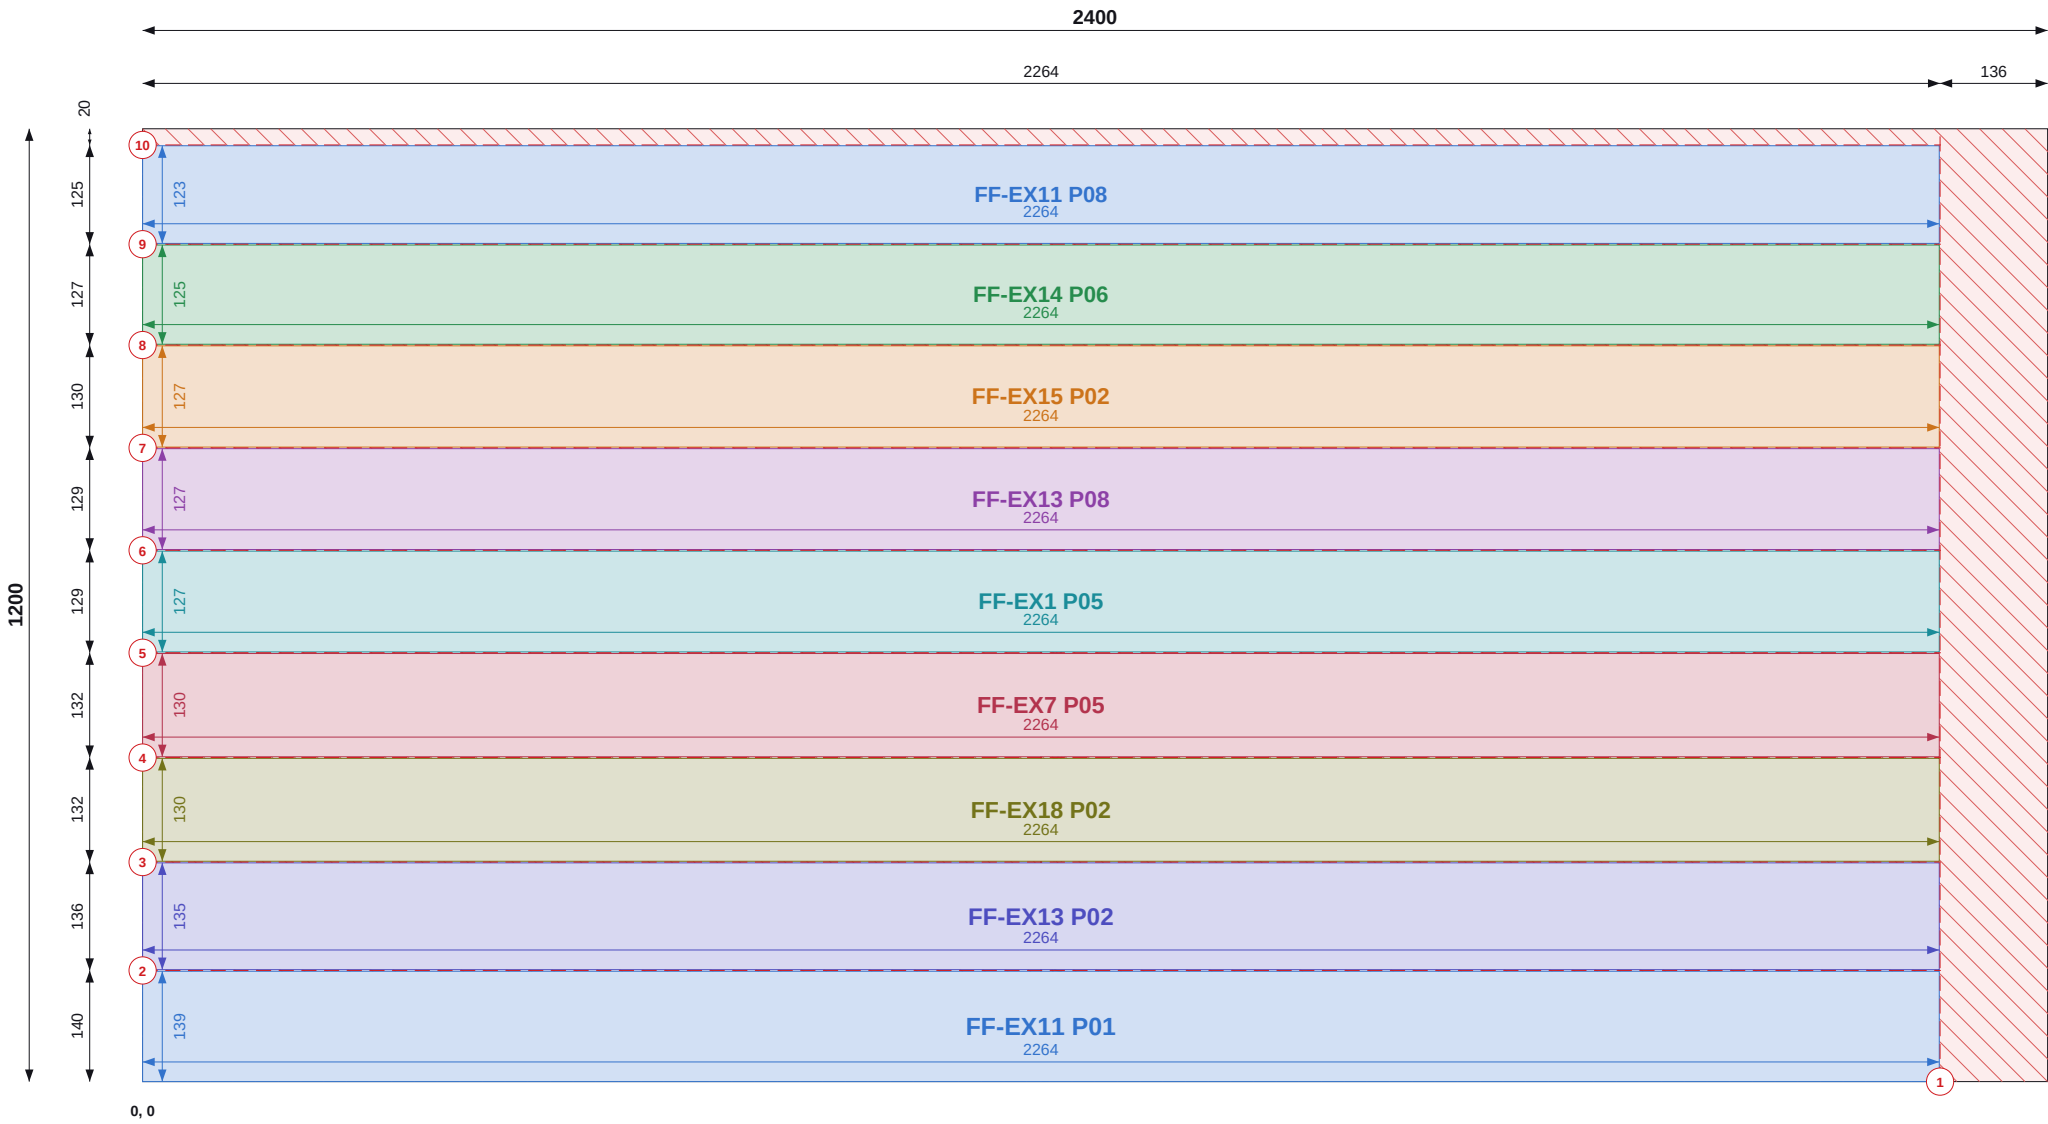

Top / left chains = saw cut positions (to cut centres). Coloured = part size and position.

SHEET 19 OF 23

THIS SHEET

| Item              | Value           |
|-------------------|-----------------|
| Parts             | 9               |
| Used / waste      | 91.4% / 0.25 m2 |
| Reusable offcuts  | 0               |
| Saw cuts / shared | 10 / 8          |

PIECES (POSITION = BOTTOM-LEFT CORNER)

| Label       | Size       | X, Y    |
|-------------|------------|---------|
| FF-EX11 P08 | 123 x 2264 | 0, 1056 |
| FF-EX14 P06 | 125 x 2264 | 0, 929  |
| FF-EX15 P02 | 127 x 2264 | 0, 799  |
| FF-EX13 P08 | 127 x 2264 | 0, 670  |
| FF-EX1 P05  | 127 x 2264 | 0, 541  |
| FF-EX7 P05  | 130 x 2264 | 0, 409  |
| FF-EX18 P02 | 130 x 2264 | 0, 278  |
| FF-EX13 P02 | 135 x 2264 | 0, 141  |
| FF-EX11 P01 | 139 x 2264 | 0, 0    |

NOTES

- Cut from PIR 120mm 1200x2400, 2mm saw kerf. Viewed on the face; dimensions from the sheet's bottom-left corner (0,0). Red numbered lines = saw cuts in order, each edge to edge.
- Coloured dimensions belong to the part of that colour: its width and height, and its position from the sheet edges. Raked parts: corner coordinates at each corner.
- Red hatch = waste. Labels = panel + piece mark on the manufacture drawing.

REVISIONS

| REV | DATE     | DESCRIPTION        |
|-----|----------|--------------------|
| C01 | 13.09.26 | Construction issue |



TLS TIMBER FRAME

Design & Manufacture

Scan: 3D model + drawings



|          |                            |
|----------|----------------------------|
| CLIENT   | PROJECT                    |
| MP Adams | MP Adams Plot 3, Eckington |


DRAWING TITLE  
**PIR CUTTING - FIRST FLOOR - SHEET 19 OF 23**

PIR 120mm 1200x2400 | First Floor

|       |      |          |       |
|-------|------|----------|-------|
| SCALE | SIZE | DATE     | DRAWN |
| NTS   | A3   | 13.09.26 | TS    |

|              |                   |     |
|--------------|-------------------|-----|
| STATUS       | DRAWING No.       | REV |
| CONSTRUCTION | P3-CP-PIR-02 / 19 | C01 |

Do not scale. All dimensions in mm. Check all dimensions on site.

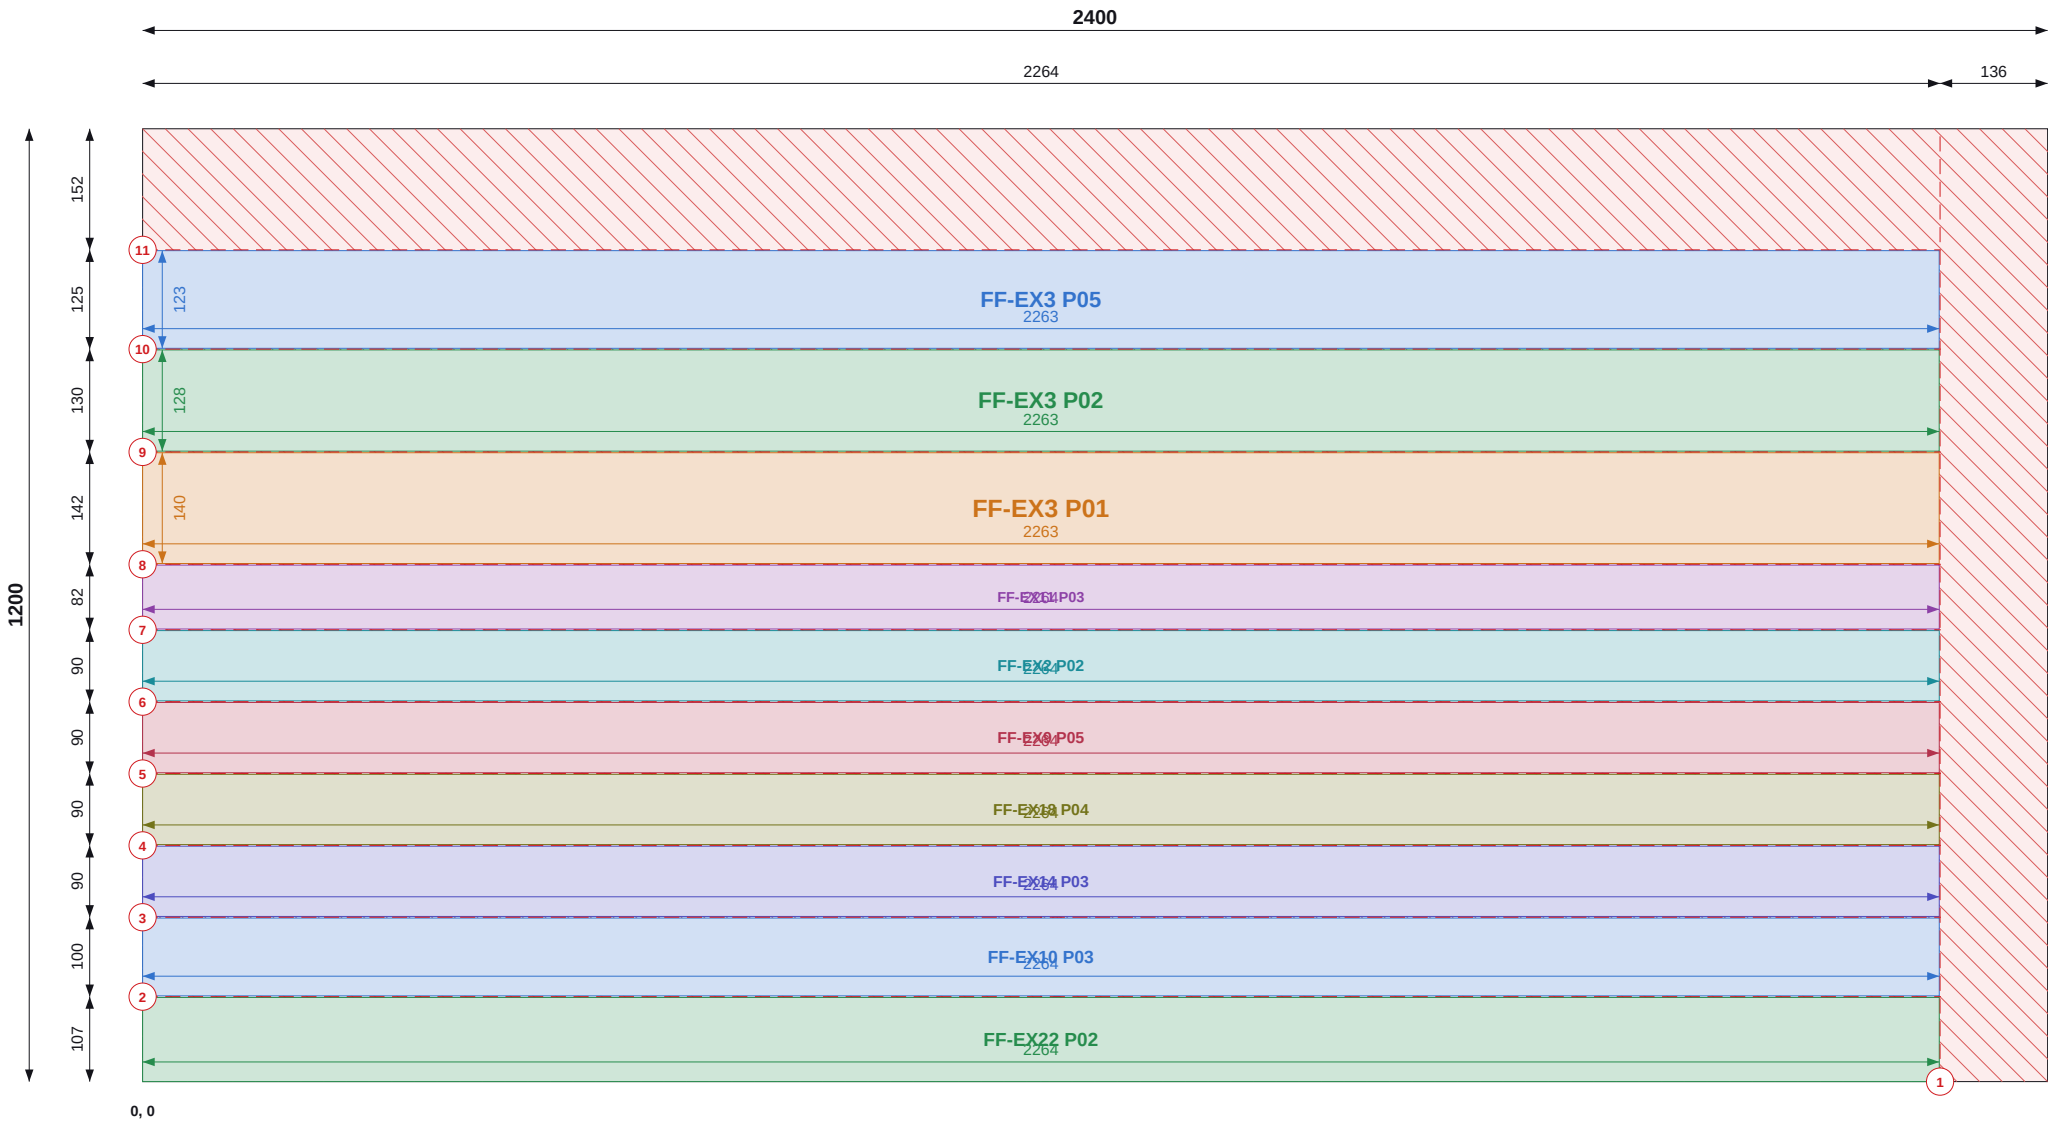

Top / left chains = saw cut positions (to cut centres). Coloured = part size and position.

SHEET 20 OF 23

THIS SHEET

| Item              | Value           |
|-------------------|-----------------|
| Parts             | 10              |
| Used / waste      | 80.8% / 0.55 m2 |
| Reusable offcuts  | 0               |
| Saw cuts / shared | 11 / 9          |

PIECES (POSITION = BOTTOM-LEFT CORNER)

| Label       | Size       | X, Y   |
|-------------|------------|--------|
| FF-EX3 P05  | 123 x 2263 | 0, 923 |
| FF-EX3 P02  | 128 x 2263 | 0, 794 |
| FF-EX3 P01  | 140 x 2263 | 0, 652 |
| FF-EX11 P03 | 80 x 2264  | 0, 570 |
| FF-EX2 P02  | 88 x 2264  | 0, 480 |
| FF-EX9 P05  | 89 x 2264  | 0, 389 |
| FF-EX18 P04 | 89 x 2264  | 0, 299 |
| FF-EX14 P03 | 89 x 2264  | 0, 208 |
| FF-EX10 P03 | 98 x 2264  | 0, 108 |
| FF-EX22 P02 | 106 x 2264 | 0, 0   |

NOTES

- Cut from PIR 120mm 1200x2400, 2mm saw kerf. Viewed on the face; dimensions from the sheet's bottom-left corner (0,0). Red numbered lines = saw cuts in order, each edge to edge.
- Coloured dimensions belong to the part of that colour: its width and height, and its position from the sheet edges. Raked parts: corner coordinates at each corner.
- Red hatch = waste. Labels = panel + piece mark on the manufacture drawing.

REVISIONS

| REV | DATE     | DESCRIPTION        |
|-----|----------|--------------------|
| C01 | 13.09.26 | Construction issue |



**TLS TIMBER FRAME**  
Design & Manufacture  
Scan: 3D model + drawings



|          |                            |
|----------|----------------------------|
| CLIENT   | PROJECT                    |
| MP Adams | MP Adams Plot 3, Eckington |


DRAWING TITLE  
**PIR CUTTING - FIRST FLOOR - SHEET 20 OF 23**

PIR 120mm 1200x2400 | First Floor

|       |      |          |       |
|-------|------|----------|-------|
| SCALE | SIZE | DATE     | DRAWN |
| NTS   | A3   | 13.09.26 | TS    |

|              |                          |     |
|--------------|--------------------------|-----|
| STATUS       | DRAWING No.              | REV |
| CONSTRUCTION | <b>P3-CP-PIR-02 / 20</b> | C01 |

Do not scale. All dimensions in mm. Check all dimensions on site.

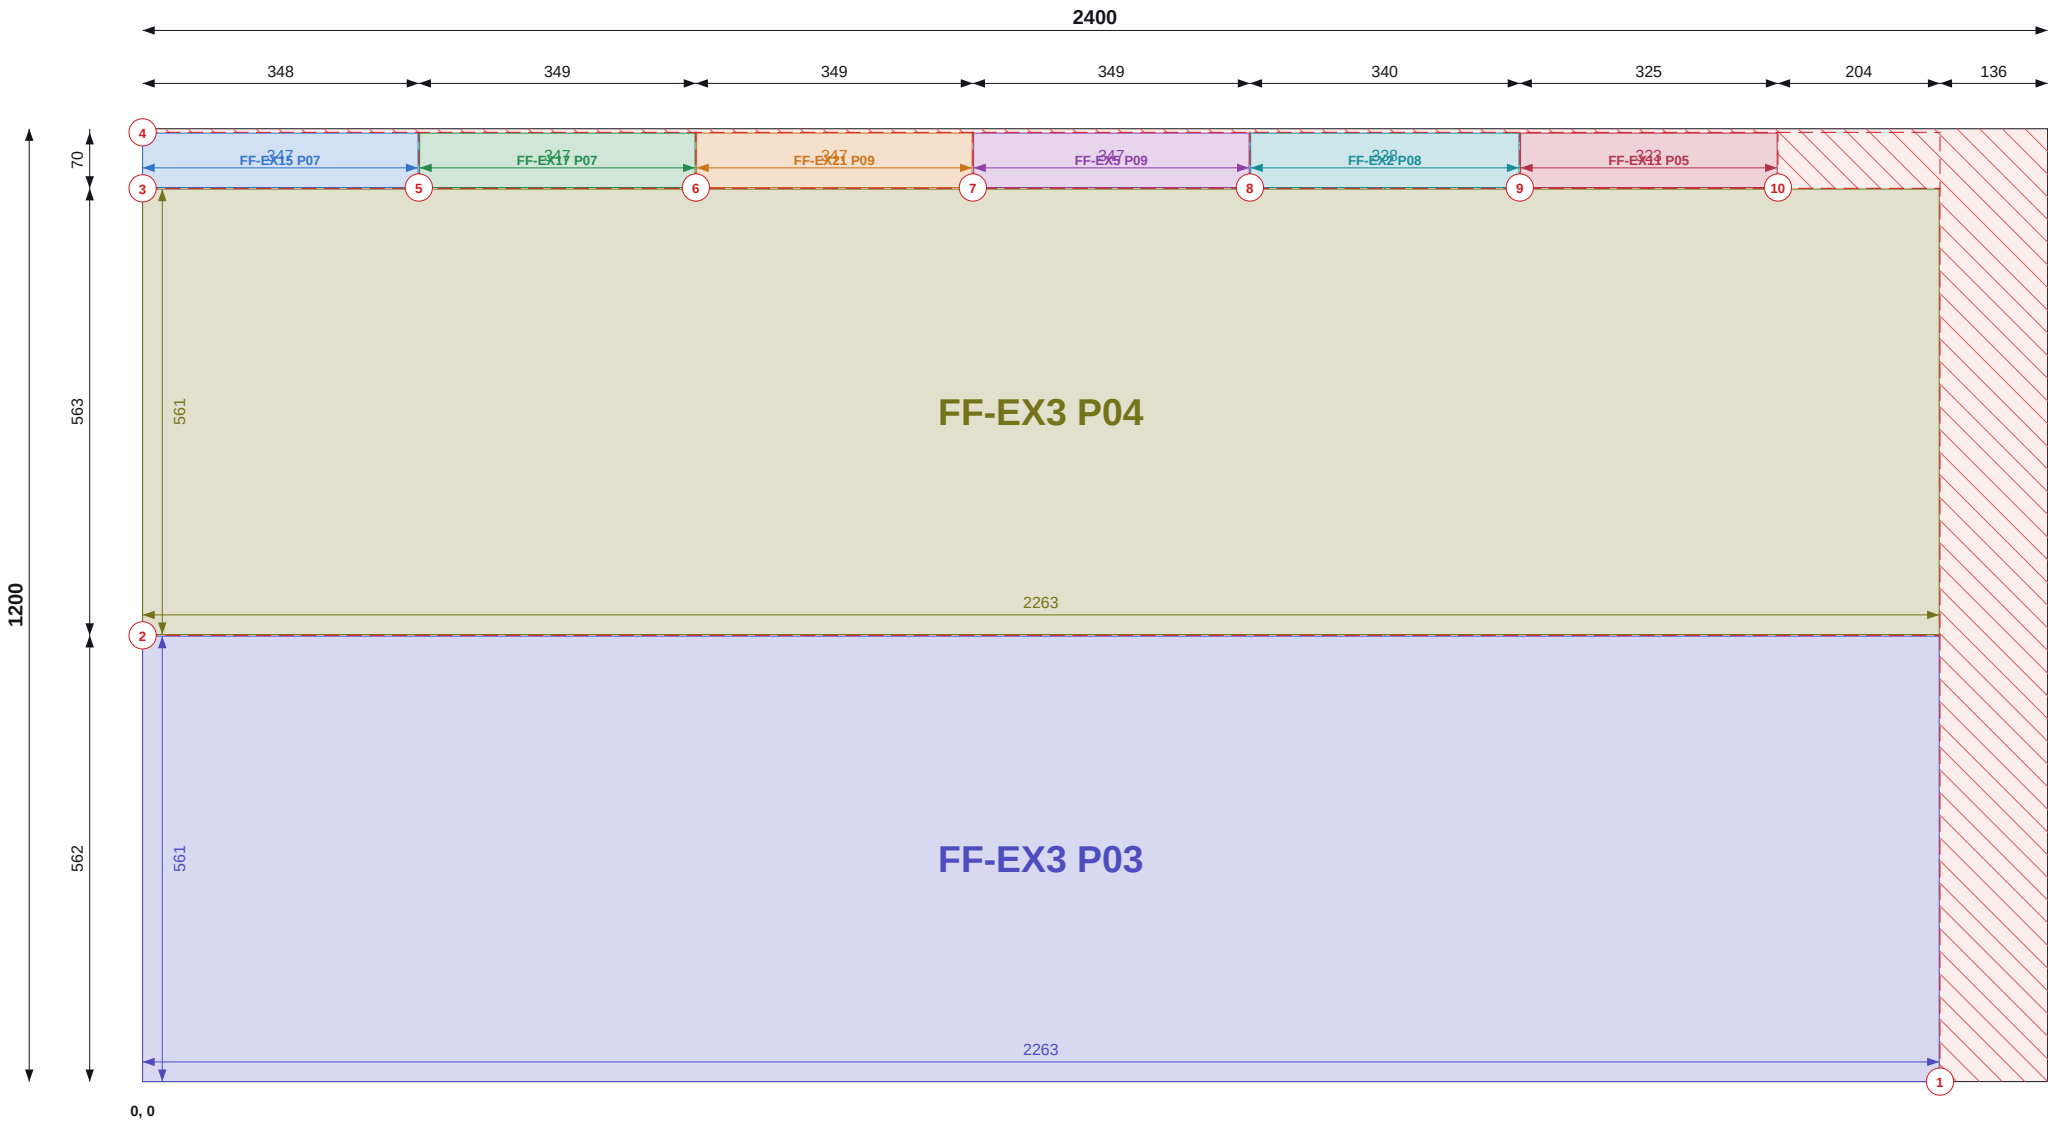

Top / left chains = saw cut positions (to cut centres). Coloured = part size and position.

SHEET 21 OF 23

THIS SHEET

| Item              | Value           |
|-------------------|-----------------|
| Parts             | 8               |
| Used / waste      | 93.1% / 0.20 m2 |
| Reusable offcuts  | 0               |
| Saw cuts / shared | 10 / 7          |

PIECES (POSITION = BOTTOM-LEFT CORNER)

| Label       | Size       | X, Y       |
|-------------|------------|------------|
| FF-EX15 P07 | 347 x 69   | 0, 1126    |
| FF-EX17 P07 | 347 x 69   | 349, 1126  |
| FF-EX21 P09 | 347 x 69   | 698, 1126  |
| FF-EX5 P09  | 347 x 69   | 1047, 1126 |
| FF-EX2 P08  | 338 x 69   | 1396, 1126 |
| FF-EX11 P05 | 323 x 69   | 1736, 1126 |
| FF-EX3 P04  | 561 x 2263 | 0, 563     |
| FF-EX3 P03  | 561 x 2263 | 0, 0       |

NOTES

- Cut from PIR 120mm 1200x2400, 2mm saw kerf. Viewed on the face; dimensions from the sheet's bottom-left corner (0,0). Red numbered lines = saw cuts in order, each edge to edge.
- Coloured dimensions belong to the part of that colour: its width and height, and its position from the sheet edges. Raked parts: corner coordinates at each corner.
- Red hatch = waste. Labels = panel + piece mark on the manufacture drawing.

REVISIONS

| REV | DATE     | DESCRIPTION        |
|-----|----------|--------------------|
| C01 | 13.09.26 | Construction issue |



TLS TIMBER FRAME

Design & Manufacture

Scan: 3D model + drawings




|          |                            |
|----------|----------------------------|
| CLIENT   | PROJECT                    |
| MP Adams | MP Adams Plot 3, Eckington |

|                                            |  |  |  |
|--------------------------------------------|--|--|--|
| DRAWING TITLE                              |  |  |  |
| PIR CUTTING - FIRST FLOOR - SHEET 21 OF 23 |  |  |  |
| PIR 120mm 1200x2400   First Floor          |  |  |  |

|       |      |          |       |
|-------|------|----------|-------|
| SCALE | SIZE | DATE     | DRAWN |
| NTS   | A3   | 13.09.26 | TS    |

|              |                   |     |
|--------------|-------------------|-----|
| STATUS       | DRAWING No.       | REV |
| CONSTRUCTION | P3-CP-PIR-02 / 21 | C01 |

Do not scale. All dimensions in mm. Check all dimensions on site.

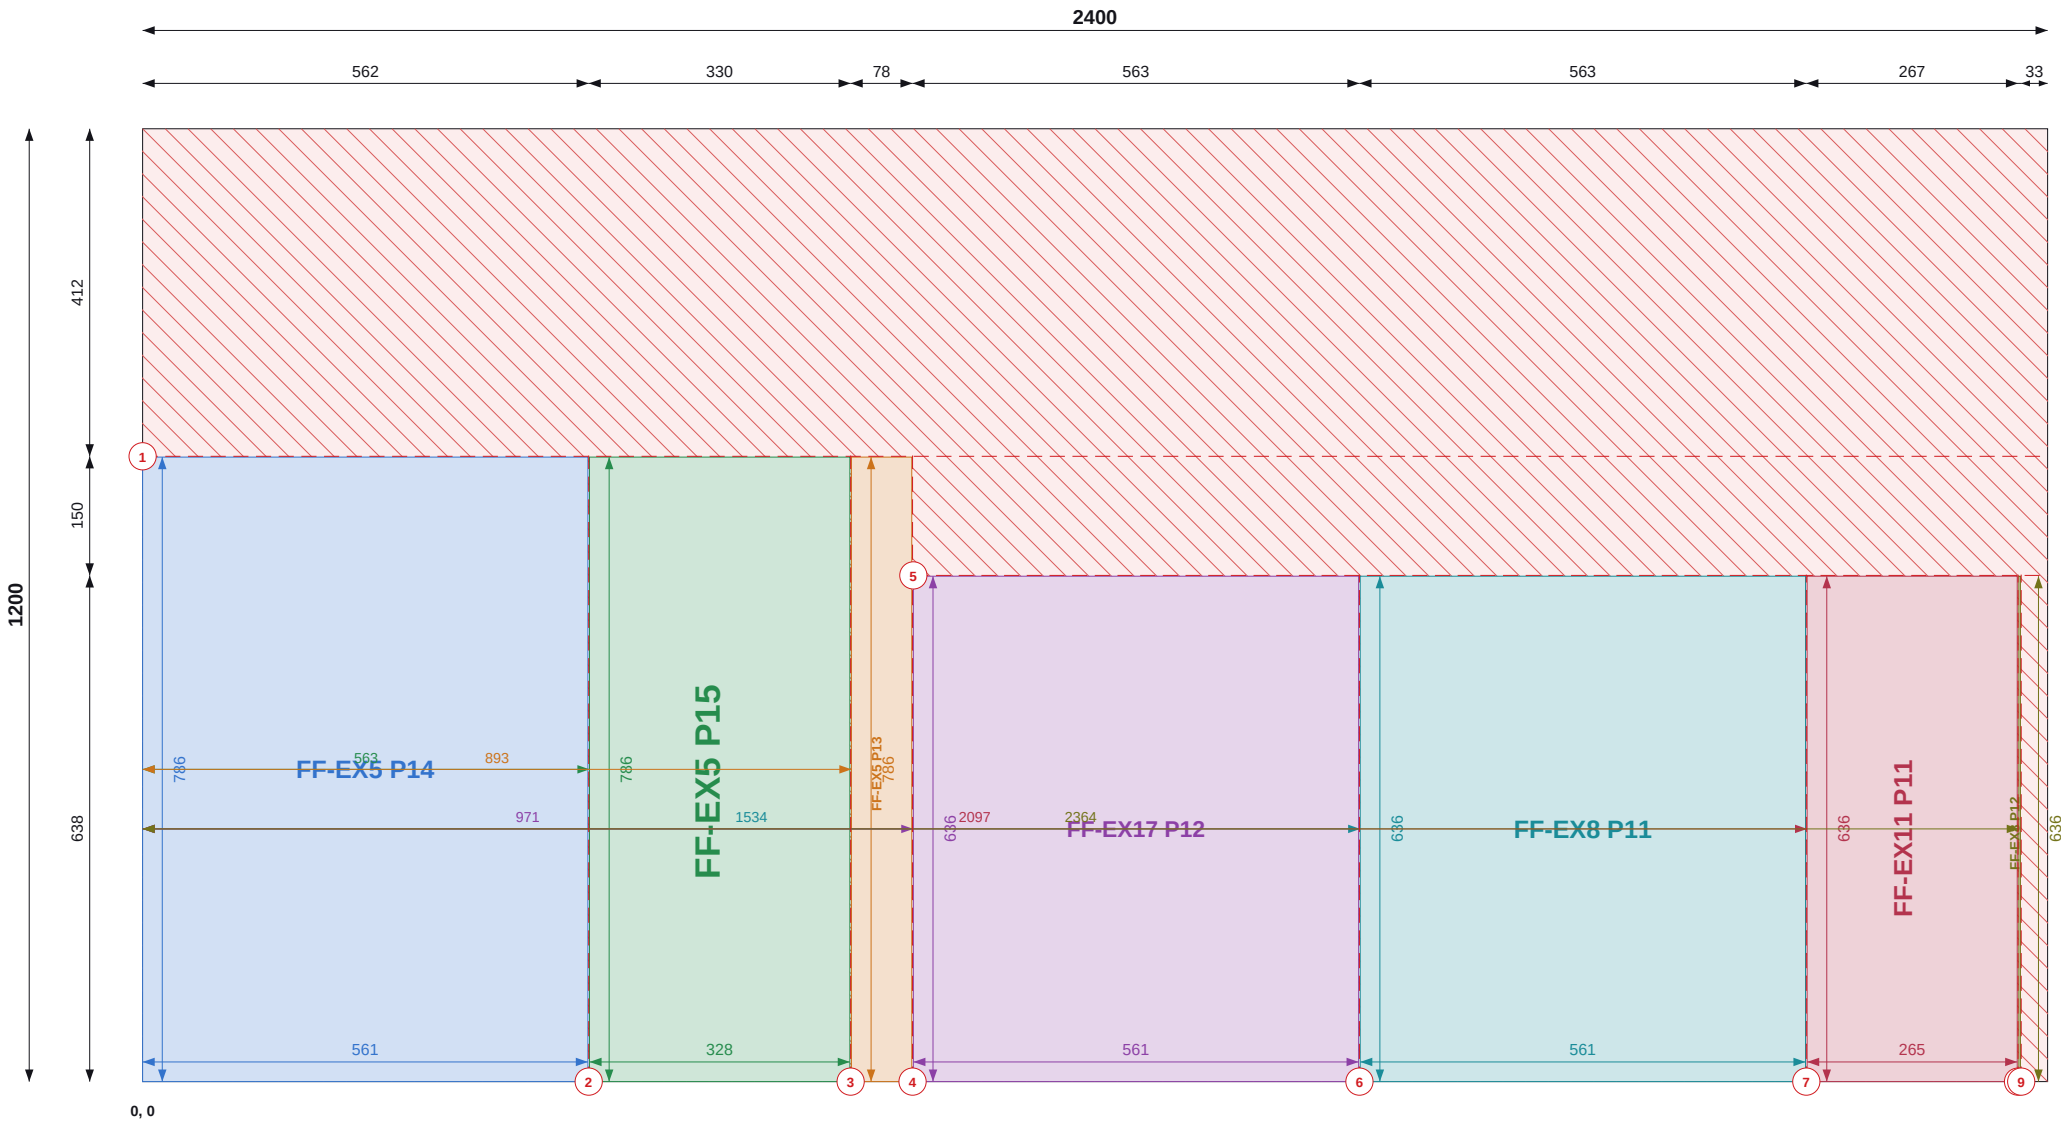

Top / left chains = saw cut positions (to cut centres). Coloured = part size and position.

SHEET 22 OF 23

THIS SHEET

| Item              | Value           |
|-------------------|-----------------|
| Parts             | 7               |
| Used / waste      | 57.0% / 1.24 m2 |
| Reusable offcuts  | 1               |
| Saw cuts / shared | 9 / 6           |

PIECES (POSITION = BOTTOM-LEFT CORNER)

| Label       | Size      | X, Y    |
|-------------|-----------|---------|
| FF-EX5 P14  | 561 x 786 | 0, 0    |
| FF-EX5 P15  | 328 x 786 | 563, 0  |
| FF-EX5 P13  | 76 x 786  | 893, 0  |
| FF-EX17 P12 | 561 x 636 | 971, 0  |
| FF-EX8 P11  | 561 x 636 | 1534, 0 |
| FF-EX11 P11 | 265 x 636 | 2097, 0 |
| FF-EX8 P12  | 2 x 636   | 2364, 0 |

NOTES

- Cut from PIR 120mm 1200x2400, 2mm saw kerf. Viewed on the face; dimensions from the sheet's bottom-left corner (0,0). Red numbered lines = saw cuts in order, each edge to edge.
- Coloured dimensions belong to the part of that colour: its width and height, and its position from the sheet edges. Raked parts: corner coordinates at each corner.
- Red hatch = waste. Labels = panel + piece mark on the manufacture drawing.

REVISIONS

| REV | DATE     | DESCRIPTION        |
|-----|----------|--------------------|
| C01 | 13.09.26 | Construction issue |



TLS TIMBER FRAME

Design & Manufacture

Scan: 3D model + drawings



|          |                            |
|----------|----------------------------|
| CLIENT   | PROJECT                    |
| MP Adams | MP Adams Plot 3, Eckington |


|                                            |
|--------------------------------------------|
| DRAWING TITLE                              |
| PIR CUTTING - FIRST FLOOR - SHEET 22 OF 23 |

PIR 120mm 1200x2400 | First Floor

|       |      |          |       |
|-------|------|----------|-------|
| SCALE | SIZE | DATE     | DRAWN |
| NTS   | A3   | 13.09.26 | TS    |

|              |                   |     |
|--------------|-------------------|-----|
| STATUS       | DRAWING No.       | REV |
| CONSTRUCTION | P3-CP-PIR-02 / 22 | C01 |

Do not scale. All dimensions in mm. Check all dimensions on site.

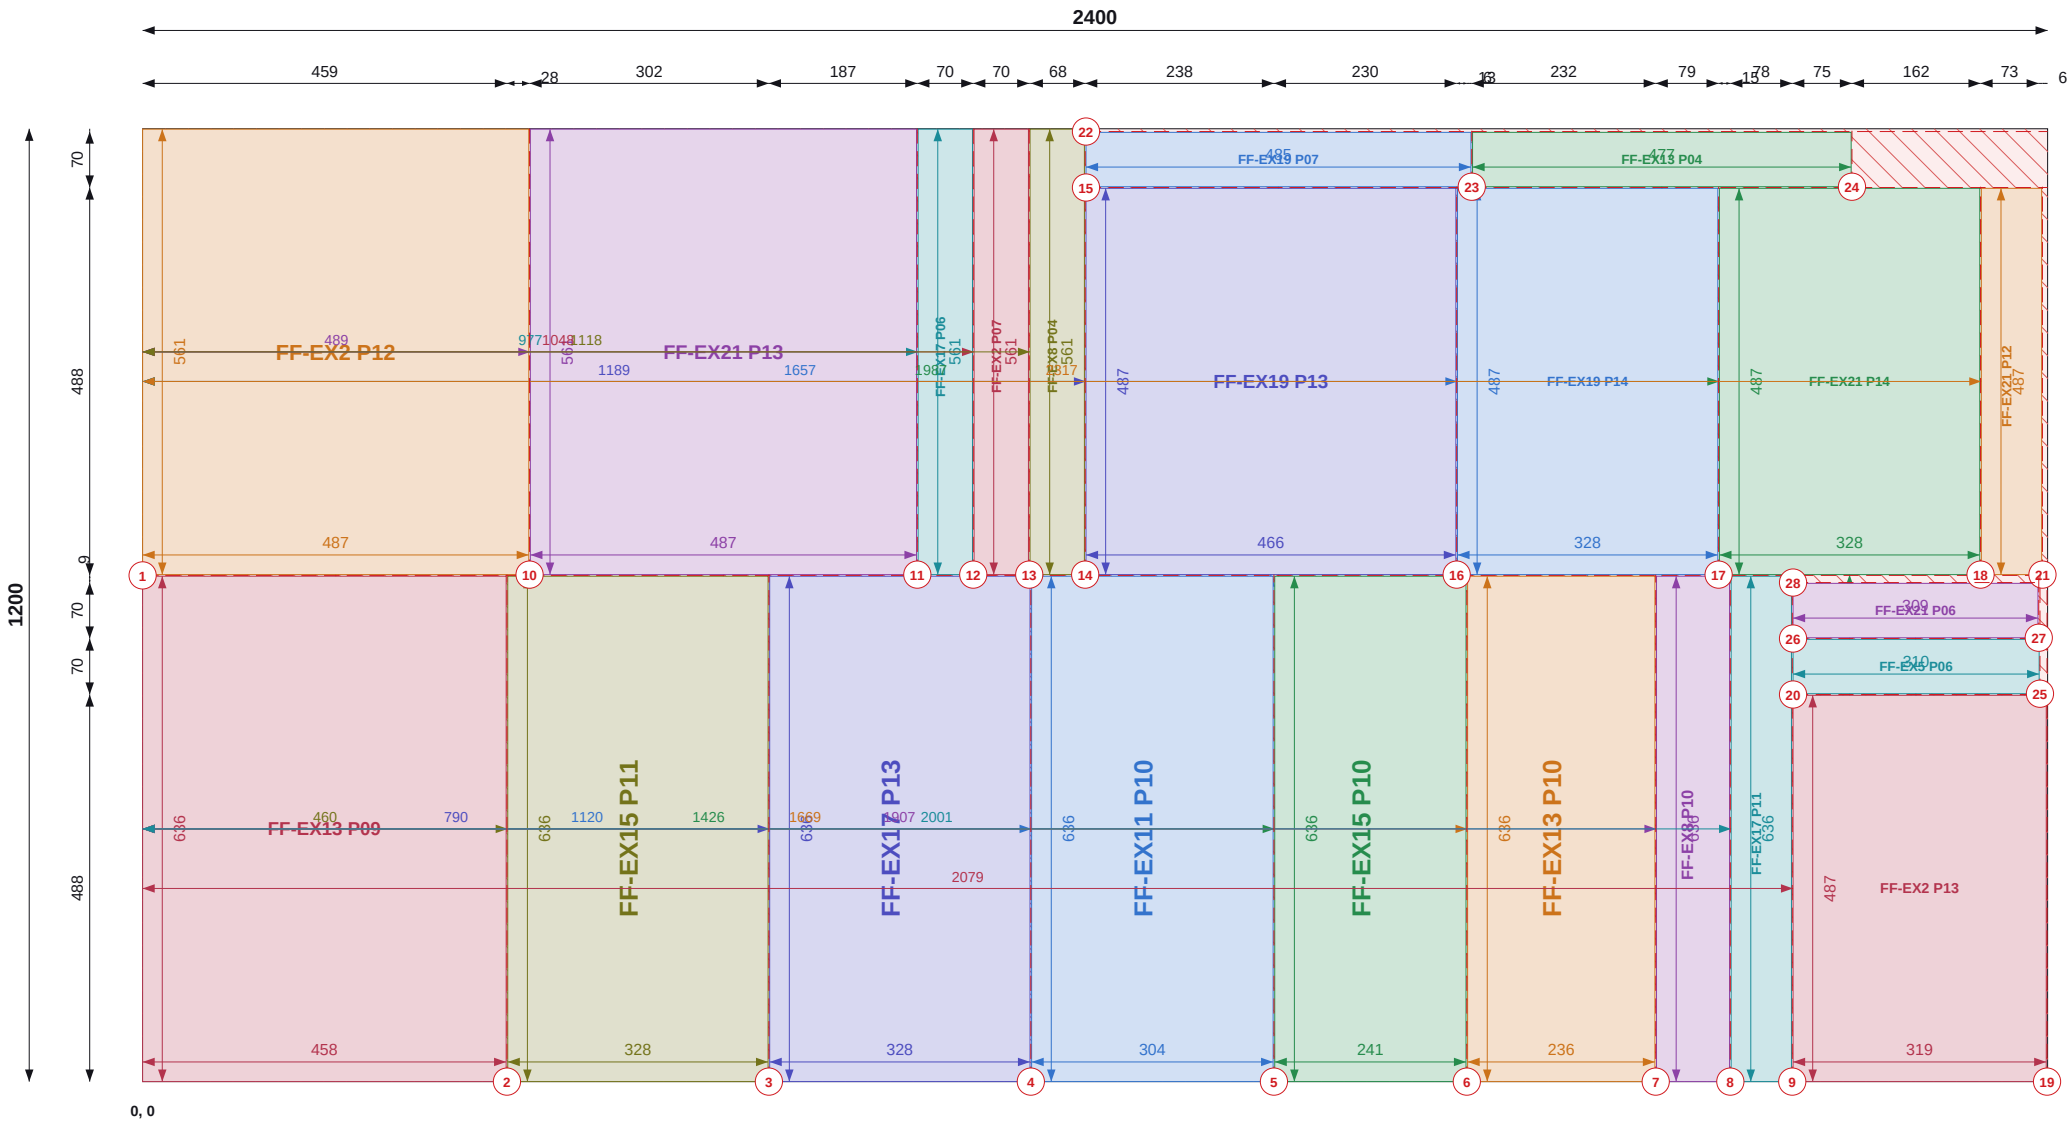

Top / left chains = saw cut positions (to cut centres). Coloured = part size and position.

SHEET 23 OF 23

THIS SHEET

| Item              | Value           |
|-------------------|-----------------|
| Parts             | 22              |
| Used / waste      | 97.9% / 0.06 m2 |
| Reusable offcuts  | 0               |
| Saw cuts / shared | 28 / 21         |

PIECES (POSITION = BOTTOM-LEFT CORNER)

| Label       | Size      | X, Y       |
|-------------|-----------|------------|
| FF-EX19 P07 | 485 x 69  | 1189, 1127 |
| FF-EX13 P04 | 477 x 69  | 1676, 1127 |
| FF-EX2 P12  | 561 x 487 | 0, 638     |
| FF-EX21 P13 | 561 x 487 | 489, 638   |
| FF-EX17 P06 | 561 x 69  | 977, 638   |
| FF-EX2 P07  | 561 x 69  | 1048, 638  |
| FF-EX8 P04  | 561 x 69  | 1118, 638  |
| FF-EX19 P13 | 466 x 487 | 1189, 638  |
| FF-EX19 P14 | 328 x 487 | 1657, 638  |
| FF-EX21 P14 | 328 x 487 | 1987, 638  |
| FF-EX21 P12 | 76 x 487  | 2317, 638  |
| FF-EX21 P06 | 309 x 69  | 2079, 559  |
| FF-EX5 P06  | 310 x 69  | 2079, 489  |
| FF-EX13 P09 | 458 x 636 | 0, 0       |
| FF-EX15 P11 | 328 x 636 | 460, 0     |
| FF-EX17 P13 | 328 x 636 | 790, 0     |
| FF-EX11 P10 | 304 x 636 | 1120, 0    |
| FF-EX15 P10 | 241 x 636 | 1426, 0    |
| FF-EX13 P10 | 236 x 636 | 1669, 0    |
| FF-EX8 P10  | 92 x 636  | 1907, 0    |
| FF-EX17 P11 | 76 x 636  | 2001, 0    |
| FF-EX2 P13  | 319 x 487 | 2079, 0    |

NOTES

- Cut from PIR 120mm 1200x2400, 2mm saw kerf. Viewed on the face; dimensions from the sheet's bottom-left corner (0,0). Red numbered lines = saw cuts in order, each edge to edge.
- Coloured dimensions belong to the part of that colour: its width and height, and its position from the sheet edges. Raked parts: corner coordinates at each corner.
- Red hatch = waste. Labels = panel + piece mark on the manufacture drawing.

REVISIONS

| REV | DATE     | DESCRIPTION        |
|-----|----------|--------------------|
| C01 | 13.09.26 | Construction issue |



TLS TIMBER FRAME

Design & Manufacture

Scan: 3D model + drawings



CLIENT

MP Adams

PROJECT

MP Adams Plot 3, Eckington

DRAWING TITLE

PIR CUTTING - FIRST FLOOR - SHEET 23 OF 23

PIR 120mm 1200x2400 | First Floor

SCALE

NTS

SIZE

A3

DATE

13.09.26

DRAWN

TS

STATUS

CONSTRUCTION


DRAWING No.

P3-CP-PIR-02 / 23

REV

C01

Do not scale. All dimensions in mm. Check all dimensions on site.

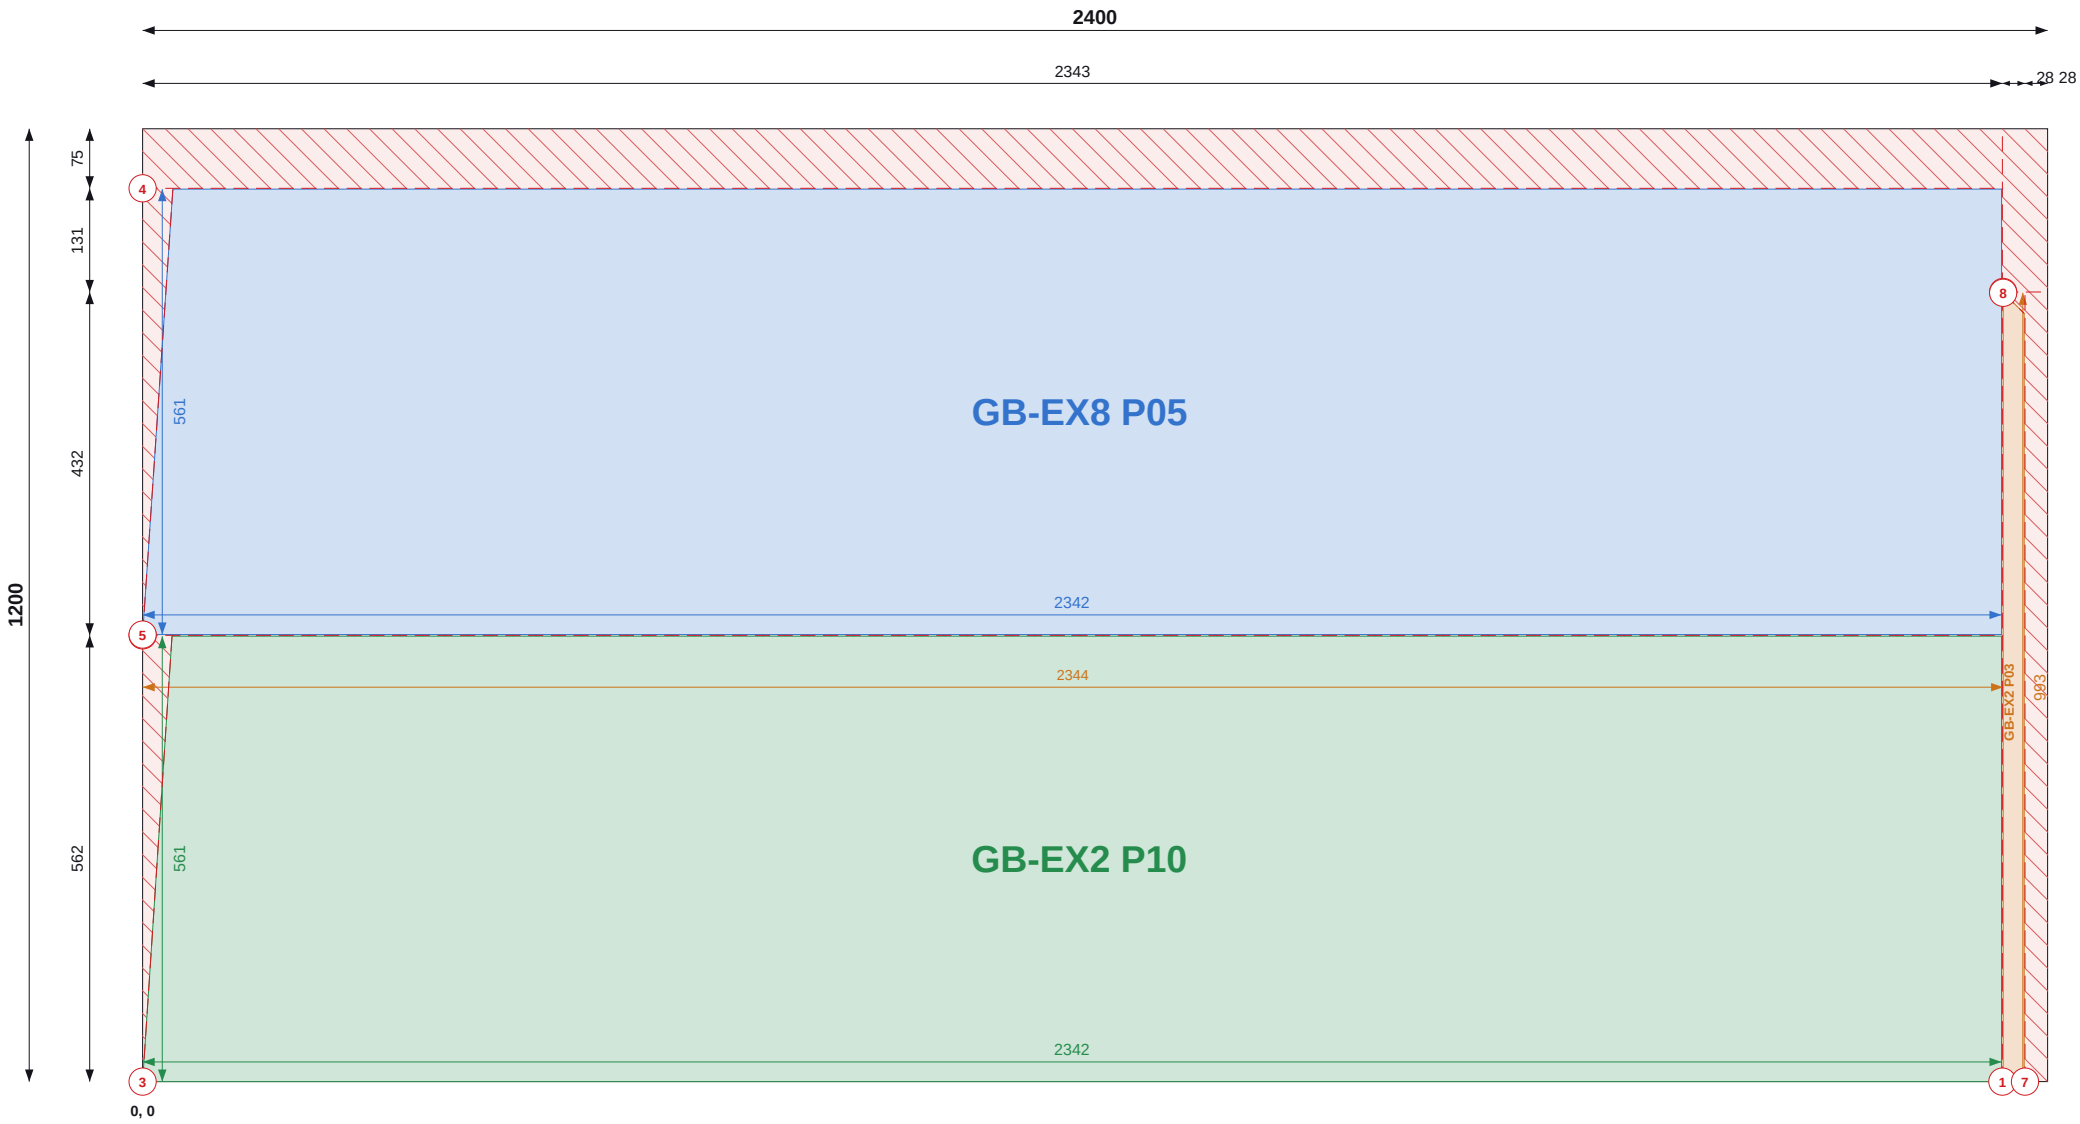

Top / left chains = saw cut positions (to cut centres). Coloured = part size and position.

## SHEET 1 OF 11

### THIS SHEET

| Item              | Value           |
|-------------------|-----------------|
| Parts             | 3               |
| Used / waste      | 91.4% / 0.25 m2 |
| Reusable offcuts  | 0               |
| Saw cuts / shared | 8 / 5           |

### PIECES (POSITION = BOTTOM-LEFT CORNER)

| Label      | Size       | X, Y    |
|------------|------------|---------|
| GB-EX8 P05 | 561 x 2342 | 0, 563  |
| GB-EX2 P10 | 561 x 2342 | 0, 0    |
| GB-EX2 P03 | 27 x 993   | 2344, 0 |

### GABLES TOTALS

| Item                              | Value           |
|-----------------------------------|-----------------|
| Sheets / pieces                   | 11 / 63         |
| Yield / waste                     | 87.6% / 3.92 m2 |
| Saw cuts / shared / on stock edge | 104 / 62 / 49   |

### NOTES

- Cut from PIR 120mm 1200x2400, 2mm saw kerf. Viewed on the face; dimensions from the sheet's bottom-left corner (0,0). Red numbered lines = saw cuts in order, each edge to edge.
- Coloured dimensions belong to the part of that colour: its width and height, and its position from the sheet edges. Raked parts: corner coordinates at each corner.
- Red hatch = waste. Labels = panel + piece mark on the manufacture drawing.

### REVISIONS

| REV | DATE     | DESCRIPTION        |
|-----|----------|--------------------|
| C01 | 13.09.26 | Construction issue |



TLS TIMBER FRAME

Design & Manufacture

Scan: 3D model + drawings



|          |                            |
|----------|----------------------------|
| CLIENT   | PROJECT                    |
| MP Adams | MP Adams Plot 3, Eckington |

|                                      |
|--------------------------------------|
| DRAWING TITLE                        |
| PIR CUTTING - GABLES - SHEET 1 OF 11 |


PIR 120mm 1200x2400 | Gables

|       |      |          |       |
|-------|------|----------|-------|
| SCALE | SIZE | DATE     | DRAWN |
| NTS   | A3   | 13.09.26 | TS    |

|              |                   |     |
|--------------|-------------------|-----|
| STATUS       | DRAWING No.       | REV |
| CONSTRUCTION | P3-CP-PIR-03 / 01 | C01 |



Do not scale. All dimensions in mm. Check all dimensions on site.

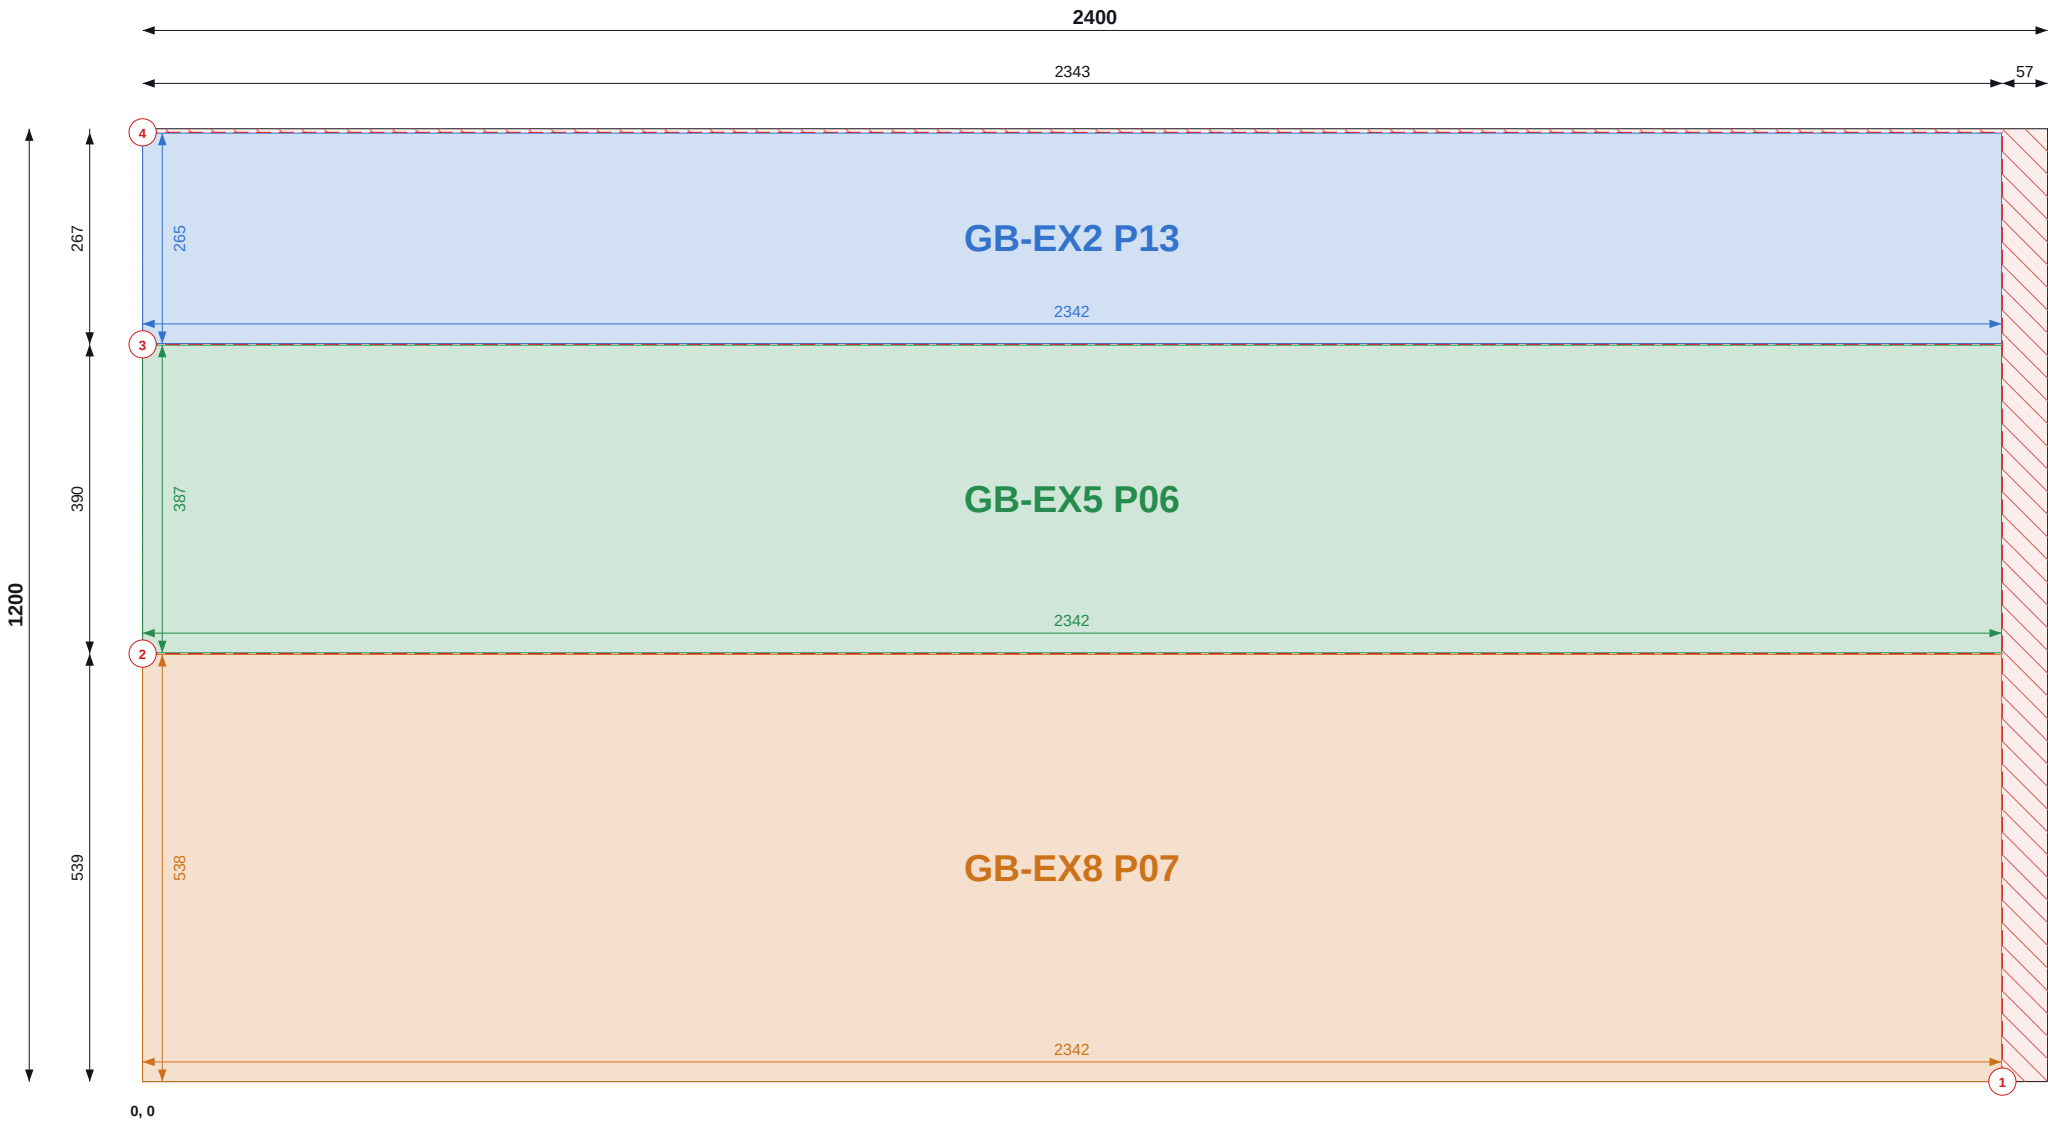

Top / left chains = saw cut positions (to cut centres). Coloured = part size and position.

### SHEET 3 OF 11

#### THIS SHEET

| Item              | Value           |
|-------------------|-----------------|
| Parts             | 3               |
| Used / waste      | 96.8% / 0.09 m2 |
| Reusable offcuts  | 0               |
| Saw cuts / shared | 4 / 2           |

#### PIECES (POSITION = BOTTOM-LEFT CORNER)

| Label      | Size       | X, Y   |
|------------|------------|--------|
| GB-EX2 P13 | 265 x 2342 | 0, 930 |
| GB-EX5 P06 | 387 x 2342 | 0, 540 |
| GB-EX8 P07 | 538 x 2342 | 0, 0   |

#### NOTES

1. Cut from PIR 120mm 1200x2400, 2mm saw kerf. Viewed on the face; dimensions from the sheet's bottom-left corner (0,0). Red numbered lines = saw cuts in order, each edge to edge.
2. Coloured dimensions belong to the part of that colour: its width and height, and its position from the sheet edges. Raked parts: corner coordinates at each corner.
3. Red hatch = waste. Labels = panel + piece mark on the manufacture drawing.

#### REVISIONS

| REV | DATE     | DESCRIPTION        |
|-----|----------|--------------------|
| C01 | 13.09.26 | Construction issue |



TLS TIMBER FRAME

Design & Manufacture

Scan: 3D model + drawings



|          |                            |
|----------|----------------------------|
| CLIENT   | PROJECT                    |
| MP Adams | MP Adams Plot 3, Eckington |


|                                      |
|--------------------------------------|
| DRAWING TITLE                        |
| PIR CUTTING - GABLES - SHEET 3 OF 11 |

PIR 120mm 1200x2400 | Gables

|       |      |          |       |
|-------|------|----------|-------|
| SCALE | SIZE | DATE     | DRAWN |
| NTS   | A3   | 13.09.26 | TS    |

|              |                   |     |
|--------------|-------------------|-----|
| STATUS       | DRAWING No.       | REV |
| CONSTRUCTION | P3-CP-PIR-03 / 03 | C01 |

Do not scale. All dimensions in mm. Check all dimensions on site.

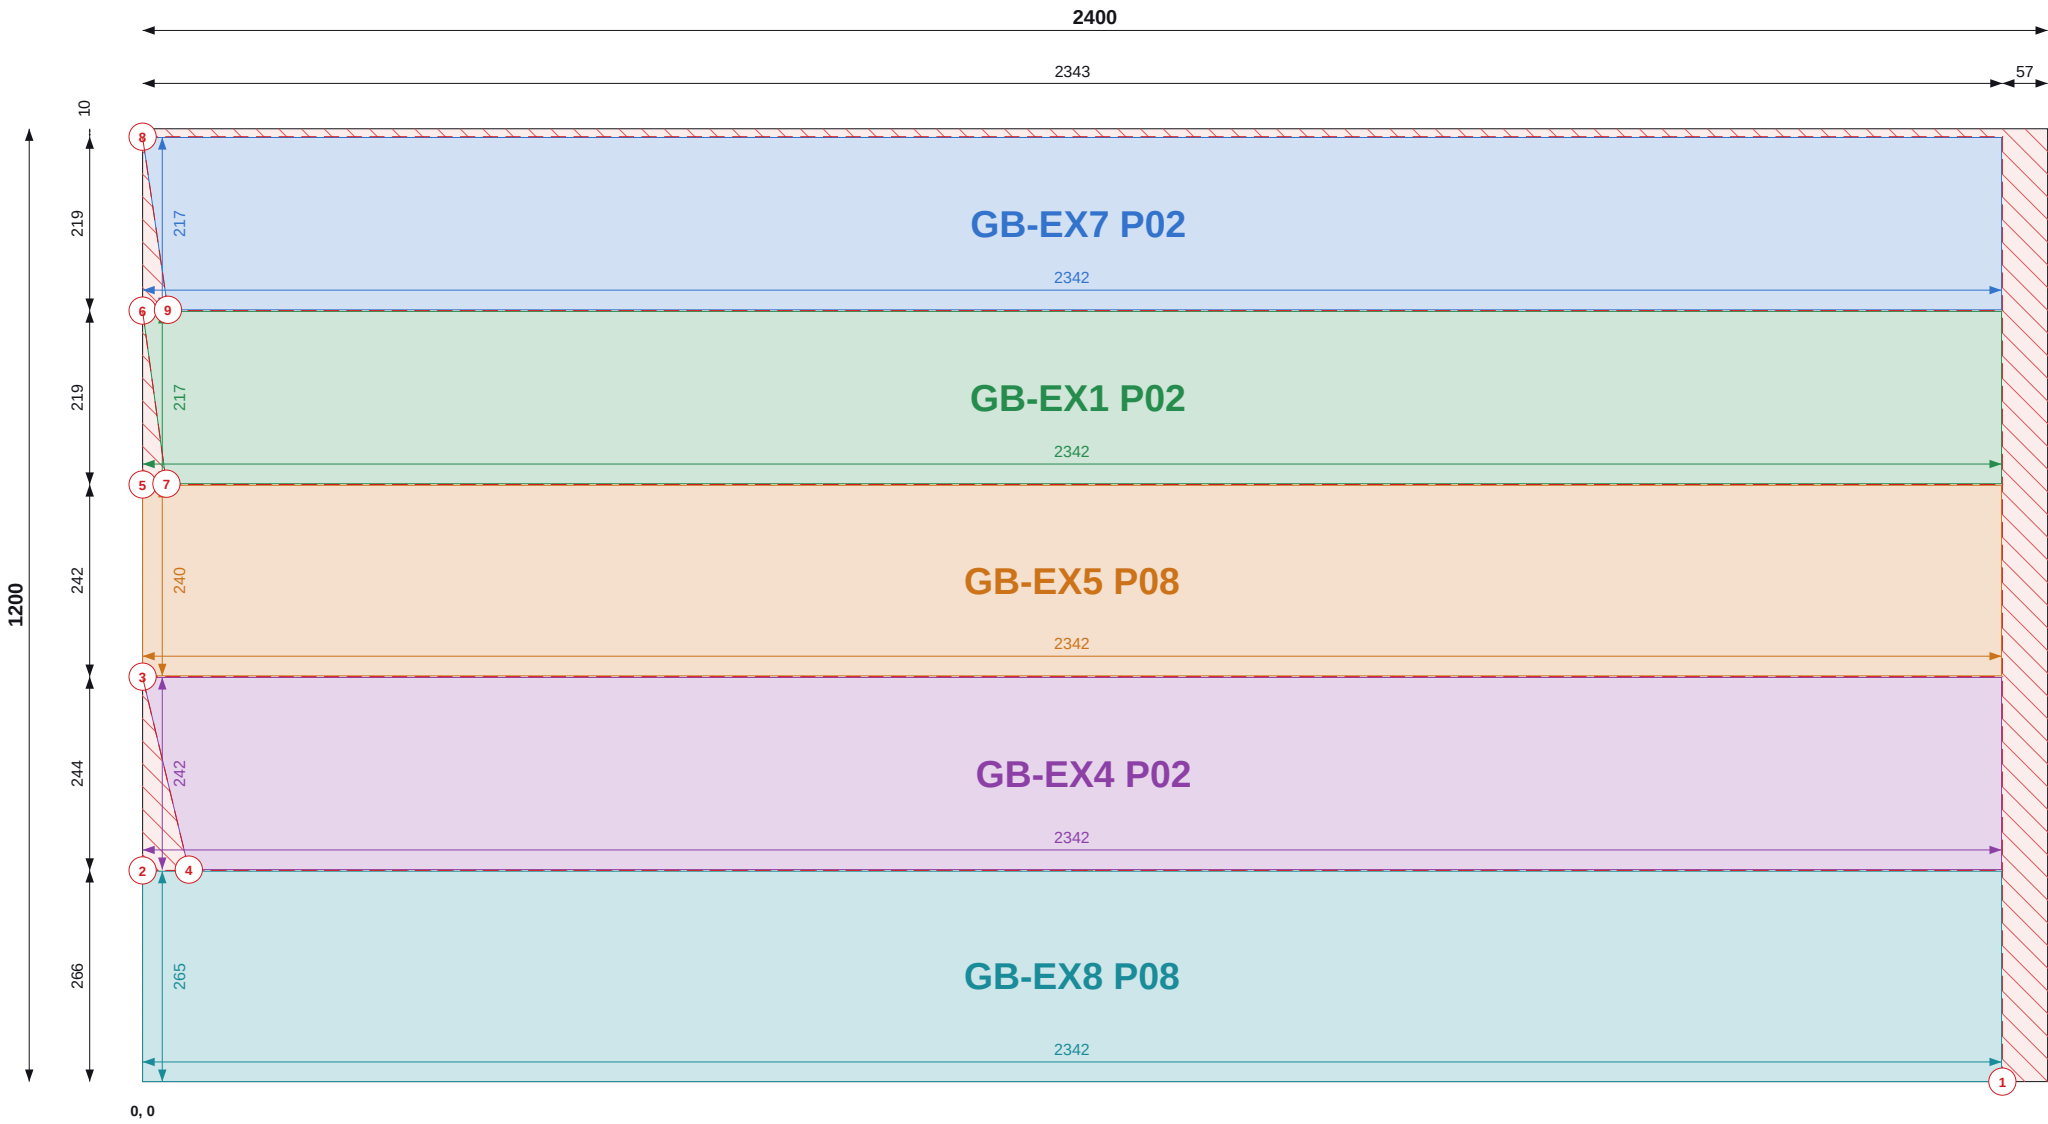

Top / left chains = saw cut positions (to cut centres). Coloured = part size and position.

SHEET 4 OF 11

THIS SHEET

| Item              | Value           |
|-------------------|-----------------|
| Parts             | 5               |
| Used / waste      | 95.6% / 0.13 m2 |
| Reusable offcuts  | 0               |
| Saw cuts / shared | 9 / 7           |

PIECES (POSITION = BOTTOM-LEFT CORNER)

| Label      | Size       | X, Y   |
|------------|------------|--------|
| GB-EX7 P02 | 217 x 2342 | 0, 972 |
| GB-EX1 P02 | 217 x 2342 | 0, 753 |
| GB-EX5 P08 | 240 x 2342 | 0, 511 |
| GB-EX4 P02 | 242 x 2342 | 0, 267 |
| GB-EX8 P08 | 265 x 2342 | 0, 0   |

NOTES

- Cut from PIR 120mm 1200x2400, 2mm saw kerf. Viewed on the face; dimensions from the sheet's bottom-left corner (0,0). Red numbered lines = saw cuts in order, each edge to edge.
- Coloured dimensions belong to the part of that colour: its width and height, and its position from the sheet edges. Raked parts: corner coordinates at each corner.
- Red hatch = waste. Labels = panel + piece mark on the manufacture drawing.

REVISIONS

| REV | DATE     | DESCRIPTION        |
|-----|----------|--------------------|
| C01 | 13.09.26 | Construction issue |



TLS TIMBER FRAME

Design & Manufacture

Scan: 3D model + drawings



|          |                            |
|----------|----------------------------|
| CLIENT   | PROJECT                    |
| MP Adams | MP Adams Plot 3, Eckington |


|                                      |
|--------------------------------------|
| DRAWING TITLE                        |
| PIR CUTTING - GABLES - SHEET 4 OF 11 |

PIR 120mm 1200x2400 | Gables

|       |      |          |       |
|-------|------|----------|-------|
| SCALE | SIZE | DATE     | DRAWN |
| NTS   | A3   | 13.09.26 | TS    |

|              |                   |     |
|--------------|-------------------|-----|
| STATUS       | DRAWING No.       | REV |
| CONSTRUCTION | P3-CP-PIR-03 / 04 | C01 |

Do not scale. All dimensions in mm. Check all dimensions on site.

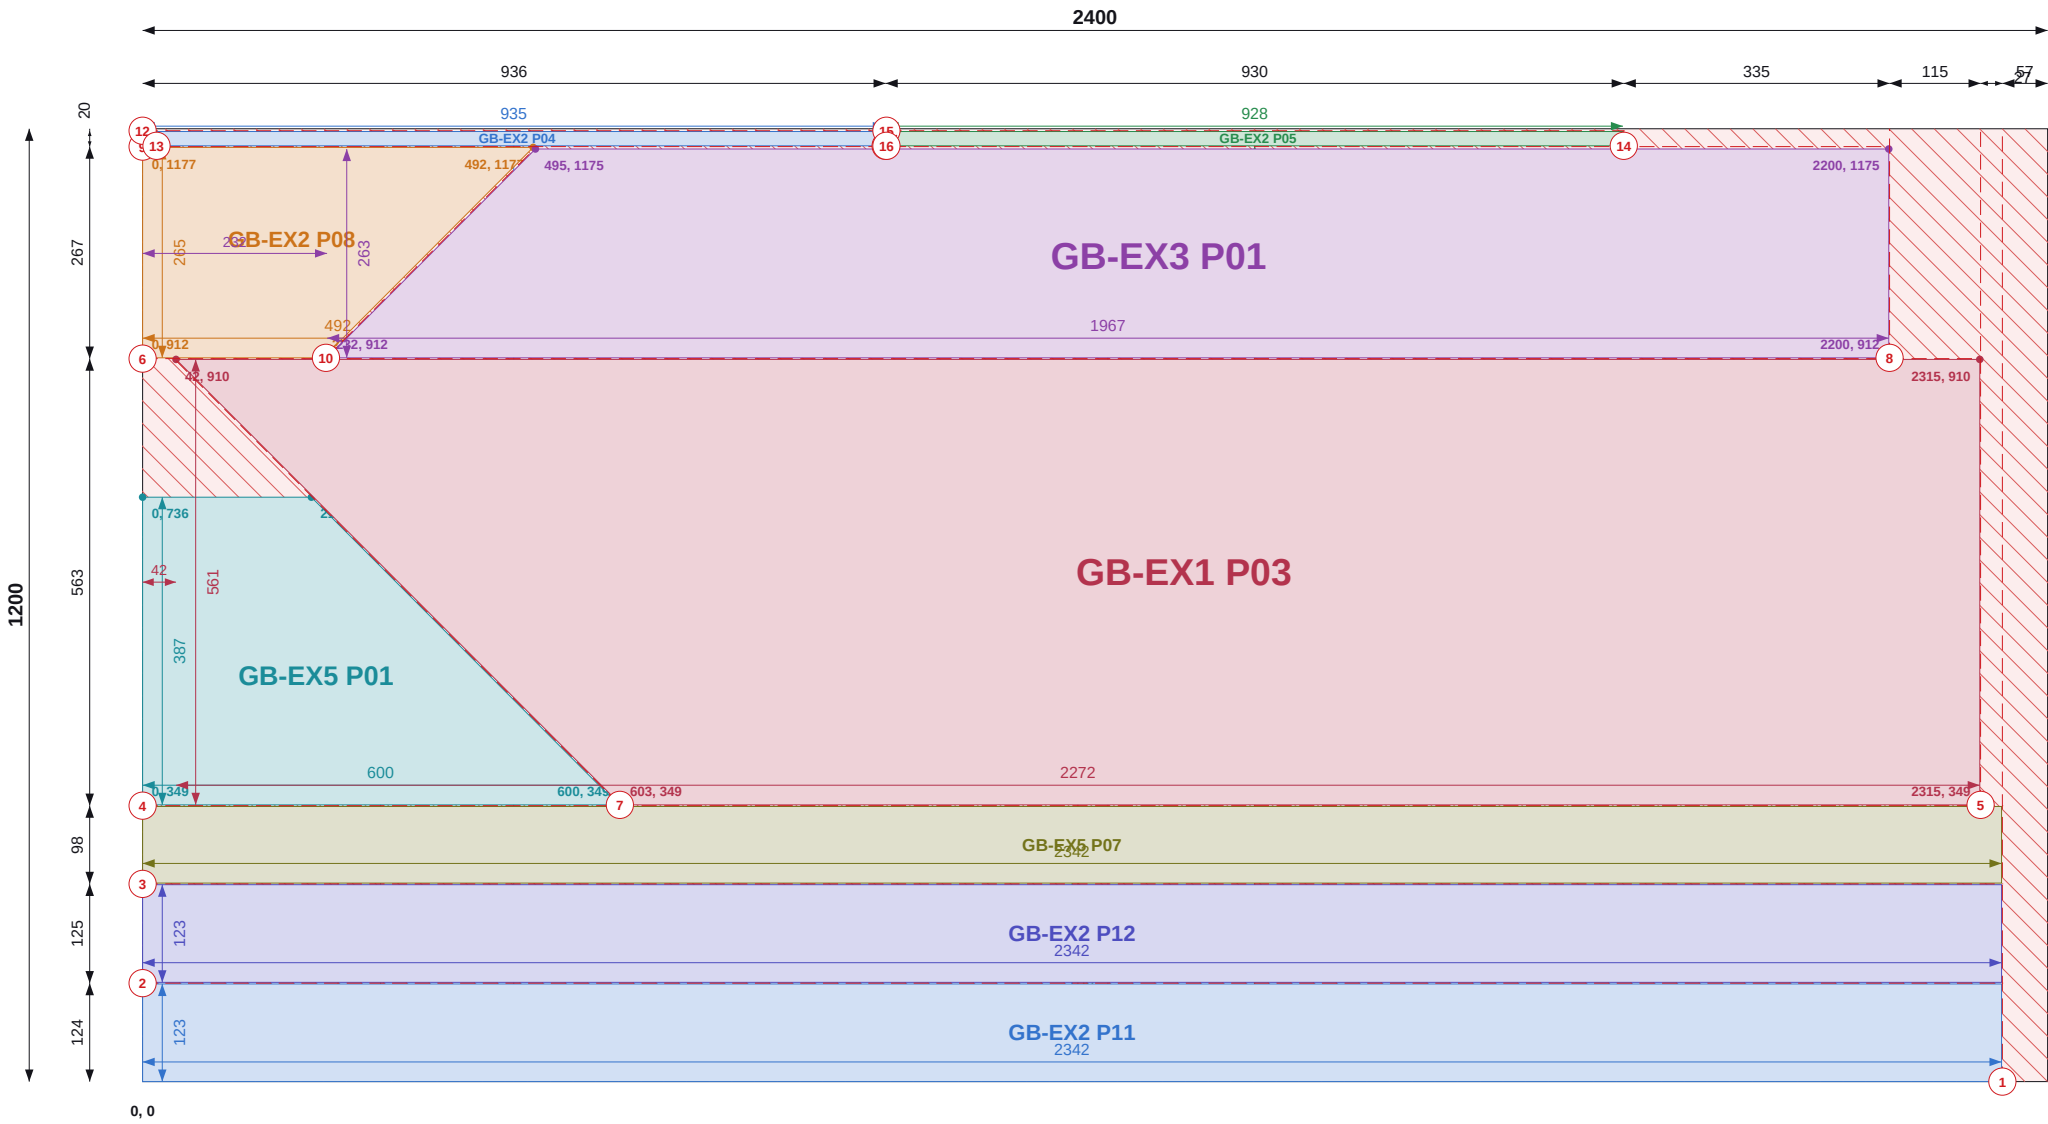

Top / left chains = saw cut positions (to cut centres). Coloured = part size and position.

SHEET 5 OF 11

THIS SHEET

| Item              | Value           |
|-------------------|-----------------|
| Parts             | 9               |
| Used / waste      | 93.4% / 0.19 m2 |
| Reusable offcuts  | 0               |
| Saw cuts / shared | 16 / 10         |

PIECES (POSITION = BOTTOM-LEFT CORNER)

| Label      | Size                    | X, Y      |
|------------|-------------------------|-----------|
| GB-EX2 P04 | 18 x 935                | 0, 1179   |
| GB-EX2 P05 | 18 x 928                | 937, 1179 |
| GB-EX2 P08 | 265 x 492 rake to 229   | 0, 912    |
| GB-EX3 P01 | 263 x 1967 rake to 1706 | 232, 912  |
| GB-EX5 P01 | 387 x 599 rake to 214   | 0, 349    |
| GB-EX1 P03 | 561 x 2272 rake to 1713 | 42, 349   |
| GB-EX5 P07 | 97 x 2342               | 0, 250    |
| GB-EX2 P12 | 123 x 2342              | 0, 125    |
| GB-EX2 P11 | 123 x 2342              | 0, 0      |

NOTES

- Cut from PIR 120mm 1200x2400, 2mm saw kerf. Viewed on the face; dimensions from the sheet's bottom-left corner (0,0). Red numbered lines = saw cuts in order, each edge to edge.
- Coloured dimensions belong to the part of that colour: its width and height, and its position from the sheet edges. Raked parts: corner coordinates at each corner.
- Red hatch = waste. Labels = panel + piece mark on the manufacture drawing.

REVISIONS

| REV | DATE     | DESCRIPTION        |
|-----|----------|--------------------|
| C01 | 13.09.26 | Construction issue |



TLS TIMBER FRAME

Design & Manufacture

Scan: 3D model + drawings



|          |                            |
|----------|----------------------------|
| CLIENT   | PROJECT                    |
| MP Adams | MP Adams Plot 3, Eckington |


|                                      |
|--------------------------------------|
| DRAWING TITLE                        |
| PIR CUTTING - GABLES - SHEET 5 OF 11 |

PIR 120mm 1200x2400 | Gables

|       |      |          |       |
|-------|------|----------|-------|
| SCALE | SIZE | DATE     | DRAWN |
| NTS   | A3   | 13.09.26 | TS    |

|              |                   |     |
|--------------|-------------------|-----|
| STATUS       | DRAWING No.       | REV |
| CONSTRUCTION | P3-CP-PIR-03 / 05 | C01 |

Do not scale. All dimensions in mm. Check all dimensions on site.

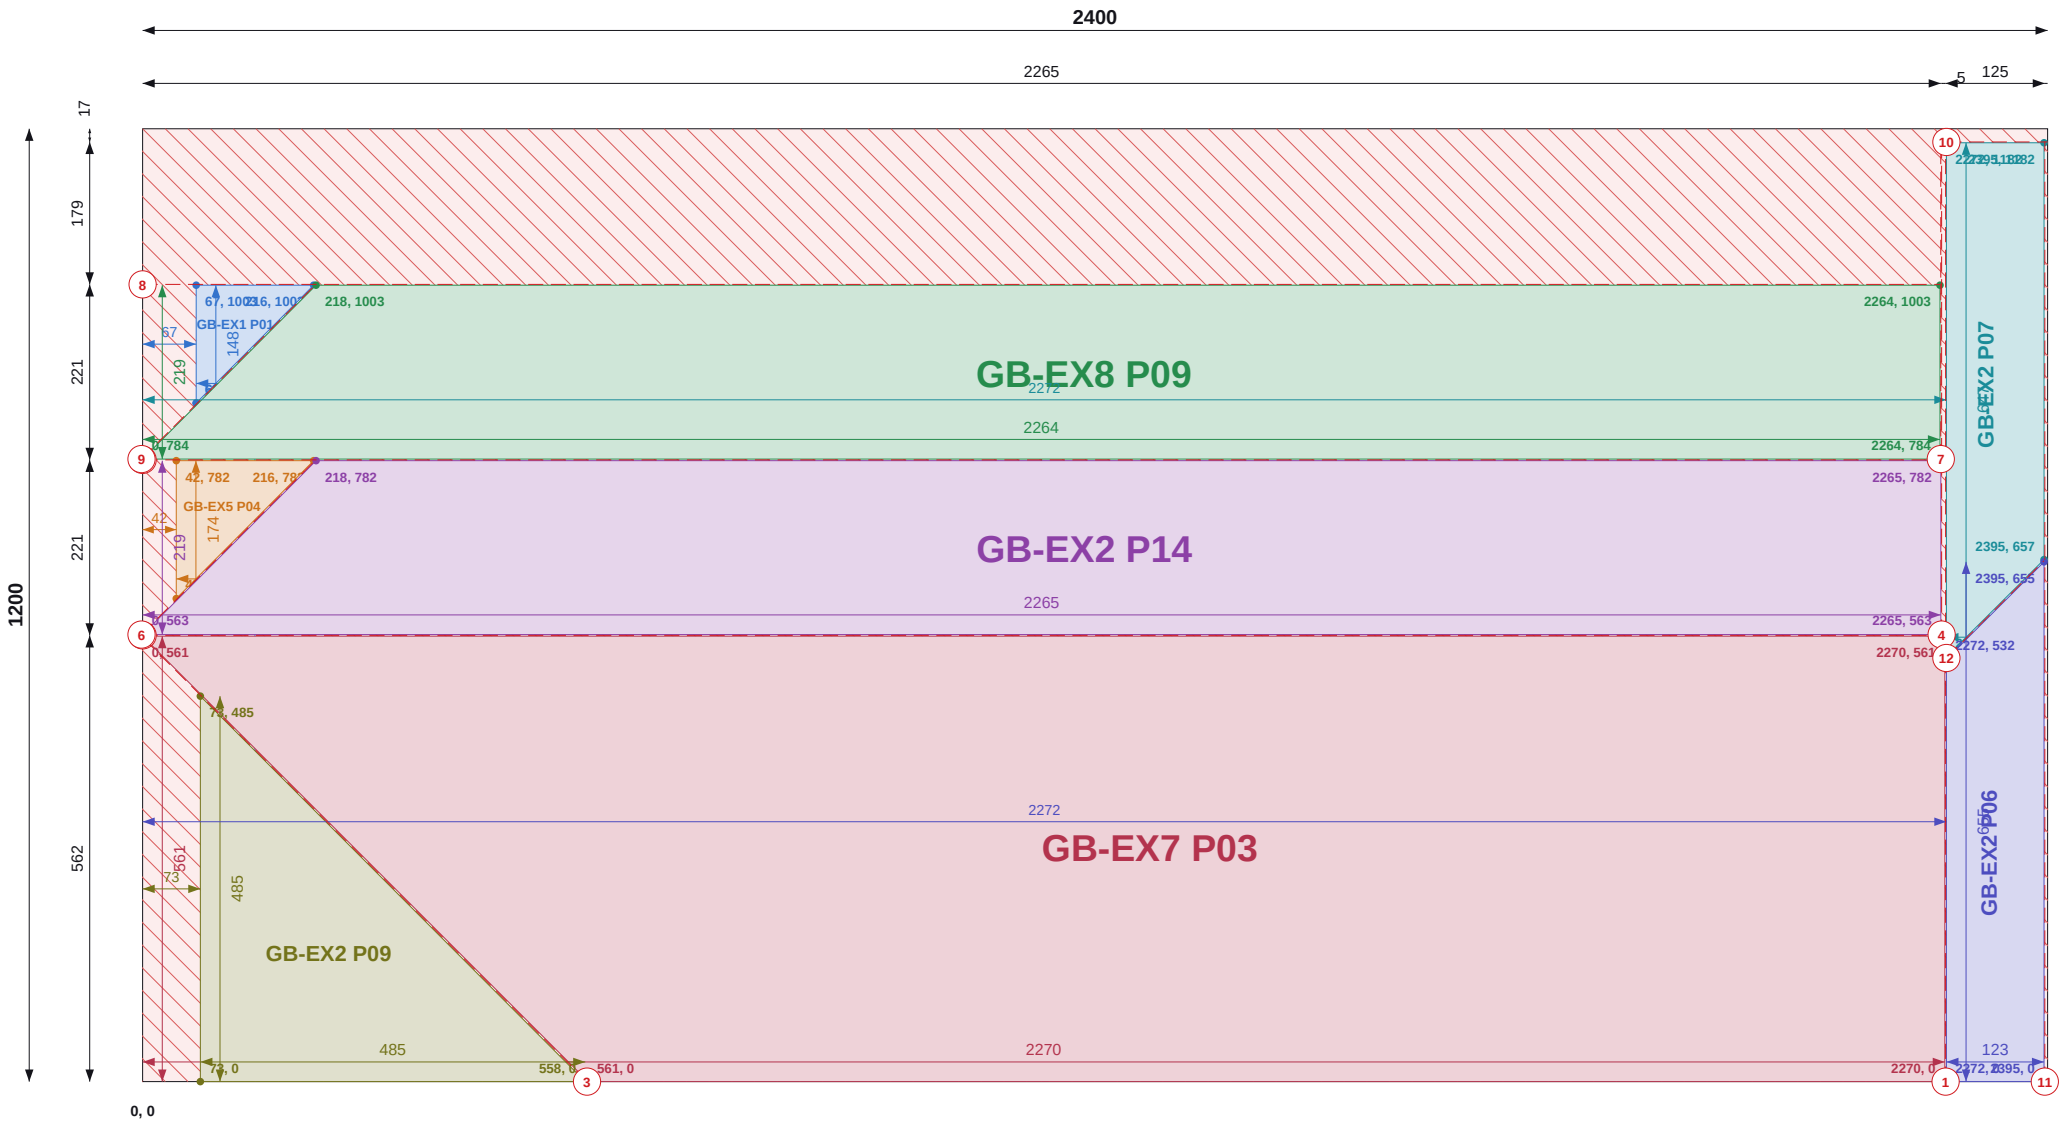

Top / left chains = saw cut positions (to cut centres). Coloured = part size and position.

SHEET 6 OF 11

THIS SHEET

| Item              | Value           |
|-------------------|-----------------|
| Parts             | 8               |
| Used / waste      | 81.6% / 0.53 m2 |
| Reusable offcuts  | 0               |
| Saw cuts / shared | 12 / 7          |

PIECES (POSITION = BOTTOM-LEFT CORNER)

| Label      | Size                    | X, Y      |
|------------|-------------------------|-----------|
| GB-EX1 P01 | 148 x 148 rake to 1     | 67, 855   |
| GB-EX8 P09 | 219 x 2264 rake to 2047 | 0, 784    |
| GB-EX5 P04 | 174 x 173 rake to 1     | 42, 608   |
| GB-EX2 P14 | 219 x 2265 rake to 2048 | 0, 563    |
| GB-EX2 P07 | 123 x 647 rake to 526   | 2272, 535 |
| GB-EX7 P03 | 561 x 2270 rake to 1710 | 0, 0      |
| GB-EX2 P09 | 485 x 485 rake to 1     | 73, 0     |
| GB-EX2 P06 | 123 x 654 rake to 533   | 2272, 0   |

NOTES

- Cut from PIR 120mm 1200x2400, 2mm saw kerf. Viewed on the face; dimensions from the sheet's bottom-left corner (0,0). Red numbered lines = saw cuts in order, each edge to edge.
- Coloured dimensions belong to the part of that colour: its width and height, and its position from the sheet edges. Raked parts: corner coordinates at each corner.
- Red hatch = waste. Labels = panel + piece mark on the manufacture drawing.

REVISIONS

| REV | DATE     | DESCRIPTION        |
|-----|----------|--------------------|
| C01 | 13.09.26 | Construction issue |



TLS TIMBER FRAME

Design & Manufacture

Scan: 3D model + drawings



|          |                            |
|----------|----------------------------|
| CLIENT   | PROJECT                    |
| MP Adams | MP Adams Plot 3, Eckington |


|                                      |
|--------------------------------------|
| DRAWING TITLE                        |
| PIR CUTTING - GABLES - SHEET 6 OF 11 |

PIR 120mm 1200x2400 | Gables

|       |      |          |       |
|-------|------|----------|-------|
| SCALE | SIZE | DATE     | DRAWN |
| NTS   | A3   | 13.09.26 | TS    |

|              |                   |     |
|--------------|-------------------|-----|
| STATUS       | DRAWING No.       | REV |
| CONSTRUCTION | P3-CP-PIR-03 / 06 | C01 |

Do not scale. All dimensions in mm. Check all dimensions on site.

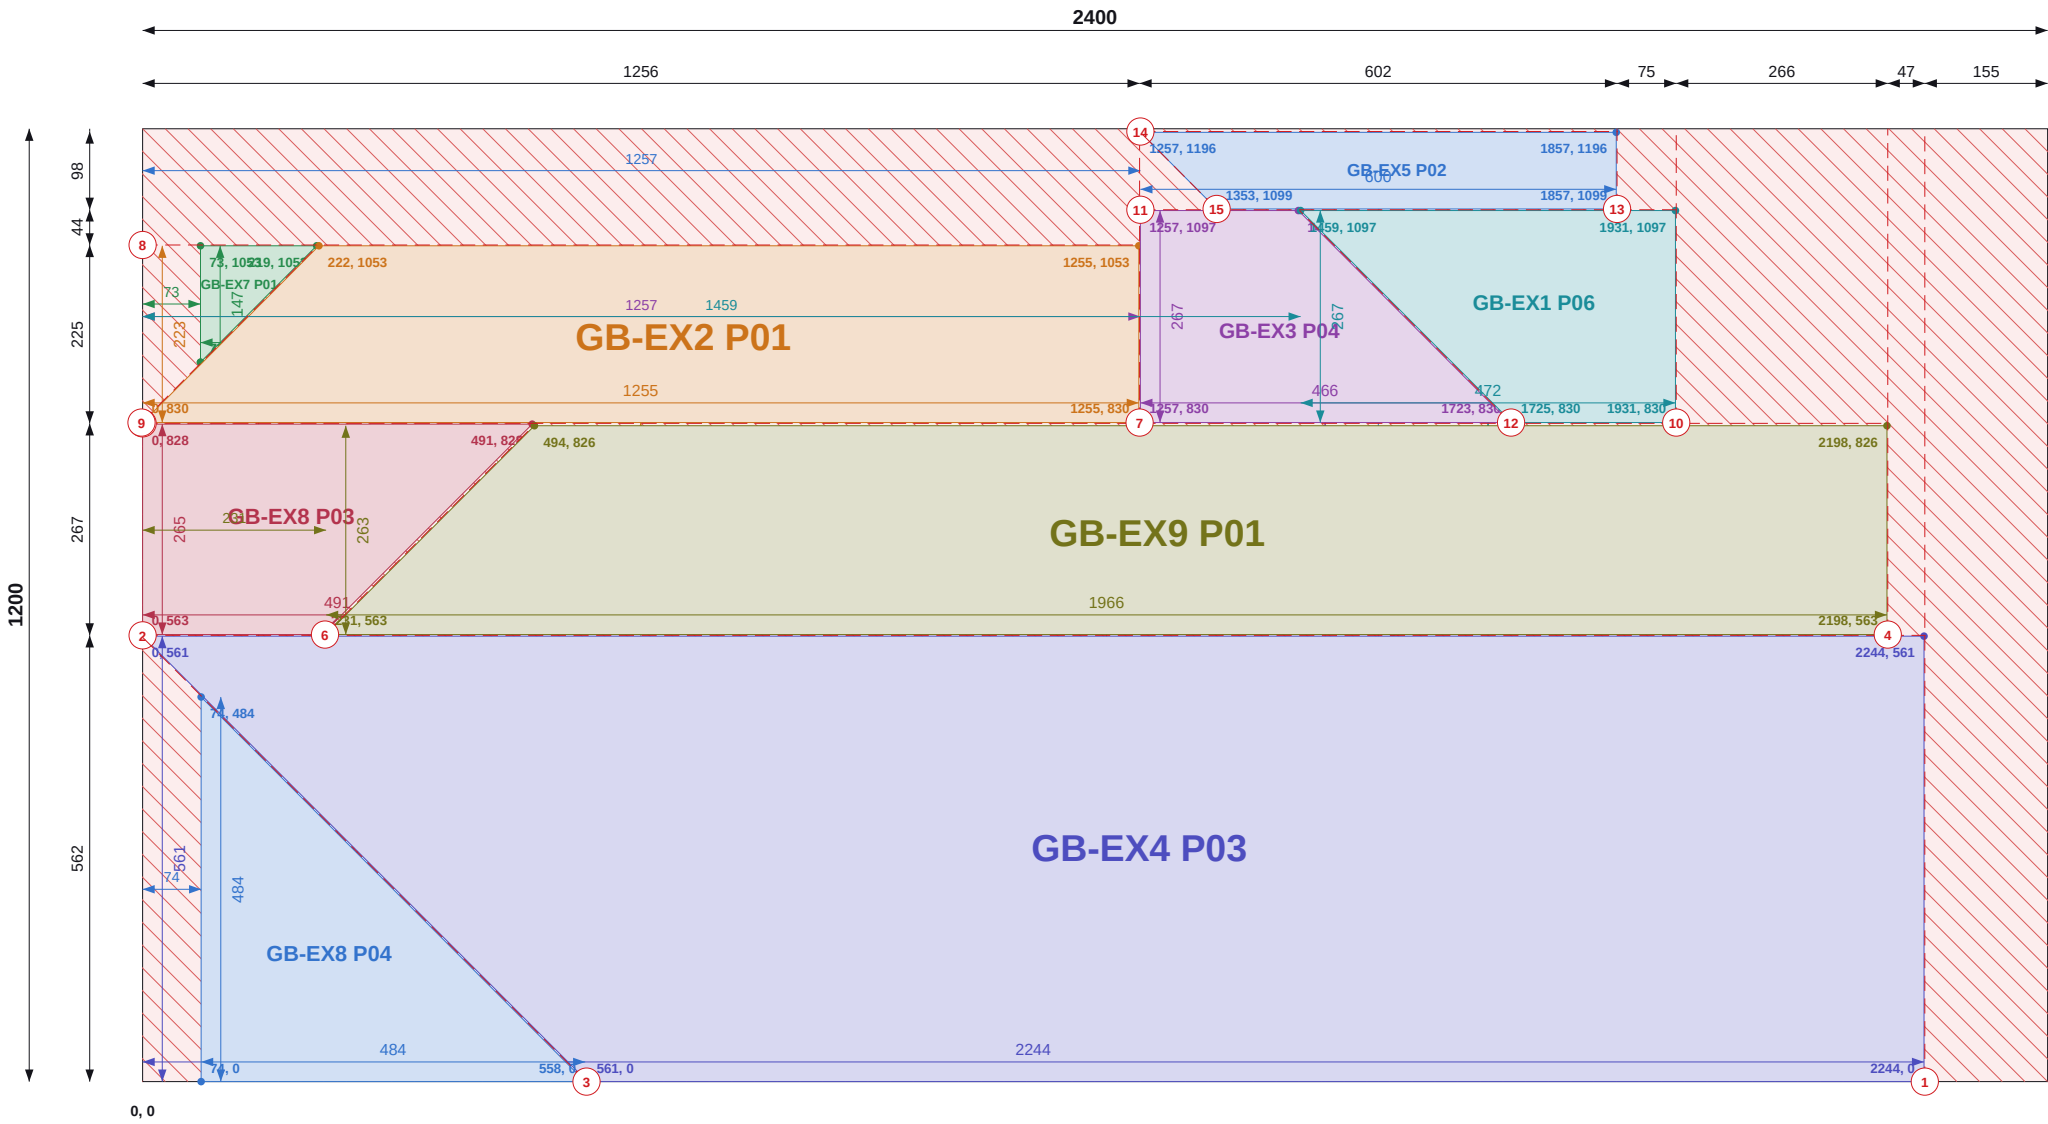

Top / left chains = saw cut positions (to cut centres). Coloured = part size and position.

SHEET 7 OF 11

THIS SHEET

| Item              | Value           |
|-------------------|-----------------|
| Parts             | 9               |
| Used / waste      | 79.7% / 0.59 m2 |
| Reusable offcuts  | 0               |
| Saw cuts / shared | 15 / 9          |

PIECES (POSITION = BOTTOM-LEFT CORNER)

| Label      | Size                    | X, Y       |
|------------|-------------------------|------------|
| GB-EX5 P02 | 97 x 599 rake to 505    | 1257, 1099 |
| GB-EX7 P01 | 147 x 146 rake to 1     | 73, 906    |
| GB-EX2 P01 | 223 x 1255 rake to 1034 | 0, 830     |
| GB-EX3 P04 | 267 x 465 rake to 200   | 1257, 830  |
| GB-EX1 P06 | 267 x 472 rake to 207   | 1459, 830  |
| GB-EX8 P03 | 265 x 491 rake to 227   | 0, 563     |
| GB-EX9 P01 | 263 x 1966 rake to 1705 | 231, 563   |
| GB-EX4 P03 | 561 x 2244 rake to 1685 | 0, 0       |
| GB-EX8 P04 | 484 x 484 rake to 1     | 74, 0      |

NOTES

- Cut from PIR 120mm 1200x2400, 2mm saw kerf. Viewed on the face; dimensions from the sheet's bottom-left corner (0,0). Red numbered lines = saw cuts in order, each edge to edge.
- Coloured dimensions belong to the part of that colour: its width and height, and its position from the sheet edges. Raked parts: corner coordinates at each corner.
- Red hatch = waste. Labels = panel + piece mark on the manufacture drawing.

REVISIONS

| REV | DATE     | DESCRIPTION        |
|-----|----------|--------------------|
| C01 | 13.09.26 | Construction issue |



TLS TIMBER FRAME

Design & Manufacture

Scan: 3D model + drawings



|          |                            |
|----------|----------------------------|
| CLIENT   | PROJECT                    |
| MP Adams | MP Adams Plot 3, Eckington |


DRAWING TITLE  
**PIR CUTTING - GABLES - SHEET 7 OF 11**

PIR 120mm 1200x2400 | Gables

|       |      |          |       |
|-------|------|----------|-------|
| SCALE | SIZE | DATE     | DRAWN |
| NTS   | A3   | 13.09.26 | TS    |

|              |                   |     |
|--------------|-------------------|-----|
| STATUS       | DRAWING No.       | REV |
| CONSTRUCTION | P3-CP-PIR-03 / 07 | C01 |

Do not scale. All dimensions in mm. Check all dimensions on site.

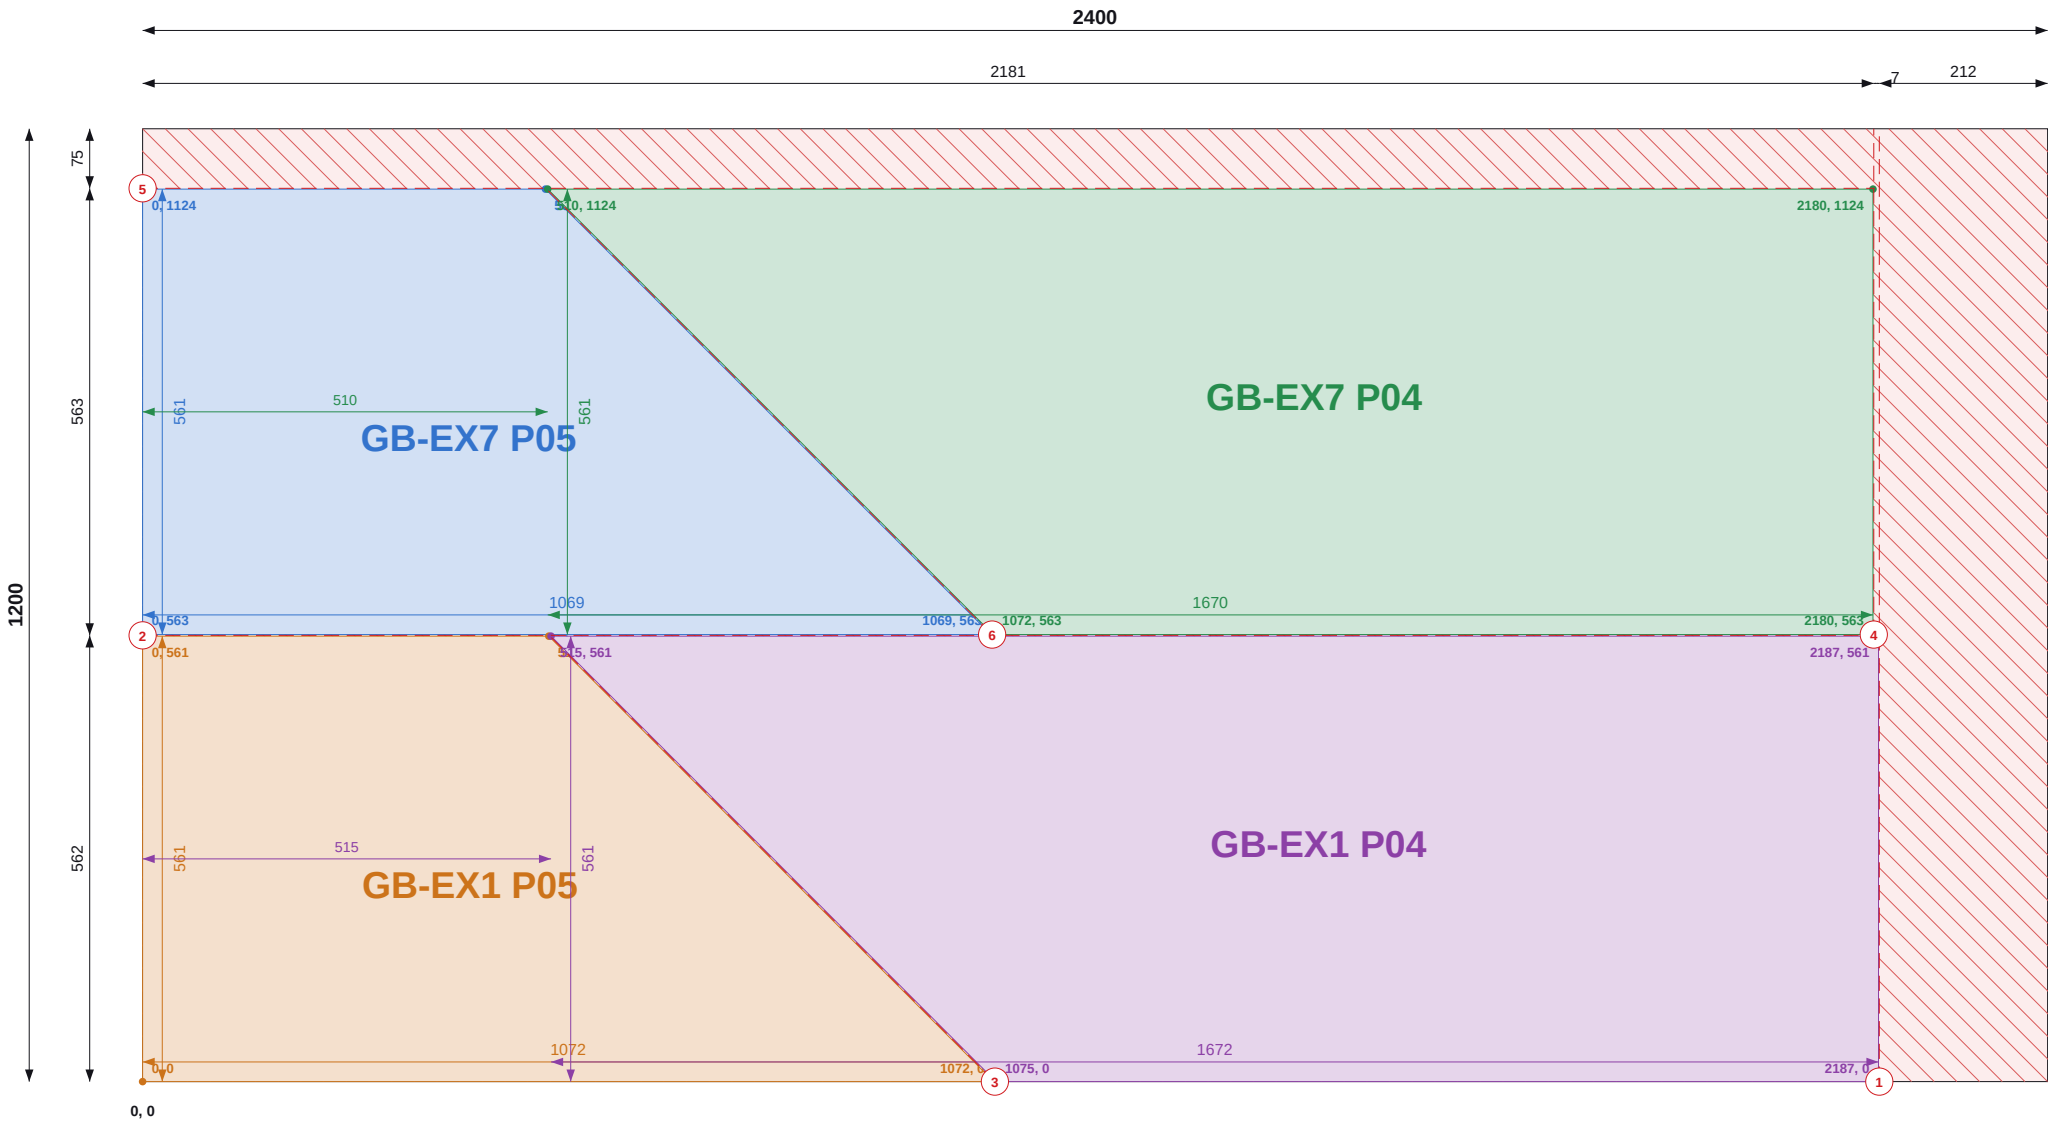

Top / left chains = saw cut positions (to cut centres). Coloured = part size and position.

SHEET 8 OF 11

THIS SHEET

| Item              | Value           |
|-------------------|-----------------|
| Parts             | 4               |
| Used / waste      | 85.0% / 0.43 m2 |
| Reusable offcuts  | 0               |
| Saw cuts / shared | 6 / 3           |

PIECES (POSITION = BOTTOM-LEFT CORNER)

| Label      | Size                    | X, Y     |
|------------|-------------------------|----------|
| GB-EX7 P05 | 561 x 1069 rake to 509  | 0, 563   |
| GB-EX7 P04 | 561 x 1670 rake to 1109 | 510, 563 |
| GB-EX1 P05 | 561 x 1072 rake to 513  | 0, 0     |
| GB-EX1 P04 | 561 x 1672 rake to 1113 | 515, 0   |

NOTES

- Cut from PIR 120mm 1200x2400, 2mm saw kerf. Viewed on the face; dimensions from the sheet's bottom-left corner (0,0). Red numbered lines = saw cuts in order, each edge to edge.
- Coloured dimensions belong to the part of that colour: its width and height, and its position from the sheet edges. Raked parts: corner coordinates at each corner.
- Red hatch = waste. Labels = panel + piece mark on the manufacture drawing.

REVISIONS

| REV | DATE     | DESCRIPTION        |
|-----|----------|--------------------|
| C01 | 13.09.26 | Construction issue |



TLS TIMBER FRAME

Design & Manufacture

Scan: 3D model + drawings



|          |                            |
|----------|----------------------------|
| CLIENT   | PROJECT                    |
| MP Adams | MP Adams Plot 3, Eckington |


DRAWING TITLE  
**PIR CUTTING - GABLES - SHEET 8 OF 11**

PIR 120mm 1200x2400 | Gables

|       |      |          |       |
|-------|------|----------|-------|
| SCALE | SIZE | DATE     | DRAWN |
| NTS   | A3   | 13.09.26 | TS    |

|              |                   |     |
|--------------|-------------------|-----|
| STATUS       | DRAWING No.       | REV |
| CONSTRUCTION | P3-CP-PIR-03 / 08 | C01 |

Do not scale. All dimensions in mm. Check all dimensions on site.

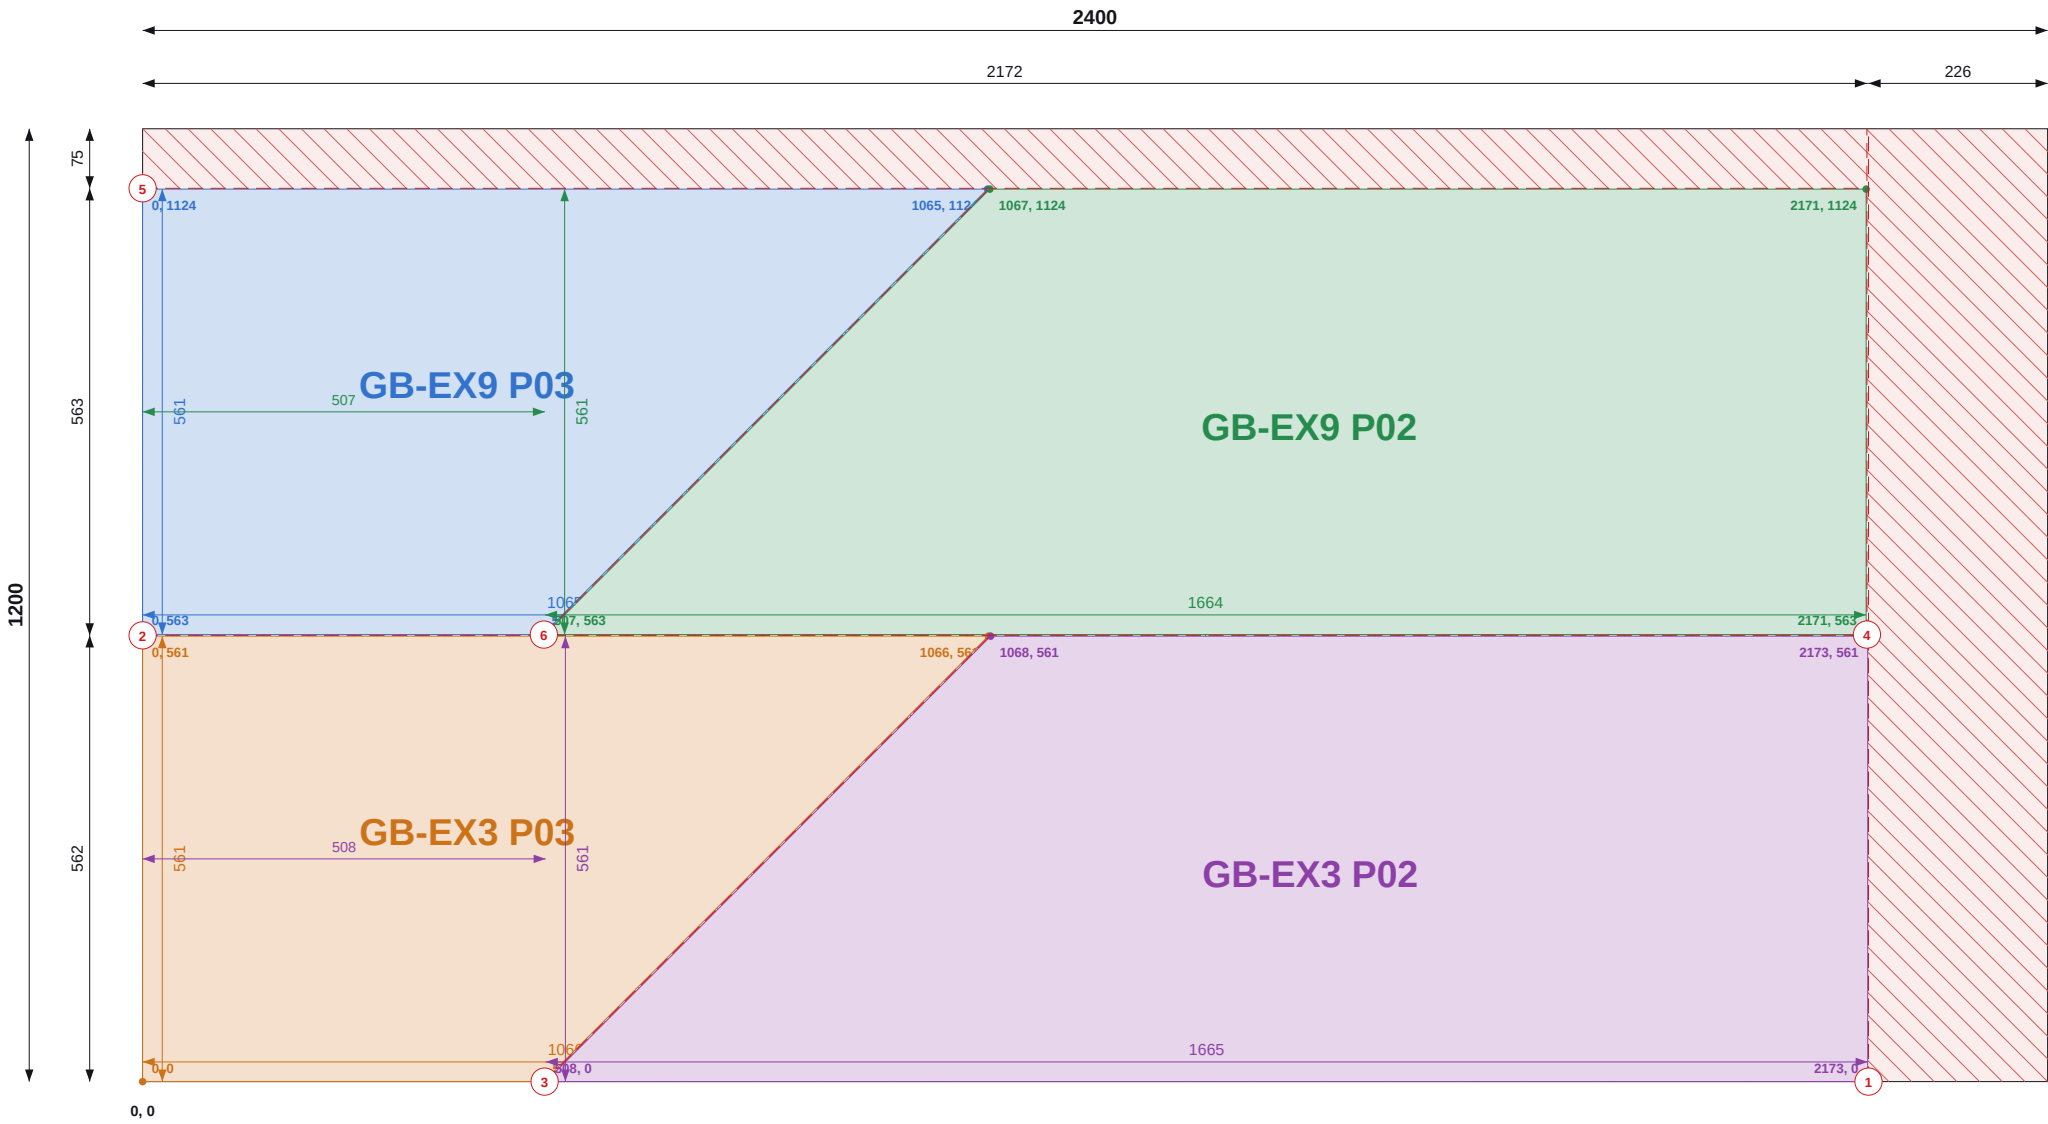

Top / left chains = saw cut positions (to cut centres). Coloured = part size and position.

SHEET 9 OF 11

THIS SHEET

| Item              | Value           |
|-------------------|-----------------|
| Parts             | 4               |
| Used / waste      | 84.5% / 0.45 m2 |
| Reusable offcuts  | 0               |
| Saw cuts / shared | 6 / 3           |

PIECES (POSITION = BOTTOM-LEFT CORNER)

| Label      | Size                    | X, Y     |
|------------|-------------------------|----------|
| GB-EX9 P03 | 561 x 1064 rake to 505  | 0, 563   |
| GB-EX9 P02 | 561 x 1664 rake to 1105 | 507, 563 |
| GB-EX3 P03 | 561 x 1065 rake to 506  | 0, 0     |
| GB-EX3 P02 | 561 x 1665 rake to 1106 | 508, 0   |

NOTES

- Cut from PIR 120mm 1200x2400, 2mm saw kerf. Viewed on the face; dimensions from the sheet's bottom-left corner (0,0). Red numbered lines = saw cuts in order, each edge to edge.
- Coloured dimensions belong to the part of that colour: its width and height, and its position from the sheet edges. Raked parts: corner coordinates at each corner.
- Red hatch = waste. Labels = panel + piece mark on the manufacture drawing.

REVISIONS

| REV | DATE     | DESCRIPTION        |
|-----|----------|--------------------|
| C01 | 13.09.26 | Construction issue |



TLS TIMBER FRAME

Design & Manufacture

Scan: 3D model + drawings



|          |                            |
|----------|----------------------------|
| CLIENT   | PROJECT                    |
| MP Adams | MP Adams Plot 3, Eckington |


DRAWING TITLE  
**PIR CUTTING - GABLES - SHEET 9 OF 11**

PIR 120mm 1200x2400 | Gables

|       |      |          |       |
|-------|------|----------|-------|
| SCALE | SIZE | DATE     | DRAWN |
| NTS   | A3   | 13.09.26 | TS    |

|              |                          |            |
|--------------|--------------------------|------------|
| STATUS       | DRAWING No.              | REV        |
| CONSTRUCTION | <b>P3-CP-PIR-03 / 09</b> | <b>C01</b> |

Do not scale. All dimensions in mm. Check all dimensions on site.

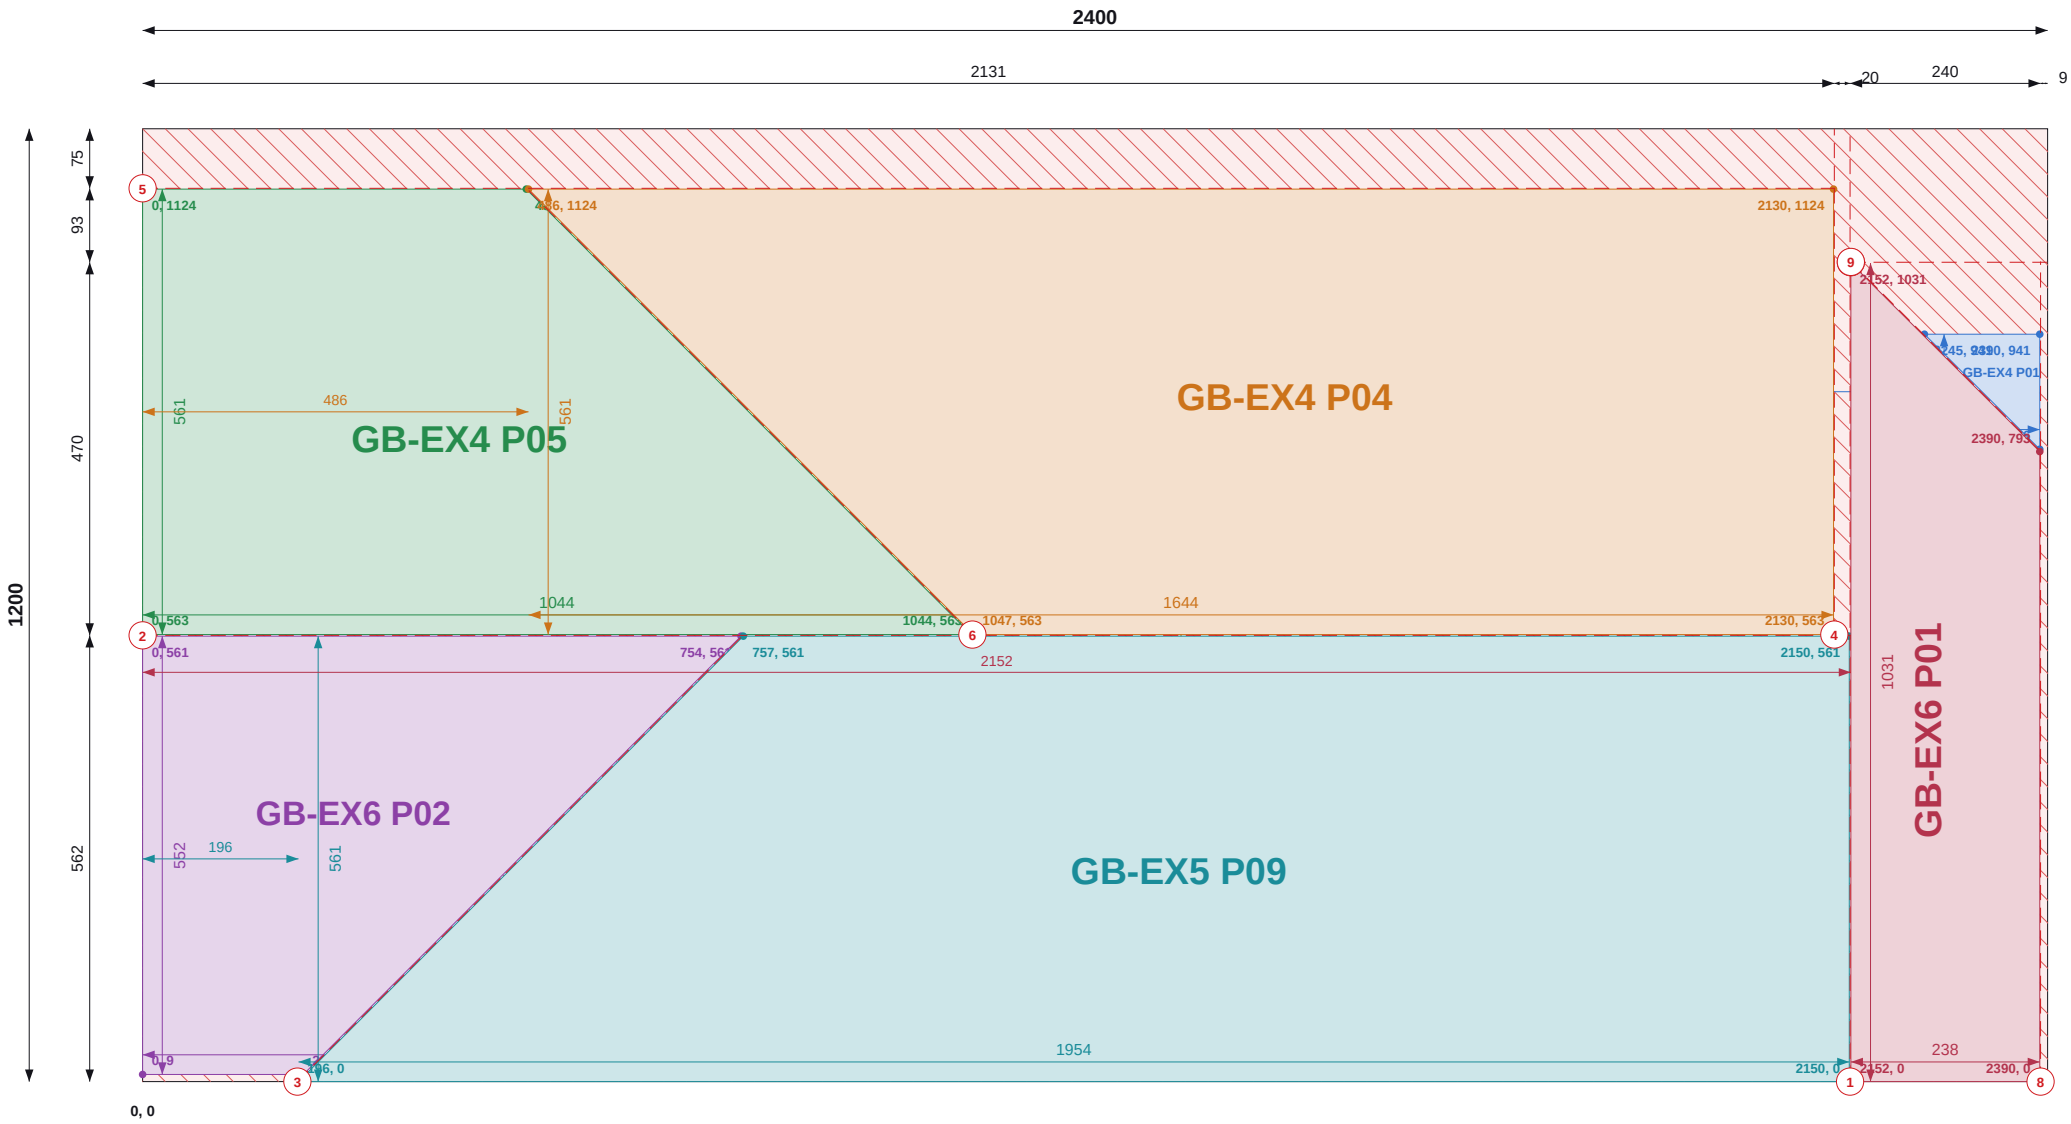

Top / left chains = saw cut positions (to cut centres). Coloured = part size and position.

SHEET 10 OF 11

THIS SHEET

| Item              | Value           |
|-------------------|-----------------|
| Parts             | 6               |
| Used / waste      | 91.1% / 0.26 m2 |
| Reusable offcuts  | 0               |
| Saw cuts / shared | 9 / 5           |

PIECES (POSITION = BOTTOM-LEFT CORNER)

| Label      | Size                    | X, Y      |
|------------|-------------------------|-----------|
| GB-EX4 P01 | 145 x 145 rake to 1     | 2245, 796 |
| GB-EX4 P05 | 561 x 1044 rake to 484  | 0, 563    |
| GB-EX4 P04 | 561 x 1644 rake to 1085 | 486, 563  |
| GB-EX6 P02 | 552 x 754 rake to 204   | 0, 9      |
| GB-EX5 P09 | 561 x 1954 rake to 1394 | 196, 0    |
| GB-EX6 P01 | 238 x 1031 rake to 795  | 2152, 0   |

NOTES

- Cut from PIR 120mm 1200x2400, 2mm saw kerf. Viewed on the face; dimensions from the sheet's bottom-left corner (0,0). Red numbered lines = saw cuts in order, each edge to edge.
- Coloured dimensions belong to the part of that colour: its width and height, and its position from the sheet edges. Raked parts: corner coordinates at each corner.
- Red hatch = waste. Labels = panel + piece mark on the manufacture drawing.

REVISIONS

| REV | DATE     | DESCRIPTION        |
|-----|----------|--------------------|
| C01 | 13.09.26 | Construction issue |



TLS TIMBER FRAME

Design & Manufacture

Scan: 3D model + drawings



|          |                            |
|----------|----------------------------|
| CLIENT   | PROJECT                    |
| MP Adams | MP Adams Plot 3, Eckington |

|                                       |
|---------------------------------------|
| DRAWING TITLE                         |
| PIR CUTTING - GABLES - SHEET 10 OF 11 |

PIR 120mm 1200x2400 | Gables

|       |      |          |       |
|-------|------|----------|-------|
| SCALE | SIZE | DATE     | DRAWN |
| NTS   | A3   | 13.09.26 | TS    |

|              |                   |     |
|--------------|-------------------|-----|
| STATUS       | DRAWING No.       | REV |
| CONSTRUCTION | P3-CP-PIR-03 / 10 | C01 |

