

Do not scale. All dimensions in mm. Check all dimensions on site.



Top / left chains = saw cut positions (to cut centres). Coloured = part size and position.

SHEET 1 OF 38

THIS SHEET

Item	Value
Parts	1
Used / waste	99.4% / 0.02 m2
Reusable offcuts	0
Saw cuts / shared	1 / 0

PIECES (POSITION = BOTTOM-LEFT CORNER)

Label	Size	X, Y
GF-EX1 S02	1197 x 2383	0, 0

GROUND FLOOR TOTALS

Item	Value
Sheets / pieces	38 / 79
Yield / waste	92.4% / 8.25 m2
Saw cuts / shared / on stock edge	119 / 41 / 118

NOTES

- Cut from OSB/3 9mm 1197x2397, 2mm saw kerf. Viewed on the face; dimensions from the sheet's bottom-left corner (0,0). Red numbered lines = saw cuts in order, each edge to edge.
- Coloured dimensions belong to the part of that colour: its width and height, and its position from the sheet edges. Raked parts: corner coordinates at each corner.
- Red hatch = waste. Labels = panel + piece mark on the manufacture drawing.

REVISIONS

REV	DATE	DESCRIPTION
C01	13.09.26	Construction issue



TLS TIMBER FRAME

Design & Manufacture

Scan: 3D model + drawings



CLIENT	PROJECT
MP Adams	MP Adams Plot 3, Eckington

DRAWING TITLE

OSB CUTTING - GROUND FLOOR - SHEET 1 OF 38

OSB/3 9mm 1197x2397 | Ground Floor

SCALE	SIZE	DATE	DRAWN
NTS	A3	13.09.26	TS

STATUS	DRAWING No.	REV
CONSTRUCTION	P3-CP-OSB-01 / 01	C01

Do not scale. All dimensions in mm. Check all dimensions on site.



Top / left chains = saw cut positions (to cut centres). Coloured = part size and position.

SHEET 2 OF 38

THIS SHEET

Item	Value
Parts	1
Used / waste	99.4% / 0.02 m2
Reusable offcuts	0
Saw cuts / shared	1 / 0

PIECES (POSITION = BOTTOM-LEFT CORNER)

Label	Size	X, Y
GF-IL2 S02	1197 x 2383	0, 0

NOTES

- Cut from OSB/3 9mm 1197x2397, 2mm saw kerf. Viewed on the face; dimensions from the sheet's bottom-left corner (0,0). Red numbered lines = saw cuts in order, each edge to edge.
- Coloured dimensions belong to the part of that colour: its width and height, and its position from the sheet edges. Raked parts: corner coordinates at each corner.
- Red hatch = waste. Labels = panel + piece mark on the manufacture drawing.

REVISIONS

REV	DATE	DESCRIPTION
C01	13.09.26	Construction issue



TLS TIMBER FRAME

Design & Manufacture

Scan: 3D model + drawings



CLIENT	PROJECT
MP Adams	MP Adams Plot 3, Eckington

DRAWING TITLE
OSB CUTTING - GROUND FLOOR - SHEET 2 OF 38

OSB/3 9mm 1197x2397 | Ground Floor

SCALE	SIZE	DATE	DRAWN
NTS	A3	13.09.26	TS

STATUS	DRAWING No.	REV
CONSTRUCTION	P3-CP-OSB-01 / 02	C01

Do not scale. All dimensions in mm. Check all dimensions on site.



Top / left chains = saw cut positions (to cut centres). Coloured = part size and position.

SHEET 3 OF 38

THIS SHEET

Item	Value
Parts	1
Used / waste	99.4% / 0.02 m2
Reusable offcuts	0
Saw cuts / shared	1 / 0

PIECES (POSITION = BOTTOM-LEFT CORNER)

Label	Size	X, Y
GF-IL5 S02	1197 x 2383	0, 0

NOTES

- Cut from OSB/3 9mm 1197x2397, 2mm saw kerf. Viewed on the face; dimensions from the sheet's bottom-left corner (0,0). Red numbered lines = saw cuts in order, each edge to edge.
- Coloured dimensions belong to the part of that colour: its width and height, and its position from the sheet edges. Raked parts: corner coordinates at each corner.
- Red hatch = waste. Labels = panel + piece mark on the manufacture drawing.

REVISIONS

REV	DATE	DESCRIPTION
C01	13.09.26	Construction issue



TLS TIMBER FRAME

Design & Manufacture

Scan: 3D model + drawings



CLIENT MP Adams	PROJECT MP Adams Plot 3, Eckington
--------------------	---------------------------------------


DRAWING TITLE
OSB CUTTING - GROUND FLOOR - SHEET 3 OF 38

OSB/3 9mm 1197x2397 | Ground Floor

SCALE NTS	SIZE A3	DATE 13.09.26	DRAWN TS
--------------	------------	------------------	-------------

STATUS CONSTRUCTION	DRAWING No. P3-CP-OSB-01 / 03	REV C01
-------------------------------	---	-------------------

Do not scale. All dimensions in mm. Check all dimensions on site.

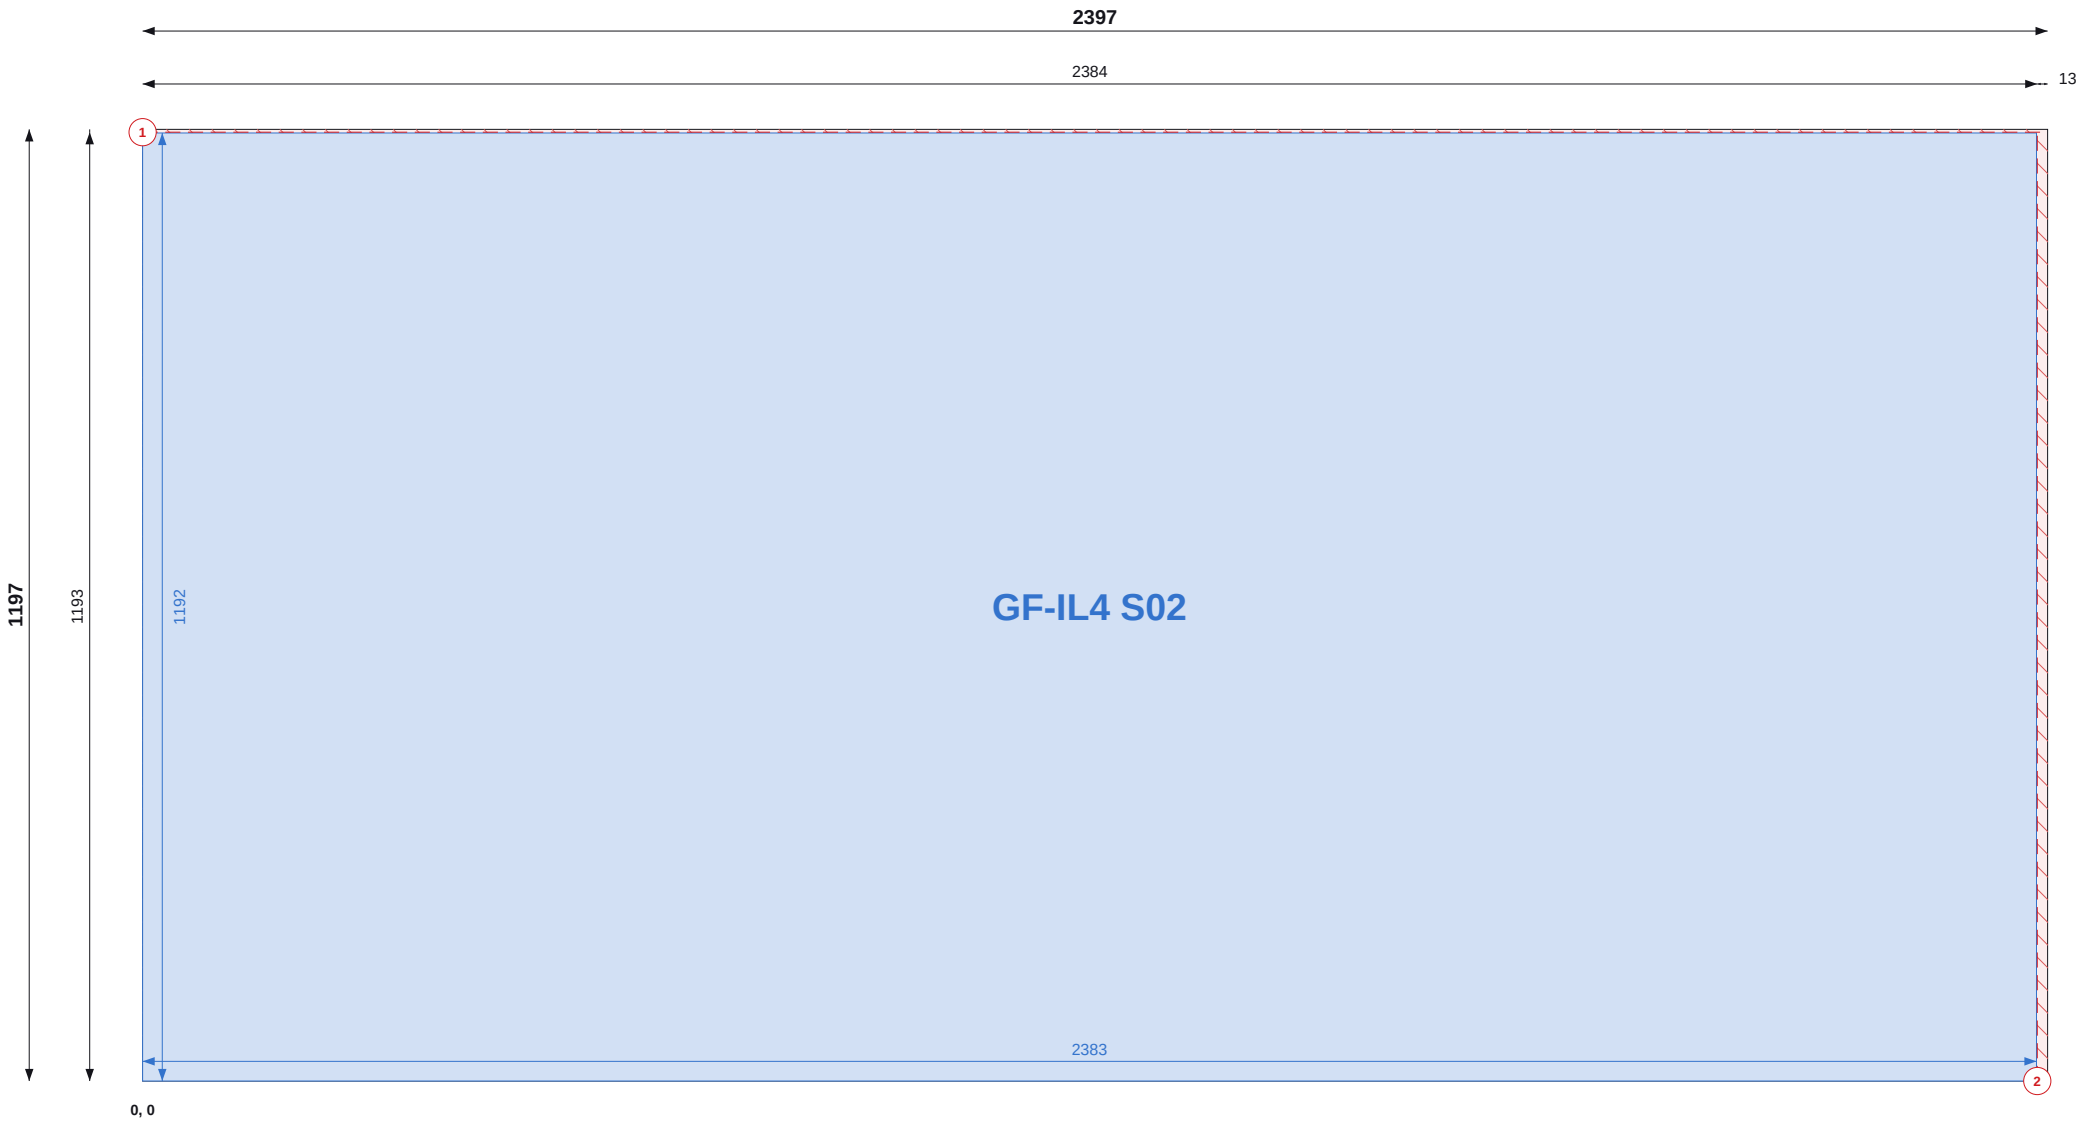

Top / left chains = saw cut positions (to cut centres). Coloured = part size and position.

SHEET 4 OF 38

THIS SHEET

Item	Value
Parts	1
Used / waste	99.0% / 0.03 m2
Reusable offcuts	0
Saw cuts / shared	2 / 0

PIECES (POSITION = BOTTOM-LEFT CORNER)

Label	Size	X, Y
GF-IL4 S02	1192 x 2383	0, 0

NOTES

- Cut from OSB/3 9mm 1197x2397, 2mm saw kerf. Viewed on the face; dimensions from the sheet's bottom-left corner (0,0). Red numbered lines = saw cuts in order, each edge to edge.
- Coloured dimensions belong to the part of that colour: its width and height, and its position from the sheet edges. Raked parts: corner coordinates at each corner.
- Red hatch = waste. Labels = panel + piece mark on the manufacture drawing.

REVISIONS

REV	DATE	DESCRIPTION
C01	13.09.26	Construction issue



TLS TIMBER FRAME

Design & Manufacture

Scan: 3D model + drawings



CLIENT	PROJECT
MP Adams	MP Adams Plot 3, Eckington


DRAWING TITLE
OSB CUTTING - GROUND FLOOR - SHEET 4 OF 38

OSB/3 9mm 1197x2397 | Ground Floor

SCALE	SIZE	DATE	DRAWN
NTS	A3	13.09.26	TS

STATUS	DRAWING No.	REV
CONSTRUCTION	P3-CP-OSB-01 / 04	C01

Do not scale. All dimensions in mm. Check all dimensions on site.

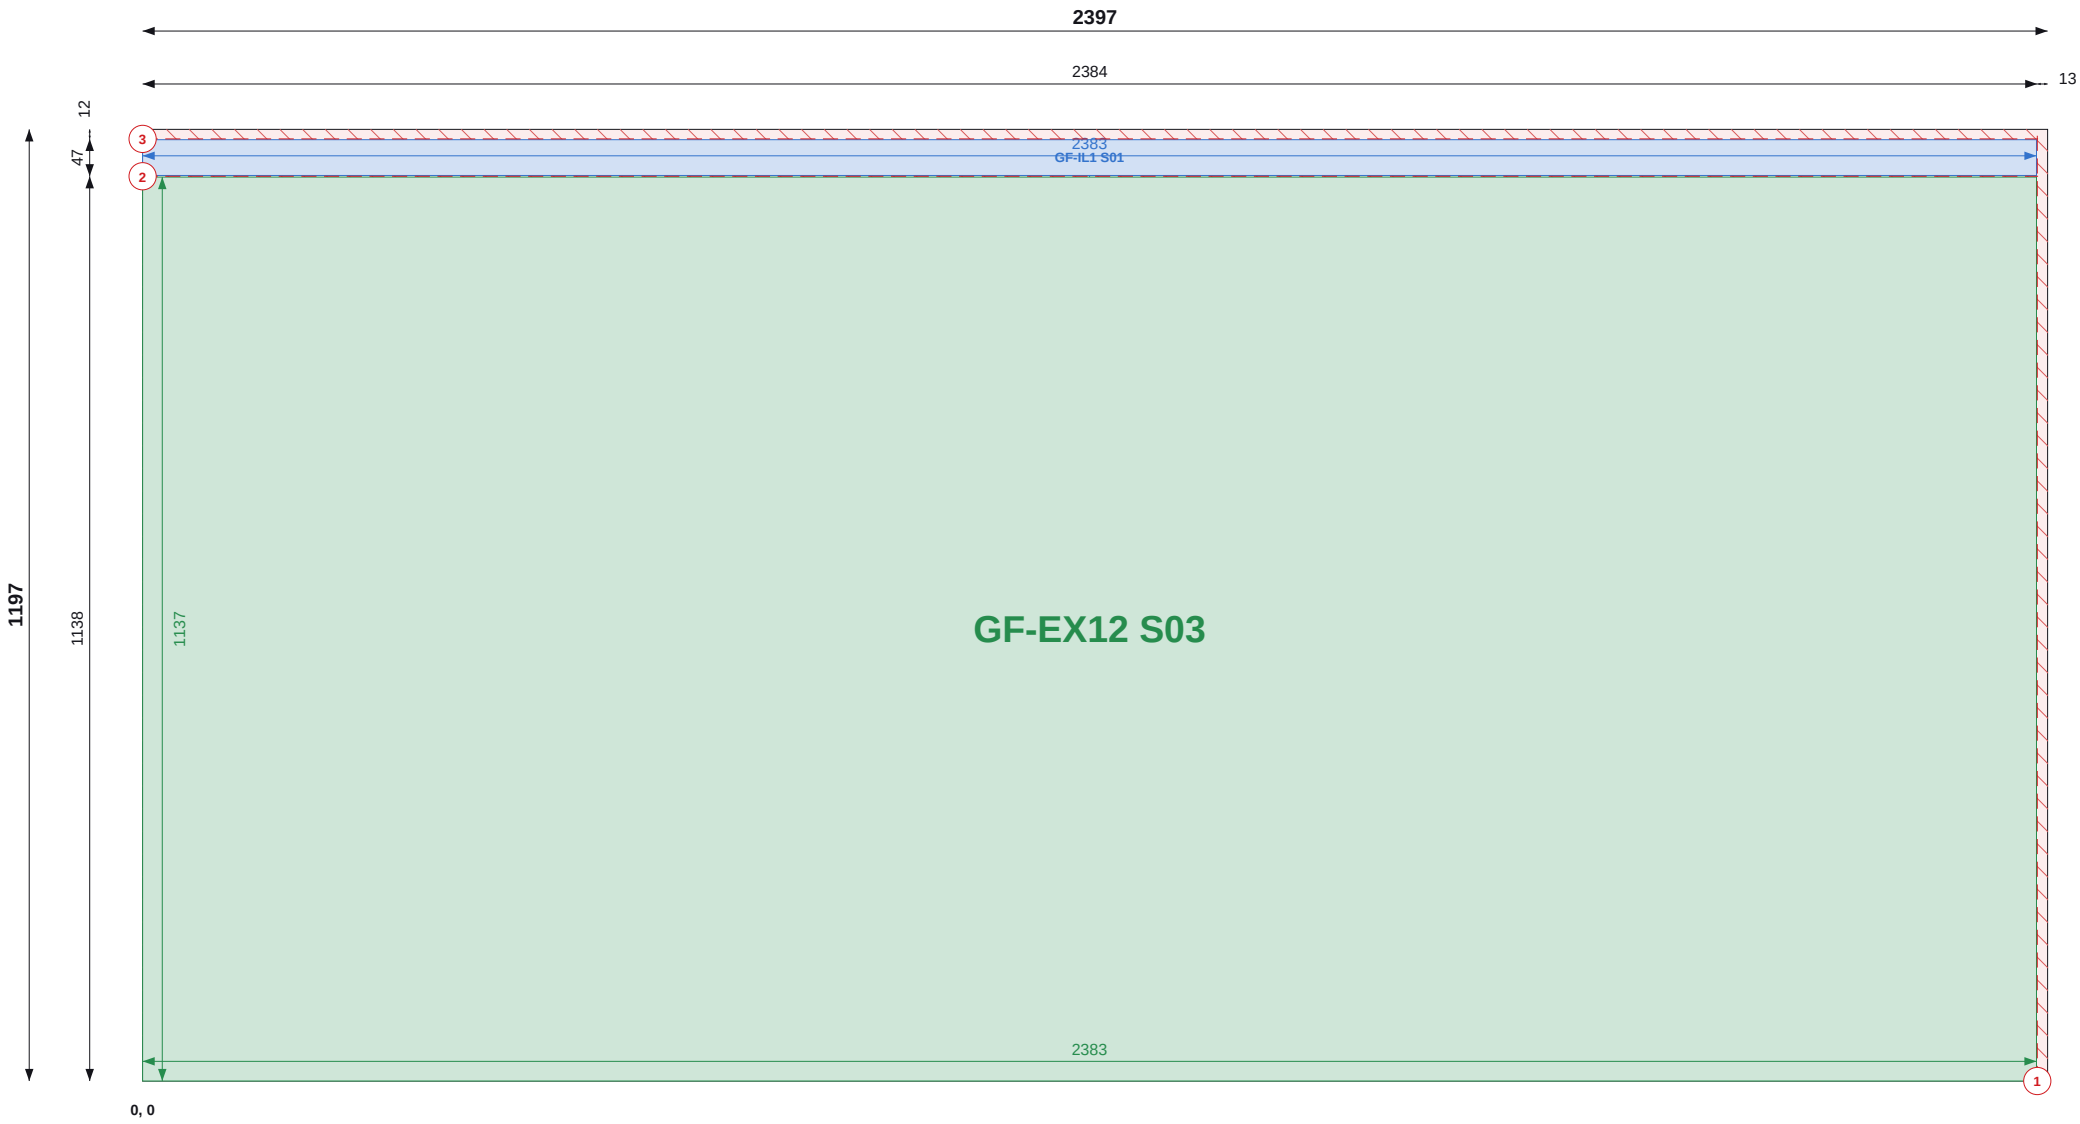

Top / left chains = saw cut positions (to cut centres). Coloured = part size and position.

SHEET 5 OF 38

THIS SHEET

Item	Value
Parts	2
Used / waste	98.2% / 0.05 m2
Reusable offcuts	0
Saw cuts / shared	3 / 1

PIECES (POSITION = BOTTOM-LEFT CORNER)

Label	Size	X, Y
GF-IL1 S01	45 x 2383	0, 1139
GF-EX12 S03	1137 x 2383	0, 0

NOTES

- Cut from OSB/3 9mm 1197x2397, 2mm saw kerf. Viewed on the face; dimensions from the sheet's bottom-left corner (0,0). Red numbered lines = saw cuts in order, each edge to edge.
- Coloured dimensions belong to the part of that colour: its width and height, and its position from the sheet edges. Raked parts: corner coordinates at each corner.
- Red hatch = waste. Labels = panel + piece mark on the manufacture drawing.

REVISIONS

REV	DATE	DESCRIPTION
C01	13.09.26	Construction issue



TLS TIMBER FRAME

Design & Manufacture

Scan: 3D model + drawings



CLIENT MP Adams	PROJECT MP Adams Plot 3, Eckington
--------------------	---------------------------------------


DRAWING TITLE OSB CUTTING - GROUND FLOOR - SHEET 5 OF 38
--

OSB/3 9mm 1197x2397 | Ground Floor

SCALE NTS	SIZE A3	DATE 13.09.26	DRAWN TS
--------------	------------	------------------	-------------

STATUS CONSTRUCTION	DRAWING No. P3-CP-OSB-01 / 05	REV C01
-------------------------------	---	-------------------

Do not scale. All dimensions in mm. Check all dimensions on site.

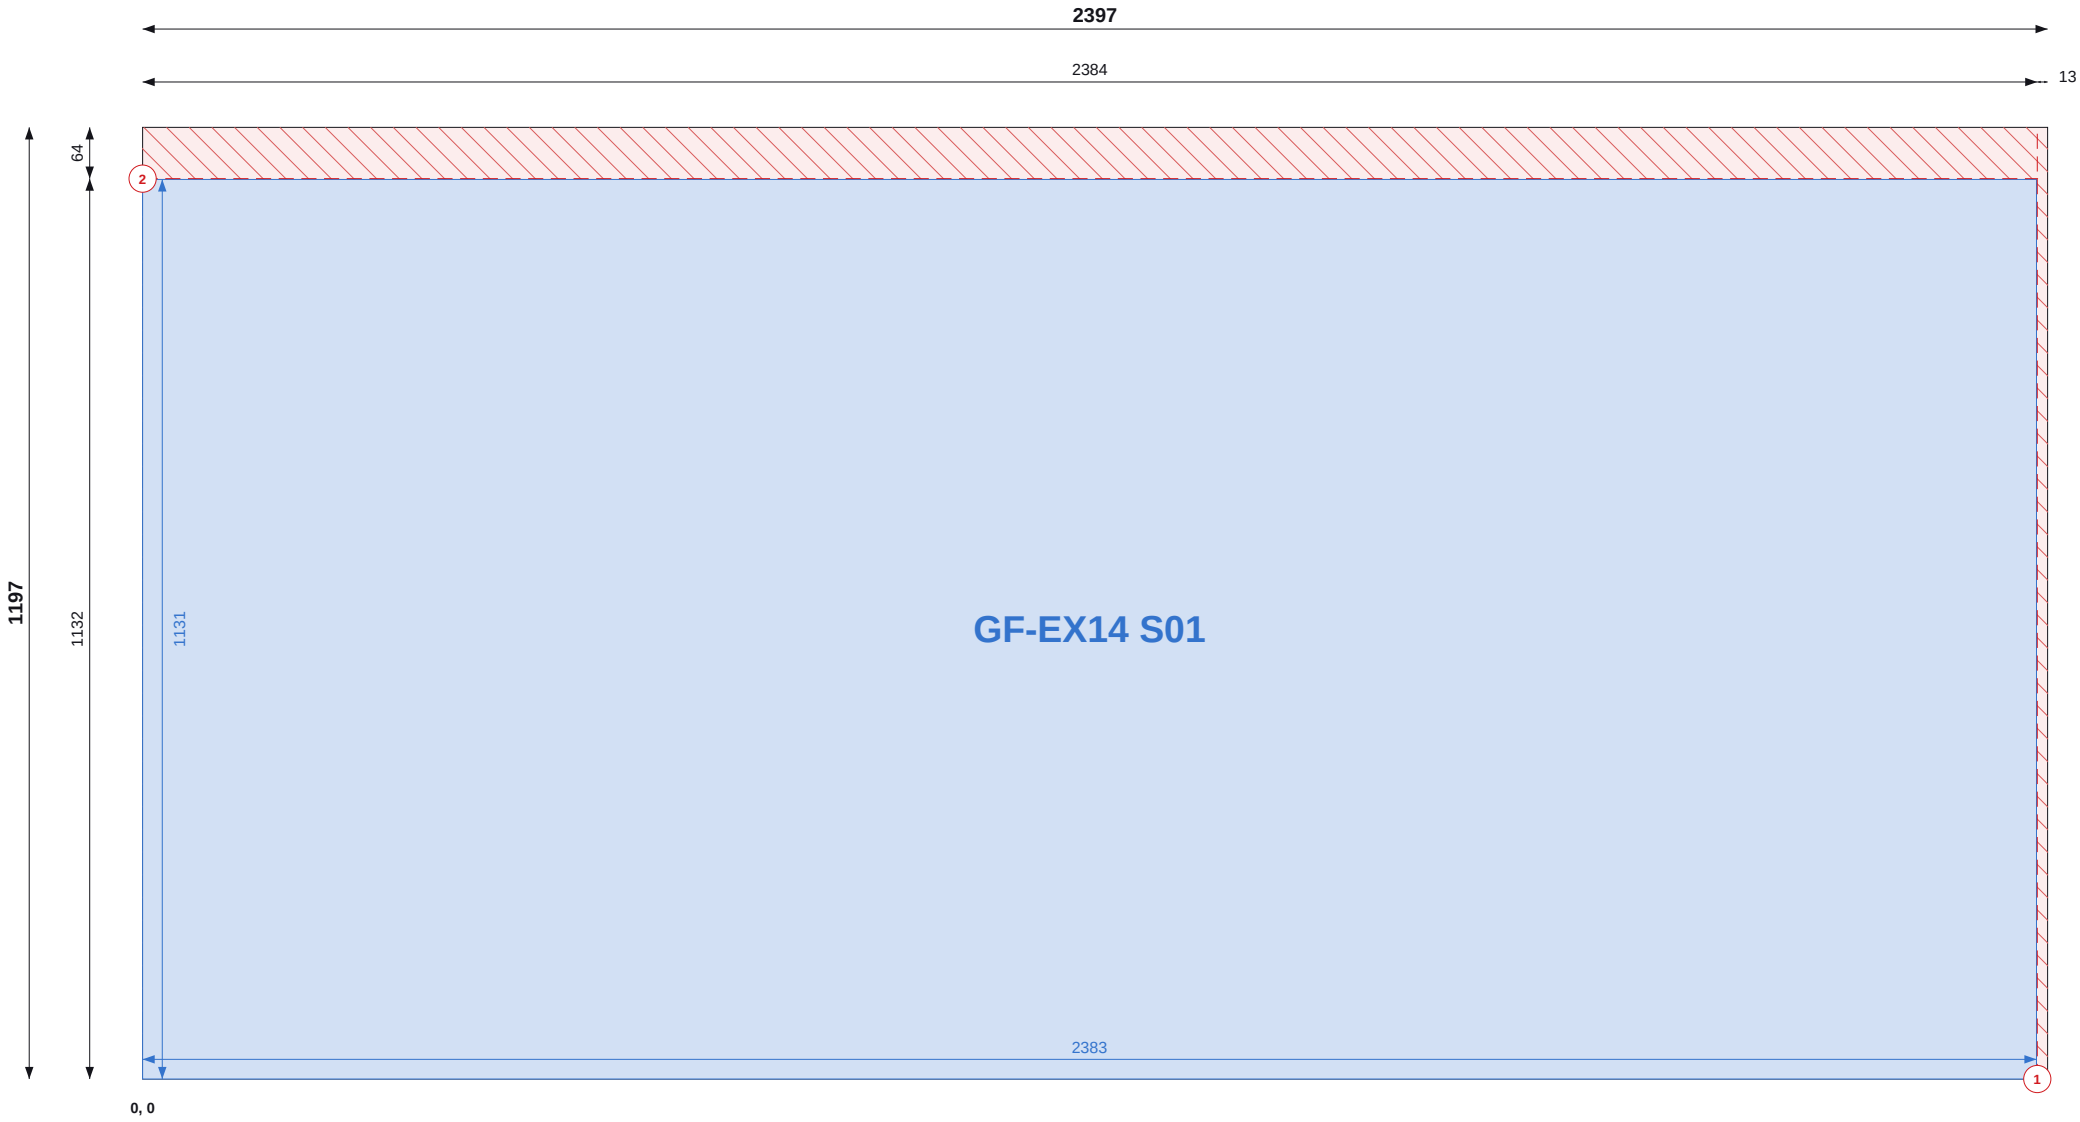

Top / left chains = saw cut positions (to cut centres). Coloured = part size and position.

SHEET 6 OF 38

THIS SHEET

Item	Value
Parts	1
Used / waste	94.0% / 0.17 m2
Reusable offcuts	0
Saw cuts / shared	2 / 0

PIECES (POSITION = BOTTOM-LEFT CORNER)

Label	Size	X, Y
GF-EX14 S01	1131 x 2383	0, 0

NOTES

- Cut from OSB/3 9mm 1197x2397, 2mm saw kerf. Viewed on the face; dimensions from the sheet's bottom-left corner (0,0). Red numbered lines = saw cuts in order, each edge to edge.
- Coloured dimensions belong to the part of that colour: its width and height, and its position from the sheet edges. Raked parts: corner coordinates at each corner.
- Red hatch = waste. Labels = panel + piece mark on the manufacture drawing.

REVISIONS

REV	DATE	DESCRIPTION
C01	13.09.26	Construction issue



TLS TIMBER FRAME

Design & Manufacture

Scan: 3D model + drawings




CLIENT	PROJECT
MP Adams	MP Adams Plot 3, Eckington

DRAWING TITLE			
OSB CUTTING - GROUND FLOOR - SHEET 6 OF 38			
OSB/3 9mm 1197x2397 Ground Floor			

SCALE	SIZE	DATE	DRAWN
NTS	A3	13.09.26	TS

STATUS	DRAWING No.	REV
CONSTRUCTION	P3-CP-OSB-01 / 06	C01

Do not scale. All dimensions in mm. Check all dimensions on site.

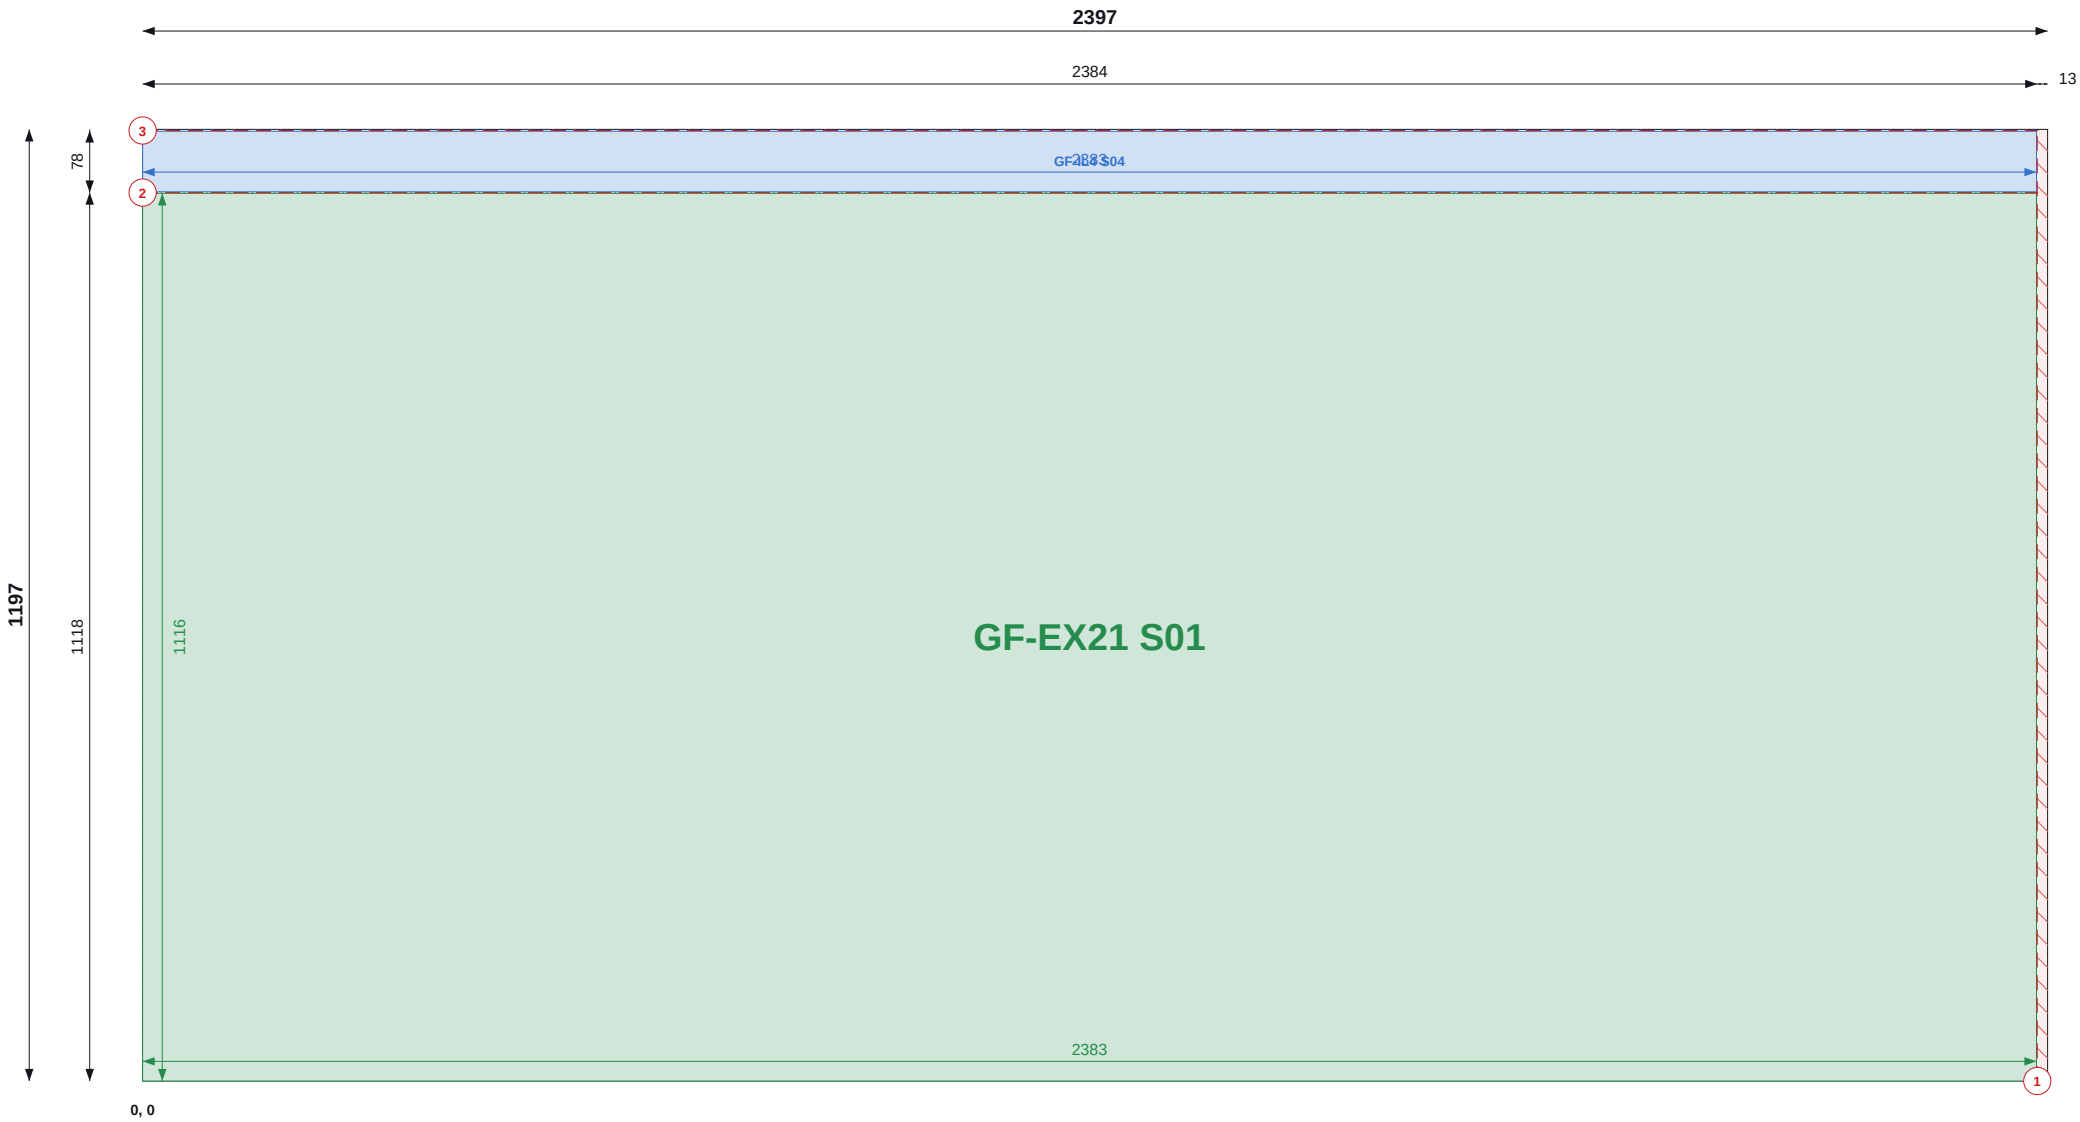

Top / left chains = saw cut positions (to cut centres). Coloured = part size and position.

SHEET 7 OF 38

THIS SHEET

Item	Value
Parts	2
Used / waste	99.0% / 0.03 m2
Reusable offcuts	0
Saw cuts / shared	3 / 1

PIECES (POSITION = BOTTOM-LEFT CORNER)

Label	Size	X, Y
GF-IL4 S04	76 x 2383	0, 1118
GF-EX21 S01	1116 x 2383	0, 0

NOTES

- Cut from OSB/3 9mm 1197x2397, 2mm saw kerf. Viewed on the face; dimensions from the sheet's bottom-left corner (0,0). Red numbered lines = saw cuts in order, each edge to edge.
- Coloured dimensions belong to the part of that colour: its width and height, and its position from the sheet edges. Raked parts: corner coordinates at each corner.
- Red hatch = waste. Labels = panel + piece mark on the manufacture drawing.

REVISIONS

REV	DATE	DESCRIPTION
C01	13.09.26	Construction issue



TLS TIMBER FRAME

Design & Manufacture

Scan: 3D model + drawings



CLIENT	PROJECT
MP Adams	MP Adams Plot 3, Eckington


DRAWING TITLE
OSB CUTTING - GROUND FLOOR - SHEET 7 OF 38

OSB/3 9mm 1197x2397 | Ground Floor

SCALE	SIZE	DATE	DRAWN
NTS	A3	13.09.26	TS

STATUS	DRAWING No.	REV
CONSTRUCTION	P3-CP-OSB-01 / 07	C01

Do not scale. All dimensions in mm. Check all dimensions on site.

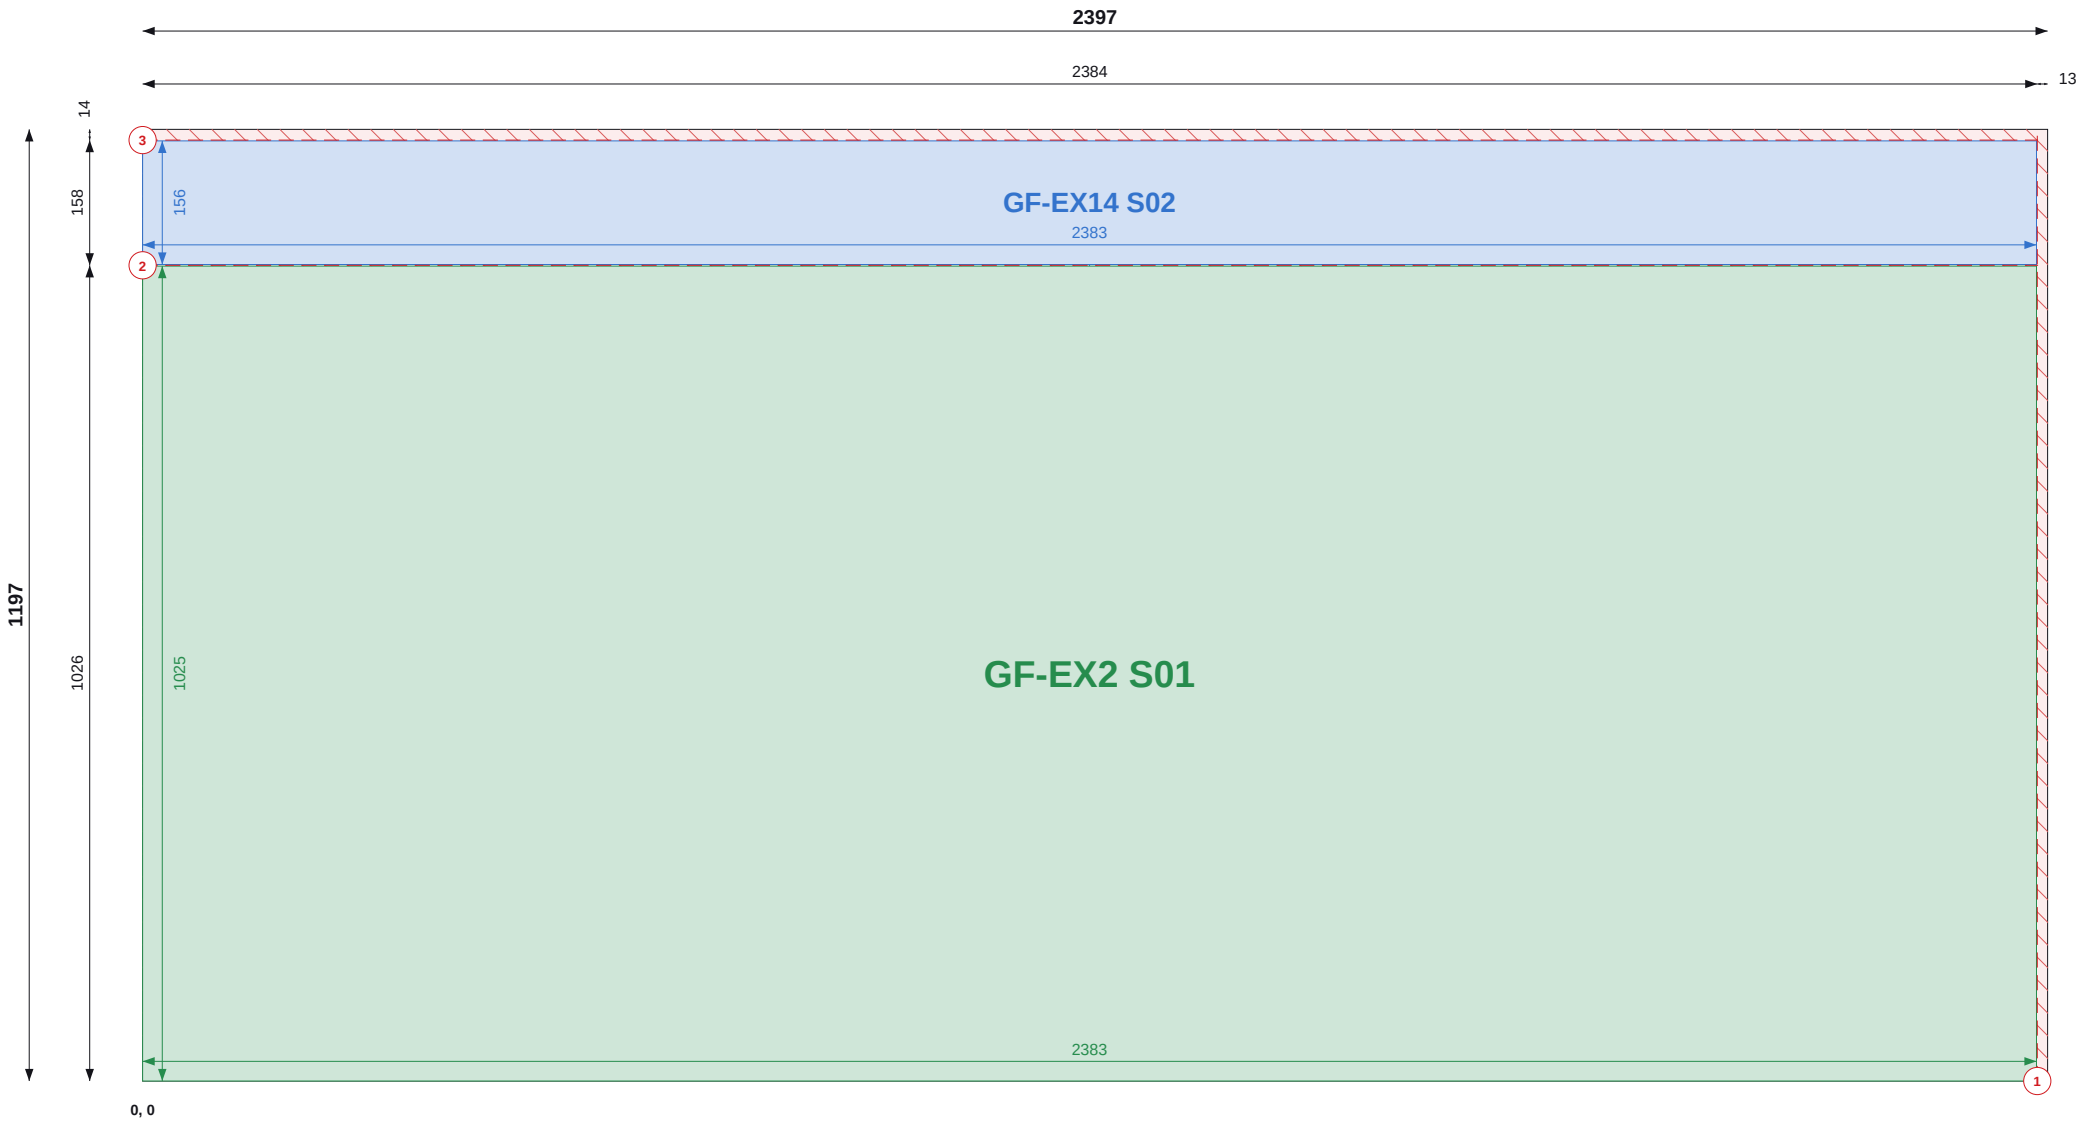

Top / left chains = saw cut positions (to cut centres). Coloured = part size and position.

SHEET 8 OF 38

THIS SHEET

Item	Value
Parts	2
Used / waste	98.0% / 0.06 m2
Reusable offcuts	0
Saw cuts / shared	3 / 1

PIECES (POSITION = BOTTOM-LEFT CORNER)

Label	Size	X, Y
GF-EX14 S02	156 x 2383	0, 1027
GF-EX2 S01	1025 x 2383	0, 0

NOTES

- Cut from OSB/3 9mm 1197x2397, 2mm saw kerf. Viewed on the face; dimensions from the sheet's bottom-left corner (0,0). Red numbered lines = saw cuts in order, each edge to edge.
- Coloured dimensions belong to the part of that colour: its width and height, and its position from the sheet edges. Raked parts: corner coordinates at each corner.
- Red hatch = waste. Labels = panel + piece mark on the manufacture drawing.

REVISIONS

REV	DATE	DESCRIPTION
C01	13.09.26	Construction issue



TLS TIMBER FRAME

Design & Manufacture

Scan: 3D model + drawings



CLIENT	PROJECT
MP Adams	MP Adams Plot 3, Eckington


DRAWING TITLE
OSB CUTTING - GROUND FLOOR - SHEET 8 OF 38

OSB/3 9mm 1197x2397 | Ground Floor

SCALE	SIZE	DATE	DRAWN
NTS	A3	13.09.26	TS

STATUS	DRAWING No.	REV
CONSTRUCTION	P3-CP-OSB-01 / 08	C01

Do not scale. All dimensions in mm. Check all dimensions on site.

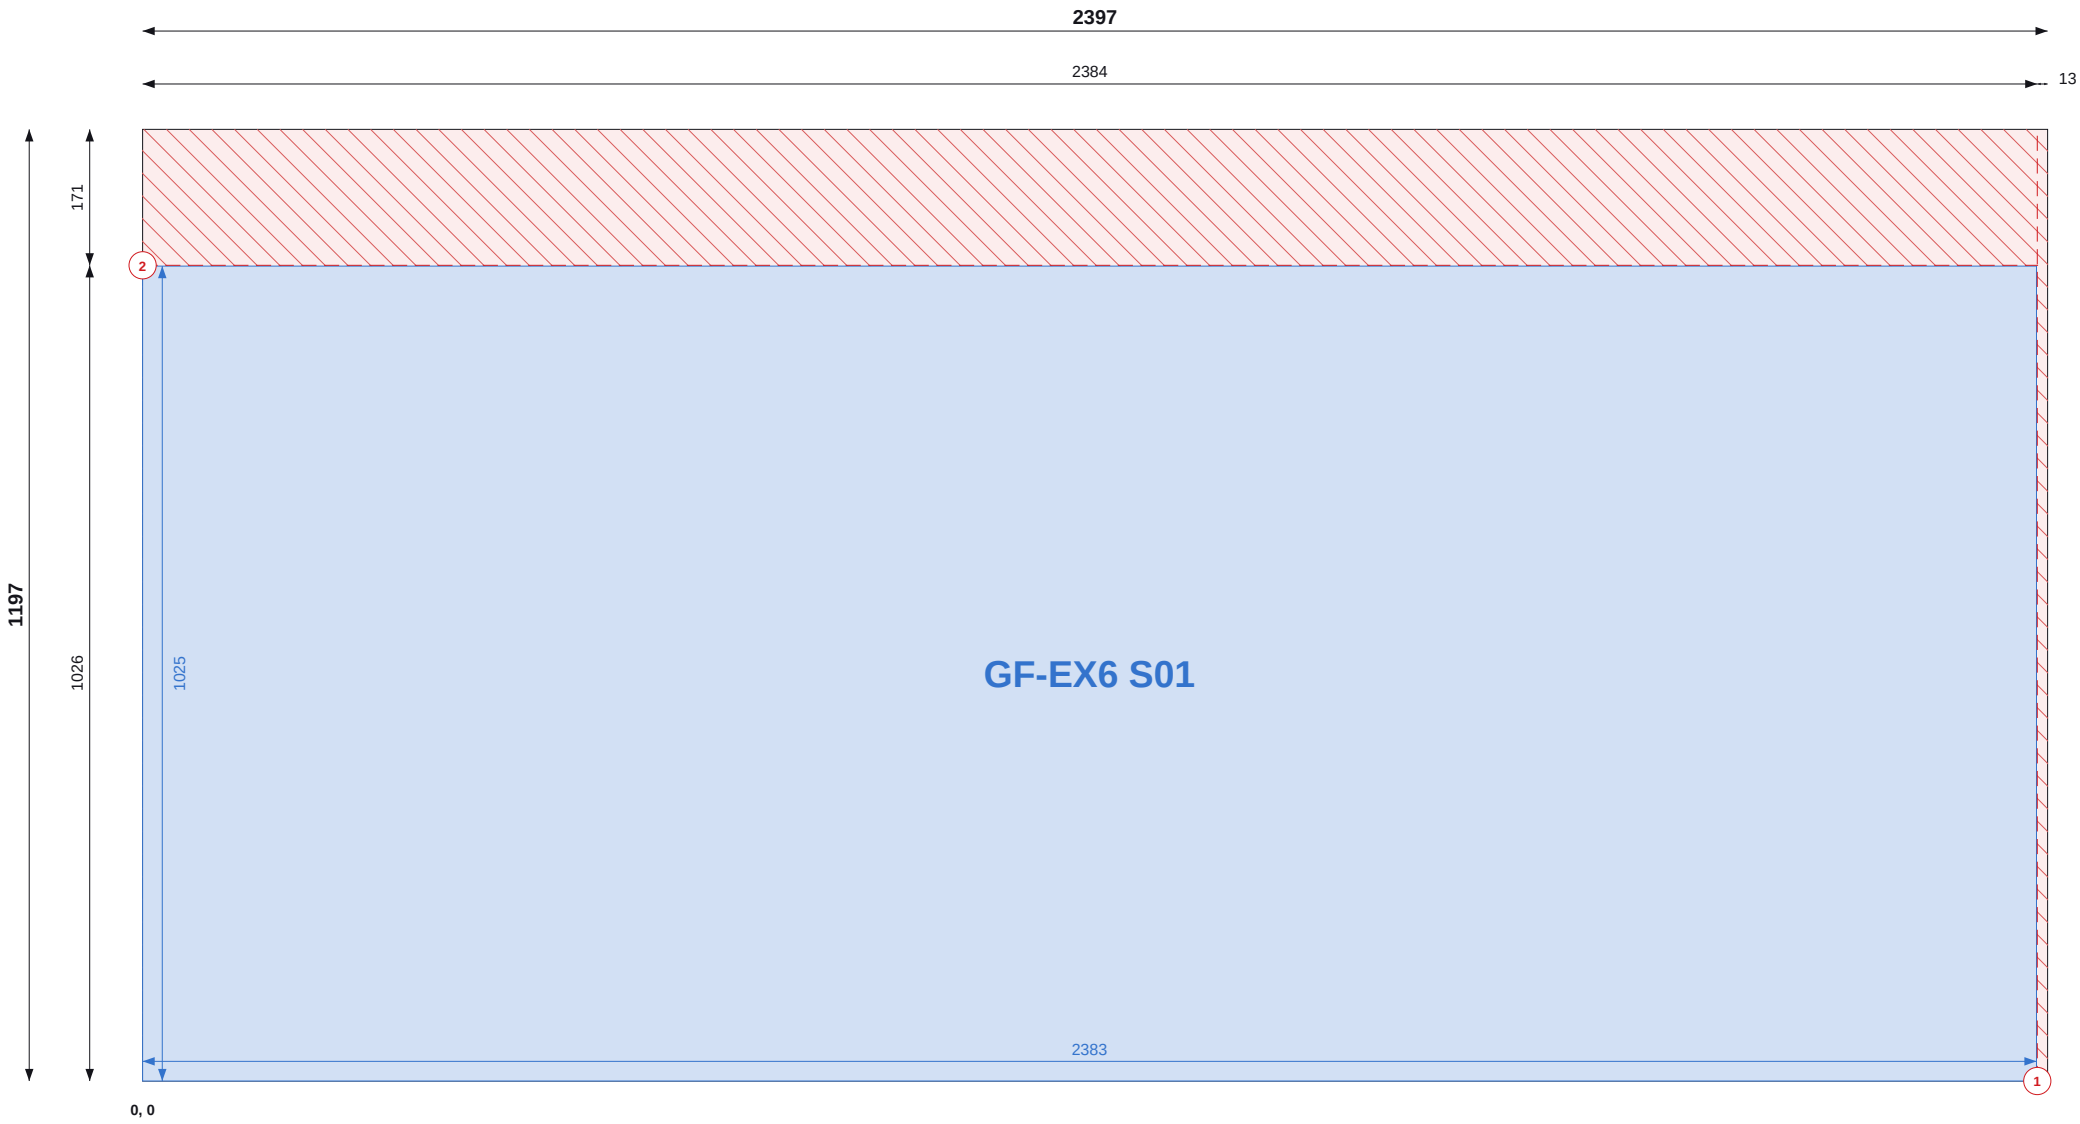

Top / left chains = saw cut positions (to cut centres). Coloured = part size and position.

SHEET 9 OF 38

THIS SHEET

Item	Value
Parts	1
Used / waste	85.1% / 0.43 m2
Reusable offcuts	0
Saw cuts / shared	2 / 0

PIECES (POSITION = BOTTOM-LEFT CORNER)

Label	Size	X, Y
GF-EX6 S01	1025 x 2383	0, 0

NOTES

- Cut from OSB/3 9mm 1197x2397, 2mm saw kerf. Viewed on the face; dimensions from the sheet's bottom-left corner (0,0). Red numbered lines = saw cuts in order, each edge to edge.
- Coloured dimensions belong to the part of that colour: its width and height, and its position from the sheet edges. Raked parts: corner coordinates at each corner.
- Red hatch = waste. Labels = panel + piece mark on the manufacture drawing.

REVISIONS

REV	DATE	DESCRIPTION
C01	13.09.26	Construction issue



TLS TIMBER FRAME
Design & Manufacture
Scan: 3D model + drawings



CLIENT MP Adams	PROJECT MP Adams Plot 3, Eckington
--------------------	---------------------------------------


DRAWING TITLE
OSB CUTTING - GROUND FLOOR - SHEET 9 OF 38

OSB/3 9mm 1197x2397 | Ground Floor

SCALE NTS	SIZE A3	DATE 13.09.26	DRAWN TS
--------------	------------	------------------	-------------

STATUS CONSTRUCTION	DRAWING No. P3-CP-OSB-01 / 09	REV C01
-------------------------------	---	-------------------

Do not scale. All dimensions in mm. Check all dimensions on site.

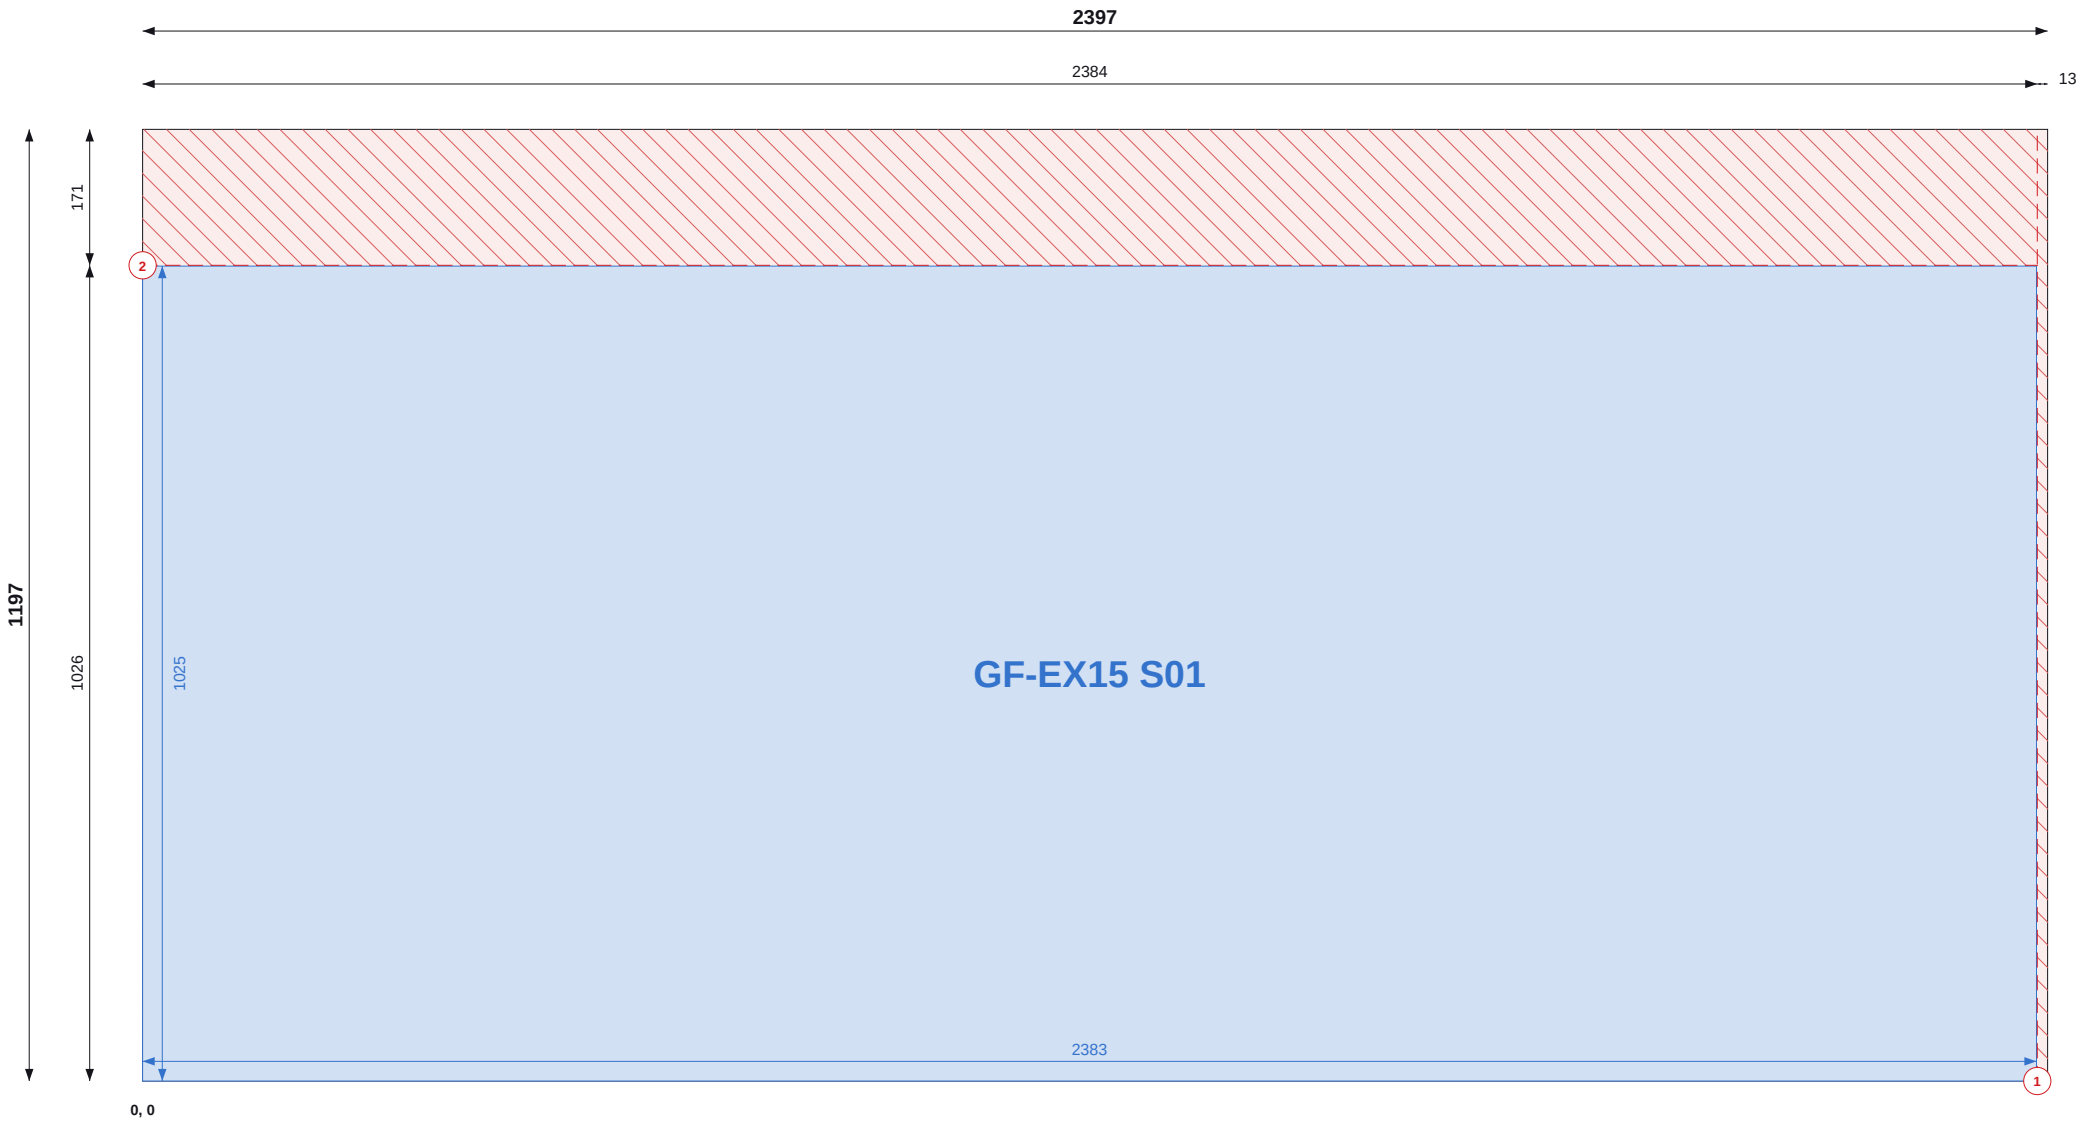

Top / left chains = saw cut positions (to cut centres). Coloured = part size and position.

SHEET 10 OF 38

THIS SHEET

Item	Value
Parts	1
Used / waste	85.1% / 0.43 m2
Reusable offcuts	0
Saw cuts / shared	2 / 0

PIECES (POSITION = BOTTOM-LEFT CORNER)

Label	Size	X, Y
GF-EX15 S01	1025 x 2383	0, 0

NOTES

1. Cut from OSB/3 9mm 1197x2397, 2mm saw kerf. Viewed on the face; dimensions from the sheet's bottom-left corner (0,0). Red numbered lines = saw cuts in order, each edge to edge.
2. Coloured dimensions belong to the part of that colour: its width and height, and its position from the sheet edges. Raked parts: corner coordinates at each corner.
3. Red hatch = waste. Labels = panel + piece mark on the manufacture drawing.

REVISIONS

REV	DATE	DESCRIPTION
C01	13.09.26	Construction issue



TLS TIMBER FRAME

Design & Manufacture

Scan: 3D model + drawings



CLIENT	PROJECT
MP Adams	MP Adams Plot 3, Eckington


DRAWING TITLE
OSB CUTTING - GROUND FLOOR - SHEET 10 OF 38

OSB/3 9mm 1197x2397 | Ground Floor

SCALE	SIZE	DATE	DRAWN
NTS	A3	13.09.26	TS

STATUS	DRAWING No.	REV
CONSTRUCTION	P3-CP-OSB-01 / 10	C01

Do not scale. All dimensions in mm. Check all dimensions on site.

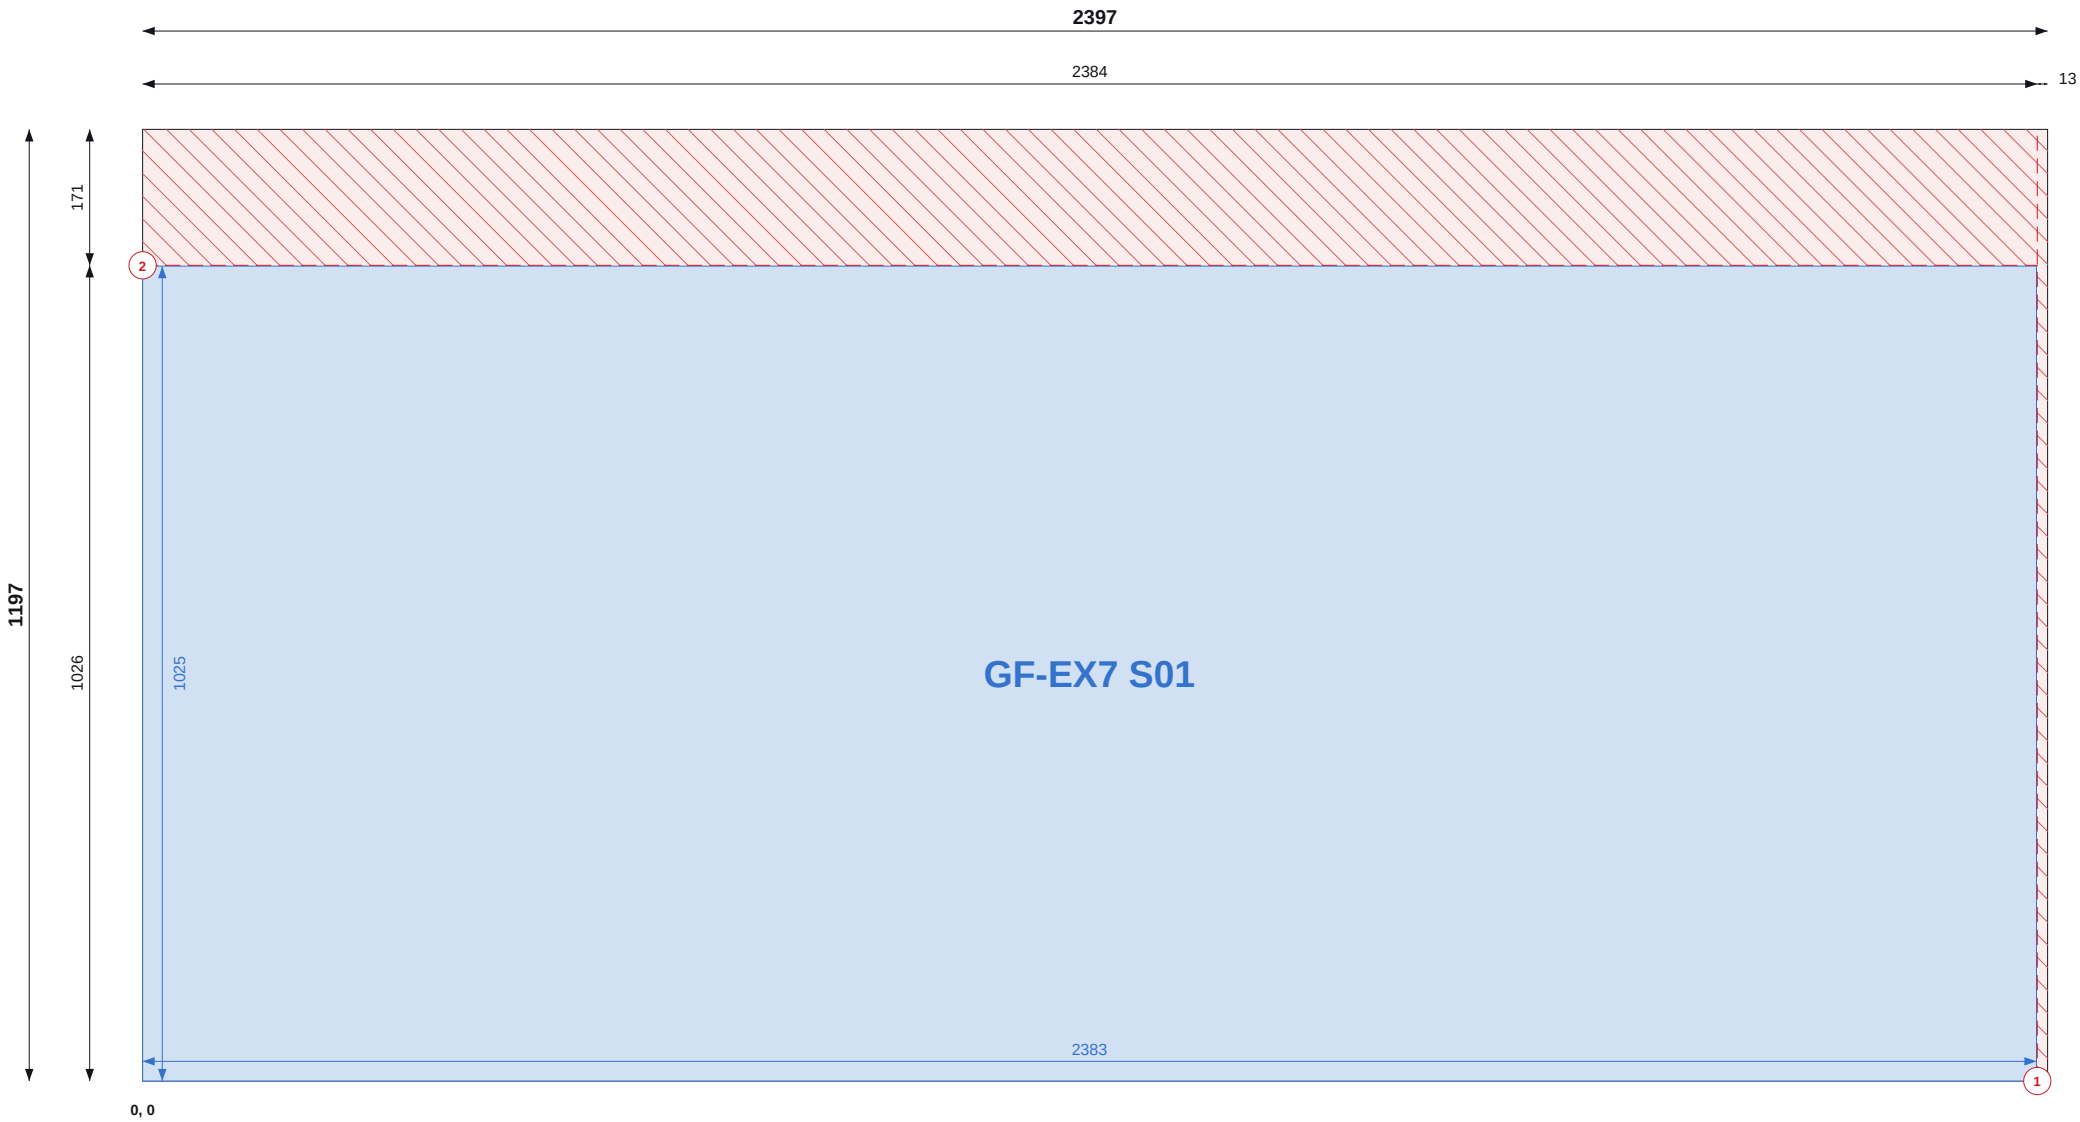

Top / left chains = saw cut positions (to cut centres). Coloured = part size and position.

SHEET 11 OF 38

THIS SHEET

Item	Value
Parts	1
Used / waste	85.1% / 0.43 m2
Reusable offcuts	0
Saw cuts / shared	2 / 0

PIECES (POSITION = BOTTOM-LEFT CORNER)

Label	Size	X, Y
GF-EX7 S01	1025 x 2383	0, 0

NOTES

- Cut from OSB/3 9mm 1197x2397, 2mm saw kerf. Viewed on the face; dimensions from the sheet's bottom-left corner (0,0). Red numbered lines = saw cuts in order, each edge to edge.
- Coloured dimensions belong to the part of that colour: its width and height, and its position from the sheet edges. Raked parts: corner coordinates at each corner.
- Red hatch = waste. Labels = panel + piece mark on the manufacture drawing.

REVISIONS

REV	DATE	DESCRIPTION
C01	13.09.26	Construction issue



TLS TIMBER FRAME

Design & Manufacture

Scan: 3D model + drawings




CLIENT	PROJECT
MP Adams	MP Adams Plot 3, Eckington

DRAWING TITLE			
OSB CUTTING - GROUND FLOOR - SHEET 11 OF 38			
OSB/3 9mm 1197x2397 Ground Floor			

SCALE	SIZE	DATE	DRAWN
NTS	A3	13.09.26	TS

STATUS	DRAWING No.	REV
CONSTRUCTION	P3-CP-OSB-01 / 11	C01

Do not scale. All dimensions in mm. Check all dimensions on site.

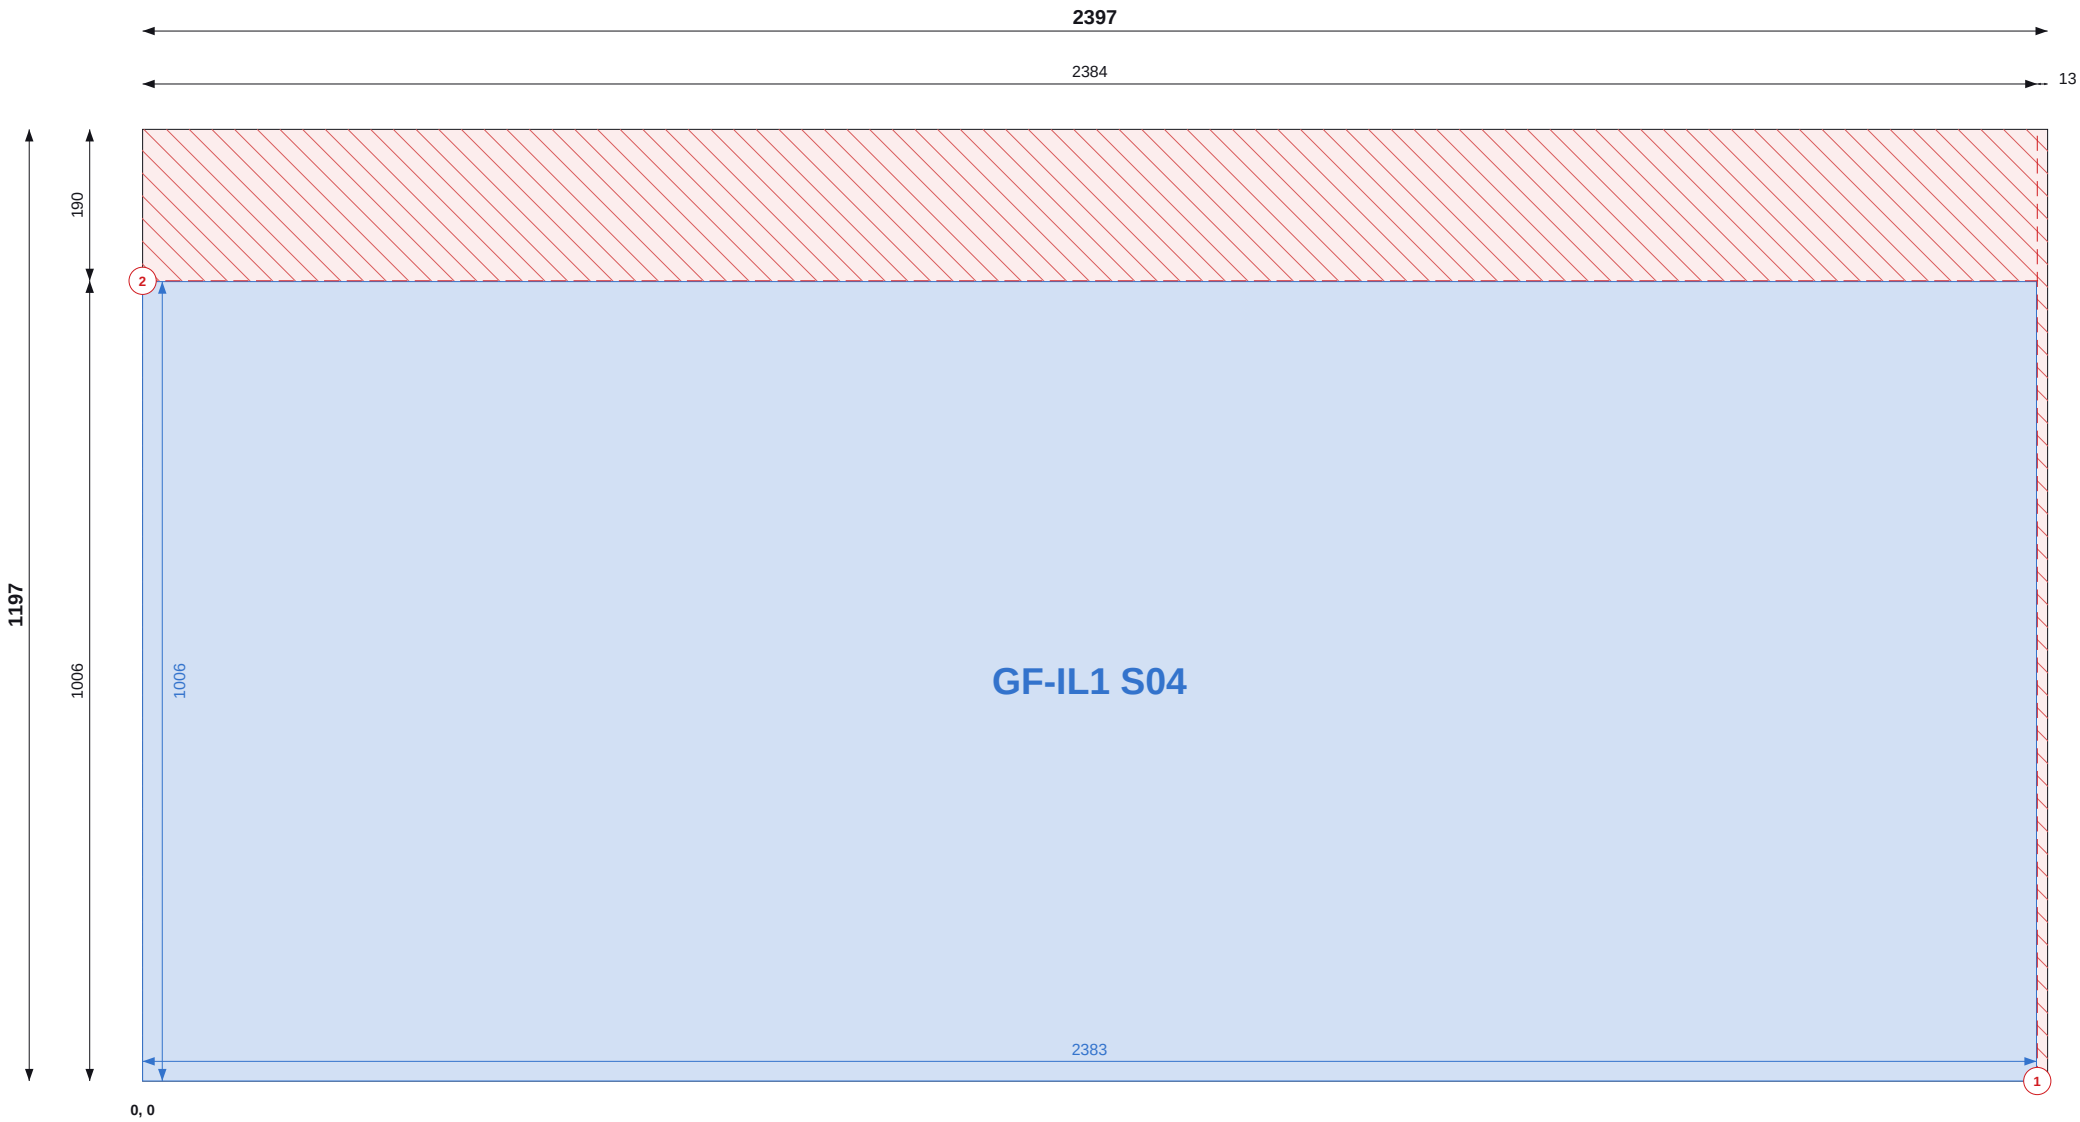

Top / left chains = saw cut positions (to cut centres). Coloured = part size and position.

SHEET 12 OF 38

THIS SHEET

Item	Value
Parts	1
Used / waste	83.5% / 0.47 m2
Reusable offcuts	0
Saw cuts / shared	2 / 0

PIECES (POSITION = BOTTOM-LEFT CORNER)

Label	Size	X, Y
GF-IL1 S04	1006 x 2383	0, 0

NOTES

- Cut from OSB/3 9mm 1197x2397, 2mm saw kerf. Viewed on the face; dimensions from the sheet's bottom-left corner (0,0). Red numbered lines = saw cuts in order, each edge to edge.
- Coloured dimensions belong to the part of that colour: its width and height, and its position from the sheet edges. Raked parts: corner coordinates at each corner.
- Red hatch = waste. Labels = panel + piece mark on the manufacture drawing.

REVISIONS

REV	DATE	DESCRIPTION
C01	13.09.26	Construction issue



TLS TIMBER FRAME

Design & Manufacture

Scan: 3D model + drawings



CLIENT	PROJECT
MP Adams	MP Adams Plot 3, Eckington


DRAWING TITLE
OSB CUTTING - GROUND FLOOR - SHEET 12 OF 38

OSB/3 9mm 1197x2397 | Ground Floor

SCALE	SIZE	DATE	DRAWN
NTS	A3	13.09.26	TS

STATUS	DRAWING No.	REV
CONSTRUCTION	P3-CP-OSB-01 / 12	C01

Do not scale. All dimensions in mm. Check all dimensions on site.

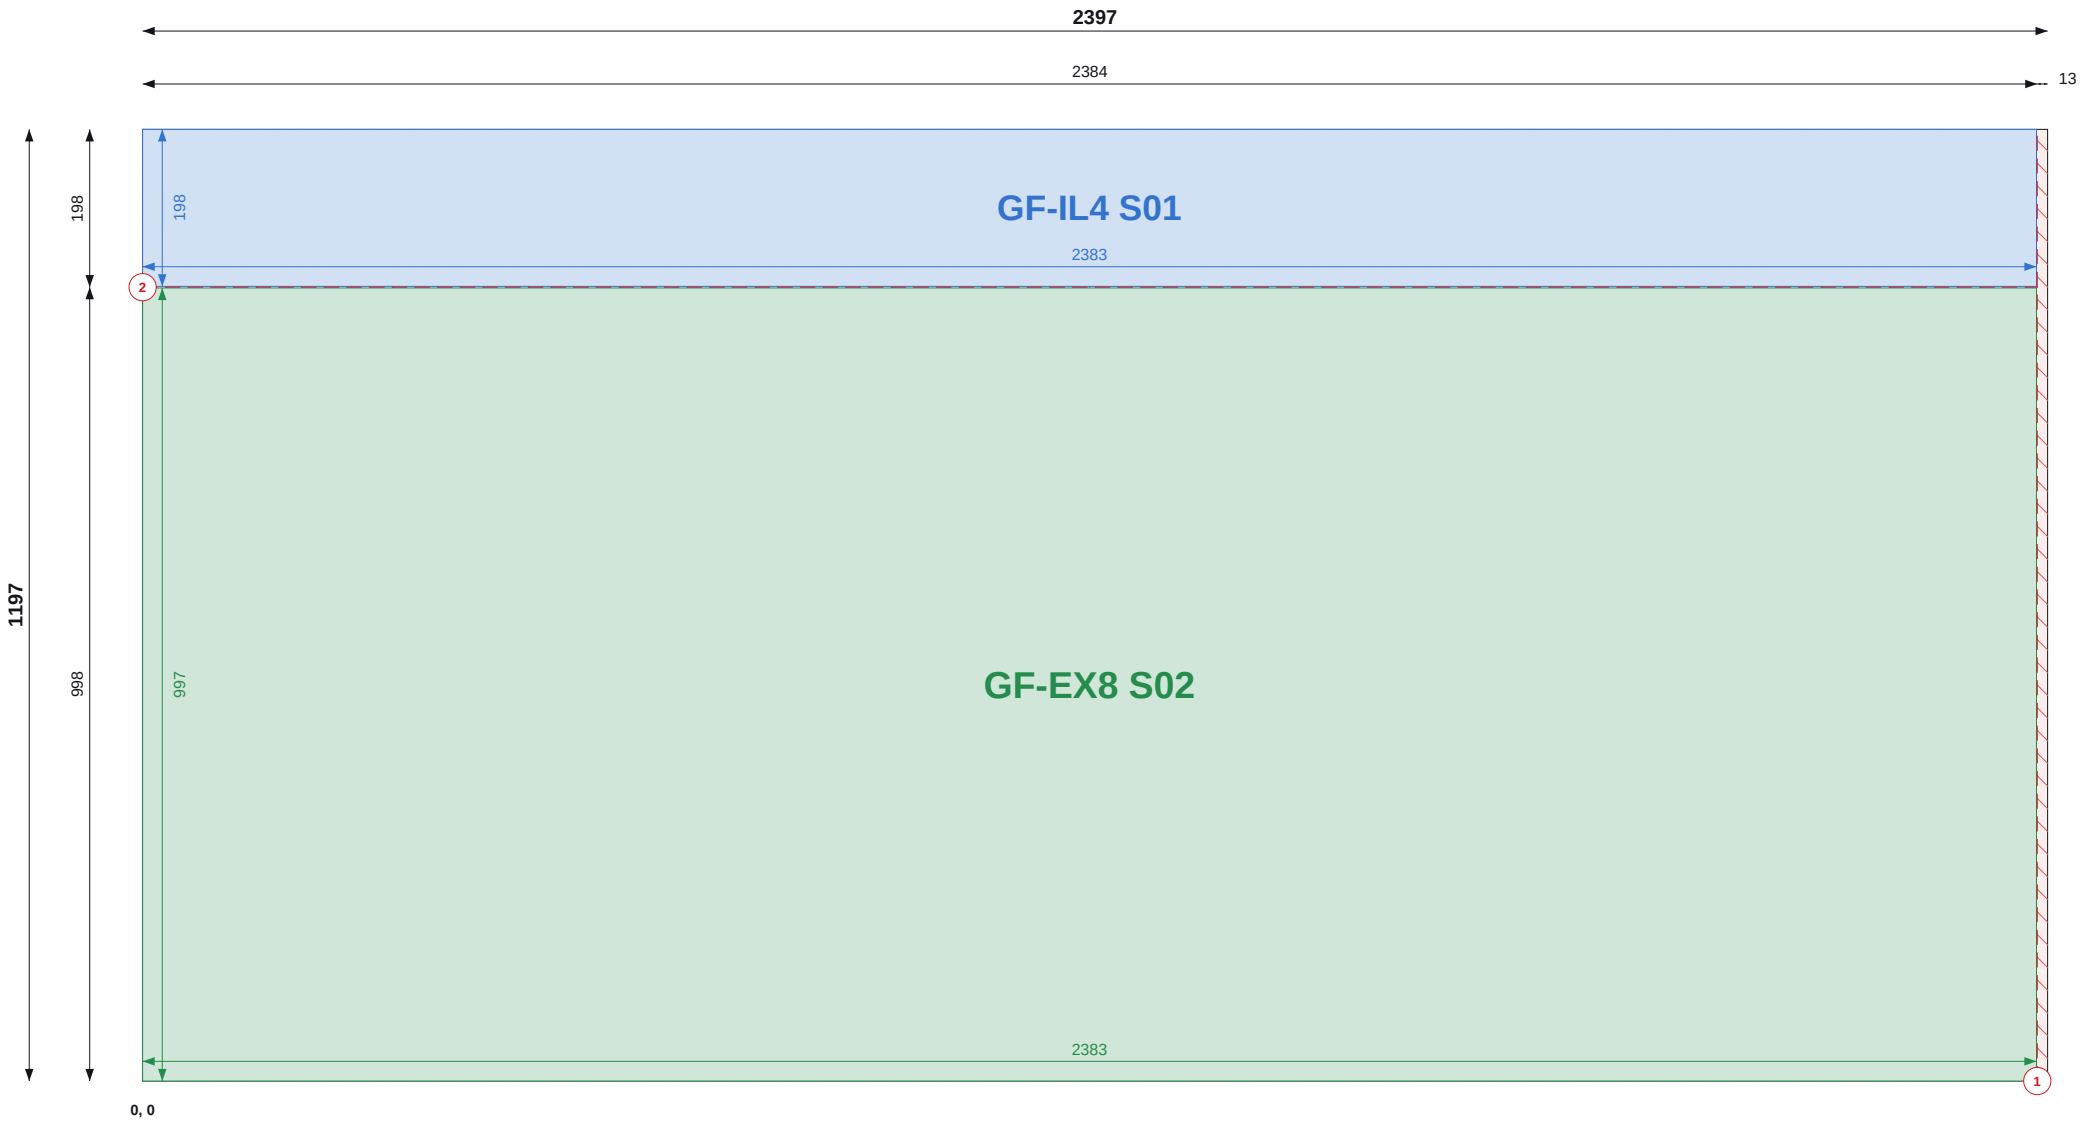

SHEET 13 OF 38

THIS SHEET

Item	Value
Parts	2
Used / waste	99.2% / 0.02 m2
Reusable offcuts	0
Saw cuts / shared	2 / 1

PIECES (POSITION = BOTTOM-LEFT CORNER)

Label	Size	X, Y
GF-IL4 S01	198 x 2383	0, 999
GF-EX8 S02	997 x 2383	0, 0

NOTES

- Cut from OSB/3 9mm 1197x2397, 2mm saw kerf. Viewed on the face; dimensions from the sheet's bottom-left corner (0,0). Red numbered lines = saw cuts in order, each edge to edge.
- Coloured dimensions belong to the part of that colour: its width and height, and its position from the sheet edges. Raked parts: corner coordinates at each corner.
- Red hatch = waste. Labels = panel + piece mark on the manufacture drawing.

REVISIONS

REV	DATE	DESCRIPTION
C01	13.09.26	Construction issue



TLS TIMBER FRAME

Design & Manufacture

Scan: 3D model + drawings




CLIENT	PROJECT
MP Adams	MP Adams Plot 3, Eckington

DRAWING TITLE			
OSB CUTTING - GROUND FLOOR - SHEET 13 OF 38			
OSB/3 9mm 1197x2397 Ground Floor			

SCALE	SIZE	DATE	DRAWN
NTS	A3	13.09.26	TS

STATUS	DRAWING No.	REV
CONSTRUCTION	P3-CP-OSB-01 / 13	C01

Do not scale. All dimensions in mm. Check all dimensions on site.

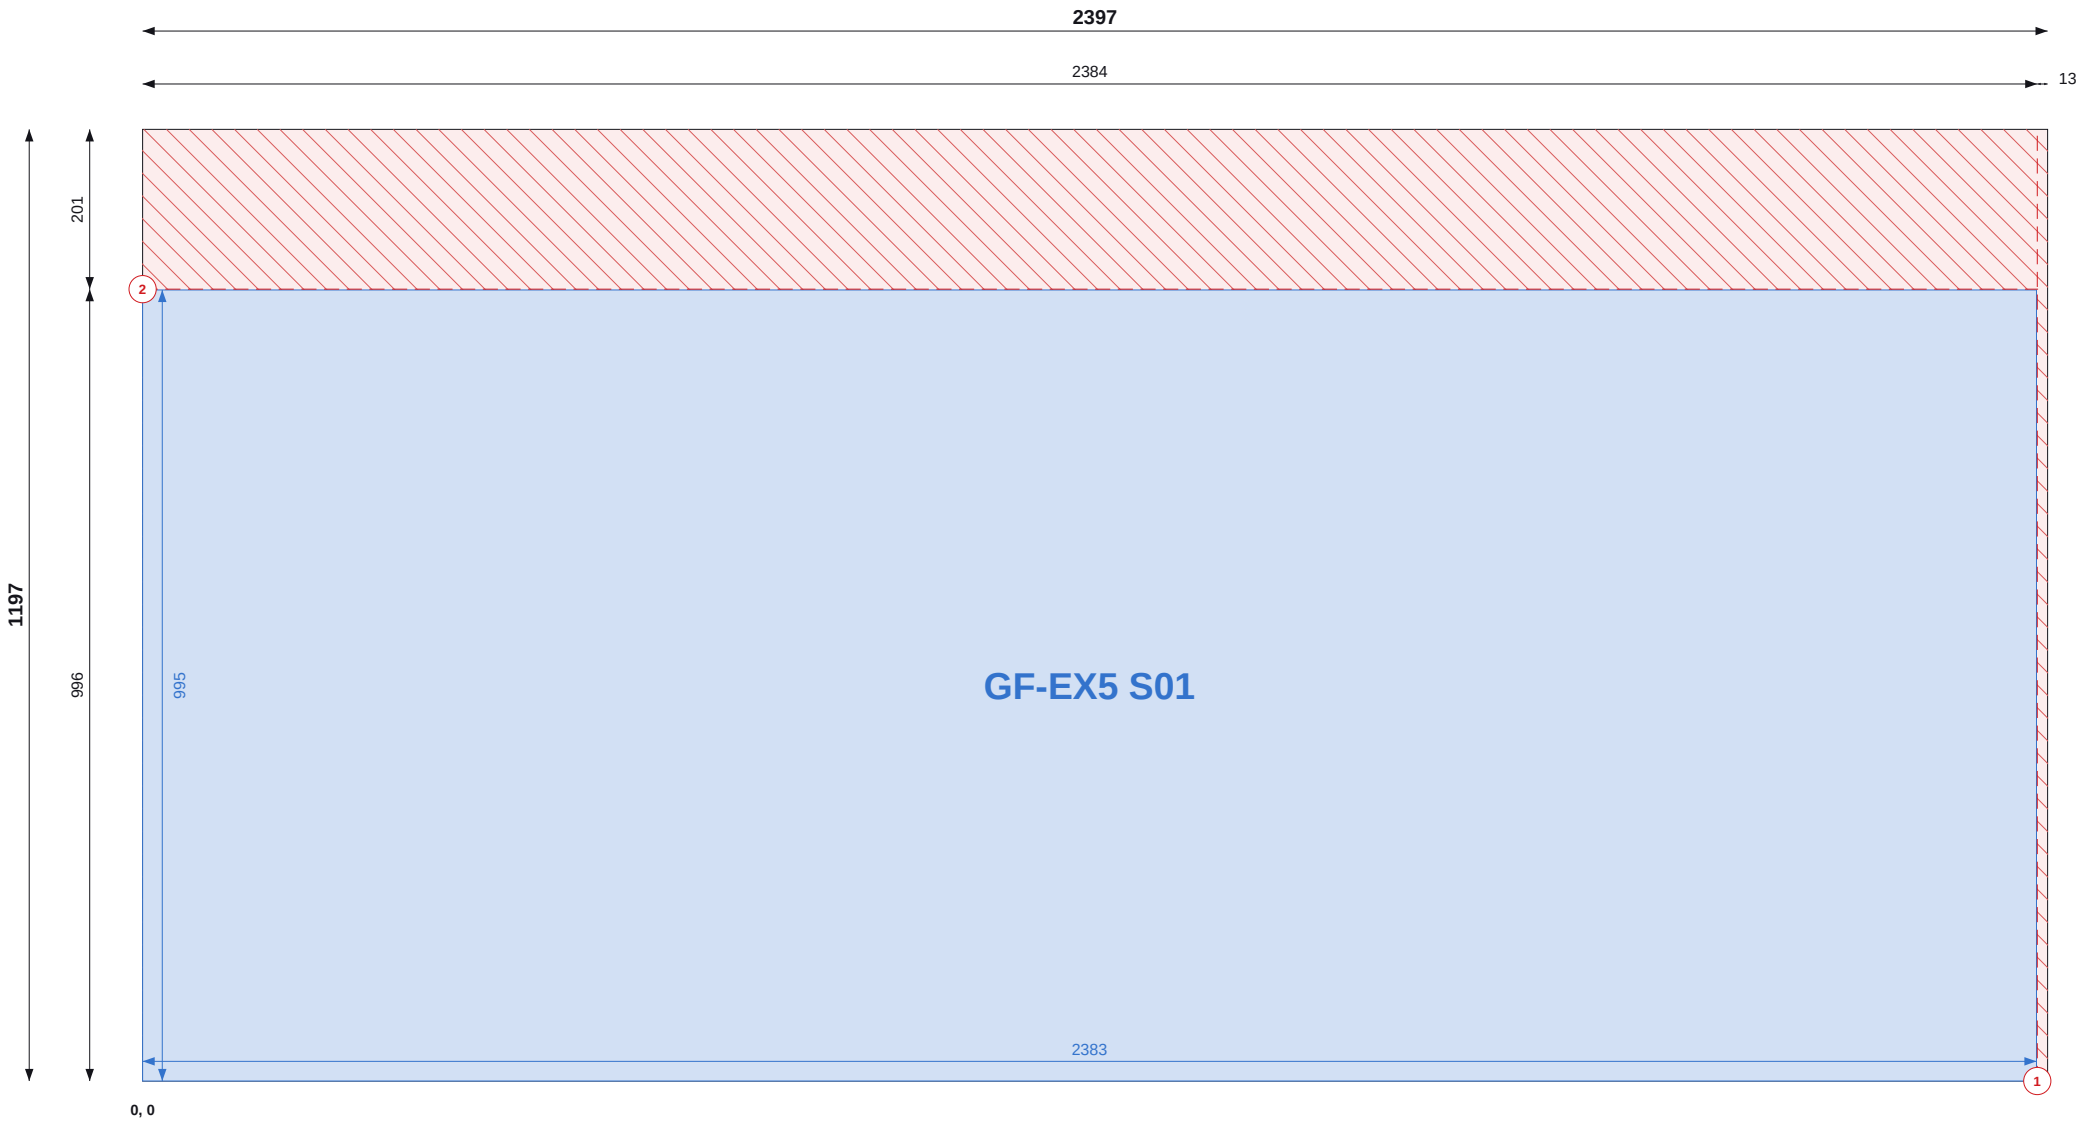

Top / left chains = saw cut positions (to cut centres). Coloured = part size and position.

SHEET 14 OF 38

THIS SHEET

Item	Value
Parts	1
Used / waste	82.6% / 0.50 m2
Reusable offcuts	0
Saw cuts / shared	2 / 0

PIECES (POSITION = BOTTOM-LEFT CORNER)

Label	Size	X, Y
GF-EX5 S01	995 x 2383	0, 0

NOTES

- Cut from OSB/3 9mm 1197x2397, 2mm saw kerf. Viewed on the face; dimensions from the sheet's bottom-left corner (0,0). Red numbered lines = saw cuts in order, each edge to edge.
- Coloured dimensions belong to the part of that colour: its width and height, and its position from the sheet edges. Raked parts: corner coordinates at each corner.
- Red hatch = waste. Labels = panel + piece mark on the manufacture drawing.

REVISIONS

REV	DATE	DESCRIPTION
C01	13.09.26	Construction issue



TLS TIMBER FRAME

Design & Manufacture

Scan: 3D model + drawings



CLIENT	PROJECT
MP Adams	MP Adams Plot 3, Eckington


DRAWING TITLE
OSB CUTTING - GROUND FLOOR - SHEET 14 OF 38

OSB/3 9mm 1197x2397 | Ground Floor

SCALE	SIZE	DATE	DRAWN
NTS	A3	13.09.26	TS

STATUS	DRAWING No.	REV
CONSTRUCTION	P3-CP-OSB-01 / 14	C01

Do not scale. All dimensions in mm. Check all dimensions on site.

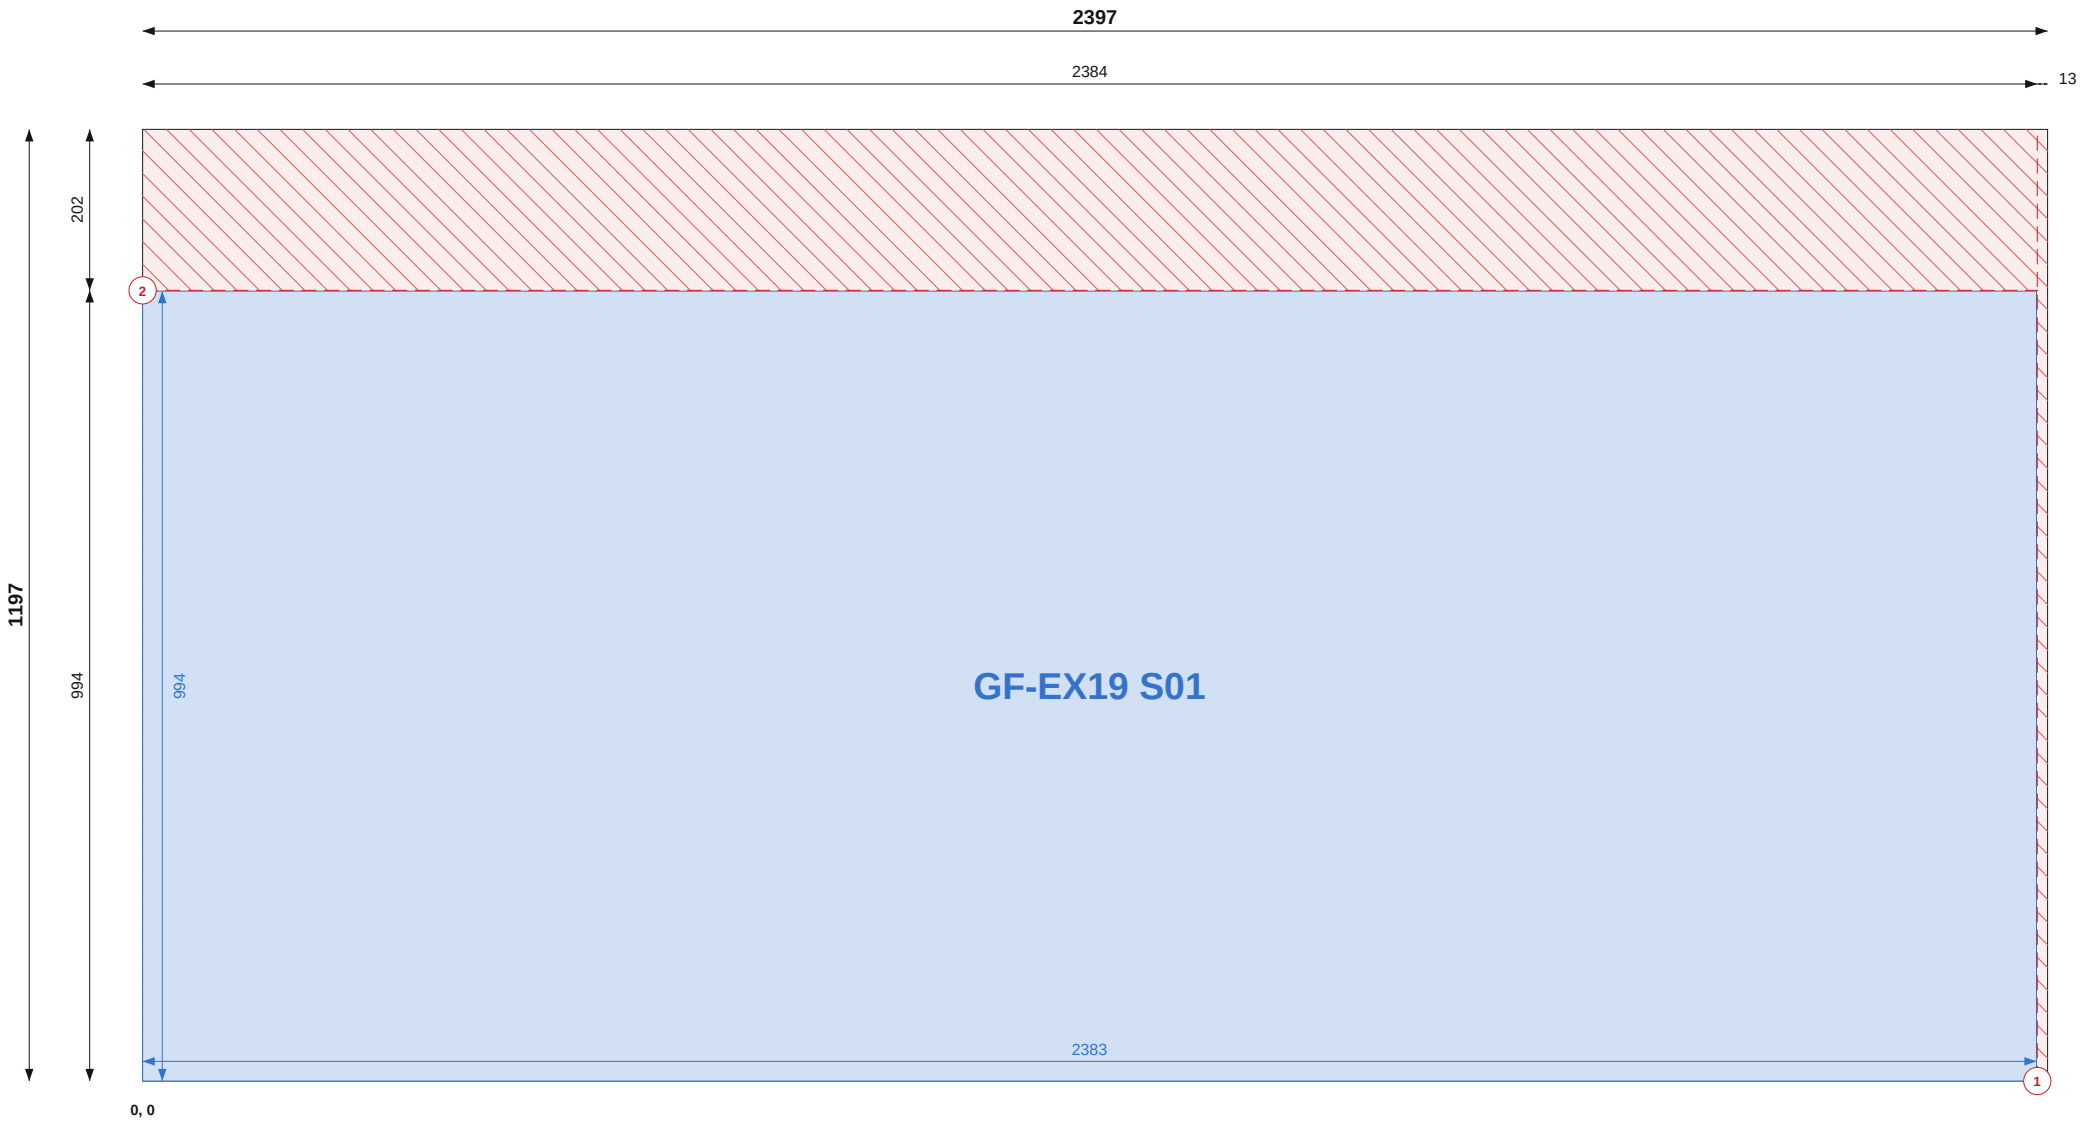

Top / left chains = saw cut positions (to cut centres). Coloured = part size and position.

SHEET 15 OF 38

THIS SHEET

Item	Value
Parts	1
Used / waste	82.5% / 0.50 m2
Reusable offcuts	0
Saw cuts / shared	2 / 0

PIECES (POSITION = BOTTOM-LEFT CORNER)

Label	Size	X, Y
GF-EX19 S01	994 x 2383	0, 0

NOTES

- Cut from OSB/3 9mm 1197x2397, 2mm saw kerf. Viewed on the face; dimensions from the sheet's bottom-left corner (0,0). Red numbered lines = saw cuts in order, each edge to edge.
- Coloured dimensions belong to the part of that colour: its width and height, and its position from the sheet edges. Raked parts: corner coordinates at each corner.
- Red hatch = waste. Labels = panel + piece mark on the manufacture drawing.

REVISIONS

REV	DATE	DESCRIPTION
C01	13.09.26	Construction issue



TLS TIMBER FRAME

Design & Manufacture

Scan: 3D model + drawings



CLIENT	PROJECT
MP Adams	MP Adams Plot 3, Eckington


DRAWING TITLE
OSB CUTTING - GROUND FLOOR - SHEET 15 OF 38

OSB/3 9mm 1197x2397 | Ground Floor

SCALE	SIZE	DATE	DRAWN
NTS	A3	13.09.26	TS

STATUS	DRAWING No.	REV
CONSTRUCTION	P3-CP-OSB-01 / 15	C01

Do not scale. All dimensions in mm. Check all dimensions on site.

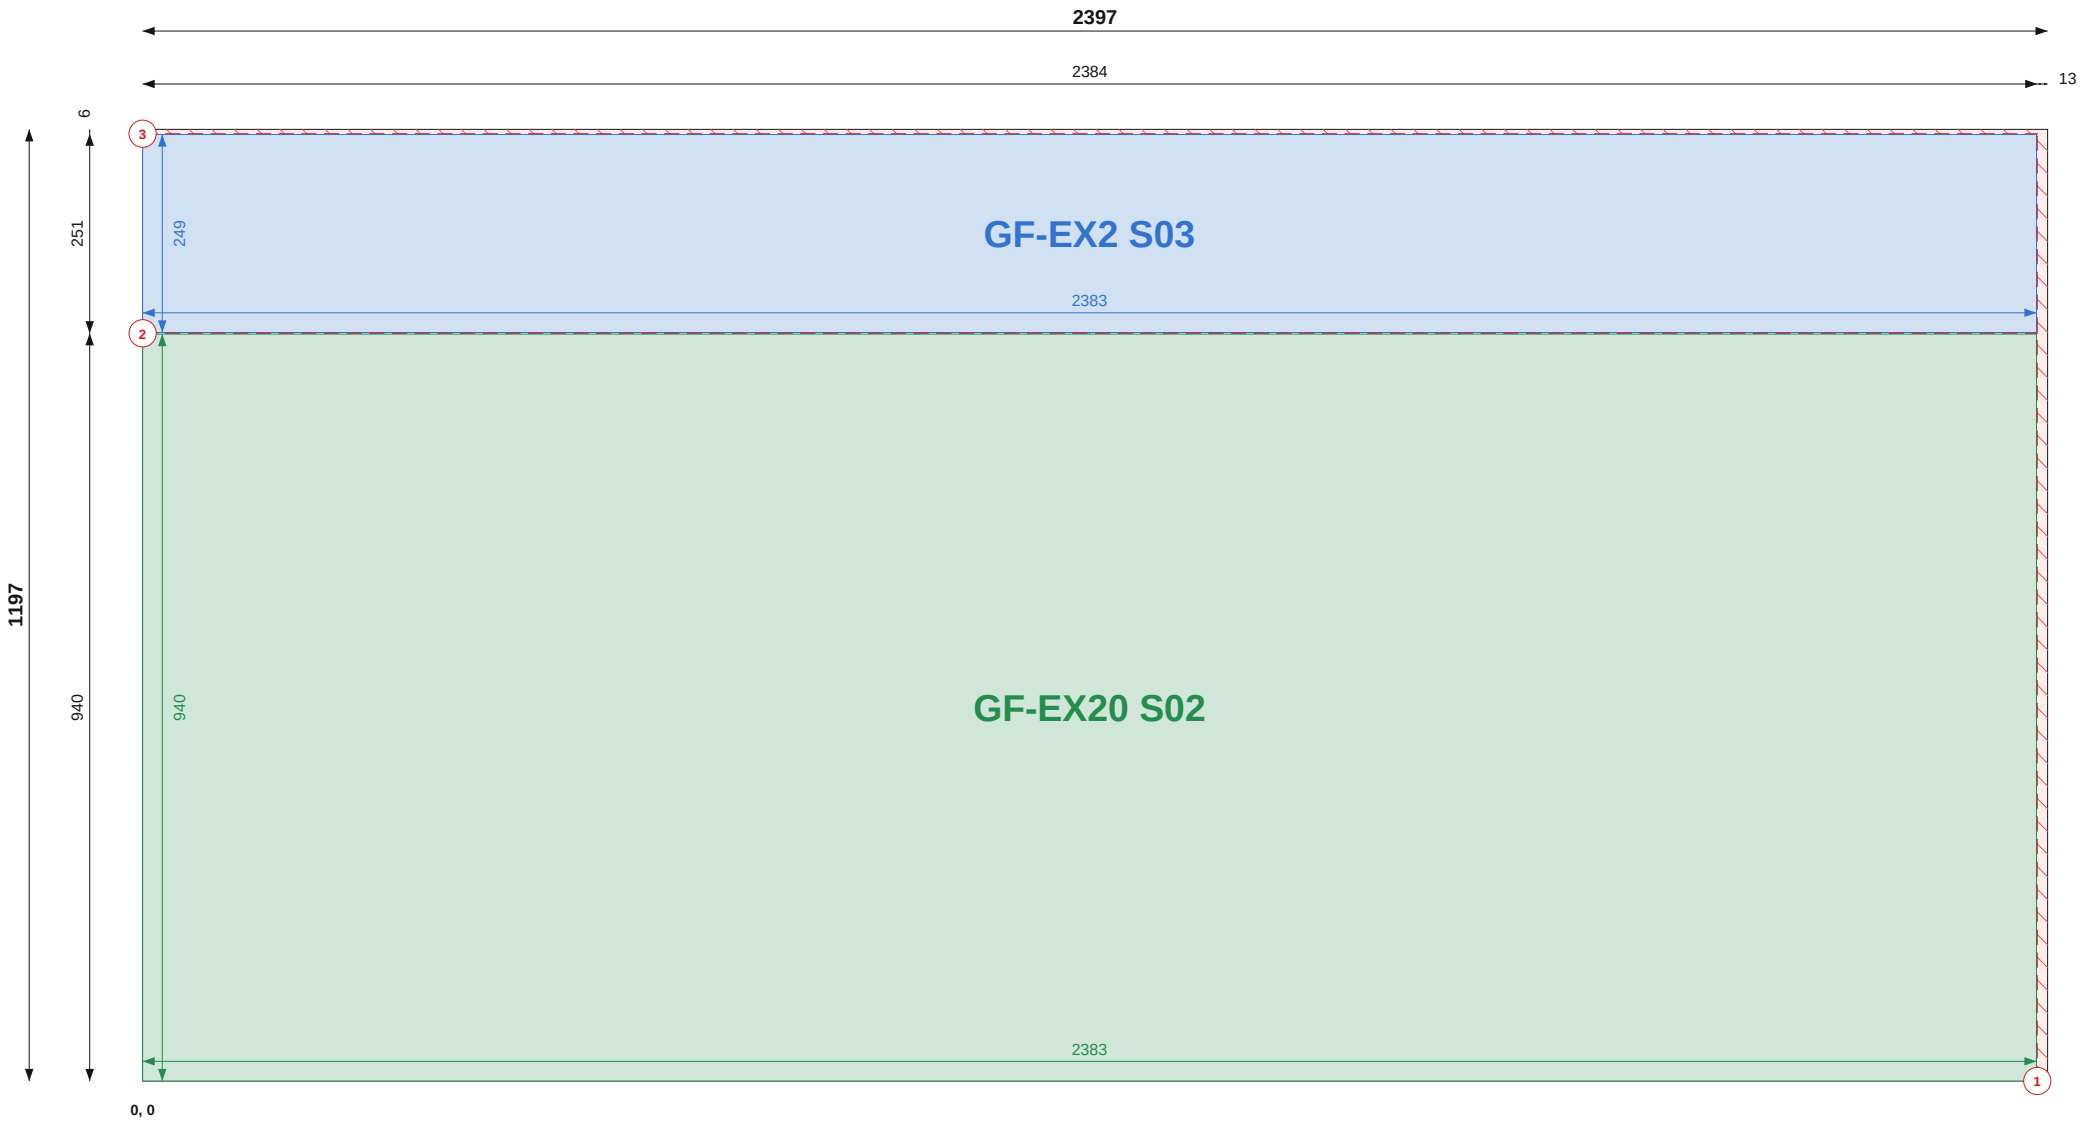

Top / left chains = saw cut positions (to cut centres). Coloured = part size and position.

SHEET 16 OF 38

THIS SHEET

Item	Value
Parts	2
Used / waste	98.7% / 0.04 m2
Reusable offcuts	0
Saw cuts / shared	3 / 1

PIECES (POSITION = BOTTOM-LEFT CORNER)

Label	Size	X, Y
GF-EX2 S03	249 x 2383	0, 942
GF-EX20 S02	940 x 2383	0, 0

NOTES

- Cut from OSB/3 9mm 1197x2397, 2mm saw kerf. Viewed on the face; dimensions from the sheet's bottom-left corner (0,0). Red numbered lines = saw cuts in order, each edge to edge.
- Coloured dimensions belong to the part of that colour: its width and height, and its position from the sheet edges. Raked parts: corner coordinates at each corner.
- Red hatch = waste. Labels = panel + piece mark on the manufacture drawing.

REVISIONS

REV	DATE	DESCRIPTION
C01	13.09.26	Construction issue



TLS TIMBER FRAME

Design & Manufacture

Scan: 3D model + drawings




CLIENT	PROJECT
MP Adams	MP Adams Plot 3, Eckington

DRAWING TITLE			
OSB CUTTING - GROUND FLOOR - SHEET 16 OF 38			
OSB/3 9mm 1197x2397 Ground Floor			

SCALE	SIZE	DATE	DRAWN
NTS	A3	13.09.26	TS

STATUS	DRAWING No.	REV
CONSTRUCTION	P3-CP-OSB-01 / 16	C01

Do not scale. All dimensions in mm. Check all dimensions on site.

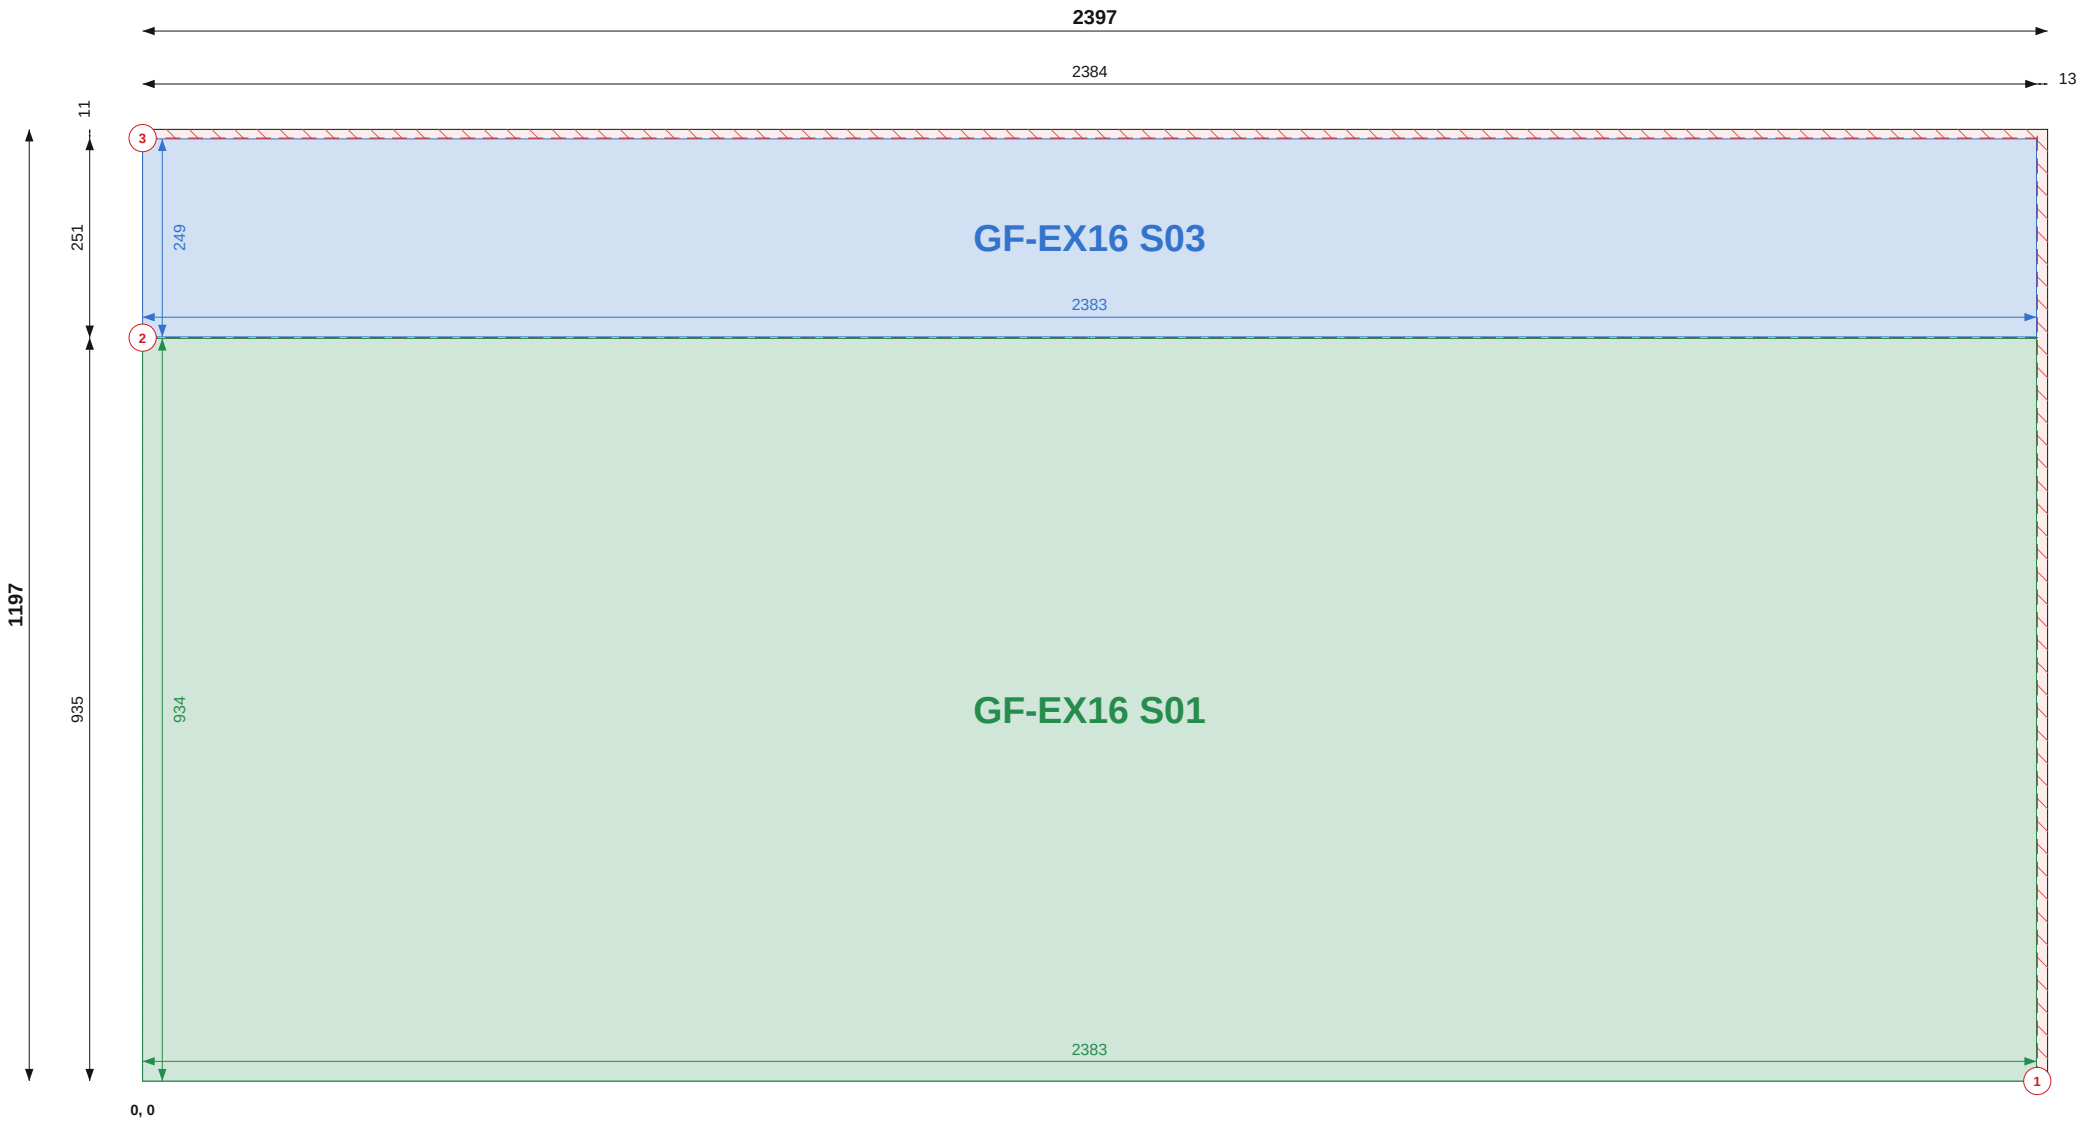

Top / left chains = saw cut positions (to cut centres). Coloured = part size and position.

SHEET 17 OF 38

THIS SHEET

Item	Value
Parts	2
Used / waste	98.3% / 0.05 m2
Reusable offcuts	0
Saw cuts / shared	3 / 1

PIECES (POSITION = BOTTOM-LEFT CORNER)

Label	Size	X, Y
GF-EX16 S03	249 x 2383	0, 936
GF-EX16 S01	934 x 2383	0, 0

NOTES

- Cut from OSB/3 9mm 1197x2397, 2mm saw kerf. Viewed on the face; dimensions from the sheet's bottom-left corner (0,0). Red numbered lines = saw cuts in order, each edge to edge.
- Coloured dimensions belong to the part of that colour: its width and height, and its position from the sheet edges. Raked parts: corner coordinates at each corner.
- Red hatch = waste. Labels = panel + piece mark on the manufacture drawing.

REVISIONS

REV	DATE	DESCRIPTION
C01	13.09.26	Construction issue



TLS TIMBER FRAME

Design & Manufacture

Scan: 3D model + drawings



CLIENT	PROJECT
MP Adams	MP Adams Plot 3, Eckington


DRAWING TITLE
OSB CUTTING - GROUND FLOOR - SHEET 17 OF 38

OSB/3 9mm 1197x2397 | Ground Floor

SCALE	SIZE	DATE	DRAWN
NTS	A3	13.09.26	TS

STATUS	DRAWING No.	REV
CONSTRUCTION	P3-CP-OSB-01 / 17	C01

Do not scale. All dimensions in mm. Check all dimensions on site.

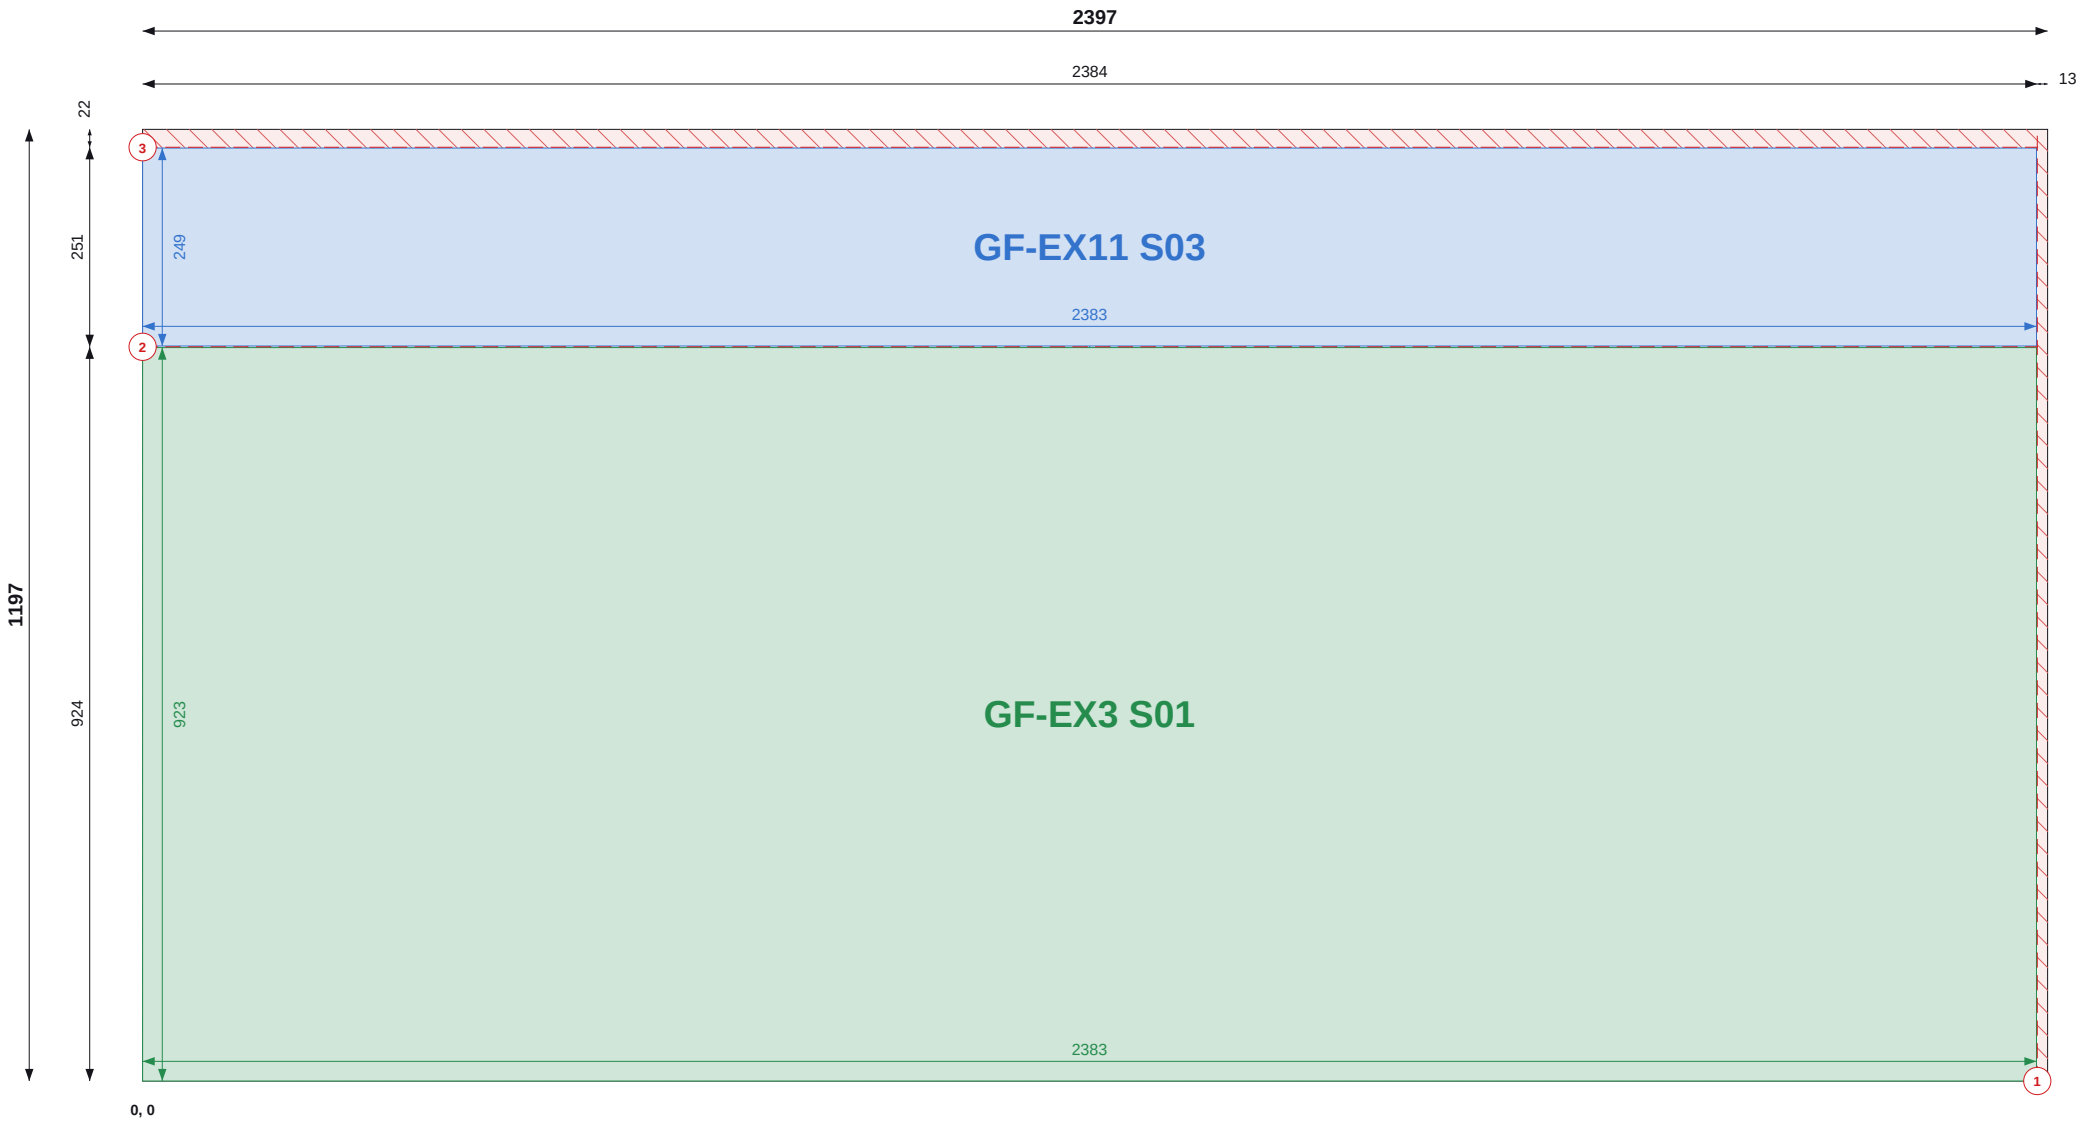

Top / left chains = saw cut positions (to cut centres). Coloured = part size and position.

SHEET 18 OF 38

THIS SHEET

Item	Value
Parts	2
Used / waste	97.3% / 0.08 m2
Reusable offcuts	0
Saw cuts / shared	3 / 1

PIECES (POSITION = BOTTOM-LEFT CORNER)

Label	Size	X, Y
GF-EX11 S03	249 x 2383	0, 925
GF-EX3 S01	923 x 2383	0, 0

NOTES

- Cut from OSB/3 9mm 1197x2397, 2mm saw kerf. Viewed on the face; dimensions from the sheet's bottom-left corner (0,0). Red numbered lines = saw cuts in order, each edge to edge.
- Coloured dimensions belong to the part of that colour: its width and height, and its position from the sheet edges. Raked parts: corner coordinates at each corner.
- Red hatch = waste. Labels = panel + piece mark on the manufacture drawing.

REVISIONS

REV	DATE	DESCRIPTION
C01	13.09.26	Construction issue



TLS TIMBER FRAME

Design & Manufacture

Scan: 3D model + drawings



CLIENT	PROJECT
MP Adams	MP Adams Plot 3, Eckington


DRAWING TITLE
OSB CUTTING - GROUND FLOOR - SHEET 18 OF 38

OSB/3 9mm 1197x2397 | Ground Floor

SCALE	SIZE	DATE	DRAWN
NTS	A3	13.09.26	TS

STATUS	DRAWING No.	REV
CONSTRUCTION	P3-CP-OSB-01 / 18	C01

Do not scale. All dimensions in mm. Check all dimensions on site.

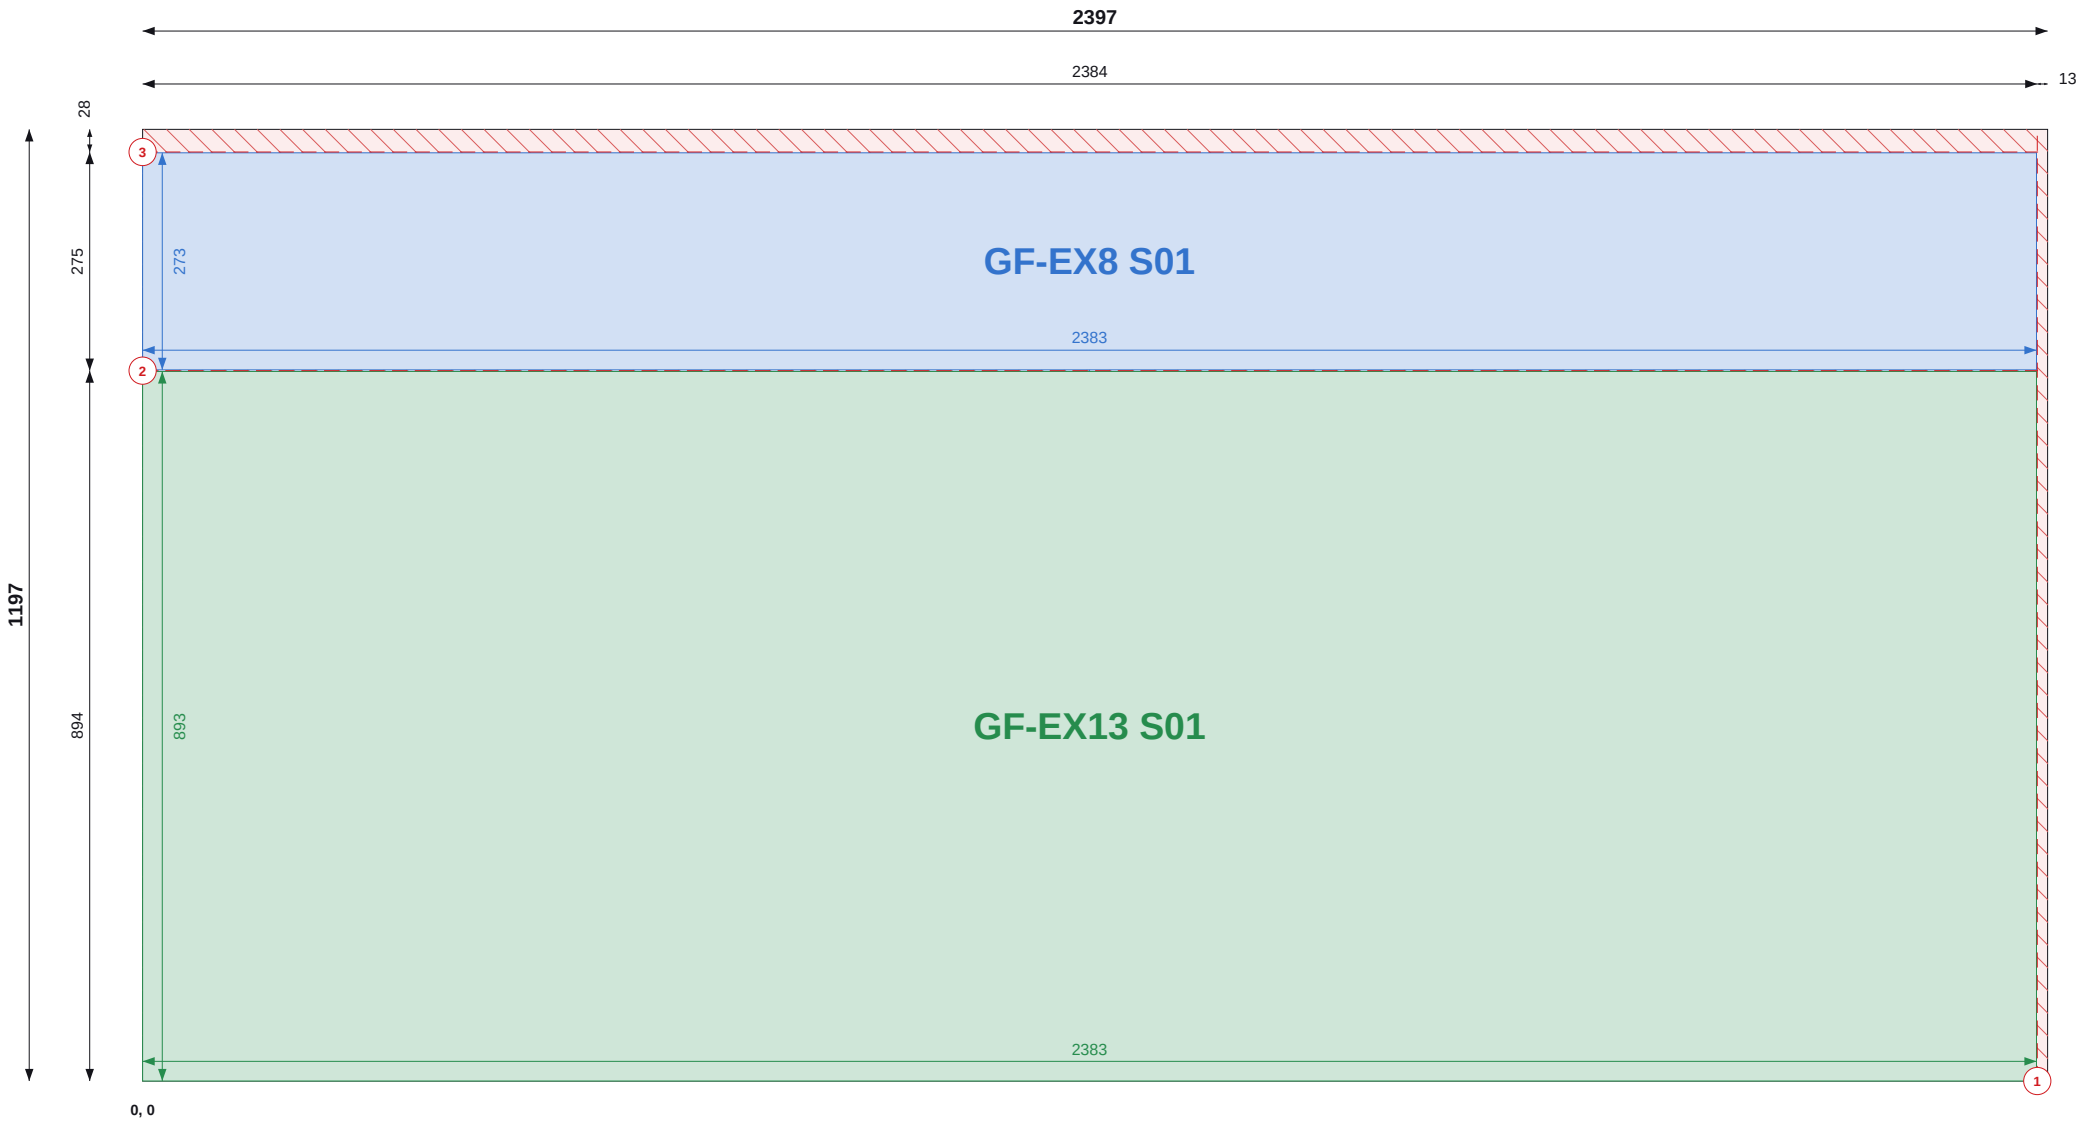

Top / left chains = saw cut positions (to cut centres). Coloured = part size and position.

SHEET 19 OF 38

THIS SHEET

Item	Value
Parts	2
Used / waste	96.8% / 0.09 m2
Reusable offcuts	0
Saw cuts / shared	3 / 1

PIECES (POSITION = BOTTOM-LEFT CORNER)

Label	Size	X, Y
GF-EX8 S01	273 x 2383	0, 895
GF-EX13 S01	893 x 2383	0, 0

NOTES

- Cut from OSB/3 9mm 1197x2397, 2mm saw kerf. Viewed on the face; dimensions from the sheet's bottom-left corner (0,0). Red numbered lines = saw cuts in order, each edge to edge.
- Coloured dimensions belong to the part of that colour: its width and height, and its position from the sheet edges. Raked parts: corner coordinates at each corner.
- Red hatch = waste. Labels = panel + piece mark on the manufacture drawing.

REVISIONS

REV	DATE	DESCRIPTION
C01	13.09.26	Construction issue



TLS TIMBER FRAME

Design & Manufacture

Scan: 3D model + drawings



CLIENT	PROJECT
MP Adams	MP Adams Plot 3, Eckington


DRAWING TITLE
OSB CUTTING - GROUND FLOOR - SHEET 19 OF 38

OSB/3 9mm 1197x2397 | Ground Floor

SCALE	SIZE	DATE	DRAWN
NTS	A3	13.09.26	TS

STATUS	DRAWING No.	REV
CONSTRUCTION	P3-CP-OSB-01 / 19	C01

Do not scale. All dimensions in mm. Check all dimensions on site.

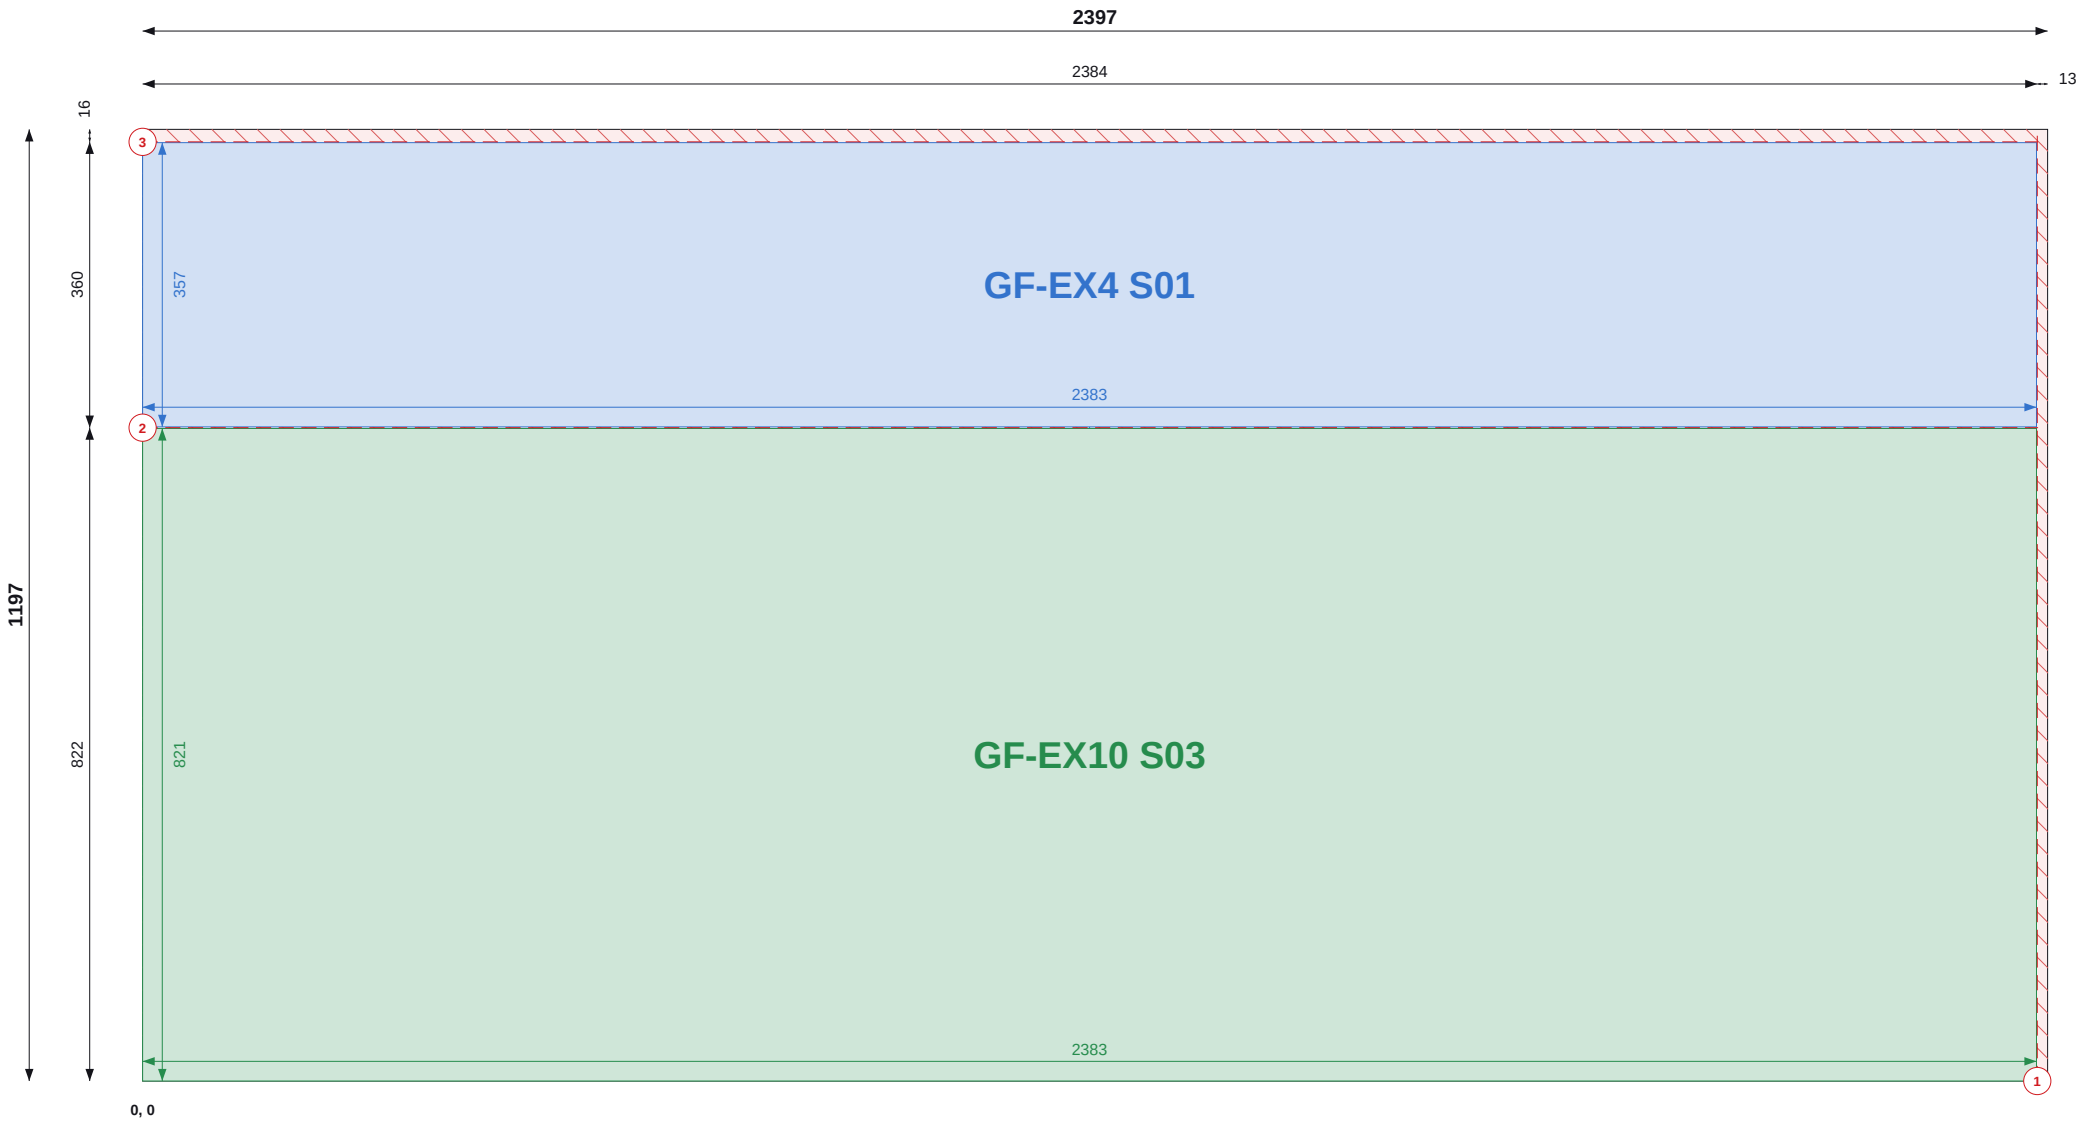

Top / left chains = saw cut positions (to cut centres). Coloured = part size and position.

SHEET 20 OF 38

THIS SHEET

Item	Value
Parts	2
Used / waste	97.9% / 0.06 m2
Reusable offcuts	0
Saw cuts / shared	3 / 1

PIECES (POSITION = BOTTOM-LEFT CORNER)

Label	Size	X, Y
GF-EX4 S01	357 x 2383	0, 823
GF-EX10 S03	821 x 2383	0, 0

NOTES

- Cut from OSB/3 9mm 1197x2397, 2mm saw kerf. Viewed on the face; dimensions from the sheet's bottom-left corner (0,0). Red numbered lines = saw cuts in order, each edge to edge.
- Coloured dimensions belong to the part of that colour: its width and height, and its position from the sheet edges. Raked parts: corner coordinates at each corner.
- Red hatch = waste. Labels = panel + piece mark on the manufacture drawing.

REVISIONS

REV	DATE	DESCRIPTION
C01	13.09.26	Construction issue



TLS TIMBER FRAME

Design & Manufacture

Scan: 3D model + drawings



CLIENT MP Adams	PROJECT MP Adams Plot 3, Eckington
--------------------	---------------------------------------


DRAWING TITLE OSB CUTTING - GROUND FLOOR - SHEET 20 OF 38

OSB/3 9mm 1197x2397 | Ground Floor

SCALE NTS	SIZE A3	DATE 13.09.26	DRAWN TS
--------------	------------	------------------	-------------

STATUS CONSTRUCTION	DRAWING No. P3-CP-OSB-01 / 20	REV C01
-------------------------------	---	-------------------

Do not scale. All dimensions in mm. Check all dimensions on site.

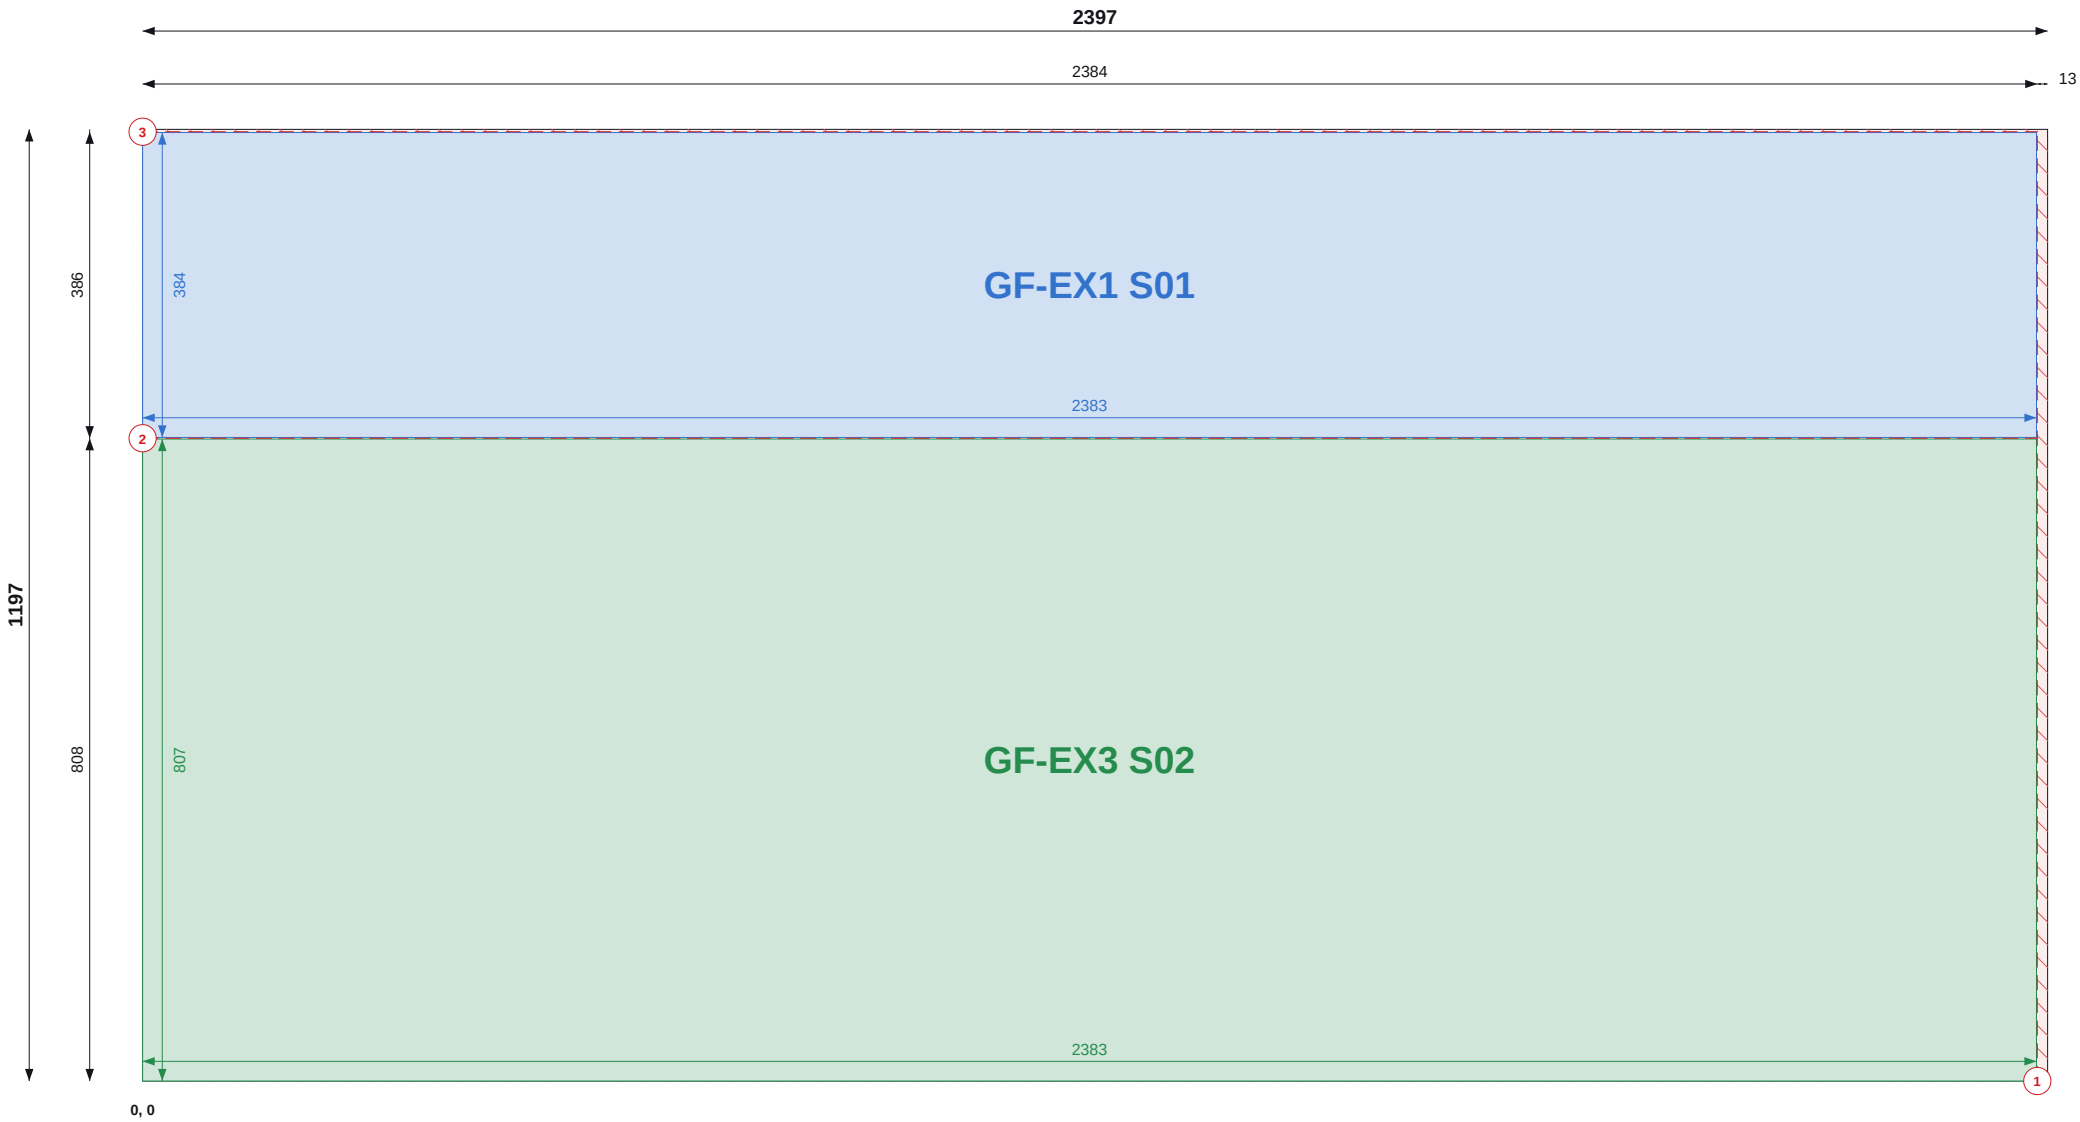

Top / left chains = saw cut positions (to cut centres). Coloured = part size and position.

SHEET 21 OF 38

THIS SHEET

Item	Value
Parts	2
Used / waste	98.9% / 0.03 m2
Reusable offcuts	0
Saw cuts / shared	3 / 1

PIECES (POSITION = BOTTOM-LEFT CORNER)

Label	Size	X, Y
GF-EX1 S01	384 x 2383	0, 809
GF-EX3 S02	807 x 2383	0, 0

NOTES

- Cut from OSB/3 9mm 1197x2397, 2mm saw kerf. Viewed on the face; dimensions from the sheet's bottom-left corner (0,0). Red numbered lines = saw cuts in order, each edge to edge.
- Coloured dimensions belong to the part of that colour: its width and height, and its position from the sheet edges. Raked parts: corner coordinates at each corner.
- Red hatch = waste. Labels = panel + piece mark on the manufacture drawing.

REVISIONS

REV	DATE	DESCRIPTION
C01	13.09.26	Construction issue



TLS TIMBER FRAME

Design & Manufacture

Scan: 3D model + drawings



CLIENT	PROJECT
MP Adams	MP Adams Plot 3, Eckington

DRAWING TITLE
OSB CUTTING - GROUND FLOOR - SHEET 21 OF 38

OSB/3 9mm 1197x2397 | Ground Floor

SCALE	SIZE	DATE	DRAWN
NTS	A3	13.09.26	TS

STATUS	DRAWING No.	REV
CONSTRUCTION	P3-CP-OSB-01 / 21	C01

Do not scale. All dimensions in mm. Check all dimensions on site.



Top / left chains = saw cut positions (to cut centres). Coloured = part size and position.

SHEET 22 OF 38

THIS SHEET

Item	Value
Parts	2
Used / waste	99.2% / 0.02 m2
Reusable offcuts	0
Saw cuts / shared	2 / 1

PIECES (POSITION = BOTTOM-LEFT CORNER)

Label	Size	X, Y
GF-IL2 S03	408 x 2383	0, 789
GF-IL2 S01	787 x 2383	0, 0

NOTES

- Cut from OSB/3 9mm 1197x2397, 2mm saw kerf. Viewed on the face; dimensions from the sheet's bottom-left corner (0,0). Red numbered lines = saw cuts in order, each edge to edge.
- Coloured dimensions belong to the part of that colour: its width and height, and its position from the sheet edges. Raked parts: corner coordinates at each corner.
- Red hatch = waste. Labels = panel + piece mark on the manufacture drawing.

REVISIONS

REV	DATE	DESCRIPTION
C01	13.09.26	Construction issue



TLS TIMBER FRAME

Design & Manufacture

Scan: 3D model + drawings




CLIENT	PROJECT
MP Adams	MP Adams Plot 3, Eckington

DRAWING TITLE			
OSB CUTTING - GROUND FLOOR - SHEET 22 OF 38			
OSB/3 9mm 1197x2397 Ground Floor			

SCALE	SIZE	DATE	DRAWN
NTS	A3	13.09.26	TS

STATUS	DRAWING No.	REV
CONSTRUCTION	P3-CP-OSB-01 / 22	C01

Do not scale. All dimensions in mm. Check all dimensions on site.

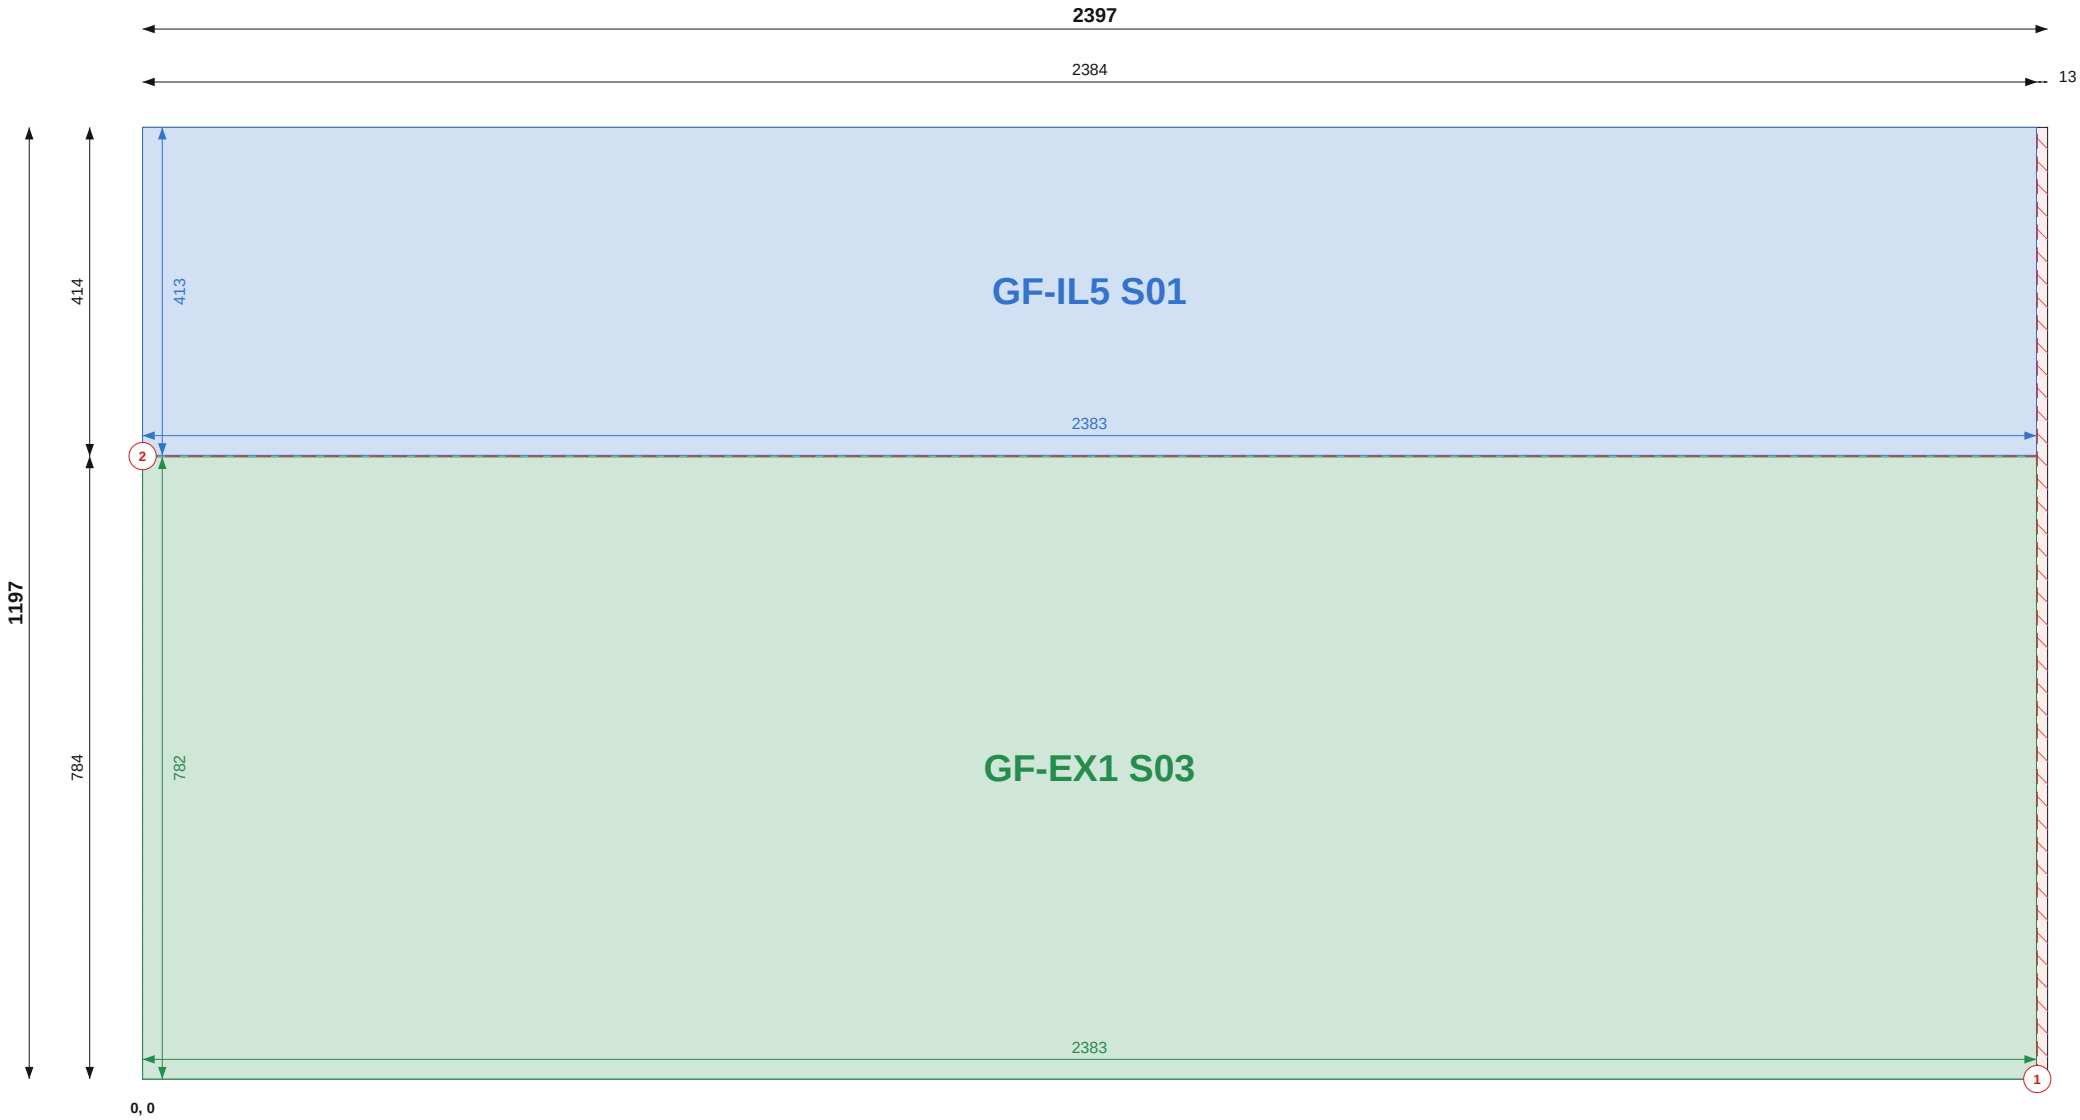

Top / left chains = saw cut positions (to cut centres). Coloured = part size and position.

SHEET 23 OF 38

THIS SHEET

Item	Value
Parts	2
Used / waste	99.2% / 0.02 m2
Reusable offcuts	0
Saw cuts / shared	2 / 1

PIECES (POSITION = BOTTOM-LEFT CORNER)

Label	Size	X, Y
GF-IL5 S01	413 x 2383	0, 784
GF-EX1 S03	782 x 2383	0, 0

NOTES

- Cut from OSB/3 9mm 1197x2397, 2mm saw kerf. Viewed on the face; dimensions from the sheet's bottom-left corner (0,0). Red numbered lines = saw cuts in order, each edge to edge.
- Coloured dimensions belong to the part of that colour: its width and height, and its position from the sheet edges. Raked parts: corner coordinates at each corner.
- Red hatch = waste. Labels = panel + piece mark on the manufacture drawing.

REVISIONS

REV	DATE	DESCRIPTION
C01	13.09.26	Construction issue



TLS TIMBER FRAME

Design & Manufacture

Scan: 3D model + drawings



CLIENT	PROJECT
MP Adams	MP Adams Plot 3, Eckington


DRAWING TITLE
OSB CUTTING - GROUND FLOOR - SHEET 23 OF 38

OSB/3 9mm 1197x2397 | Ground Floor

SCALE	SIZE	DATE	DRAWN
NTS	A3	13.09.26	TS

STATUS	DRAWING No.	REV
CONSTRUCTION	P3-CP-OSB-01 / 23	C01

Do not scale. All dimensions in mm. Check all dimensions on site.

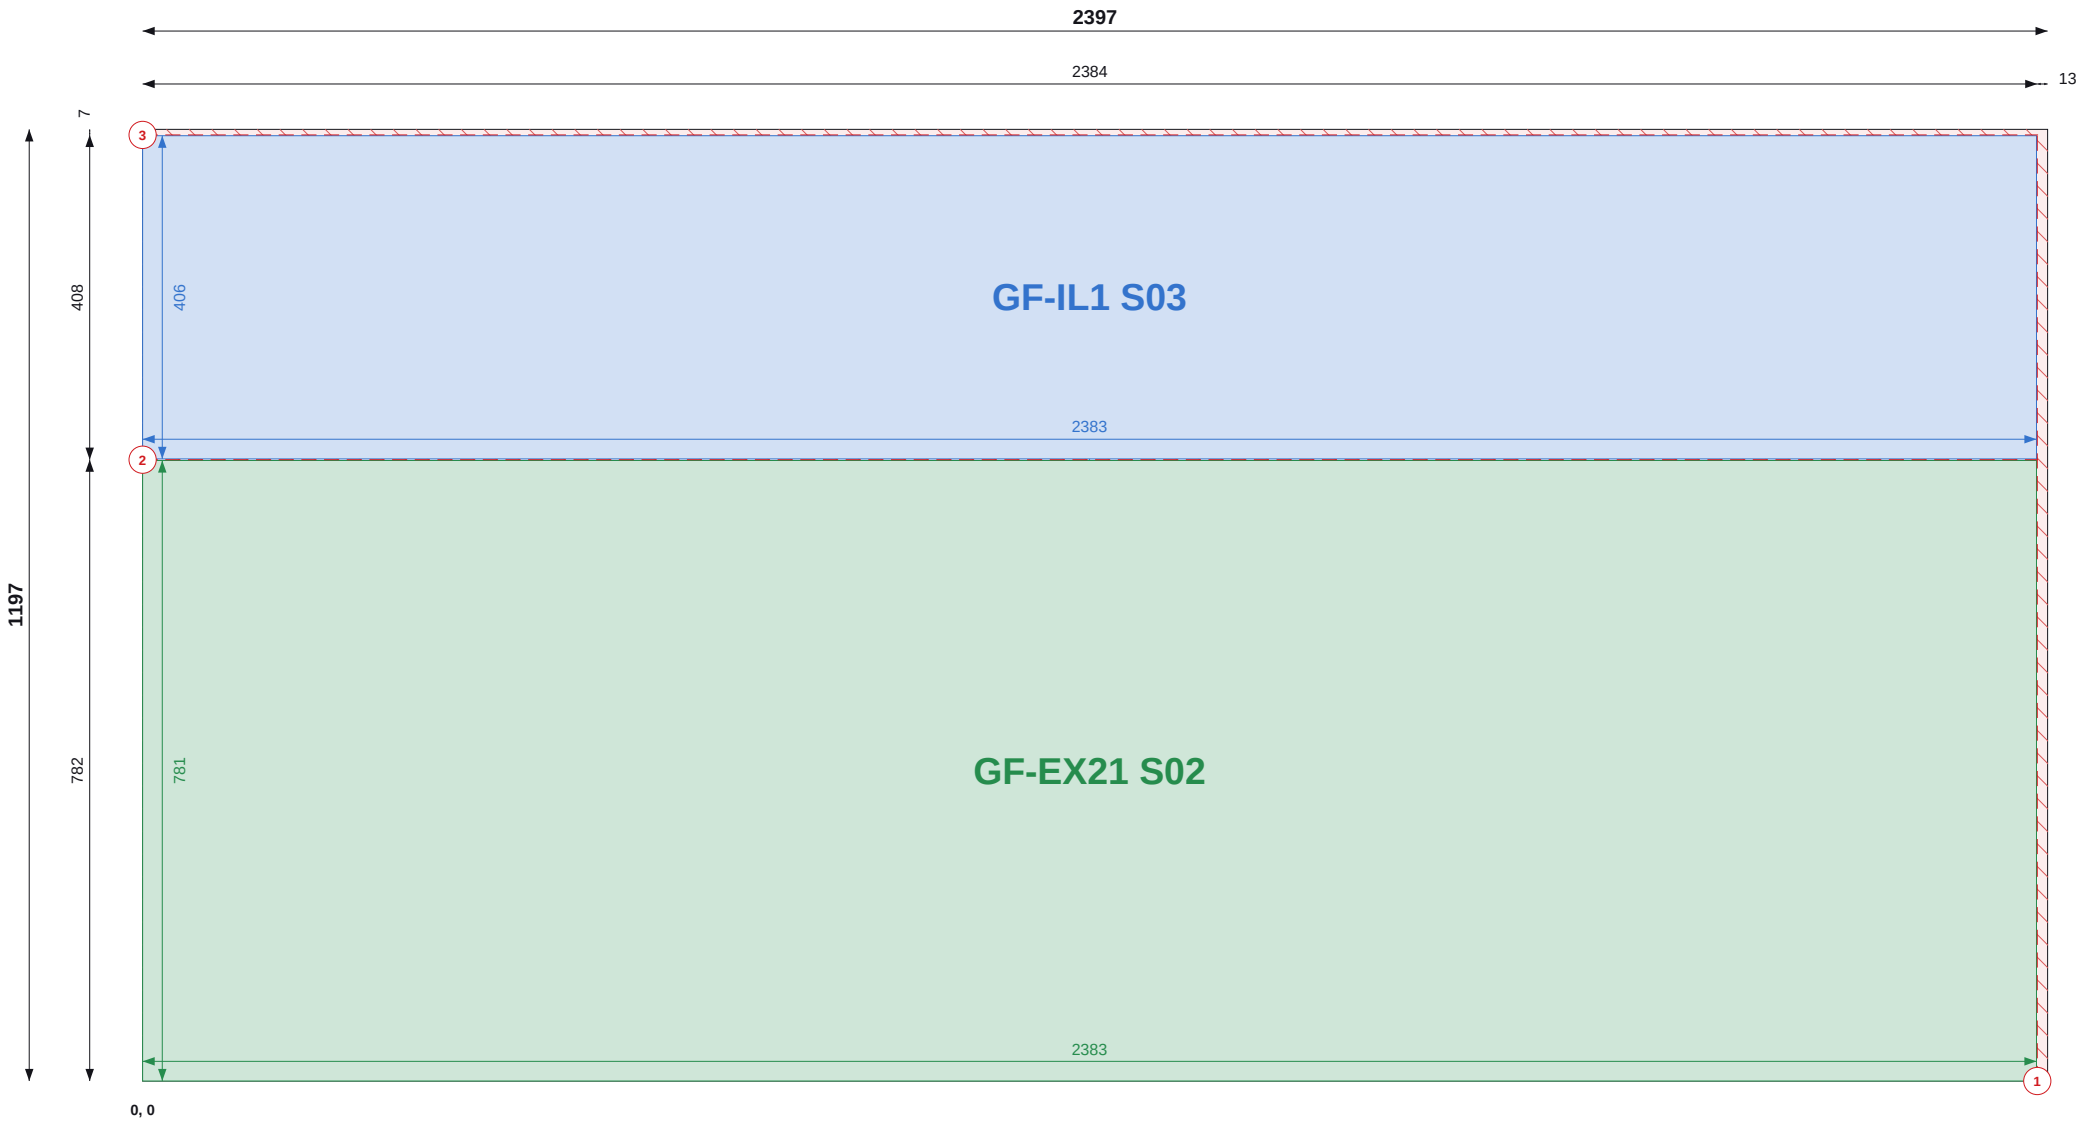

Top / left chains = saw cut positions (to cut centres). Coloured = part size and position.

SHEET 24 OF 38

THIS SHEET

Item	Value
Parts	2
Used / waste	98.6% / 0.04 m2
Reusable offcuts	0
Saw cuts / shared	3 / 1

PIECES (POSITION = BOTTOM-LEFT CORNER)

Label	Size	X, Y
GF-IL1 S03	406 x 2383	0, 783
GF-EX21 S02	781 x 2383	0, 0

NOTES

- Cut from OSB/3 9mm 1197x2397, 2mm saw kerf. Viewed on the face; dimensions from the sheet's bottom-left corner (0,0). Red numbered lines = saw cuts in order, each edge to edge.
- Coloured dimensions belong to the part of that colour: its width and height, and its position from the sheet edges. Raked parts: corner coordinates at each corner.
- Red hatch = waste. Labels = panel + piece mark on the manufacture drawing.

REVISIONS

REV	DATE	DESCRIPTION
C01	13.09.26	Construction issue



TLS TIMBER FRAME

Design & Manufacture

Scan: 3D model + drawings



CLIENT MP Adams	PROJECT MP Adams Plot 3, Eckington
--------------------	---------------------------------------


DRAWING TITLE OSB CUTTING - GROUND FLOOR - SHEET 24 OF 38

OSB/3 9mm 1197x2397 | Ground Floor

SCALE NTS	SIZE A3	DATE 13.09.26	DRAWN TS
--------------	------------	------------------	-------------

STATUS CONSTRUCTION	DRAWING No. P3-CP-OSB-01 / 24	REV C01
-------------------------------	---	-------------------

Do not scale. All dimensions in mm. Check all dimensions on site.

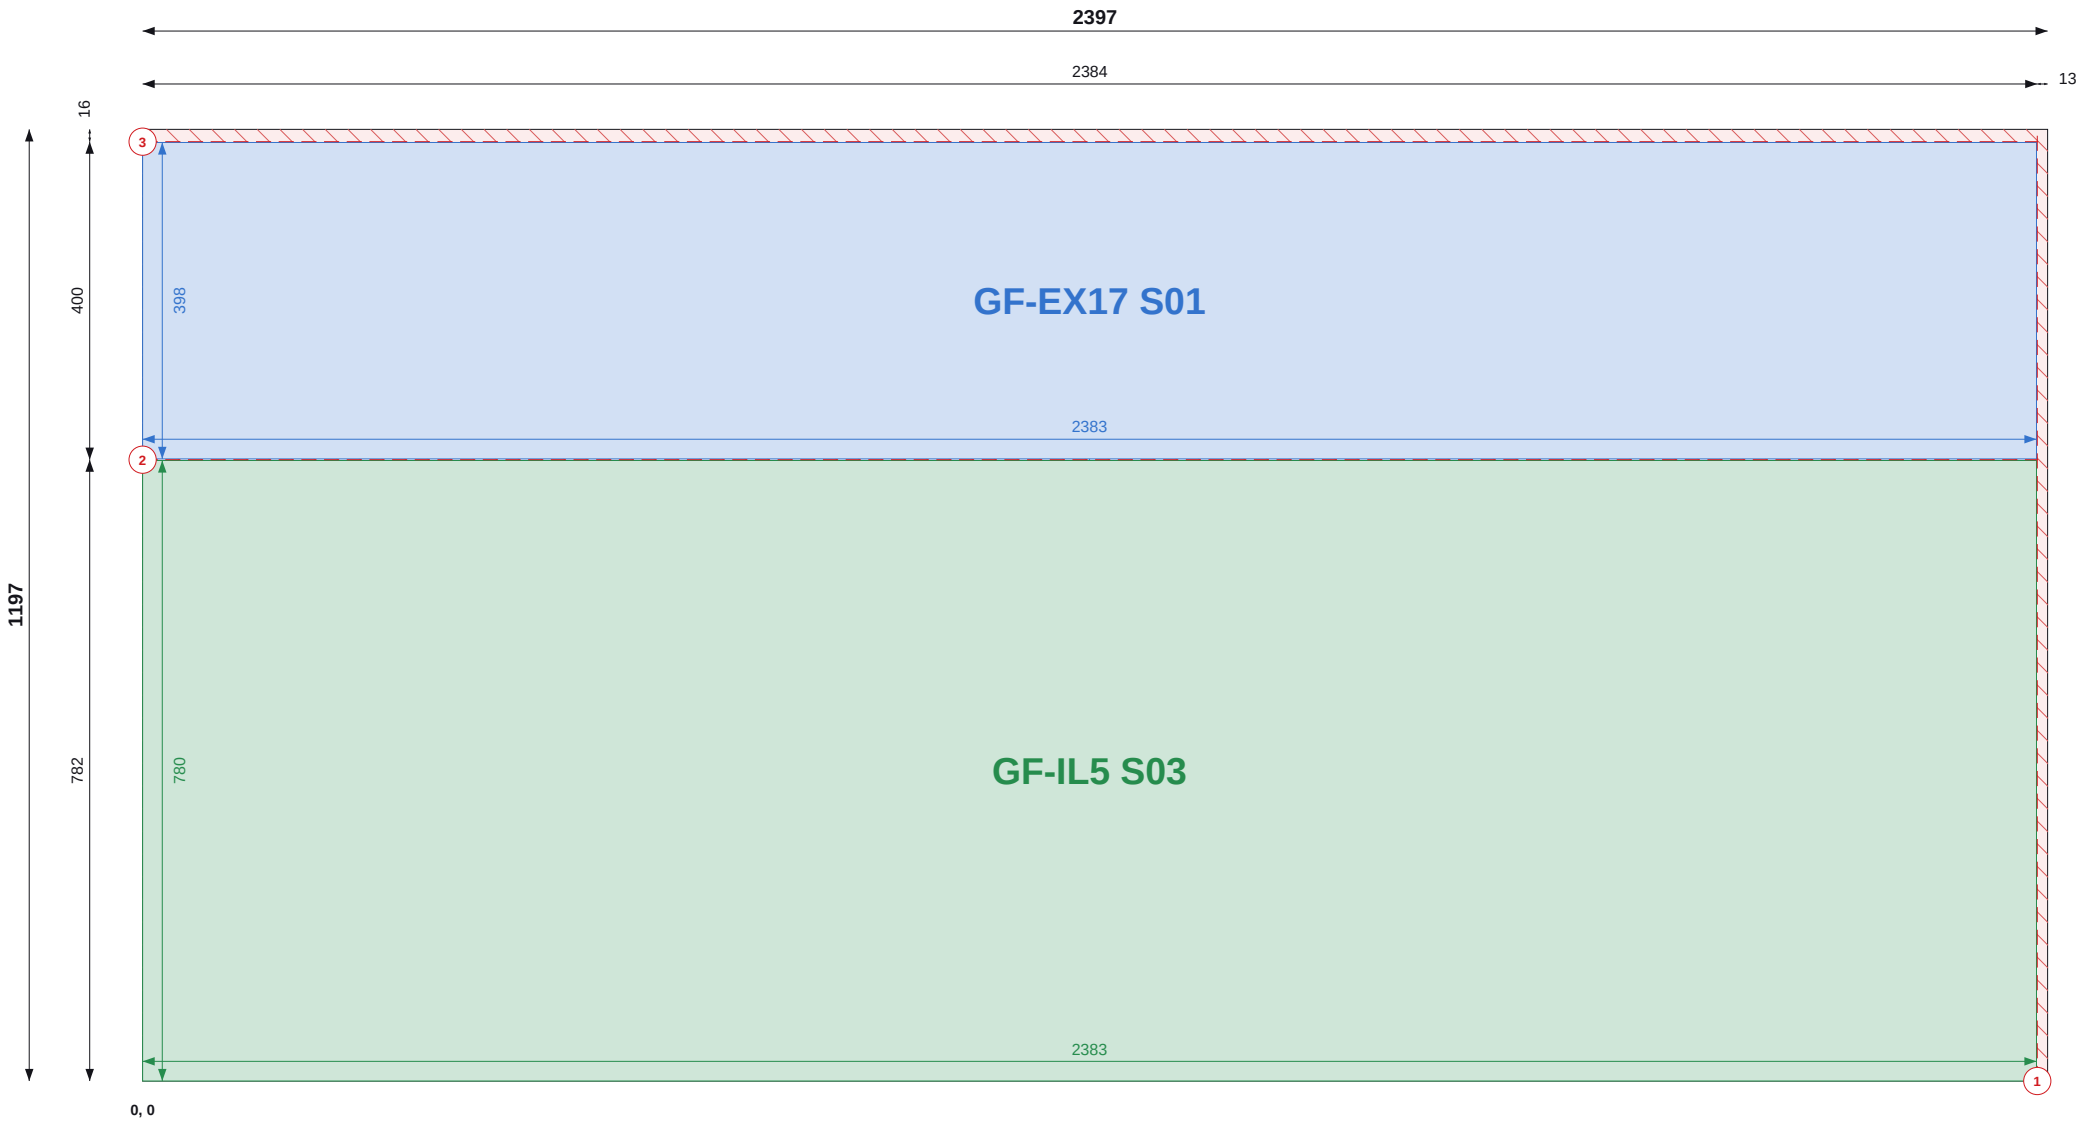

Top / left chains = saw cut positions (to cut centres). Coloured = part size and position.

SHEET 25 OF 38

THIS SHEET

Item	Value
Parts	2
Used / waste	97.9% / 0.06 m2
Reusable offcuts	0
Saw cuts / shared	3 / 1

PIECES (POSITION = BOTTOM-LEFT CORNER)

Label	Size	X, Y
GF-EX17 S01	398 x 2383	0, 782
GF-IL5 S03	780 x 2383	0, 0

NOTES

- Cut from OSB/3 9mm 1197x2397, 2mm saw kerf. Viewed on the face; dimensions from the sheet's bottom-left corner (0,0). Red numbered lines = saw cuts in order, each edge to edge.
- Coloured dimensions belong to the part of that colour: its width and height, and its position from the sheet edges. Raked parts: corner coordinates at each corner.
- Red hatch = waste. Labels = panel + piece mark on the manufacture drawing.

REVISIONS

REV	DATE	DESCRIPTION
C01	13.09.26	Construction issue



TLS TIMBER FRAME

Design & Manufacture

Scan: 3D model + drawings



CLIENT	PROJECT
MP Adams	MP Adams Plot 3, Eckington


DRAWING TITLE
OSB CUTTING - GROUND FLOOR - SHEET 25 OF 38

OSB/3 9mm 1197x2397 | Ground Floor

SCALE	SIZE	DATE	DRAWN
NTS	A3	13.09.26	TS

STATUS	DRAWING No.	REV
CONSTRUCTION	P3-CP-OSB-01 / 25	C01

Do not scale. All dimensions in mm. Check all dimensions on site.

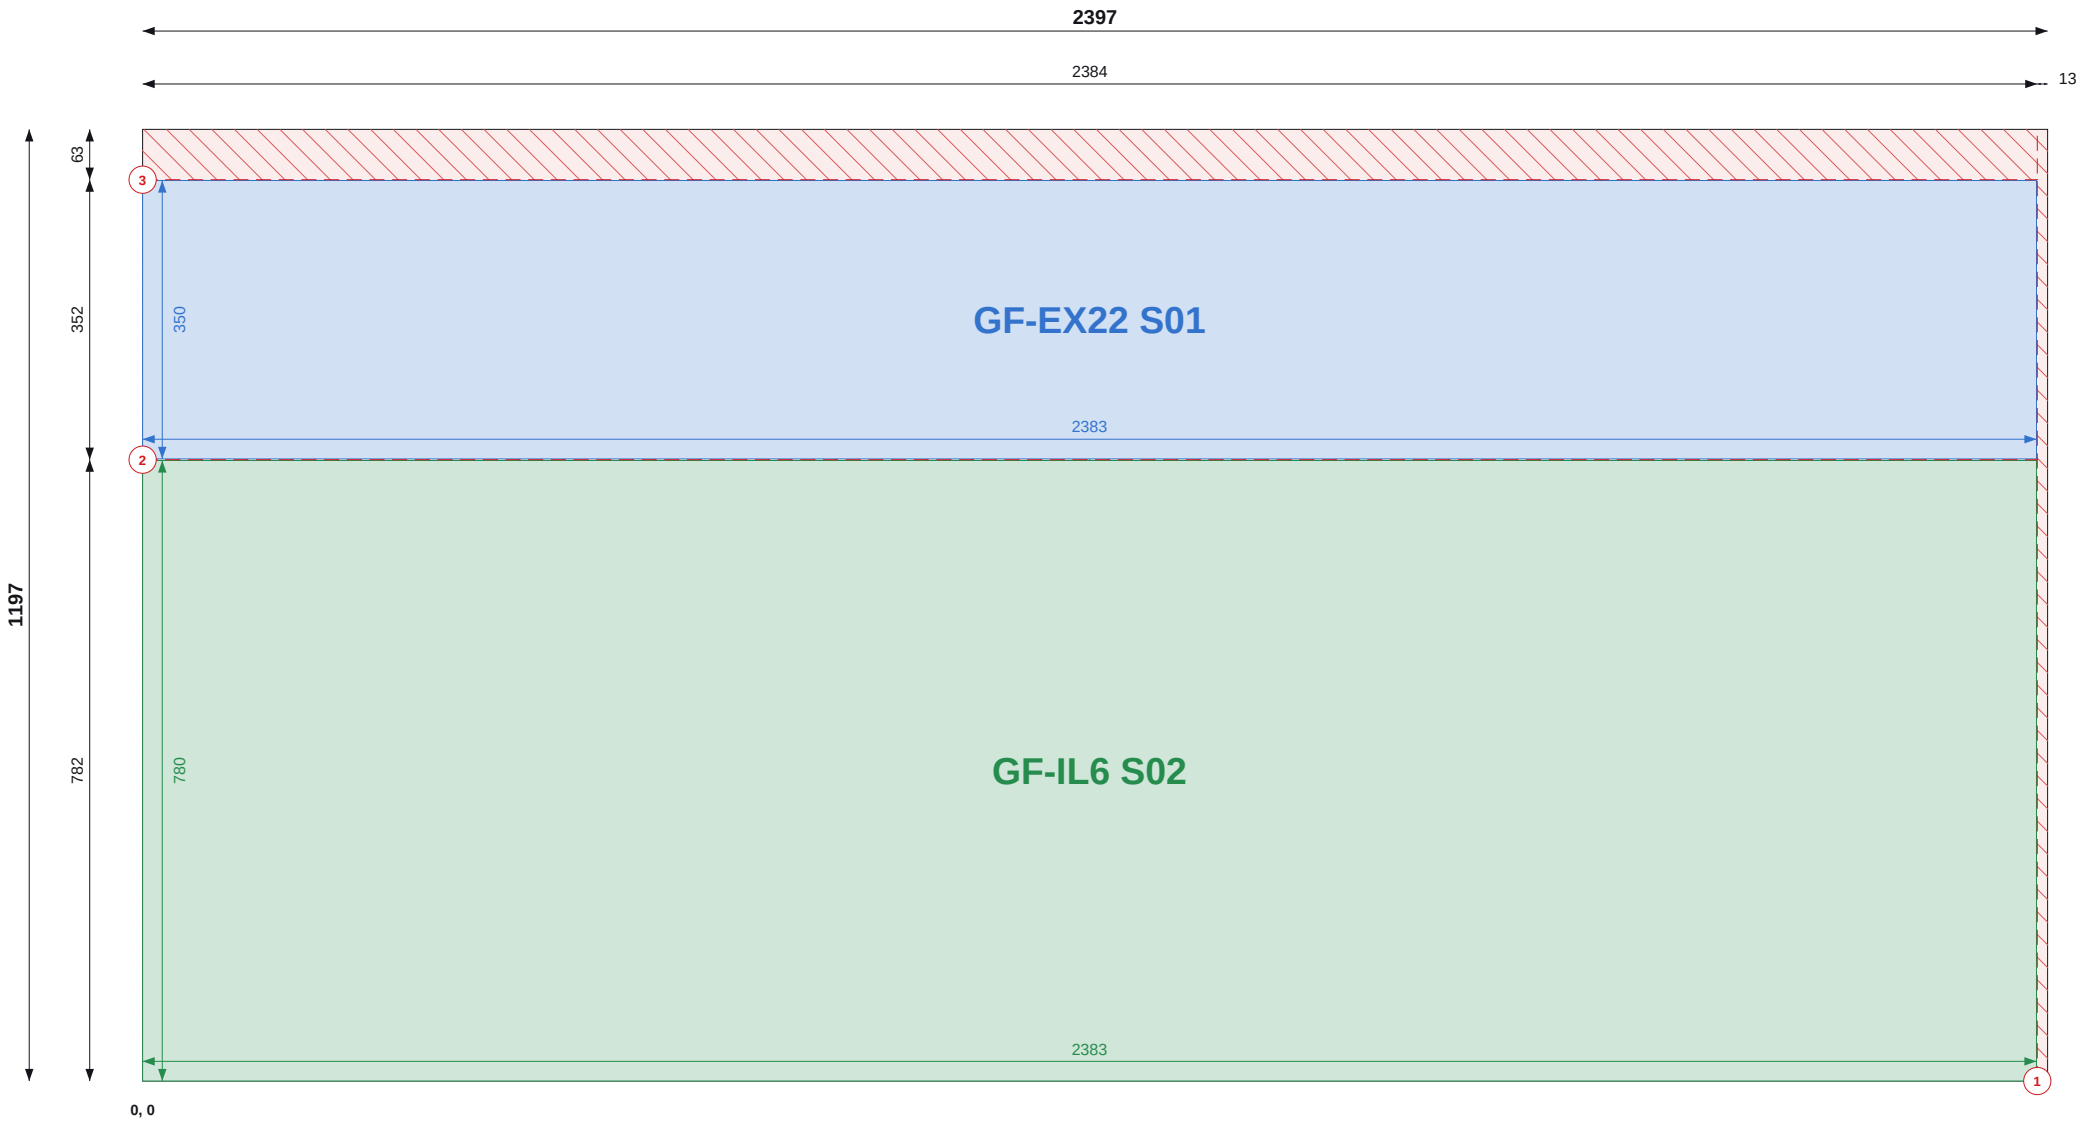

Top / left chains = saw cut positions (to cut centres). Coloured = part size and position.

SHEET 26 OF 38

THIS SHEET

Item	Value
Parts	2
Used / waste	93.9% / 0.17 m2
Reusable offcuts	0
Saw cuts / shared	3 / 1

PIECES (POSITION = BOTTOM-LEFT CORNER)

Label	Size	X, Y
GF-EX22 S01	350 x 2383	0, 782
GF-IL6 S02	780 x 2383	0, 0

NOTES

- Cut from OSB/3 9mm 1197x2397, 2mm saw kerf. Viewed on the face; dimensions from the sheet's bottom-left corner (0,0). Red numbered lines = saw cuts in order, each edge to edge.
- Coloured dimensions belong to the part of that colour: its width and height, and its position from the sheet edges. Raked parts: corner coordinates at each corner.
- Red hatch = waste. Labels = panel + piece mark on the manufacture drawing.

REVISIONS

REV	DATE	DESCRIPTION
C01	13.09.26	Construction issue



TLS TIMBER FRAME

Design & Manufacture

Scan: 3D model + drawings



CLIENT	PROJECT
MP Adams	MP Adams Plot 3, Eckington


DRAWING TITLE
OSB CUTTING - GROUND FLOOR - SHEET 26 OF 38

OSB/3 9mm 1197x2397 | Ground Floor

SCALE	SIZE	DATE	DRAWN
NTS	A3	13.09.26	TS

STATUS	DRAWING No.	REV
CONSTRUCTION	P3-CP-OSB-01 / 26	C01

Do not scale. All dimensions in mm. Check all dimensions on site.

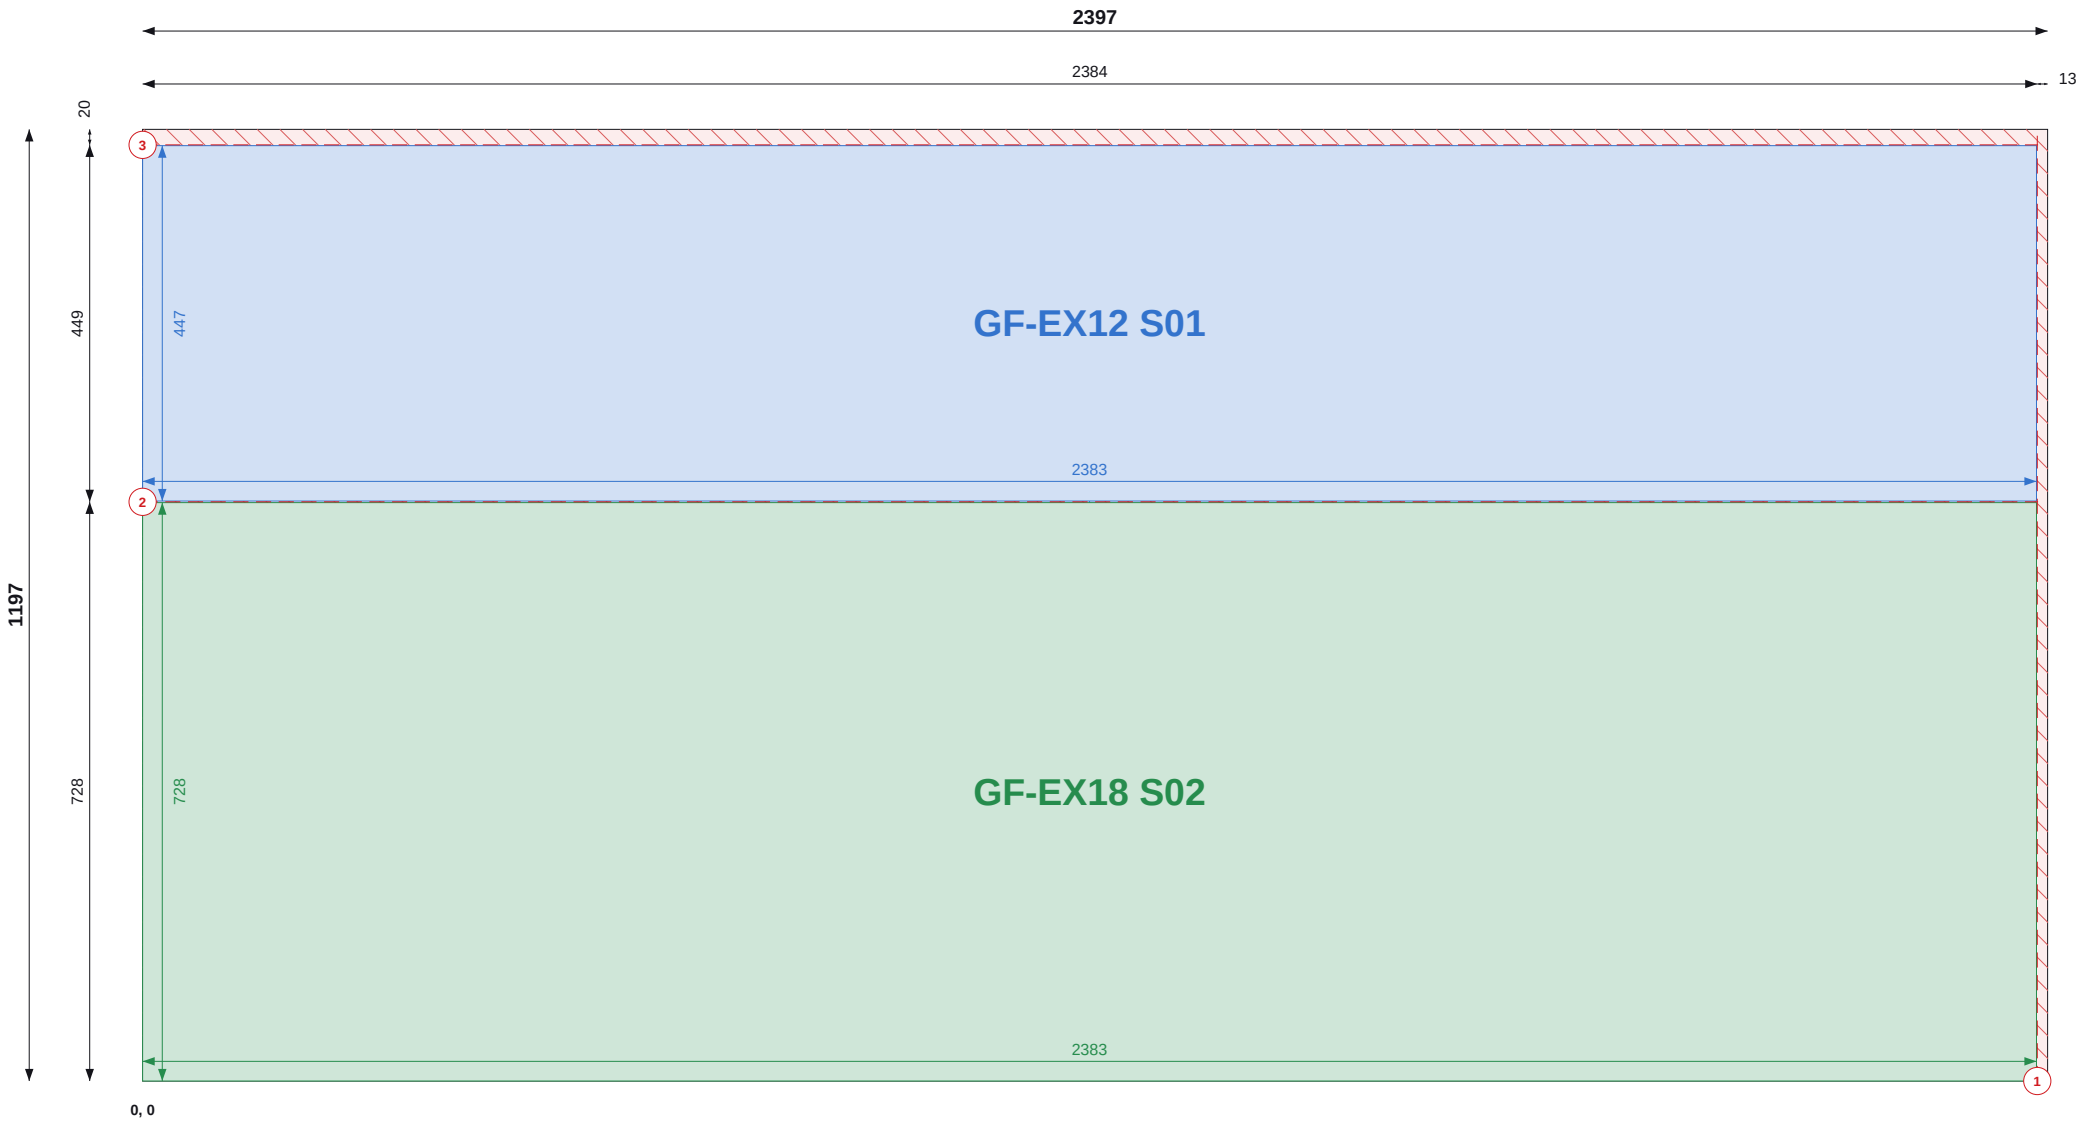

Top / left chains = saw cut positions (to cut centres). Coloured = part size and position.

SHEET 27 OF 38

THIS SHEET

Item	Value
Parts	2
Used / waste	97.5% / 0.07 m2
Reusable offcuts	0
Saw cuts / shared	3 / 1

PIECES (POSITION = BOTTOM-LEFT CORNER)

Label	Size	X, Y
GF-EX12 S01	447 x 2383	0, 730
GF-EX18 S02	728 x 2383	0, 0

NOTES

- Cut from OSB/3 9mm 1197x2397, 2mm saw kerf. Viewed on the face; dimensions from the sheet's bottom-left corner (0,0). Red numbered lines = saw cuts in order, each edge to edge.
- Coloured dimensions belong to the part of that colour: its width and height, and its position from the sheet edges. Raked parts: corner coordinates at each corner.
- Red hatch = waste. Labels = panel + piece mark on the manufacture drawing.

REVISIONS

REV	DATE	DESCRIPTION
C01	13.09.26	Construction issue



TLS TIMBER FRAME

Design & Manufacture

Scan: 3D model + drawings



CLIENT	PROJECT
MP Adams	MP Adams Plot 3, Eckington


DRAWING TITLE
OSB CUTTING - GROUND FLOOR - SHEET 27 OF 38

OSB/3 9mm 1197x2397 | Ground Floor

SCALE	SIZE	DATE	DRAWN
NTS	A3	13.09.26	TS

STATUS	DRAWING No.	REV
CONSTRUCTION	P3-CP-OSB-01 / 27	C01

Do not scale. All dimensions in mm. Check all dimensions on site.

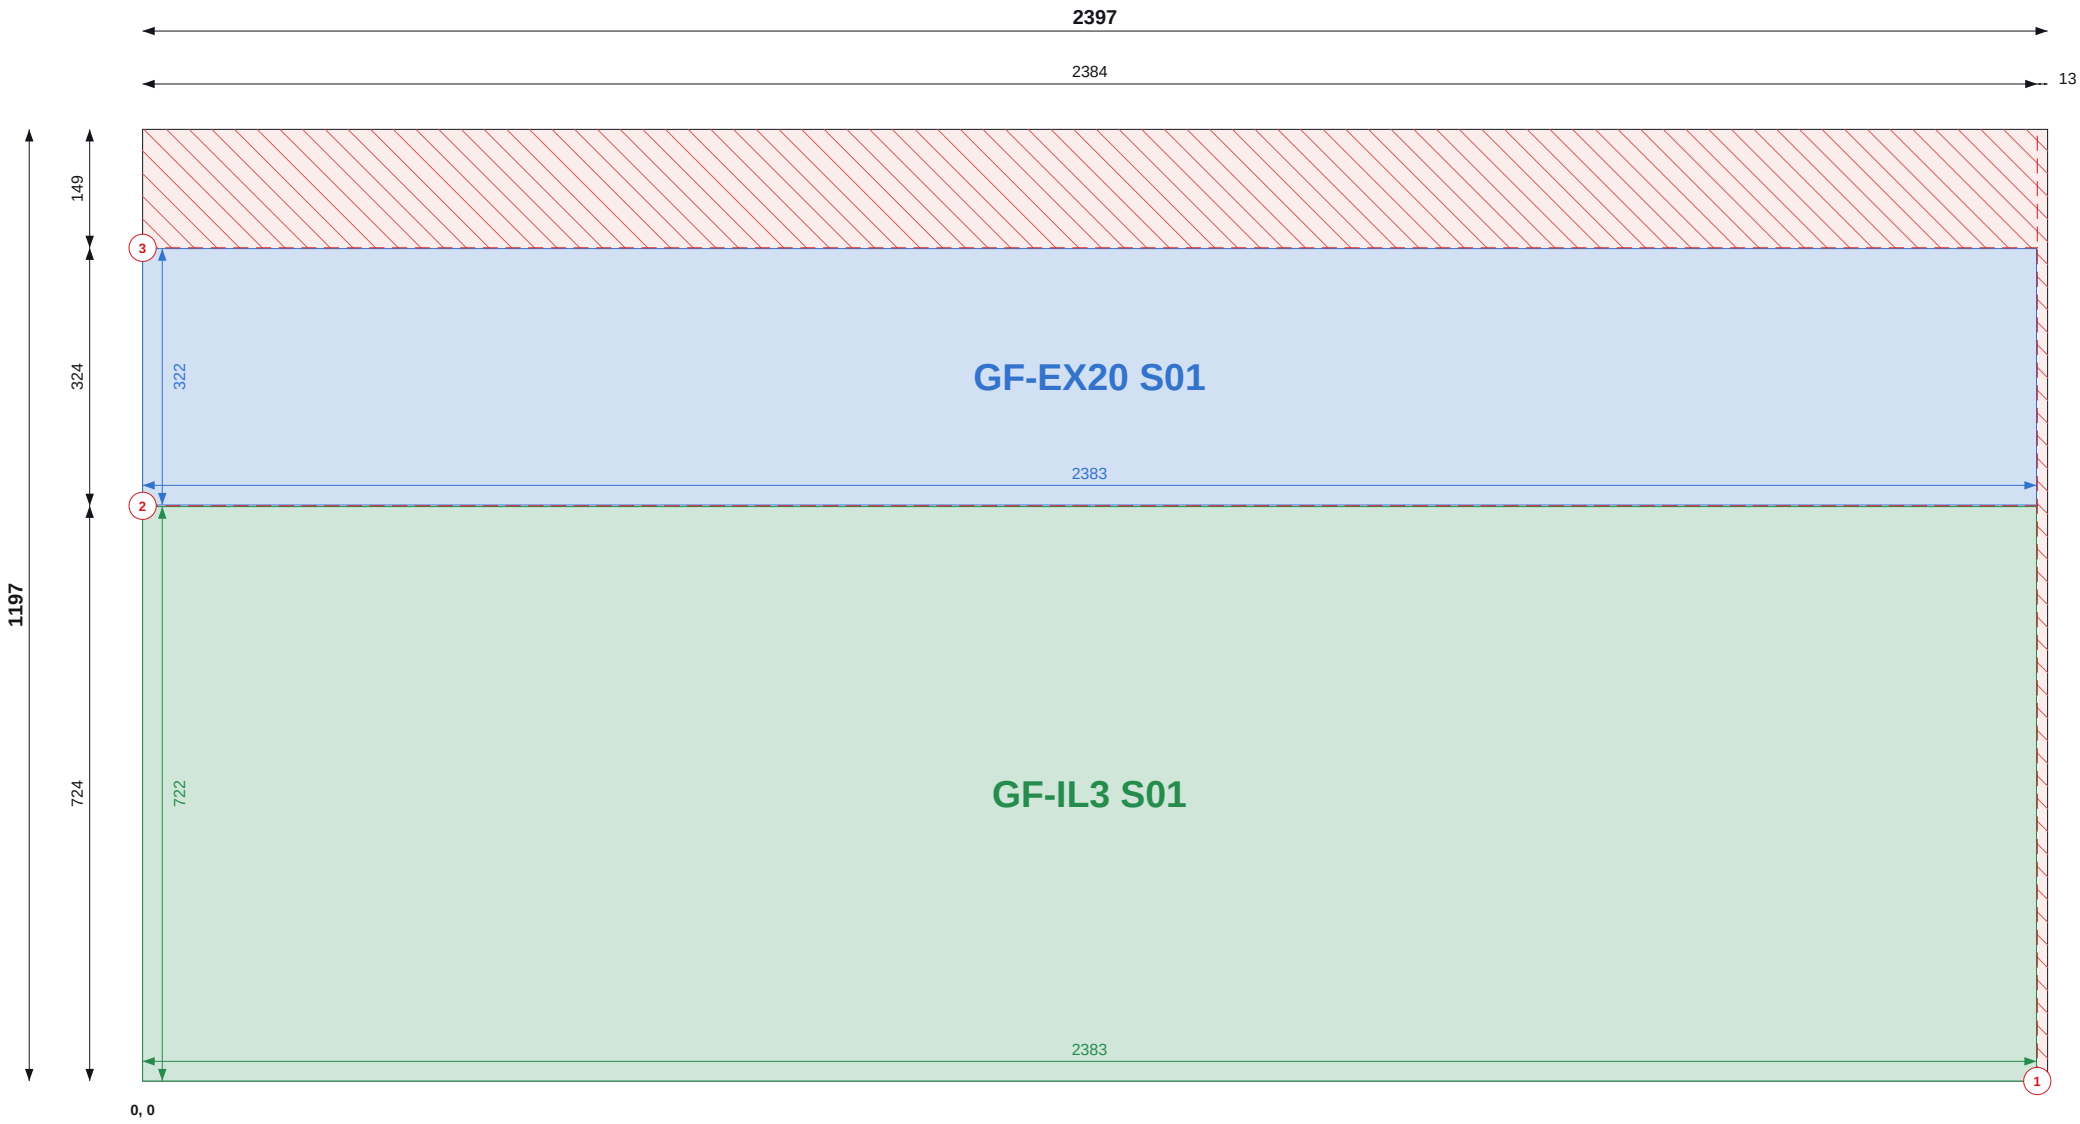

Top / left chains = saw cut positions (to cut centres). Coloured = part size and position.

SHEET 28 OF 38

THIS SHEET

Item	Value
Parts	2
Used / waste	86.8% / 0.38 m2
Reusable offcuts	0
Saw cuts / shared	3 / 1

PIECES (POSITION = BOTTOM-LEFT CORNER)

Label	Size	X, Y
GF-EX20 S01	322 x 2383	0, 724
GF-IL3 S01	722 x 2383	0, 0

NOTES

- Cut from OSB/3 9mm 1197x2397, 2mm saw kerf. Viewed on the face; dimensions from the sheet's bottom-left corner (0,0). Red numbered lines = saw cuts in order, each edge to edge.
- Coloured dimensions belong to the part of that colour: its width and height, and its position from the sheet edges. Raked parts: corner coordinates at each corner.
- Red hatch = waste. Labels = panel + piece mark on the manufacture drawing.

REVISIONS

REV	DATE	DESCRIPTION
C01	13.09.26	Construction issue



TLS TIMBER FRAME

Design & Manufacture

Scan: 3D model + drawings



CLIENT	PROJECT
MP Adams	MP Adams Plot 3, Eckington


DRAWING TITLE
OSB CUTTING - GROUND FLOOR - SHEET 28 OF 38

OSB/3 9mm 1197x2397 | Ground Floor

SCALE	SIZE	DATE	DRAWN
NTS	A3	13.09.26	TS

STATUS	DRAWING No.	REV
CONSTRUCTION	P3-CP-OSB-01 / 28	C01

Do not scale. All dimensions in mm. Check all dimensions on site.

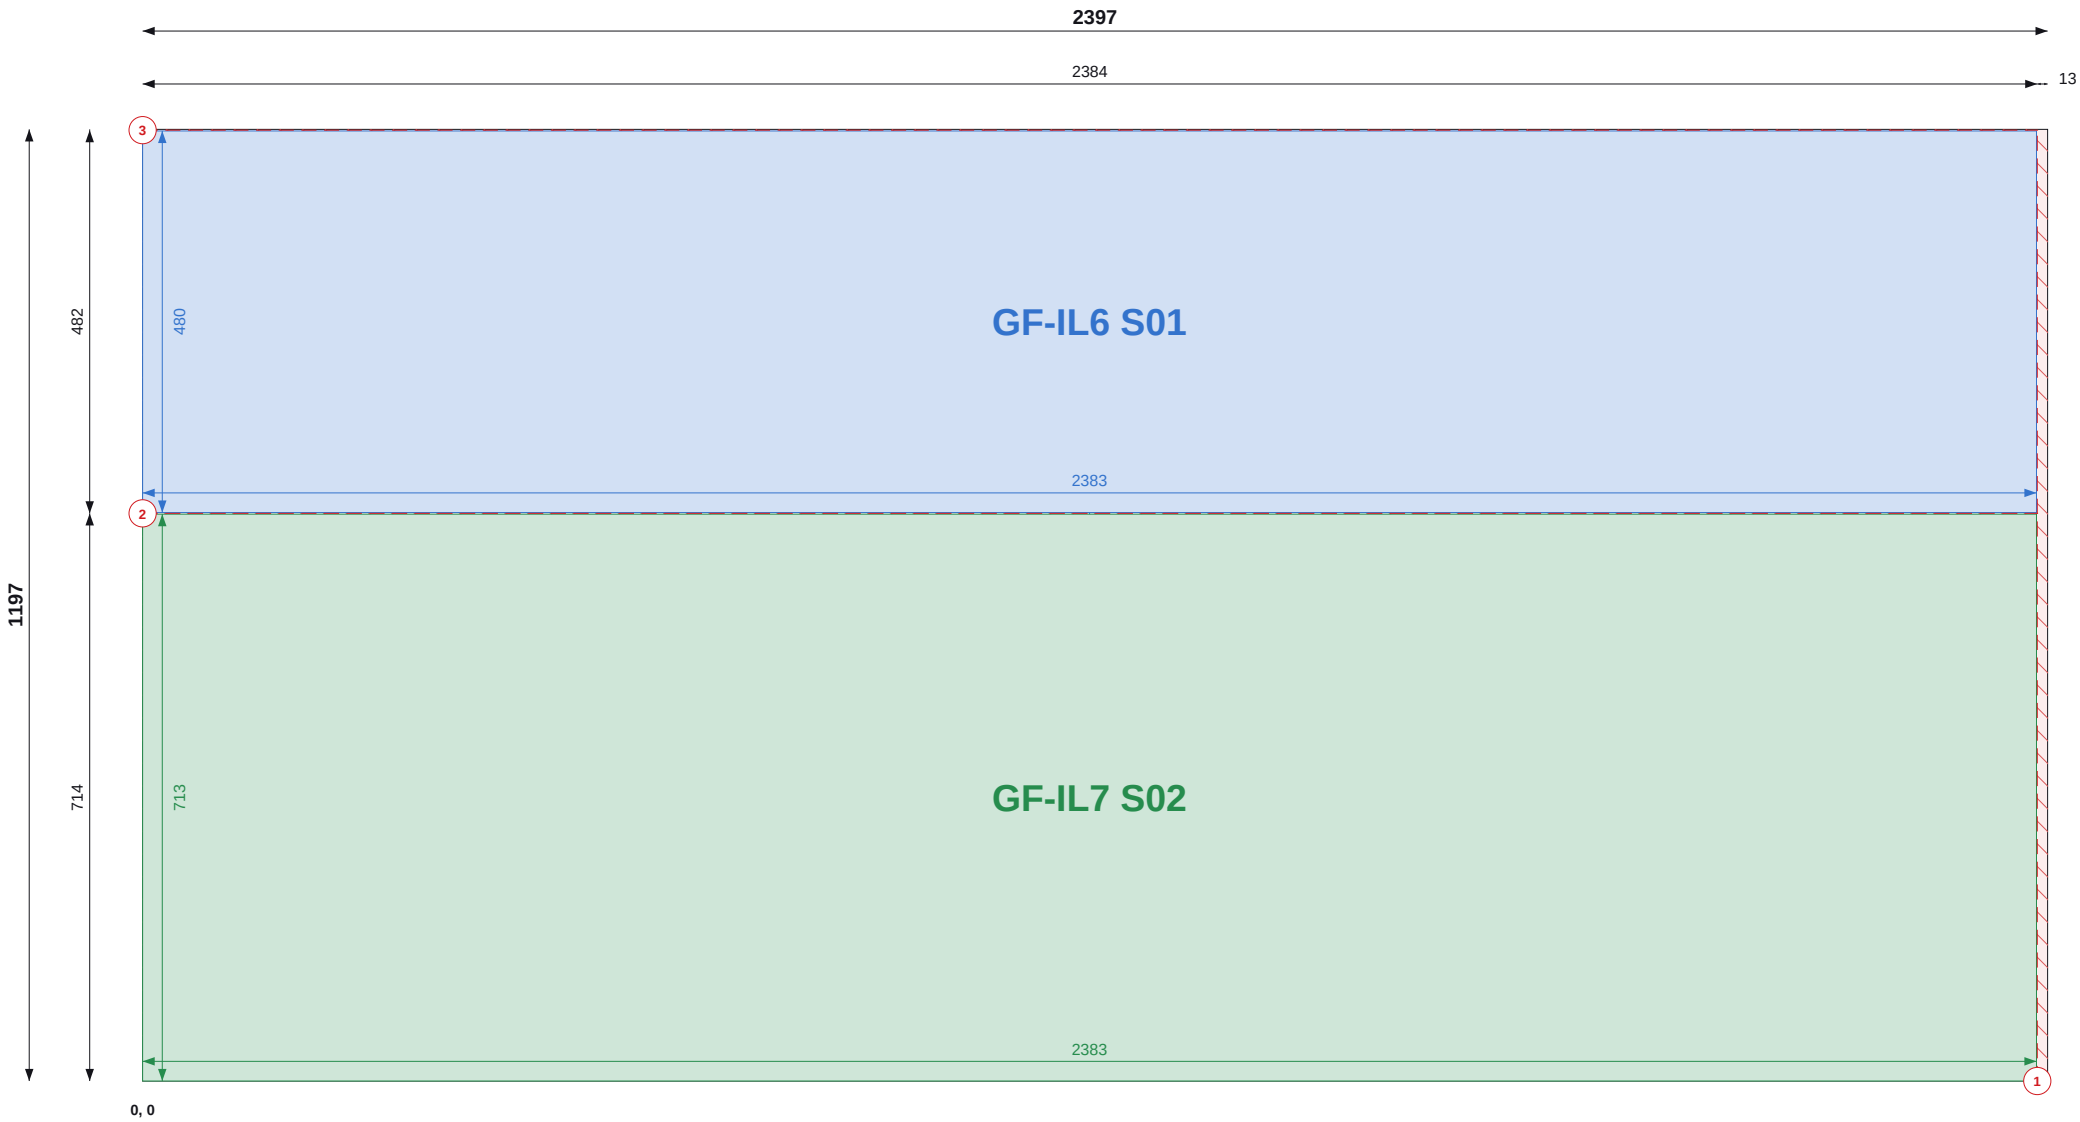

Top / left chains = saw cut positions (to cut centres). Coloured = part size and position.

SHEET 29 OF 38

THIS SHEET

Item	Value
Parts	2
Used / waste	99.1% / 0.03 m2
Reusable offcuts	0
Saw cuts / shared	3 / 1

PIECES (POSITION = BOTTOM-LEFT CORNER)

Label	Size	X, Y
GF-IL6 S01	480 x 2383	0, 715
GF-IL7 S02	713 x 2383	0, 0

NOTES

1. Cut from OSB/3 9mm 1197x2397, 2mm saw kerf. Viewed on the face; dimensions from the sheet's bottom-left corner (0,0). Red numbered lines = saw cuts in order, each edge to edge.
2. Coloured dimensions belong to the part of that colour: its width and height, and its position from the sheet edges. Raked parts: corner coordinates at each corner.
3. Red hatch = waste. Labels = panel + piece mark on the manufacture drawing.

REVISIONS

REV	DATE	DESCRIPTION
C01	13.09.26	Construction issue



TLS TIMBER FRAME

Design & Manufacture

Scan: 3D model + drawings



CLIENT	PROJECT
MP Adams	MP Adams Plot 3, Eckington


DRAWING TITLE
OSB CUTTING - GROUND FLOOR - SHEET 29 OF 38

OSB/3 9mm 1197x2397 | Ground Floor

SCALE	SIZE	DATE	DRAWN
NTS	A3	13.09.26	TS

STATUS	DRAWING No.	REV
CONSTRUCTION	P3-CP-OSB-01 / 29	C01

Do not scale. All dimensions in mm. Check all dimensions on site.

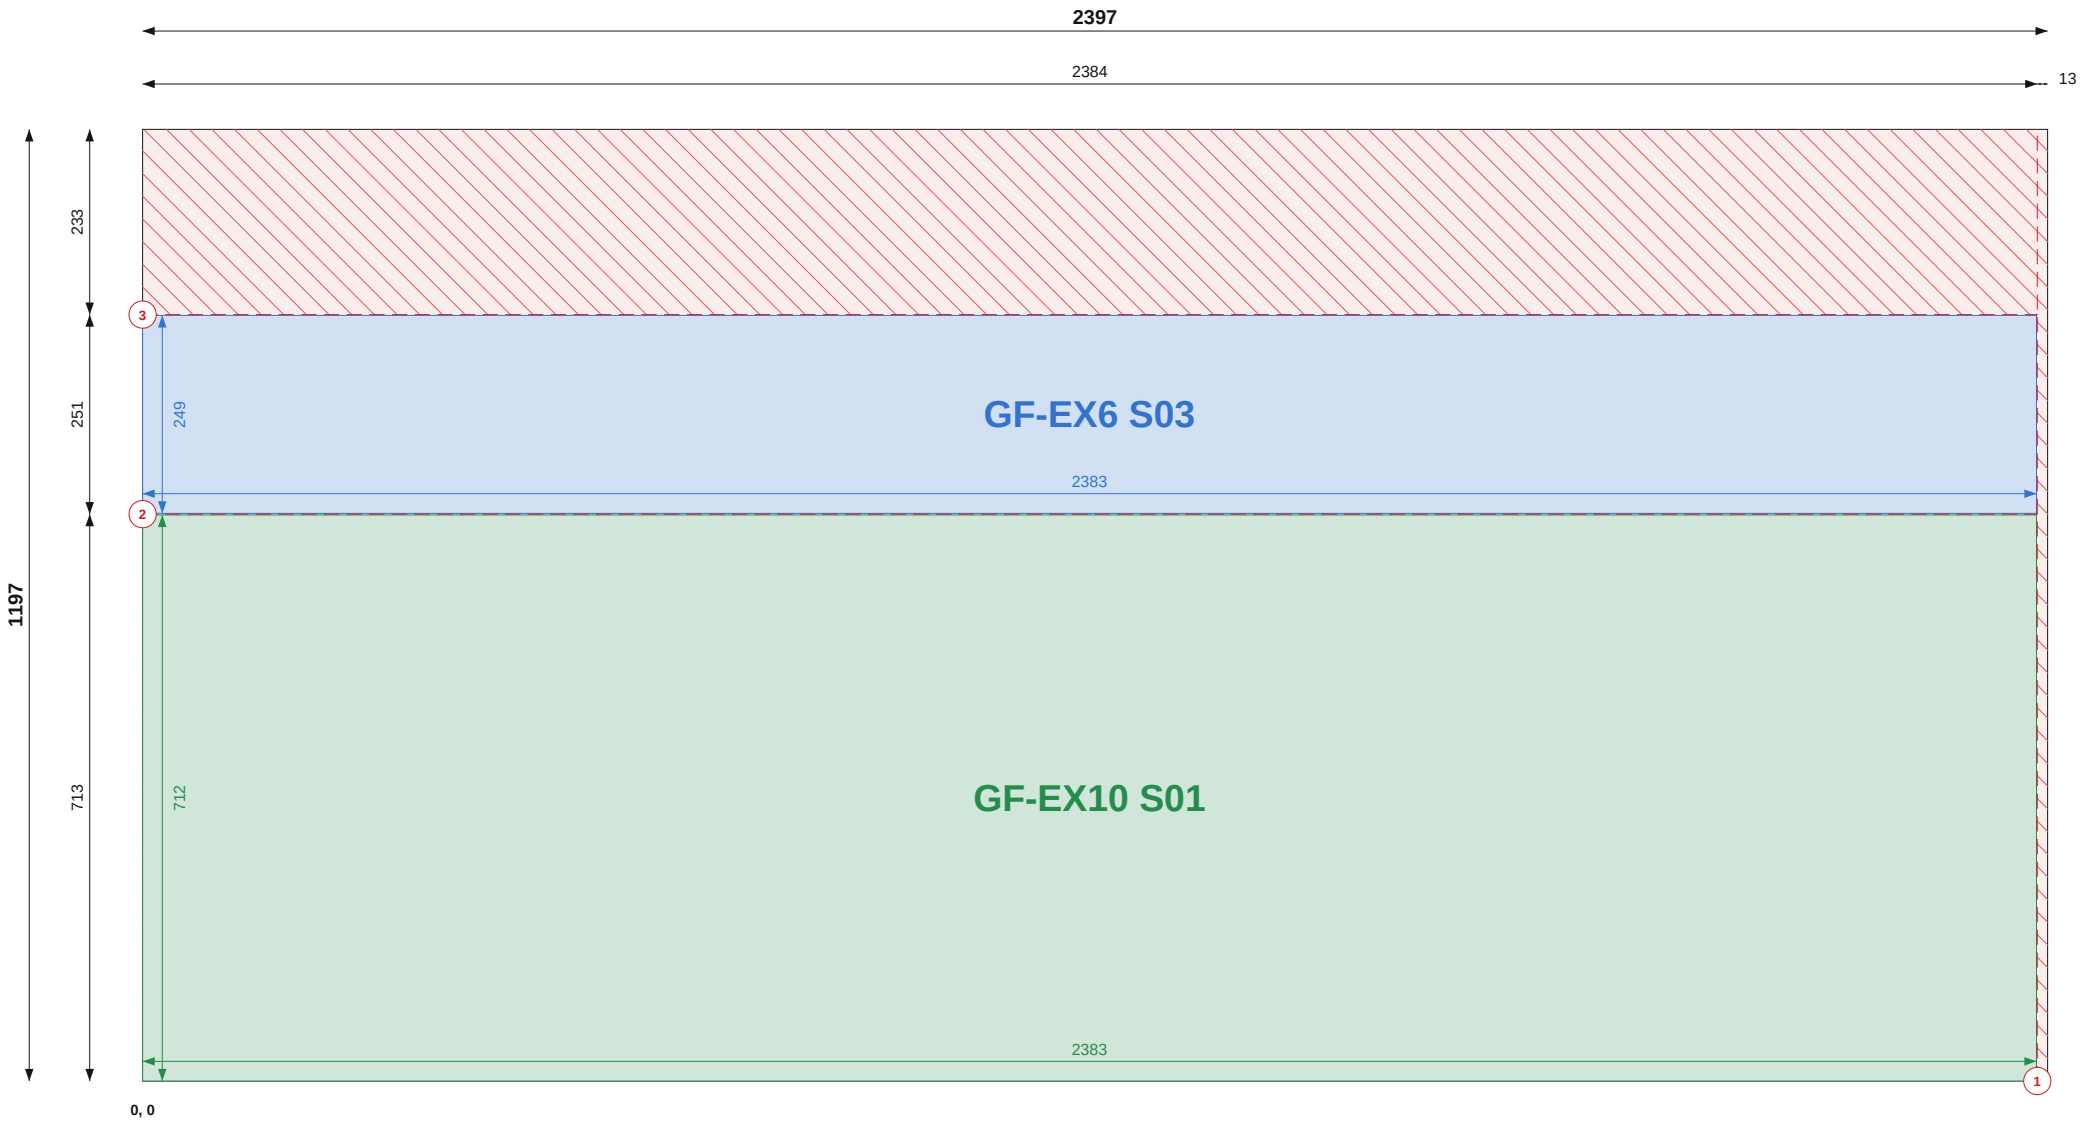

Top / left chains = saw cut positions (to cut centres). Coloured = part size and position.

SHEET 30 OF 38

THIS SHEET

Item	Value
Parts	2
Used / waste	79.8% / 0.58 m2
Reusable offcuts	0
Saw cuts / shared	3 / 1

PIECES (POSITION = BOTTOM-LEFT CORNER)

Label	Size	X, Y
GF-EX6 S03	249 x 2383	0, 714
GF-EX10 S01	712 x 2383	0, 0

NOTES

- Cut from OSB/3 9mm 1197x2397, 2mm saw kerf. Viewed on the face; dimensions from the sheet's bottom-left corner (0,0). Red numbered lines = saw cuts in order, each edge to edge.
- Coloured dimensions belong to the part of that colour: its width and height, and its position from the sheet edges. Raked parts: corner coordinates at each corner.
- Red hatch = waste. Labels = panel + piece mark on the manufacture drawing.

REVISIONS

REV	DATE	DESCRIPTION
C01	13.09.26	Construction issue



TLS TIMBER FRAME

Design & Manufacture

Scan: 3D model + drawings



CLIENT	PROJECT
MP Adams	MP Adams Plot 3, Eckington


DRAWING TITLE
OSB CUTTING - GROUND FLOOR - SHEET 30 OF 38

OSB/3 9mm 1197x2397 | Ground Floor

SCALE	SIZE	DATE	DRAWN
NTS	A3	13.09.26	TS

STATUS	DRAWING No.	REV
CONSTRUCTION	P3-CP-OSB-01 / 30	C01

Do not scale. All dimensions in mm. Check all dimensions on site.

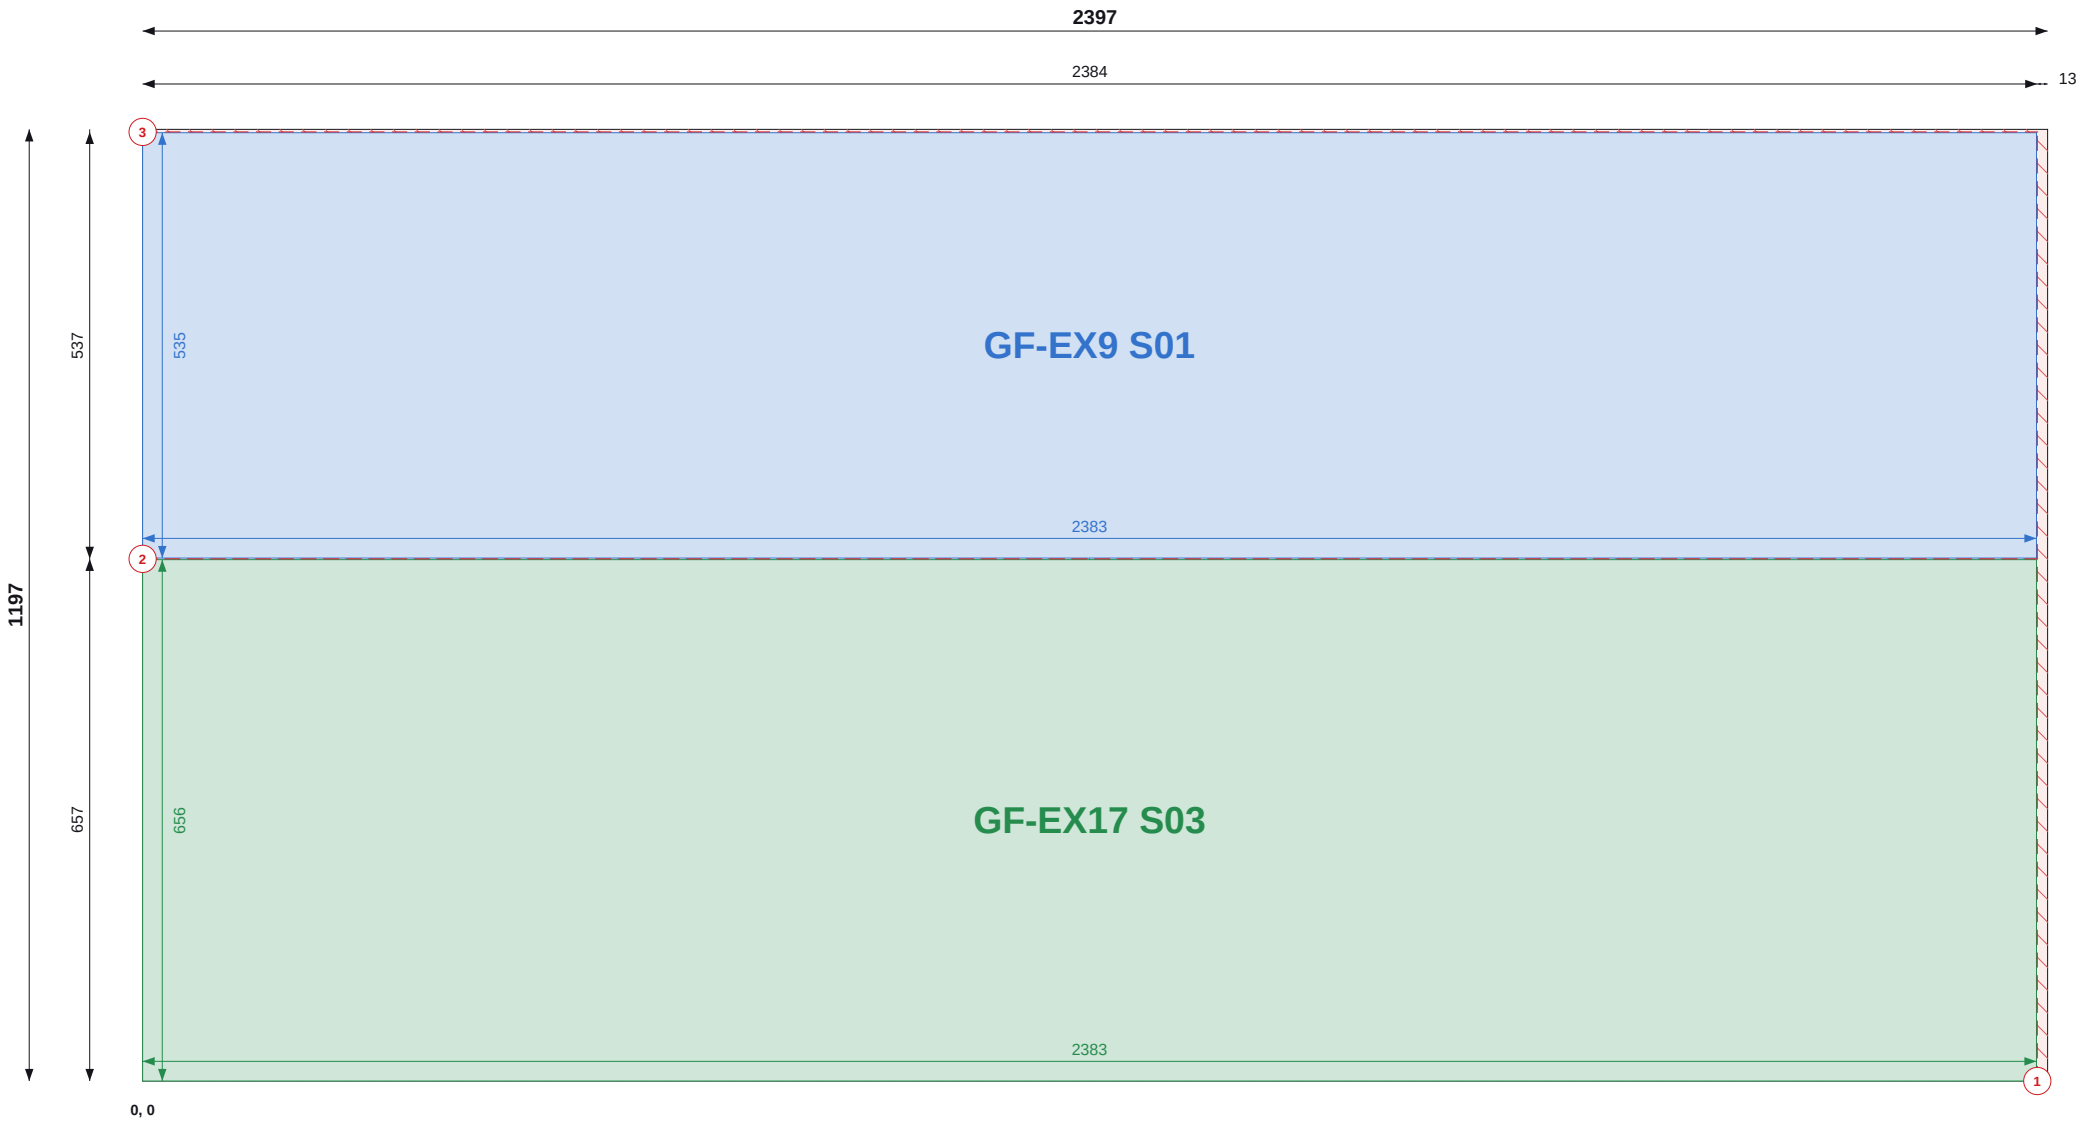

Top / left chains = saw cut positions (to cut centres). Coloured = part size and position.

SHEET 31 OF 38

THIS SHEET

Item	Value
Parts	2
Used / waste	98.9% / 0.03 m2
Reusable offcuts	0
Saw cuts / shared	3 / 1

PIECES (POSITION = BOTTOM-LEFT CORNER)

Label	Size	X, Y
GF-EX9 S01	535 x 2383	0, 658
GF-EX17 S03	656 x 2383	0, 0

NOTES

- Cut from OSB/3 9mm 1197x2397, 2mm saw kerf. Viewed on the face; dimensions from the sheet's bottom-left corner (0,0). Red numbered lines = saw cuts in order, each edge to edge.
- Coloured dimensions belong to the part of that colour: its width and height, and its position from the sheet edges. Raked parts: corner coordinates at each corner.
- Red hatch = waste. Labels = panel + piece mark on the manufacture drawing.

REVISIONS

REV	DATE	DESCRIPTION
C01	13.09.26	Construction issue



TLS TIMBER FRAME

Design & Manufacture

Scan: 3D model + drawings



CLIENT	PROJECT
MP Adams	MP Adams Plot 3, Eckington


DRAWING TITLE
OSB CUTTING - GROUND FLOOR - SHEET 31 OF 38

OSB/3 9mm 1197x2397 | Ground Floor

SCALE	SIZE	DATE	DRAWN
NTS	A3	13.09.26	TS

STATUS	DRAWING No.	REV
CONSTRUCTION	P3-CP-OSB-01 / 31	C01

Do not scale. All dimensions in mm. Check all dimensions on site.

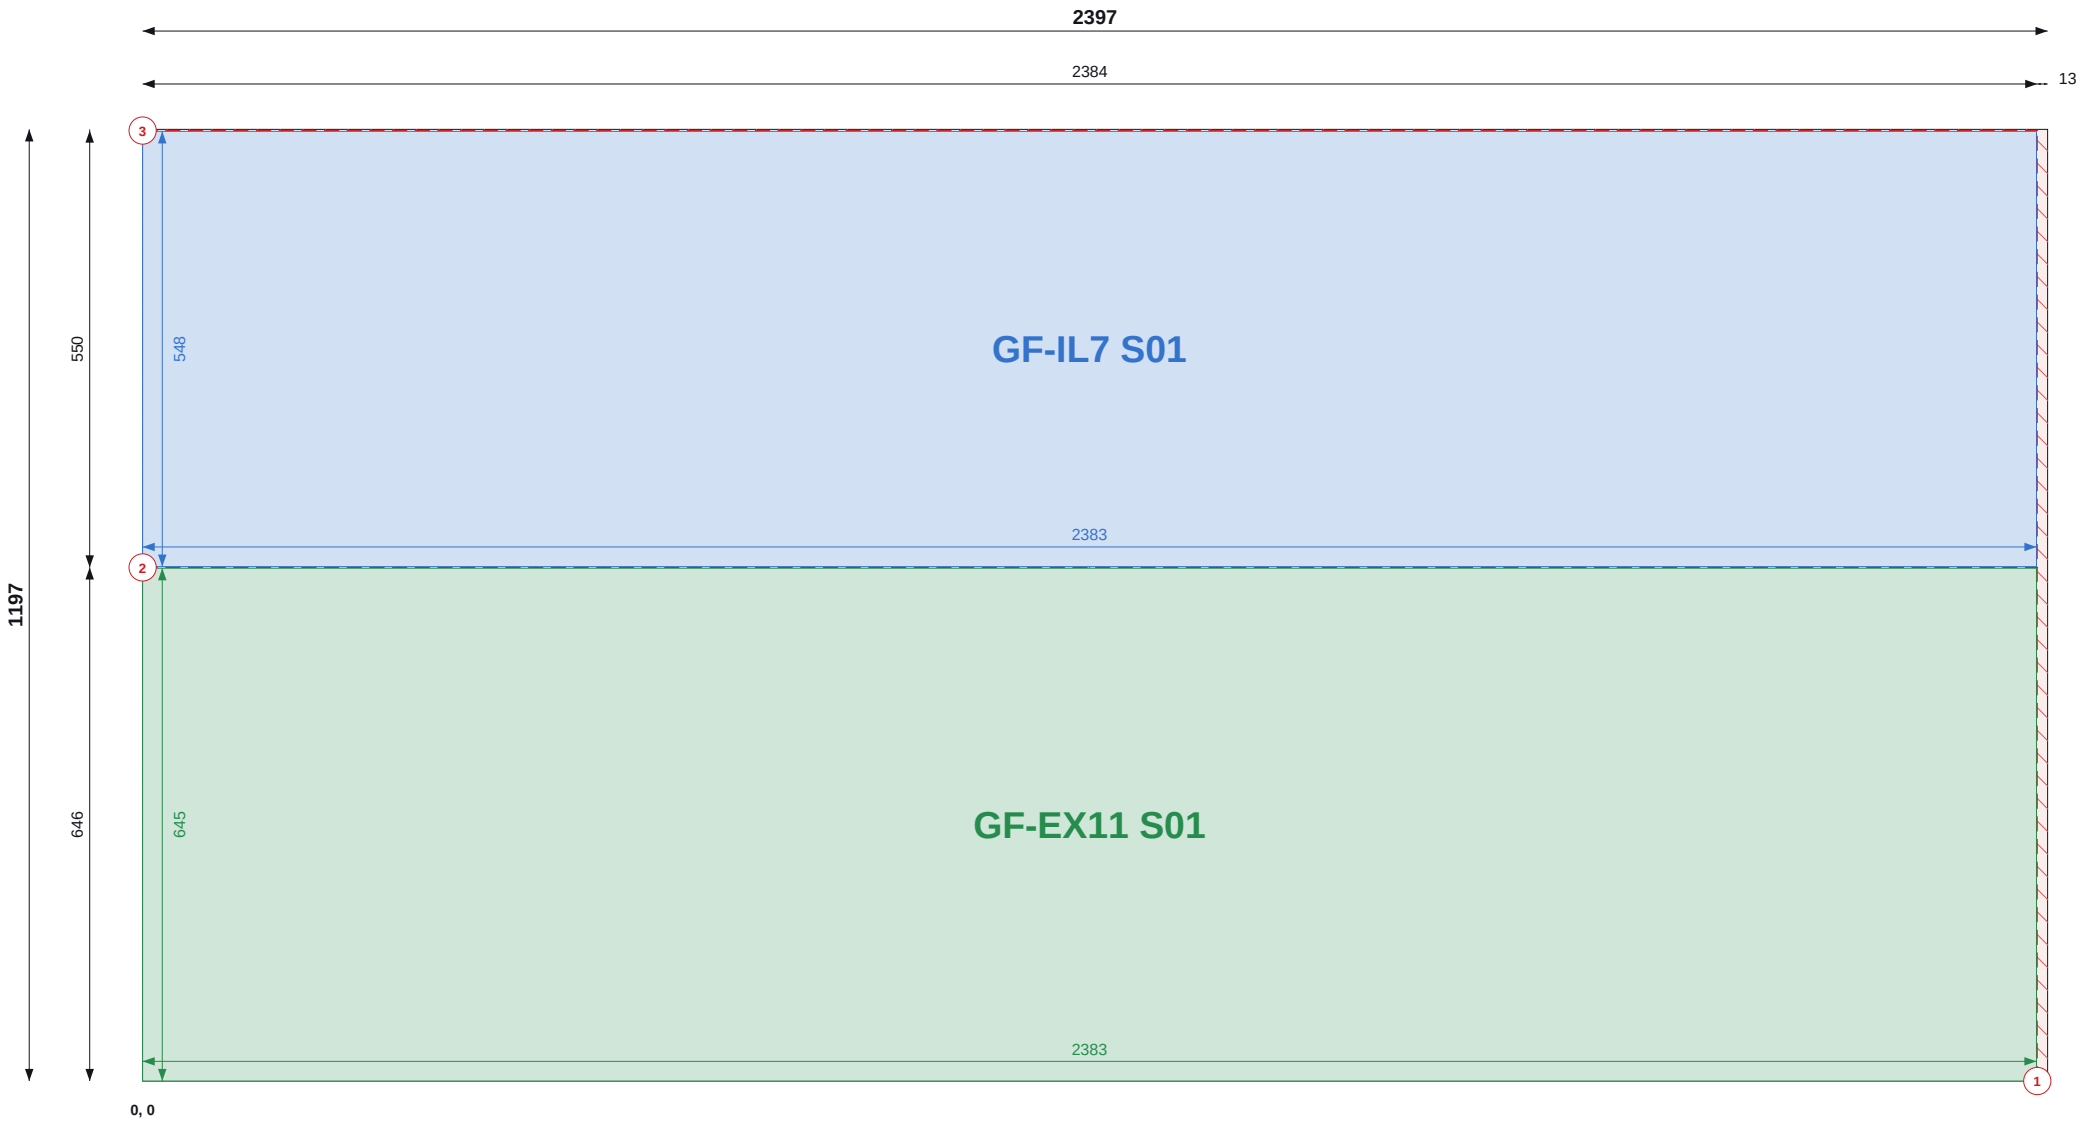

Top / left chains = saw cut positions (to cut centres). Coloured = part size and position.

SHEET 32 OF 38

THIS SHEET

Item	Value
Parts	2
Used / waste	99.0% / 0.03 m2
Reusable offcuts	0
Saw cuts / shared	3 / 1

PIECES (POSITION = BOTTOM-LEFT CORNER)

Label	Size	X, Y
GF-IL7 S01	548 x 2383	0, 647
GF-EX11 S01	645 x 2383	0, 0

NOTES

- Cut from OSB/3 9mm 1197x2397, 2mm saw kerf. Viewed on the face; dimensions from the sheet's bottom-left corner (0,0). Red numbered lines = saw cuts in order, each edge to edge.
- Coloured dimensions belong to the part of that colour: its width and height, and its position from the sheet edges. Raked parts: corner coordinates at each corner.
- Red hatch = waste. Labels = panel + piece mark on the manufacture drawing.

REVISIONS

REV	DATE	DESCRIPTION
C01	13.09.26	Construction issue



TLS TIMBER FRAME

Design & Manufacture

Scan: 3D model + drawings



CLIENT	PROJECT
MP Adams	MP Adams Plot 3, Eckington


DRAWING TITLE
OSB CUTTING - GROUND FLOOR - SHEET 32 OF 38

OSB/3 9mm 1197x2397 | Ground Floor

SCALE	SIZE	DATE	DRAWN
NTS	A3	13.09.26	TS

STATUS	DRAWING No.	REV
CONSTRUCTION	P3-CP-OSB-01 / 32	C01

Do not scale. All dimensions in mm. Check all dimensions on site.

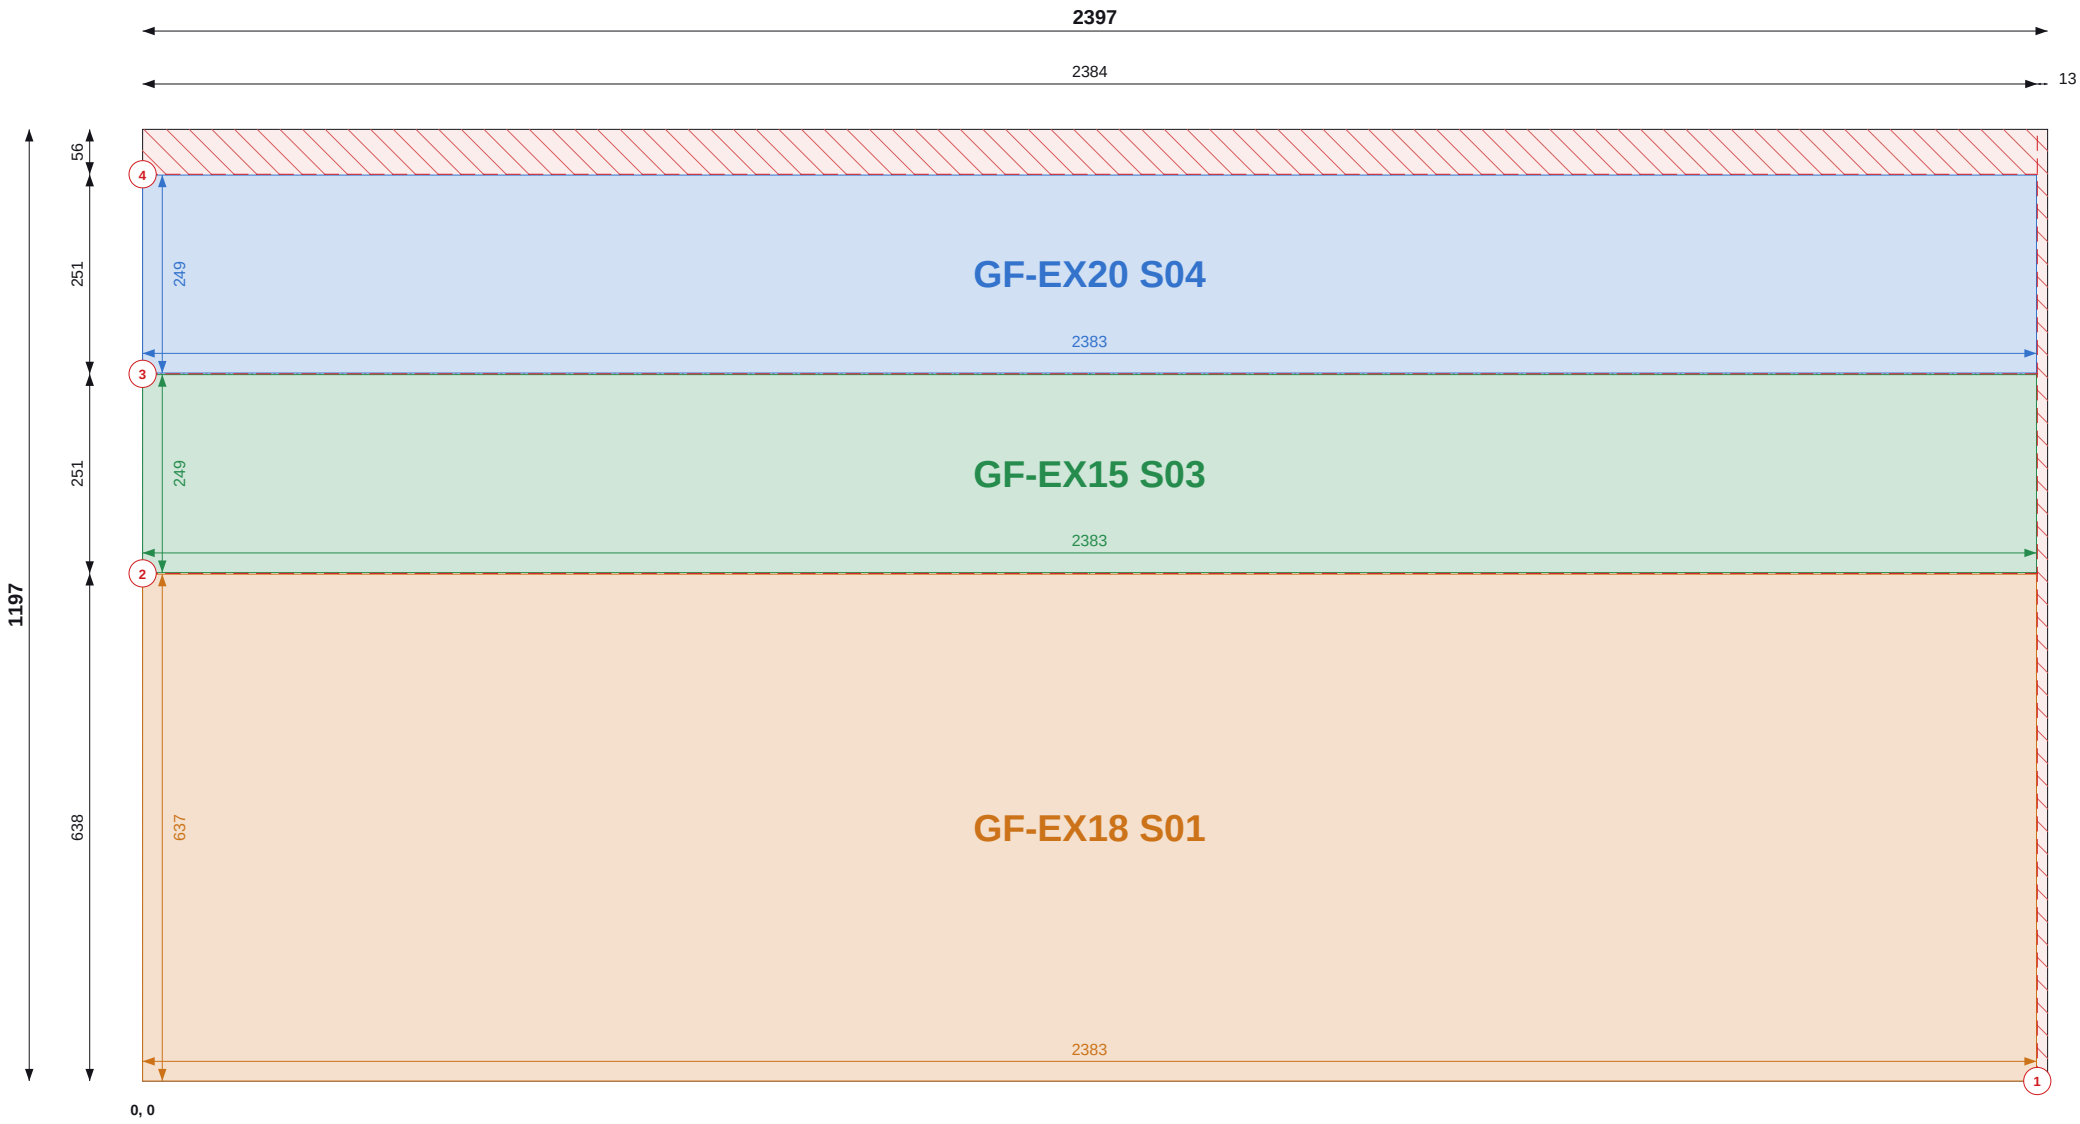

SHEET 33 OF 38

THIS SHEET

Item	Value
Parts	3
Used / waste	94.3% / 0.16 m2
Reusable offcuts	0
Saw cuts / shared	4 / 2

PIECES (POSITION = BOTTOM-LEFT CORNER)

Label	Size	X, Y
GF-EX20 S04	249 x 2383	0, 890
GF-EX15 S03	249 x 2383	0, 639
GF-EX18 S01	637 x 2383	0, 0

NOTES

- Cut from OSB/3 9mm 1197x2397, 2mm saw kerf. Viewed on the face; dimensions from the sheet's bottom-left corner (0,0). Red numbered lines = saw cuts in order, each edge to edge.
- Coloured dimensions belong to the part of that colour: its width and height, and its position from the sheet edges. Raked parts: corner coordinates at each corner.
- Red hatch = waste. Labels = panel + piece mark on the manufacture drawing.

REVISIONS

REV	DATE	DESCRIPTION
C01	13.09.26	Construction issue



TLS TIMBER FRAME

Design & Manufacture

Scan: 3D model + drawings



CLIENT	PROJECT
MP Adams	MP Adams Plot 3, Eckington


DRAWING TITLE
OSB CUTTING - GROUND FLOOR - SHEET 33 OF 38

OSB/3 9mm 1197x2397 | Ground Floor

SCALE	SIZE	DATE	DRAWN
NTS	A3	13.09.26	TS

STATUS	DRAWING No.	REV
CONSTRUCTION	P3-CP-OSB-01 / 33	C01

Do not scale. All dimensions in mm. Check all dimensions on site.

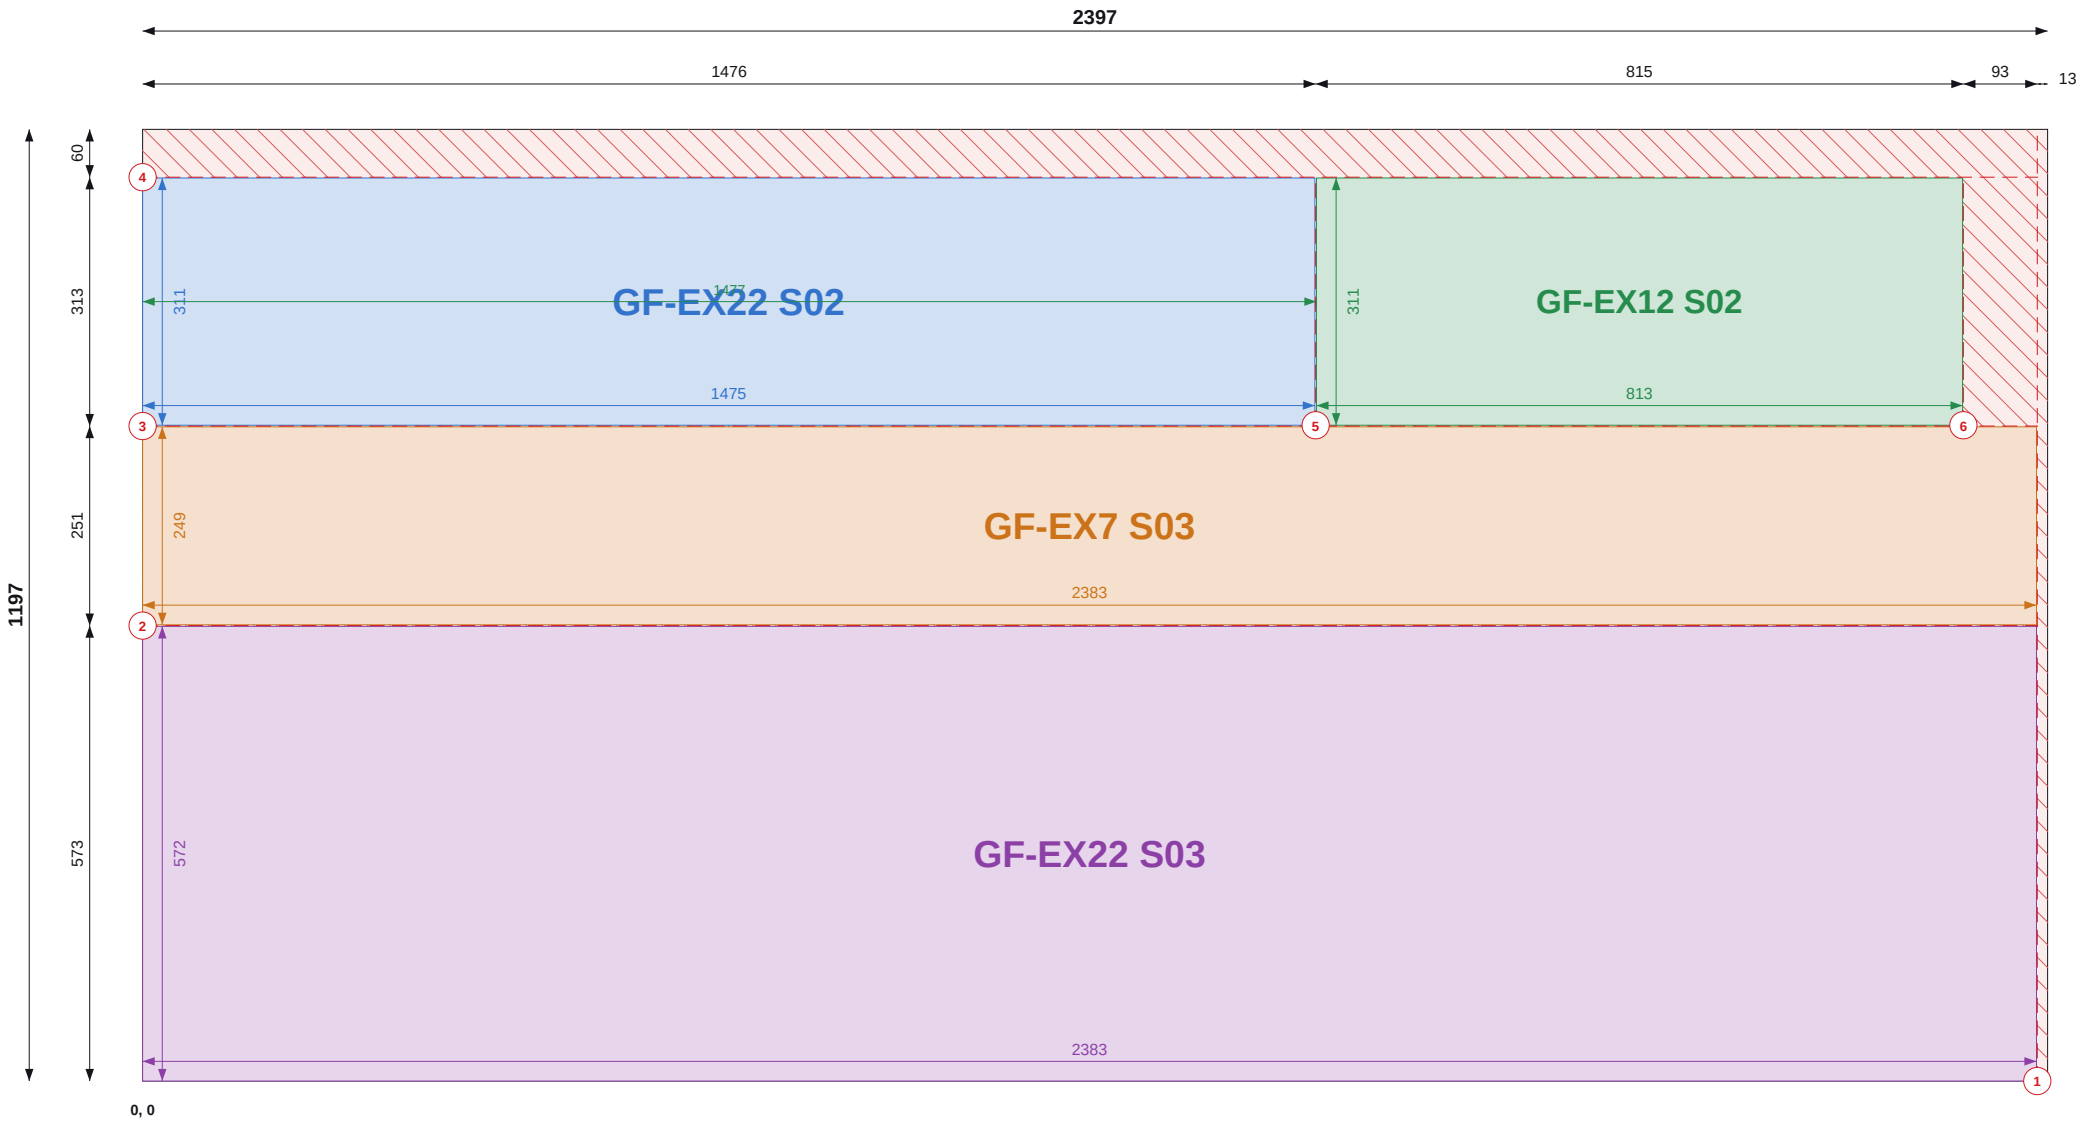

Top / left chains = saw cut positions (to cut centres). Coloured = part size and position.

SHEET 34 OF 38

THIS SHEET

Item	Value
Parts	4
Used / waste	93.0% / 0.20 m2
Reusable offcuts	0
Saw cuts / shared	6 / 3

PIECES (POSITION = BOTTOM-LEFT CORNER)

Label	Size	X, Y
GF-EX22 S02	1475 x 311	0, 825
GF-EX12 S02	813 x 311	1477, 825
GF-EX7 S03	249 x 2383	0, 574
GF-EX22 S03	572 x 2383	0, 0

NOTES

- Cut from OSB/3 9mm 1197x2397, 2mm saw kerf. Viewed on the face; dimensions from the sheet's bottom-left corner (0,0). Red numbered lines = saw cuts in order, each edge to edge.
- Coloured dimensions belong to the part of that colour: its width and height, and its position from the sheet edges. Raked parts: corner coordinates at each corner.
- Red hatch = waste. Labels = panel + piece mark on the manufacture drawing.

REVISIONS

REV	DATE	DESCRIPTION
C01	13.09.26	Construction issue



TLS TIMBER FRAME

Design & Manufacture

Scan: 3D model + drawings



CLIENT MP Adams	PROJECT MP Adams Plot 3, Eckington
--------------------	---------------------------------------


DRAWING TITLE
OSB CUTTING - GROUND FLOOR - SHEET 34 OF 38

OSB/3 9mm 1197x2397 | Ground Floor

SCALE NTS	SIZE A3	DATE 13.09.26	DRAWN TS
--------------	------------	------------------	-------------

STATUS CONSTRUCTION	DRAWING No. P3-CP-OSB-01 / 34	REV C01
------------------------	----------------------------------	------------

Do not scale. All dimensions in mm. Check all dimensions on site.

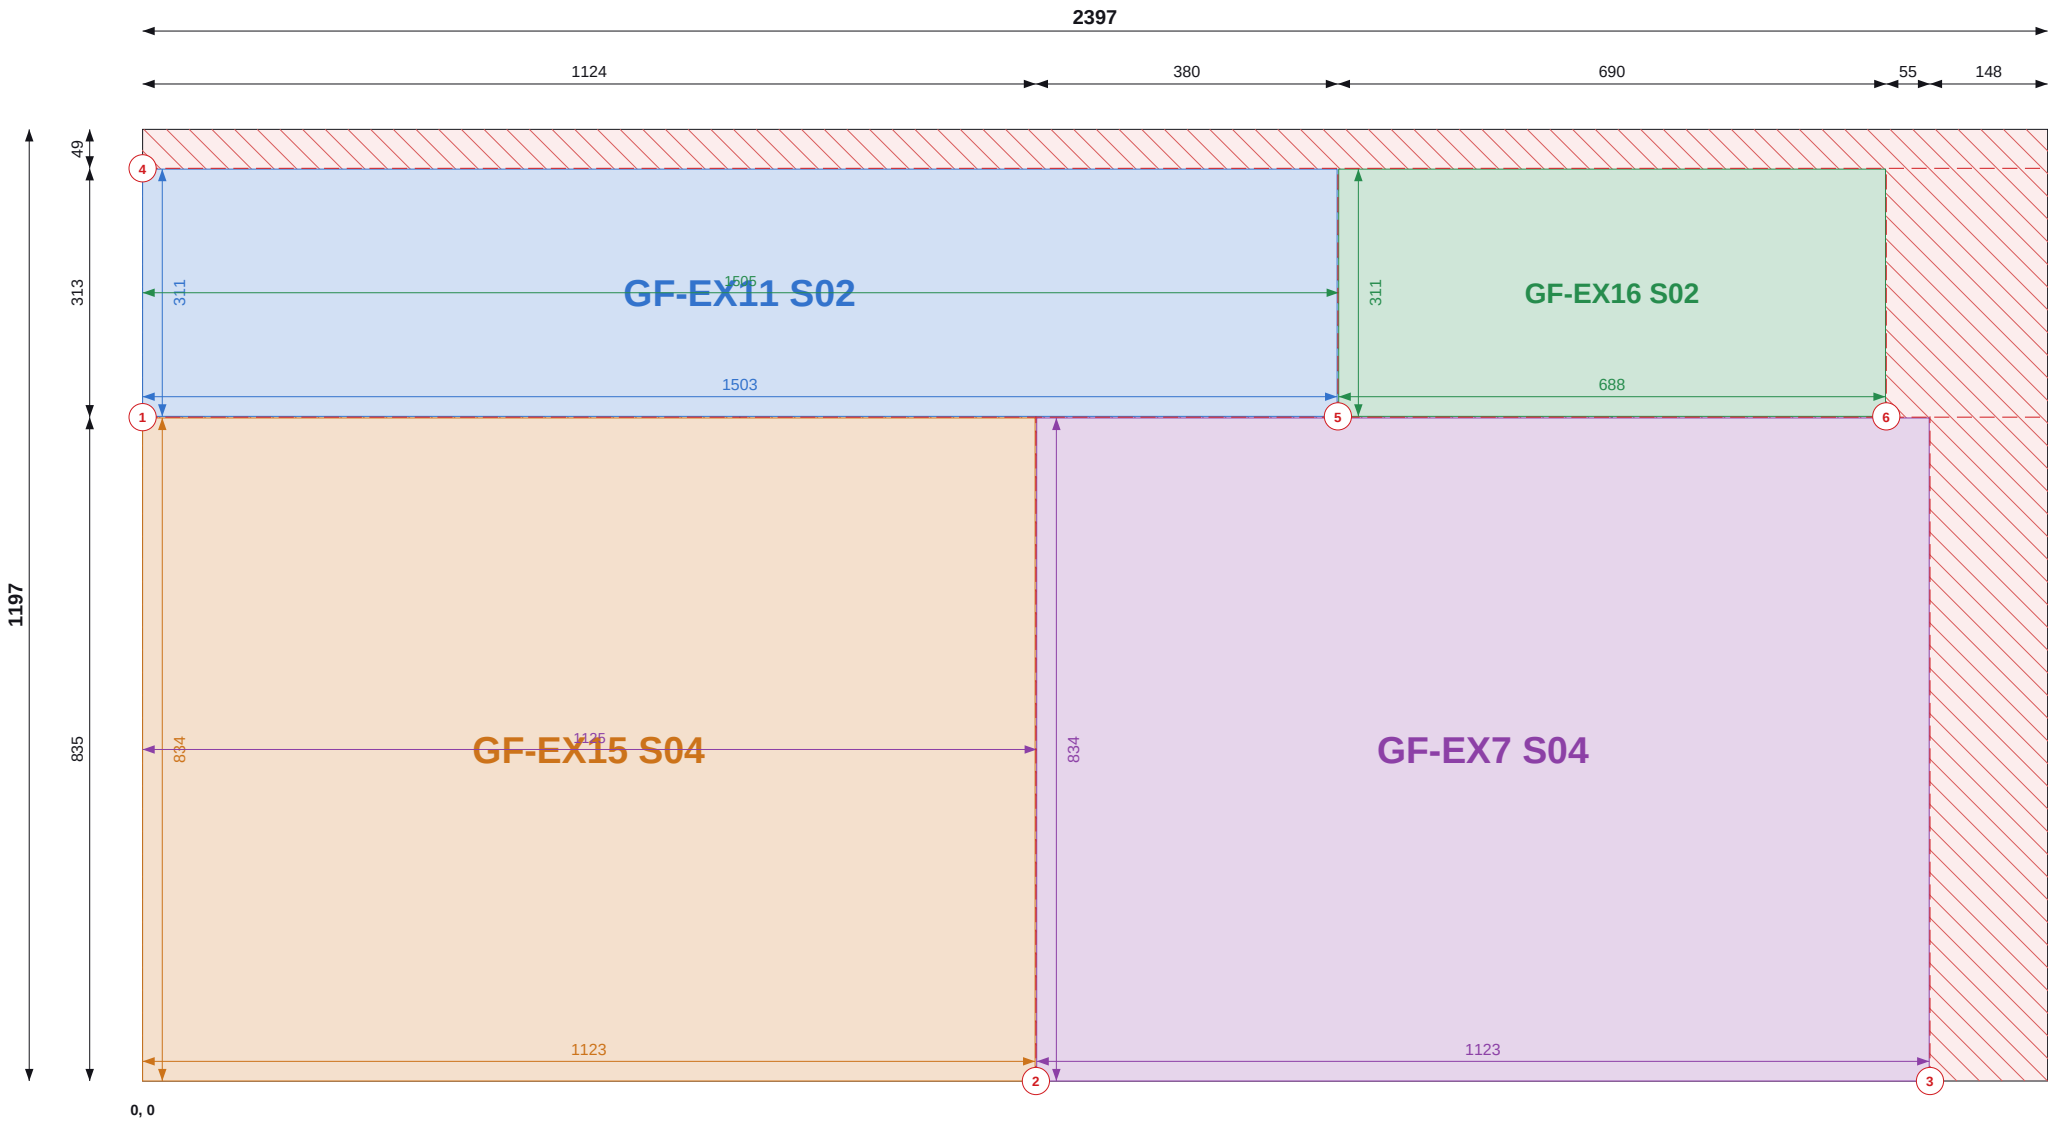

SHEET 35 OF 38

THIS SHEET

Item	Value
Parts	4
Used / waste	89.0% / 0.31 m2
Reusable offcuts	0
Saw cuts / shared	6 / 3

PIECES (POSITION = BOTTOM-LEFT CORNER)

Label	Size	X, Y
GF-EX11 S02	1503 x 311	0, 836
GF-EX16 S02	688 x 311	1505, 836
GF-EX15 S04	1123 x 834	0, 0
GF-EX7 S04	1123 x 834	1125, 0

NOTES

- Cut from OSB/3 9mm 1197x2397, 2mm saw kerf. Viewed on the face; dimensions from the sheet's bottom-left corner (0,0). Red numbered lines = saw cuts in order, each edge to edge.
- Coloured dimensions belong to the part of that colour: its width and height, and its position from the sheet edges. Raked parts: corner coordinates at each corner.
- Red hatch = waste. Labels = panel + piece mark on the manufacture drawing.

REVISIONS

REV	DATE	DESCRIPTION
C01	13.09.26	Construction issue



TLS TIMBER FRAME

Design & Manufacture

Scan: 3D model + drawings



CLIENT	PROJECT
MP Adams	MP Adams Plot 3, Eckington


DRAWING TITLE
OSB CUTTING - GROUND FLOOR - SHEET 35 OF 38

OSB/3 9mm 1197x2397 | Ground Floor

SCALE	SIZE	DATE	DRAWN
NTS	A3	13.09.26	TS

STATUS	DRAWING No.	REV
CONSTRUCTION	P3-CP-OSB-01 / 35	C01

Do not scale. All dimensions in mm. Check all dimensions on site.

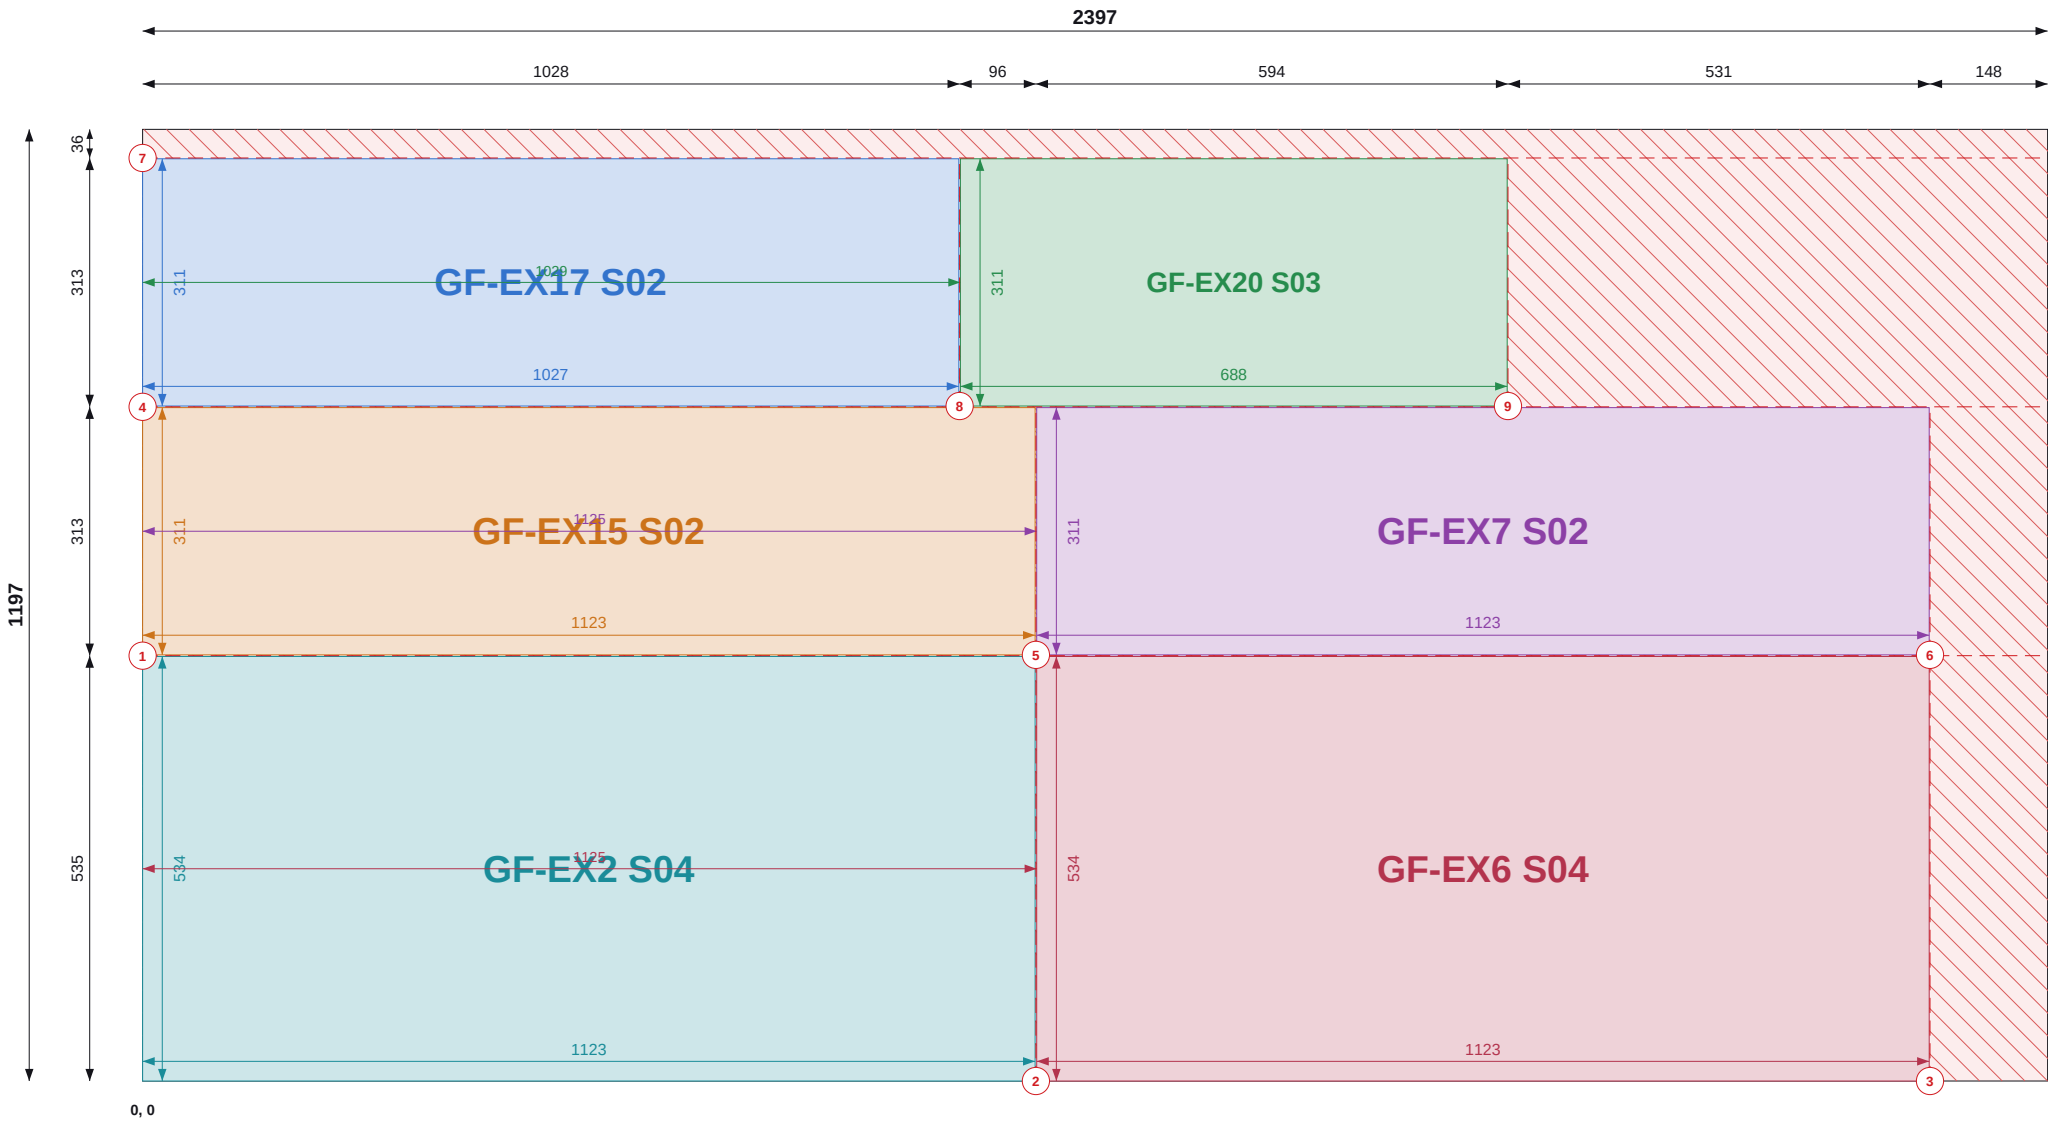

Top / left chains = saw cut positions (to cut centres). Coloured = part size and position.

SHEET 36 OF 38

THIS SHEET

Item	Value
Parts	6
Used / waste	84.7% / 0.44 m2
Reusable offcuts	1
Saw cuts / shared	9 / 5

PIECES (POSITION = BOTTOM-LEFT CORNER)

Label	Size	X, Y
GF-EX17 S02	1027 x 311	0, 849
GF-EX20 S03	688 x 311	1029, 849
GF-EX15 S02	1123 x 311	0, 536
GF-EX7 S02	1123 x 311	1125, 536
GF-EX2 S04	1123 x 534	0, 0
GF-EX6 S04	1123 x 534	1125, 0

NOTES

- Cut from OSB/3 9mm 1197x2397, 2mm saw kerf. Viewed on the face; dimensions from the sheet's bottom-left corner (0,0). Red numbered lines = saw cuts in order, each edge to edge.
- Coloured dimensions belong to the part of that colour: its width and height, and its position from the sheet edges. Raked parts: corner coordinates at each corner.
- Red hatch = waste. Labels = panel + piece mark on the manufacture drawing.

REVISIONS

REV	DATE	DESCRIPTION
C01	13.09.26	Construction issue



TLS TIMBER FRAME

Design & Manufacture

Scan: 3D model + drawings



CLIENT	PROJECT
MP Adams	MP Adams Plot 3, Eckington


DRAWING TITLE
OSB CUTTING - GROUND FLOOR - SHEET 36 OF 38

OSB/3 9mm 1197x2397 | Ground Floor

SCALE	SIZE	DATE	DRAWN
NTS	A3	13.09.26	TS

STATUS	DRAWING No.	REV
CONSTRUCTION	P3-CP-OSB-01 / 36	C01

Do not scale. All dimensions in mm. Check all dimensions on site.

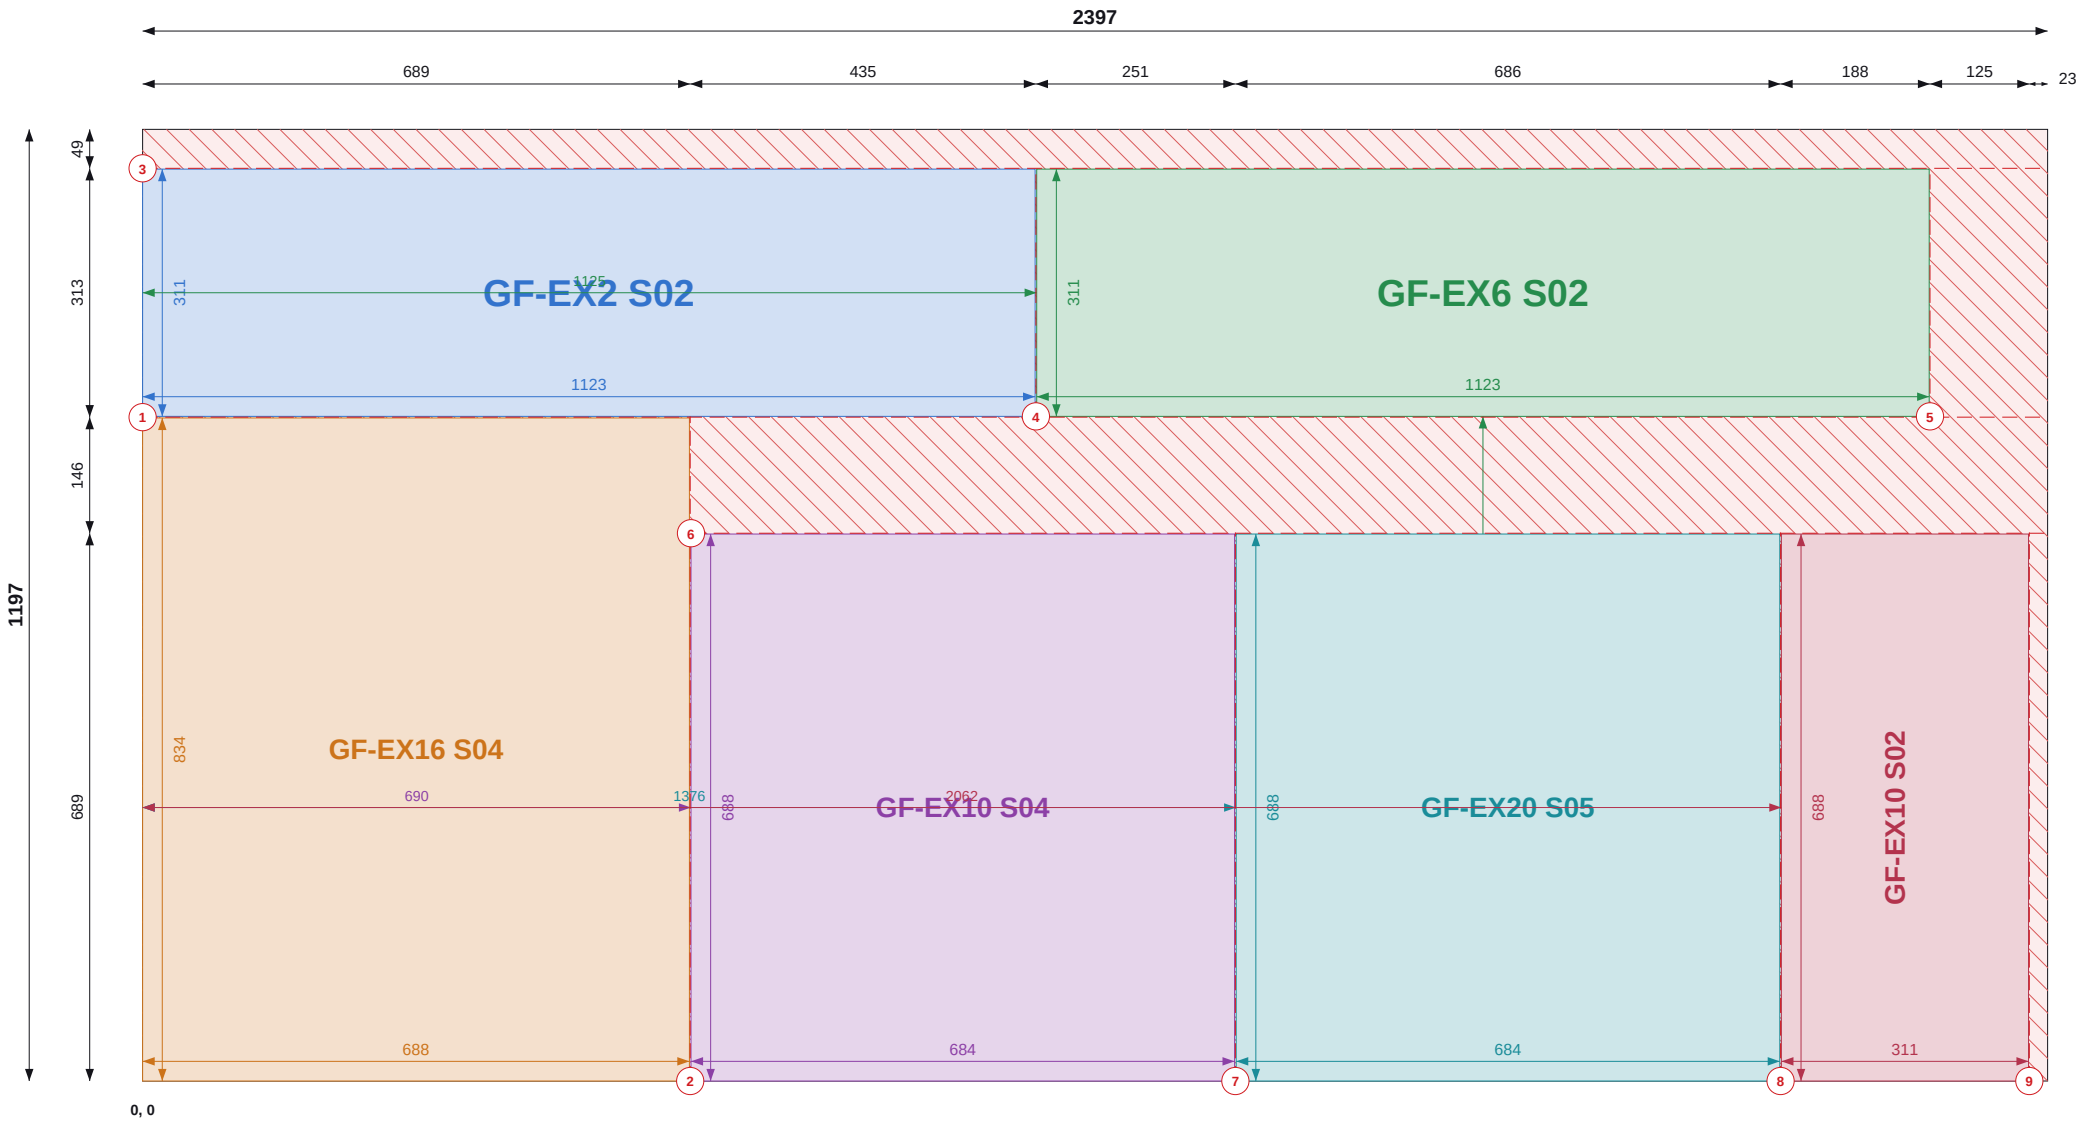

Top / left chains = saw cut positions (to cut centres). Coloured = part size and position.

SHEET 37 OF 38

THIS SHEET

Item	Value
Parts	6
Used / waste	84.6% / 0.44 m2
Reusable offcuts	0
Saw cuts / shared	9 / 5

PIECES (POSITION = BOTTOM-LEFT CORNER)

Label	Size	X, Y
GF-EX2 S02	1123 x 311	0, 836
GF-EX6 S02	1123 x 311	1125, 836
GF-EX16 S04	688 x 834	0, 0
GF-EX10 S04	688 x 684	690, 0
GF-EX20 S05	688 x 684	1376, 0
GF-EX10 S02	688 x 311	2062, 0

NOTES

- Cut from OSB/3 9mm 1197x2397, 2mm saw kerf. Viewed on the face; dimensions from the sheet's bottom-left corner (0,0). Red numbered lines = saw cuts in order, each edge to edge.
- Coloured dimensions belong to the part of that colour: its width and height, and its position from the sheet edges. Raked parts: corner coordinates at each corner.
- Red hatch = waste. Labels = panel + piece mark on the manufacture drawing.

REVISIONS

REV	DATE	DESCRIPTION
C01	13.09.26	Construction issue



TLS TIMBER FRAME

Design & Manufacture

Scan: 3D model + drawings



CLIENT MP Adams	PROJECT MP Adams Plot 3, Eckington
--------------------	---------------------------------------


DRAWING TITLE OSB CUTTING - GROUND FLOOR - SHEET 37 OF 38

OSB/3 9mm 1197x2397 | Ground Floor

SCALE NTS	SIZE A3	DATE 13.09.26	DRAWN TS
--------------	------------	------------------	-------------

STATUS CONSTRUCTION	DRAWING No. P3-CP-OSB-01 / 37	REV C01
-------------------------------	---	-------------------

Do not scale. All dimensions in mm. Check all dimensions on site.

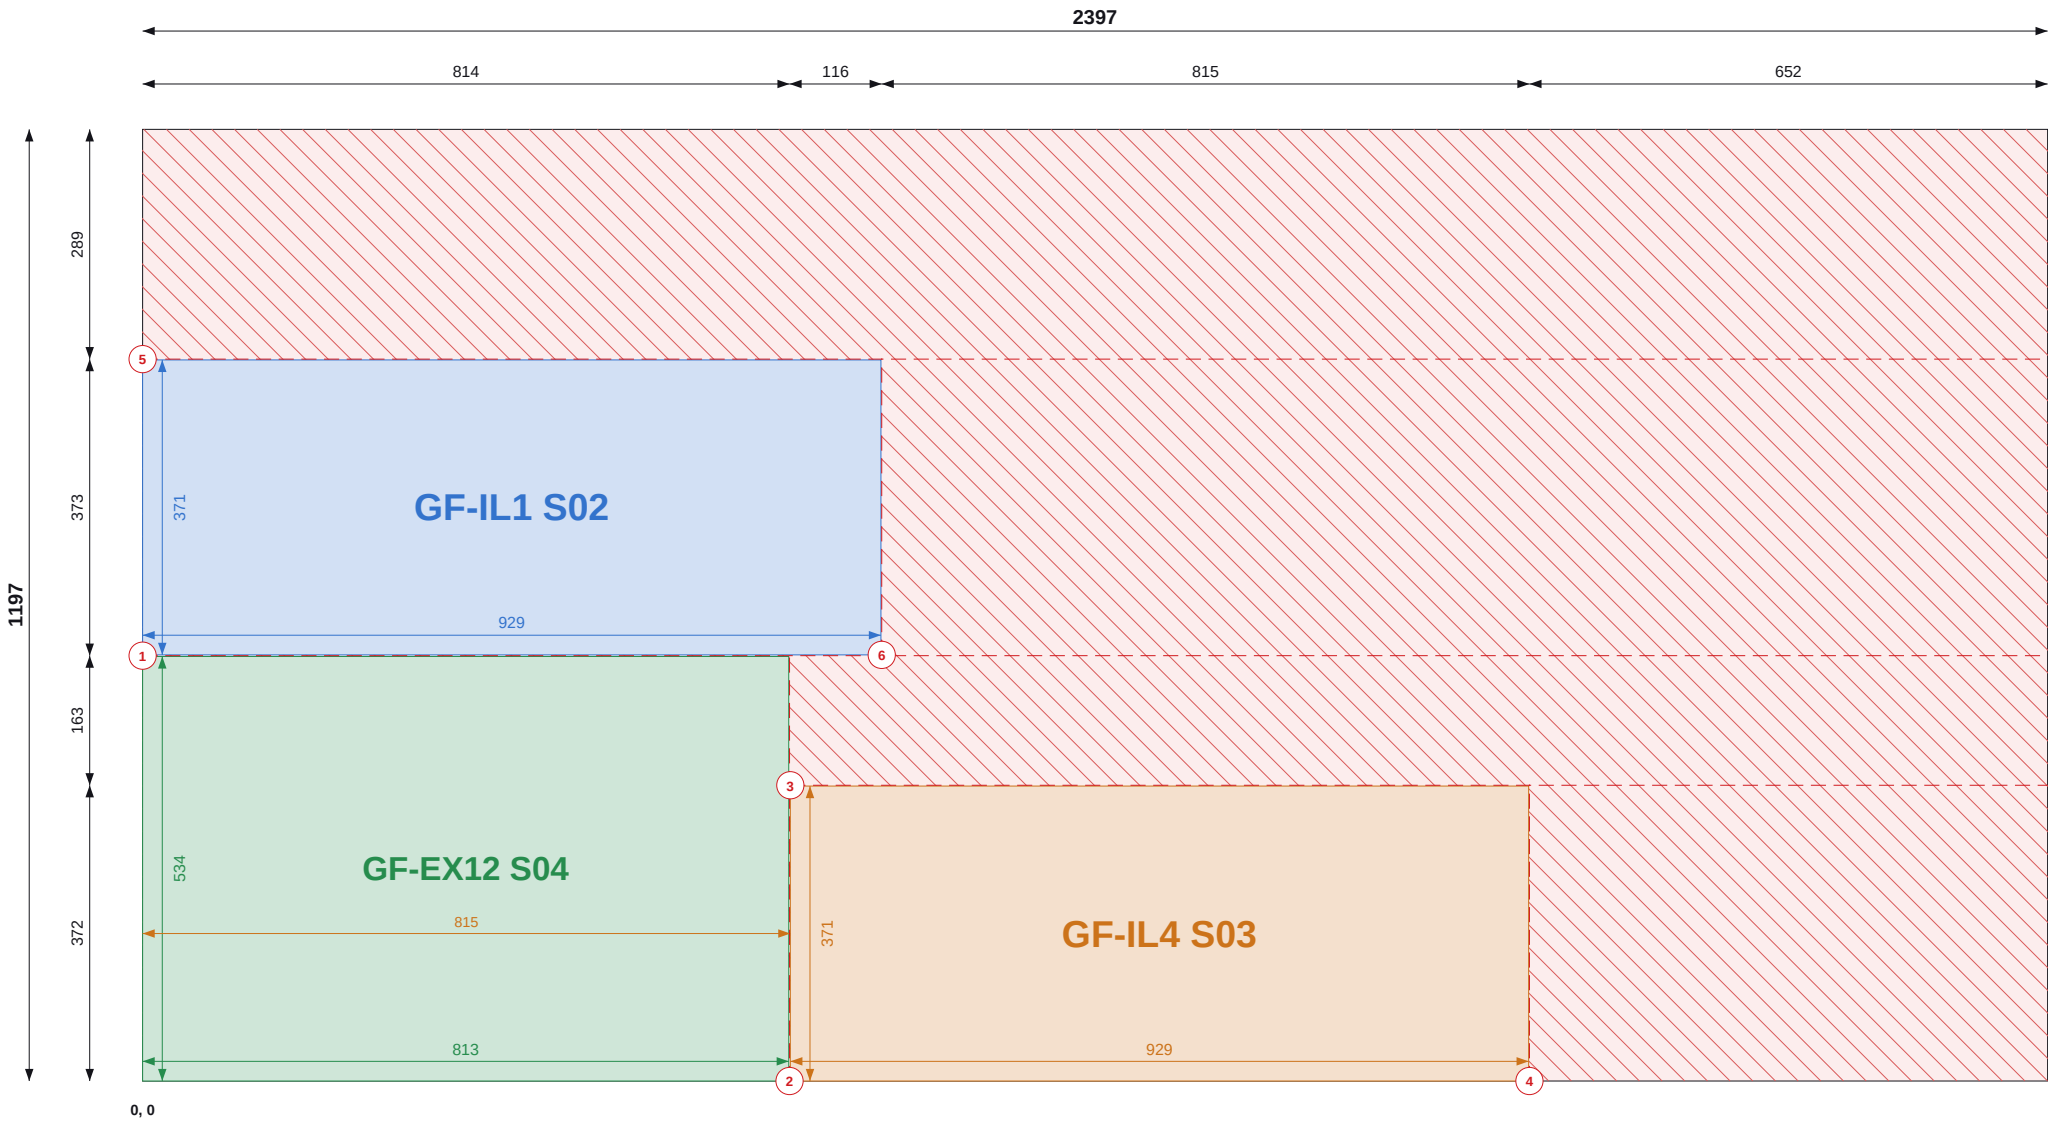

SHEET 38 OF 38

THIS SHEET

Item	Value
Parts	3
Used / waste	39.2% / 1.75 m2
Reusable offcuts	2
Saw cuts / shared	6 / 2

PIECES (POSITION = BOTTOM-LEFT CORNER)

Label	Size	X, Y
GF-IL1 S02	929 x 371	0, 536
GF-EX12 S04	813 x 534	0, 0
GF-IL4 S03	929 x 371	815, 0

NOTES

- Cut from OSB/3 9mm 1197x2397, 2mm saw kerf. Viewed on the face; dimensions from the sheet's bottom-left corner (0,0). Red numbered lines = saw cuts in order, each edge to edge.
- Coloured dimensions belong to the part of that colour: its width and height, and its position from the sheet edges. Raked parts: corner coordinates at each corner.
- Red hatch = waste. Labels = panel + piece mark on the manufacture drawing.

REVISIONS

REV	DATE	DESCRIPTION
C01	13.09.26	Construction issue



TLS TIMBER FRAME
Design & Manufacture
Scan: 3D model + drawings



CLIENT MP Adams	PROJECT MP Adams Plot 3, Eckington
--------------------	---------------------------------------


DRAWING TITLE
OSB CUTTING - GROUND FLOOR - SHEET 38 OF 38

OSB/3 9mm 1197x2397 | Ground Floor

SCALE NTS	SIZE A3	DATE 13.09.26	DRAWN TS
--------------	------------	------------------	-------------

STATUS CONSTRUCTION	DRAWING No. P3-CP-OSB-01 / 38	REV C01
-------------------------------	---	-------------------

Do not scale. All dimensions in mm. Check all dimensions on site.

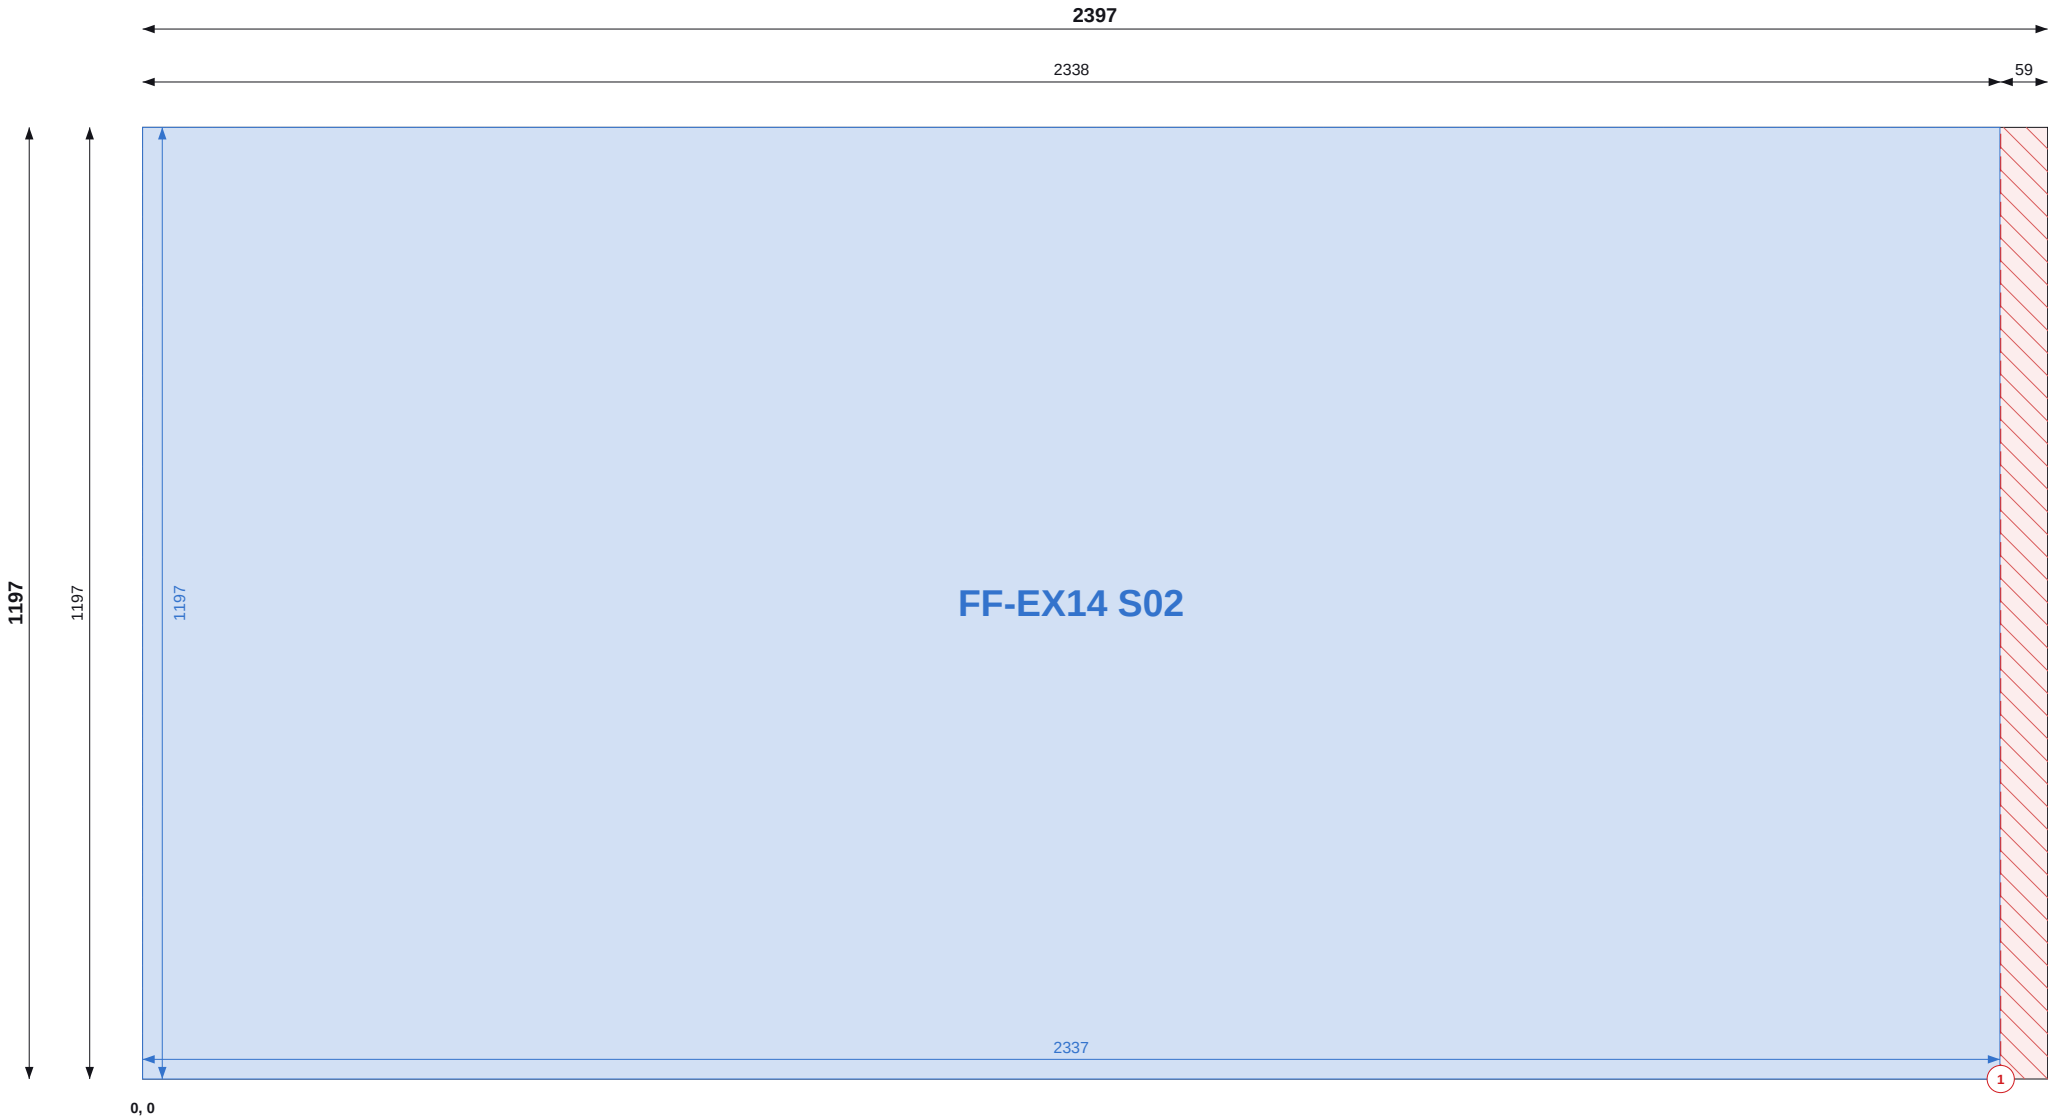

SHEET 1 OF 34

THIS SHEET

Item	Value
Parts	1
Used / waste	97.5% / 0.07 m2
Reusable offcuts	0
Saw cuts / shared	1 / 0

PIECES (POSITION = BOTTOM-LEFT CORNER)

Label	Size	X, Y
FF-EX14 S02	1197 x 2337	0, 0

FIRST FLOOR TOTALS

Item	Value
Sheets / pieces	34 / 67
Yield / waste	90.3% / 9.42 m2
Saw cuts / shared / on stock edge	104 / 33 / 105

NOTES

- Cut from OSB/3 9mm 1197x2397, 2mm saw kerf. Viewed on the face; dimensions from the sheet's bottom-left corner (0,0). Red numbered lines = saw cuts in order, each edge to edge.
- Coloured dimensions belong to the part of that colour: its width and height, and its position from the sheet edges. Raked parts: corner coordinates at each corner.
- Red hatch = waste. Labels = panel + piece mark on the manufacture drawing.

REVISIONS

REV	DATE	DESCRIPTION
C01	13.09.26	Construction issue



TLS TIMBER FRAME

Design & Manufacture

Scan: 3D model + drawings



CLIENT	PROJECT
MP Adams	MP Adams Plot 3, Eckington

DRAWING TITLE			
OSB CUTTING - FIRST FLOOR - SHEET 1 OF 34			
OSB/3 9mm 1197x2397 First Floor			

SCALE	SIZE	DATE	DRAWN
NTS	A3	13.09.26	TS

STATUS	DRAWING No.	REV
CONSTRUCTION	P3-CP-OSB-02 / 01	C01

Do not scale. All dimensions in mm. Check all dimensions on site.



SHEET 2 OF 34

THIS SHEET

Item	Value
Parts	1
Used / waste	97.5% / 0.07 m2
Reusable offcuts	0
Saw cuts / shared	1 / 0

PIECES (POSITION = BOTTOM-LEFT CORNER)

Label	Size	X, Y
FF-IL2 S02	1197 x 2337	0, 0

NOTES

- Cut from OSB/3 9mm 1197x2397, 2mm saw kerf. Viewed on the face; dimensions from the sheet's bottom-left corner (0,0). Red numbered lines = saw cuts in order, each edge to edge.
- Coloured dimensions belong to the part of that colour: its width and height, and its position from the sheet edges. Raked parts: corner coordinates at each corner.
- Red hatch = waste. Labels = panel + piece mark on the manufacture drawing.

REVISIONS

REV	DATE	DESCRIPTION
C01	13.09.26	Construction issue



TLS TIMBER FRAME

Design & Manufacture

Scan: 3D model + drawings



CLIENT	PROJECT
MP Adams	MP Adams Plot 3, Eckington


DRAWING TITLE
OSB CUTTING - FIRST FLOOR - SHEET 2 OF 34

OSB/3 9mm 1197x2397 | First Floor

SCALE	SIZE	DATE	DRAWN
NTS	A3	13.09.26	TS

STATUS	DRAWING No.	REV
CONSTRUCTION	P3-CP-OSB-02 / 02	C01

Do not scale. All dimensions in mm. Check all dimensions on site.

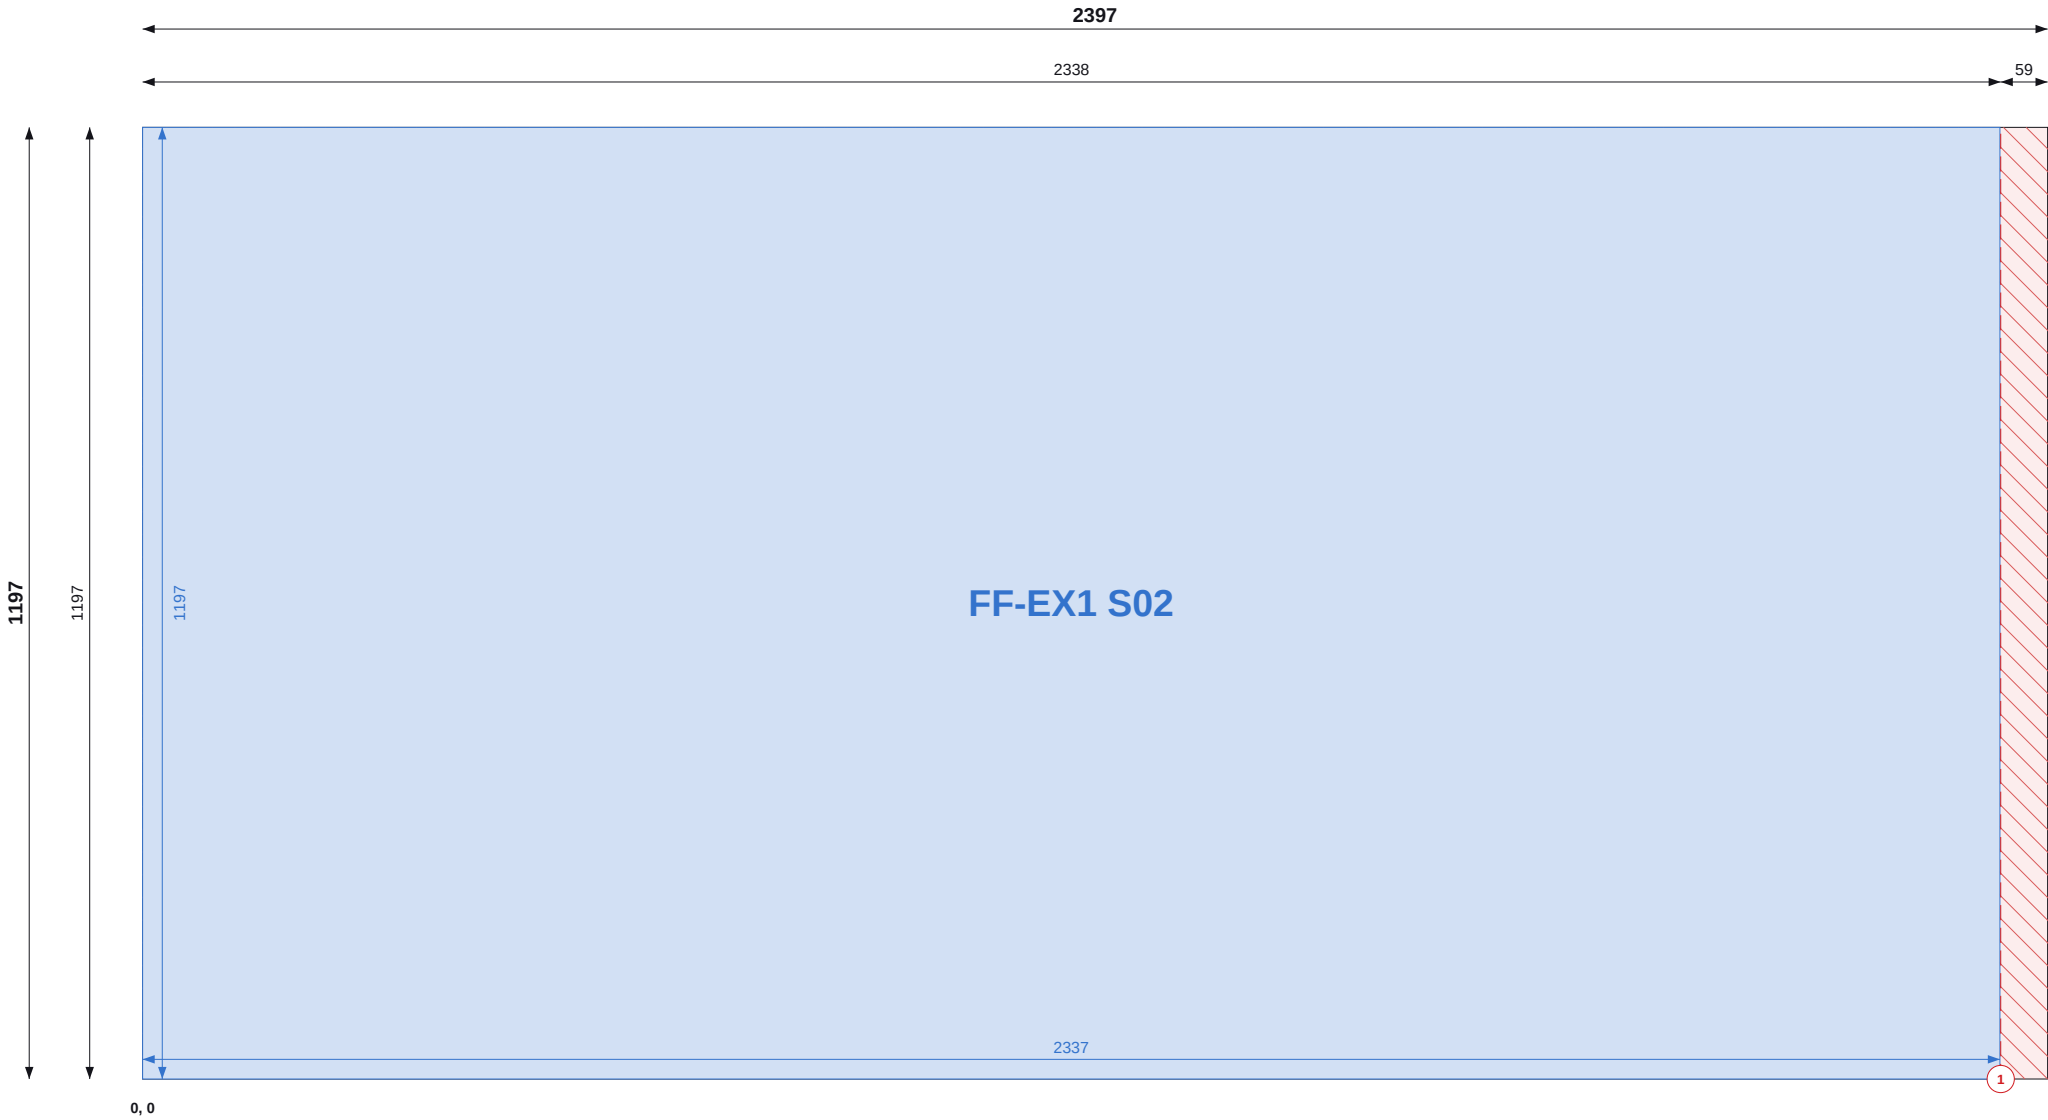

Top / left chains = saw cut positions (to cut centres). Coloured = part size and position.

SHEET 3 OF 34

THIS SHEET

Item	Value
Parts	1
Used / waste	97.5% / 0.07 m2
Reusable offcuts	0
Saw cuts / shared	1 / 0

PIECES (POSITION = BOTTOM-LEFT CORNER)

Label	Size	X, Y
FF-EX1 S02	1197 x 2337	0, 0

NOTES

- Cut from OSB/3 9mm 1197x2397, 2mm saw kerf. Viewed on the face; dimensions from the sheet's bottom-left corner (0,0). Red numbered lines = saw cuts in order, each edge to edge.
- Coloured dimensions belong to the part of that colour: its width and height, and its position from the sheet edges. Raked parts: corner coordinates at each corner.
- Red hatch = waste. Labels = panel + piece mark on the manufacture drawing.

REVISIONS

REV	DATE	DESCRIPTION
C01	13.09.26	Construction issue



TLS TIMBER FRAME

Design & Manufacture

Scan: 3D model + drawings



CLIENT	PROJECT
MP Adams	MP Adams Plot 3, Eckington


DRAWING TITLE
OSB CUTTING - FIRST FLOOR - SHEET 3 OF 34

OSB/3 9mm 1197x2397 | First Floor

SCALE	SIZE	DATE	DRAWN
NTS	A3	13.09.26	TS

STATUS	DRAWING No.	REV
CONSTRUCTION	P3-CP-OSB-02 / 03	C01

Do not scale. All dimensions in mm. Check all dimensions on site.

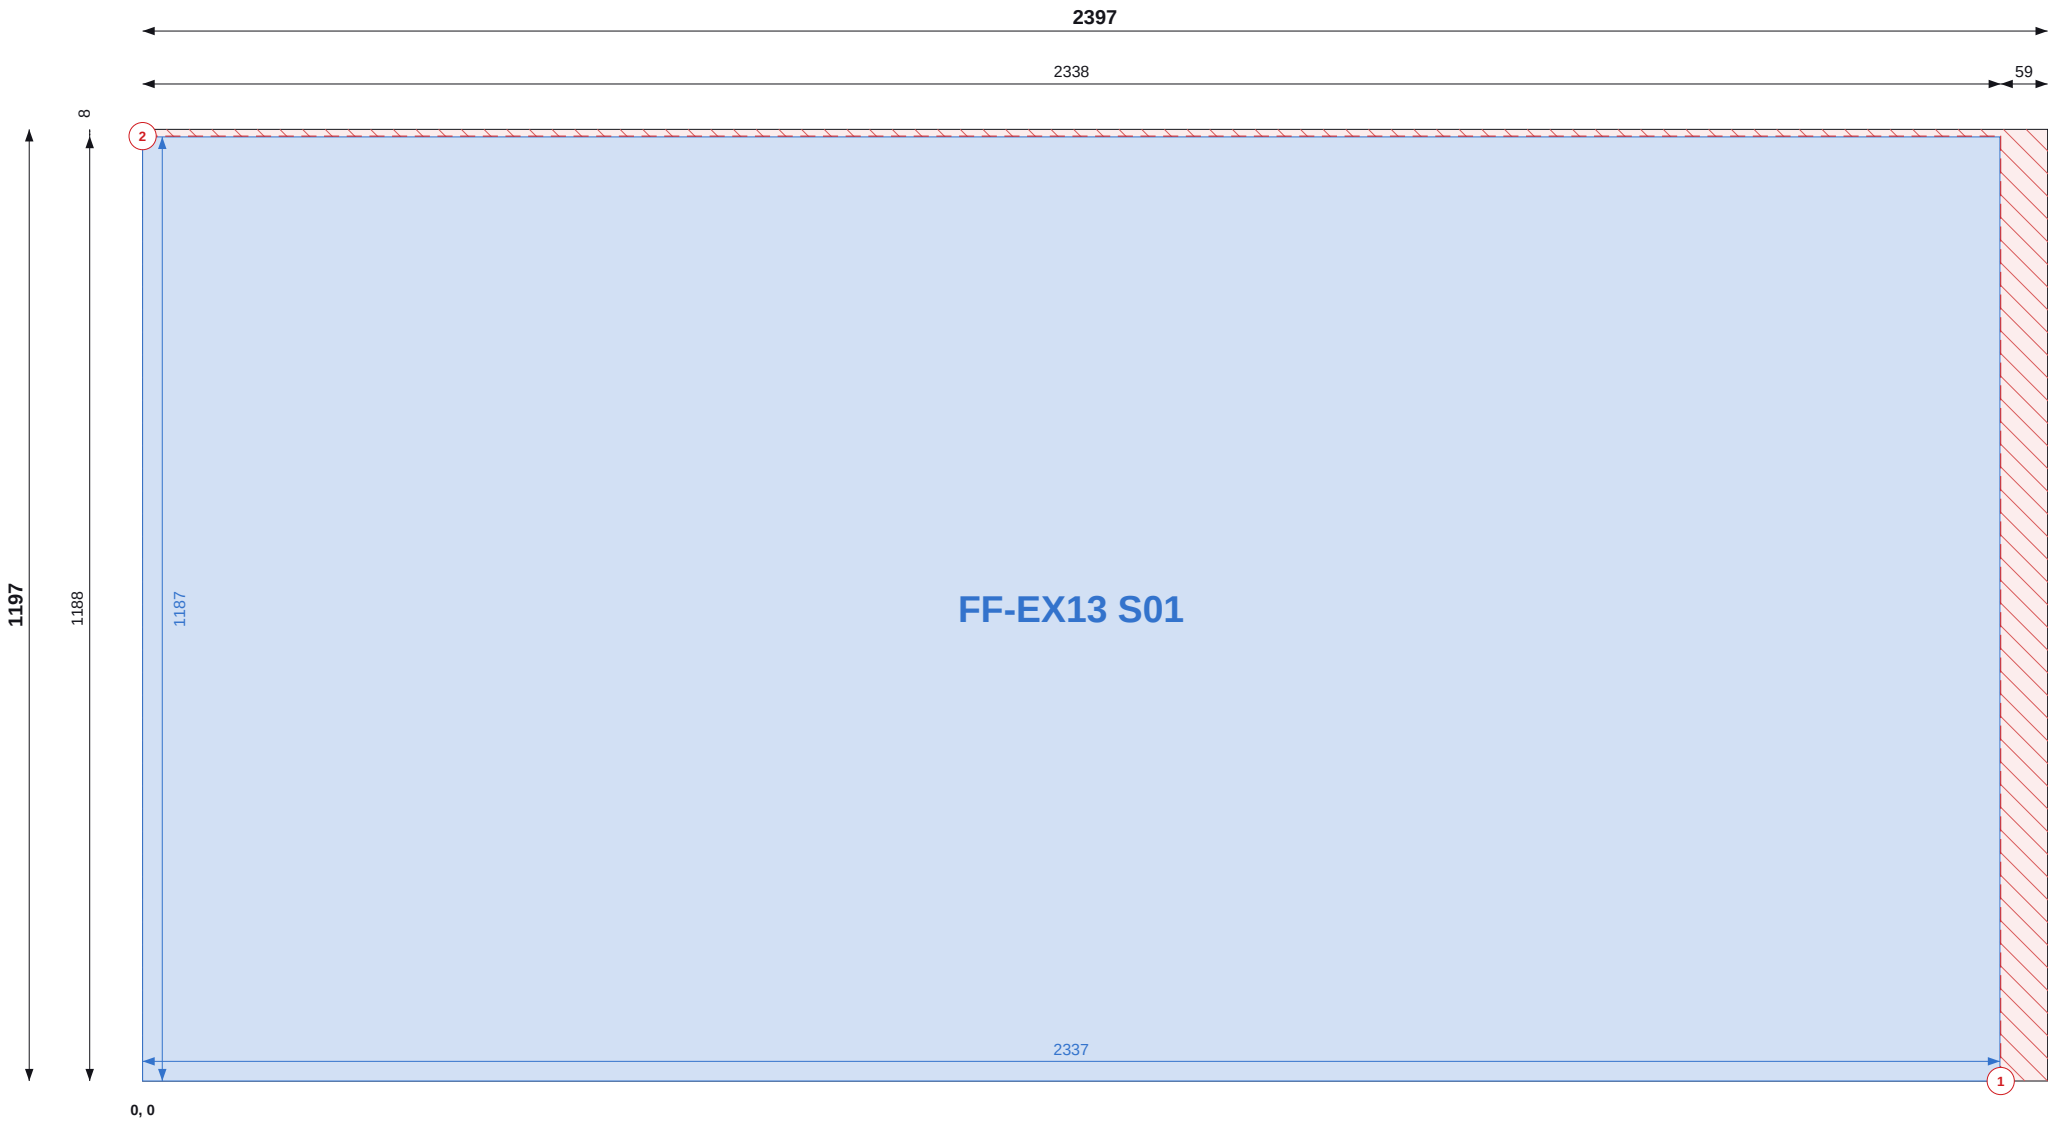

Top / left chains = saw cut positions (to cut centres). Coloured = part size and position.

SHEET 4 OF 34

THIS SHEET

Item	Value
Parts	1
Used / waste	96.7% / 0.09 m2
Reusable offcuts	0
Saw cuts / shared	2 / 0

PIECES (POSITION = BOTTOM-LEFT CORNER)

Label	Size	X, Y
FF-EX13 S01	1187 x 2337	0, 0

NOTES

- Cut from OSB/3 9mm 1197x2397, 2mm saw kerf. Viewed on the face; dimensions from the sheet's bottom-left corner (0,0). Red numbered lines = saw cuts in order, each edge to edge.
- Coloured dimensions belong to the part of that colour: its width and height, and its position from the sheet edges. Raked parts: corner coordinates at each corner.
- Red hatch = waste. Labels = panel + piece mark on the manufacture drawing.

REVISIONS

REV	DATE	DESCRIPTION
C01	13.09.26	Construction issue



TLS TIMBER FRAME

Design & Manufacture

Scan: 3D model + drawings




CLIENT	PROJECT
MP Adams	MP Adams Plot 3, Eckington

DRAWING TITLE			
OSB CUTTING - FIRST FLOOR - SHEET 4 OF 34			
OSB/3 9mm 1197x2397 First Floor			

SCALE	SIZE	DATE	DRAWN
NTS	A3	13.09.26	TS

STATUS	DRAWING No.	REV
CONSTRUCTION	P3-CP-OSB-02 / 04	C01

Do not scale. All dimensions in mm. Check all dimensions on site.

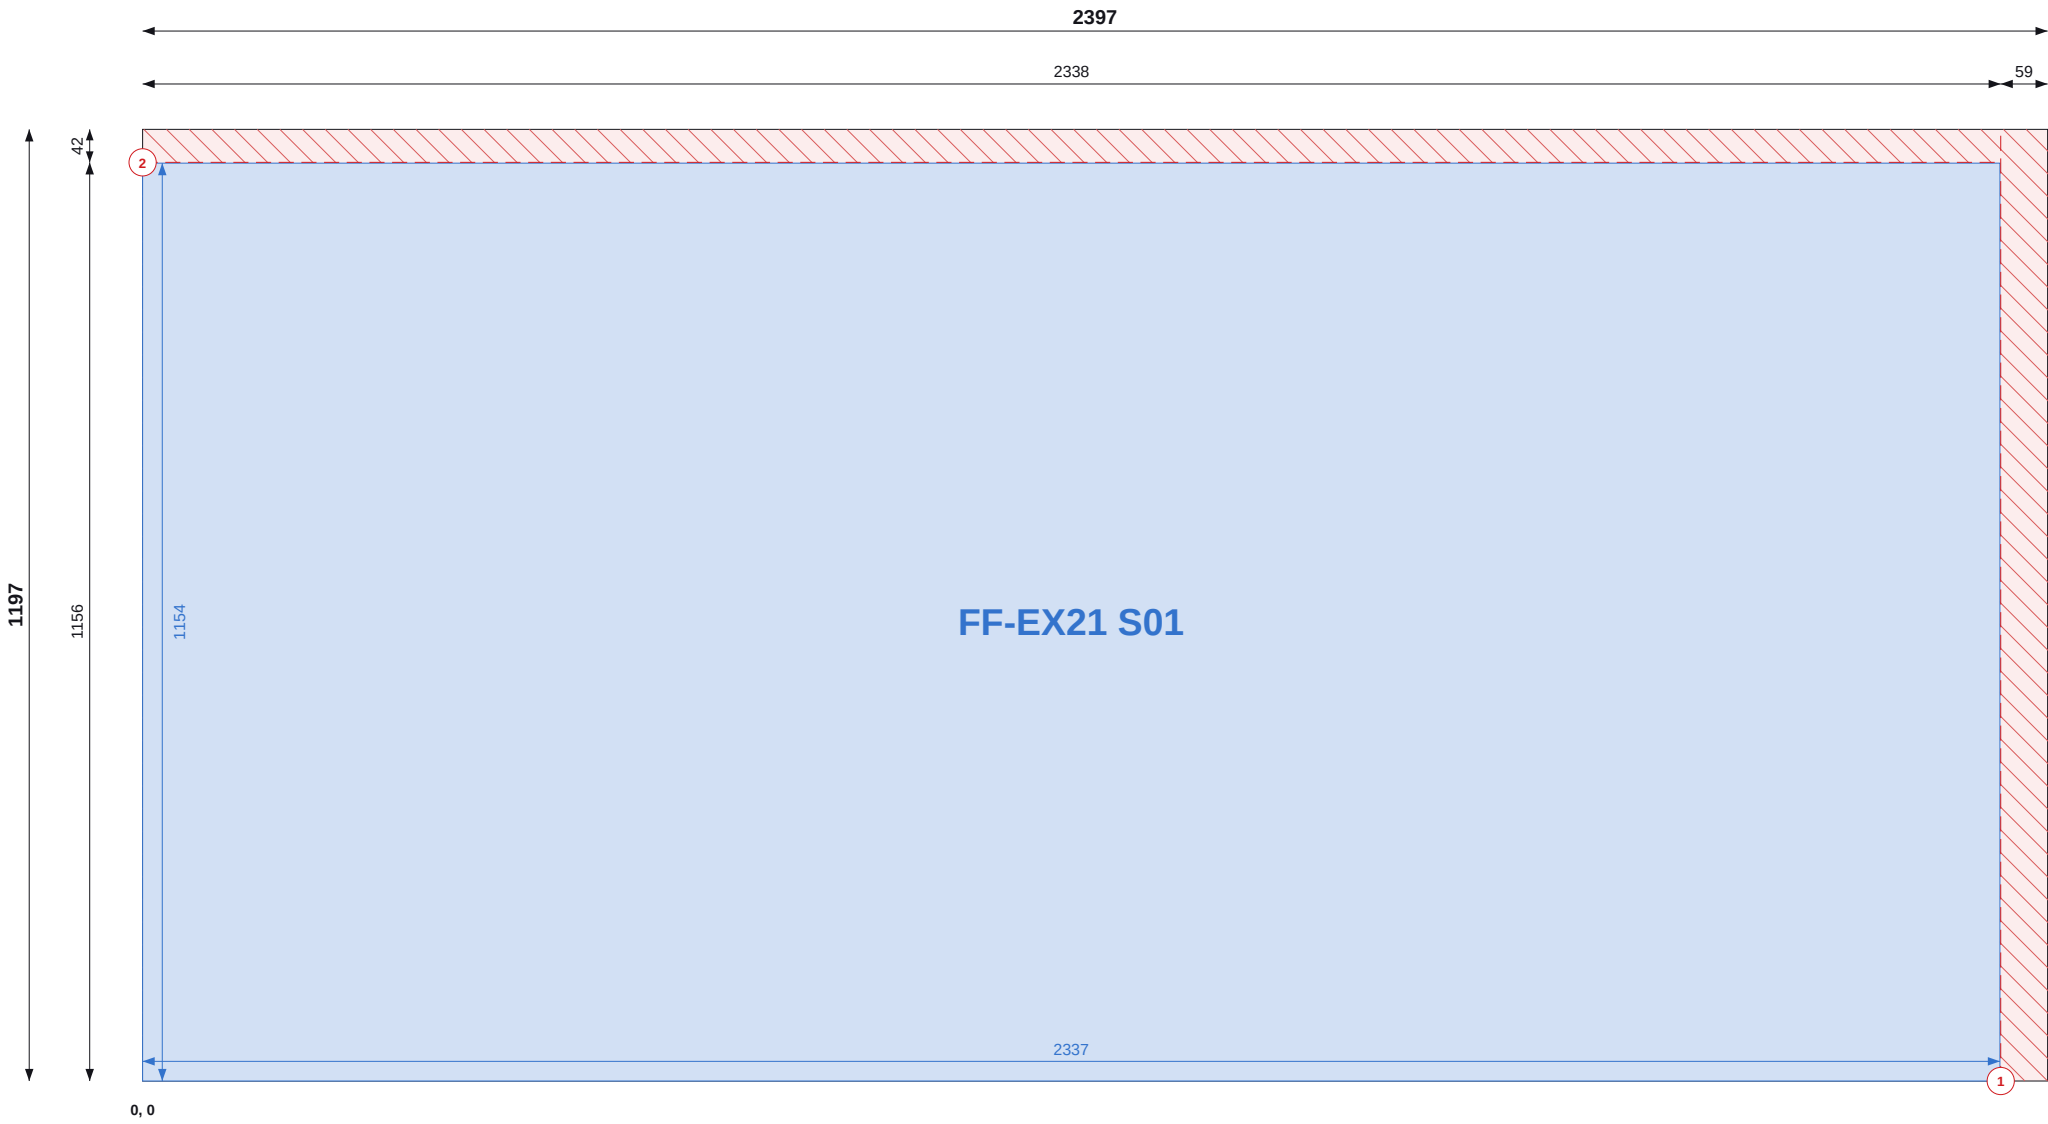

Top / left chains = saw cut positions (to cut centres). Coloured = part size and position.

SHEET 5 OF 34

THIS SHEET

Item	Value
Parts	1
Used / waste	94.0% / 0.17 m2
Reusable offcuts	0
Saw cuts / shared	2 / 0

PIECES (POSITION = BOTTOM-LEFT CORNER)

Label	Size	X, Y
FF-EX21 S01	1154 x 2337	0, 0

NOTES

- Cut from OSB/3 9mm 1197x2397, 2mm saw kerf. Viewed on the face; dimensions from the sheet's bottom-left corner (0,0). Red numbered lines = saw cuts in order, each edge to edge.
- Coloured dimensions belong to the part of that colour: its width and height, and its position from the sheet edges. Raked parts: corner coordinates at each corner.
- Red hatch = waste. Labels = panel + piece mark on the manufacture drawing.

REVISIONS

REV	DATE	DESCRIPTION
C01	13.09.26	Construction issue



TLS TIMBER FRAME

Design & Manufacture

Scan: 3D model + drawings




CLIENT	PROJECT
MP Adams	MP Adams Plot 3, Eckington

DRAWING TITLE			
OSB CUTTING - FIRST FLOOR - SHEET 5 OF 34			
OSB/3 9mm 1197x2397 First Floor			

SCALE	SIZE	DATE	DRAWN
NTS	A3	13.09.26	TS

STATUS	DRAWING No.	REV
CONSTRUCTION	P3-CP-OSB-02 / 05	C01

Do not scale. All dimensions in mm. Check all dimensions on site.

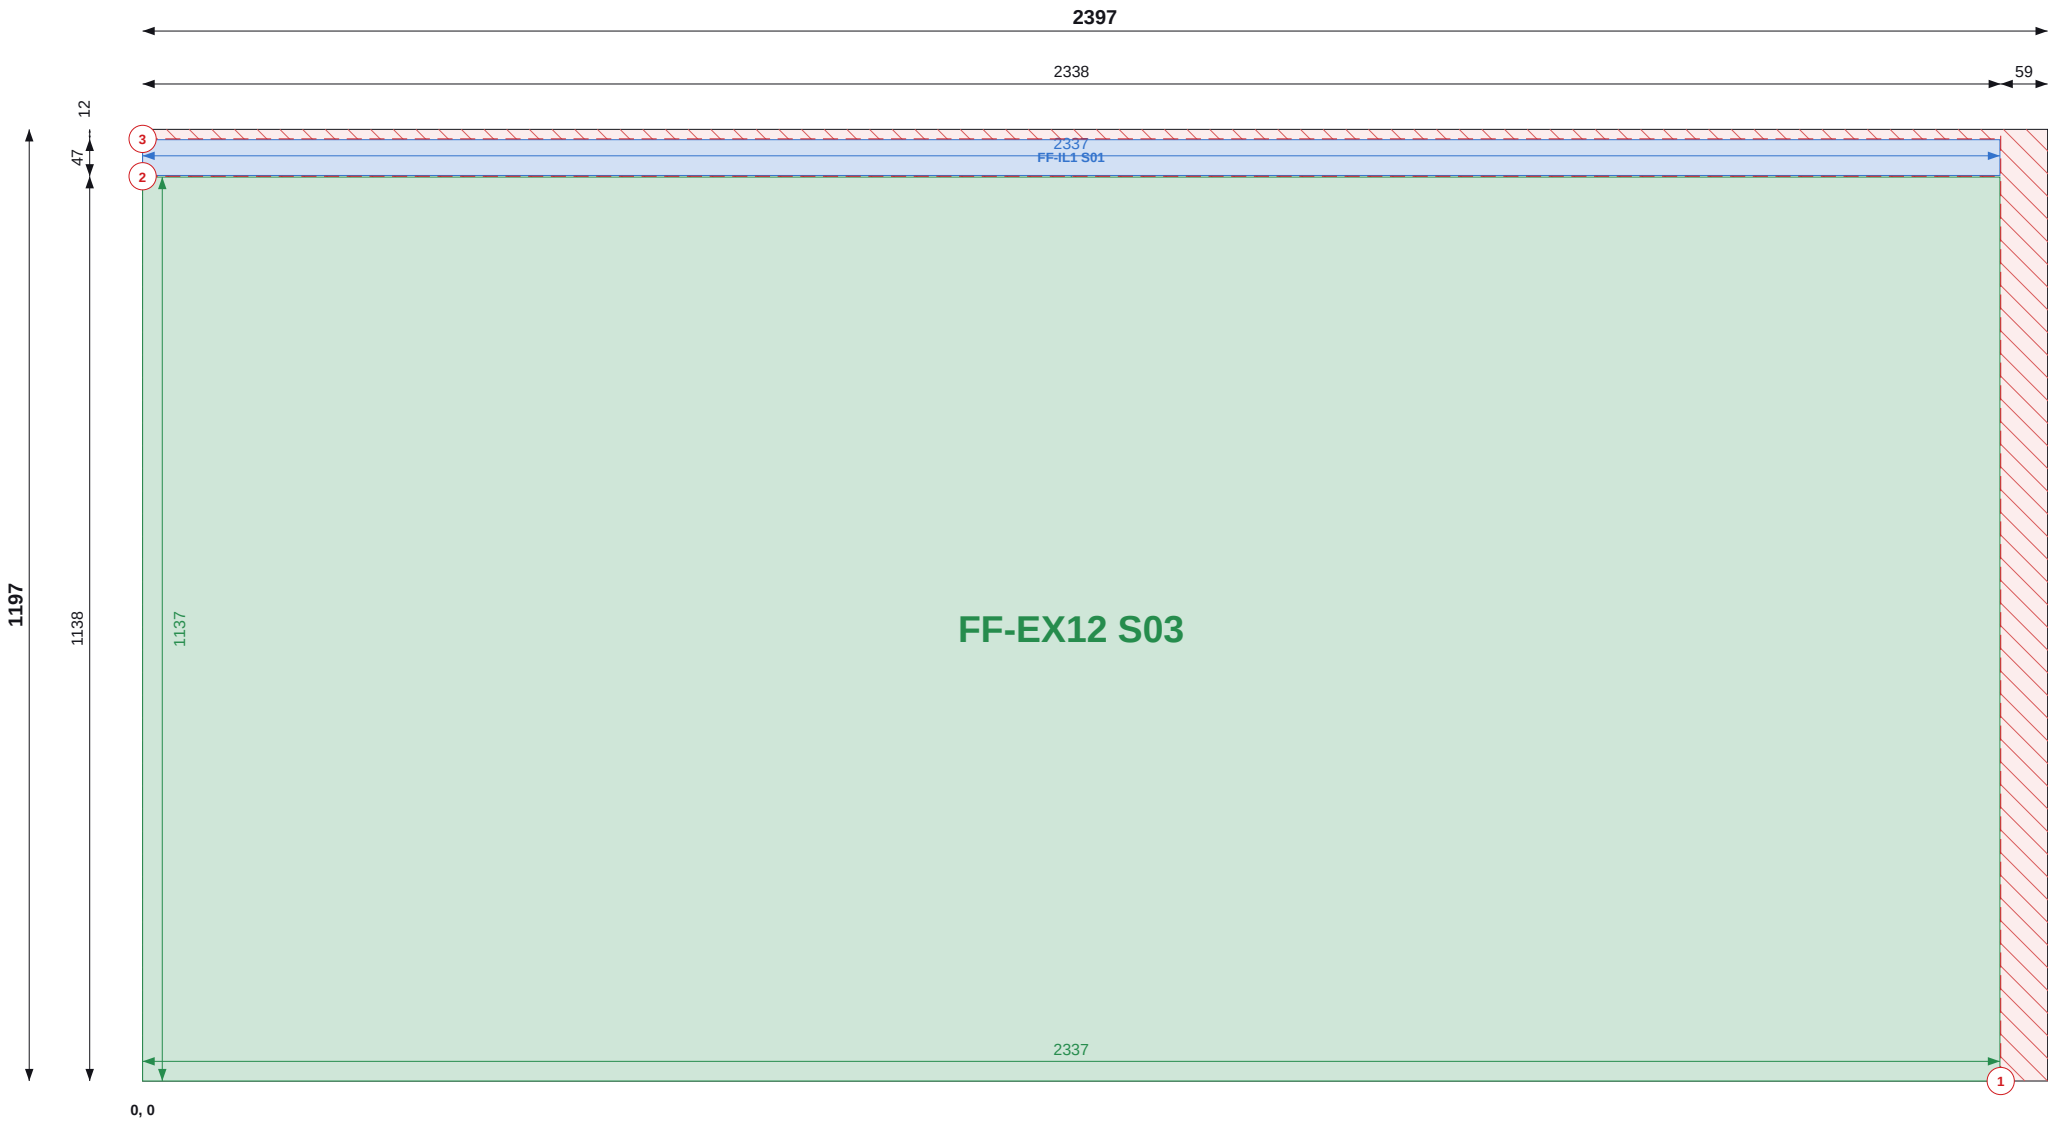

Top / left chains = saw cut positions (to cut centres). Coloured = part size and position.

SHEET 6 OF 34

THIS SHEET

Item	Value
Parts	2
Used / waste	96.3% / 0.11 m2
Reusable offcuts	0
Saw cuts / shared	3 / 1

PIECES (POSITION = BOTTOM-LEFT CORNER)

Label	Size	X, Y
FF-IL1 S01	45 x 2337	0, 1139
FF-EX12 S03	1137 x 2337	0, 0

NOTES

- Cut from OSB/3 9mm 1197x2397, 2mm saw kerf. Viewed on the face; dimensions from the sheet's bottom-left corner (0,0). Red numbered lines = saw cuts in order, each edge to edge.
- Coloured dimensions belong to the part of that colour: its width and height, and its position from the sheet edges. Raked parts: corner coordinates at each corner.
- Red hatch = waste. Labels = panel + piece mark on the manufacture drawing.

REVISIONS

REV	DATE	DESCRIPTION
C01	13.09.26	Construction issue



TLS TIMBER FRAME

Design & Manufacture

Scan: 3D model + drawings




CLIENT MP Adams	PROJECT MP Adams Plot 3, Eckington
--------------------	---------------------------------------

DRAWING TITLE OSB CUTTING - FIRST FLOOR - SHEET 6 OF 34			
OSB/3 9mm 1197x2397 First Floor			

SCALE NTS	SIZE A3	DATE 13.09.26	DRAWN TS
--------------	------------	------------------	-------------

STATUS CONSTRUCTION	DRAWING No. P3-CP-OSB-02 / 06	REV C01
------------------------	----------------------------------	------------

Do not scale. All dimensions in mm. Check all dimensions on site.

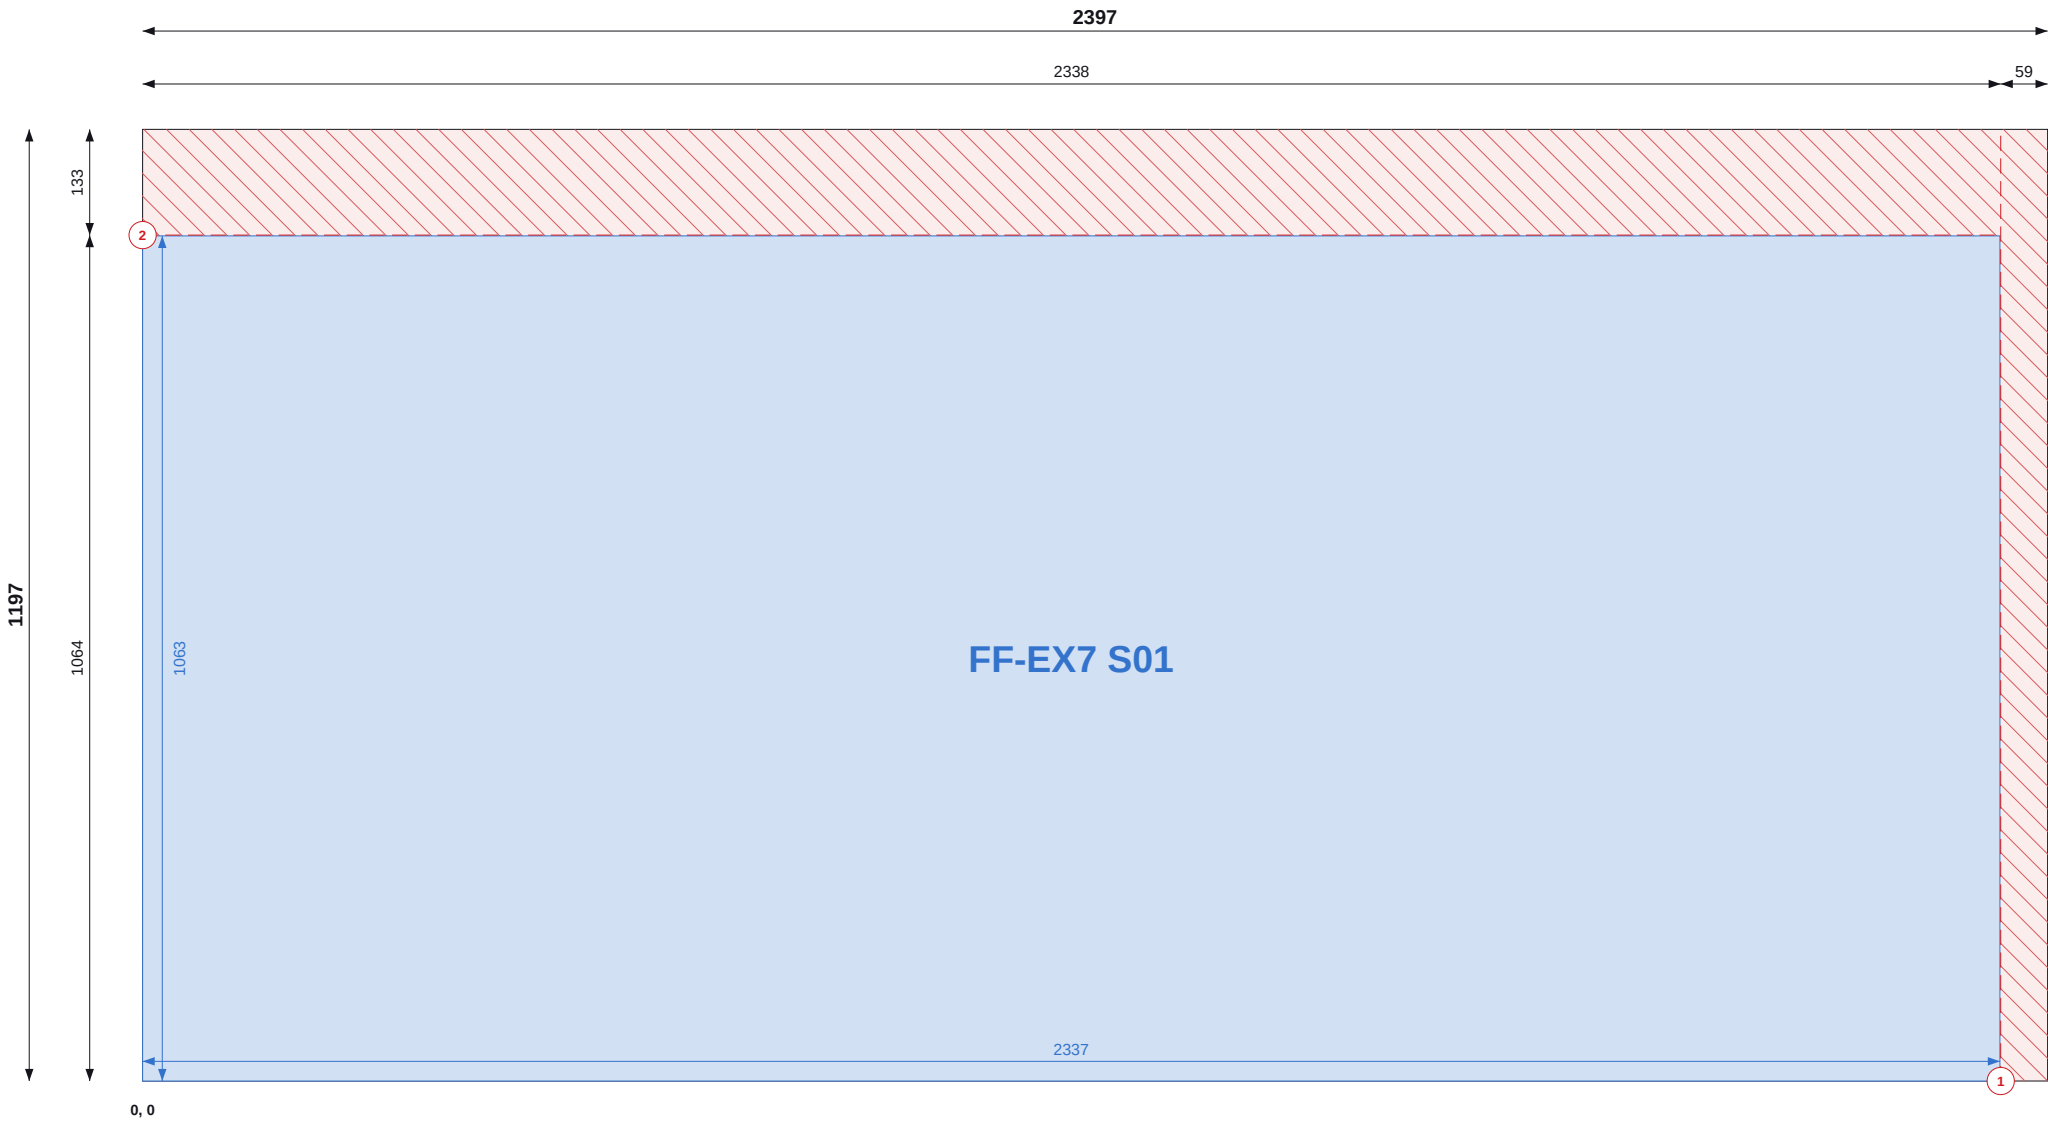

Top / left chains = saw cut positions (to cut centres). Coloured = part size and position.

SHEET 7 OF 34

THIS SHEET

Item	Value
Parts	1
Used / waste	86.6% / 0.38 m2
Reusable offcuts	0
Saw cuts / shared	2 / 0

PIECES (POSITION = BOTTOM-LEFT CORNER)

Label	Size	X, Y
FF-EX7 S01	1063 x 2337	0, 0

NOTES

- Cut from OSB/3 9mm 1197x2397, 2mm saw kerf. Viewed on the face; dimensions from the sheet's bottom-left corner (0,0). Red numbered lines = saw cuts in order, each edge to edge.
- Coloured dimensions belong to the part of that colour: its width and height, and its position from the sheet edges. Raked parts: corner coordinates at each corner.
- Red hatch = waste. Labels = panel + piece mark on the manufacture drawing.

REVISIONS

REV	DATE	DESCRIPTION
C01	13.09.26	Construction issue



TLS TIMBER FRAME

Design & Manufacture

Scan: 3D model + drawings



CLIENT	PROJECT
MP Adams	MP Adams Plot 3, Eckington


DRAWING TITLE
OSB CUTTING - FIRST FLOOR - SHEET 7 OF 34

OSB/3 9mm 1197x2397 | First Floor

SCALE	SIZE	DATE	DRAWN
NTS	A3	13.09.26	TS

STATUS	DRAWING No.	REV
CONSTRUCTION	P3-CP-OSB-02 / 07	C01

Do not scale. All dimensions in mm. Check all dimensions on site.

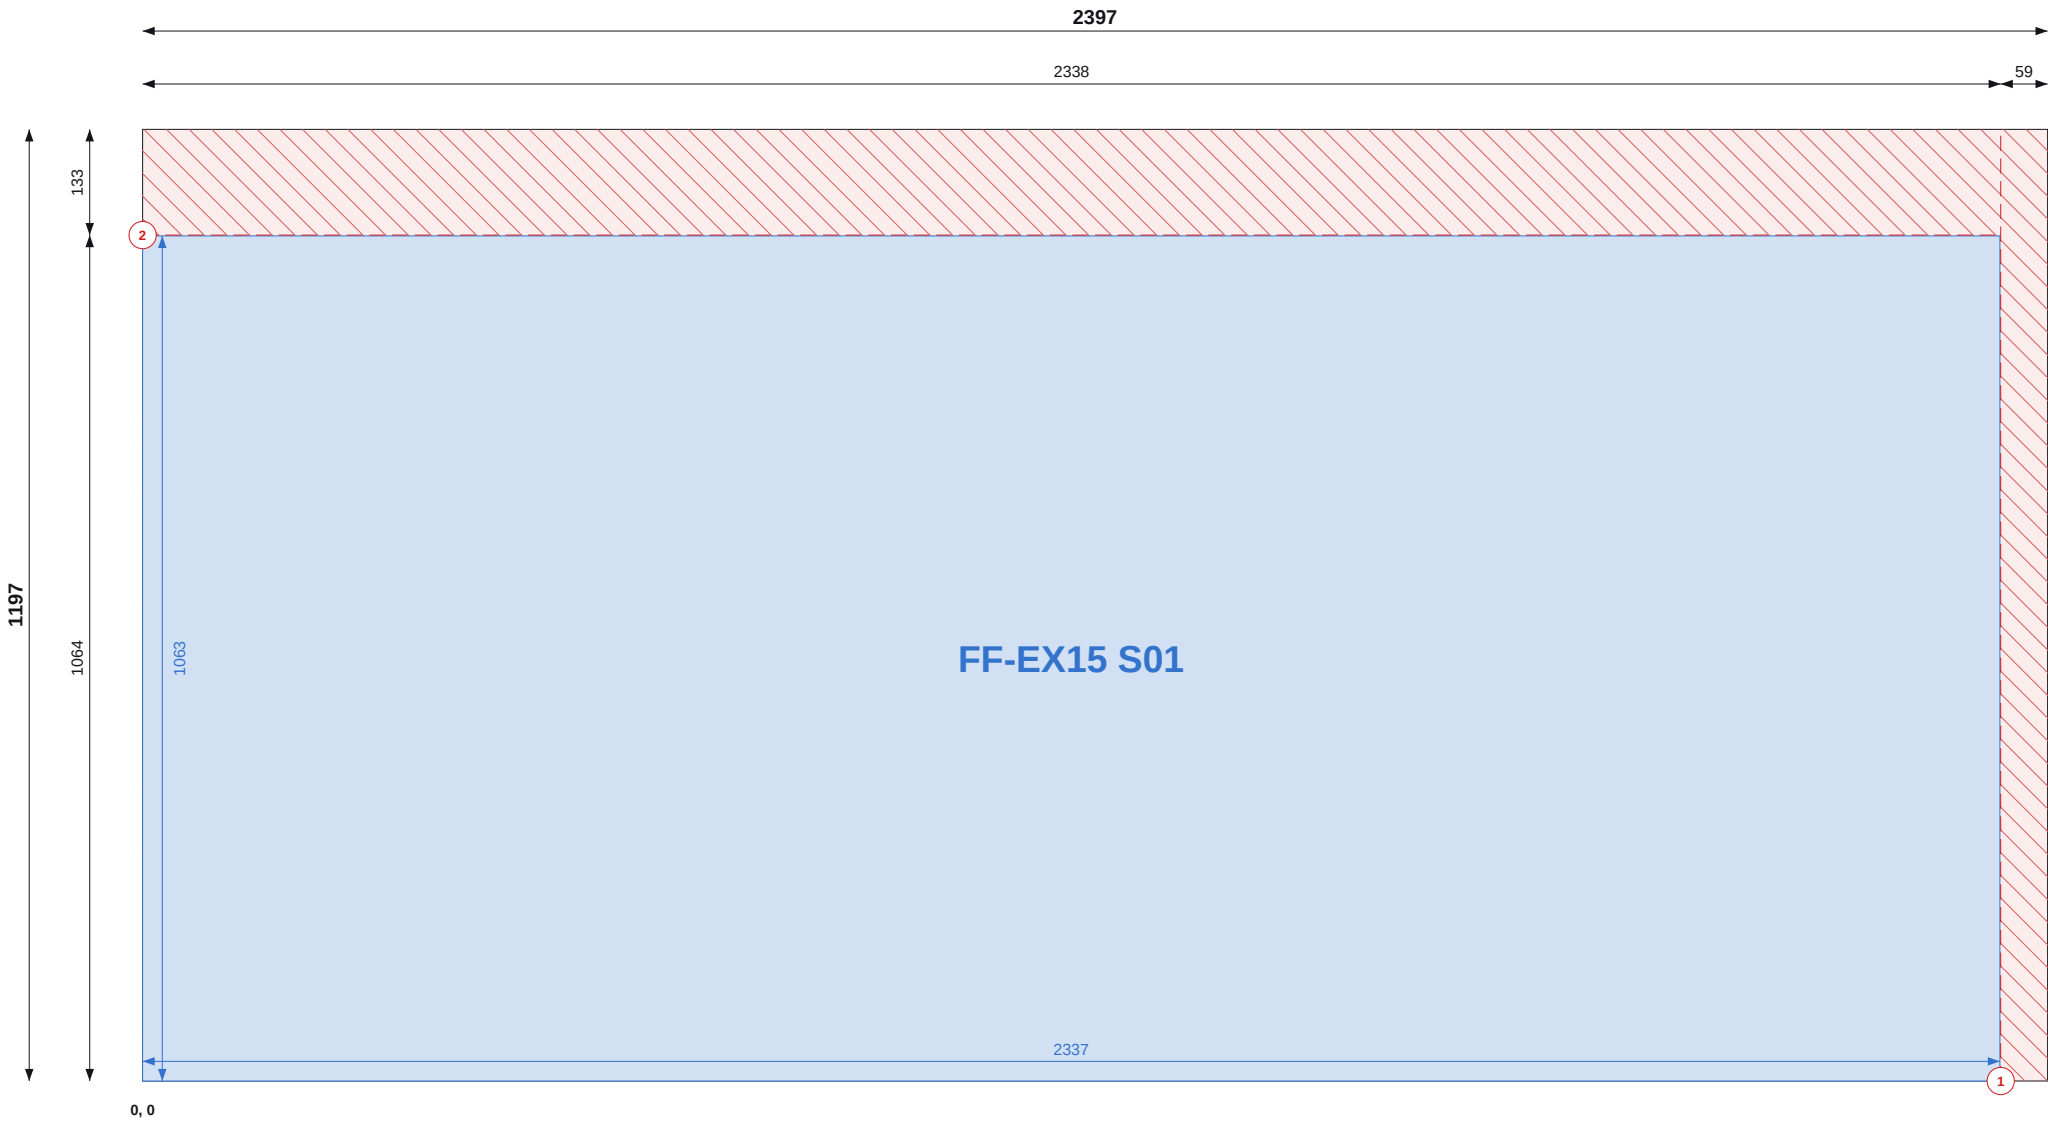

Top / left chains = saw cut positions (to cut centres). Coloured = part size and position.

SHEET 8 OF 34

THIS SHEET

Item	Value
Parts	1
Used / waste	86.6% / 0.38 m2
Reusable offcuts	0
Saw cuts / shared	2 / 0

PIECES (POSITION = BOTTOM-LEFT CORNER)

Label	Size	X, Y
FF-EX15 S01	1063 x 2337	0, 0

NOTES

- Cut from OSB/3 9mm 1197x2397, 2mm saw kerf. Viewed on the face; dimensions from the sheet's bottom-left corner (0,0). Red numbered lines = saw cuts in order, each edge to edge.
- Coloured dimensions belong to the part of that colour: its width and height, and its position from the sheet edges. Raked parts: corner coordinates at each corner.
- Red hatch = waste. Labels = panel + piece mark on the manufacture drawing.

REVISIONS

REV	DATE	DESCRIPTION
C01	13.09.26	Construction issue



TLS TIMBER FRAME

Design & Manufacture

Scan: 3D model + drawings




CLIENT	PROJECT
MP Adams	MP Adams Plot 3, Eckington

DRAWING TITLE			
OSB CUTTING - FIRST FLOOR - SHEET 8 OF 34			
OSB/3 9mm 1197x2397 First Floor			

SCALE	SIZE	DATE	DRAWN
NTS	A3	13.09.26	TS

STATUS	DRAWING No.	REV
CONSTRUCTION	P3-CP-OSB-02 / 08	C01

Do not scale. All dimensions in mm. Check all dimensions on site.

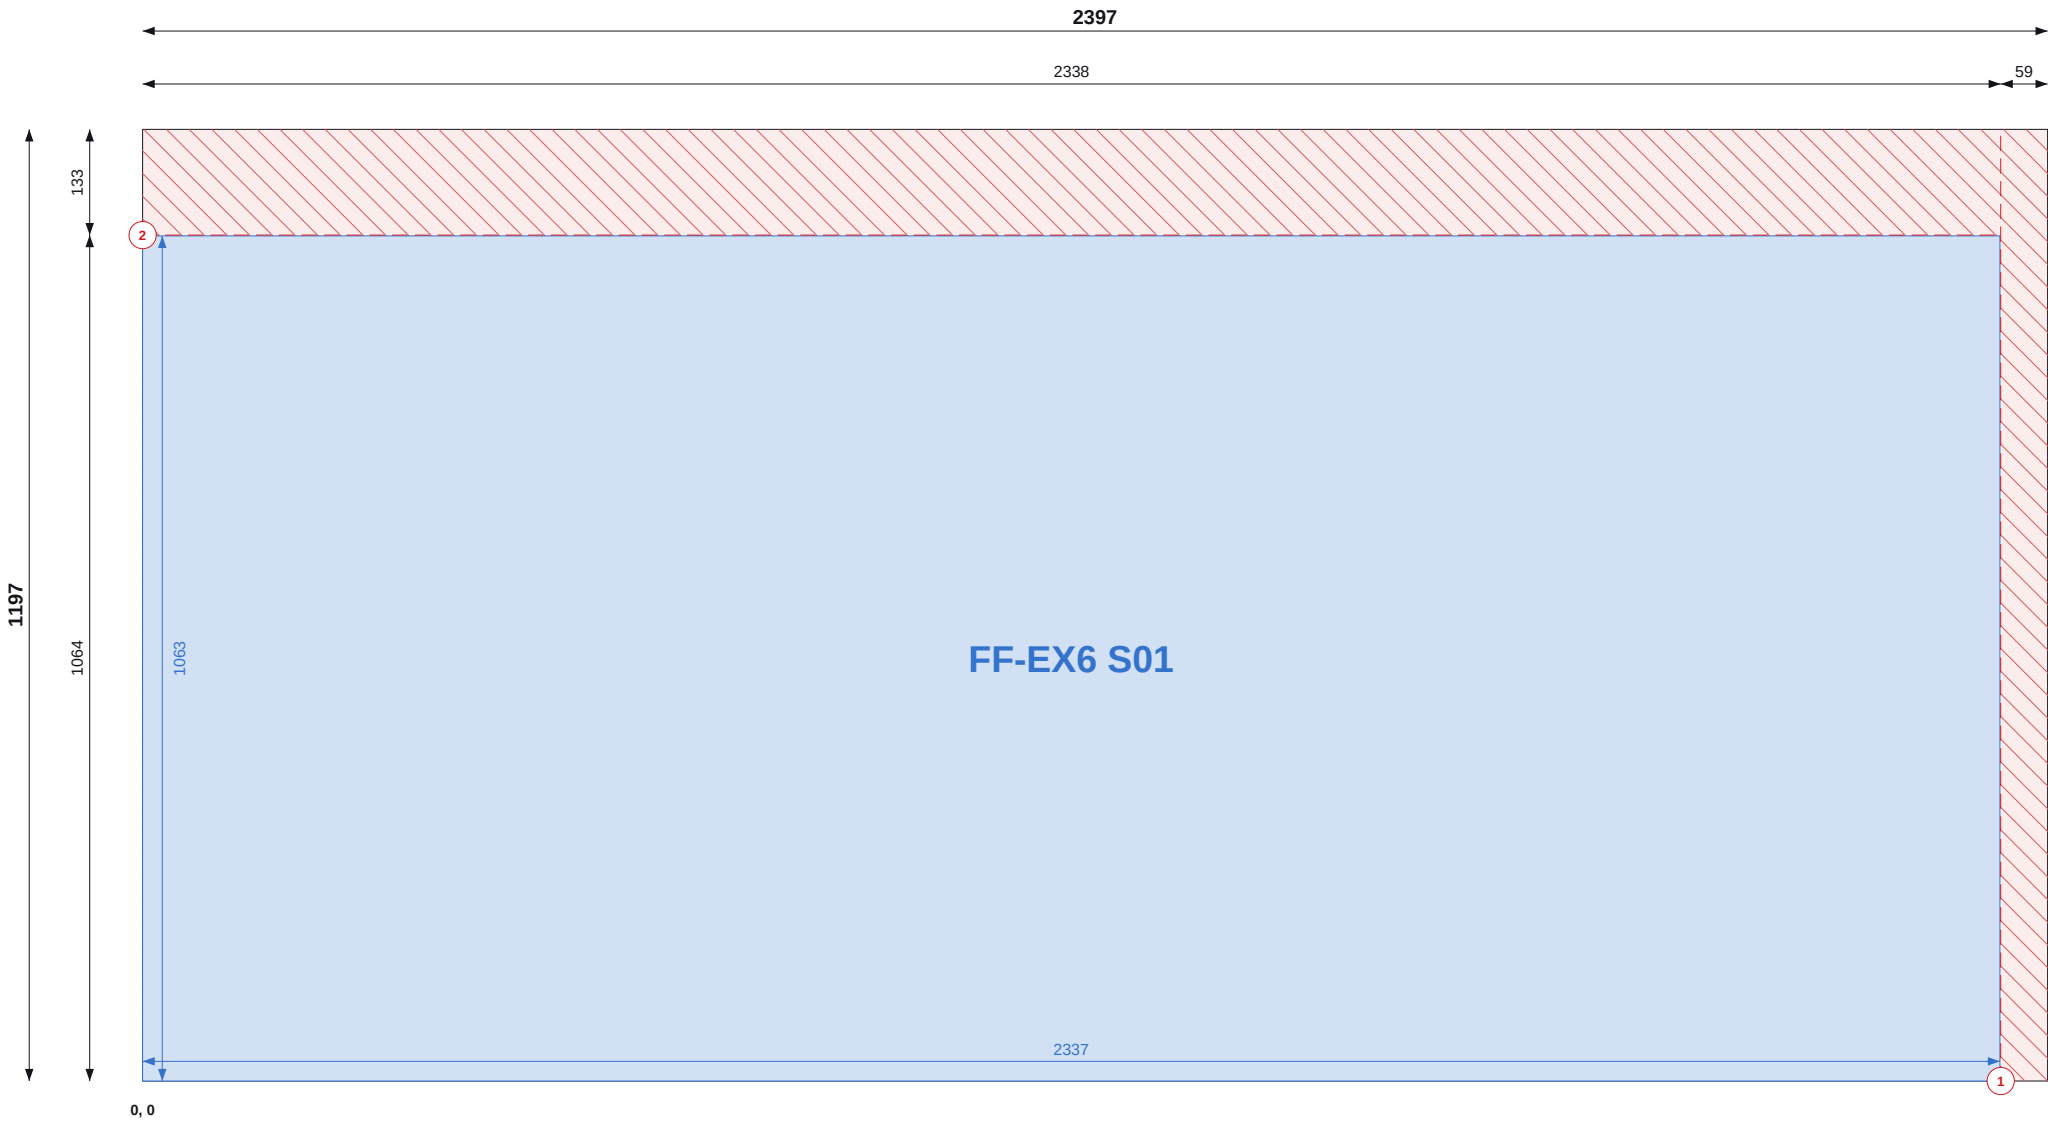

Top / left chains = saw cut positions (to cut centres). Coloured = part size and position.

SHEET 9 OF 34

THIS SHEET

Item	Value
Parts	1
Used / waste	86.6% / 0.38 m2
Reusable offcuts	0
Saw cuts / shared	2 / 0

PIECES (POSITION = BOTTOM-LEFT CORNER)

Label	Size	X, Y
FF-EX6 S01	1063 x 2337	0, 0

NOTES

- Cut from OSB/3 9mm 1197x2397, 2mm saw kerf. Viewed on the face; dimensions from the sheet's bottom-left corner (0,0). Red numbered lines = saw cuts in order, each edge to edge.
- Coloured dimensions belong to the part of that colour: its width and height, and its position from the sheet edges. Raked parts: corner coordinates at each corner.
- Red hatch = waste. Labels = panel + piece mark on the manufacture drawing.

REVISIONS

REV	DATE	DESCRIPTION
C01	13.09.26	Construction issue



TLS TIMBER FRAME

Design & Manufacture

Scan: 3D model + drawings



CLIENT	PROJECT
MP Adams	MP Adams Plot 3, Eckington


DRAWING TITLE
OSB CUTTING - FIRST FLOOR - SHEET 9 OF 34

OSB/3 9mm 1197x2397 | First Floor

SCALE	SIZE	DATE	DRAWN
NTS	A3	13.09.26	TS

STATUS	DRAWING No.	REV
CONSTRUCTION	P3-CP-OSB-02 / 09	C01

Do not scale. All dimensions in mm. Check all dimensions on site.

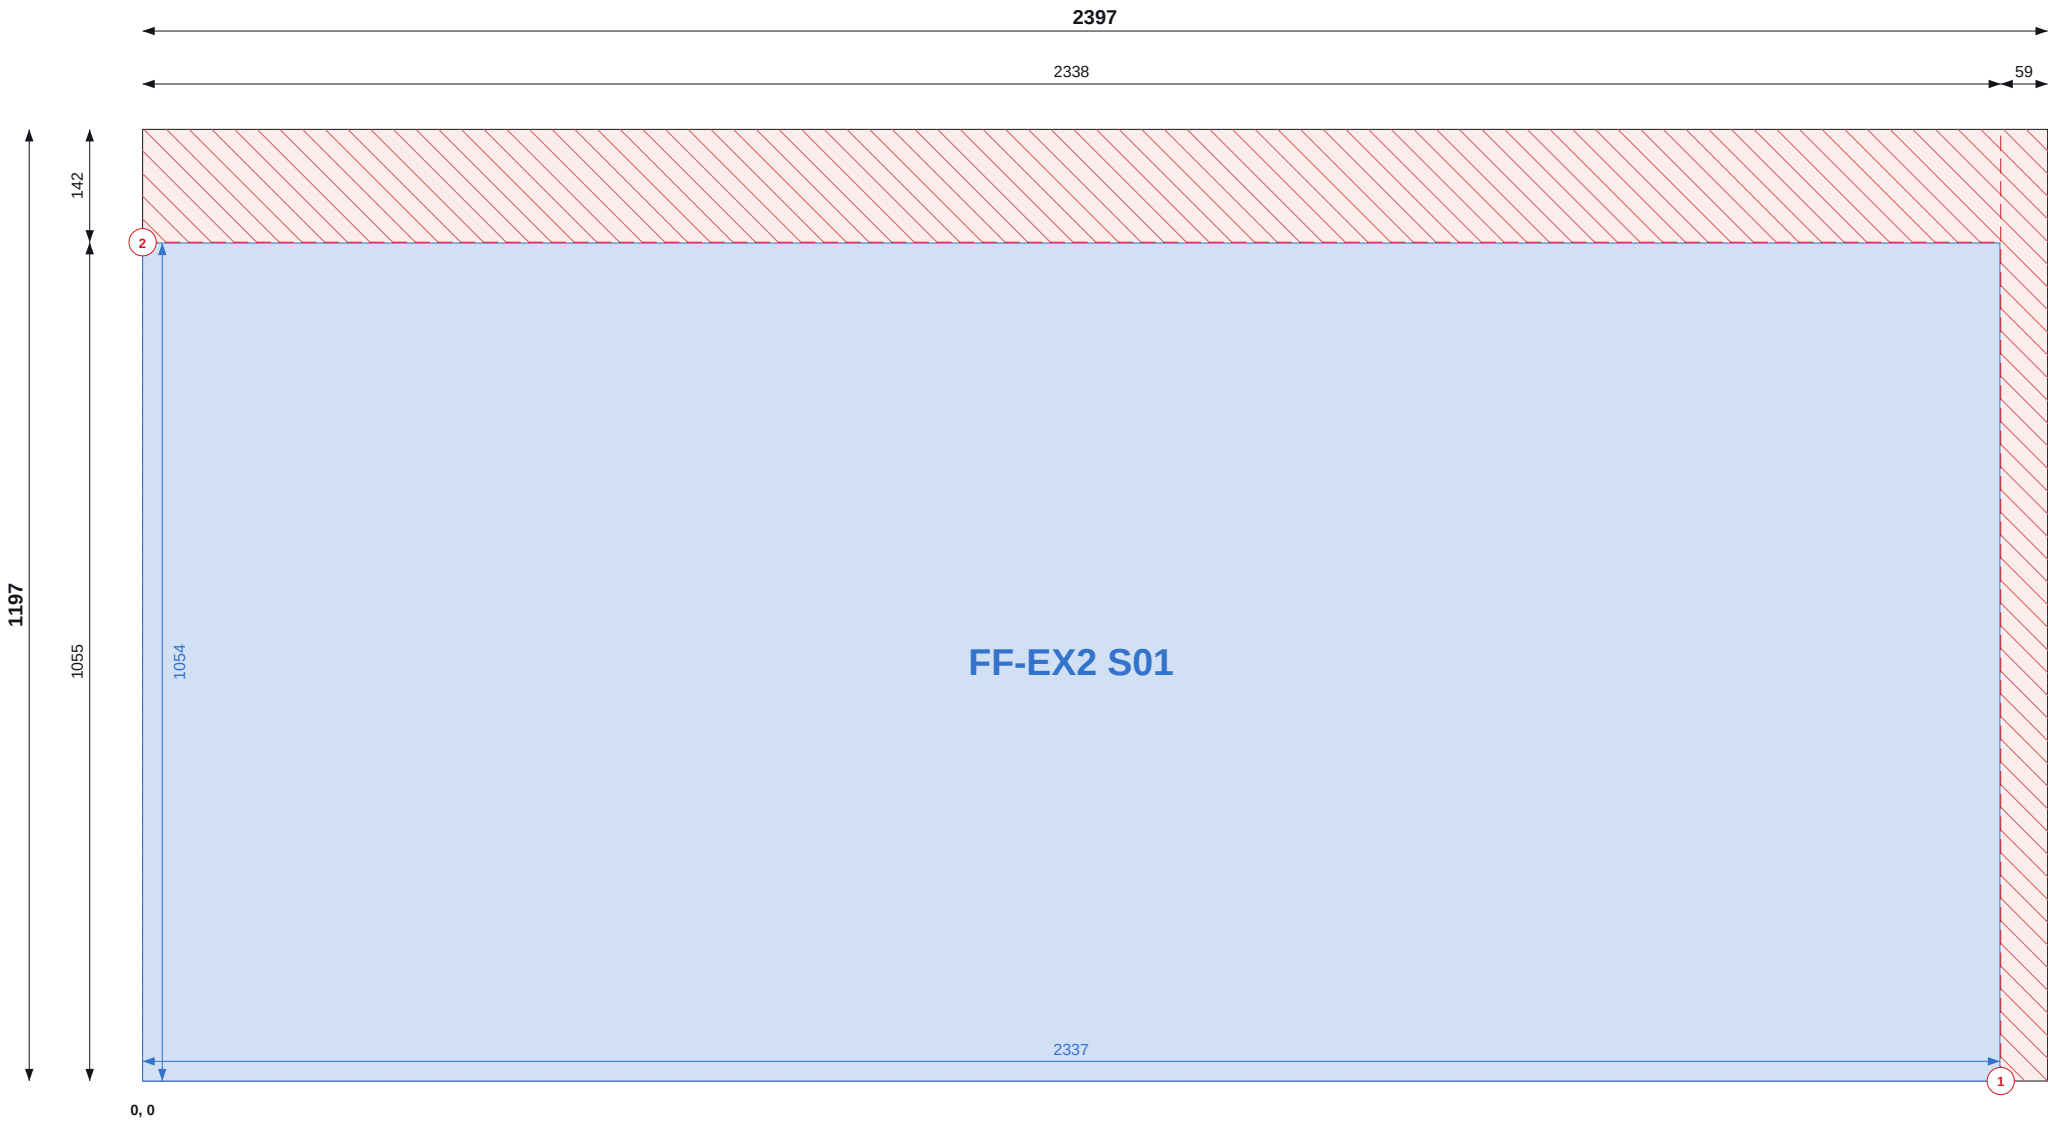

Top / left chains = saw cut positions (to cut centres). Coloured = part size and position.

SHEET 10 OF 34

THIS SHEET

Item	Value
Parts	1
Used / waste	85.8% / 0.41 m2
Reusable offcuts	0
Saw cuts / shared	2 / 0

PIECES (POSITION = BOTTOM-LEFT CORNER)

Label	Size	X, Y
FF-EX2 S01	1054 x 2337	0, 0

NOTES

- Cut from OSB/3 9mm 1197x2397, 2mm saw kerf. Viewed on the face; dimensions from the sheet's bottom-left corner (0,0). Red numbered lines = saw cuts in order, each edge to edge.
- Coloured dimensions belong to the part of that colour: its width and height, and its position from the sheet edges. Raked parts: corner coordinates at each corner.
- Red hatch = waste. Labels = panel + piece mark on the manufacture drawing.

REVISIONS

REV	DATE	DESCRIPTION
C01	13.09.26	Construction issue



TLS TIMBER FRAME

Design & Manufacture

Scan: 3D model + drawings



CLIENT	PROJECT
MP Adams	MP Adams Plot 3, Eckington


DRAWING TITLE
OSB CUTTING - FIRST FLOOR - SHEET 10 OF 34

OSB/3 9mm 1197x2397 | First Floor

SCALE	SIZE	DATE	DRAWN
NTS	A3	13.09.26	TS

STATUS	DRAWING No.	REV
CONSTRUCTION	P3-CP-OSB-02 / 10	C01

Do not scale. All dimensions in mm. Check all dimensions on site.

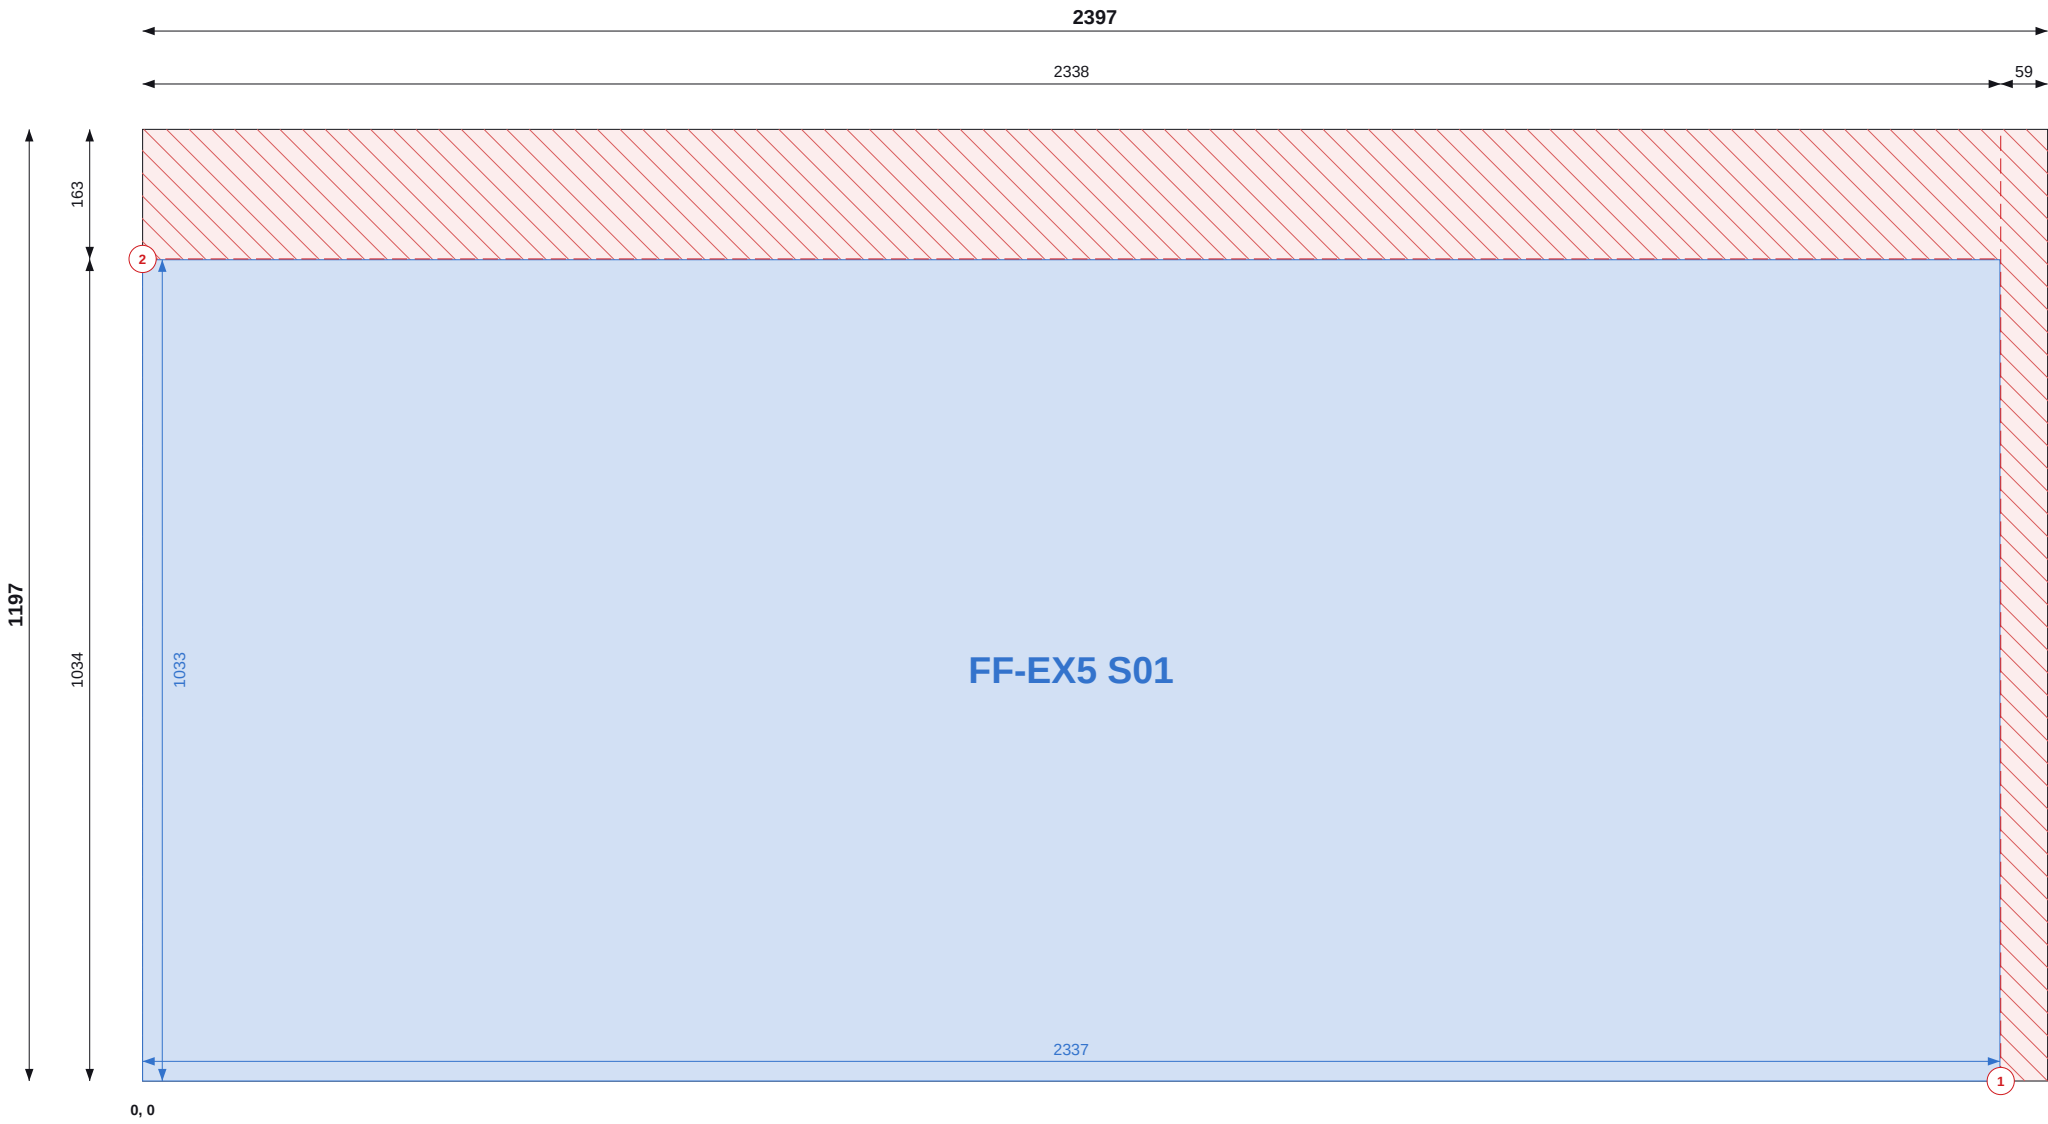

Top / left chains = saw cut positions (to cut centres). Coloured = part size and position.

SHEET 11 OF 34

THIS SHEET

Item	Value
Parts	1
Used / waste	84.1% / 0.46 m2
Reusable offcuts	0
Saw cuts / shared	2 / 0

PIECES (POSITION = BOTTOM-LEFT CORNER)

Label	Size	X, Y
FF-EX5 S01	1033 x 2337	0, 0

NOTES

- Cut from OSB/3 9mm 1197x2397, 2mm saw kerf. Viewed on the face; dimensions from the sheet's bottom-left corner (0,0). Red numbered lines = saw cuts in order, each edge to edge.
- Coloured dimensions belong to the part of that colour: its width and height, and its position from the sheet edges. Raked parts: corner coordinates at each corner.
- Red hatch = waste. Labels = panel + piece mark on the manufacture drawing.

REVISIONS

REV	DATE	DESCRIPTION
C01	13.09.26	Construction issue



TLS TIMBER FRAME

Design & Manufacture

Scan: 3D model + drawings



CLIENT	PROJECT
MP Adams	MP Adams Plot 3, Eckington


DRAWING TITLE
OSB CUTTING - FIRST FLOOR - SHEET 11 OF 34

OSB/3 9mm 1197x2397 | First Floor

SCALE	SIZE	DATE	DRAWN
NTS	A3	13.09.26	TS

STATUS	DRAWING No.	REV
CONSTRUCTION	P3-CP-OSB-02 / 11	C01

Do not scale. All dimensions in mm. Check all dimensions on site.

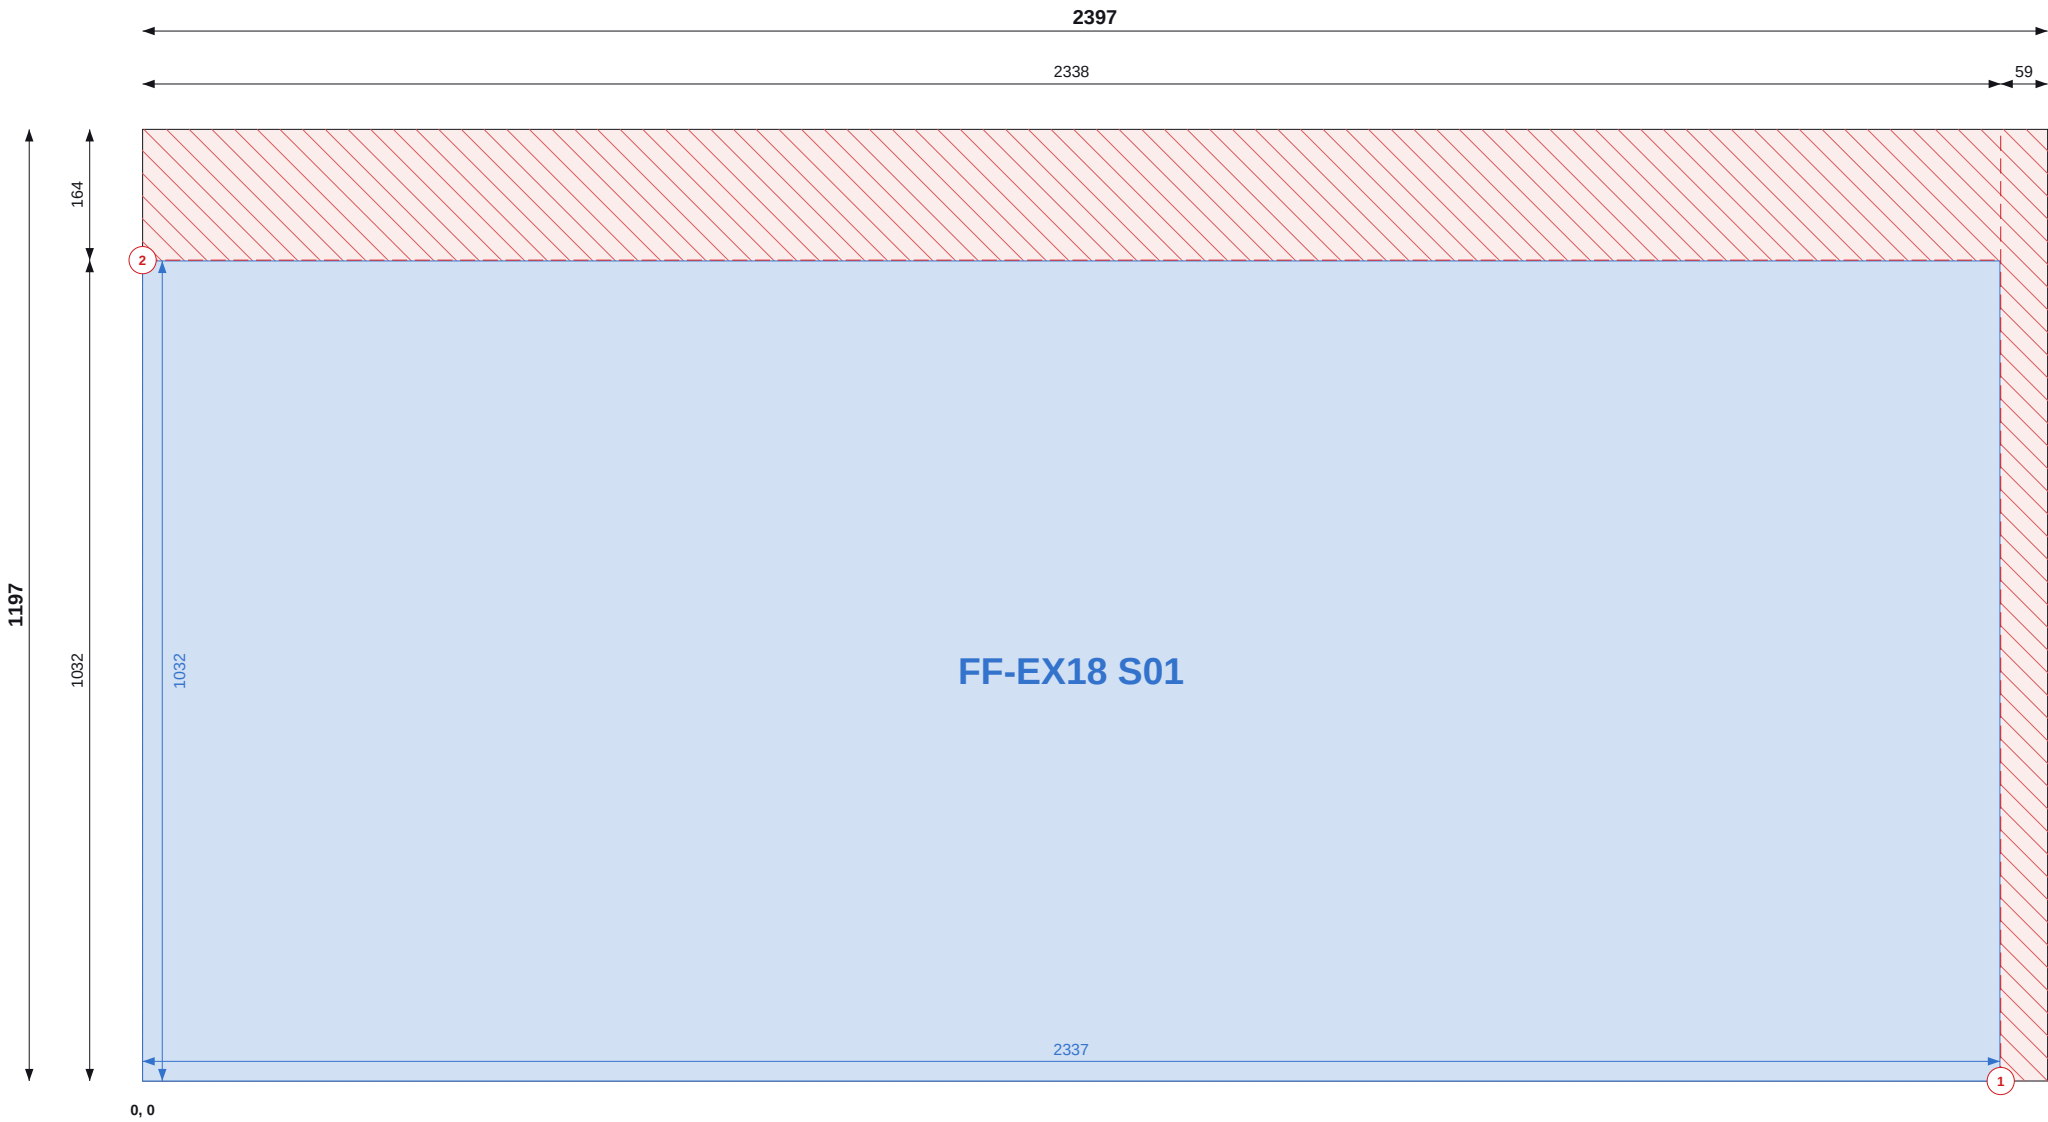

Top / left chains = saw cut positions (to cut centres). Coloured = part size and position.

SHEET 12 OF 34

THIS SHEET

Item	Value
Parts	1
Used / waste	84.0% / 0.46 m2
Reusable offcuts	0
Saw cuts / shared	2 / 0

PIECES (POSITION = BOTTOM-LEFT CORNER)

Label	Size	X, Y
FF-EX18 S01	1032 x 2337	0, 0

NOTES

- Cut from OSB/3 9mm 1197x2397, 2mm saw kerf. Viewed on the face; dimensions from the sheet's bottom-left corner (0,0). Red numbered lines = saw cuts in order, each edge to edge.
- Coloured dimensions belong to the part of that colour: its width and height, and its position from the sheet edges. Raked parts: corner coordinates at each corner.
- Red hatch = waste. Labels = panel + piece mark on the manufacture drawing.

REVISIONS

REV	DATE	DESCRIPTION
C01	13.09.26	Construction issue



TLS TIMBER FRAME

Design & Manufacture

Scan: 3D model + drawings



CLIENT	PROJECT
MP Adams	MP Adams Plot 3, Eckington


DRAWING TITLE
OSB CUTTING - FIRST FLOOR - SHEET 12 OF 34

OSB/3 9mm 1197x2397 | First Floor

SCALE	SIZE	DATE	DRAWN
NTS	A3	13.09.26	TS

STATUS	DRAWING No.	REV
CONSTRUCTION	P3-CP-OSB-02 / 12	C01

Do not scale. All dimensions in mm. Check all dimensions on site.

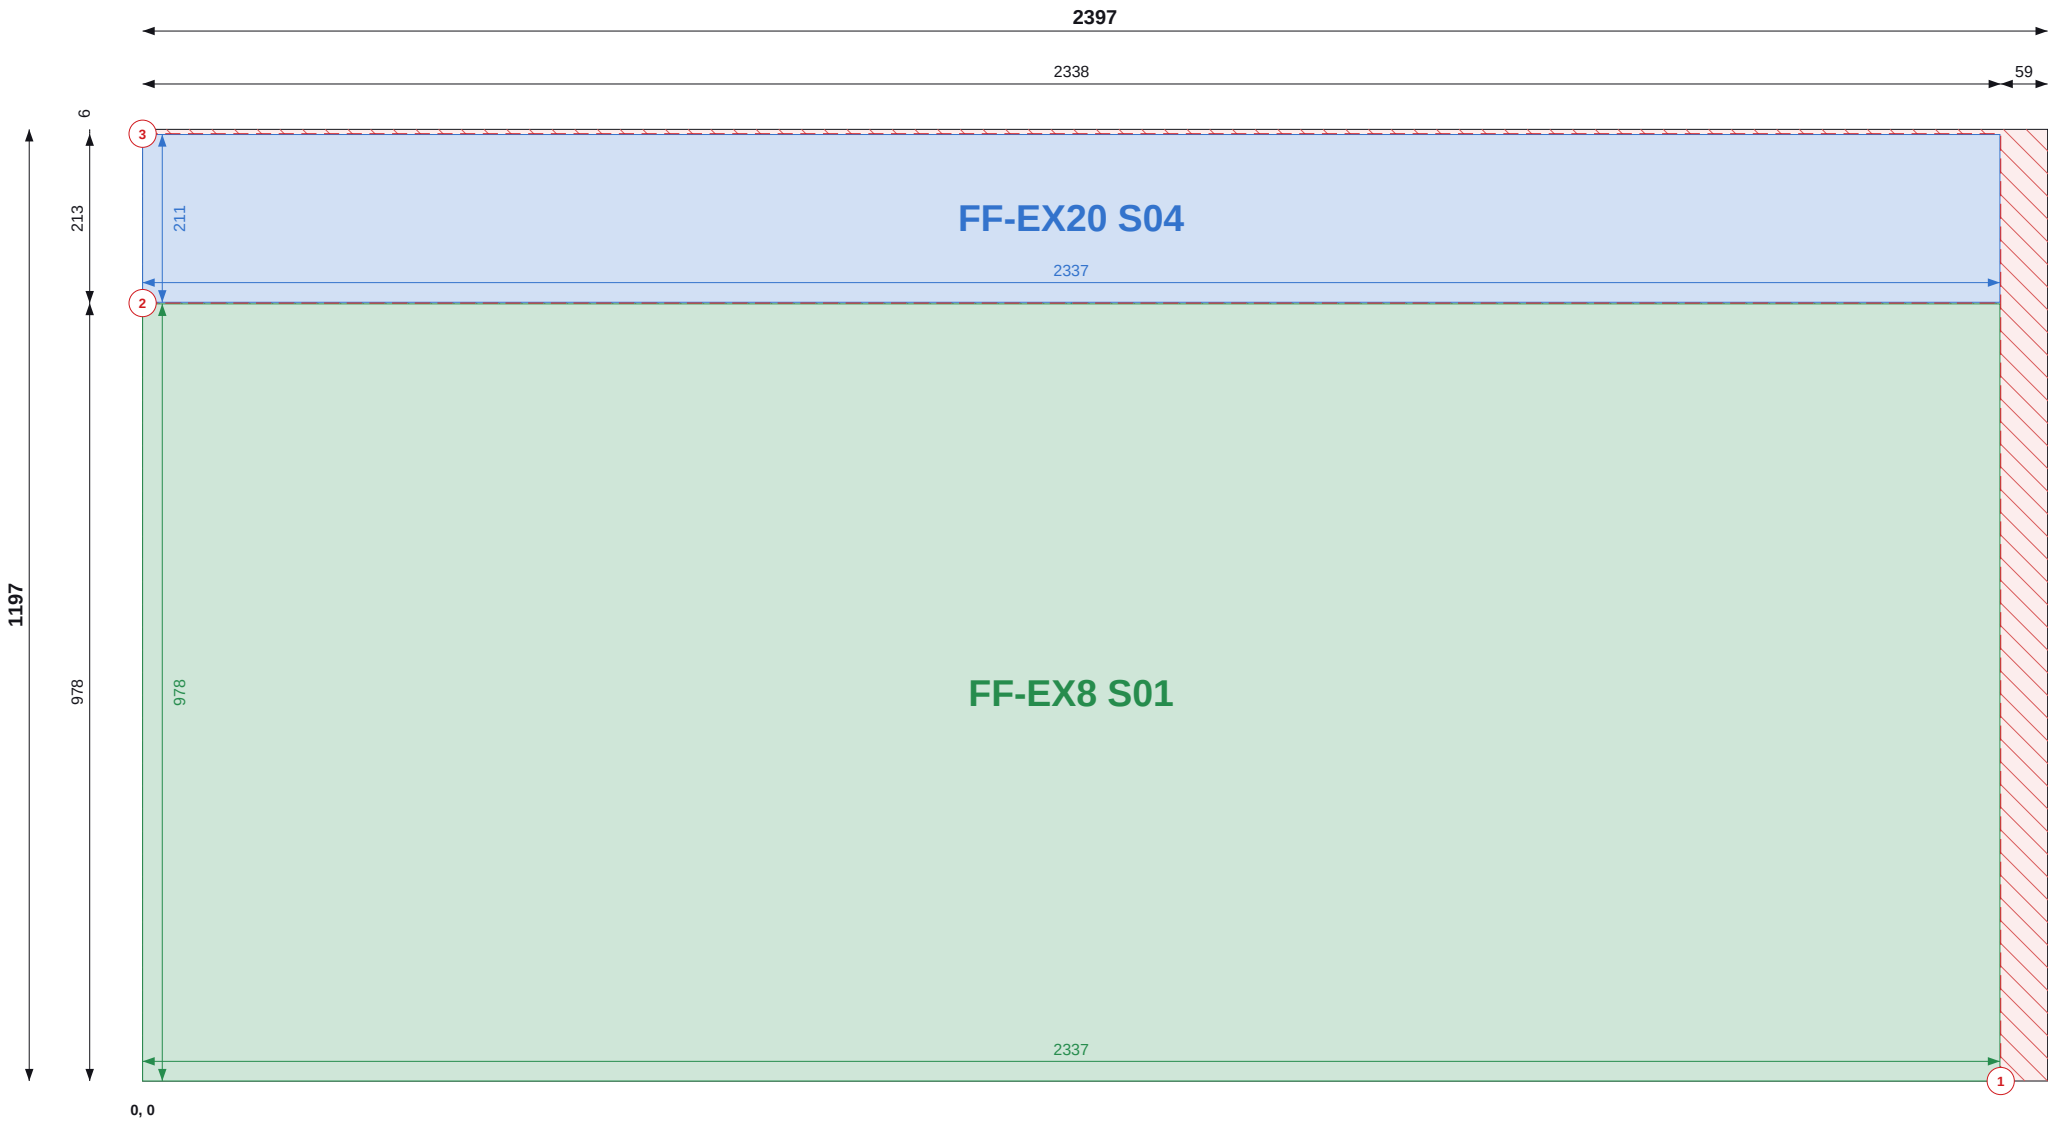

Top / left chains = saw cut positions (to cut centres). Coloured = part size and position.

SHEET 13 OF 34

THIS SHEET

Item	Value
Parts	2
Used / waste	96.8% / 0.09 m2
Reusable offcuts	0
Saw cuts / shared	3 / 1

PIECES (POSITION = BOTTOM-LEFT CORNER)

Label	Size	X, Y
FF-EX20 S04	211 x 2337	0, 980
FF-EX8 S01	978 x 2337	0, 0

NOTES

- Cut from OSB/3 9mm 1197x2397, 2mm saw kerf. Viewed on the face; dimensions from the sheet's bottom-left corner (0,0). Red numbered lines = saw cuts in order, each edge to edge.
- Coloured dimensions belong to the part of that colour: its width and height, and its position from the sheet edges. Raked parts: corner coordinates at each corner.
- Red hatch = waste. Labels = panel + piece mark on the manufacture drawing.

REVISIONS

REV	DATE	DESCRIPTION
C01	13.09.26	Construction issue



TLS TIMBER FRAME

Design & Manufacture

Scan: 3D model + drawings



CLIENT	PROJECT
MP Adams	MP Adams Plot 3, Eckington


DRAWING TITLE
OSB CUTTING - FIRST FLOOR - SHEET 13 OF 34

OSB/3 9mm 1197x2397 | First Floor

SCALE	SIZE	DATE	DRAWN
NTS	A3	13.09.26	TS

STATUS	DRAWING No.	REV
CONSTRUCTION	P3-CP-OSB-02 / 13	C01

Do not scale. All dimensions in mm. Check all dimensions on site.

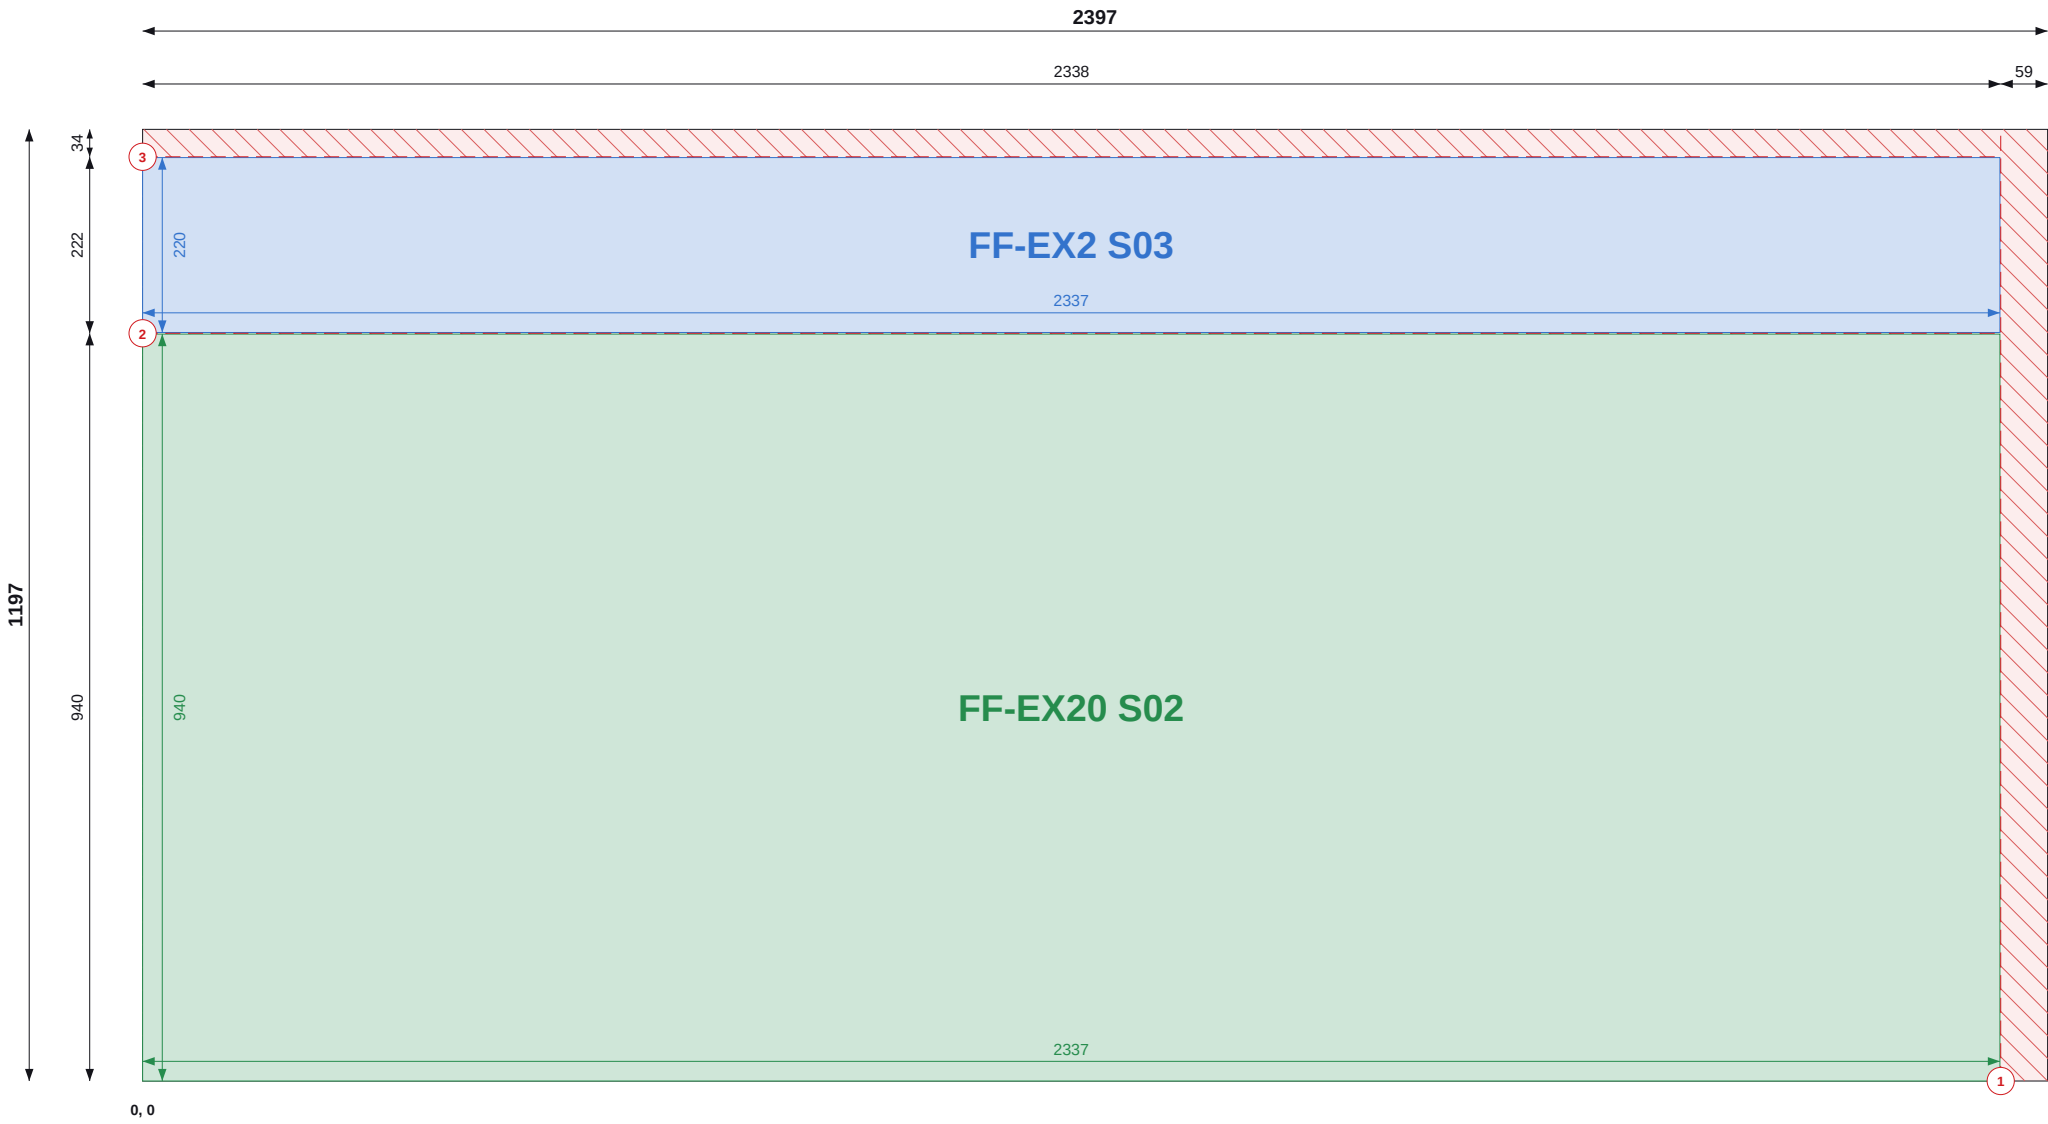

Top / left chains = saw cut positions (to cut centres). Coloured = part size and position.

SHEET 14 OF 34

THIS SHEET

Item	Value
Parts	2
Used / waste	94.4% / 0.16 m2
Reusable offcuts	0
Saw cuts / shared	3 / 1

PIECES (POSITION = BOTTOM-LEFT CORNER)

Label	Size	X, Y
FF-EX2 S03	220 x 2337	0, 942
FF-EX20 S02	940 x 2337	0, 0

NOTES

1. Cut from OSB/3 9mm 1197x2397, 2mm saw kerf. Viewed on the face; dimensions from the sheet's bottom-left corner (0,0). Red numbered lines = saw cuts in order, each edge to edge.
2. Coloured dimensions belong to the part of that colour: its width and height, and its position from the sheet edges. Raked parts: corner coordinates at each corner.
3. Red hatch = waste. Labels = panel + piece mark on the manufacture drawing.

REVISIONS

REV	DATE	DESCRIPTION
C01	13.09.26	Construction issue



TLS TIMBER FRAME

Design & Manufacture

Scan: 3D model + drawings




CLIENT	PROJECT
MP Adams	MP Adams Plot 3, Eckington

DRAWING TITLE			
OSB CUTTING - FIRST FLOOR - SHEET 14 OF 34			
OSB/3 9mm 1197x2397 First Floor			

SCALE	SIZE	DATE	DRAWN
NTS	A3	13.09.26	TS

STATUS	DRAWING No.	REV
CONSTRUCTION	P3-CP-OSB-02 / 14	C01

Do not scale. All dimensions in mm. Check all dimensions on site.

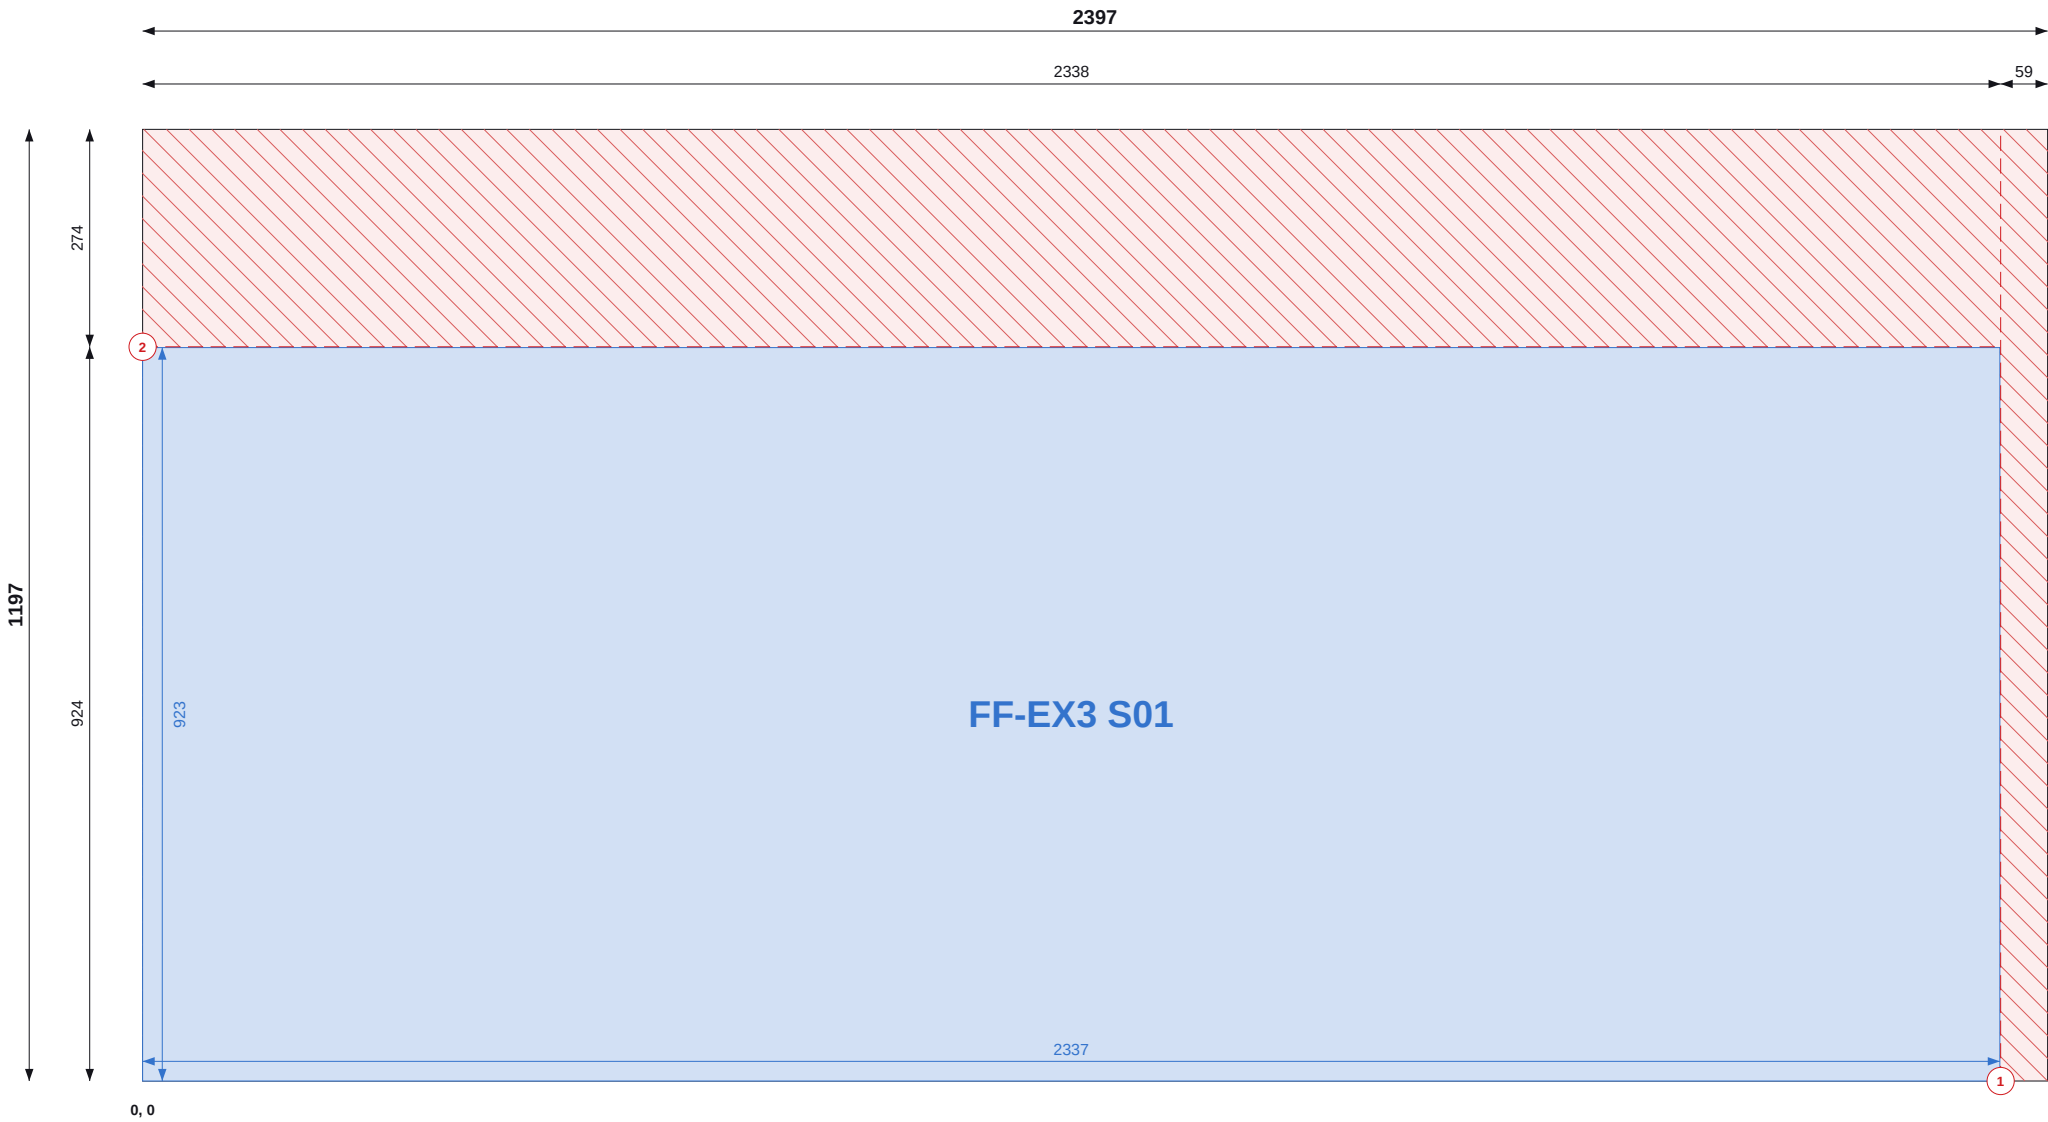

Top / left chains = saw cut positions (to cut centres). Coloured = part size and position.

SHEET 15 OF 34

THIS SHEET

Item	Value
Parts	1
Used / waste	75.1% / 0.71 m2
Reusable offcuts	0
Saw cuts / shared	2 / 0

PIECES (POSITION = BOTTOM-LEFT CORNER)

Label	Size	X, Y
FF-EX3 S01	923 x 2337	0, 0

NOTES

- Cut from OSB/3 9mm 1197x2397, 2mm saw kerf. Viewed on the face; dimensions from the sheet's bottom-left corner (0,0). Red numbered lines = saw cuts in order, each edge to edge.
- Coloured dimensions belong to the part of that colour: its width and height, and its position from the sheet edges. Raked parts: corner coordinates at each corner.
- Red hatch = waste. Labels = panel + piece mark on the manufacture drawing.

REVISIONS

REV	DATE	DESCRIPTION
C01	13.09.26	Construction issue



TLS TIMBER FRAME

Design & Manufacture

Scan: 3D model + drawings



CLIENT	PROJECT
MP Adams	MP Adams Plot 3, Eckington


DRAWING TITLE
OSB CUTTING - FIRST FLOOR - SHEET 15 OF 34

OSB/3 9mm 1197x2397 | First Floor

SCALE	SIZE	DATE	DRAWN
NTS	A3	13.09.26	TS

STATUS	DRAWING No.	REV
CONSTRUCTION	P3-CP-OSB-02 / 15	C01

Do not scale. All dimensions in mm. Check all dimensions on site.

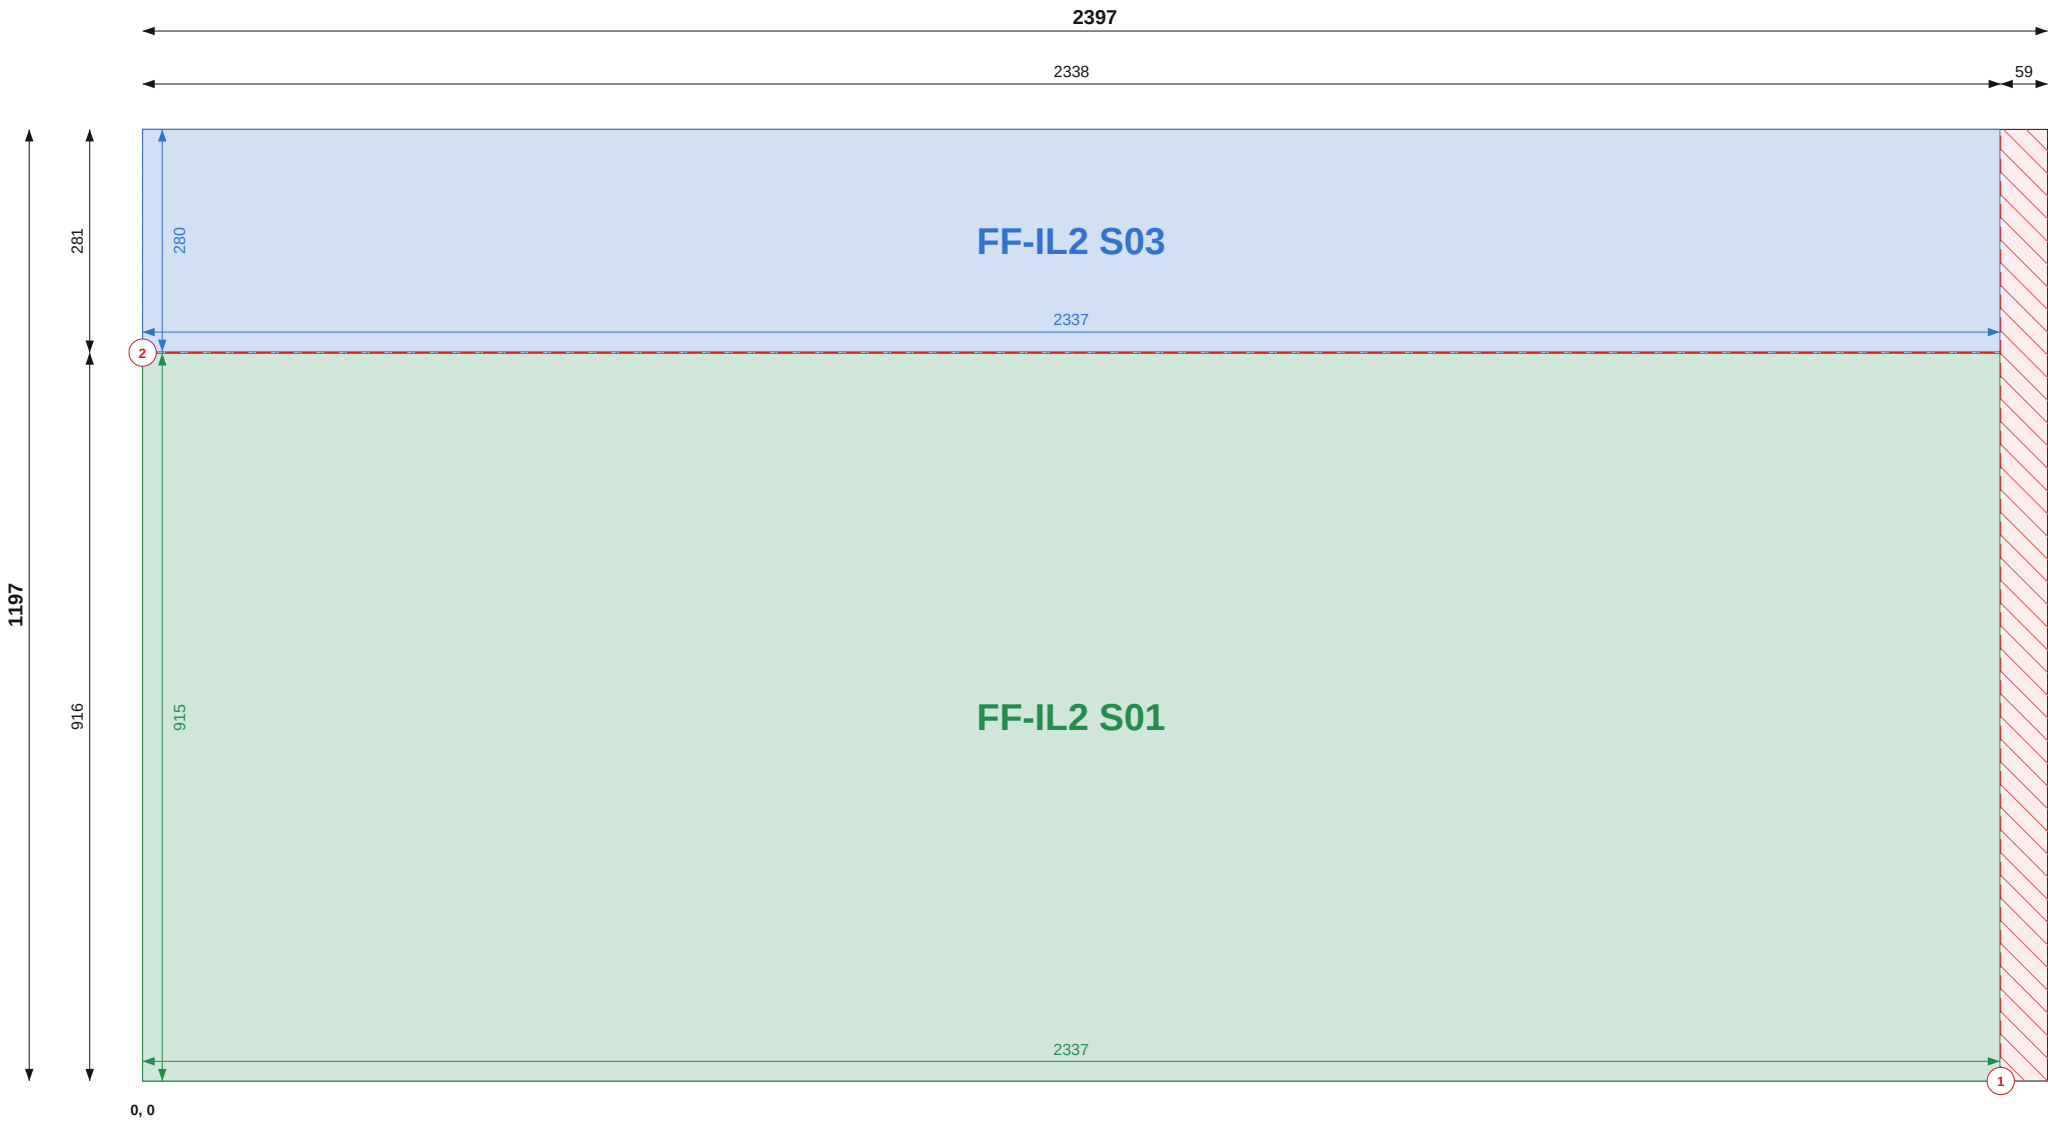

Top / left chains = saw cut positions (to cut centres). Coloured = part size and position.

SHEET 16 OF 34

THIS SHEET

Item	Value
Parts	2
Used / waste	97.3% / 0.08 m2
Reusable offcuts	0
Saw cuts / shared	2 / 1

PIECES (POSITION = BOTTOM-LEFT CORNER)

Label	Size	X, Y
FF-IL2 S03	280 x 2337	0, 917
FF-IL2 S01	915 x 2337	0, 0

NOTES

- Cut from OSB/3 9mm 1197x2397, 2mm saw kerf. Viewed on the face; dimensions from the sheet's bottom-left corner (0,0). Red numbered lines = saw cuts in order, each edge to edge.
- Coloured dimensions belong to the part of that colour: its width and height, and its position from the sheet edges. Raked parts: corner coordinates at each corner.
- Red hatch = waste. Labels = panel + piece mark on the manufacture drawing.

REVISIONS

REV	DATE	DESCRIPTION
C01	13.09.26	Construction issue



TLS TIMBER FRAME

Design & Manufacture

Scan: 3D model + drawings




CLIENT	PROJECT
MP Adams	MP Adams Plot 3, Eckington

DRAWING TITLE			
OSB CUTTING - FIRST FLOOR - SHEET 16 OF 34			
OSB/3 9mm 1197x2397 First Floor			

SCALE	SIZE	DATE	DRAWN
NTS	A3	13.09.26	TS

STATUS	DRAWING No.	REV
CONSTRUCTION	P3-CP-OSB-02 / 16	C01

Do not scale. All dimensions in mm. Check all dimensions on site.

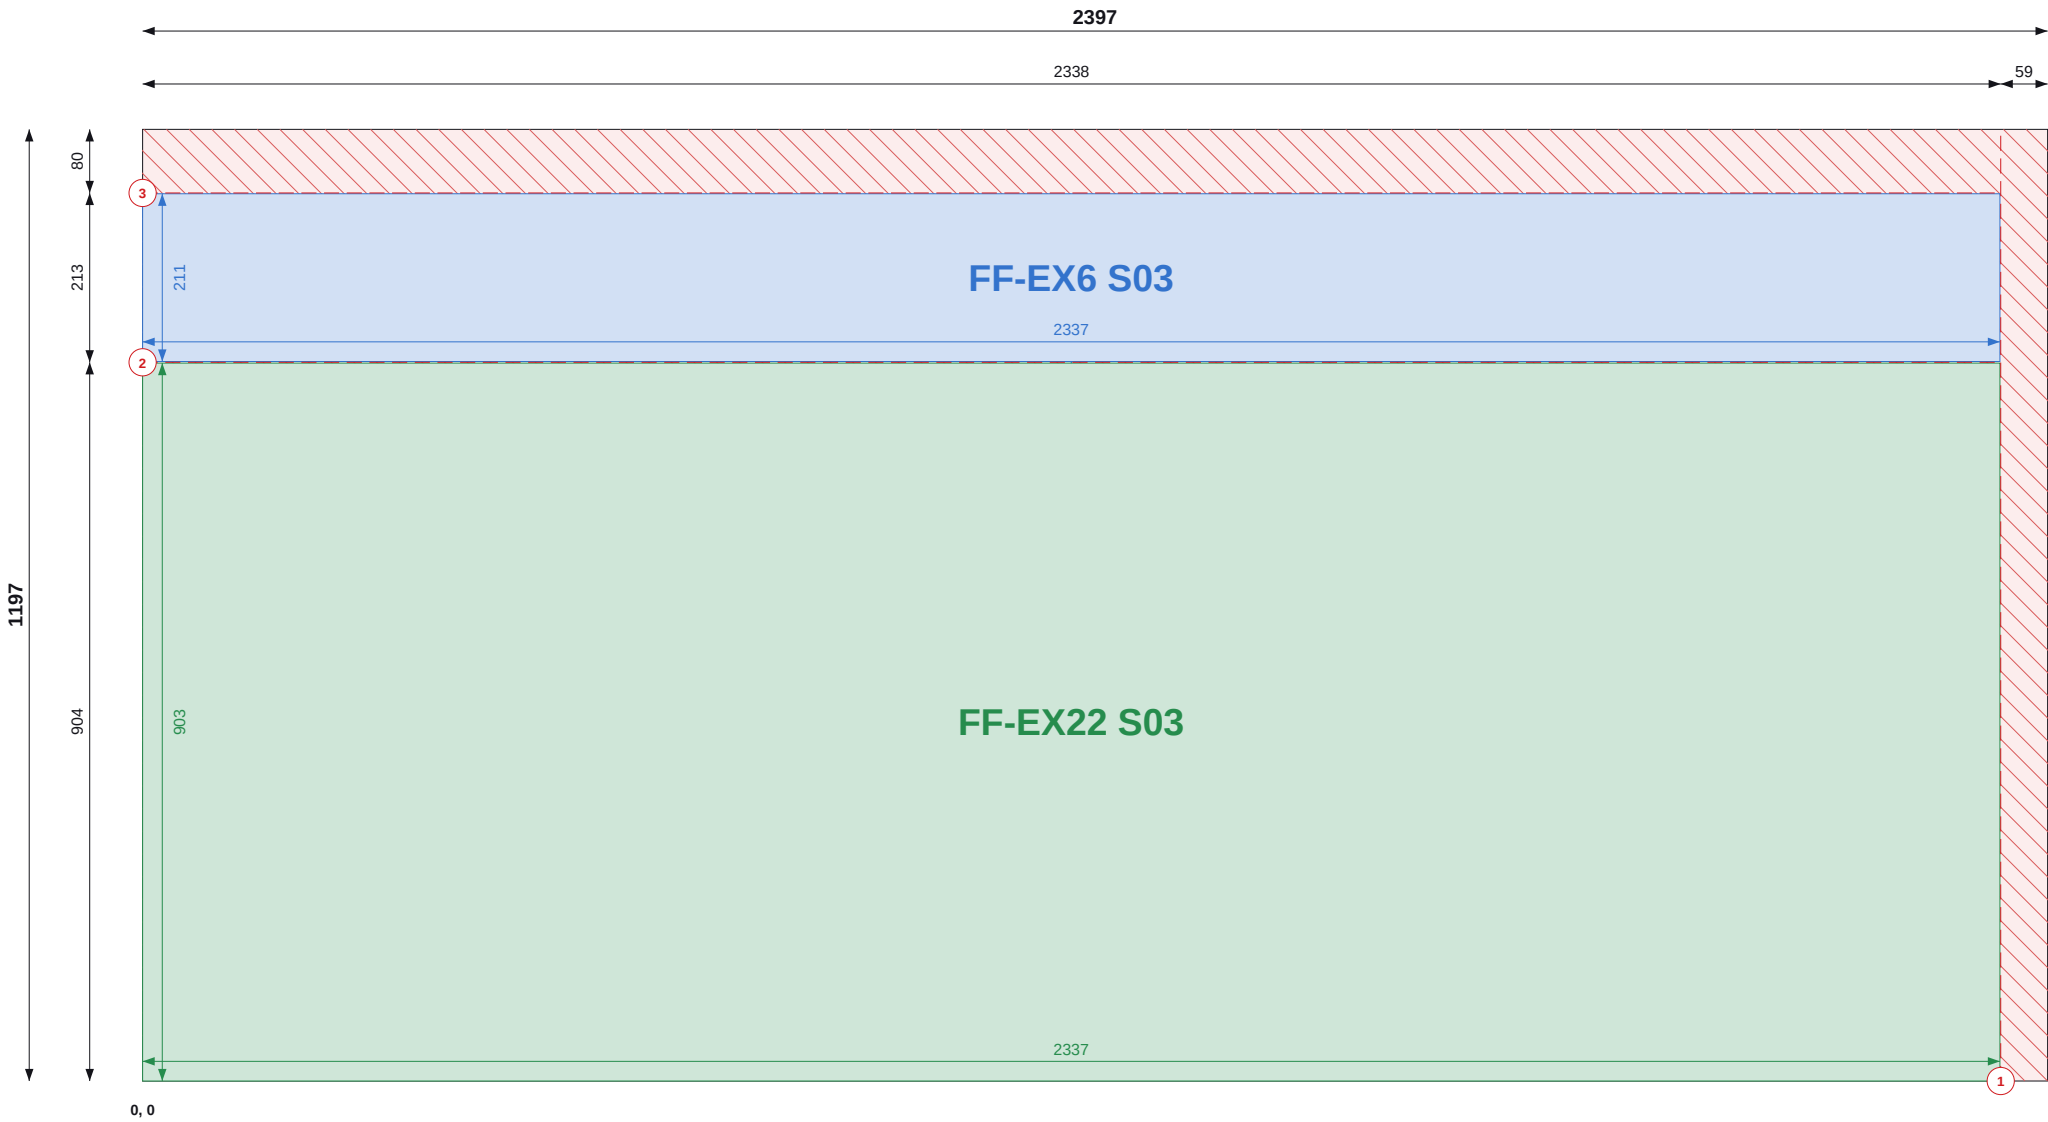

Top / left chains = saw cut positions (to cut centres). Coloured = part size and position.

SHEET 17 OF 34

THIS SHEET

Item	Value
Parts	2
Used / waste	90.7% / 0.27 m2
Reusable offcuts	0
Saw cuts / shared	3 / 1

PIECES (POSITION = BOTTOM-LEFT CORNER)

Label	Size	X, Y
FF-EX6 S03	211 x 2337	0, 905
FF-EX22 S03	903 x 2337	0, 0

NOTES

1. Cut from OSB/3 9mm 1197x2397, 2mm saw kerf. Viewed on the face; dimensions from the sheet's bottom-left corner (0,0). Red numbered lines = saw cuts in order, each edge to edge.
2. Coloured dimensions belong to the part of that colour: its width and height, and its position from the sheet edges. Raked parts: corner coordinates at each corner.
3. Red hatch = waste. Labels = panel + piece mark on the manufacture drawing.

REVISIONS

REV	DATE	DESCRIPTION
C01	13.09.26	Construction issue



TLS TIMBER FRAME

Design & Manufacture

Scan: 3D model + drawings




CLIENT MP Adams	PROJECT MP Adams Plot 3, Eckington
--------------------	---------------------------------------

DRAWING TITLE OSB CUTTING - FIRST FLOOR - SHEET 17 OF 34			
OSB/3 9mm 1197x2397 First Floor			

SCALE NTS	SIZE A3	DATE 13.09.26	DRAWN TS
--------------	------------	------------------	-------------

STATUS CONSTRUCTION	DRAWING No. P3-CP-OSB-02 / 17	REV C01
-------------------------------	---	-------------------

Do not scale. All dimensions in mm. Check all dimensions on site.

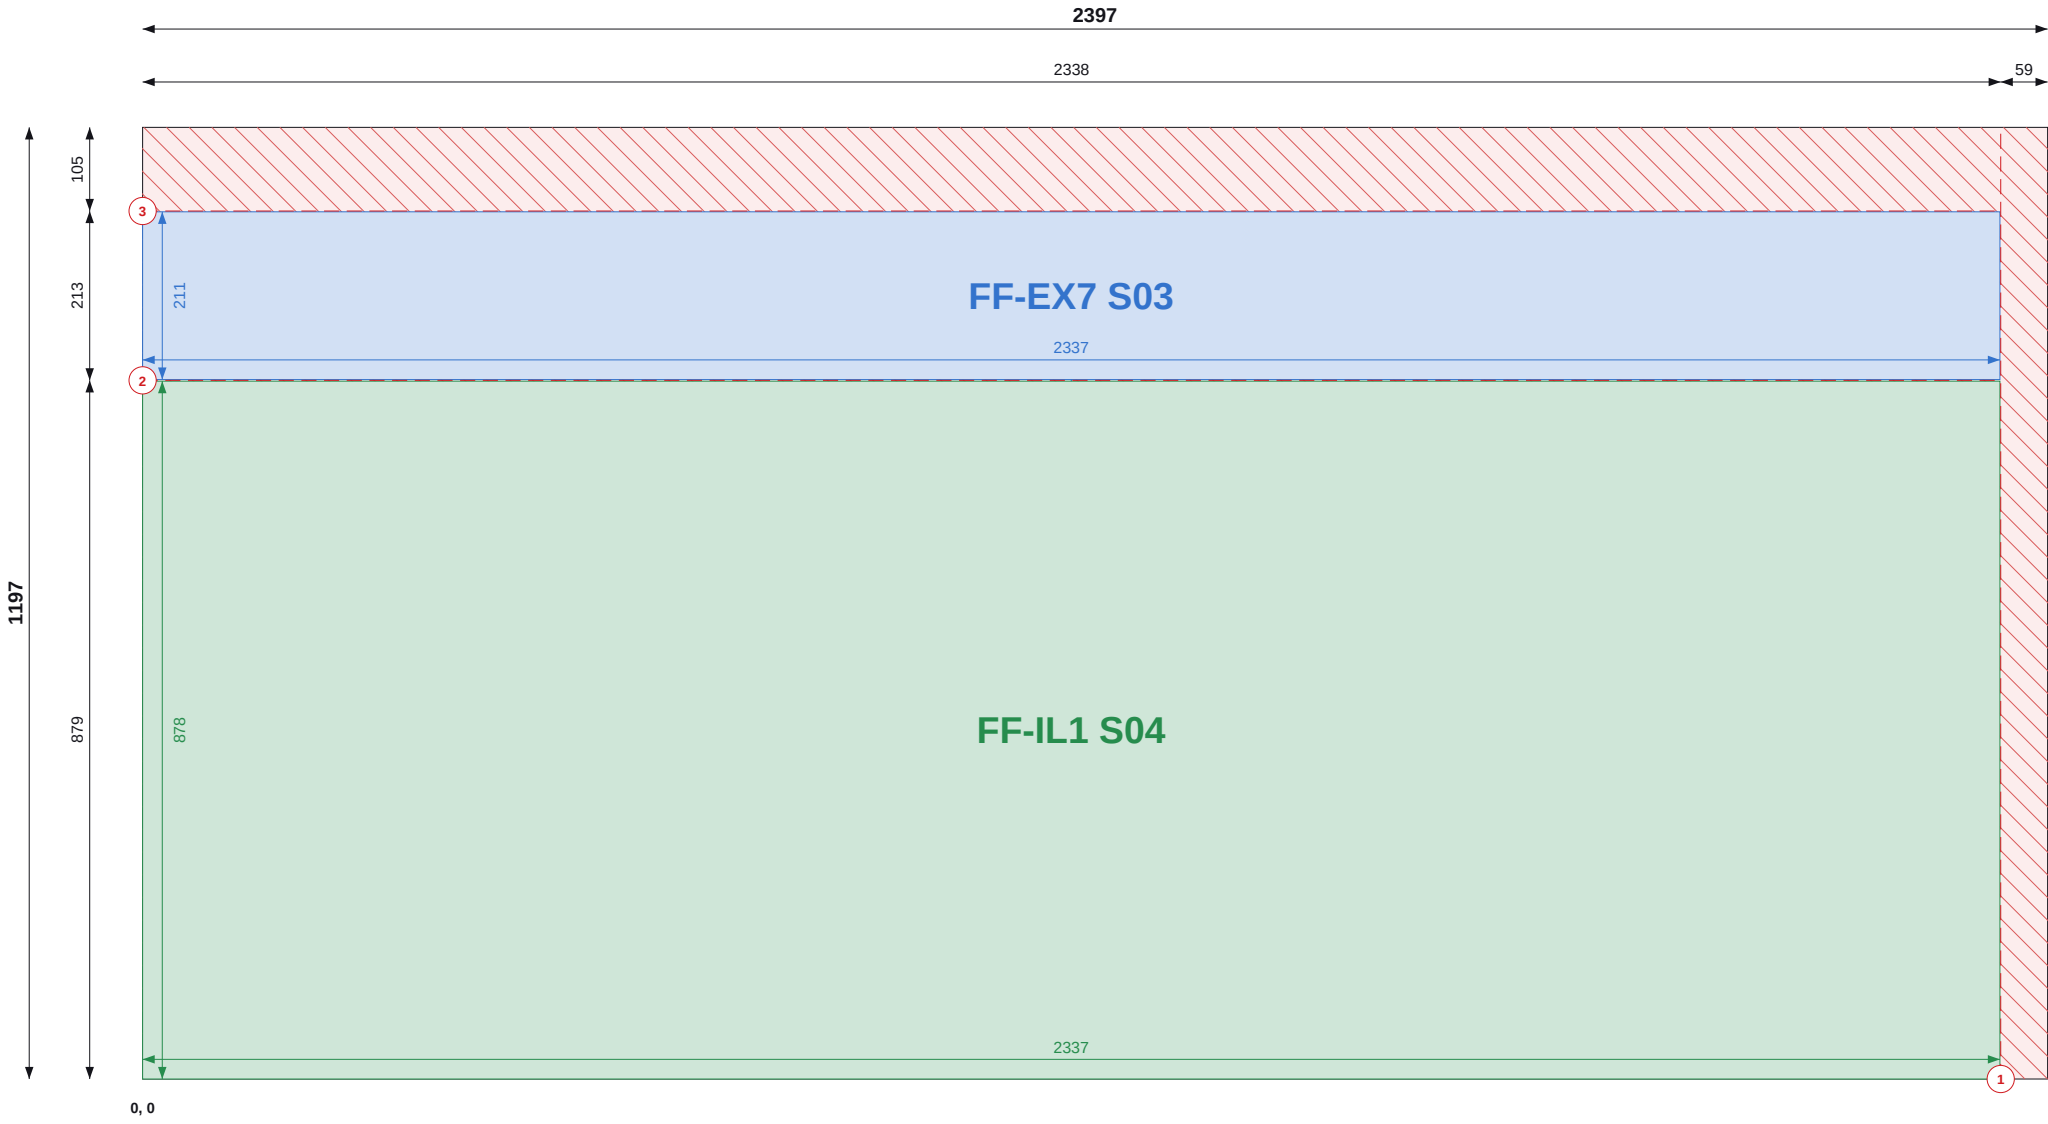

Top / left chains = saw cut positions (to cut centres). Coloured = part size and position.

SHEET 18 OF 34

THIS SHEET

Item	Value
Parts	2
Used / waste	88.7% / 0.32 m2
Reusable offcuts	0
Saw cuts / shared	3 / 1

PIECES (POSITION = BOTTOM-LEFT CORNER)

Label	Size	X, Y
FF-EX7 S03	211 x 2337	0, 880
FF-IL1 S04	878 x 2337	0, 0

NOTES

- Cut from OSB/3 9mm 1197x2397, 2mm saw kerf. Viewed on the face; dimensions from the sheet's bottom-left corner (0,0). Red numbered lines = saw cuts in order, each edge to edge.
- Coloured dimensions belong to the part of that colour: its width and height, and its position from the sheet edges. Raked parts: corner coordinates at each corner.
- Red hatch = waste. Labels = panel + piece mark on the manufacture drawing.

REVISIONS

REV	DATE	DESCRIPTION
C01	13.09.26	Construction issue



TLS TIMBER FRAME

Design & Manufacture

Scan: 3D model + drawings




CLIENT	PROJECT
MP Adams	MP Adams Plot 3, Eckington

DRAWING TITLE			
OSB CUTTING - FIRST FLOOR - SHEET 18 OF 34			
OSB/3 9mm 1197x2397 First Floor			

SCALE	SIZE	DATE	DRAWN
NTS	A3	13.09.26	TS

STATUS	DRAWING No.	REV
CONSTRUCTION	P3-CP-OSB-02 / 18	C01

Do not scale. All dimensions in mm. Check all dimensions on site.

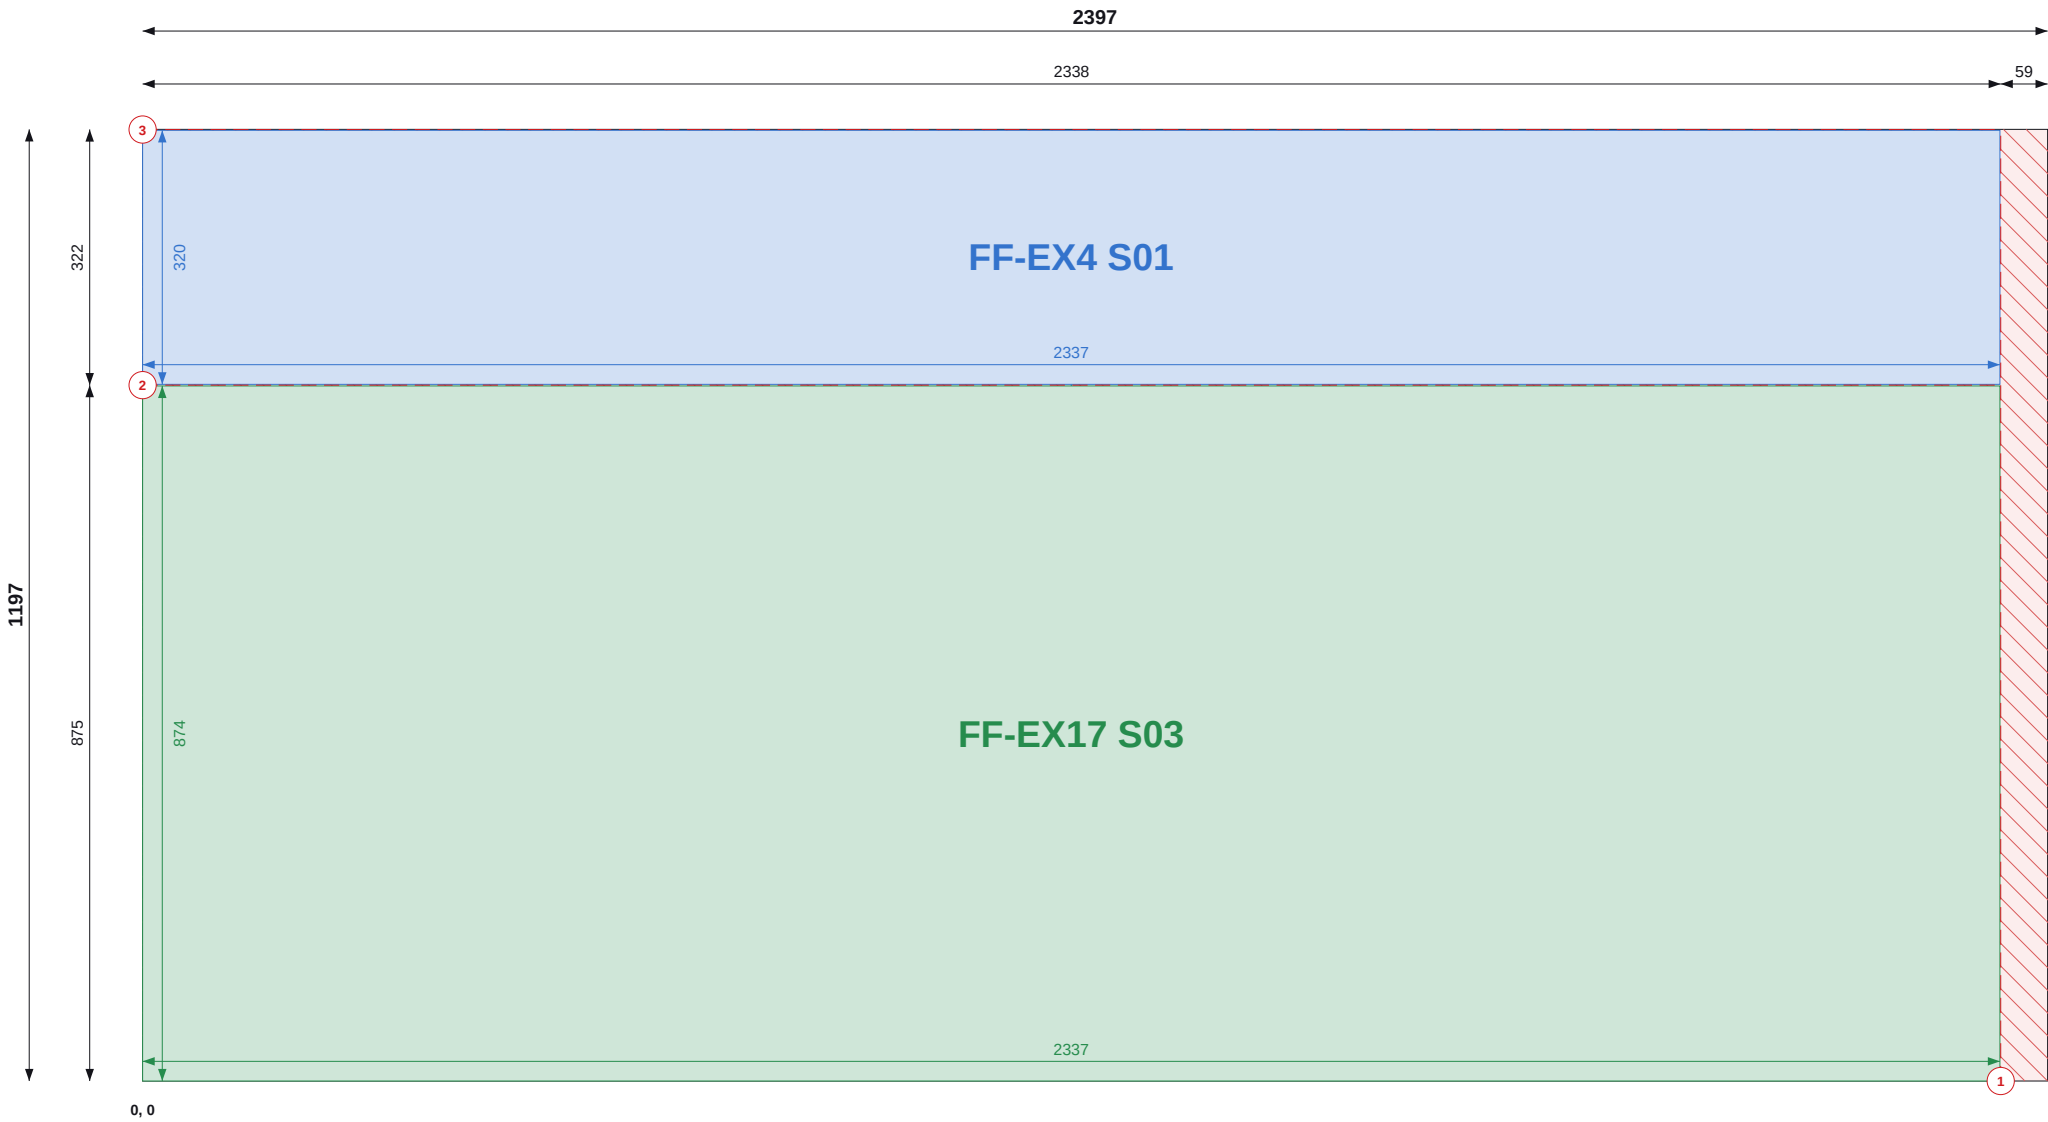

Top / left chains = saw cut positions (to cut centres). Coloured = part size and position.

SHEET 19 OF 34

THIS SHEET

Item	Value
Parts	2
Used / waste	97.2% / 0.08 m2
Reusable offcuts	0
Saw cuts / shared	3 / 1

PIECES (POSITION = BOTTOM-LEFT CORNER)

Label	Size	X, Y
FF-EX4 S01	320 x 2337	0, 876
FF-EX17 S03	874 x 2337	0, 0

NOTES

- Cut from OSB/3 9mm 1197x2397, 2mm saw kerf. Viewed on the face; dimensions from the sheet's bottom-left corner (0,0). Red numbered lines = saw cuts in order, each edge to edge.
- Coloured dimensions belong to the part of that colour: its width and height, and its position from the sheet edges. Raked parts: corner coordinates at each corner.
- Red hatch = waste. Labels = panel + piece mark on the manufacture drawing.

REVISIONS

REV	DATE	DESCRIPTION
C01	13.09.26	Construction issue



TLS TIMBER FRAME

Design & Manufacture

Scan: 3D model + drawings




CLIENT MP Adams	PROJECT MP Adams Plot 3, Eckington
--------------------	---------------------------------------

DRAWING TITLE OSB CUTTING - FIRST FLOOR - SHEET 19 OF 34			
OSB/3 9mm 1197x2397 First Floor			

SCALE NTS	SIZE A3	DATE 13.09.26	DRAWN TS
--------------	------------	------------------	-------------

STATUS CONSTRUCTION	DRAWING No. P3-CP-OSB-02 / 19	REV C01
-------------------------------	---	-------------------

Do not scale. All dimensions in mm. Check all dimensions on site.

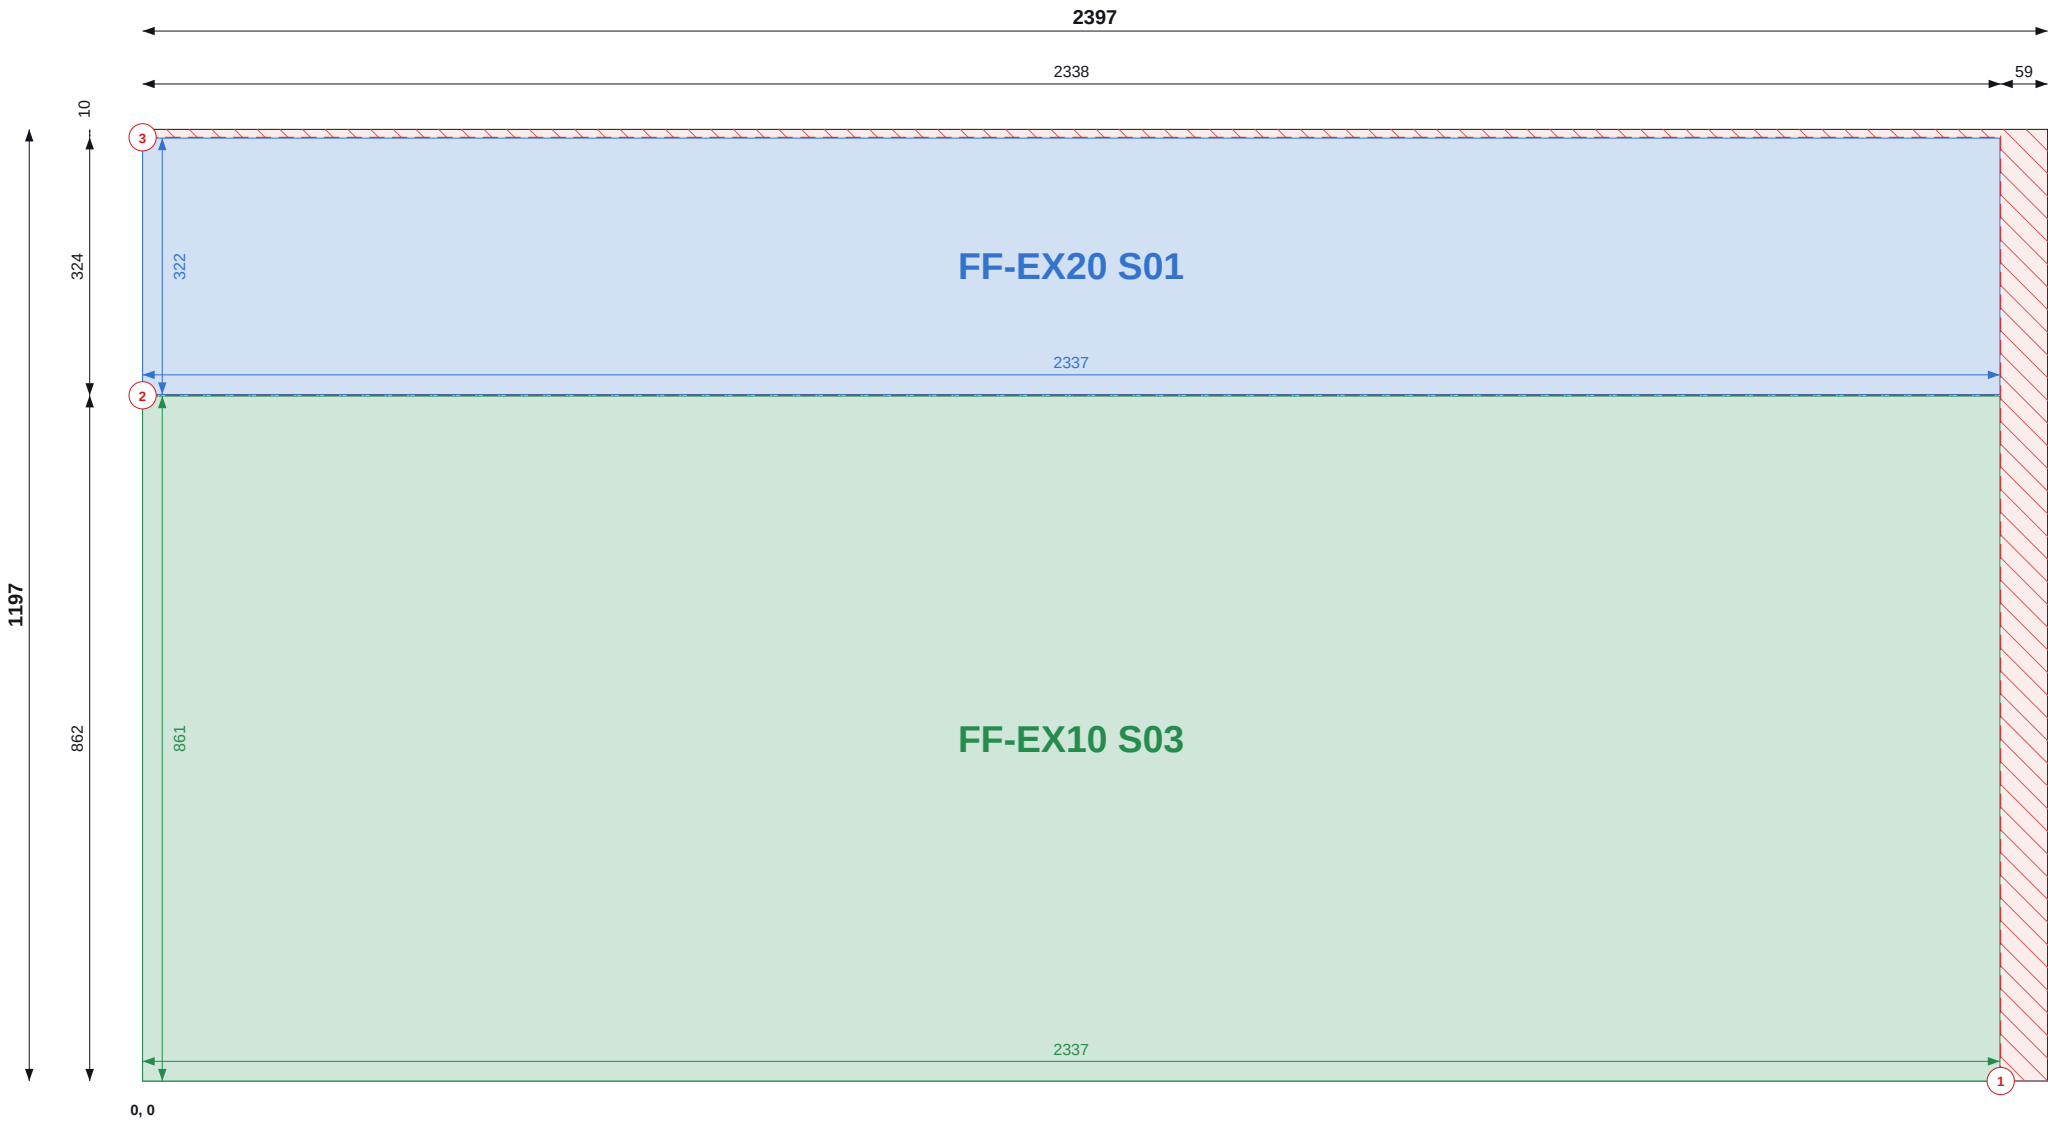

Top / left chains = saw cut positions (to cut centres). Coloured = part size and position.

SHEET 20 OF 34

THIS SHEET

Item	Value
Parts	2
Used / waste	96.4% / 0.10 m2
Reusable offcuts	0
Saw cuts / shared	3 / 1

PIECES (POSITION = BOTTOM-LEFT CORNER)

Label	Size	X, Y
FF-EX20 S01	322 x 2337	0, 863
FF-EX10 S03	861 x 2337	0, 0

NOTES

- Cut from OSB/3 9mm 1197x2397, 2mm saw kerf. Viewed on the face; dimensions from the sheet's bottom-left corner (0,0). Red numbered lines = saw cuts in order, each edge to edge.
- Coloured dimensions belong to the part of that colour: its width and height, and its position from the sheet edges. Raked parts: corner coordinates at each corner.
- Red hatch = waste. Labels = panel + piece mark on the manufacture drawing.

REVISIONS

REV	DATE	DESCRIPTION
C01	13.09.26	Construction issue



TLS TIMBER FRAME

Design & Manufacture

Scan: 3D model + drawings




CLIENT MP Adams	PROJECT MP Adams Plot 3, Eckington
--------------------	---------------------------------------

DRAWING TITLE OSB CUTTING - FIRST FLOOR - SHEET 20 OF 34			
OSB/3 9mm 1197x2397 First Floor			

SCALE NTS	SIZE A3	DATE 13.09.26	DRAWN TS
--------------	------------	------------------	-------------

STATUS CONSTRUCTION	DRAWING No. P3-CP-OSB-02 / 20	REV C01
-------------------------------	---	-------------------

Do not scale. All dimensions in mm. Check all dimensions on site.

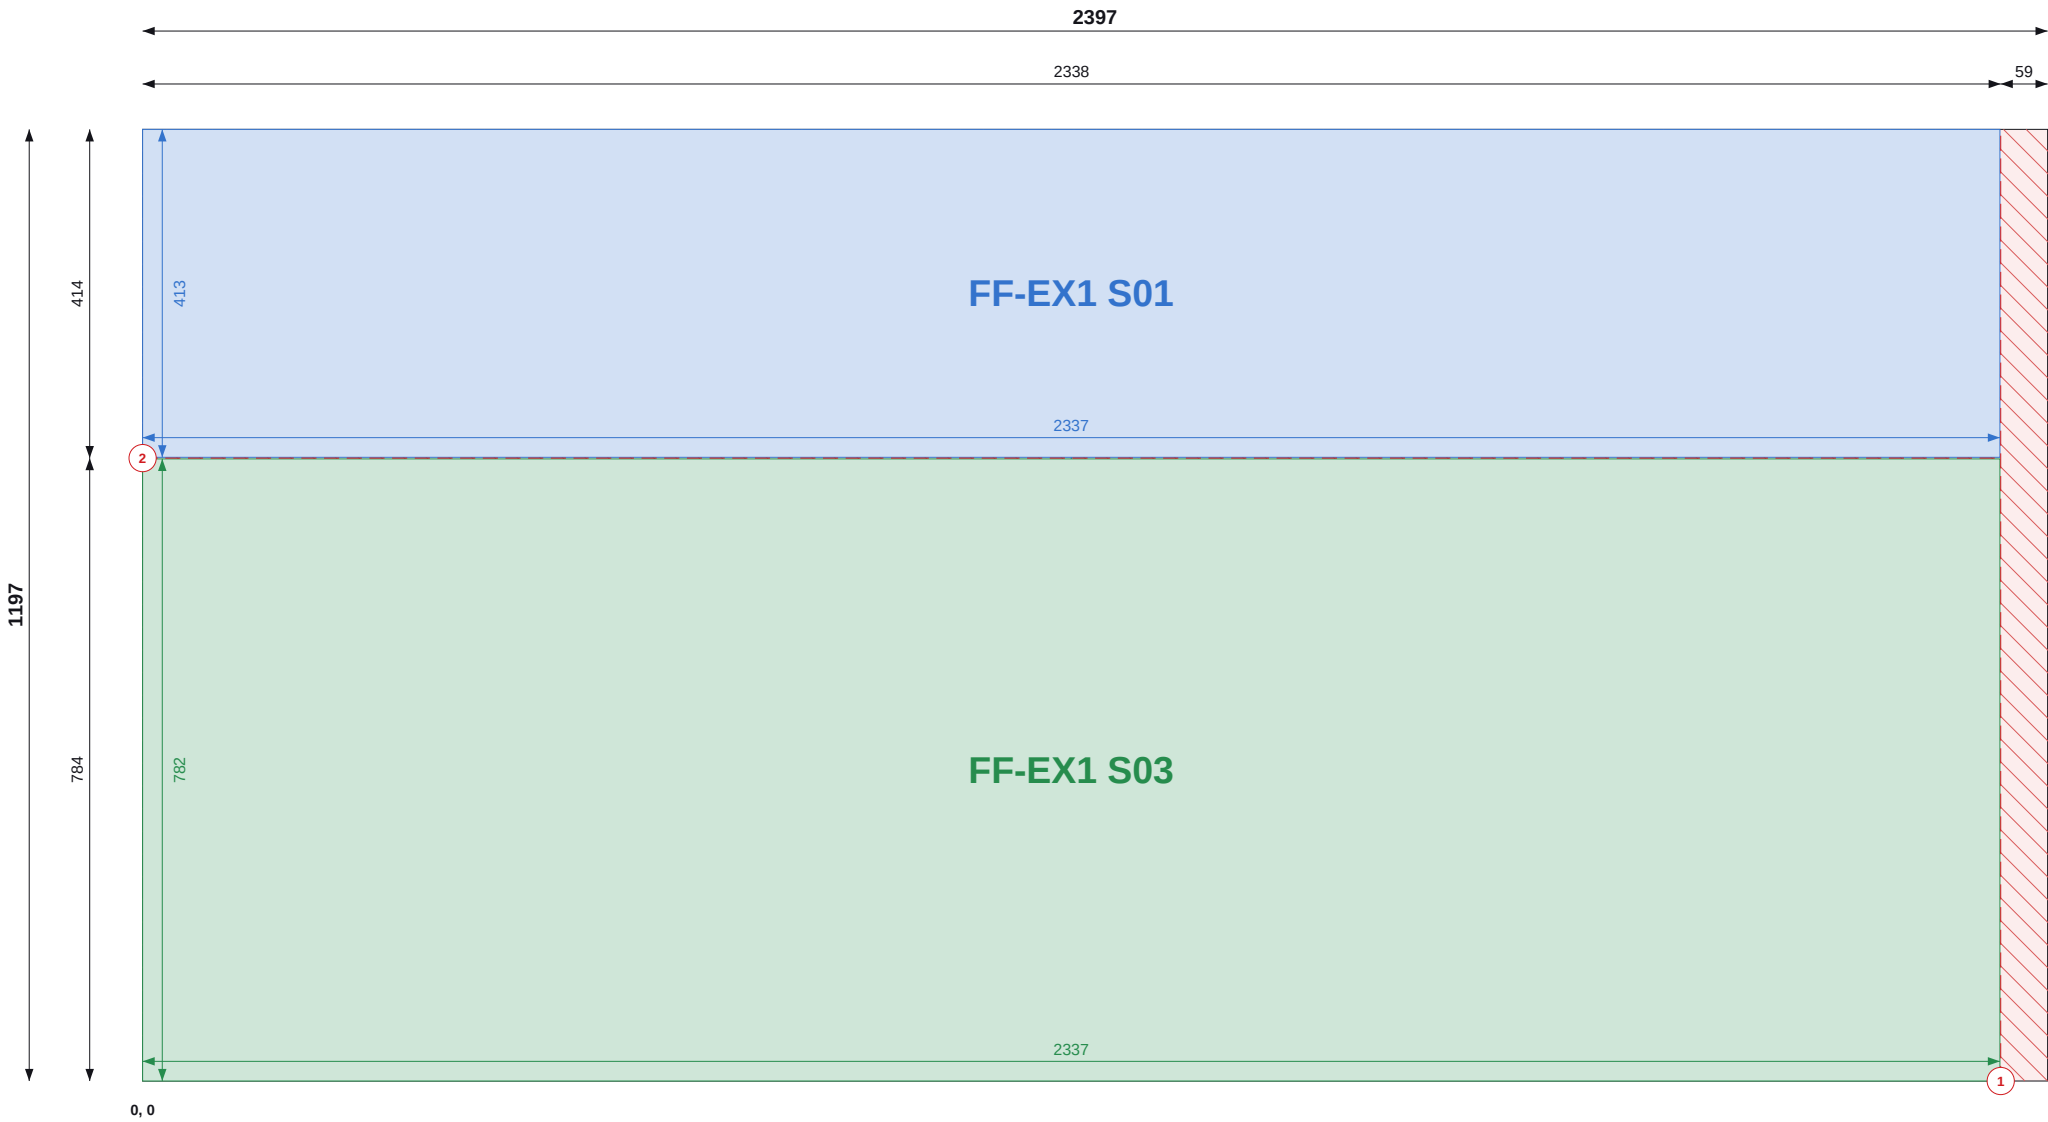

Top / left chains = saw cut positions (to cut centres). Coloured = part size and position.

SHEET 21 OF 34

THIS SHEET

Item	Value
Parts	2
Used / waste	97.3% / 0.08 m2
Reusable offcuts	0
Saw cuts / shared	2 / 1

PIECES (POSITION = BOTTOM-LEFT CORNER)

Label	Size	X, Y
FF-EX1 S01	413 x 2337	0, 784
FF-EX1 S03	782 x 2337	0, 0

NOTES

- Cut from OSB/3 9mm 1197x2397, 2mm saw kerf. Viewed on the face; dimensions from the sheet's bottom-left corner (0,0). Red numbered lines = saw cuts in order, each edge to edge.
- Coloured dimensions belong to the part of that colour: its width and height, and its position from the sheet edges. Raked parts: corner coordinates at each corner.
- Red hatch = waste. Labels = panel + piece mark on the manufacture drawing.

REVISIONS

REV	DATE	DESCRIPTION
C01	13.09.26	Construction issue



TLS TIMBER FRAME

Design & Manufacture

Scan: 3D model + drawings




CLIENT MP Adams	PROJECT MP Adams Plot 3, Eckington
--------------------	---------------------------------------

DRAWING TITLE OSB CUTTING - FIRST FLOOR - SHEET 21 OF 34			
OSB/3 9mm 1197x2397 First Floor			

SCALE NTS	SIZE A3	DATE 13.09.26	DRAWN TS
--------------	------------	------------------	-------------

STATUS CONSTRUCTION	DRAWING No. P3-CP-OSB-02 / 21	REV C01
-------------------------------	---	-------------------

Do not scale. All dimensions in mm. Check all dimensions on site.

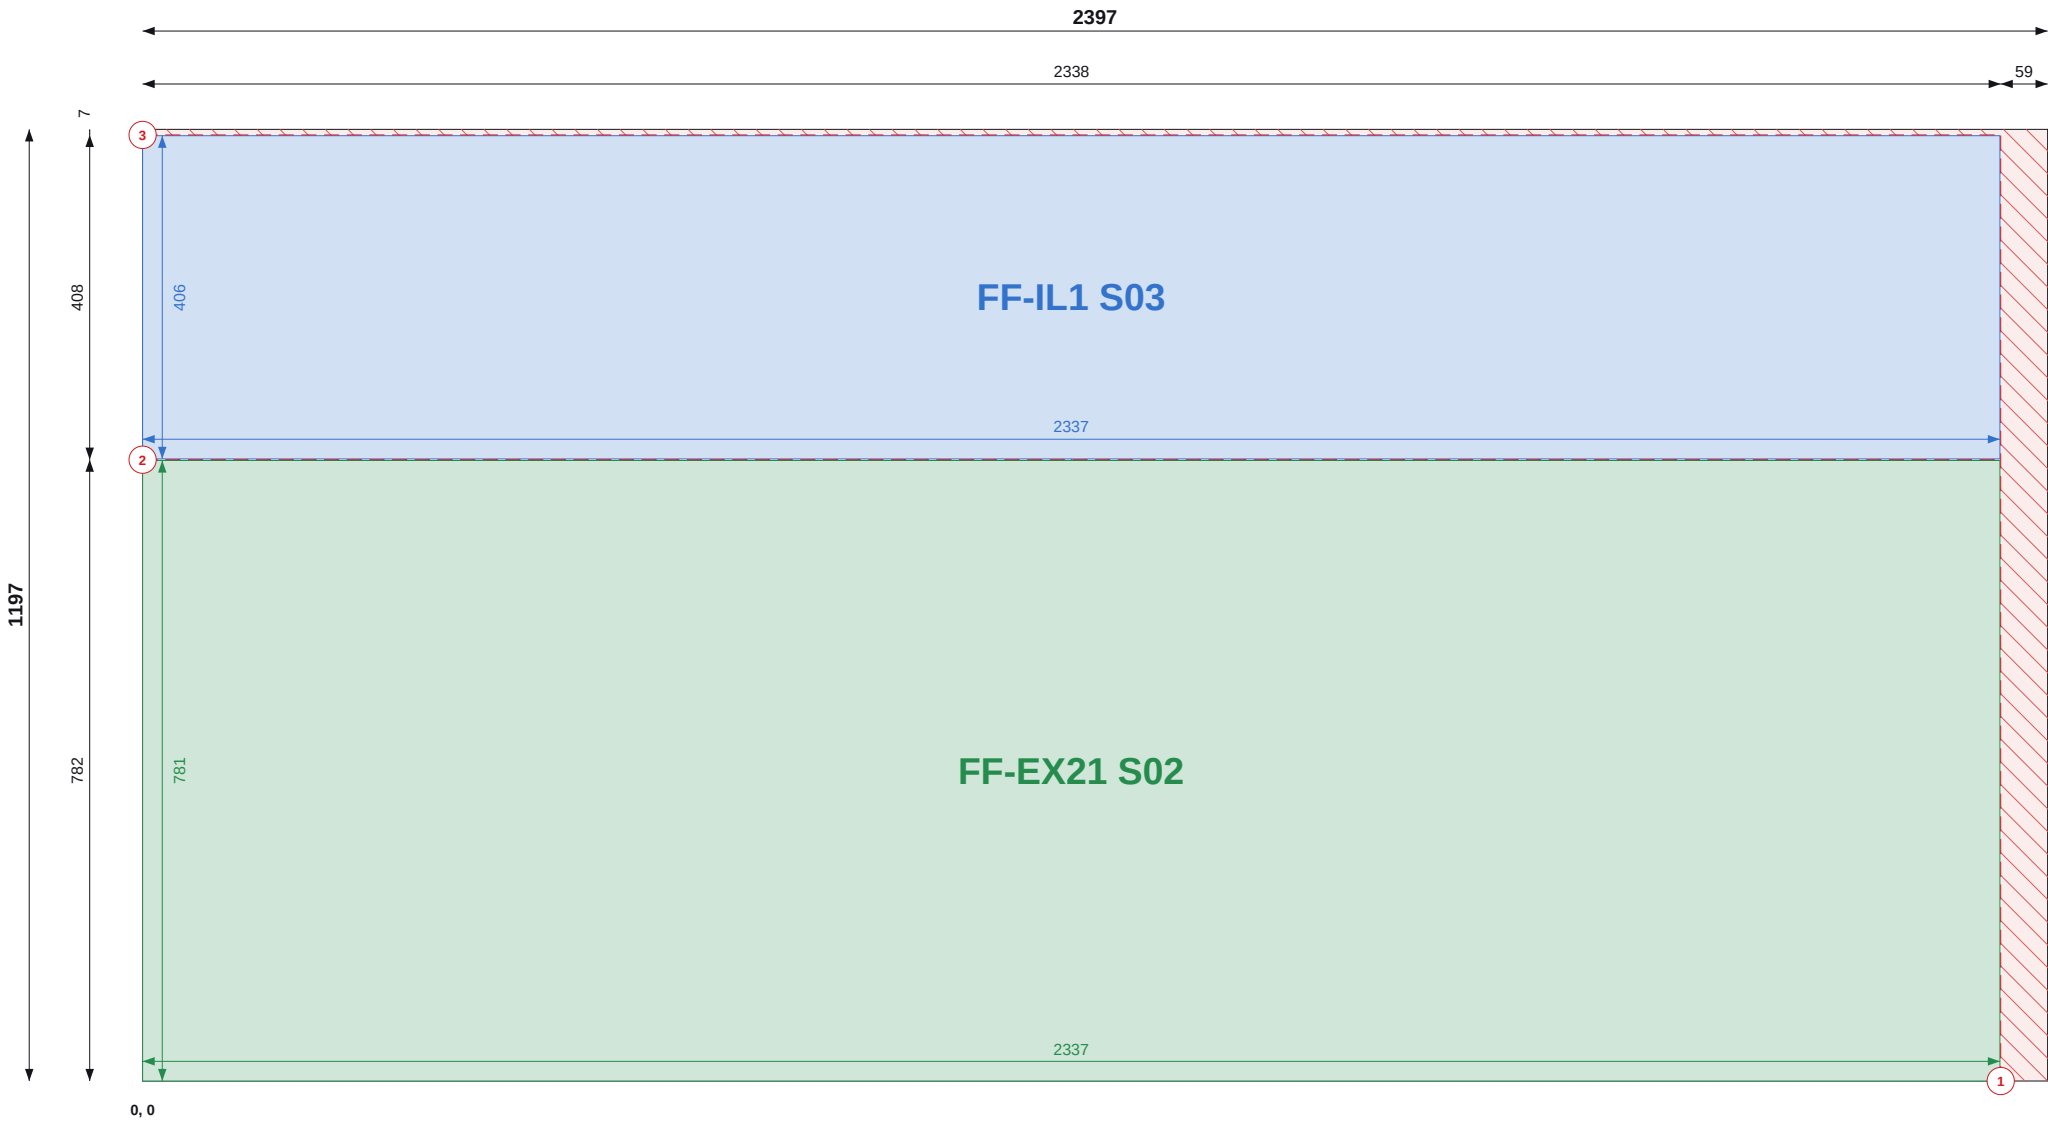

Top / left chains = saw cut positions (to cut centres). Coloured = part size and position.

SHEET 22 OF 34

THIS SHEET

Item	Value
Parts	2
Used / waste	96.7% / 0.10 m2
Reusable offcuts	0
Saw cuts / shared	3 / 1

PIECES (POSITION = BOTTOM-LEFT CORNER)

Label	Size	X, Y
FF-IL1 S03	406 x 2337	0, 783
FF-EX21 S02	781 x 2337	0, 0

NOTES

- Cut from OSB/3 9mm 1197x2397, 2mm saw kerf. Viewed on the face; dimensions from the sheet's bottom-left corner (0,0). Red numbered lines = saw cuts in order, each edge to edge.
- Coloured dimensions belong to the part of that colour: its width and height, and its position from the sheet edges. Raked parts: corner coordinates at each corner.
- Red hatch = waste. Labels = panel + piece mark on the manufacture drawing.

REVISIONS

REV	DATE	DESCRIPTION
C01	13.09.26	Construction issue



TLS TIMBER FRAME

Design & Manufacture

Scan: 3D model + drawings




CLIENT MP Adams	PROJECT MP Adams Plot 3, Eckington
--------------------	---------------------------------------

DRAWING TITLE OSB CUTTING - FIRST FLOOR - SHEET 22 OF 34 OSB/3 9mm 1197x2397 First Floor			
SCALE NTS	SIZE A3	DATE 13.09.26	DRAWN TS

STATUS CONSTRUCTION	DRAWING No. P3-CP-OSB-02 / 22	REV C01
-------------------------------	---	-------------------

Do not scale. All dimensions in mm. Check all dimensions on site.

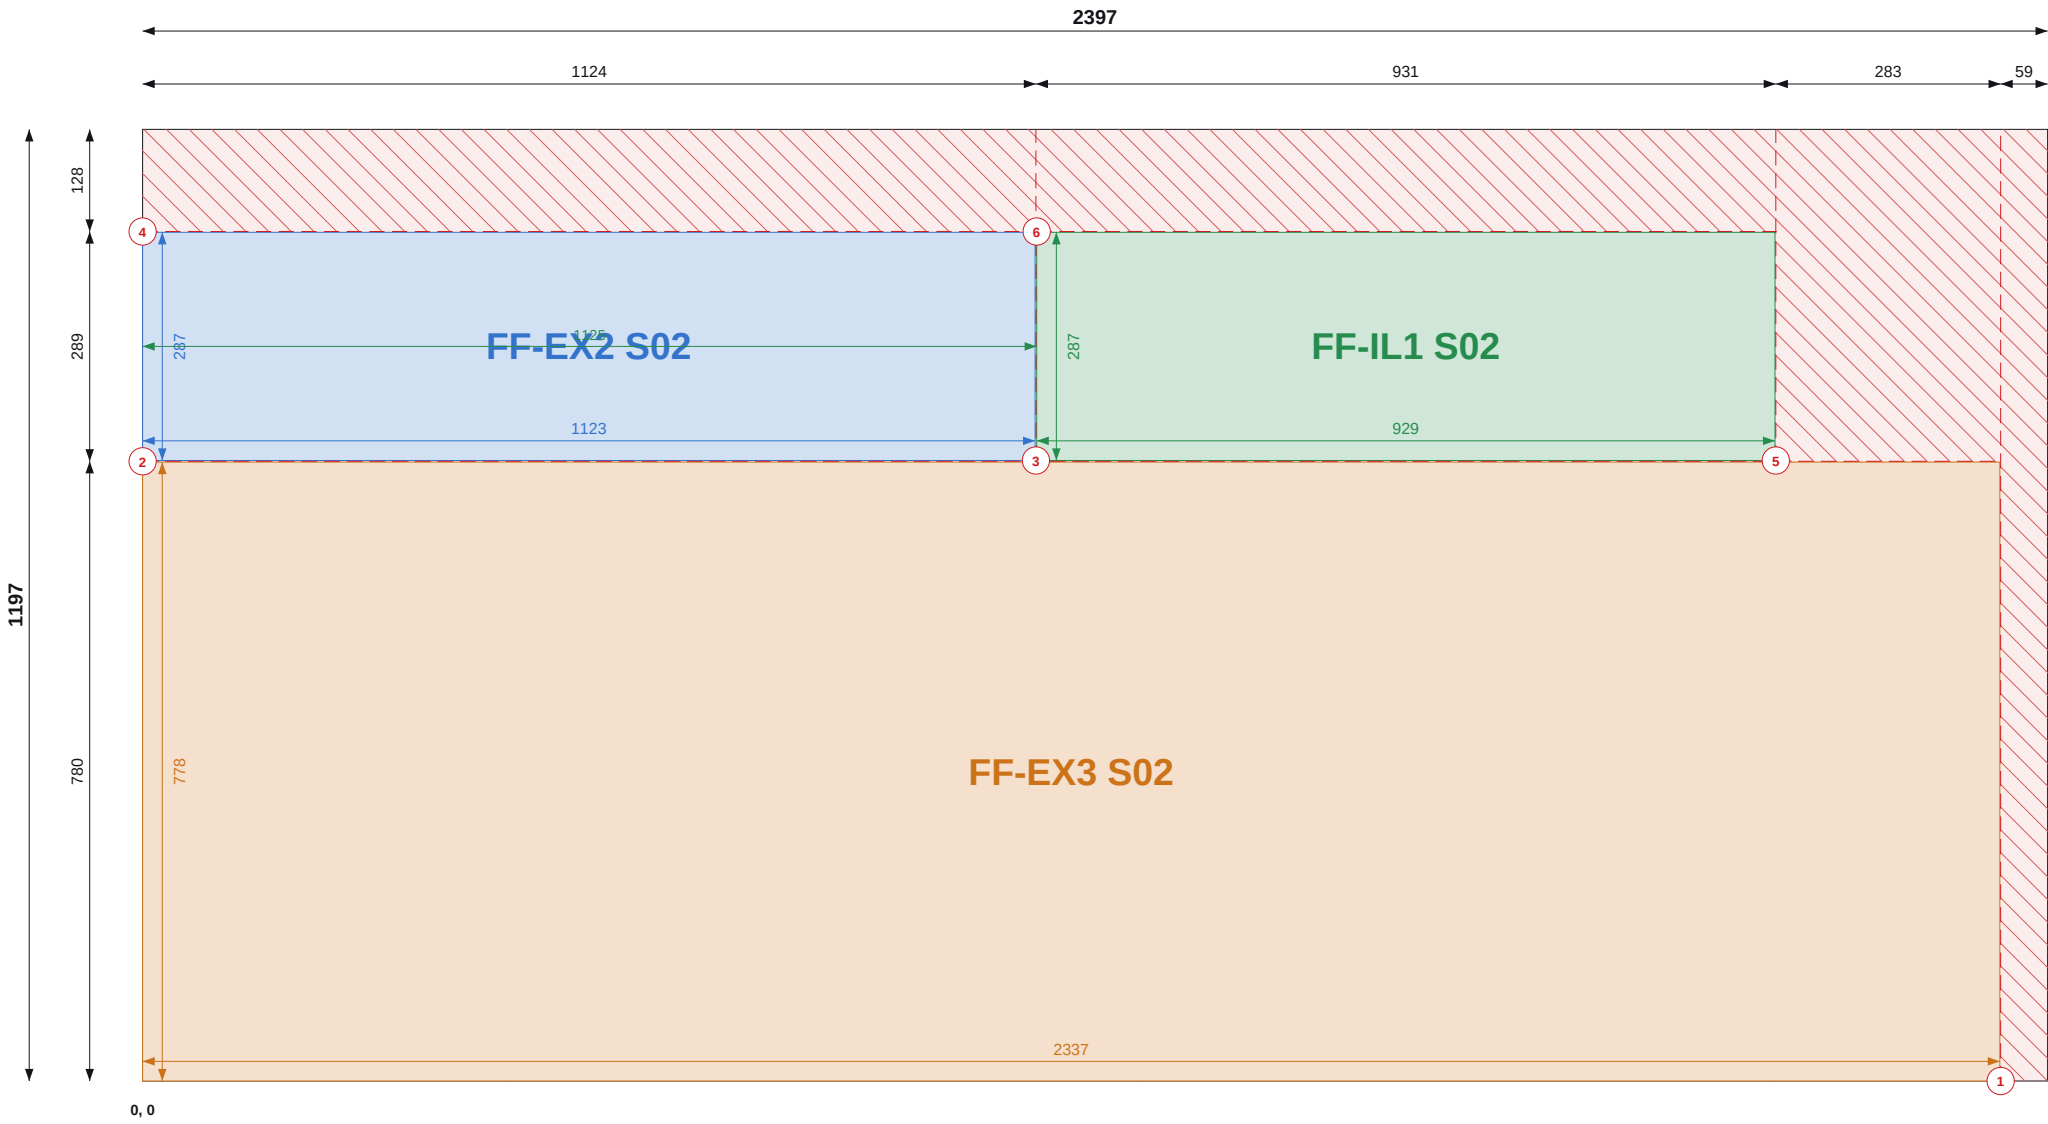

Top / left chains = saw cut positions (to cut centres). Coloured = part size and position.

SHEET 23 OF 34

THIS SHEET

Item	Value
Parts	3
Used / waste	83.9% / 0.46 m2
Reusable offcuts	0
Saw cuts / shared	6 / 2

PIECES (POSITION = BOTTOM-LEFT CORNER)

Label	Size	X, Y
FF-EX2 S02	1123 x 287	0, 780
FF-IL1 S02	929 x 287	1125, 780
FF-EX3 S02	778 x 2337	0, 0

NOTES

- Cut from OSB/3 9mm 1197x2397, 2mm saw kerf. Viewed on the face; dimensions from the sheet's bottom-left corner (0,0). Red numbered lines = saw cuts in order, each edge to edge.
- Coloured dimensions belong to the part of that colour: its width and height, and its position from the sheet edges. Raked parts: corner coordinates at each corner.
- Red hatch = waste. Labels = panel + piece mark on the manufacture drawing.

REVISIONS

REV	DATE	DESCRIPTION
C01	13.09.26	Construction issue



TLS TIMBER FRAME

Design & Manufacture

Scan: 3D model + drawings



CLIENT	PROJECT
MP Adams	MP Adams Plot 3, Eckington


DRAWING TITLE
OSB CUTTING - FIRST FLOOR - SHEET 23 OF 34

OSB/3 9mm 1197x2397 | First Floor

SCALE	SIZE	DATE	DRAWN
NTS	A3	13.09.26	TS

STATUS	DRAWING No.	REV
CONSTRUCTION	P3-CP-OSB-02 / 23	C01

Do not scale. All dimensions in mm. Check all dimensions on site.

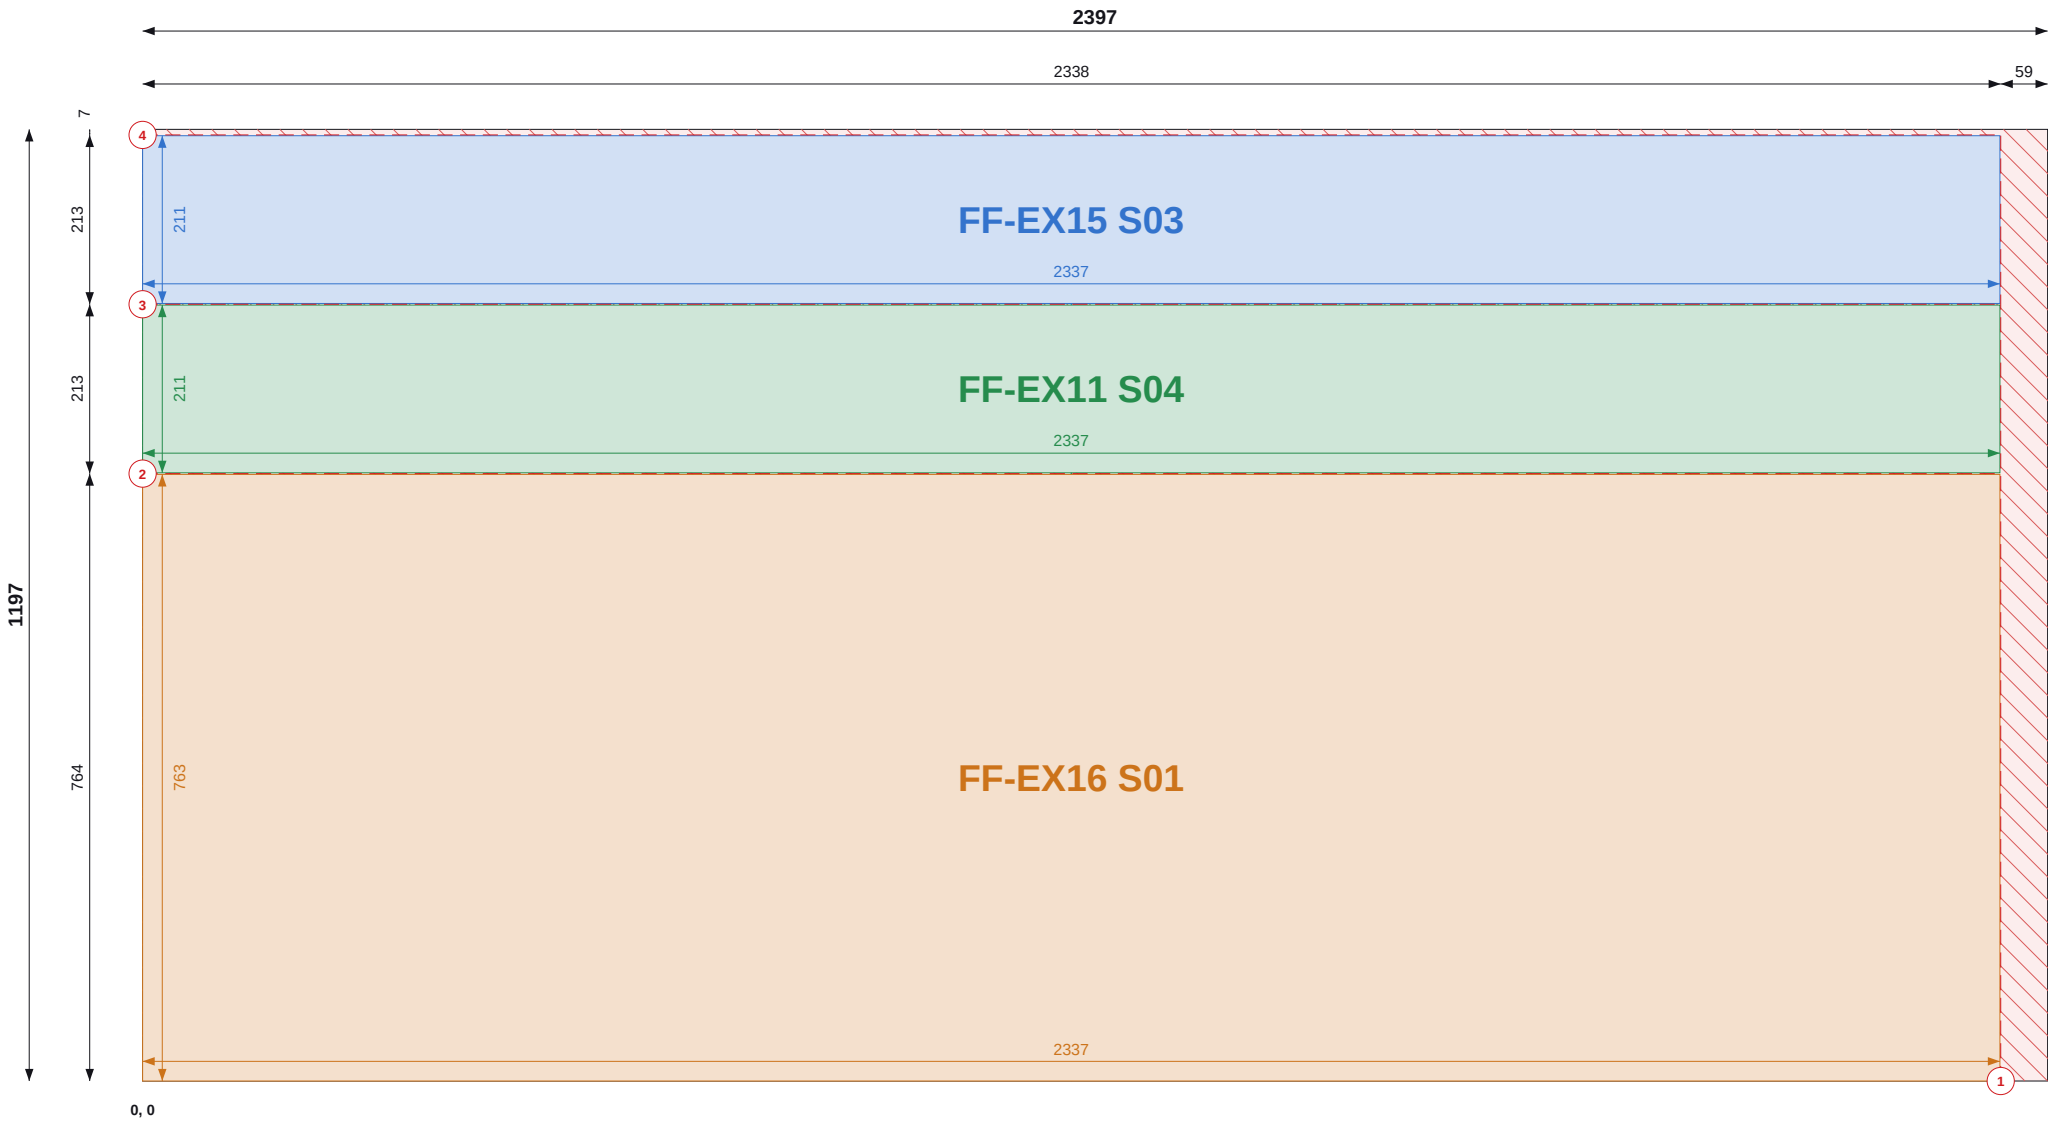

Top / left chains = saw cut positions (to cut centres). Coloured = part size and position.

SHEET 24 OF 34

THIS SHEET

Item	Value
Parts	3
Used / waste	96.5% / 0.10 m2
Reusable offcuts	0
Saw cuts / shared	4 / 2

PIECES (POSITION = BOTTOM-LEFT CORNER)

Label	Size	X, Y
FF-EX15 S03	211 x 2337	0, 978
FF-EX11 S04	211 x 2337	0, 765
FF-EX16 S01	763 x 2337	0, 0

NOTES

- Cut from OSB/3 9mm 1197x2397, 2mm saw kerf. Viewed on the face; dimensions from the sheet's bottom-left corner (0,0). Red numbered lines = saw cuts in order, each edge to edge.
- Coloured dimensions belong to the part of that colour: its width and height, and its position from the sheet edges. Raked parts: corner coordinates at each corner.
- Red hatch = waste. Labels = panel + piece mark on the manufacture drawing.

REVISIONS

REV	DATE	DESCRIPTION
C01	13.09.26	Construction issue



TLS TIMBER FRAME

Design & Manufacture

Scan: 3D model + drawings



CLIENT	PROJECT
MP Adams	MP Adams Plot 3, Eckington


DRAWING TITLE
OSB CUTTING - FIRST FLOOR - SHEET 24 OF 34

OSB/3 9mm 1197x2397 | First Floor

SCALE	SIZE	DATE	DRAWN
NTS	A3	13.09.26	TS

STATUS	DRAWING No.	REV
CONSTRUCTION	P3-CP-OSB-02 / 24	C01

Do not scale. All dimensions in mm. Check all dimensions on site.

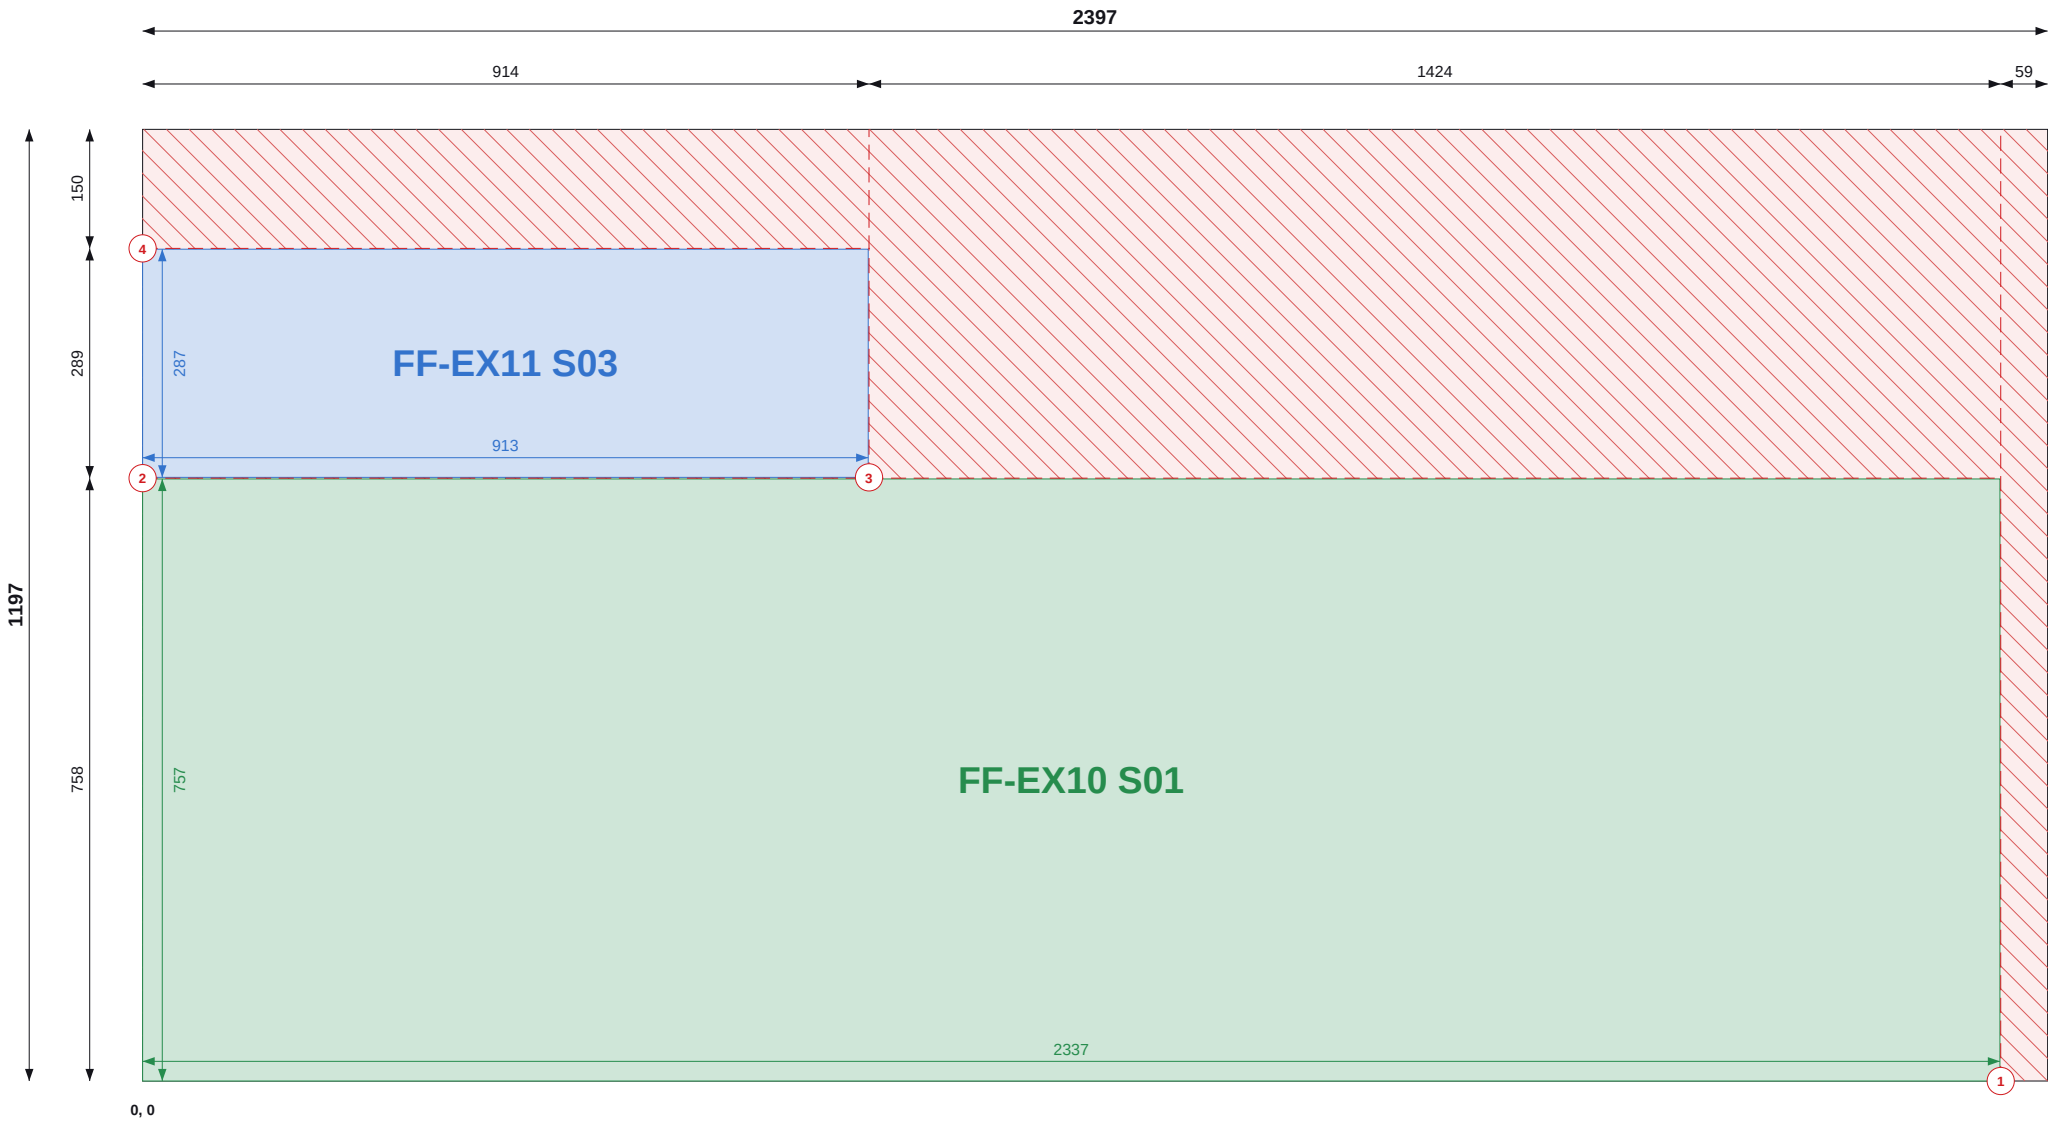

Top / left chains = saw cut positions (to cut centres). Coloured = part size and position.

SHEET 25 OF 34

THIS SHEET

Item	Value
Parts	2
Used / waste	70.8% / 0.84 m2
Reusable offcuts	1
Saw cuts / shared	4 / 1

PIECES (POSITION = BOTTOM-LEFT CORNER)

Label	Size	X, Y
FF-EX11 S03	913 x 287	0, 759
FF-EX10 S01	757 x 2337	0, 0

NOTES

- Cut from OSB/3 9mm 1197x2397, 2mm saw kerf. Viewed on the face; dimensions from the sheet's bottom-left corner (0,0). Red numbered lines = saw cuts in order, each edge to edge.
- Coloured dimensions belong to the part of that colour: its width and height, and its position from the sheet edges. Raked parts: corner coordinates at each corner.
- Red hatch = waste. Labels = panel + piece mark on the manufacture drawing.

REVISIONS

REV	DATE	DESCRIPTION
C01	13.09.26	Construction issue



TLS TIMBER FRAME

Design & Manufacture

Scan: 3D model + drawings



CLIENT	PROJECT
MP Adams	MP Adams Plot 3, Eckington

DRAWING TITLE
OSB CUTTING - FIRST FLOOR - SHEET 25 OF 34
OSB/3 9mm 1197x2397 First Floor

SCALE	SIZE	DATE	DRAWN
NTS	A3	13.09.26	TS

STATUS	DRAWING No.	REV
CONSTRUCTION	P3-CP-OSB-02 / 25	C01

Do not scale. All dimensions in mm. Check all dimensions on site.



Top / left chains = saw cut positions (to cut centres). Coloured = part size and position.

SHEET 26 OF 34

THIS SHEET

Item	Value
Parts	2
Used / waste	97.3% / 0.08 m2
Reusable offcuts	0
Saw cuts / shared	2 / 1

PIECES (POSITION = BOTTOM-LEFT CORNER)

Label	Size	X, Y
FF-EX14 S01	439 x 2337	0, 758
FF-EX14 S03	756 x 2337	0, 0

NOTES

- Cut from OSB/3 9mm 1197x2397, 2mm saw kerf. Viewed on the face; dimensions from the sheet's bottom-left corner (0,0). Red numbered lines = saw cuts in order, each edge to edge.
- Coloured dimensions belong to the part of that colour: its width and height, and its position from the sheet edges. Raked parts: corner coordinates at each corner.
- Red hatch = waste. Labels = panel + piece mark on the manufacture drawing.

REVISIONS

REV	DATE	DESCRIPTION
C01	13.09.26	Construction issue



TLS TIMBER FRAME

Design & Manufacture

Scan: 3D model + drawings




CLIENT	PROJECT
MP Adams	MP Adams Plot 3, Eckington

DRAWING TITLE			
OSB CUTTING - FIRST FLOOR - SHEET 26 OF 34			
OSB/3 9mm 1197x2397 First Floor			

SCALE	SIZE	DATE	DRAWN
NTS	A3	13.09.26	TS

STATUS	DRAWING No.	REV
CONSTRUCTION	P3-CP-OSB-02 / 26	C01

Do not scale. All dimensions in mm. Check all dimensions on site.

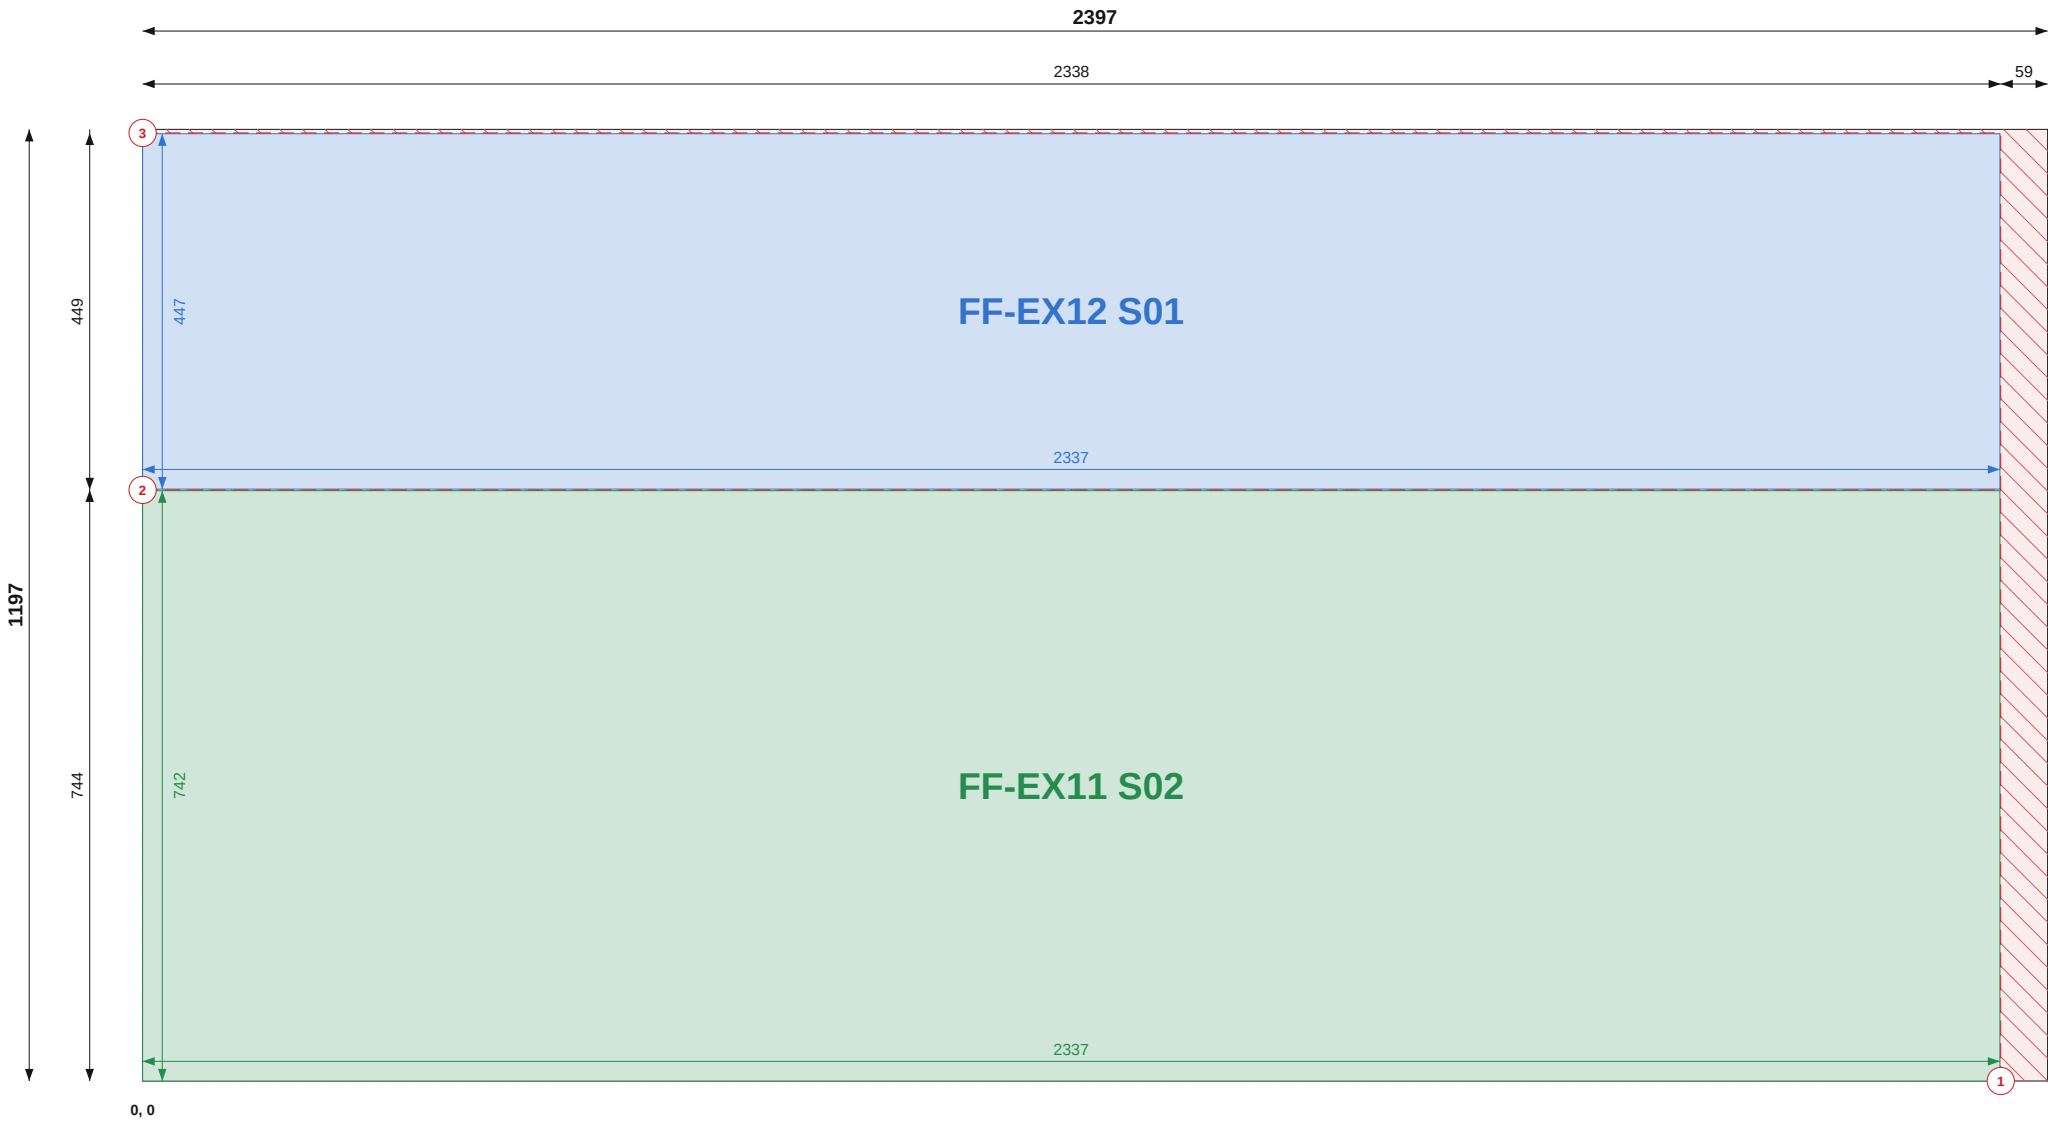

Top / left chains = saw cut positions (to cut centres). Coloured = part size and position.

SHEET 27 OF 34

THIS SHEET

Item	Value
Parts	2
Used / waste	96.9% / 0.09 m2
Reusable offcuts	0
Saw cuts / shared	3 / 1

PIECES (POSITION = BOTTOM-LEFT CORNER)

Label	Size	X, Y
FF-EX12 S01	447 x 2337	0, 744
FF-EX11 S02	742 x 2337	0, 0

NOTES

- Cut from OSB/3 9mm 1197x2397, 2mm saw kerf. Viewed on the face; dimensions from the sheet's bottom-left corner (0,0). Red numbered lines = saw cuts in order, each edge to edge.
- Coloured dimensions belong to the part of that colour: its width and height, and its position from the sheet edges. Raked parts: corner coordinates at each corner.
- Red hatch = waste. Labels = panel + piece mark on the manufacture drawing.

REVISIONS

REV	DATE	DESCRIPTION
C01	13.09.26	Construction issue



TLS TIMBER FRAME

Design & Manufacture

Scan: 3D model + drawings




CLIENT MP Adams	PROJECT MP Adams Plot 3, Eckington
--------------------	---------------------------------------

DRAWING TITLE OSB CUTTING - FIRST FLOOR - SHEET 27 OF 34			
OSB/3 9mm 1197x2397 First Floor			

SCALE NTS	SIZE A3	DATE 13.09.26	DRAWN TS
--------------	------------	------------------	-------------

STATUS CONSTRUCTION	DRAWING No. P3-CP-OSB-02 / 27	REV C01
-------------------------------	---	-------------------

Do not scale. All dimensions in mm. Check all dimensions on site.

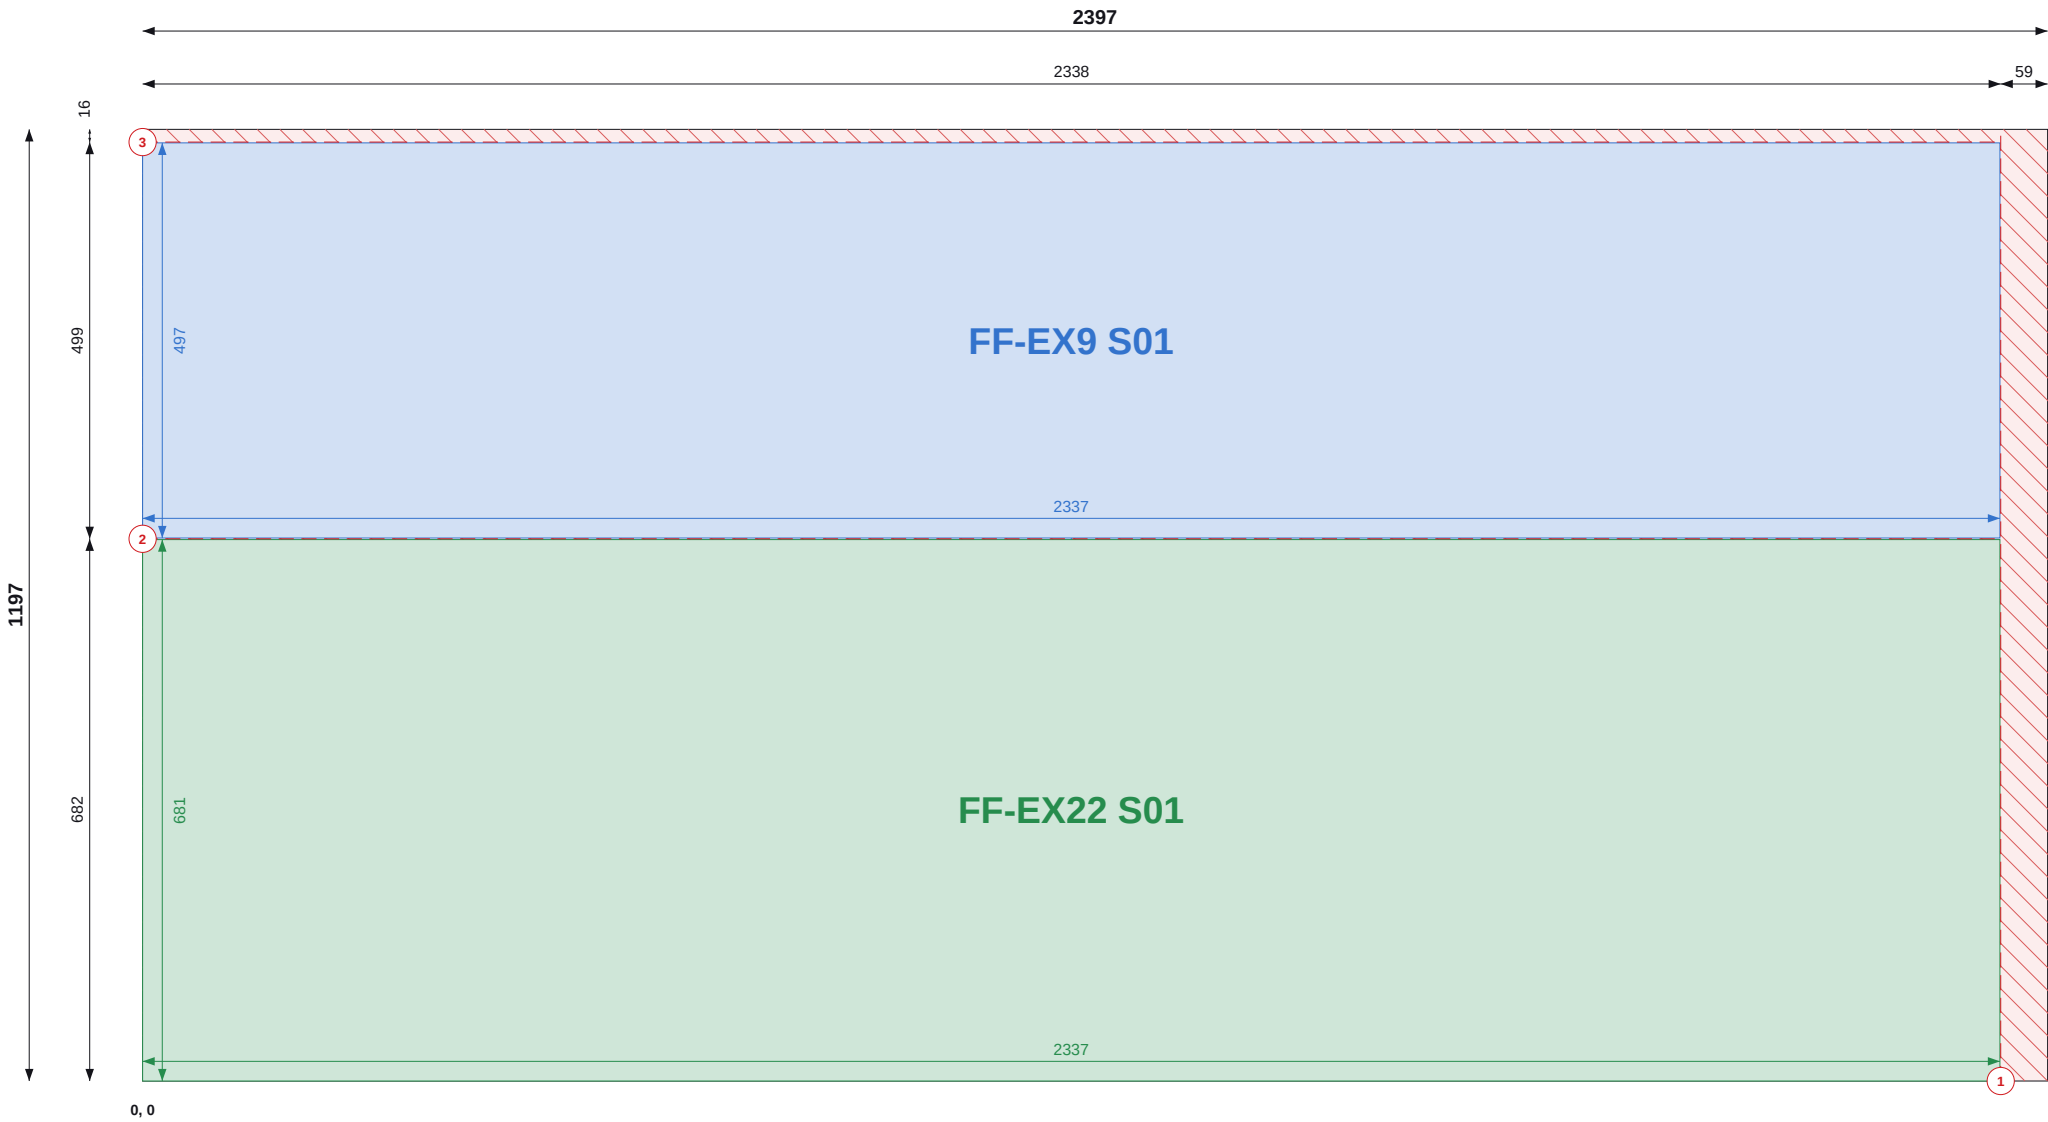

Top / left chains = saw cut positions (to cut centres). Coloured = part size and position.

SHEET 28 OF 34

THIS SHEET

Item	Value
Parts	2
Used / waste	95.9% / 0.12 m2
Reusable offcuts	0
Saw cuts / shared	3 / 1

PIECES (POSITION = BOTTOM-LEFT CORNER)

Label	Size	X, Y
FF-EX9 S01	497 x 2337	0, 683
FF-EX22 S01	681 x 2337	0, 0

NOTES

- Cut from OSB/3 9mm 1197x2397, 2mm saw kerf. Viewed on the face; dimensions from the sheet's bottom-left corner (0,0). Red numbered lines = saw cuts in order, each edge to edge.
- Coloured dimensions belong to the part of that colour: its width and height, and its position from the sheet edges. Raked parts: corner coordinates at each corner.
- Red hatch = waste. Labels = panel + piece mark on the manufacture drawing.

REVISIONS

REV	DATE	DESCRIPTION
C01	13.09.26	Construction issue



TLS TIMBER FRAME

Design & Manufacture

Scan: 3D model + drawings



CLIENT	PROJECT
MP Adams	MP Adams Plot 3, Eckington


DRAWING TITLE
OSB CUTTING - FIRST FLOOR - SHEET 28 OF 34

OSB/3 9mm 1197x2397 | First Floor

SCALE	SIZE	DATE	DRAWN
NTS	A3	13.09.26	TS

STATUS	DRAWING No.	REV
CONSTRUCTION	P3-CP-OSB-02 / 28	C01

Do not scale. All dimensions in mm. Check all dimensions on site.

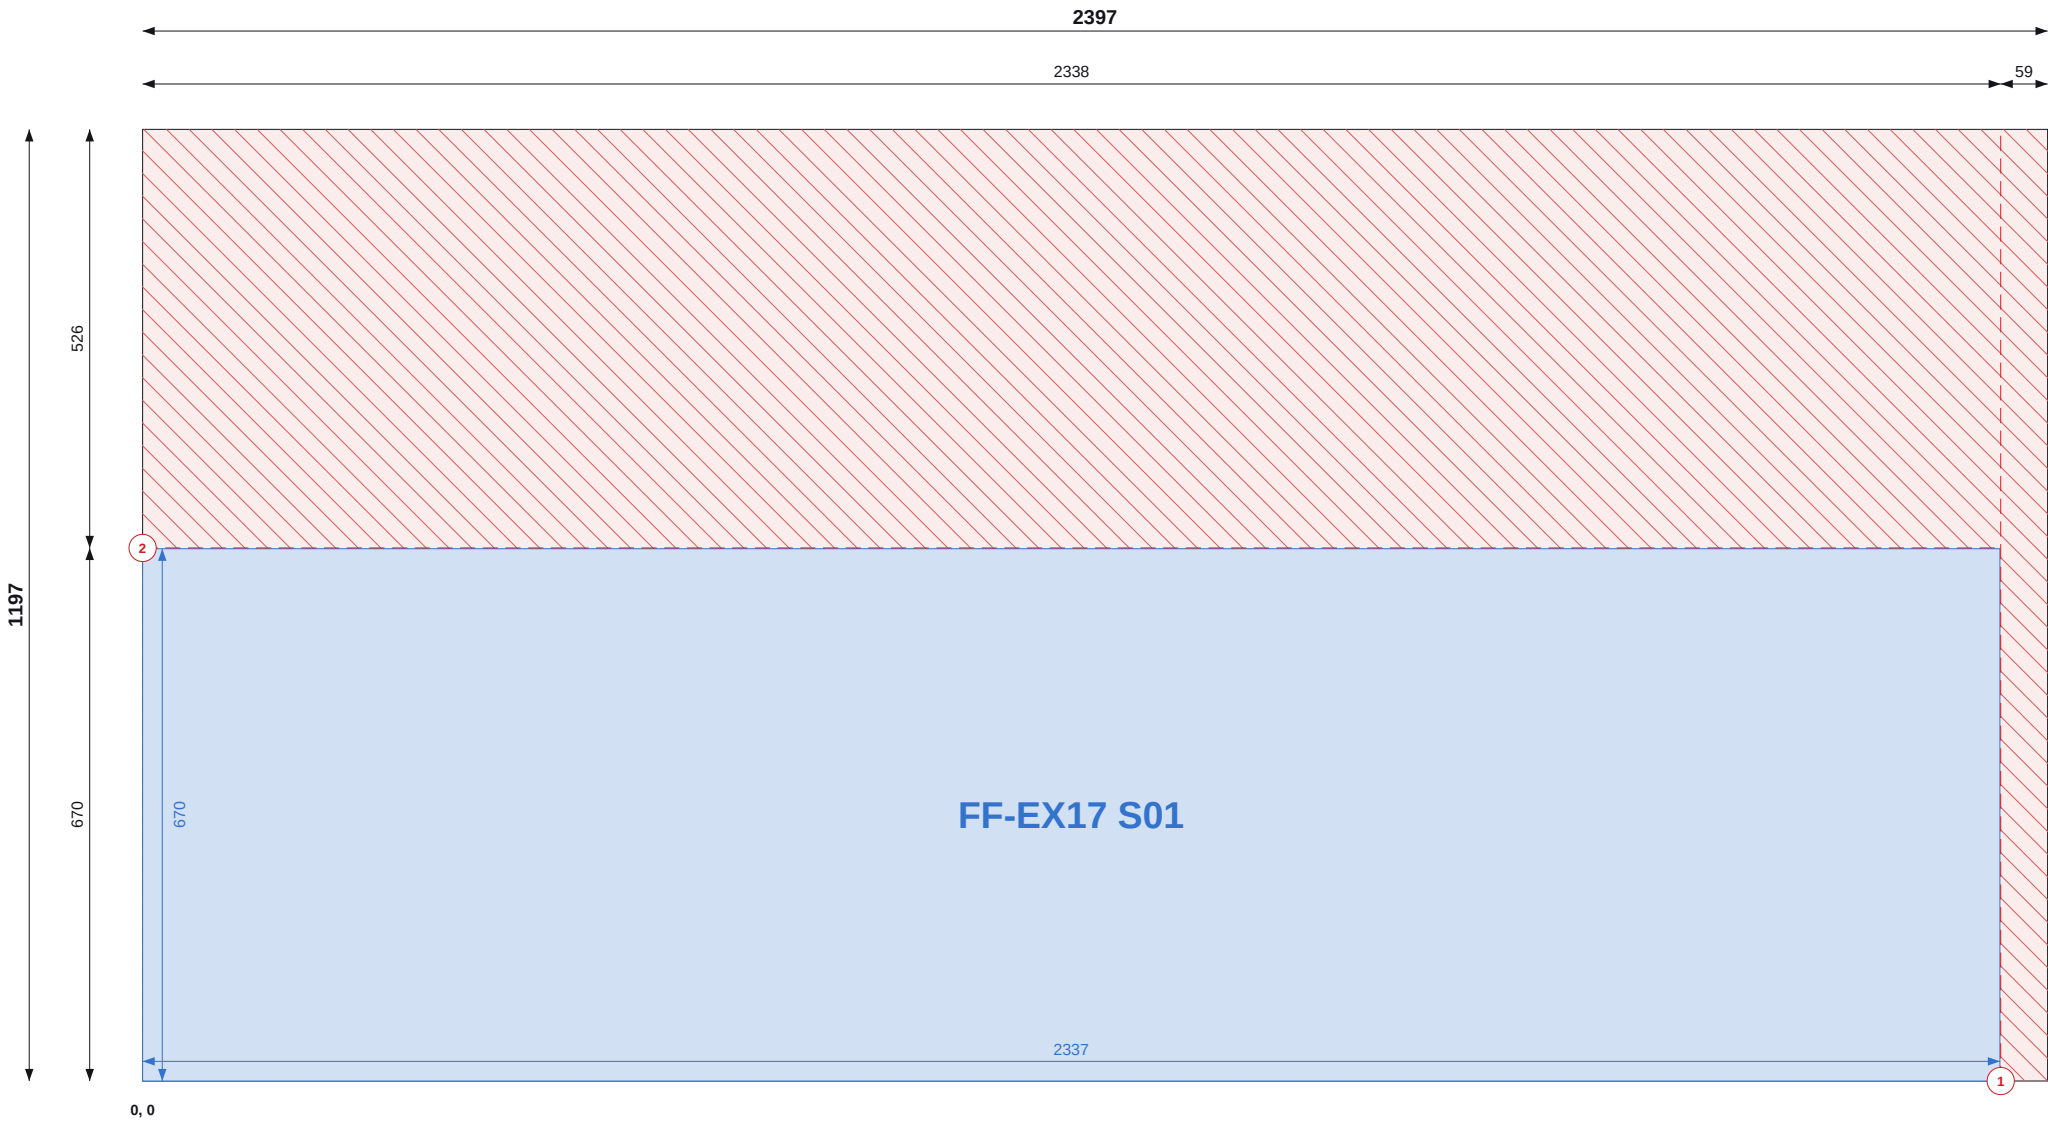

Top / left chains = saw cut positions (to cut centres). Coloured = part size and position.

SHEET 29 OF 34

THIS SHEET

Item	Value
Parts	1
Used / waste	54.5% / 1.30 m2
Reusable offcuts	1
Saw cuts / shared	2 / 0

PIECES (POSITION = BOTTOM-LEFT CORNER)

Label	Size	X, Y
FF-EX17 S01	670 x 2337	0, 0

NOTES

- Cut from OSB/3 9mm 1197x2397, 2mm saw kerf. Viewed on the face; dimensions from the sheet's bottom-left corner (0,0). Red numbered lines = saw cuts in order, each edge to edge.
- Coloured dimensions belong to the part of that colour: its width and height, and its position from the sheet edges. Raked parts: corner coordinates at each corner.
- Red hatch = waste. Labels = panel + piece mark on the manufacture drawing.

REVISIONS

REV	DATE	DESCRIPTION
C01	13.09.26	Construction issue



TLS TIMBER FRAME

Design & Manufacture

Scan: 3D model + drawings



CLIENT	PROJECT
MP Adams	MP Adams Plot 3, Eckington


DRAWING TITLE
OSB CUTTING - FIRST FLOOR - SHEET 29 OF 34

OSB/3 9mm 1197x2397 | First Floor

SCALE	SIZE	DATE	DRAWN
NTS	A3	13.09.26	TS

STATUS	DRAWING No.	REV
CONSTRUCTION	P3-CP-OSB-02 / 29	C01

Do not scale. All dimensions in mm. Check all dimensions on site.

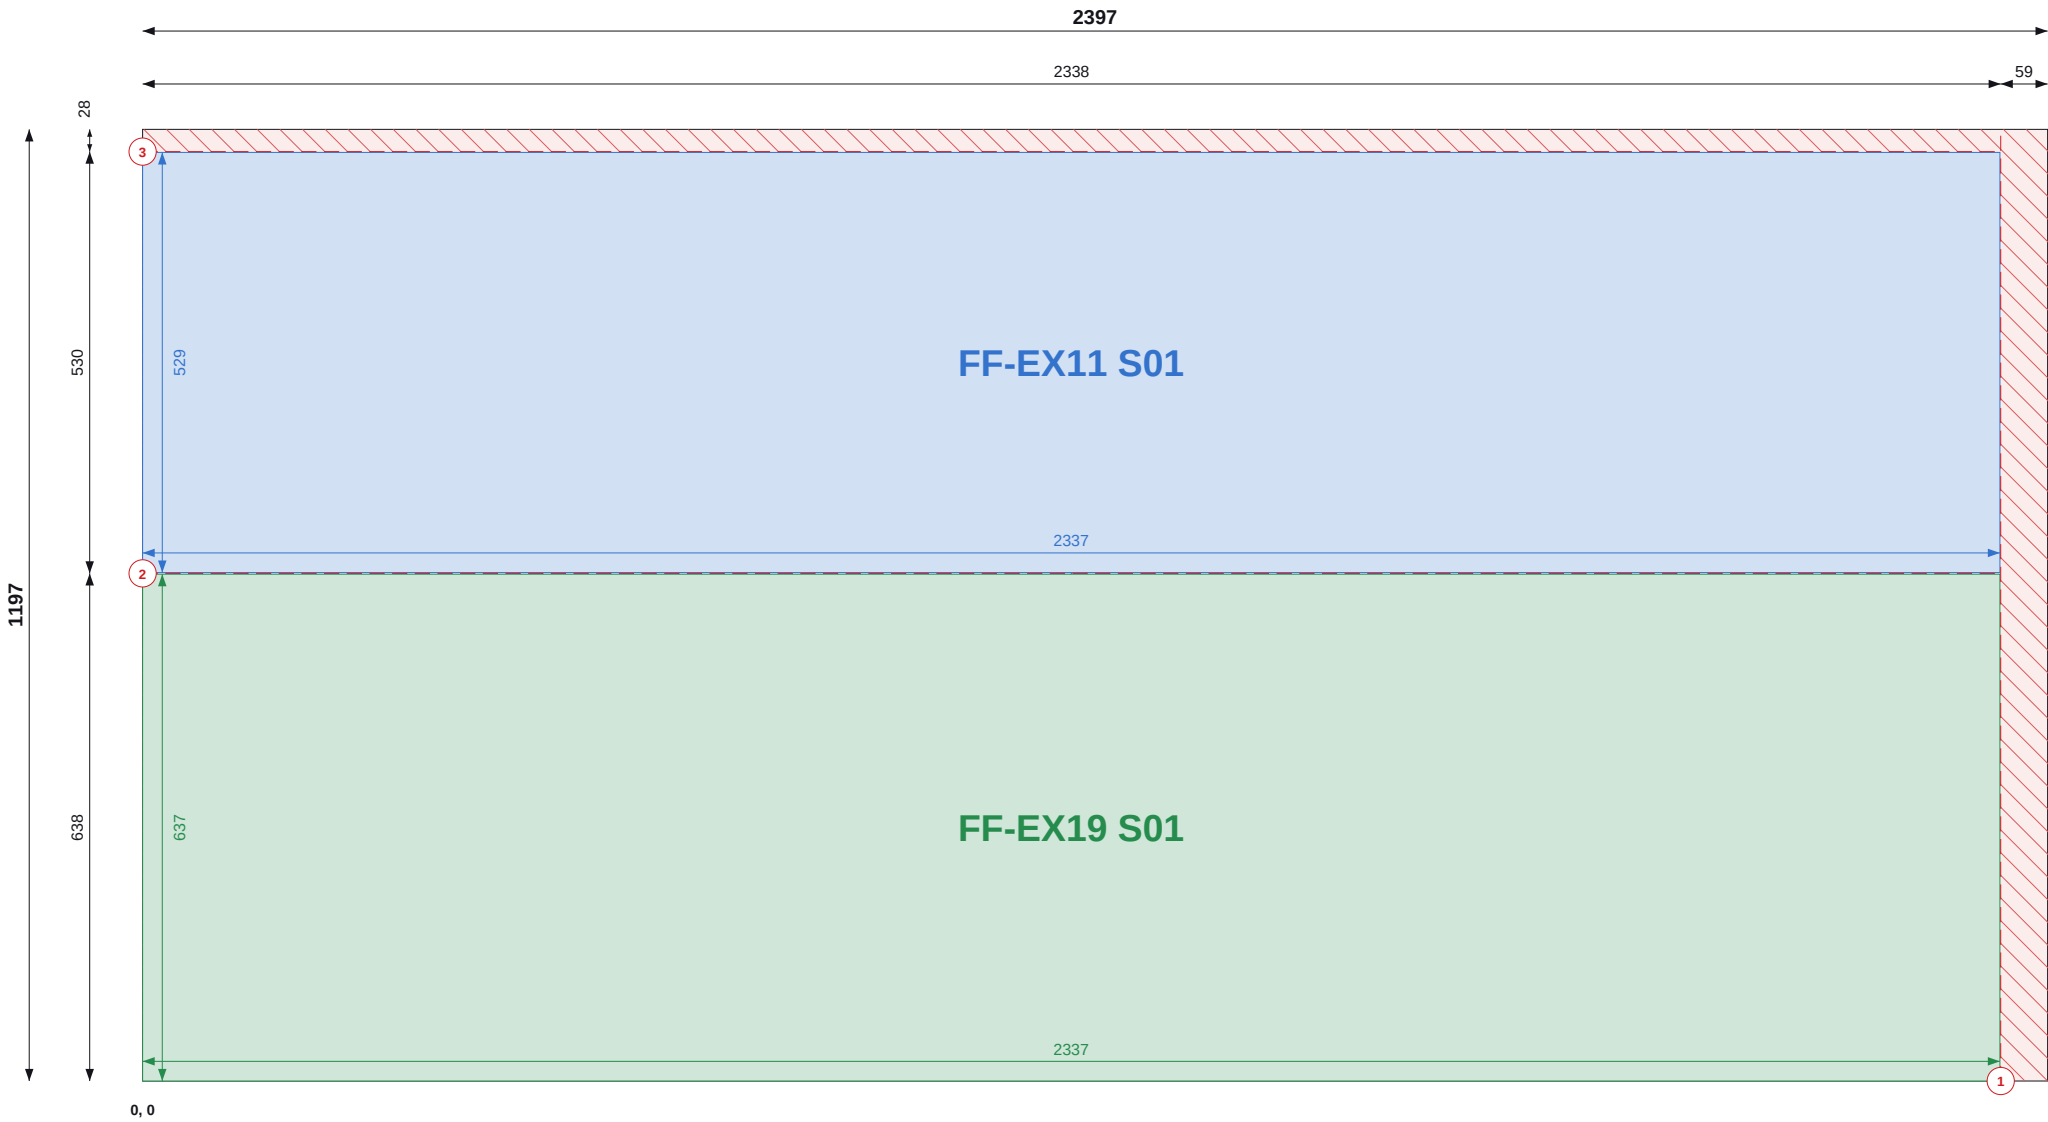

Top / left chains = saw cut positions (to cut centres). Coloured = part size and position.

SHEET 30 OF 34

THIS SHEET

Item	Value
Parts	2
Used / waste	95.0% / 0.14 m2
Reusable offcuts	0
Saw cuts / shared	3 / 1

PIECES (POSITION = BOTTOM-LEFT CORNER)

Label	Size	X, Y
FF-EX11 S01	529 x 2337	0, 639
FF-EX19 S01	637 x 2337	0, 0

NOTES

- Cut from OSB/3 9mm 1197x2397, 2mm saw kerf. Viewed on the face; dimensions from the sheet's bottom-left corner (0,0). Red numbered lines = saw cuts in order, each edge to edge.
- Coloured dimensions belong to the part of that colour: its width and height, and its position from the sheet edges. Raked parts: corner coordinates at each corner.
- Red hatch = waste. Labels = panel + piece mark on the manufacture drawing.

REVISIONS

REV	DATE	DESCRIPTION
C01	13.09.26	Construction issue



TLS TIMBER FRAME

Design & Manufacture

Scan: 3D model + drawings



CLIENT MP Adams	PROJECT MP Adams Plot 3, Eckington
--------------------	---------------------------------------


DRAWING TITLE OSB CUTTING - FIRST FLOOR - SHEET 30 OF 34
--

OSB/3 9mm 1197x2397 | First Floor

SCALE NTS	SIZE A3	DATE 13.09.26	DRAWN TS
--------------	------------	------------------	-------------

STATUS CONSTRUCTION	DRAWING No. P3-CP-OSB-02 / 30	REV C01
-------------------------------	---	-------------------

Do not scale. All dimensions in mm. Check all dimensions on site.

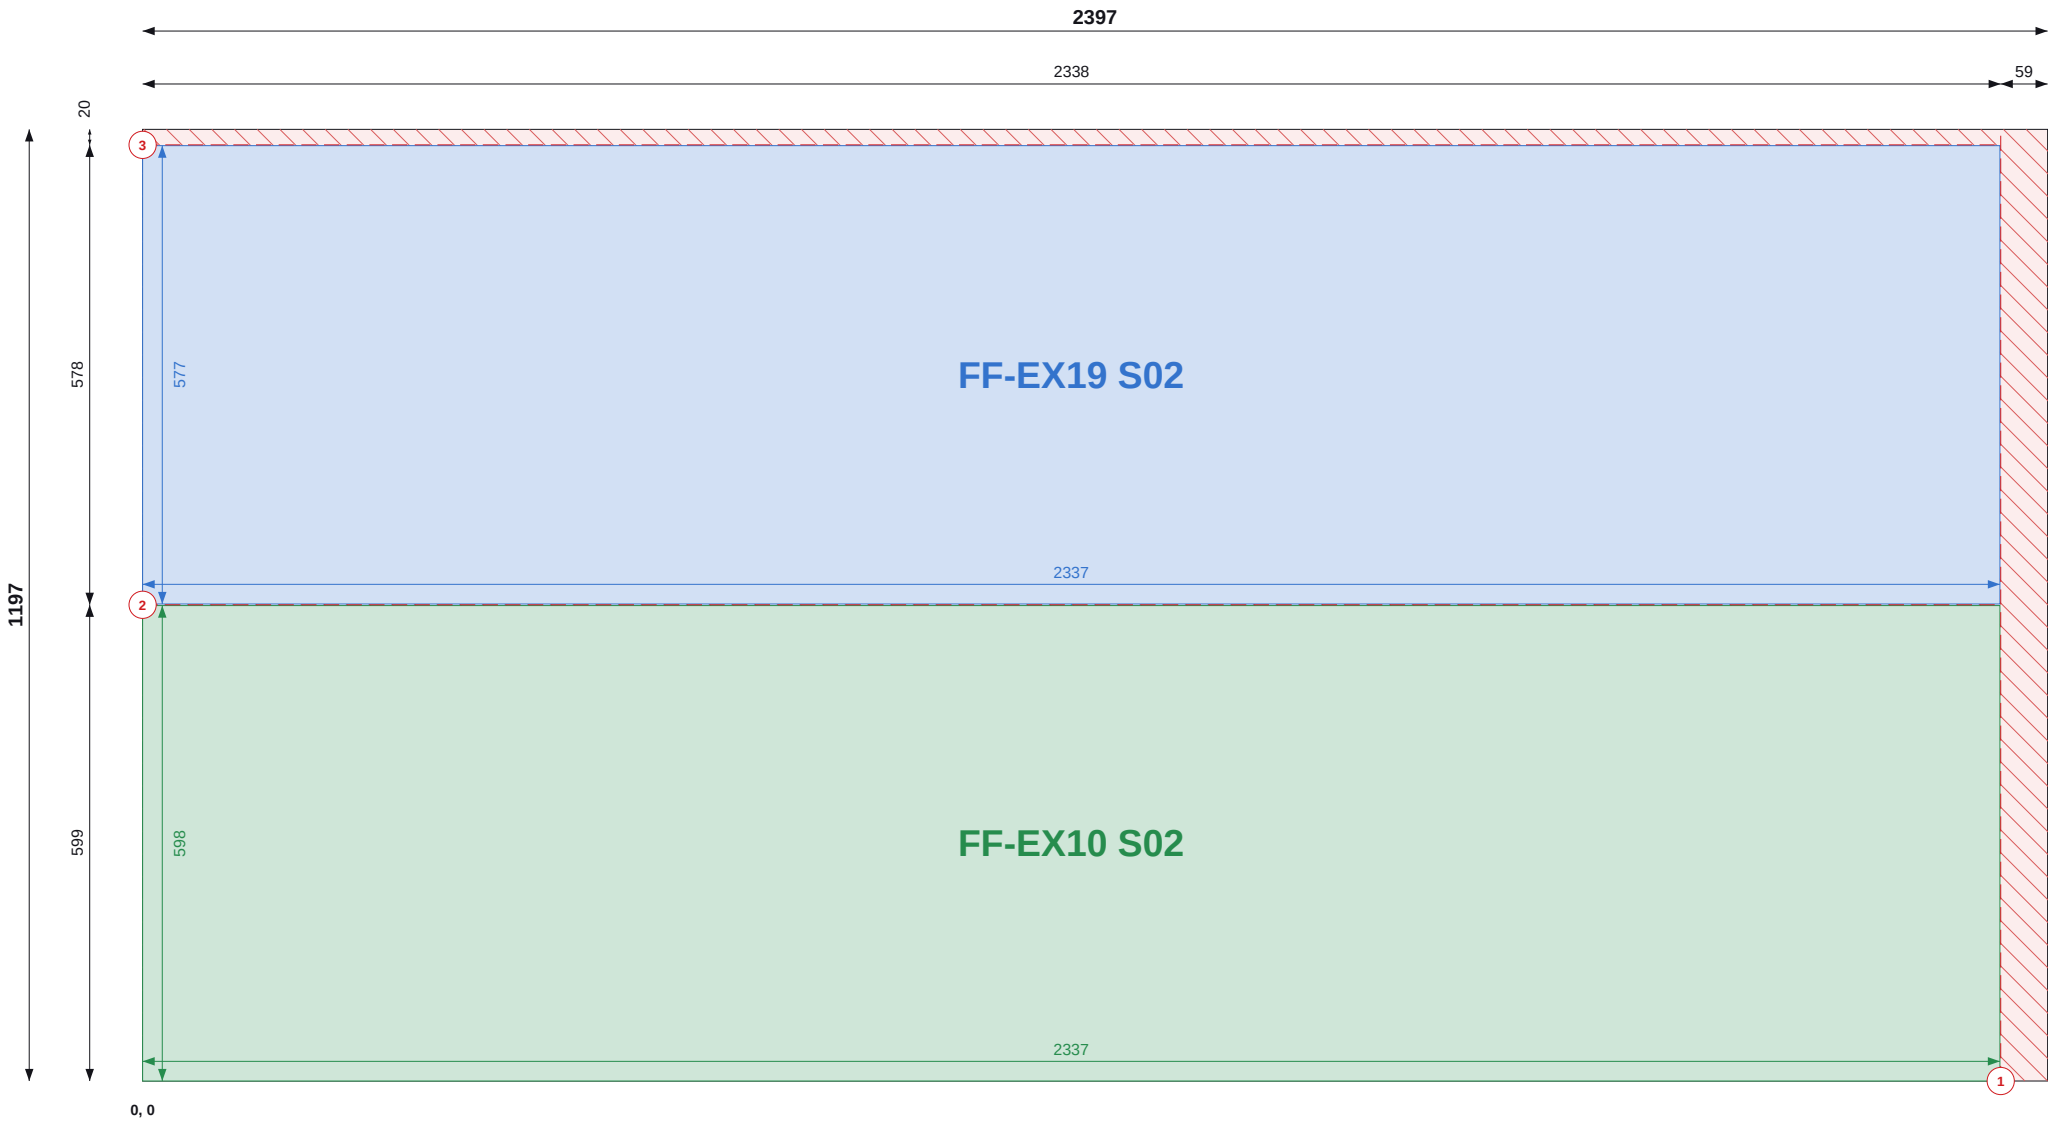

Top / left chains = saw cut positions (to cut centres). Coloured = part size and position.

SHEET 31 OF 34

THIS SHEET

Item	Value
Parts	2
Used / waste	95.7% / 0.12 m2
Reusable offcuts	0
Saw cuts / shared	3 / 1

PIECES (POSITION = BOTTOM-LEFT CORNER)

Label	Size	X, Y
FF-EX19 S02	577 x 2337	0, 600
FF-EX10 S02	598 x 2337	0, 0

NOTES

- Cut from OSB/3 9mm 1197x2397, 2mm saw kerf. Viewed on the face; dimensions from the sheet's bottom-left corner (0,0). Red numbered lines = saw cuts in order, each edge to edge.
- Coloured dimensions belong to the part of that colour: its width and height, and its position from the sheet edges. Raked parts: corner coordinates at each corner.
- Red hatch = waste. Labels = panel + piece mark on the manufacture drawing.

REVISIONS

REV	DATE	DESCRIPTION
C01	13.09.26	Construction issue



TLS TIMBER FRAME

Design & Manufacture

Scan: 3D model + drawings



CLIENT MP Adams	PROJECT MP Adams Plot 3, Eckington
--------------------	---------------------------------------


DRAWING TITLE OSB CUTTING - FIRST FLOOR - SHEET 31 OF 34
--

OSB/3 9mm 1197x2397 | First Floor

SCALE NTS	SIZE A3	DATE 13.09.26	DRAWN TS
--------------	------------	------------------	-------------

STATUS CONSTRUCTION	DRAWING No. P3-CP-OSB-02 / 31	REV C01
-------------------------------	---	-------------------

Do not scale. All dimensions in mm. Check all dimensions on site.

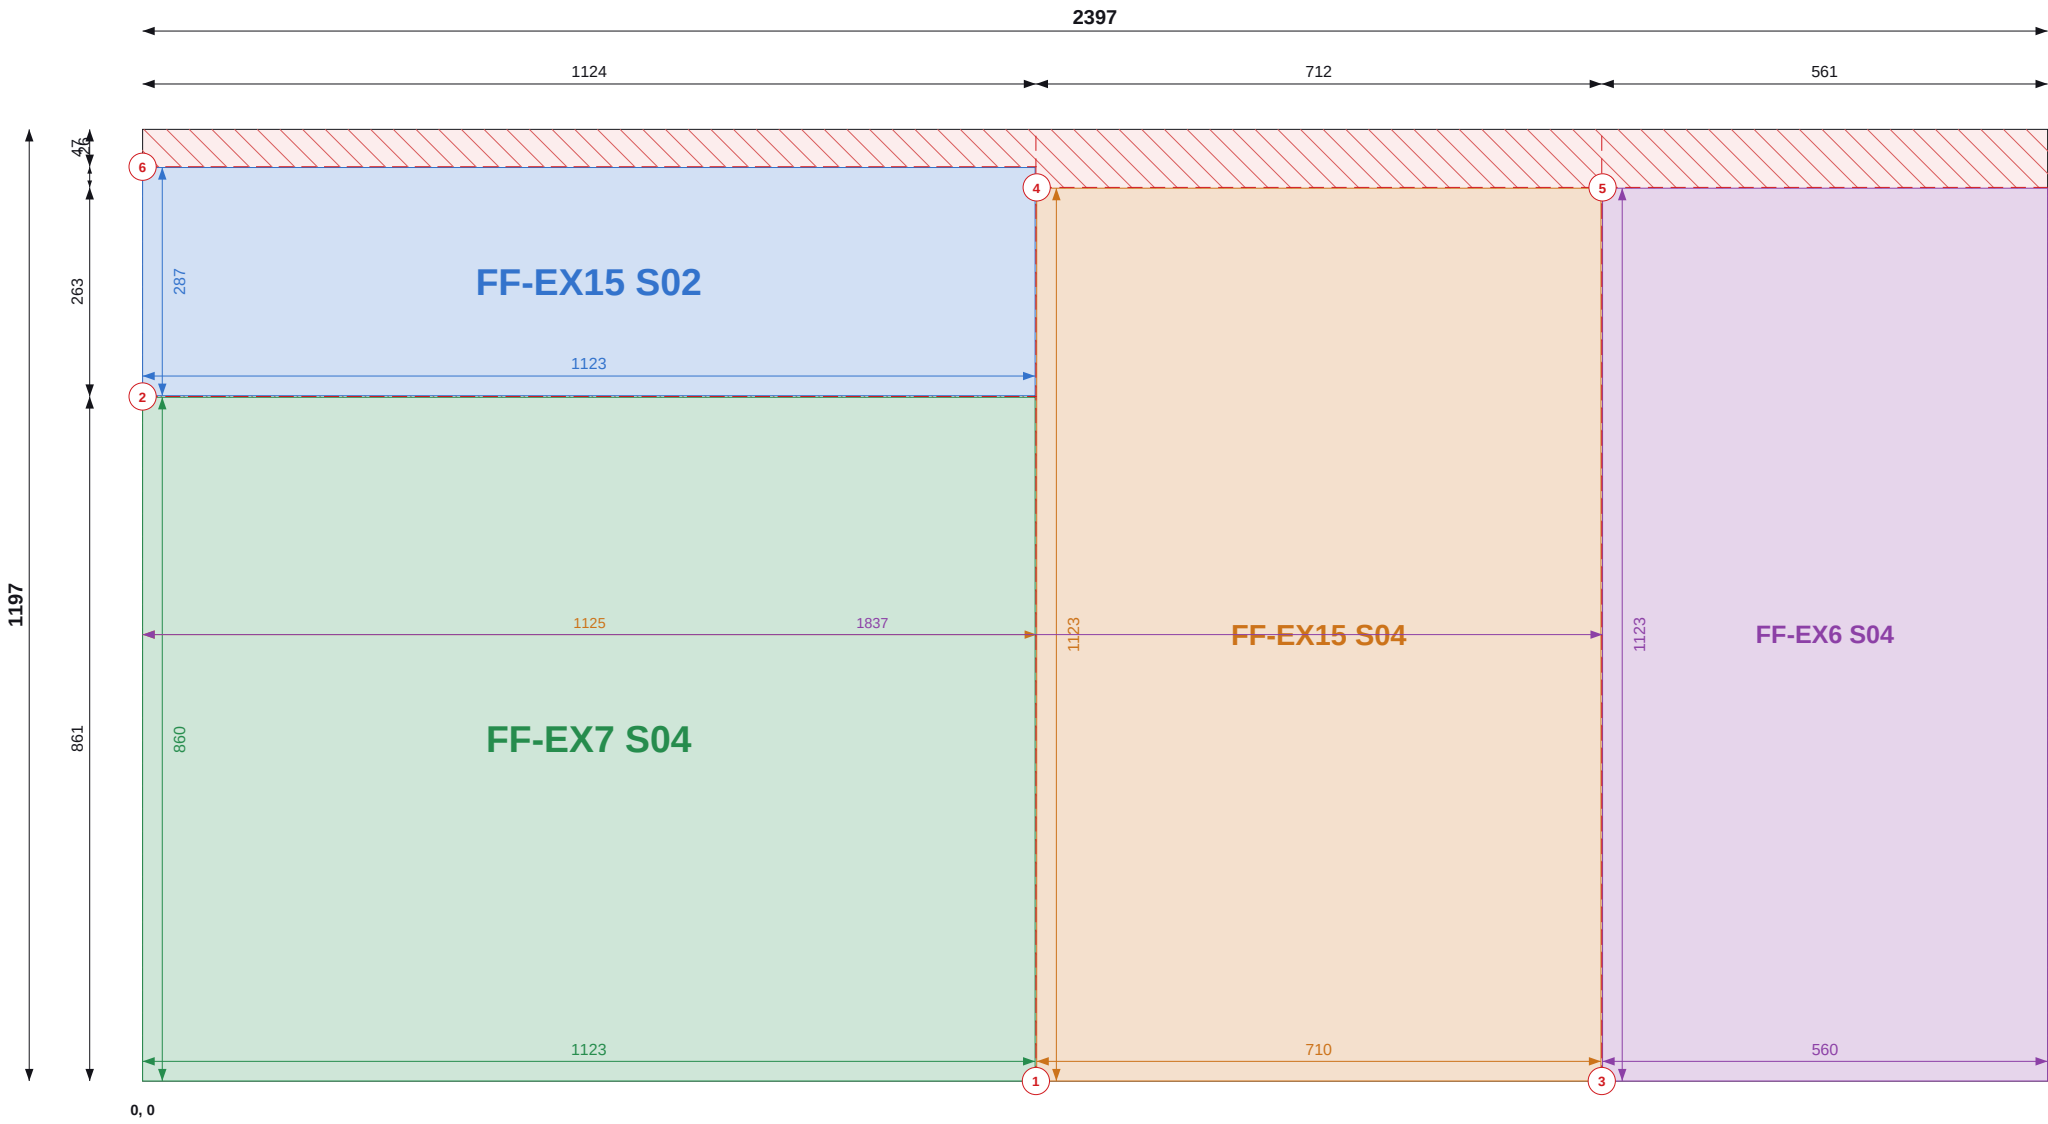

SHEET 32 OF 34

THIS SHEET

Item	Value
Parts	4
Used / waste	94.6% / 0.15 m2
Reusable offcuts	0
Saw cuts / shared	6 / 3

PIECES (POSITION = BOTTOM-LEFT CORNER)

Label	Size	X, Y
FF-EX15 S02	1123 x 287	0, 862
FF-EX7 S04	1123 x 860	0, 0
FF-EX15 S04	1123 x 710	1125, 0
FF-EX6 S04	1123 x 560	1837, 0

NOTES

- Cut from OSB/3 9mm 1197x2397, 2mm saw kerf. Viewed on the face; dimensions from the sheet's bottom-left corner (0,0). Red numbered lines = saw cuts in order, each edge to edge.
- Coloured dimensions belong to the part of that colour: its width and height, and its position from the sheet edges. Raked parts: corner coordinates at each corner.
- Red hatch = waste. Labels = panel + piece mark on the manufacture drawing.

REVISIONS

REV	DATE	DESCRIPTION
C01	13.09.26	Construction issue



TLS TIMBER FRAME

Design & Manufacture

Scan: 3D model + drawings



CLIENT MP Adams	PROJECT MP Adams Plot 3, Eckington
--------------------	---------------------------------------


DRAWING TITLE OSB CUTTING - FIRST FLOOR - SHEET 32 OF 34
--

OSB/3 9mm 1197x2397 | First Floor

SCALE NTS	SIZE A3	DATE 13.09.26	DRAWN TS
--------------	------------	------------------	-------------

STATUS CONSTRUCTION	DRAWING No. P3-CP-OSB-02 / 32	REV C01
-------------------------------	---	-------------------

Do not scale. All dimensions in mm. Check all dimensions on site.

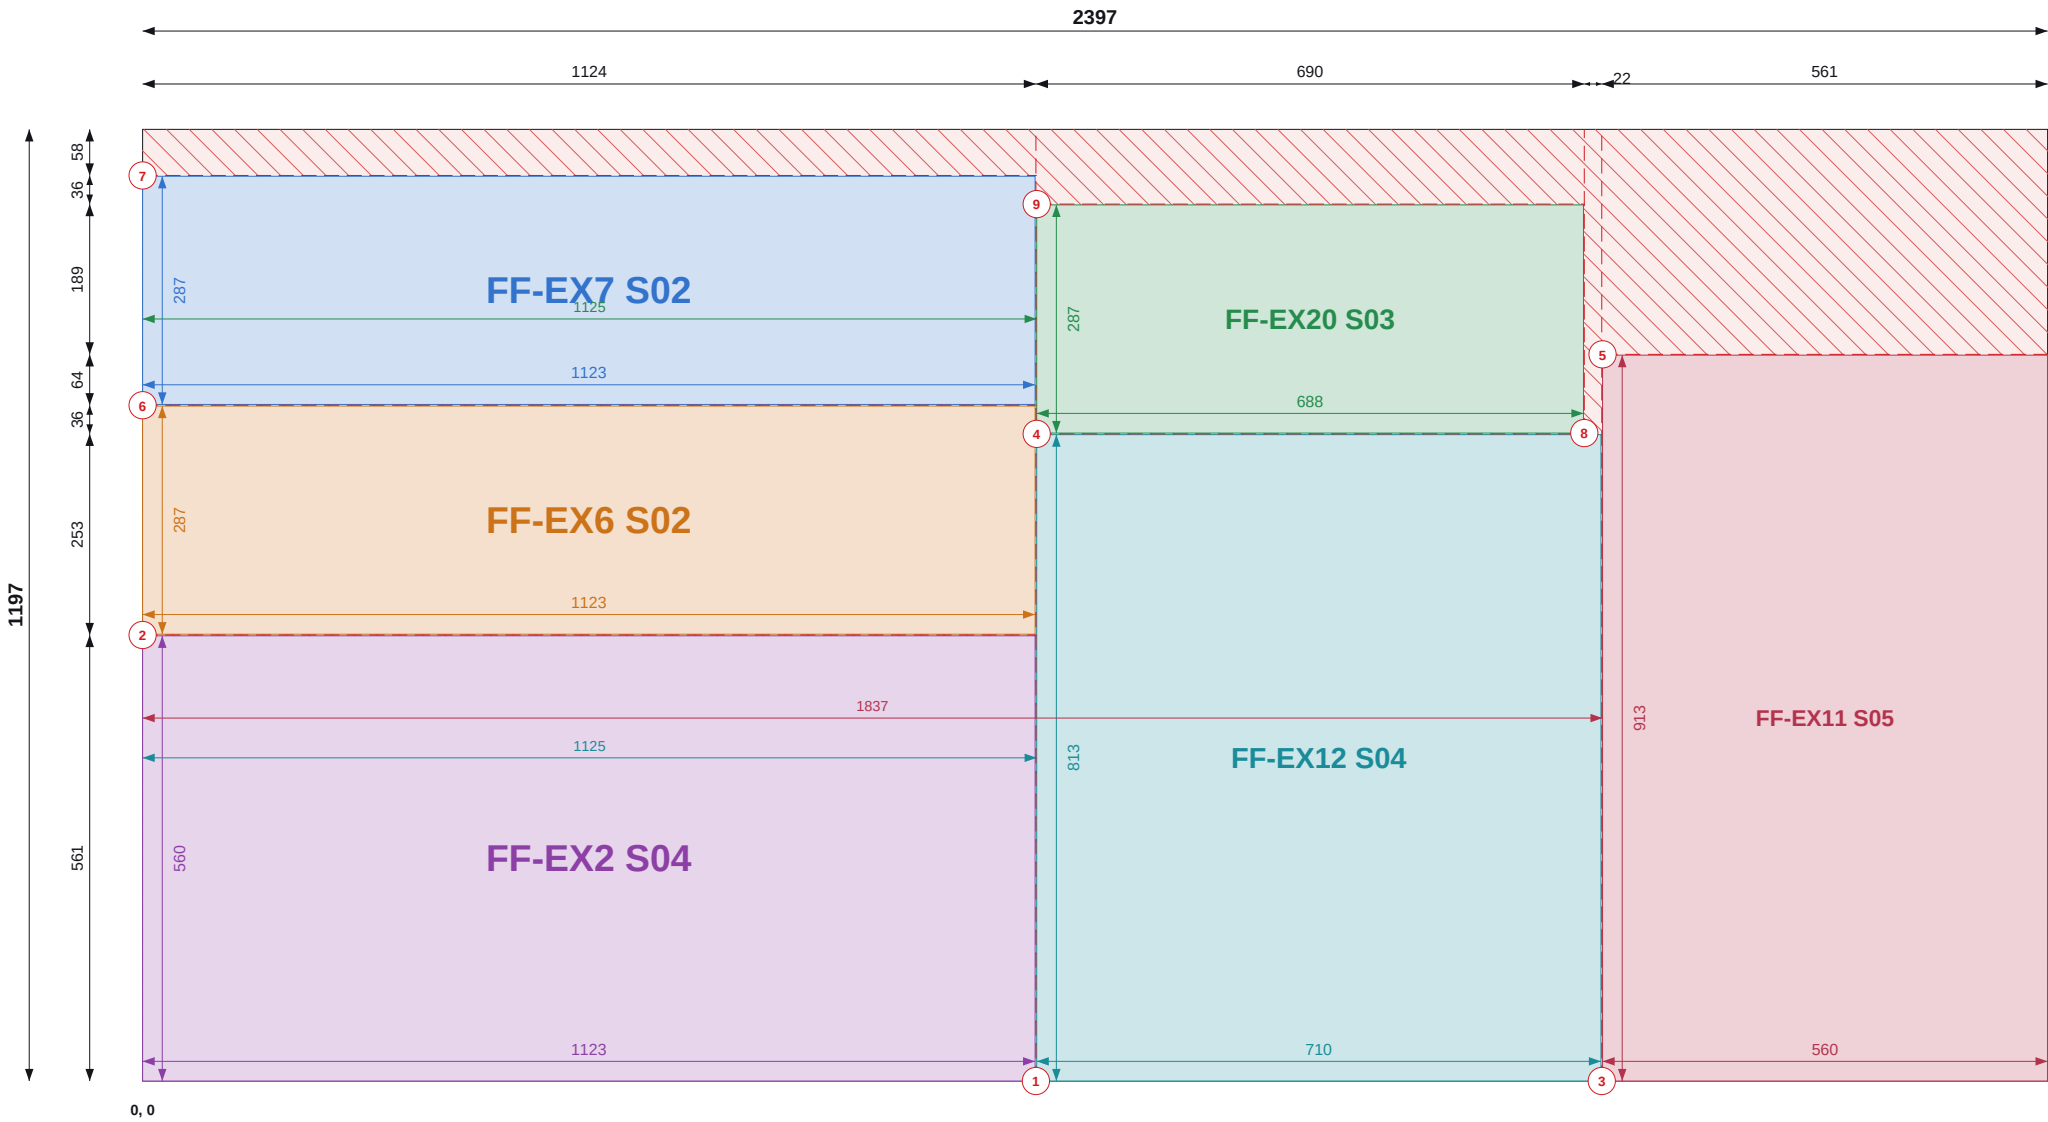

Top / left chains = saw cut positions (to cut centres). Coloured = part size and position.

SHEET 33 OF 34

THIS SHEET

Item	Value
Parts	6
Used / waste	89.2% / 0.31 m2
Reusable offcuts	0
Saw cuts / shared	9 / 5

PIECES (POSITION = BOTTOM-LEFT CORNER)

Label	Size	X, Y
FF-EX7 S02	1123 x 287	0, 851
FF-EX20 S03	688 x 287	1125, 815
FF-EX6 S02	1123 x 287	0, 562
FF-EX2 S04	1123 x 560	0, 0
FF-EX12 S04	813 x 710	1125, 0
FF-EX11 S05	913 x 560	1837, 0

NOTES

- Cut from OSB/3 9mm 1197x2397, 2mm saw kerf. Viewed on the face; dimensions from the sheet's bottom-left corner (0,0). Red numbered lines = saw cuts in order, each edge to edge.
- Coloured dimensions belong to the part of that colour: its width and height, and its position from the sheet edges. Raked parts: corner coordinates at each corner.
- Red hatch = waste. Labels = panel + piece mark on the manufacture drawing.

REVISIONS

REV	DATE	DESCRIPTION
C01	13.09.26	Construction issue



TLS TIMBER FRAME

Design & Manufacture

Scan: 3D model + drawings



CLIENT MP Adams	PROJECT MP Adams Plot 3, Eckington
--------------------	---------------------------------------


DRAWING TITLE OSB CUTTING - FIRST FLOOR - SHEET 33 OF 34
--

OSB/3 9mm 1197x2397 | First Floor

SCALE NTS	SIZE A3	DATE 13.09.26	DRAWN TS
--------------	------------	------------------	-------------

STATUS CONSTRUCTION	DRAWING No. P3-CP-OSB-02 / 33	REV C01
-------------------------------	---	-------------------

Do not scale. All dimensions in mm. Check all dimensions on site.

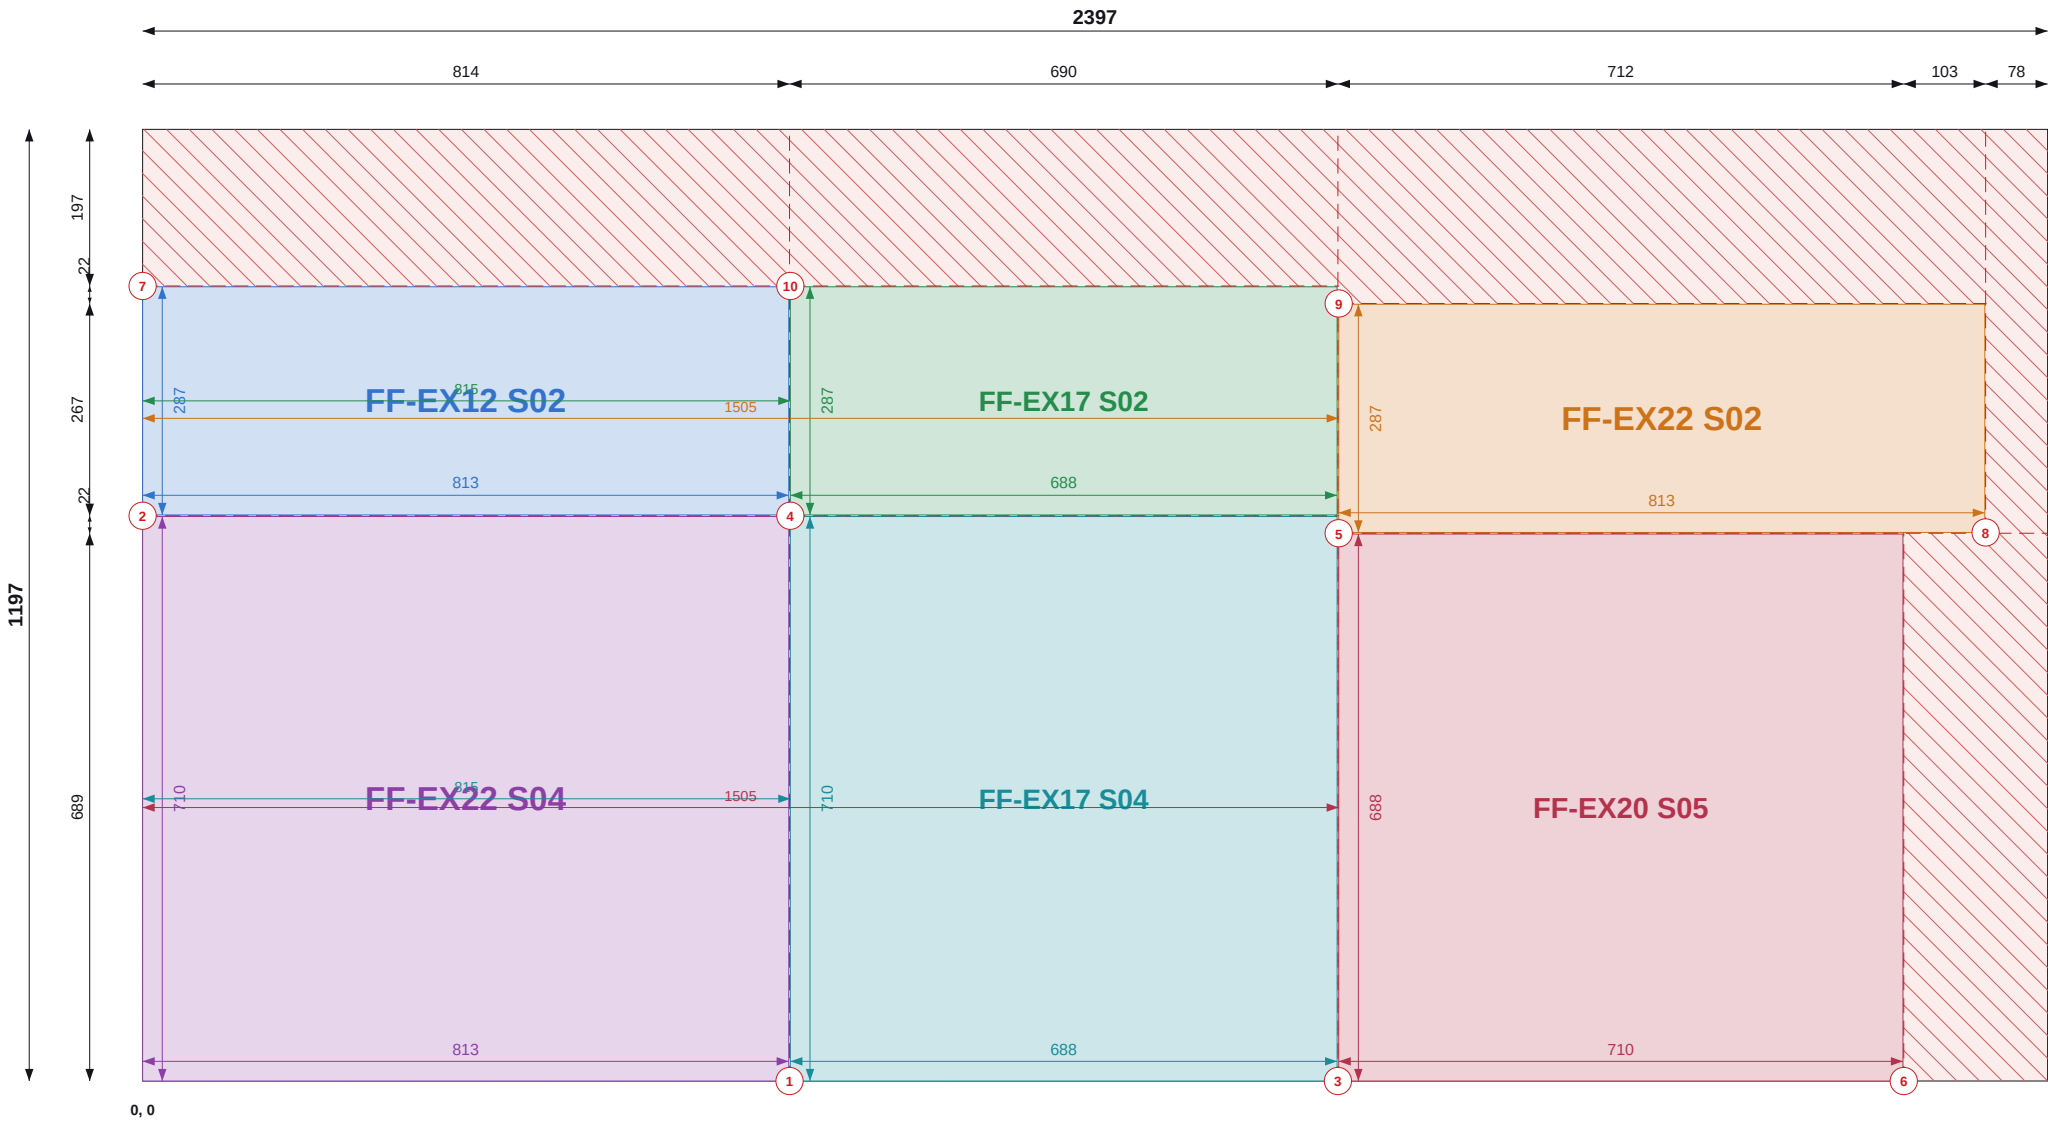

Top / left chains = saw cut positions (to cut centres). Coloured = part size and position.

SHEET 34 OF 34

THIS SHEET

Item	Value
Parts	6
Used / waste	77.3% / 0.65 m2
Reusable offcuts	0
Saw cuts / shared	10 / 5

PIECES (POSITION = BOTTOM-LEFT CORNER)

Label	Size	X, Y
FF-EX12 S02	813 x 287	0, 712
FF-EX17 S02	688 x 287	815, 712
FF-EX22 S02	813 x 287	1505, 690
FF-EX22 S04	813 x 710	0, 0
FF-EX17 S04	688 x 710	815, 0
FF-EX20 S05	688 x 710	1505, 0

NOTES

- Cut from OSB/3 9mm 1197x2397, 2mm saw kerf. Viewed on the face; dimensions from the sheet's bottom-left corner (0,0). Red numbered lines = saw cuts in order, each edge to edge.
- Coloured dimensions belong to the part of that colour: its width and height, and its position from the sheet edges. Raked parts: corner coordinates at each corner.
- Red hatch = waste. Labels = panel + piece mark on the manufacture drawing.

REVISIONS

REV	DATE	DESCRIPTION
C01	13.09.26	Construction issue



TLS TIMBER FRAME

Design & Manufacture

Scan: 3D model + drawings



CLIENT MP Adams	PROJECT MP Adams Plot 3, Eckington
--------------------	---------------------------------------


DRAWING TITLE
OSB CUTTING - FIRST FLOOR - SHEET 34 OF 34

OSB/3 9mm 1197x2397 | First Floor

SCALE NTS	SIZE A3	DATE 13.09.26	DRAWN TS
--------------	------------	------------------	-------------

STATUS CONSTRUCTION	DRAWING No. P3-CP-OSB-02 / 34	REV C01
-------------------------------	---	-------------------

Do not scale. All dimensions in mm. Check all dimensions on site.

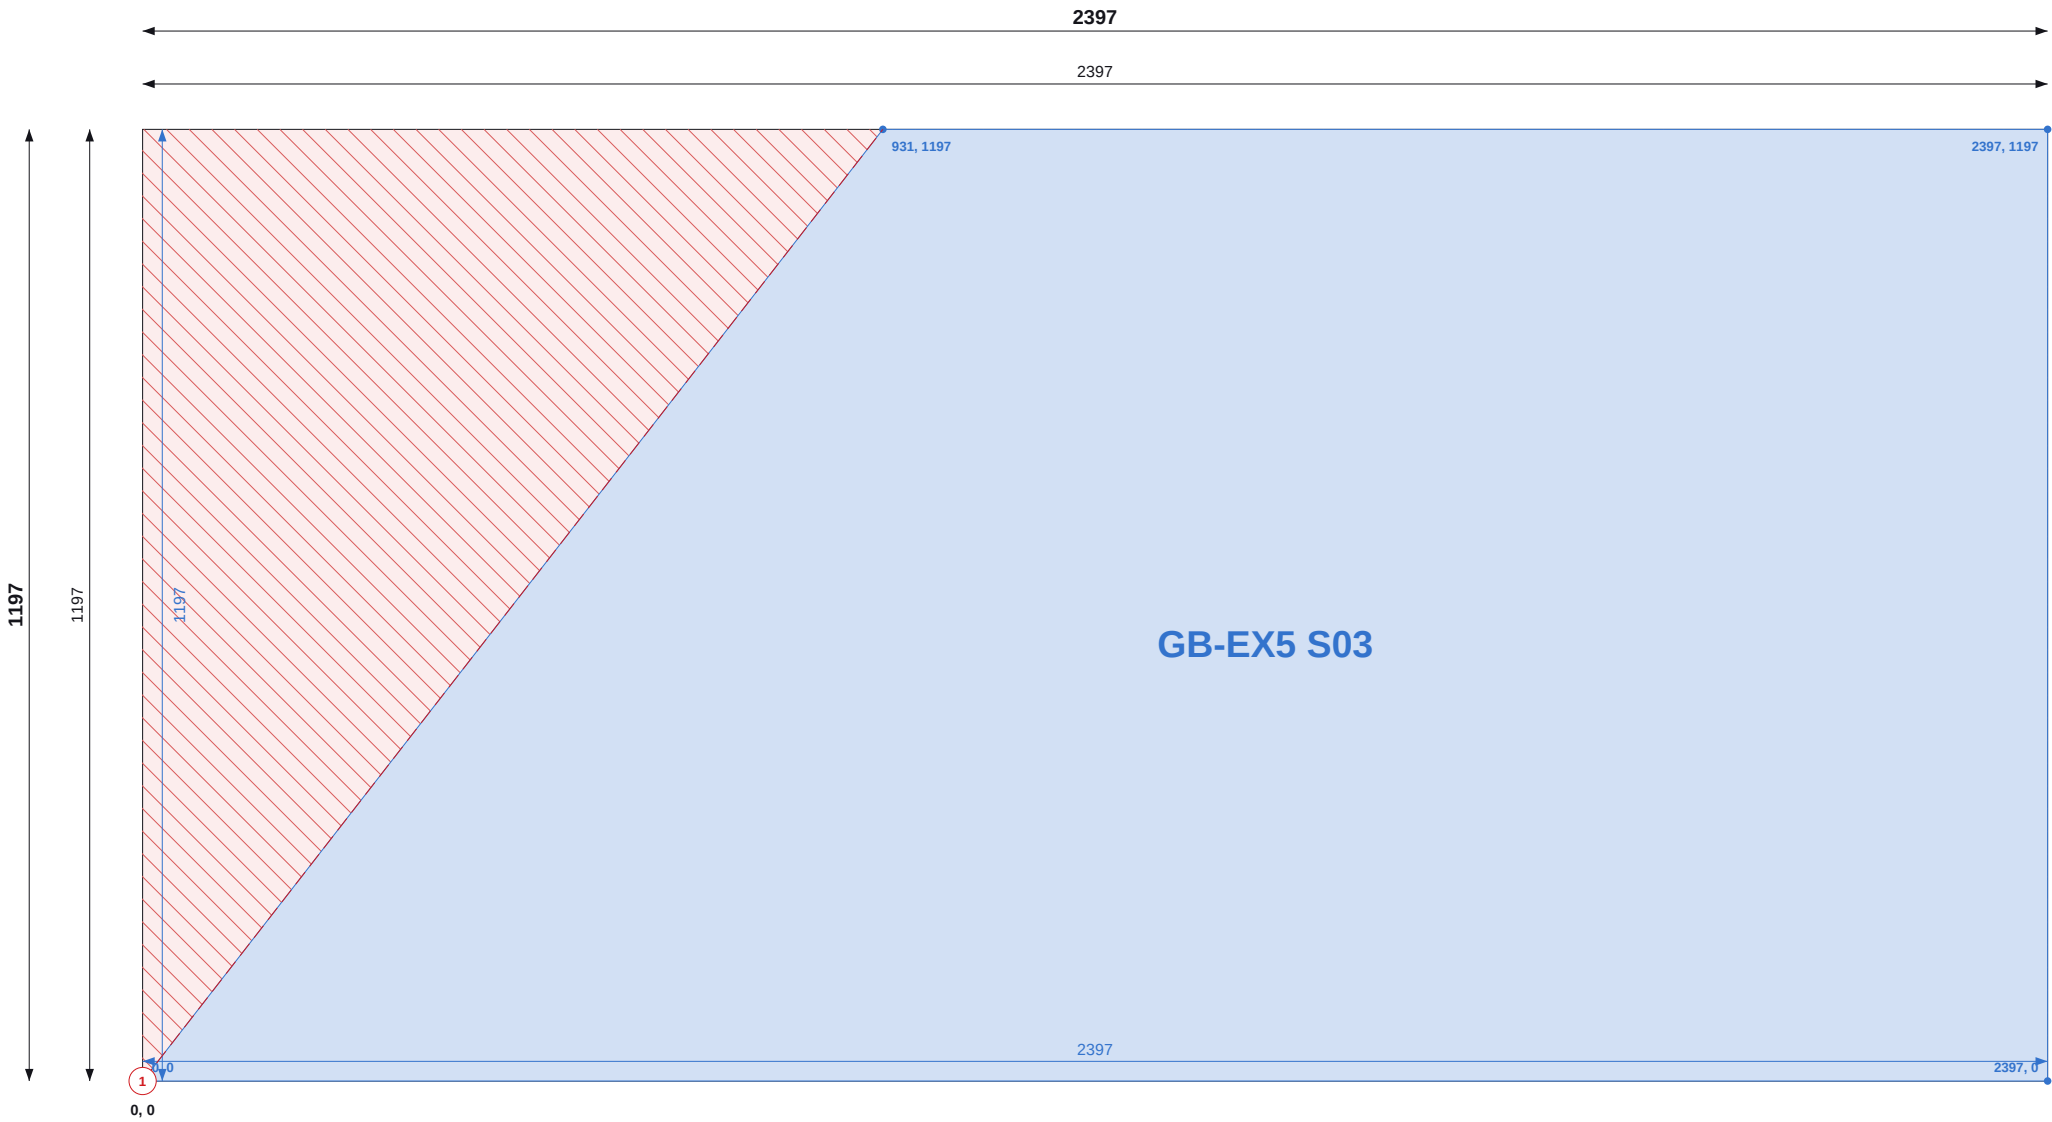

Top / left chains = saw cut positions (to cut centres). Coloured = part size and position.

SHEET 2 OF 14

THIS SHEET

Item	Value
Parts	1
Used / waste	80.6% / 0.56 m2
Reusable offcuts	0
Saw cuts / shared	1 / 1

PIECES (POSITION = BOTTOM-LEFT CORNER)

Label	Size	X, Y
GB-EX5 S03	1197 x 2397 rake to 1466	0, 0

NOTES

- Cut from OSB/3 9mm 1197x2397, 2mm saw kerf. Viewed on the face; dimensions from the sheet's bottom-left corner (0,0). Red numbered lines = saw cuts in order, each edge to edge.
- Coloured dimensions belong to the part of that colour: its width and height, and its position from the sheet edges. Raked parts: corner coordinates at each corner.
- Red hatch = waste. Labels = panel + piece mark on the manufacture drawing.

REVISIONS

REV	DATE	DESCRIPTION
C01	13.09.26	Construction issue



TLS TIMBER FRAME

Design & Manufacture

Scan: 3D model + drawings



CLIENT MP Adams	PROJECT MP Adams Plot 3, Eckington
--------------------	---------------------------------------

DRAWING TITLE OSB CUTTING - GABLES - SHEET 2 OF 14
--


OSB/3 9mm 1197x2397 | Gables

SCALE NTS	SIZE A3	DATE 13.09.26	DRAWN TS
--------------	------------	------------------	-------------

STATUS CONSTRUCTION	DRAWING No. P3-CP-OSB-03 / 02	REV C01
-------------------------------	---	-------------------

Item	Value
Parts	1
Used / waste	74.2% / 0.74 m2
Reusable offcuts	0
Saw cuts / shared	2 / 1

Label	Size	X, Y
GB-EX9 S03	1197 x 2378 rake to 1182	0, 0

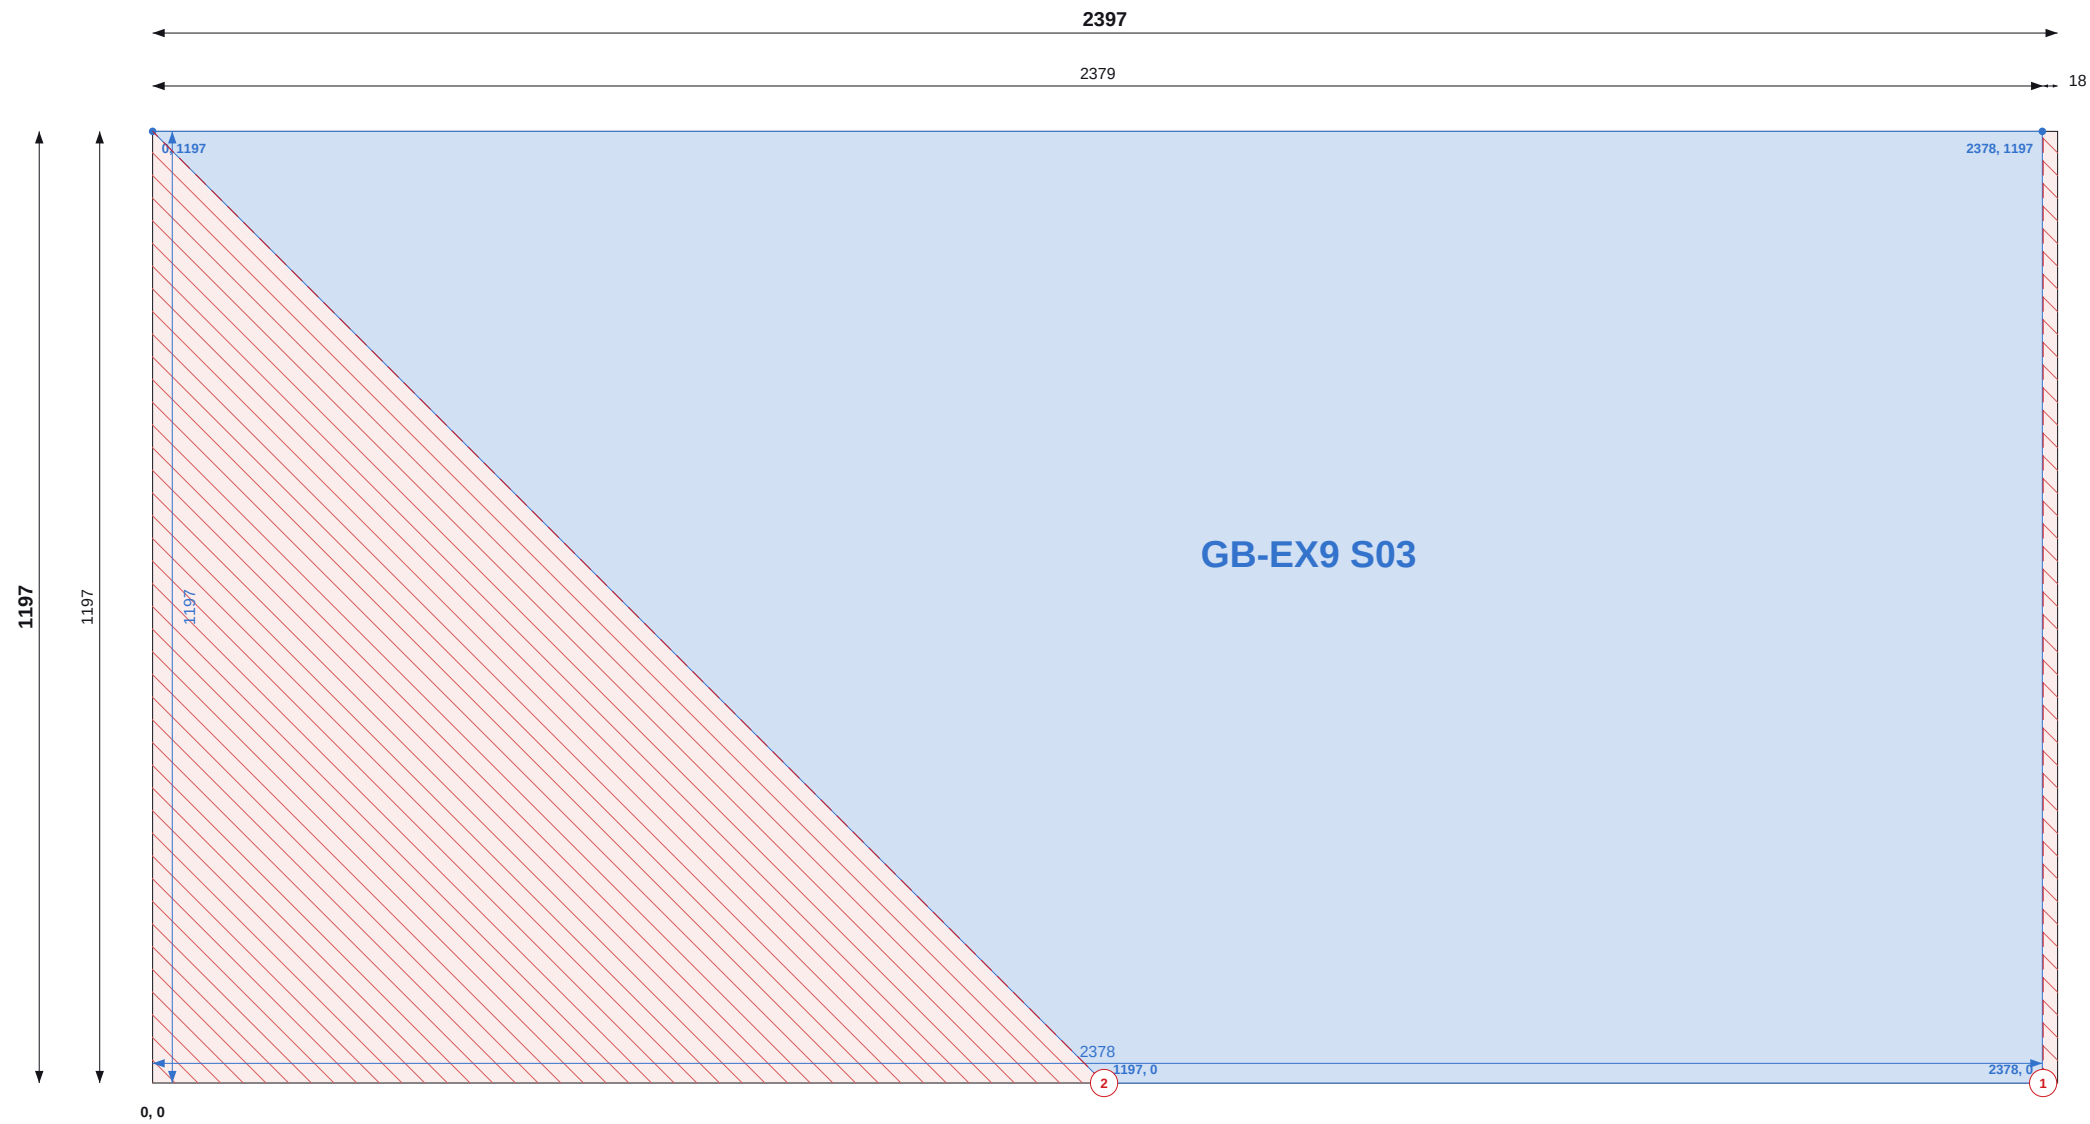

Top / left chains = saw cut positions (to cut centres). Coloured = part size and position.

1. Cut from OSB/3 9mm 1197x2397, 2mm saw kerf. Viewed on the face; dimensions from the sheet's bottom-left corner (0,0). Red numbered lines = saw cuts in order, each edge to edge.
2. Coloured dimensions belong to the part of that colour: its width and height, and its position from the sheet edges. Raked parts: corner coordinates at each corner.
3. Red hatch = waste. Labels = panel + piece mark on the manufacture drawing.

REV	DATE	DESCRIPTION
C01	13.09.26	Construction issue



Design & Manufacture

Scan: 3D model + drawings



CLIENT	PROJECT
MP Adams	MP Adams Plot 3, Eckington

DRAWING TITLE


OSB CUTTING - GABLES - SHEET 3 OF 14

OSB/3 9mm 1197x2397 | Gables

SCALE	SIZE	DATE	DRAWN
NTS	A3	13.09.26	TS

STATUS	DRAWING No.	REV
CONSTRUCTION	P3-CP-OSB-03 / 03	C01

Do not scale. All dimensions in mm. Check all dimensions on site.

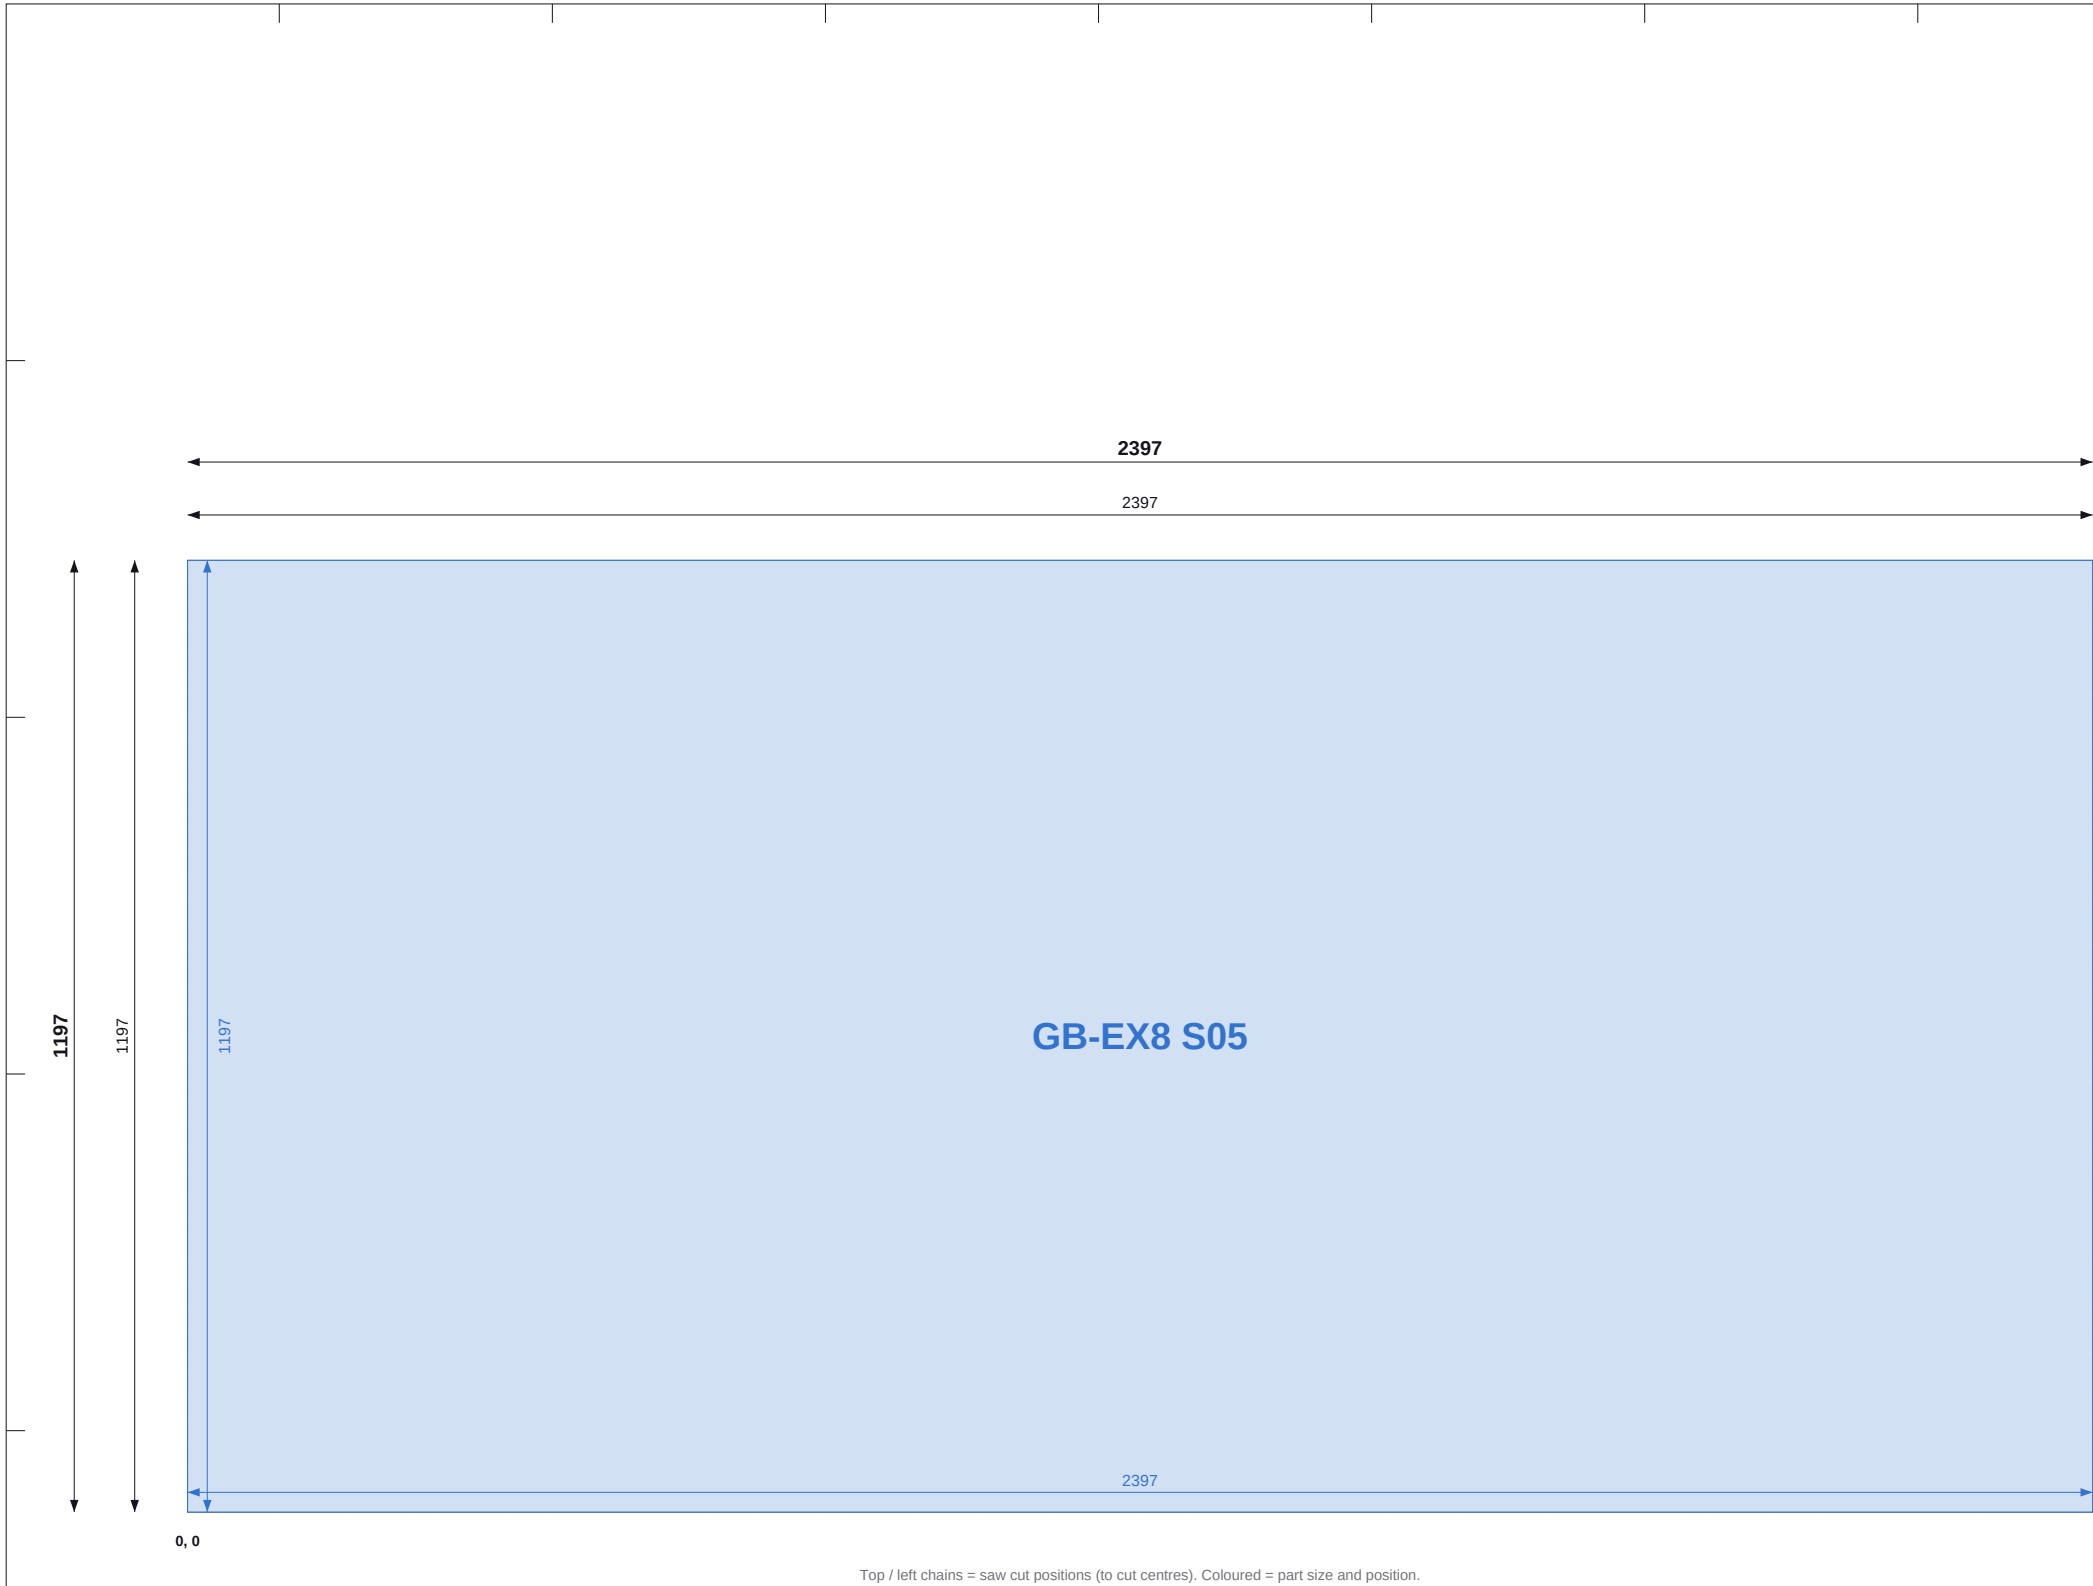

Top / left chains = saw cut positions (to cut centres). Coloured = part size and position.

SHEET 4 OF 14

THIS SHEET

Item	Value
Parts	1
Used / waste	100.0% / 0.00 m2
Reusable offcuts	0
Saw cuts / shared	0 / 0

PIECES (POSITION = BOTTOM-LEFT CORNER)

Label	Size	X, Y
GB-EX8 S05	1197 x 2397	0, 0

NOTES

- Cut from OSB/3 9mm 1197x2397, 2mm saw kerf. Viewed on the face; dimensions from the sheet's bottom-left corner (0,0). Red numbered lines = saw cuts in order, each edge to edge.
- Coloured dimensions belong to the part of that colour: its width and height, and its position from the sheet edges. Raked parts: corner coordinates at each corner.
- Red hatch = waste. Labels = panel + piece mark on the manufacture drawing.

REVISIONS

REV	DATE	DESCRIPTION
C01	13.09.26	Construction issue



TLS TIMBER FRAME

Design & Manufacture

Scan: 3D model + drawings



CLIENT	PROJECT
MP Adams	MP Adams Plot 3, Eckington

DRAWING TITLE
OSB CUTTING - GABLES - SHEET 4 OF 14

OSB/3 9mm 1197x2397 | Gables

SCALE	SIZE	DATE	DRAWN
NTS	A3	13.09.26	TS

STATUS	DRAWING No.	REV
CONSTRUCTION	P3-CP-OSB-03 / 04	C01

Item	Value
Parts	2
Used / waste	97.5% / 0.07 m2
Reusable offcuts	0
Saw cuts / shared	2 / 1

Label	Size	X, Y
GB-EX1 S03	1197 x 2380 rake to 1185	0, 0
GB-EX1 S04	922 x 1180 rake to 260	12, 0

1. Cut from OSB/3 9mm 1197x2397, 2mm saw kerf. Viewed on the face; dimensions from the sheet's bottom-left corner (0,0). Red numbered lines = saw cuts in order, each edge to edge.
2. Coloured dimensions belong to the part of that colour: its width and height, and its position from the sheet edges. Raked parts: corner coordinates at each corner.
3. Red hatch = waste. Labels = panel + piece mark on the manufacture drawing.

REV	DATE	DESCRIPTION
C01	13.09.26	Construction issue



Design & Manufacture

Scan: 3D model + drawings



CLIENT

MP Adams

PROJECT

MP Adams Plot 3, Eckington

DRAWING TITLE

OSB CUTTING - GABLES - SHEET 5 OF 14


OSB/3 9mm 1197x2397 | Gables

SCALE	SIZE	DATE	DRAWN
NTS	A3	13.09.26	TS

STATUS	DRAWING No.	REV
CONSTRUCTION	P3-CP-OSB-03 / 05	C01

Do not scale. All dimensions in mm. Check all dimensions on site.

Do not scale. All dimensions in mm. Check all dimensions on site.

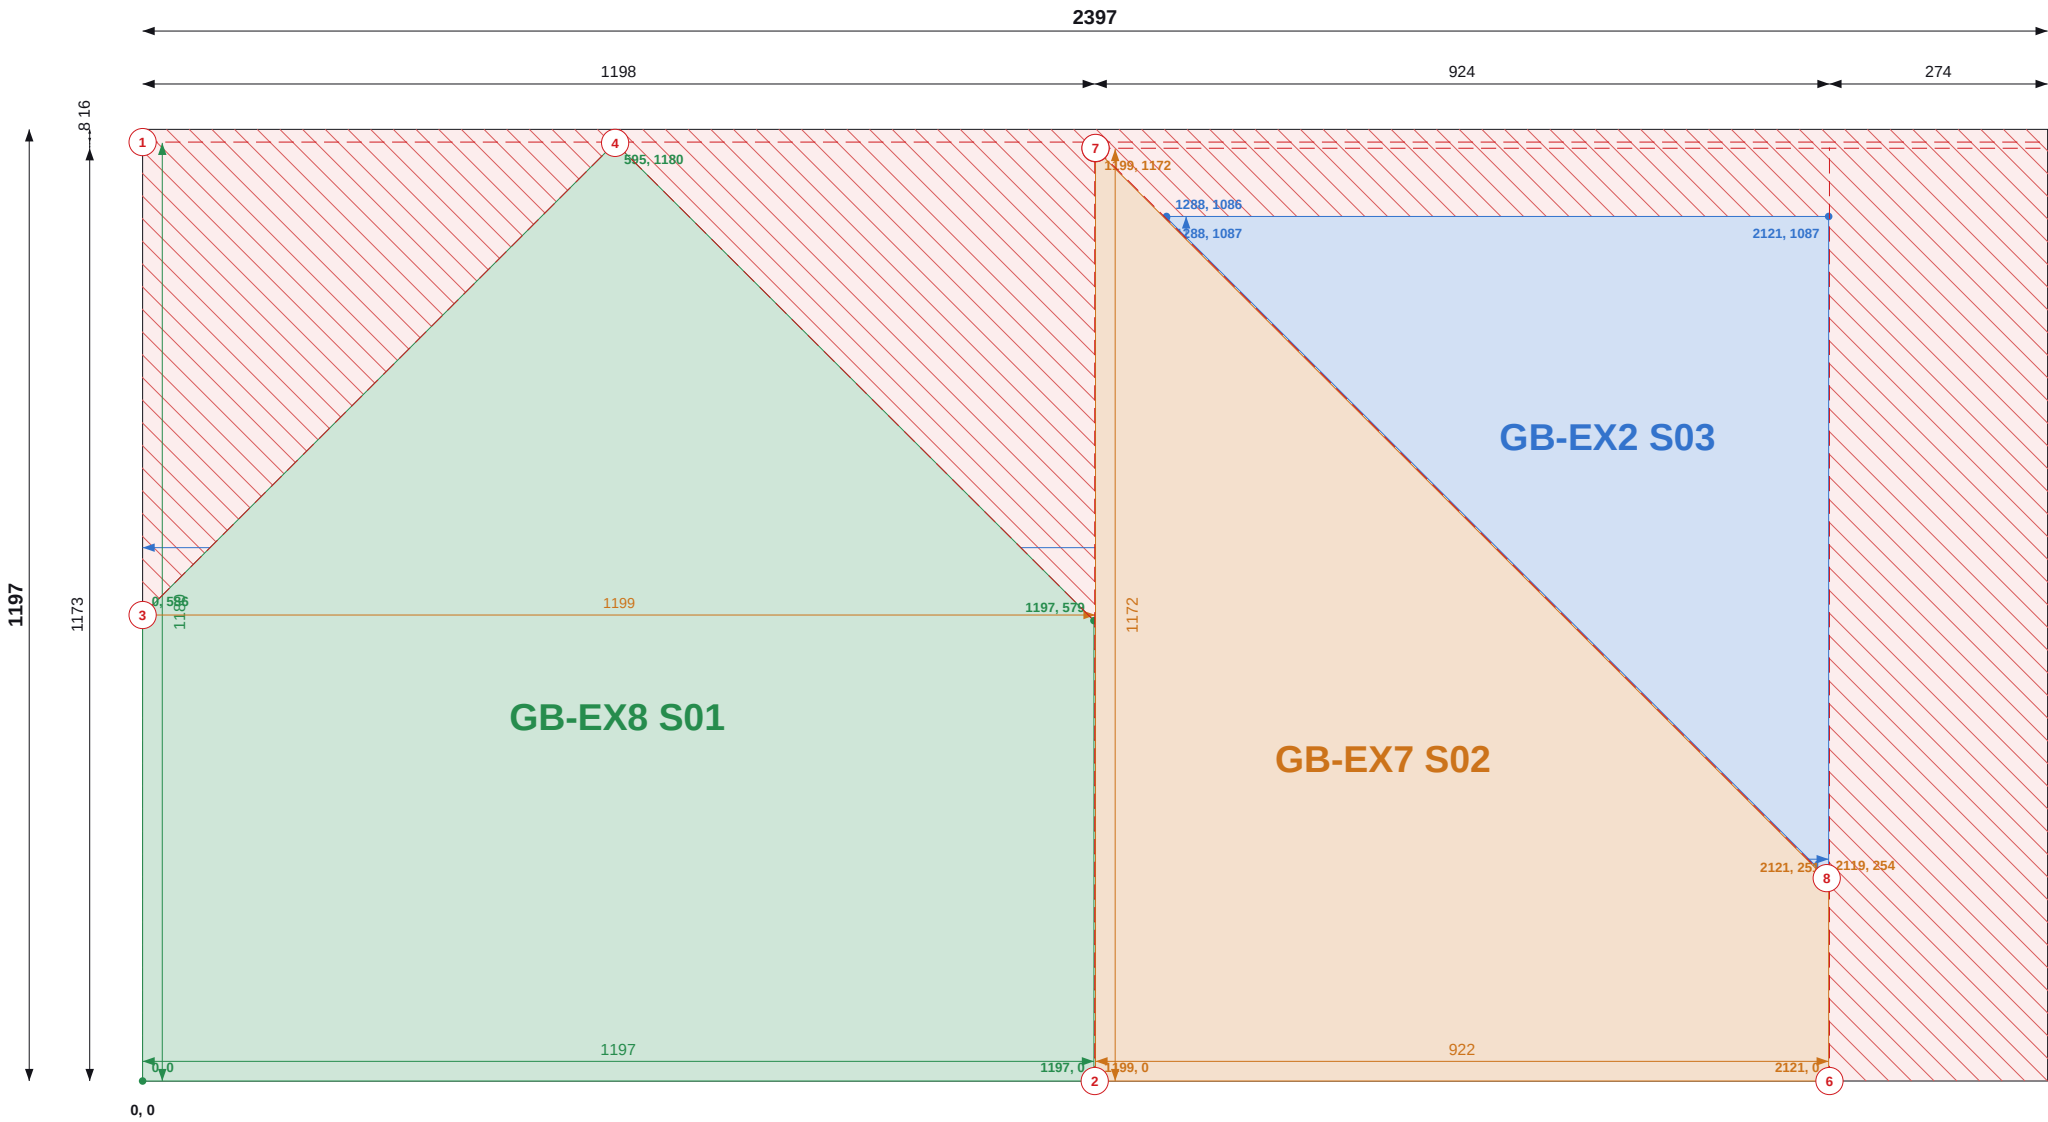

Top / left chains = saw cut positions (to cut centres). Coloured = part size and position.

SHEET 6 OF 14

THIS SHEET

Item	Value
Parts	3
Used / waste	71.8% / 0.81 m2
Reusable offcuts	0
Saw cuts / shared	8 / 5

PIECES (POSITION = BOTTOM-LEFT CORNER)

Label	Size	X, Y
GB-EX2 S03	833 x 833 rake to 3	1288, 254
GB-EX8 S01	1197 x 587 rake to 580	0, 0
GB-EX7 S02	922 x 1172 rake to 252	1199, 0

NOTES

- Cut from OSB/3 9mm 1197x2397, 2mm saw kerf. Viewed on the face; dimensions from the sheet's bottom-left corner (0,0). Red numbered lines = saw cuts in order, each edge to edge.
- Coloured dimensions belong to the part of that colour: its width and height, and its position from the sheet edges. Raked parts: corner coordinates at each corner.
- Red hatch = waste. Labels = panel + piece mark on the manufacture drawing.

REVISIONS

REV	DATE	DESCRIPTION
C01	13.09.26	Construction issue



TLS TIMBER FRAME

Design & Manufacture

Scan: 3D model + drawings



CLIENT	PROJECT
MP Adams	MP Adams Plot 3, Eckington


DRAWING TITLE
OSB CUTTING - GABLES - SHEET 6 OF 14

OSB/3 9mm 1197x2397 | Gables

SCALE	SIZE	DATE	DRAWN
NTS	A3	13.09.26	TS

STATUS	DRAWING No.	REV
CONSTRUCTION	P3-CP-OSB-03 / 06	C01

Do not scale. All dimensions in mm. Check all dimensions on site.

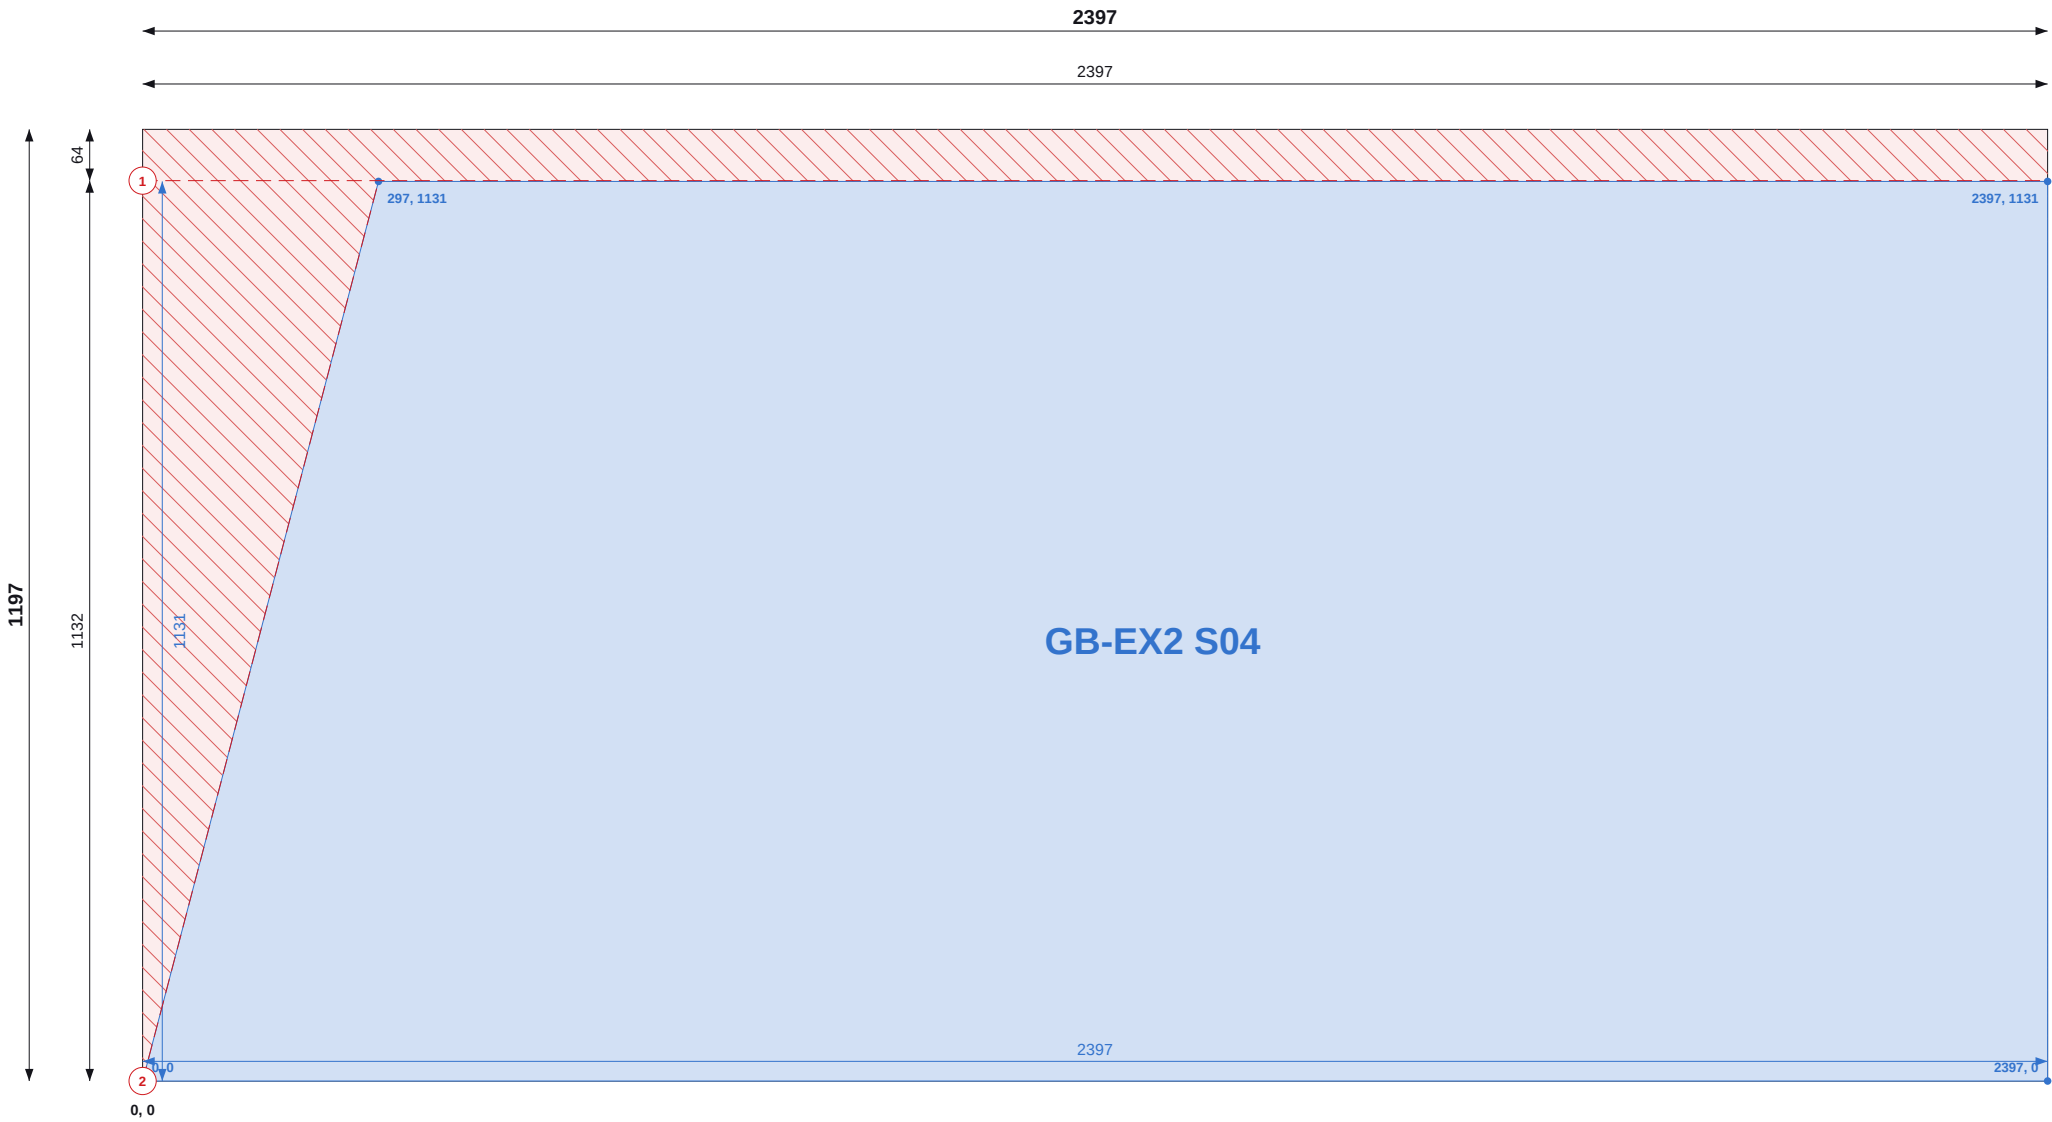

Top / left chains = saw cut positions (to cut centres). Coloured = part size and position.

SHEET 7 OF 14

THIS SHEET

Item	Value
Parts	1
Used / waste	88.7% / 0.32 m2
Reusable offcuts	0
Saw cuts / shared	2 / 1

PIECES (POSITION = BOTTOM-LEFT CORNER)

Label	Size	X, Y
GB-EX2 S04	1131 x 2397 rake to 2100	0, 0

NOTES

- Cut from OSB/3 9mm 1197x2397, 2mm saw kerf. Viewed on the face; dimensions from the sheet's bottom-left corner (0,0). Red numbered lines = saw cuts in order, each edge to edge.
- Coloured dimensions belong to the part of that colour: its width and height, and its position from the sheet edges. Raked parts: corner coordinates at each corner.
- Red hatch = waste. Labels = panel + piece mark on the manufacture drawing.

REVISIONS

REV	DATE	DESCRIPTION
C01	13.09.26	Construction issue



TLS TIMBER FRAME

Design & Manufacture

Scan: 3D model + drawings



CLIENT	PROJECT
MP Adams	MP Adams Plot 3, Eckington


DRAWING TITLE
OSB CUTTING - GABLES - SHEET 7 OF 14

OSB/3 9mm 1197x2397 | Gables

SCALE	SIZE	DATE	DRAWN
NTS	A3	13.09.26	TS

STATUS	DRAWING No.	REV
CONSTRUCTION	P3-CP-OSB-03 / 07	C01

Do not scale. All dimensions in mm. Check all dimensions on site.

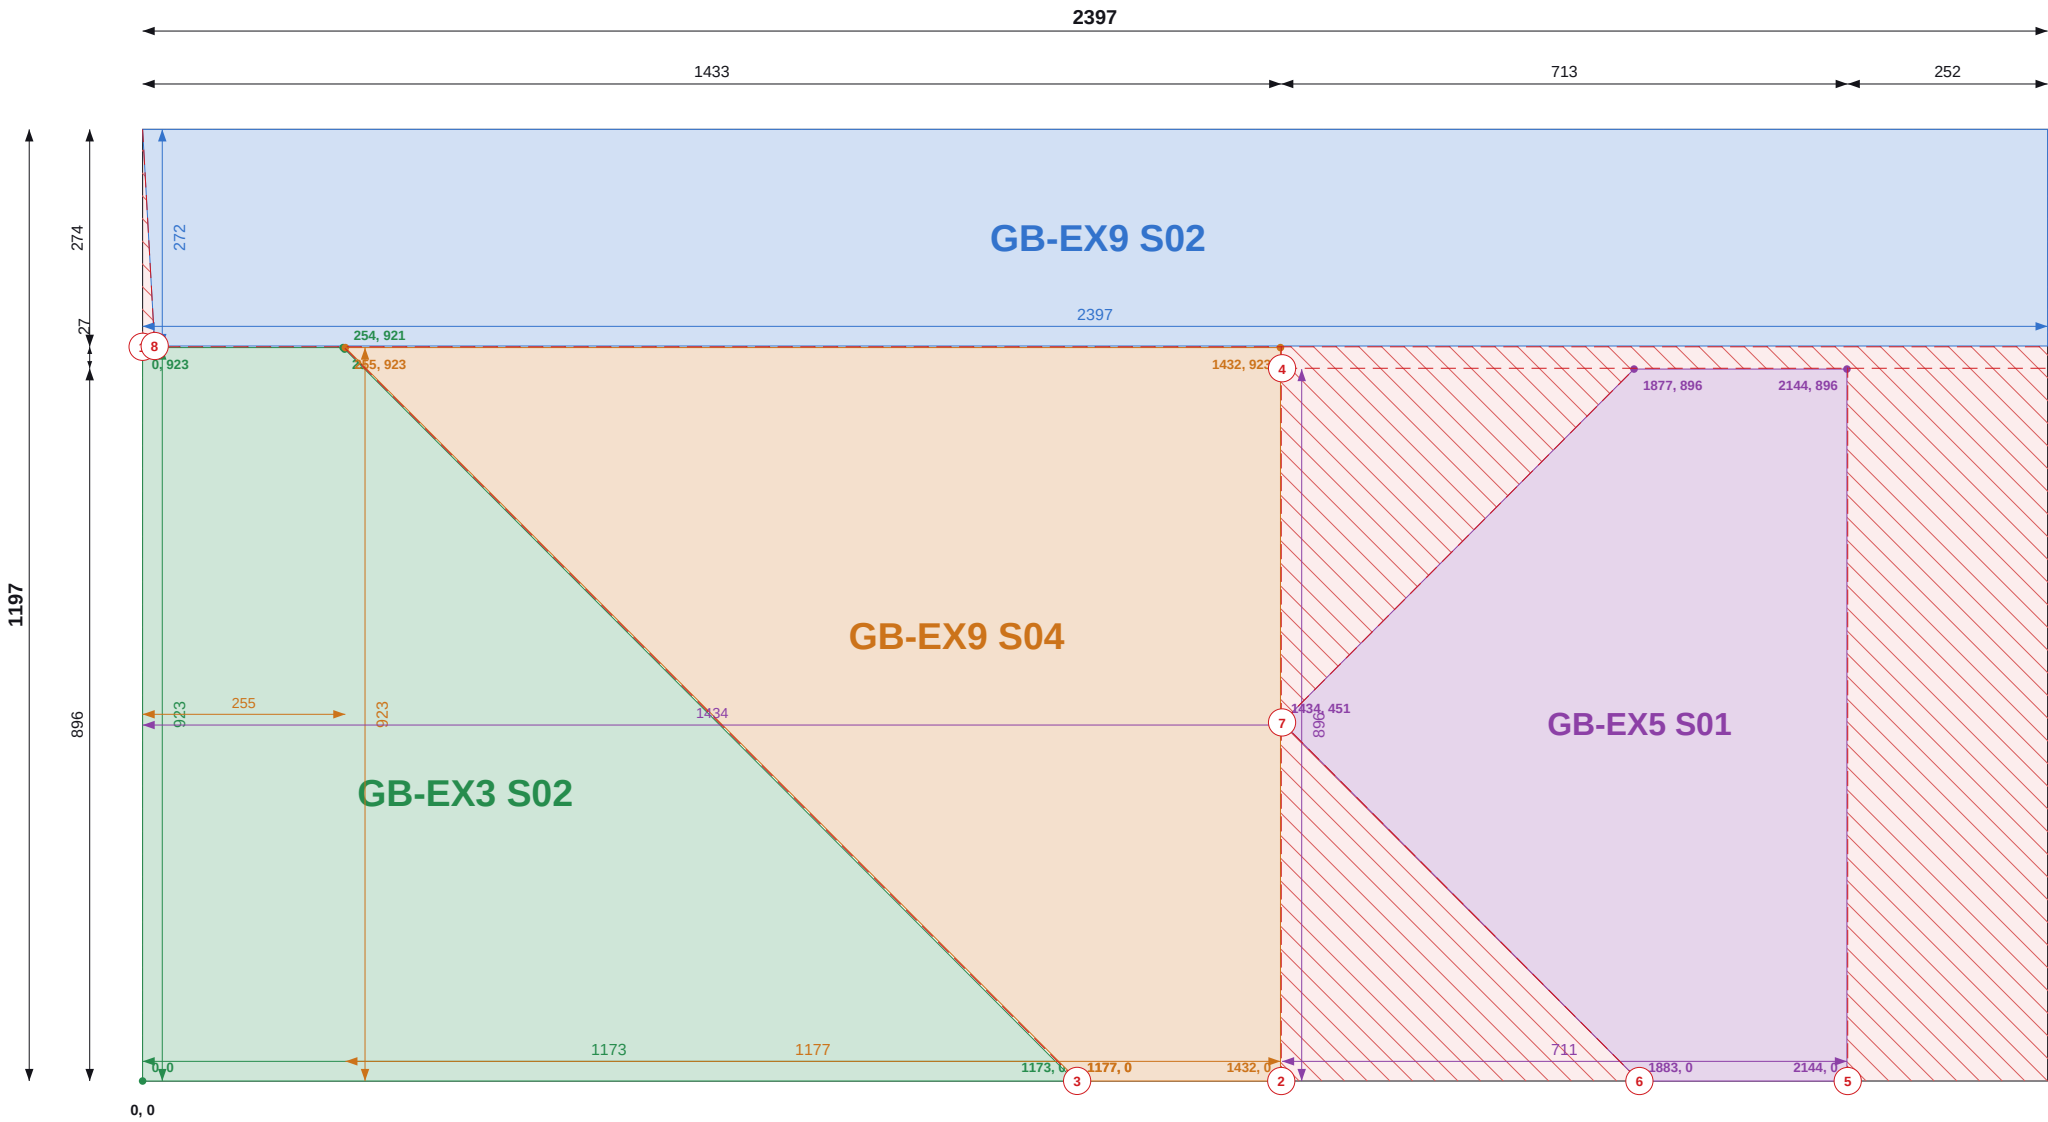

Top / left chains = saw cut positions (to cut centres). Coloured = part size and position.

SHEET 8 OF 14

THIS SHEET

Item	Value
Parts	4
Used / waste	83.8% / 0.46 m2
Reusable offcuts	0
Saw cuts / shared	8 / 6

PIECES (POSITION = BOTTOM-LEFT CORNER)

Label	Size	X, Y
GB-EX9 S02	272 x 2397	0, 925
GB-EX3 S02	923 x 1173 rake to 253	0, 0
GB-EX9 S04	923 x 1177 rake to 255	255, 0
GB-EX5 S01	896 x 269 rake to 262	1434, 0

NOTES

- Cut from OSB/3 9mm 1197x2397, 2mm saw kerf. Viewed on the face; dimensions from the sheet's bottom-left corner (0,0). Red numbered lines = saw cuts in order, each edge to edge.
- Coloured dimensions belong to the part of that colour: its width and height, and its position from the sheet edges. Raked parts: corner coordinates at each corner.
- Red hatch = waste. Labels = panel + piece mark on the manufacture drawing.

REVISIONS

REV	DATE	DESCRIPTION
C01	13.09.26	Construction issue



TLS TIMBER FRAME

Design & Manufacture

Scan: 3D model + drawings



CLIENT MP Adams	PROJECT MP Adams Plot 3, Eckington
--------------------	---------------------------------------

DRAWING TITLE OSB CUTTING - GABLES - SHEET 8 OF 14

OSB/3 9mm 1197x2397 | Gables

SCALE NTS	SIZE A3	DATE 13.09.26	DRAWN TS
--------------	------------	------------------	-------------

STATUS CONSTRUCTION	DRAWING No. P3-CP-OSB-03 / 08	REV C01
------------------------	----------------------------------	------------

Item	Value
Parts	3
Used / waste	97.0% / 0.09 m2
Reusable offcuts	0
Saw cuts / shared	5 / 3

PIECES (POSITION = BOTTOM-LEFT CORNER)

Label	Size	X, Y
GB-EX1 S02	273 x 2397	0, 921
GB-EX4 S04	898 x 1152 rake to 257	0, 21
GB-EX7 S01	919 x 2093 rake to 1177	238, 0

NOTES

1. Cut from OSB/3 9mm 1197x2397, 2mm saw kerf. Viewed on the face; dimensions from the sheet's bottom-left corner (0,0). Red numbered lines = saw cuts in order, each edge to edge.
2. Coloured dimensions belong to the part of that colour: its width and height, and its position from the sheet edges. Raked parts: corner coordinates at each corner.
3. Red hatch = waste. Labels = panel + piece mark on the manufacture drawing.

REVISIONS

REV	DATE	DESCRIPTION
C01	13.09.26	Construction issue



TLS TIMBER FRAME

Design & Manufacture 

Scan: 3D model + drawings



CLIENT

MP Adams

PROJECT

MP Adams Plot 3, Eckington

DRAWING TITLE

OSB CUTTING - GABLES - SHEET 9 OF 14


OSB/3 9mm 1197x2397 | Gables

SCALE	SIZE	DATE	DRAWN
NTS	A3	13.09.26	TS

STATUS CONSTRUCTION	DRAWING No. P3-CP-OSB-03 / 09	REV C01
---	---	---

Do not scale. All dimensions in mm. Check all dimensions on site.

Do not scale. All dimensions in mm. Check all dimensions on site.

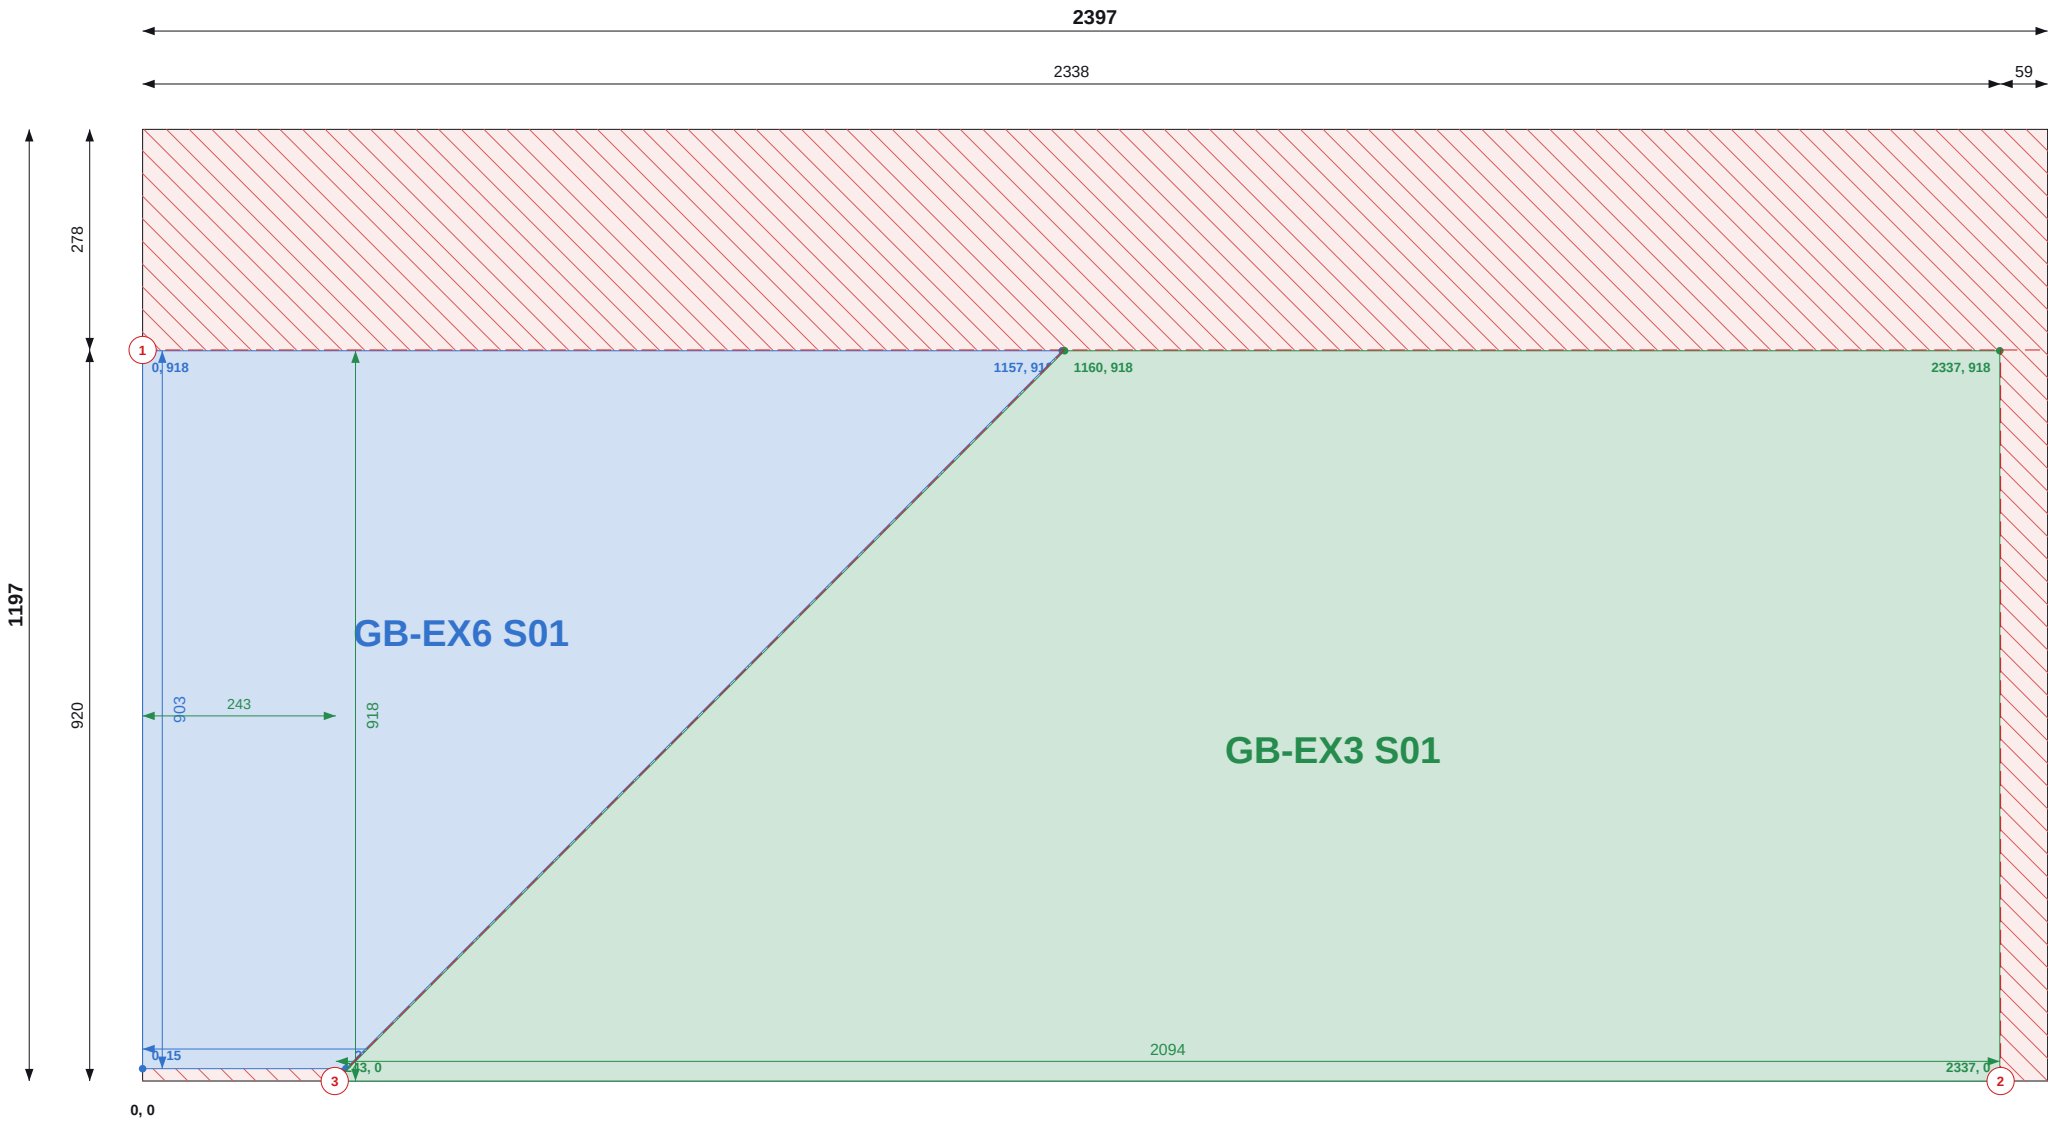

Top / left chains = saw cut positions (to cut centres). Coloured = part size and position.

SHEET 10 OF 14

THIS SHEET

Item	Value
Parts	2
Used / waste	74.6% / 0.73 m2
Reusable offcuts	0
Saw cuts / shared	3 / 1

PIECES (POSITION = BOTTOM-LEFT CORNER)

Label	Size	X, Y
GB-EX6 S01	903 x 1157 rake to 257	0, 15
GB-EX3 S01	918 x 2094 rake to 1178	243, 0

NOTES

- Cut from OSB/3 9mm 1197x2397, 2mm saw kerf. Viewed on the face; dimensions from the sheet's bottom-left corner (0,0). Red numbered lines = saw cuts in order, each edge to edge.
- Coloured dimensions belong to the part of that colour: its width and height, and its position from the sheet edges. Raked parts: corner coordinates at each corner.
- Red hatch = waste. Labels = panel + piece mark on the manufacture drawing.

REVISIONS

REV	DATE	DESCRIPTION
C01	13.09.26	Construction issue



TLS TIMBER FRAME

Design & Manufacture

Scan: 3D model + drawings



CLIENT MP Adams	PROJECT MP Adams Plot 3, Eckington
--------------------	---------------------------------------


DRAWING TITLE OSB CUTTING - GABLES - SHEET 10 OF 14

OSB/3 9mm 1197x2397 | Gables

SCALE NTS	SIZE A3	DATE 13.09.26	DRAWN TS
--------------	------------	------------------	-------------

STATUS CONSTRUCTION	DRAWING No. P3-CP-OSB-03 / 10	REV C01
-------------------------------	---	-------------------

Do not scale. All dimensions in mm. Check all dimensions on site.

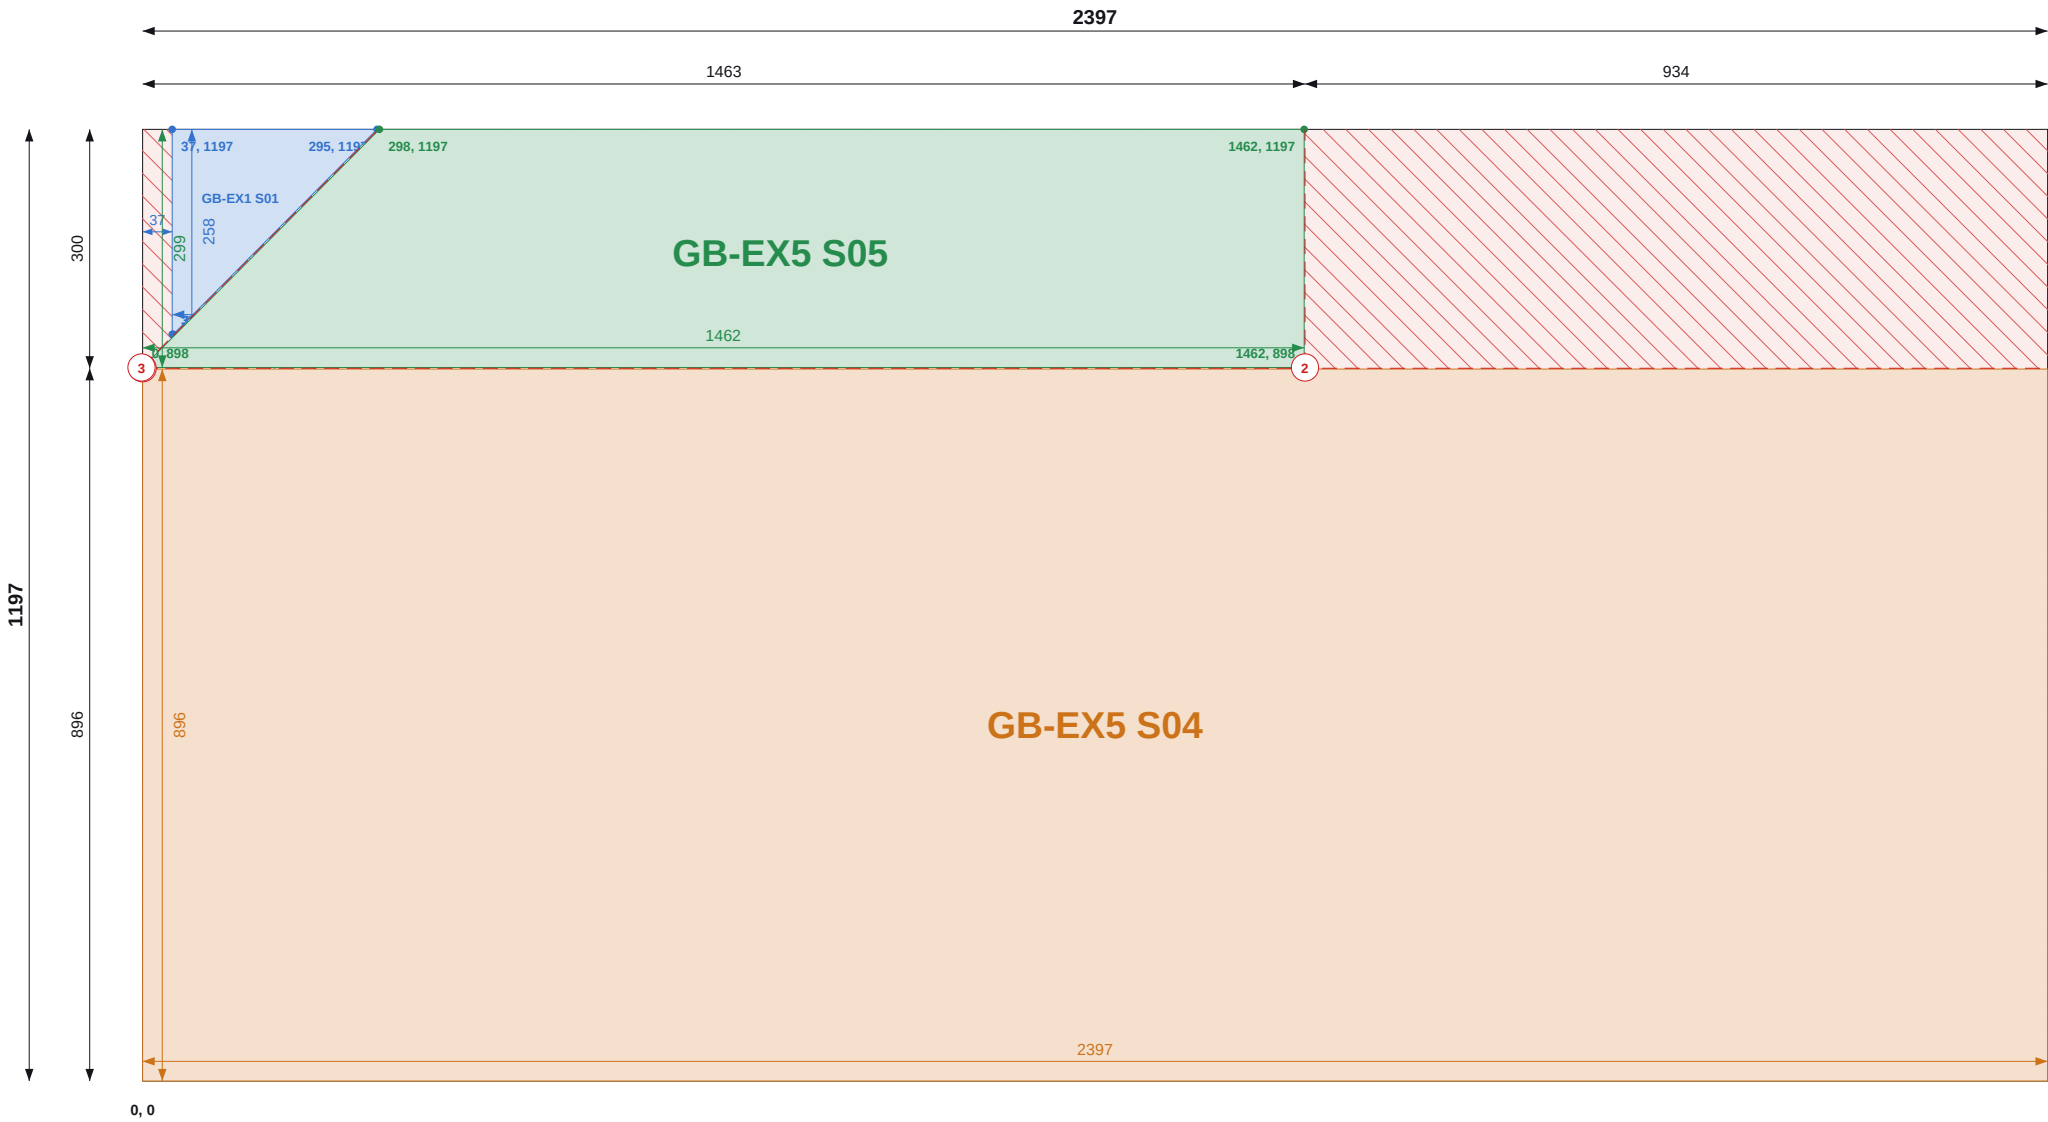

Top / left chains = saw cut positions (to cut centres). Coloured = part size and position.

SHEET 11 OF 14

THIS SHEET

Item	Value
Parts	3
Used / waste	89.7% / 0.30 m2
Reusable offcuts	0
Saw cuts / shared	3 / 2

PIECES (POSITION = BOTTOM-LEFT CORNER)

Label	Size	X, Y
GB-EX1 S01	258 x 258 rake to 3	37, 939
GB-EX5 S05	299 x 1461 rake to 1165	0, 898
GB-EX5 S04	896 x 2397	0, 0

NOTES

- Cut from OSB/3 9mm 1197x2397, 2mm saw kerf. Viewed on the face; dimensions from the sheet's bottom-left corner (0,0). Red numbered lines = saw cuts in order, each edge to edge.
- Coloured dimensions belong to the part of that colour: its width and height, and its position from the sheet edges. Raked parts: corner coordinates at each corner.
- Red hatch = waste. Labels = panel + piece mark on the manufacture drawing.

REVISIONS

REV	DATE	DESCRIPTION
C01	13.09.26	Construction issue



TLS TIMBER FRAME

Design & Manufacture

Scan: 3D model + drawings



CLIENT	PROJECT
MP Adams	MP Adams Plot 3, Eckington

DRAWING TITLE
OSB CUTTING - GABLES - SHEET 11 OF 14

OSB/3 9mm 1197x2397 | Gables

SCALE	SIZE	DATE	DRAWN
NTS	A3	13.09.26	TS

STATUS	DRAWING No.	REV
CONSTRUCTION	P3-CP-OSB-03 / 11	C01

Do not scale. All dimensions in mm. Check all dimensions on site.



SHEET 12 OF 14

THIS SHEET

Item	Value
Parts	2
Used / waste	95.3% / 0.14 m2
Reusable offcuts	0
Saw cuts / shared	2 / 2

PIECES (POSITION = BOTTOM-LEFT CORNER)

Label	Size	X, Y
GB-EX8 S06	321 x 2397	0, 876
GB-EX8 S04	874 x 2397 rake to 2100	0, 0

NOTES

- Cut from OSB/3 9mm 1197x2397, 2mm saw kerf. Viewed on the face; dimensions from the sheet's bottom-left corner (0,0). Red numbered lines = saw cuts in order, each edge to edge.
- Coloured dimensions belong to the part of that colour: its width and height, and its position from the sheet edges. Raked parts: corner coordinates at each corner.
- Red hatch = waste. Labels = panel + piece mark on the manufacture drawing.

REVISIONS

REV	DATE	DESCRIPTION
C01	13.09.26	Construction issue



TLS TIMBER FRAME

Design & Manufacture

Scan: 3D model + drawings



CLIENT MP Adams	PROJECT MP Adams Plot 3, Eckington
--------------------	---------------------------------------

DRAWING TITLE OSB CUTTING - GABLES - SHEET 12 OF 14

OSB/3 9mm 1197x2397 | Gables

SCALE NTS	SIZE A3	DATE 13.09.26	DRAWN TS
--------------	------------	------------------	-------------

STATUS CONSTRUCTION	DRAWING No. P3-CP-OSB-03 / 12	REV C01
-------------------------------	---	-------------------

Item	Value
Parts	4
Used / waste	79.5% / 0.59 m2
Reusable offcuts	0
Saw cuts / shared	8 / 5

Label	Size	X, Y
GB-EX4 S02	297 x 2397	0, 884
GB-EX5 S02	264 x 264 rake to 3	770, 424
GB-EX2 S06	688 x 882	0, 0
GB-EX2 S01	688 x 1190 rake to 1183	690, 0

1. Cut from OSB/3 9mm 1197x2397, 2mm saw kerf. Viewed on the face; dimensions from the sheet's bottom-left corner (0,0). Red numbered lines = saw cuts in order, each edge to edge.
2. Coloured dimensions belong to the part of that colour: its width and height, and its position from the sheet edges. Raked parts: corner coordinates at each corner.
3. Red hatch = waste. Labels = panel + piece mark on the manufacture drawing.

REV	DATE	DESCRIPTION
C01	13.09.26	Construction issue

Design & Manufacture 

Scan: 3D model + drawings



CLIENT

MP Adams

PROJECT

MP Adams Plot 3, Eckington

DRAWING TITLE

OSB CUTTING - GABLES - SHEET 13 OF 14

OSB/3 9mm 1197x2397 | Gables

SCALE	SIZE	DATE	DRAWN
NTS	A3	13.09.26	TS

STATUS

CONSTRUCTION

DRAWING No.


P3-CP-OSB-03 / 13

REV

C01

Do not scale. All dimensions in mm. Check all dimensions on site.

Do not scale. All dimensions in mm. Check all dimensions on site.

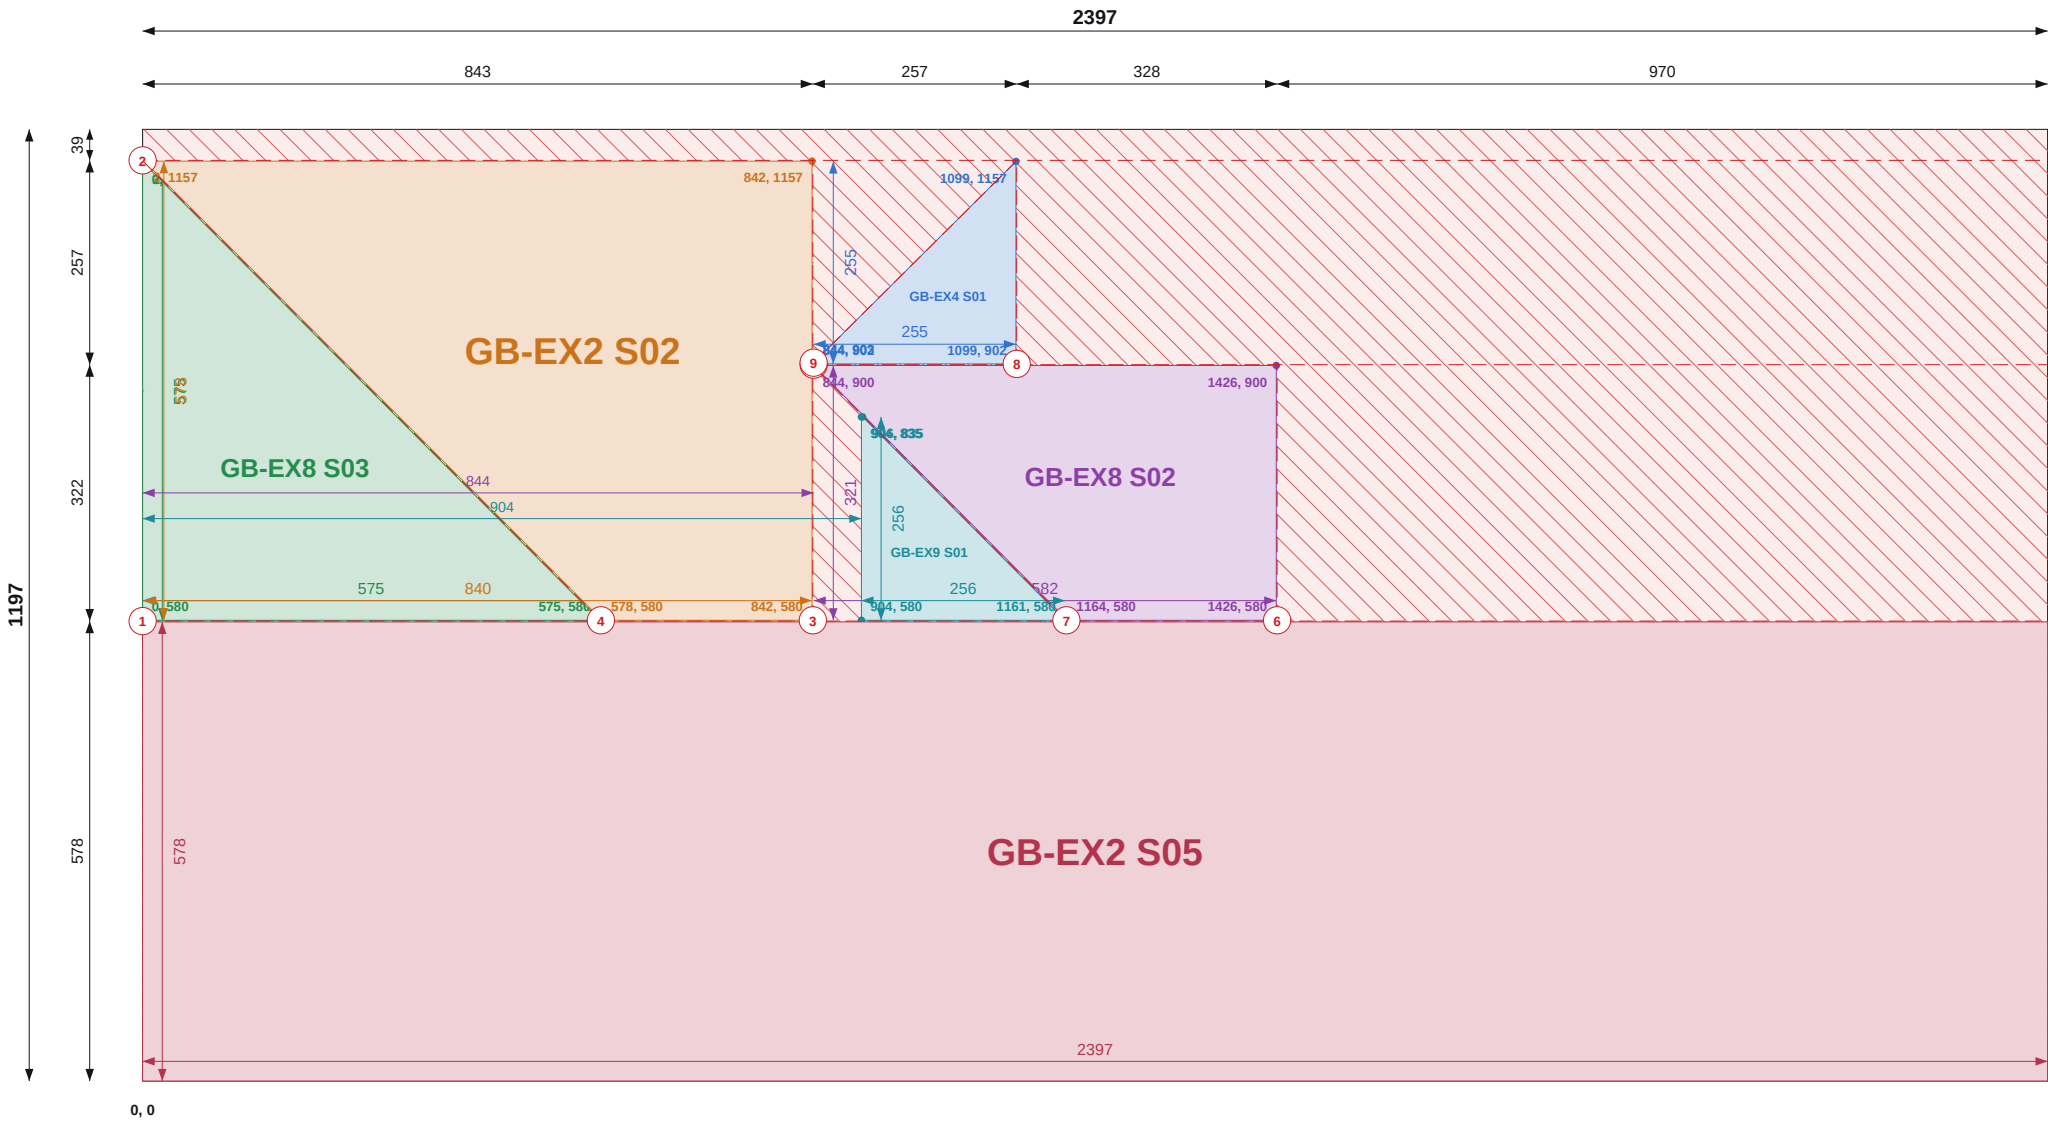

SHEET 14 OF 14

THIS SHEET

Item	Value
Parts	6
Used / waste	72.1% / 0.80 m2
Reusable offcuts	1
Saw cuts / shared	9 / 6

PIECES (POSITION = BOTTOM-LEFT CORNER)

Label	Size	X, Y
GB-EX4 S01	255 x 255 rake to 3	844, 902
GB-EX8 S03	575 x 575 rake to 3	0, 580
GB-EX2 S02	578 x 840 rake to 265	2, 580
GB-EX8 S02	321 x 582 rake to 264	844, 580
GB-EX9 S01	256 x 256 rake to 3	904, 580
GB-EX2 S05	578 x 2397	0, 0

NOTES

- Cut from OSB/3 9mm 1197x2397, 2mm saw kerf. Viewed on the face; dimensions from the sheet's bottom-left corner (0,0). Red numbered lines = saw cuts in order, each edge to edge.
- Coloured dimensions belong to the part of that colour: its width and height, and its position from the sheet edges. Raked parts: corner coordinates at each corner.
- Red hatch = waste. Labels = panel + piece mark on the manufacture drawing.

REVISIONS

REV	DATE	DESCRIPTION
C01	13.09.26	Construction issue



TLS TIMBER FRAME
Design & Manufacture
Scan: 3D model + drawings



CLIENT MP Adams	PROJECT MP Adams Plot 3, Eckington
--------------------	---------------------------------------

DRAWING TITLE
OSB CUTTING - GABLES - SHEET 14 OF 14

OSB/3 9mm 1197x2397 | Gables

SCALE NTS	SIZE A3	DATE 13.09.26	DRAWN TS
--------------	------------	------------------	-------------

STATUS CONSTRUCTION	DRAWING No. P3-CP-OSB-03 / 14	REV C01
-------------------------------	---	-------------------